


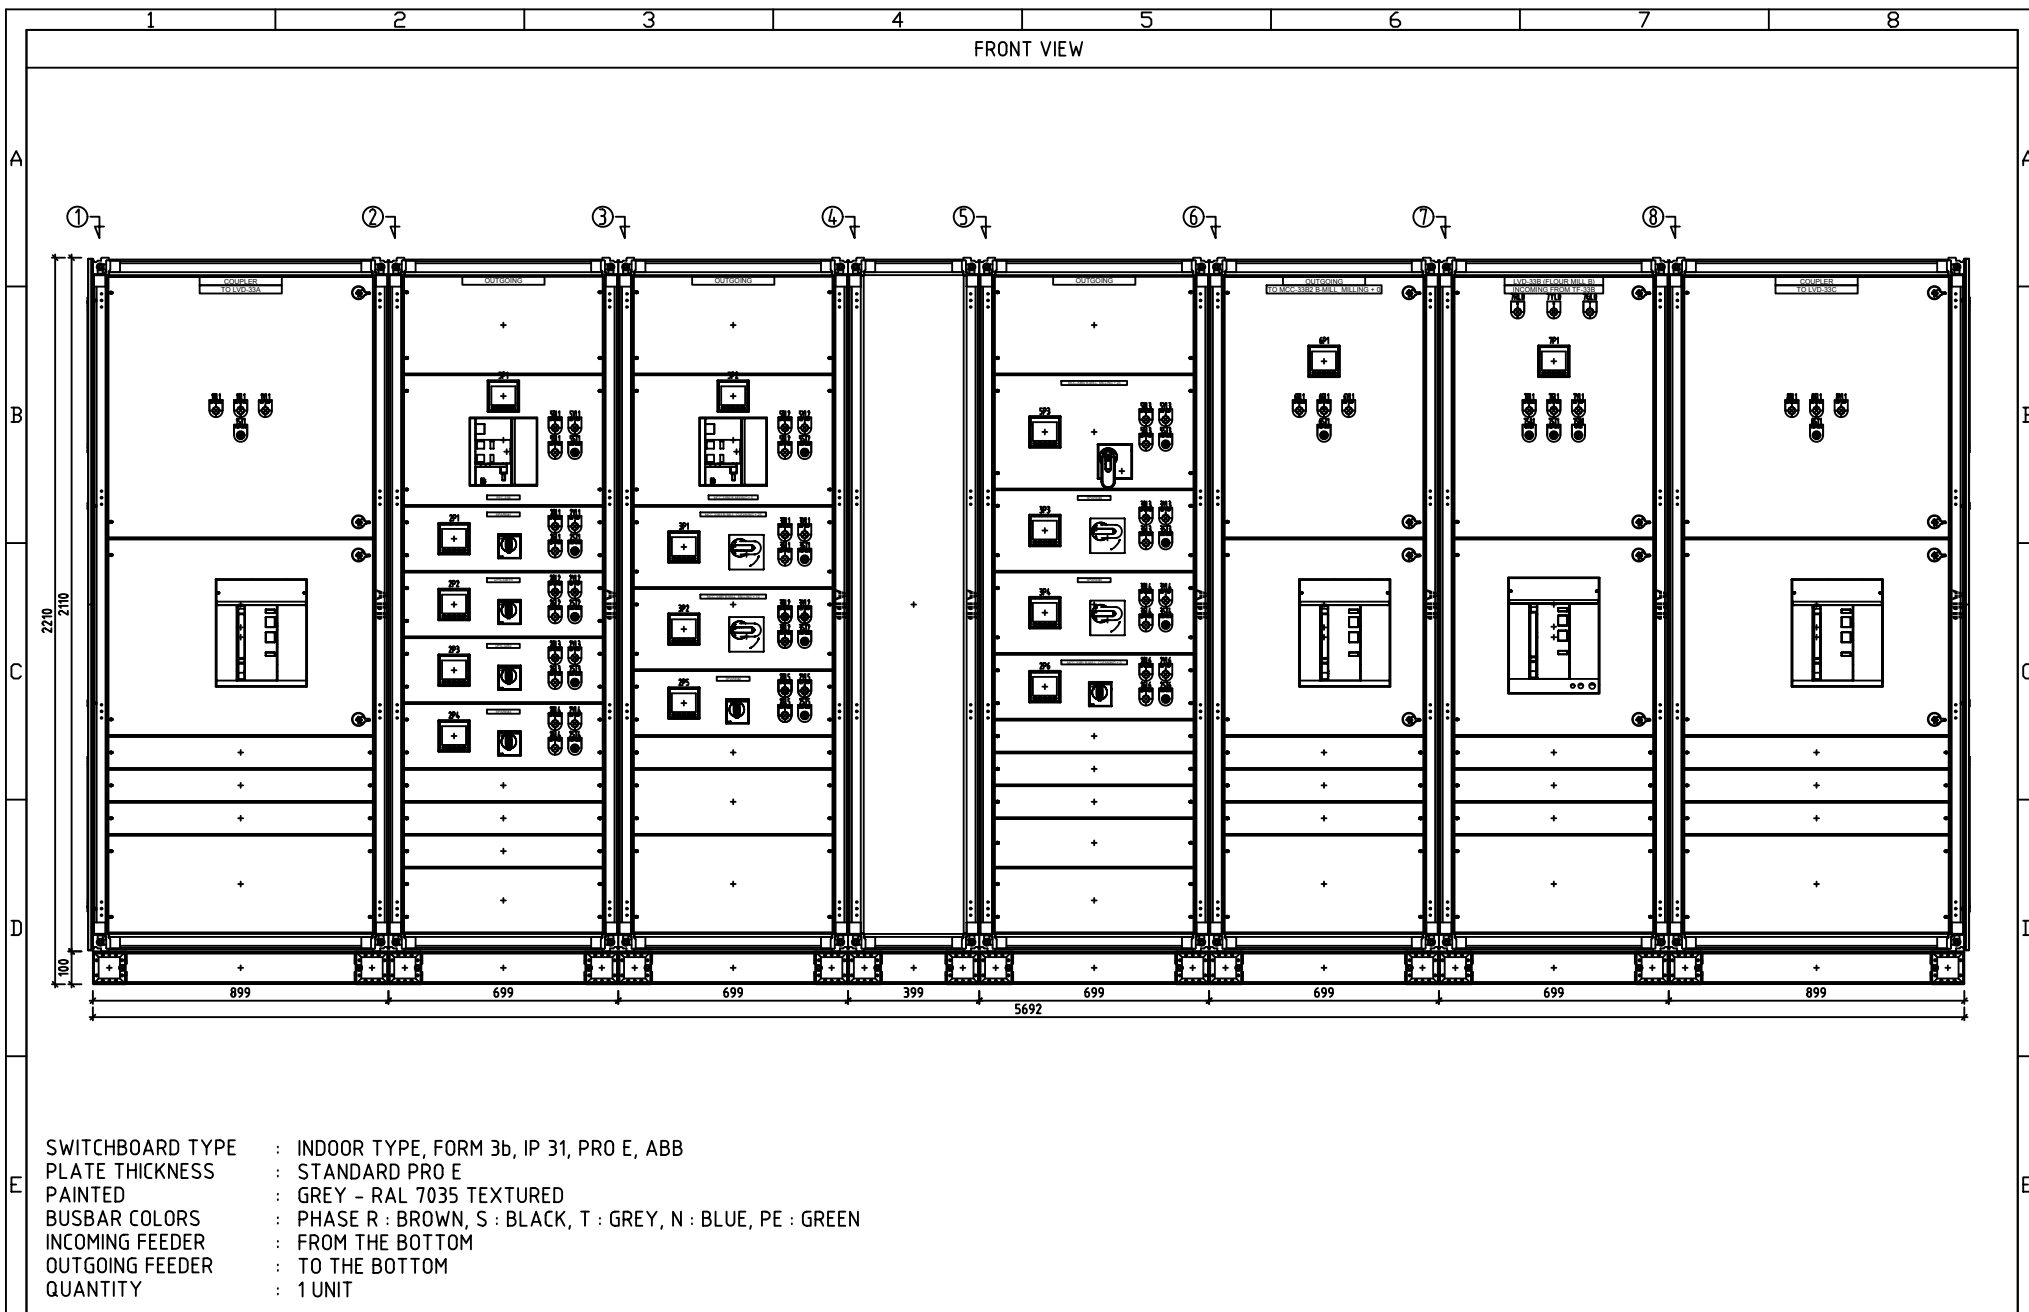


SWITCHBOARD TYPE : INDOOR TYPE, FORM 3b, IP 31, PRO E, ABB
 PLATE THICKNESS : STANDARD PRO E
 PAINTED : GREY - RAL 7035 TEXTURED
 BUSBAR COLORS : PHASE R : BROWN, S : BLACK, T : GREY, N : BLUE, PE : GREEN
 INCOMING FEEDER : FROM THE BOTTOM
 OUTGOING FEEDER : TO THE BOTTOM
 QUANTITY : 1 UNIT





PROJECT : WILMAR FLOUR MILL	DRAWING TITLE : OUTLINE DRAWING LVD-33B (FLOUR MILL B)		DATE	DRAWN	SIGN	VERIFIED	SIGN	DESCRIPTION	REV	PAGE
			06-07-2020	YD		SBR		FOR APPROVAL	1	
			...	YD		SBR		FOR APPROVAL R1	2	
			12-08-2020	YD		SBR		FOR APPROVAL R2	3	
CUSTOMER : PT. ABB SAKTI INDUSTRI	NO DR/JO : DR-017/IND.2020	SCALE : 1:23	12-08-2020	YD		SBR		FOR APPROVAL R2	4	15
	NO DWG. : ABB-001	Dimension in mm	25-08-2020	YD		SBR		FOR APPROVAL R3	5	


FRONT VIEW (COVER REMOVED)

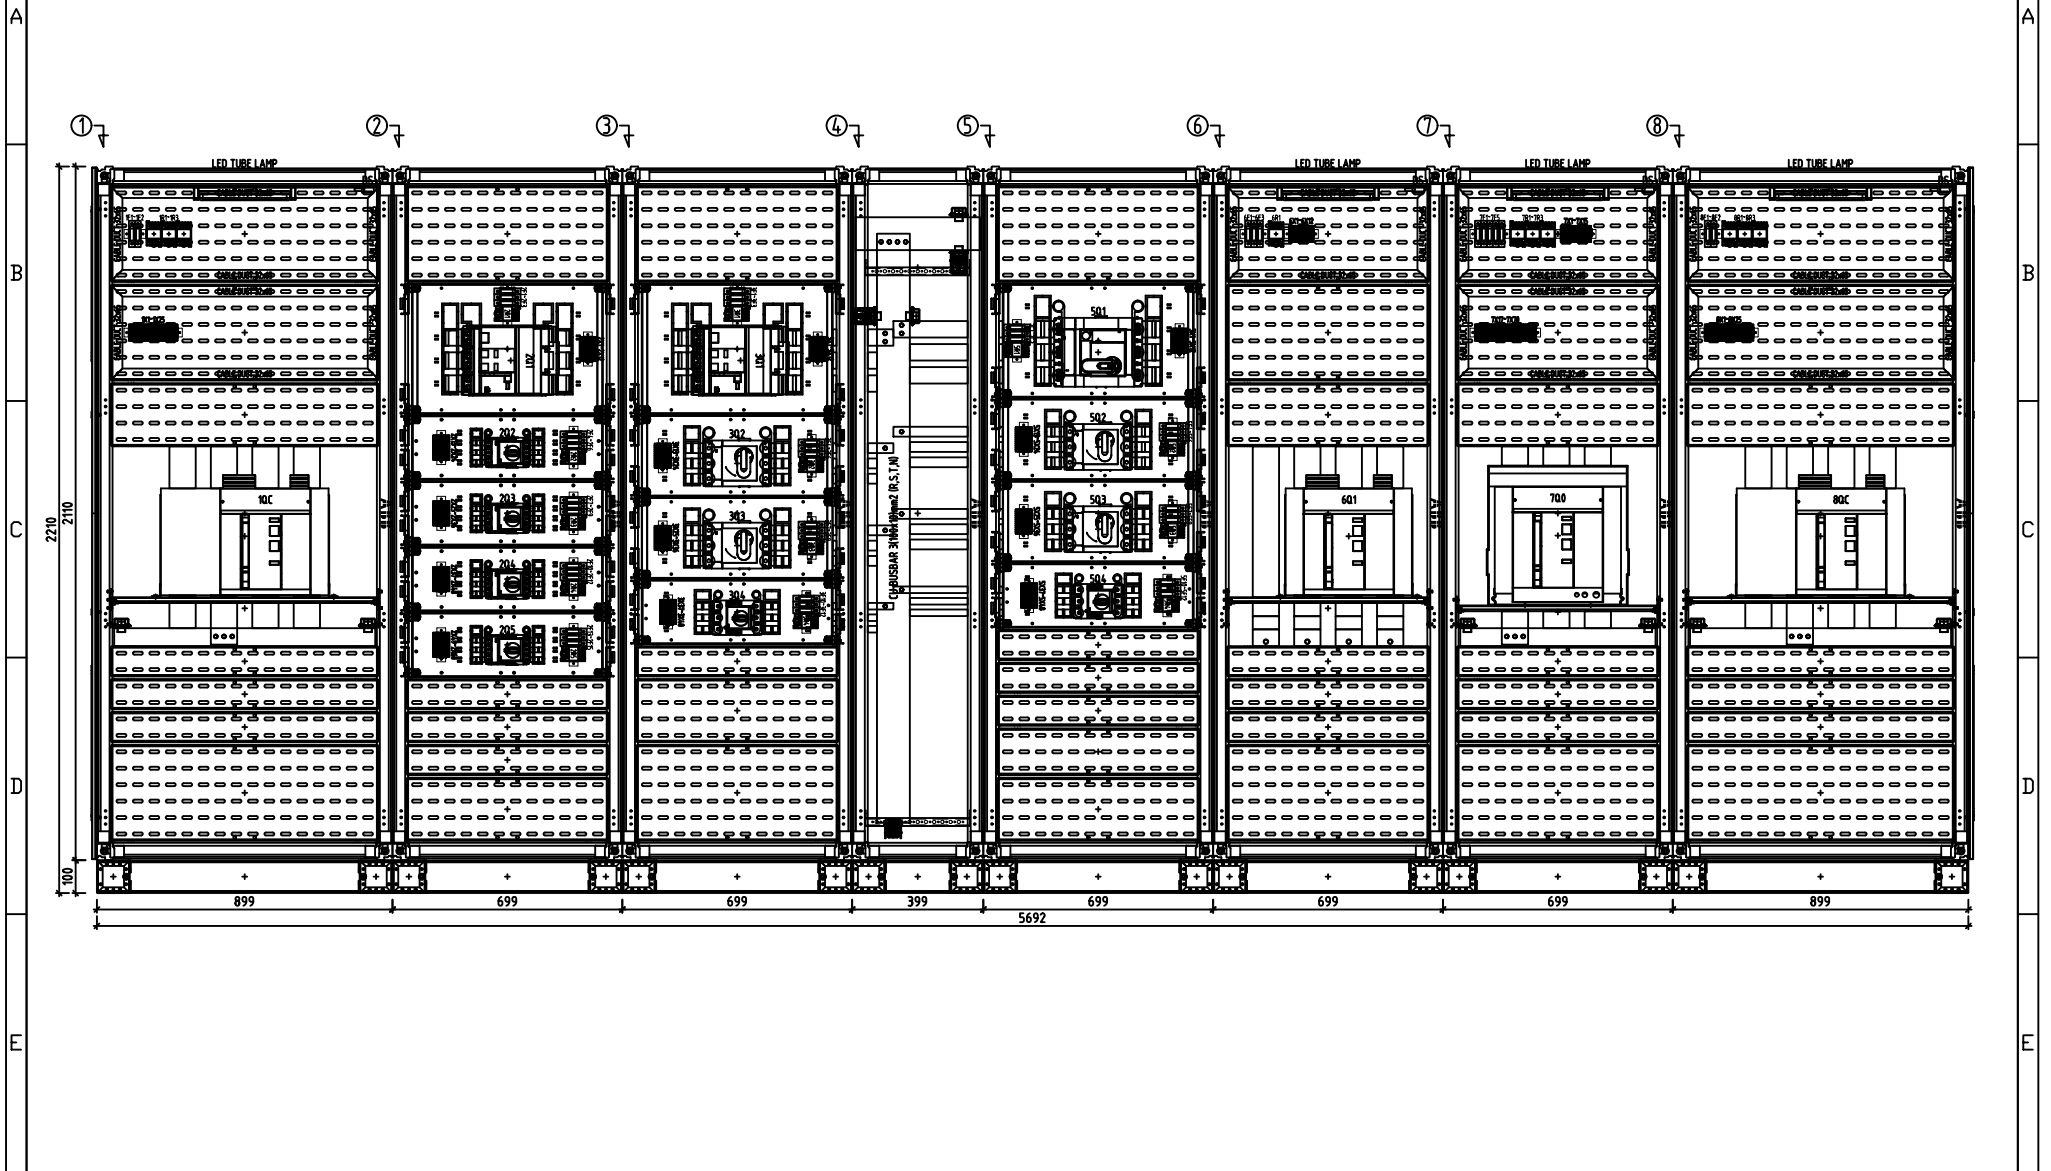



FRONT VIEW (COVER & BLANK PLATE REMOVED)

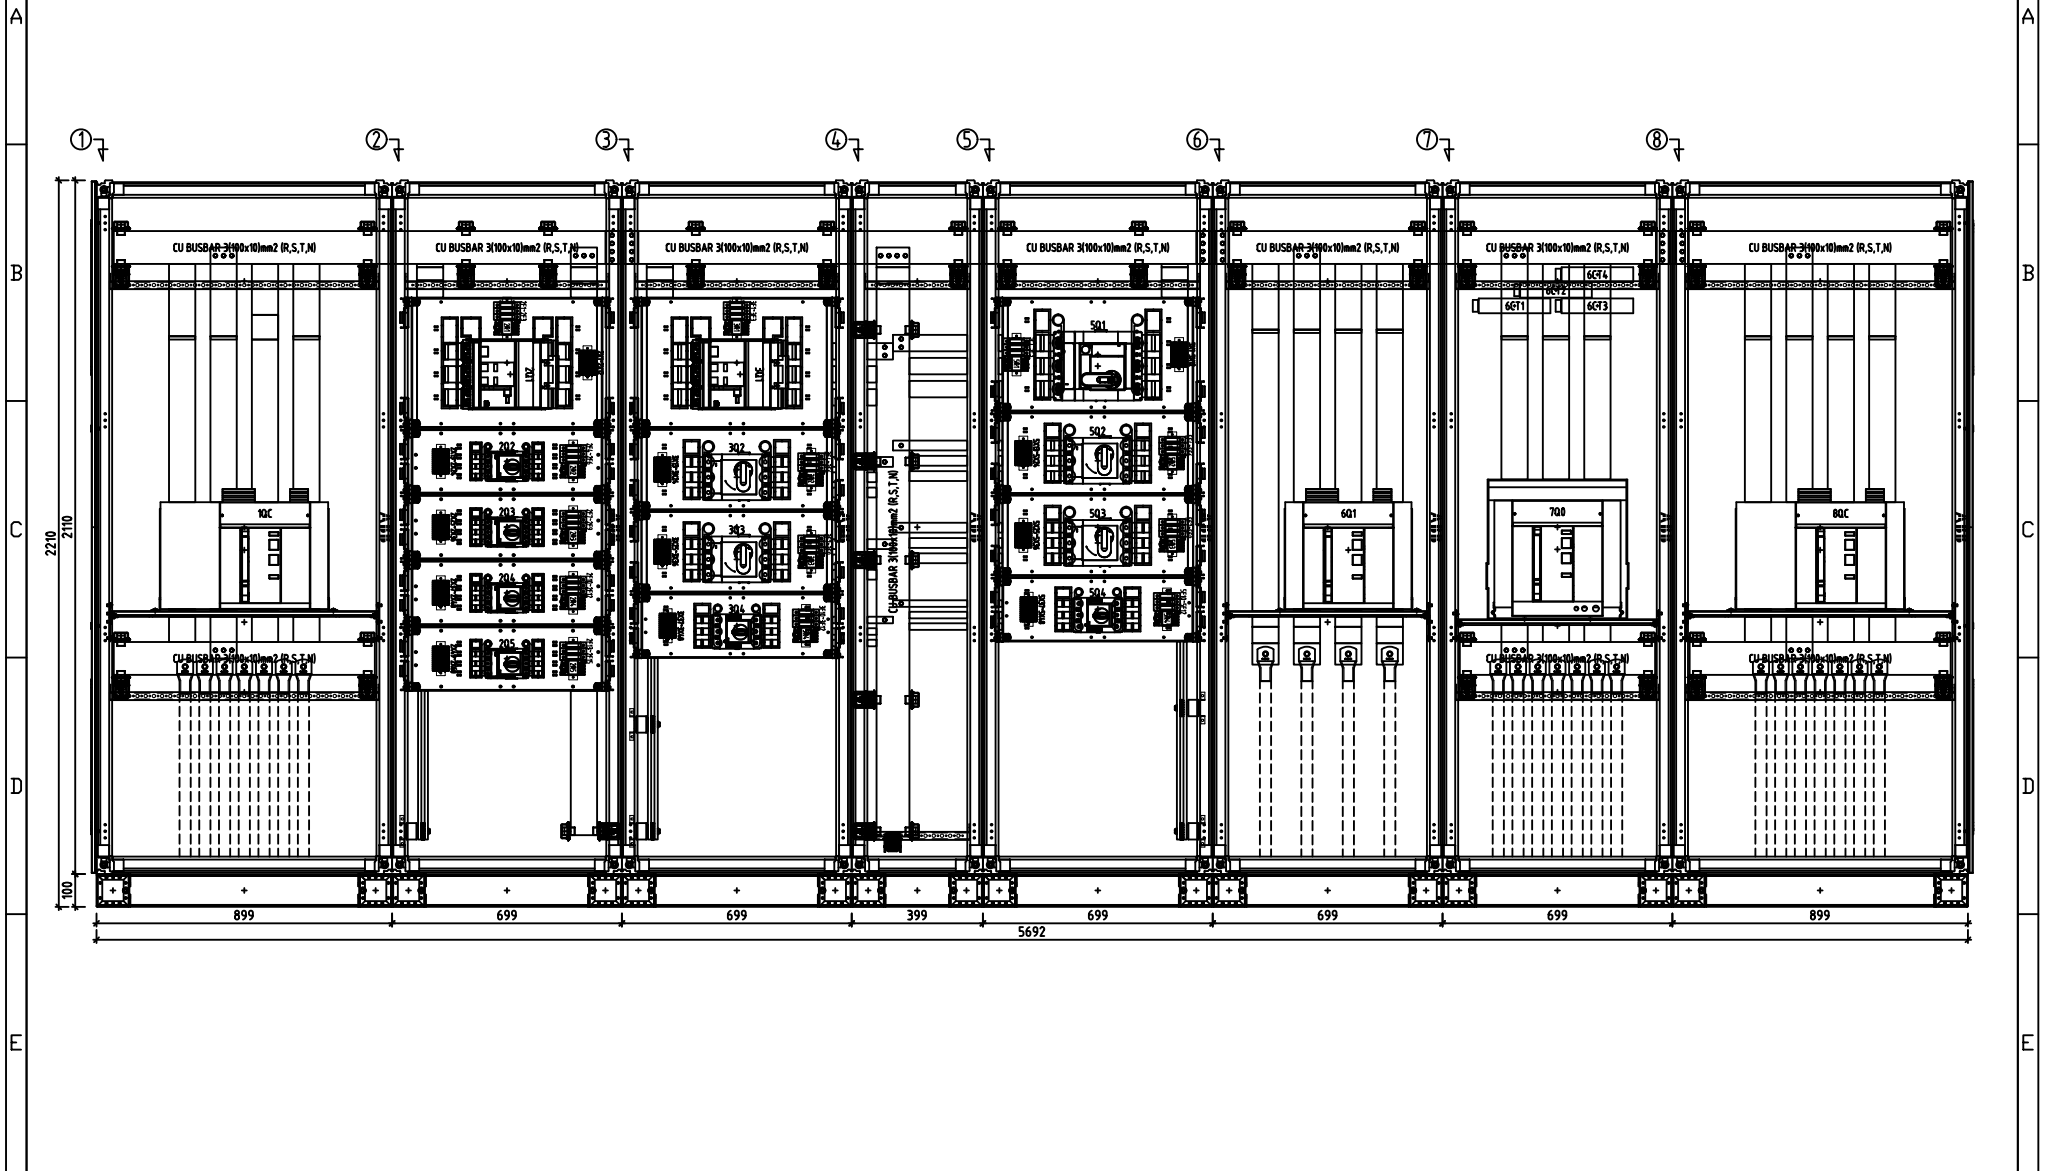

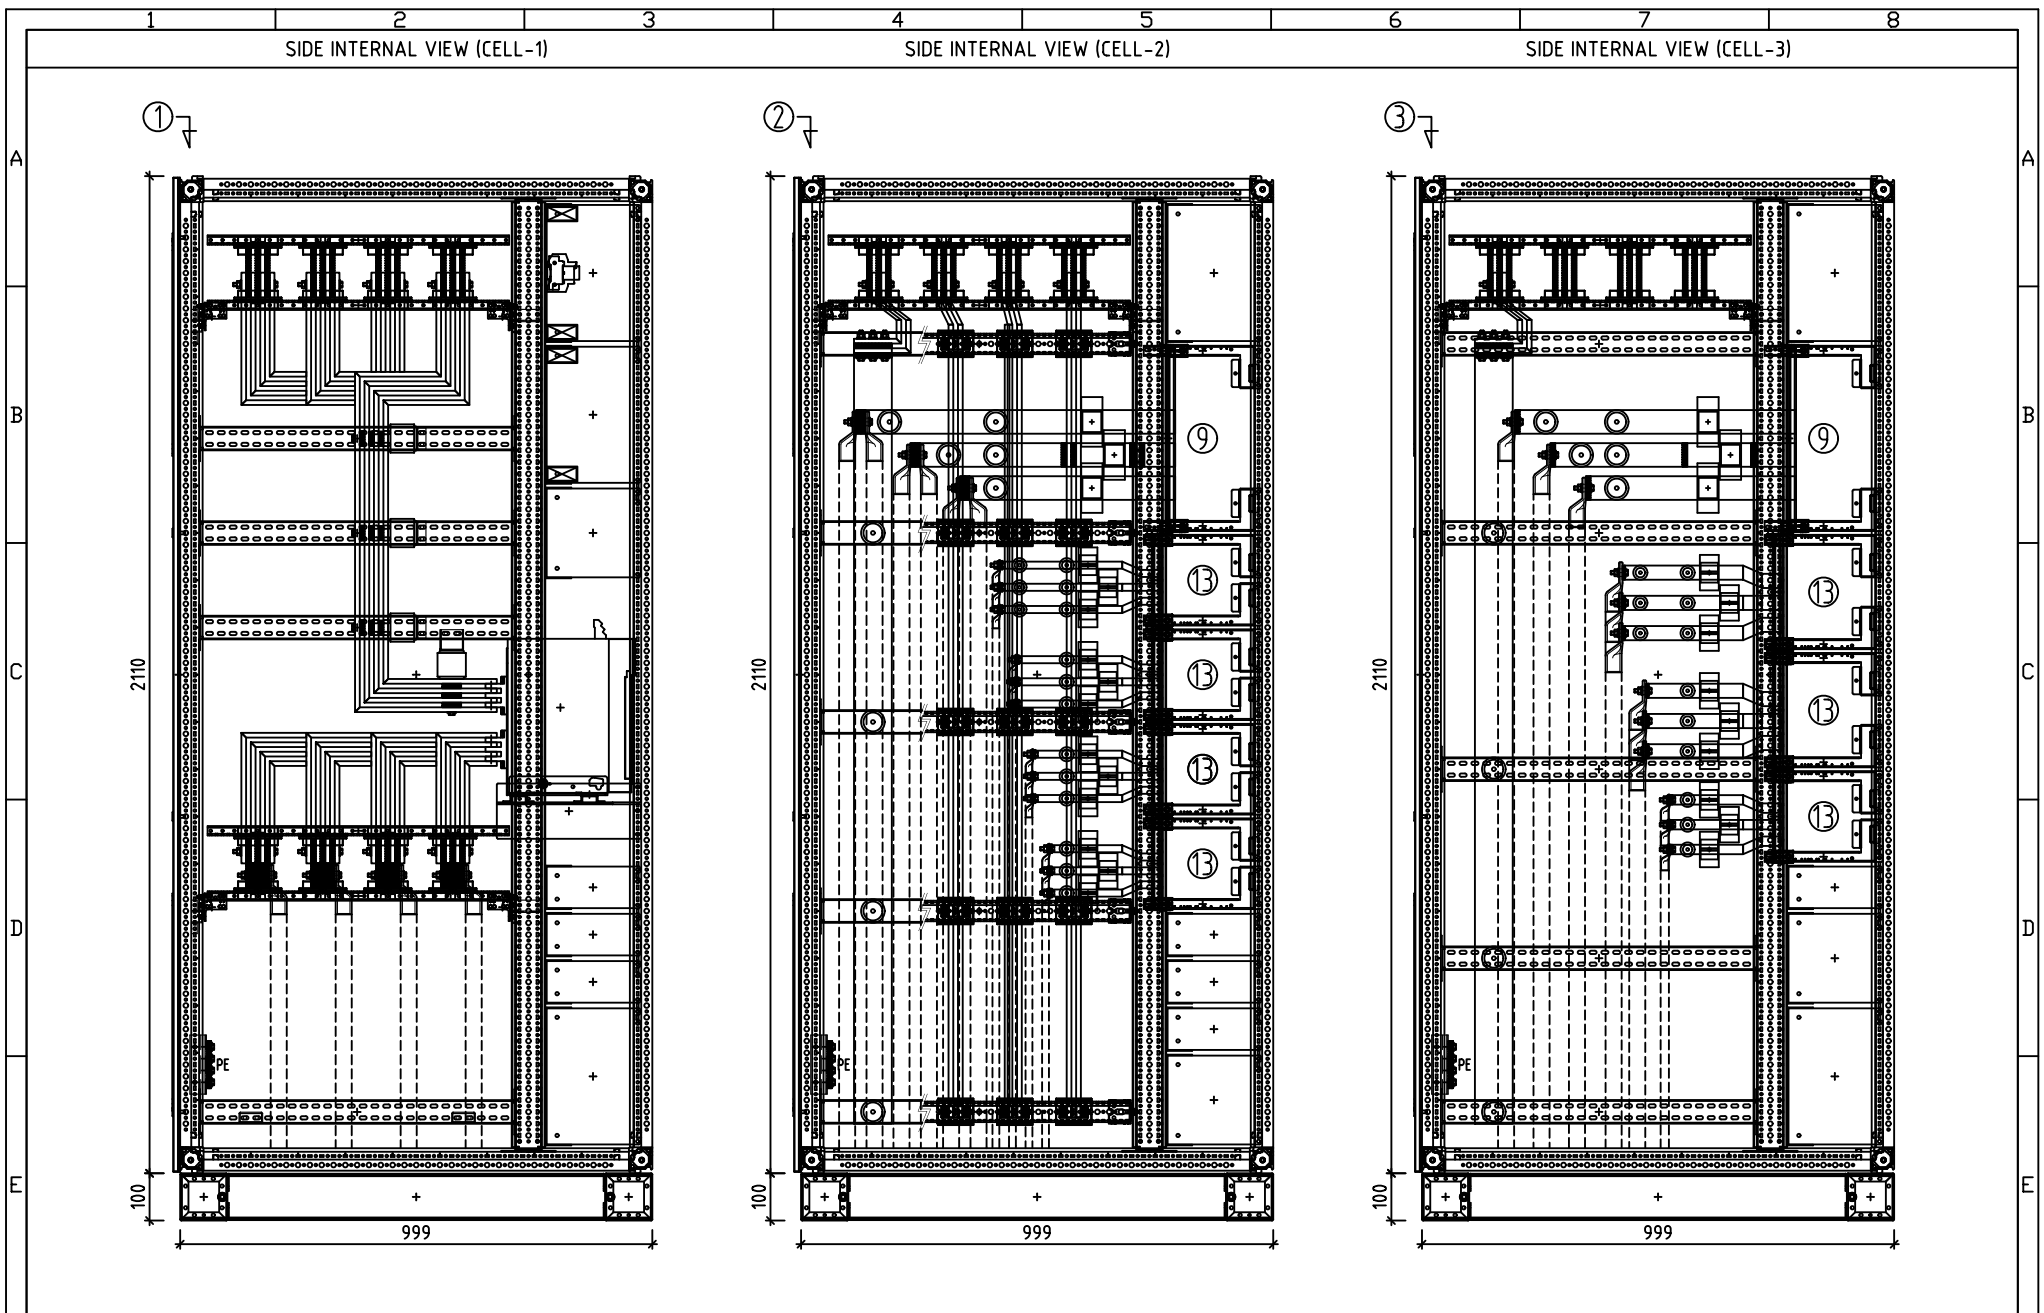


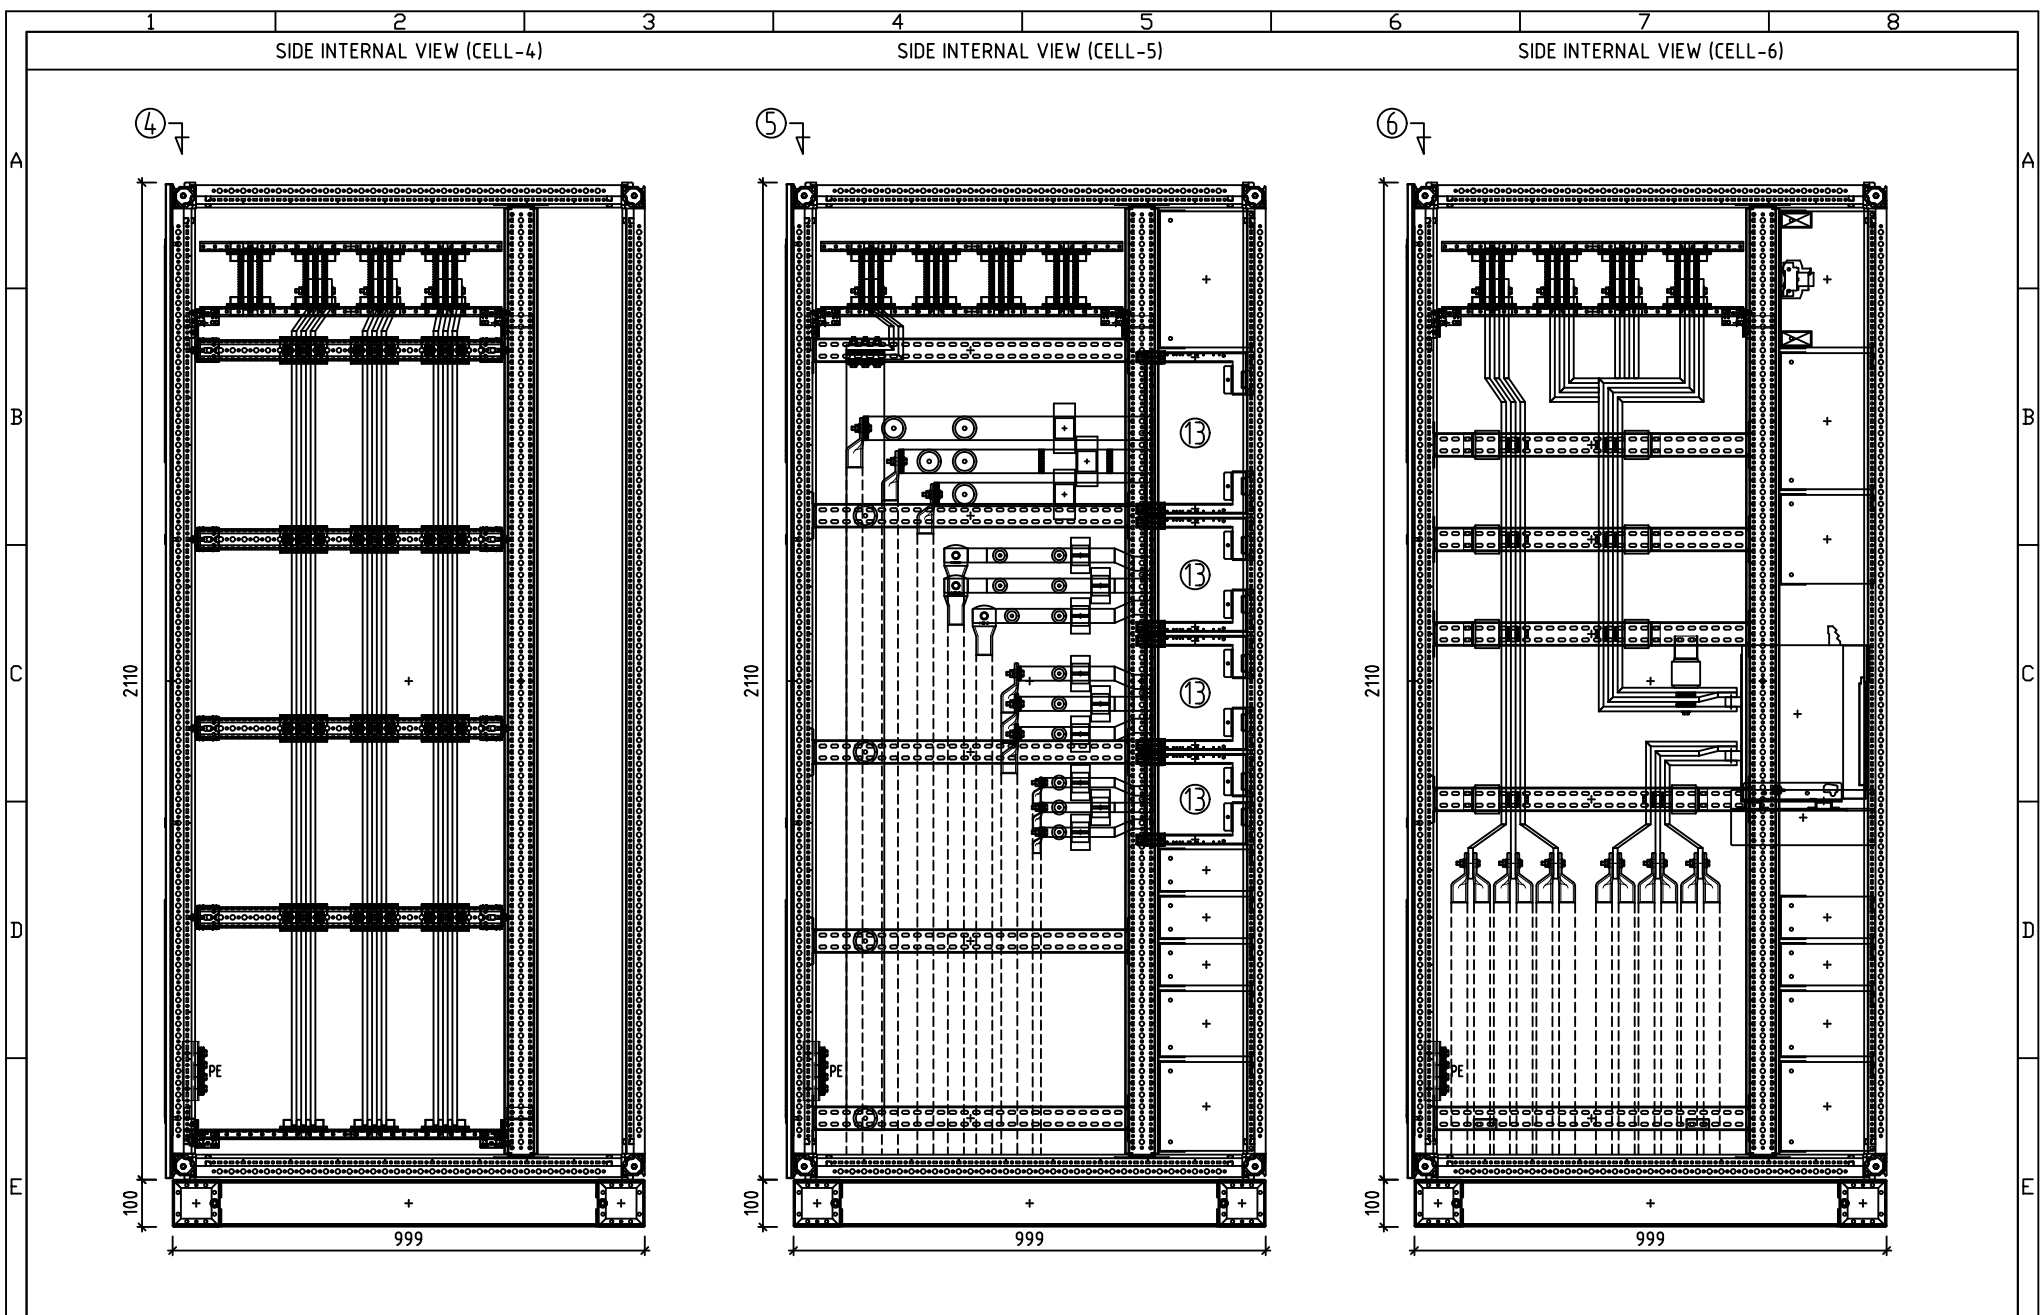

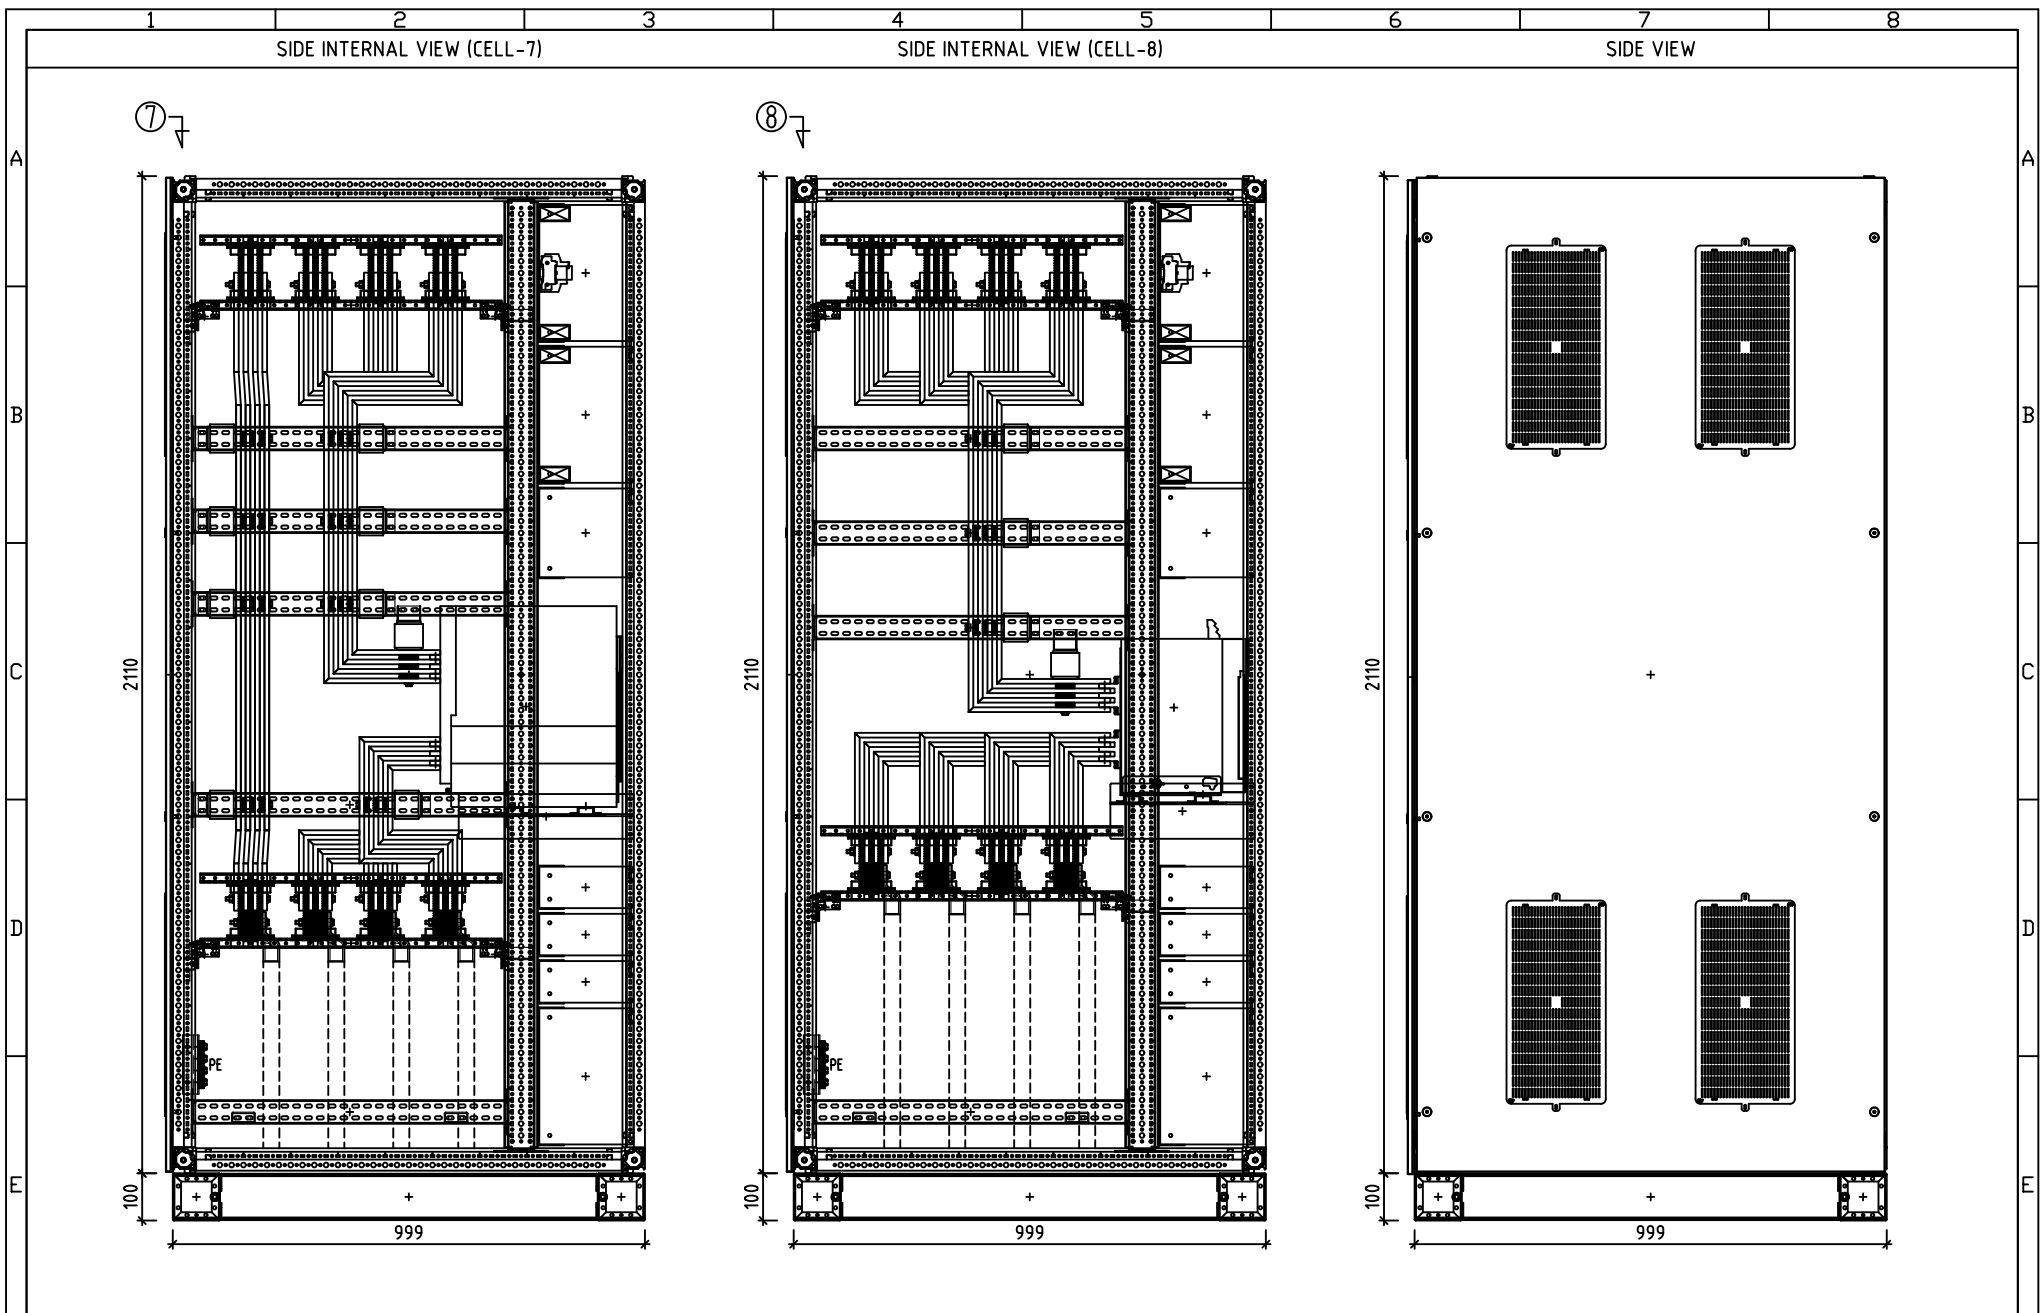


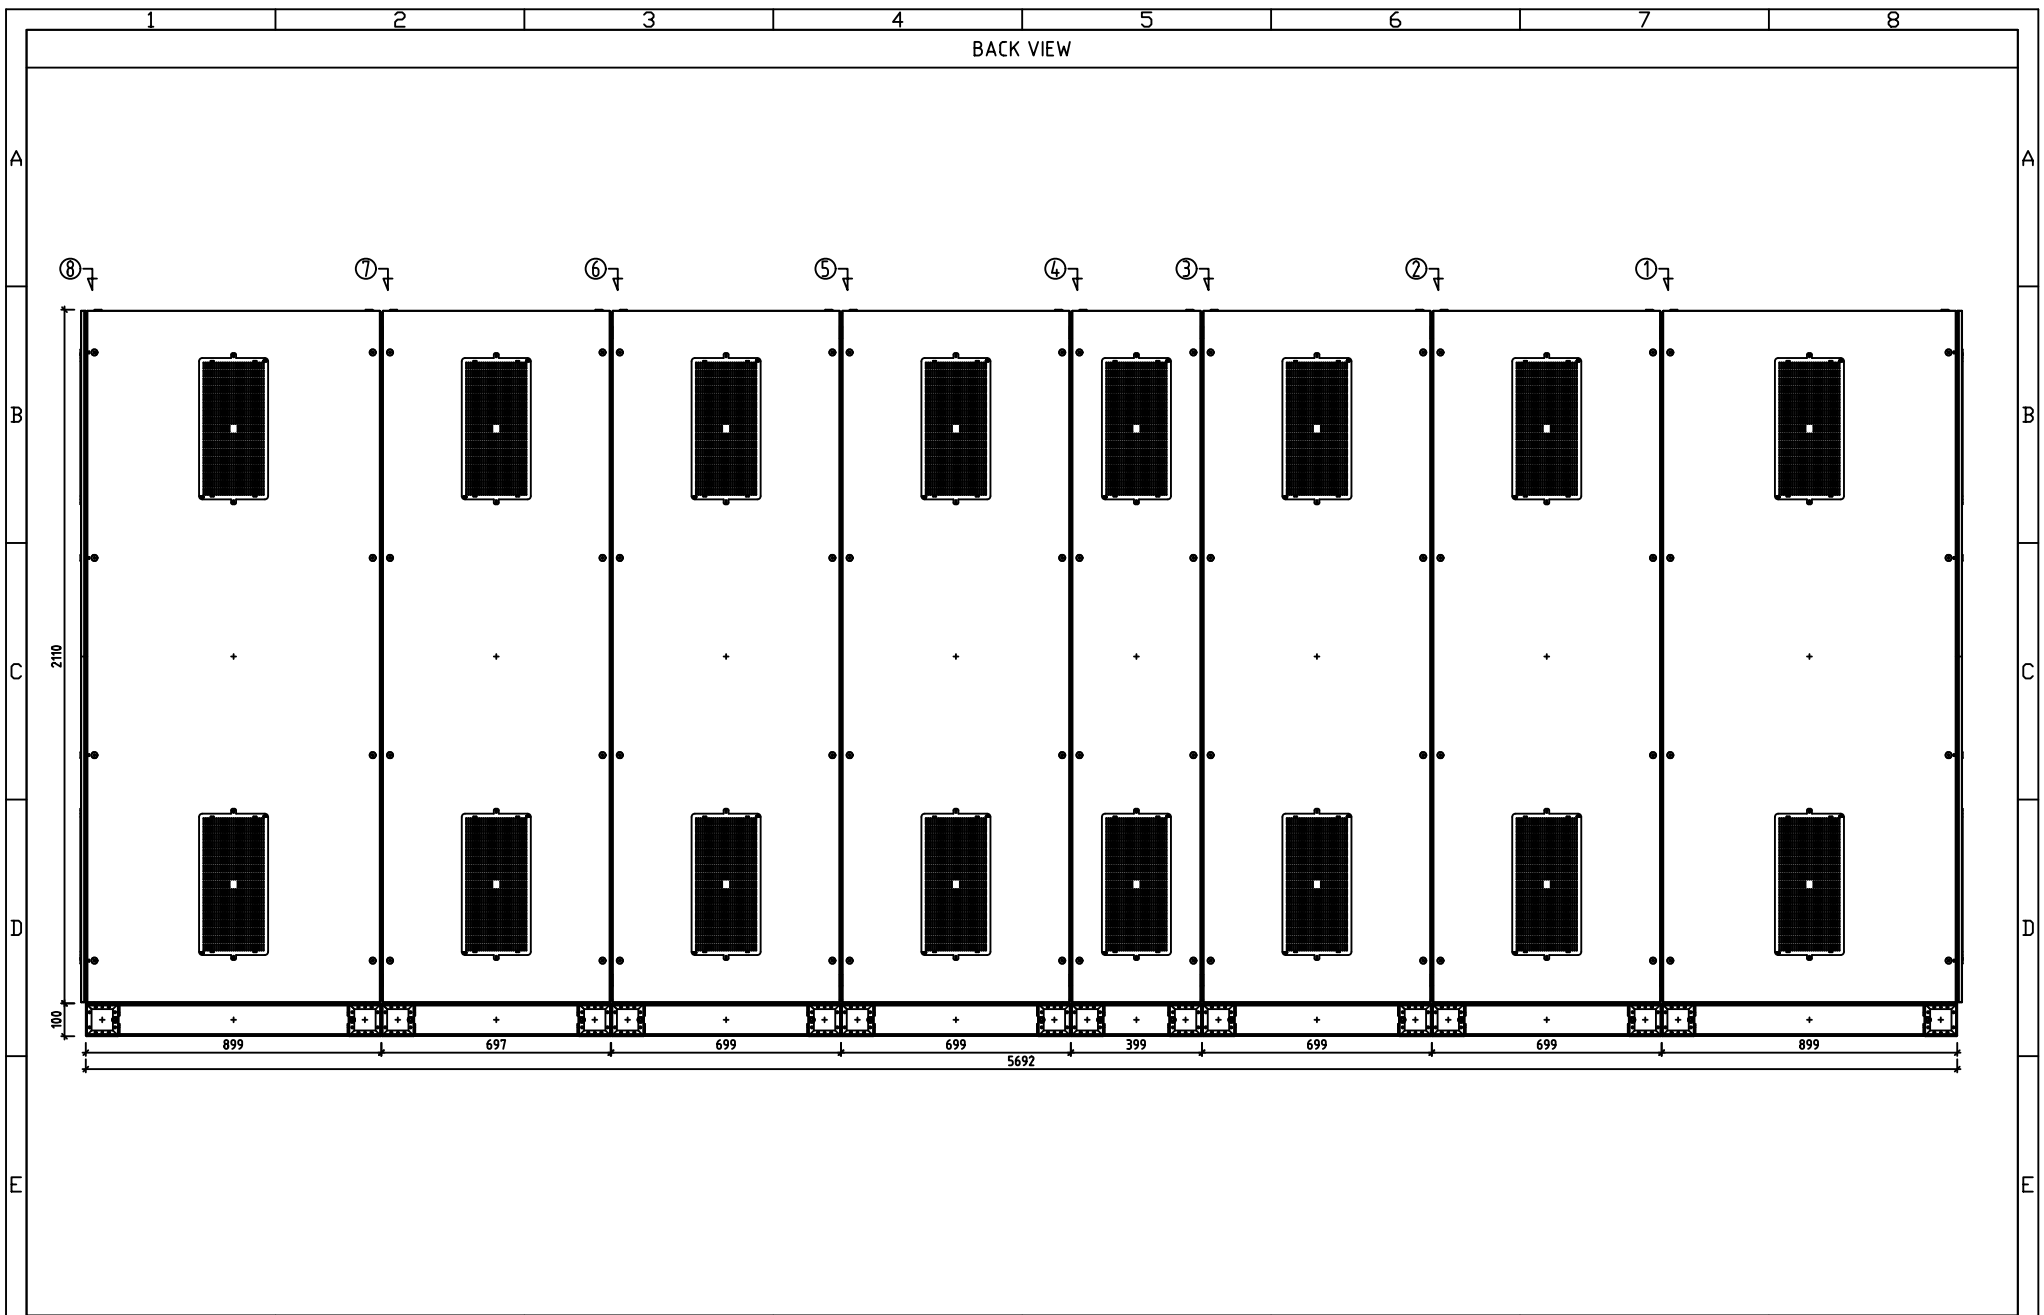



 PMElectric Best Value Electrical Solution	PROJECT : WILMAR FLOUR MILL	DRAWING TITLE : OUTLINE DRAWING LVD-33B (FLOUR MILL B)		DATE	DRAWN	SIGN	VERIFIED	SIGN	DESCRIPTION	REV	PAGE 7 15
				06-07-2020	YD		SBR		FOR APPROVAL	△	
				...-...-...	YD	14	SBR		FOR APPROVAL R1	△	
				12-08-2020	YD	26	SBR		FOR APPROVAL R2	△	
				25-08-2020	YD		SBR		FOR APPROVAL R3	△	
	CUSTOMER : PT. ABB SAKTI INDUSTRI	NO DR/JO : DR-017/IND.2020	SCALE : 1:23								
		NO DWG. : ABB-001	Dimension in mm								

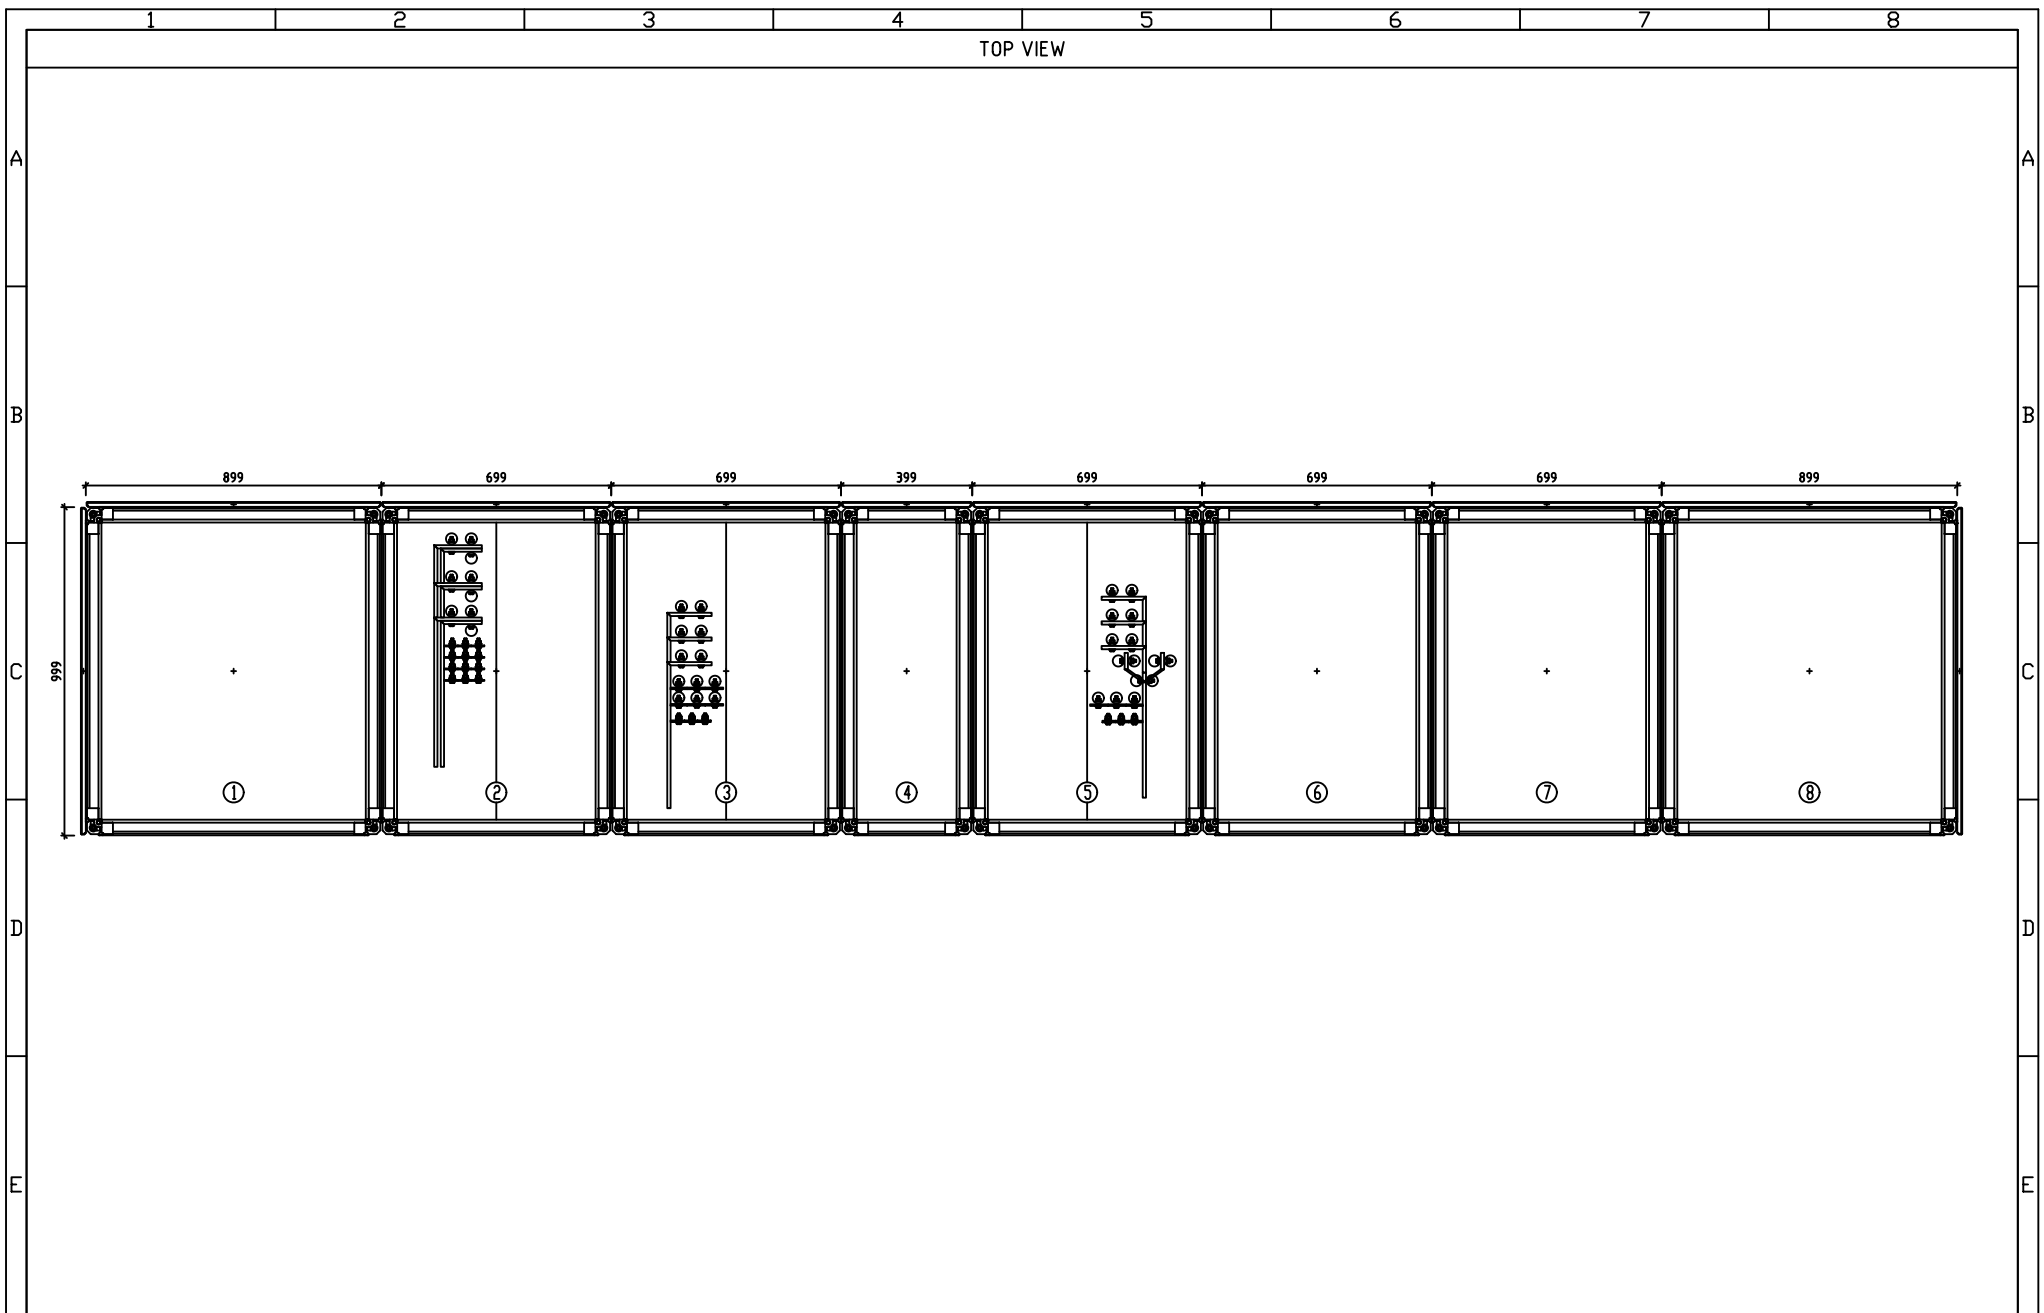


PMElectric Best Value Electrical Solution	PROJECT : WILMAR FLOUR MILL CUSTOMER : PT. ABB SAKTI INDUSTRI	DRAWING TITLE : OUTLINE DRAWING LVD-33B (FLOUR MILL B) NO DR/JO : DR-017/IND.2020 NO DWG. : ABB-001		SCALE : 1:23 Dimension in mm	DATE	DRAWN	SIGN	VERIFIED	SIGN	DESCRIPTION	REV	PAGE 8 / 15
					06-07-2020	YD		SBR		FOR APPROVAL	△	
					...	YD		SBR		FOR APPROVAL R1	△	
					12-08-2020	YD		SBR		FOR APPROVAL R2	△	
					25-08-2020	YD		SBR		FOR APPROVAL R3	△	

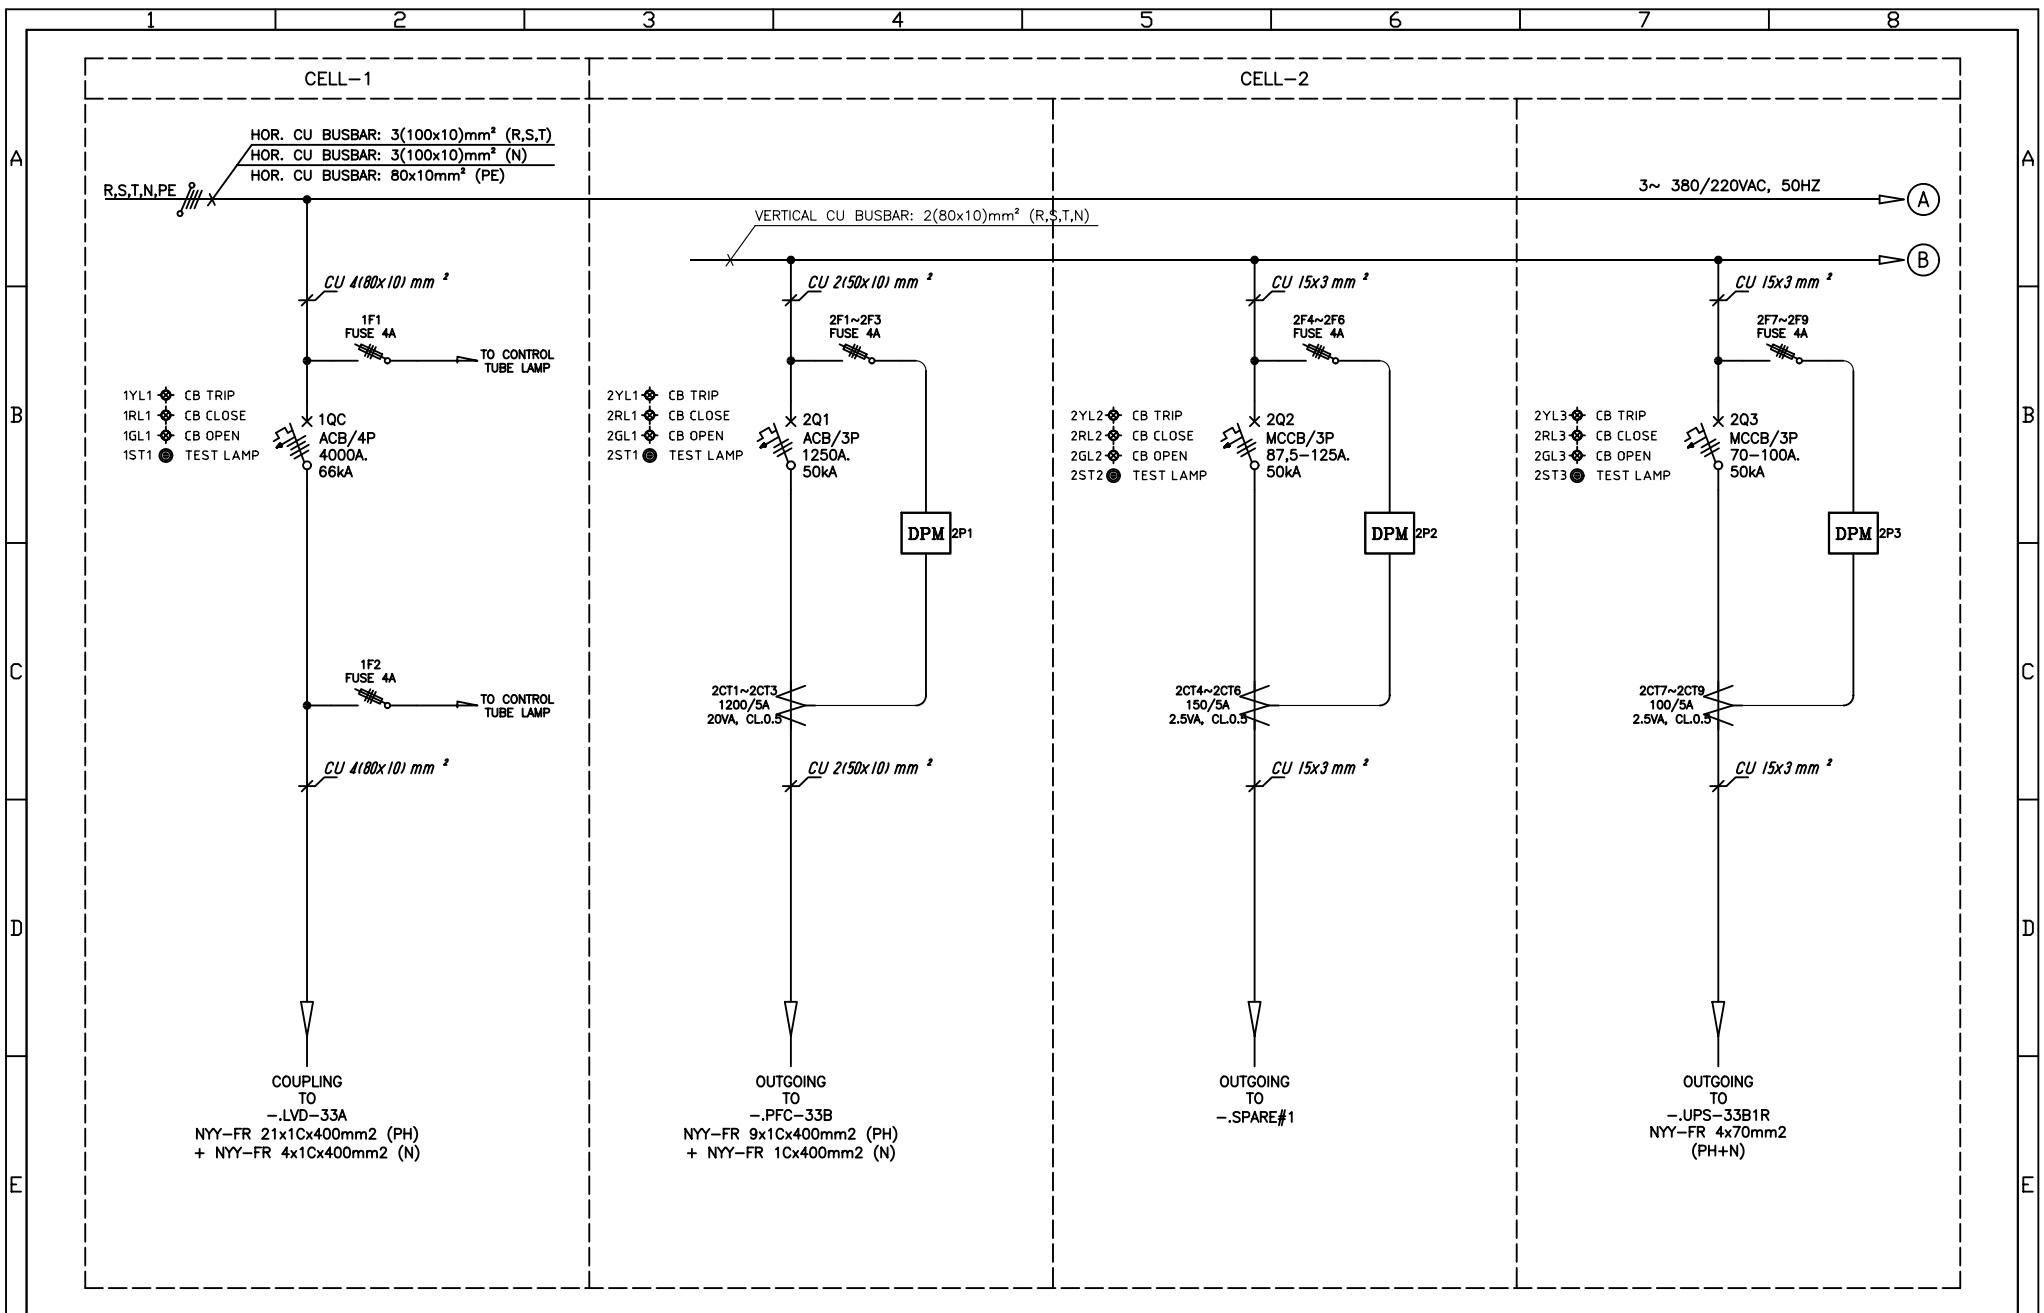

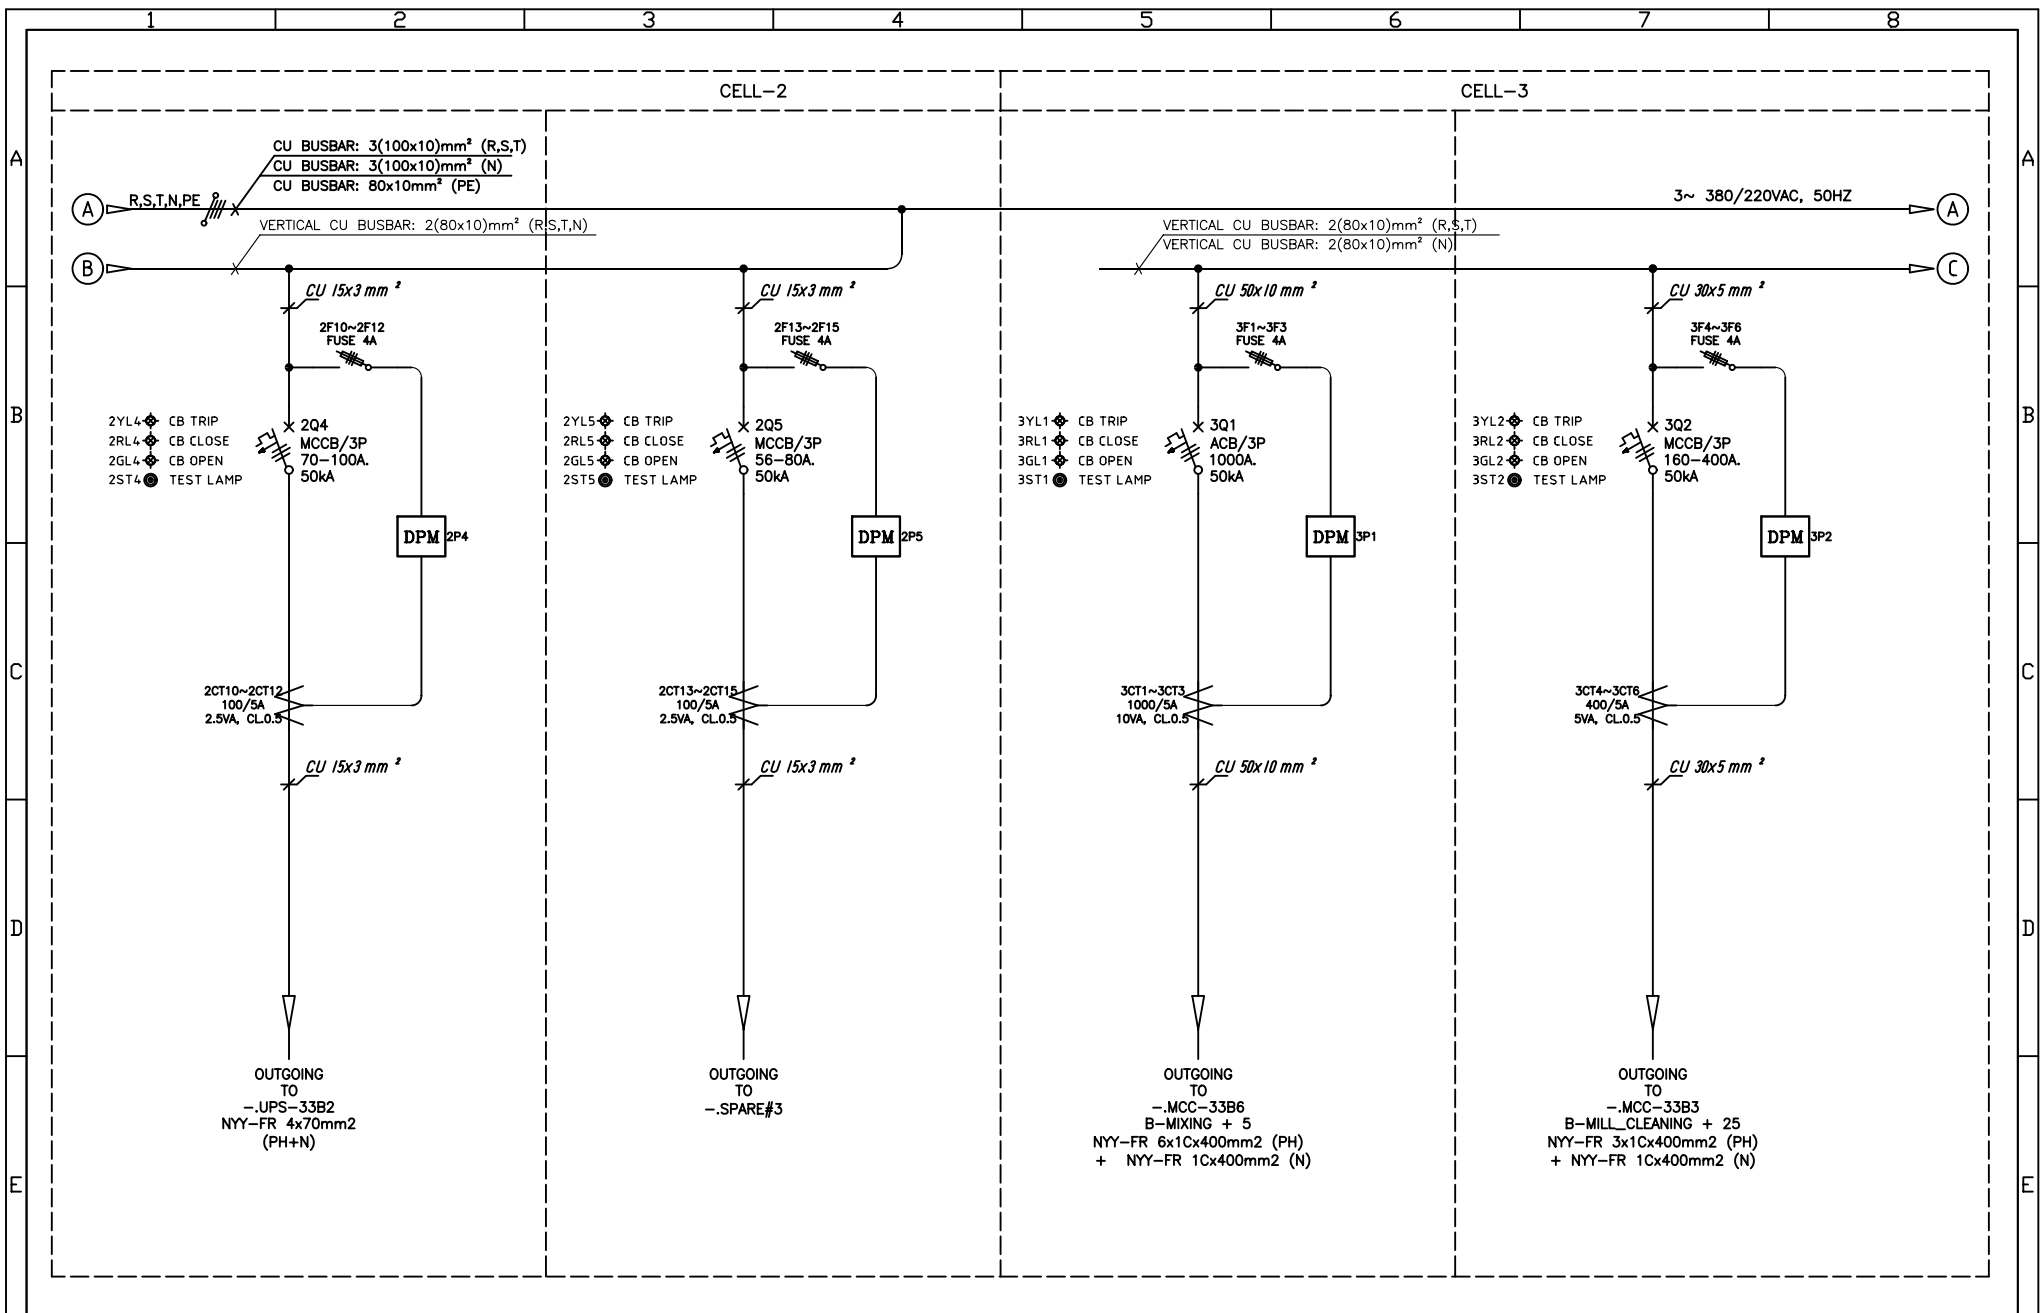


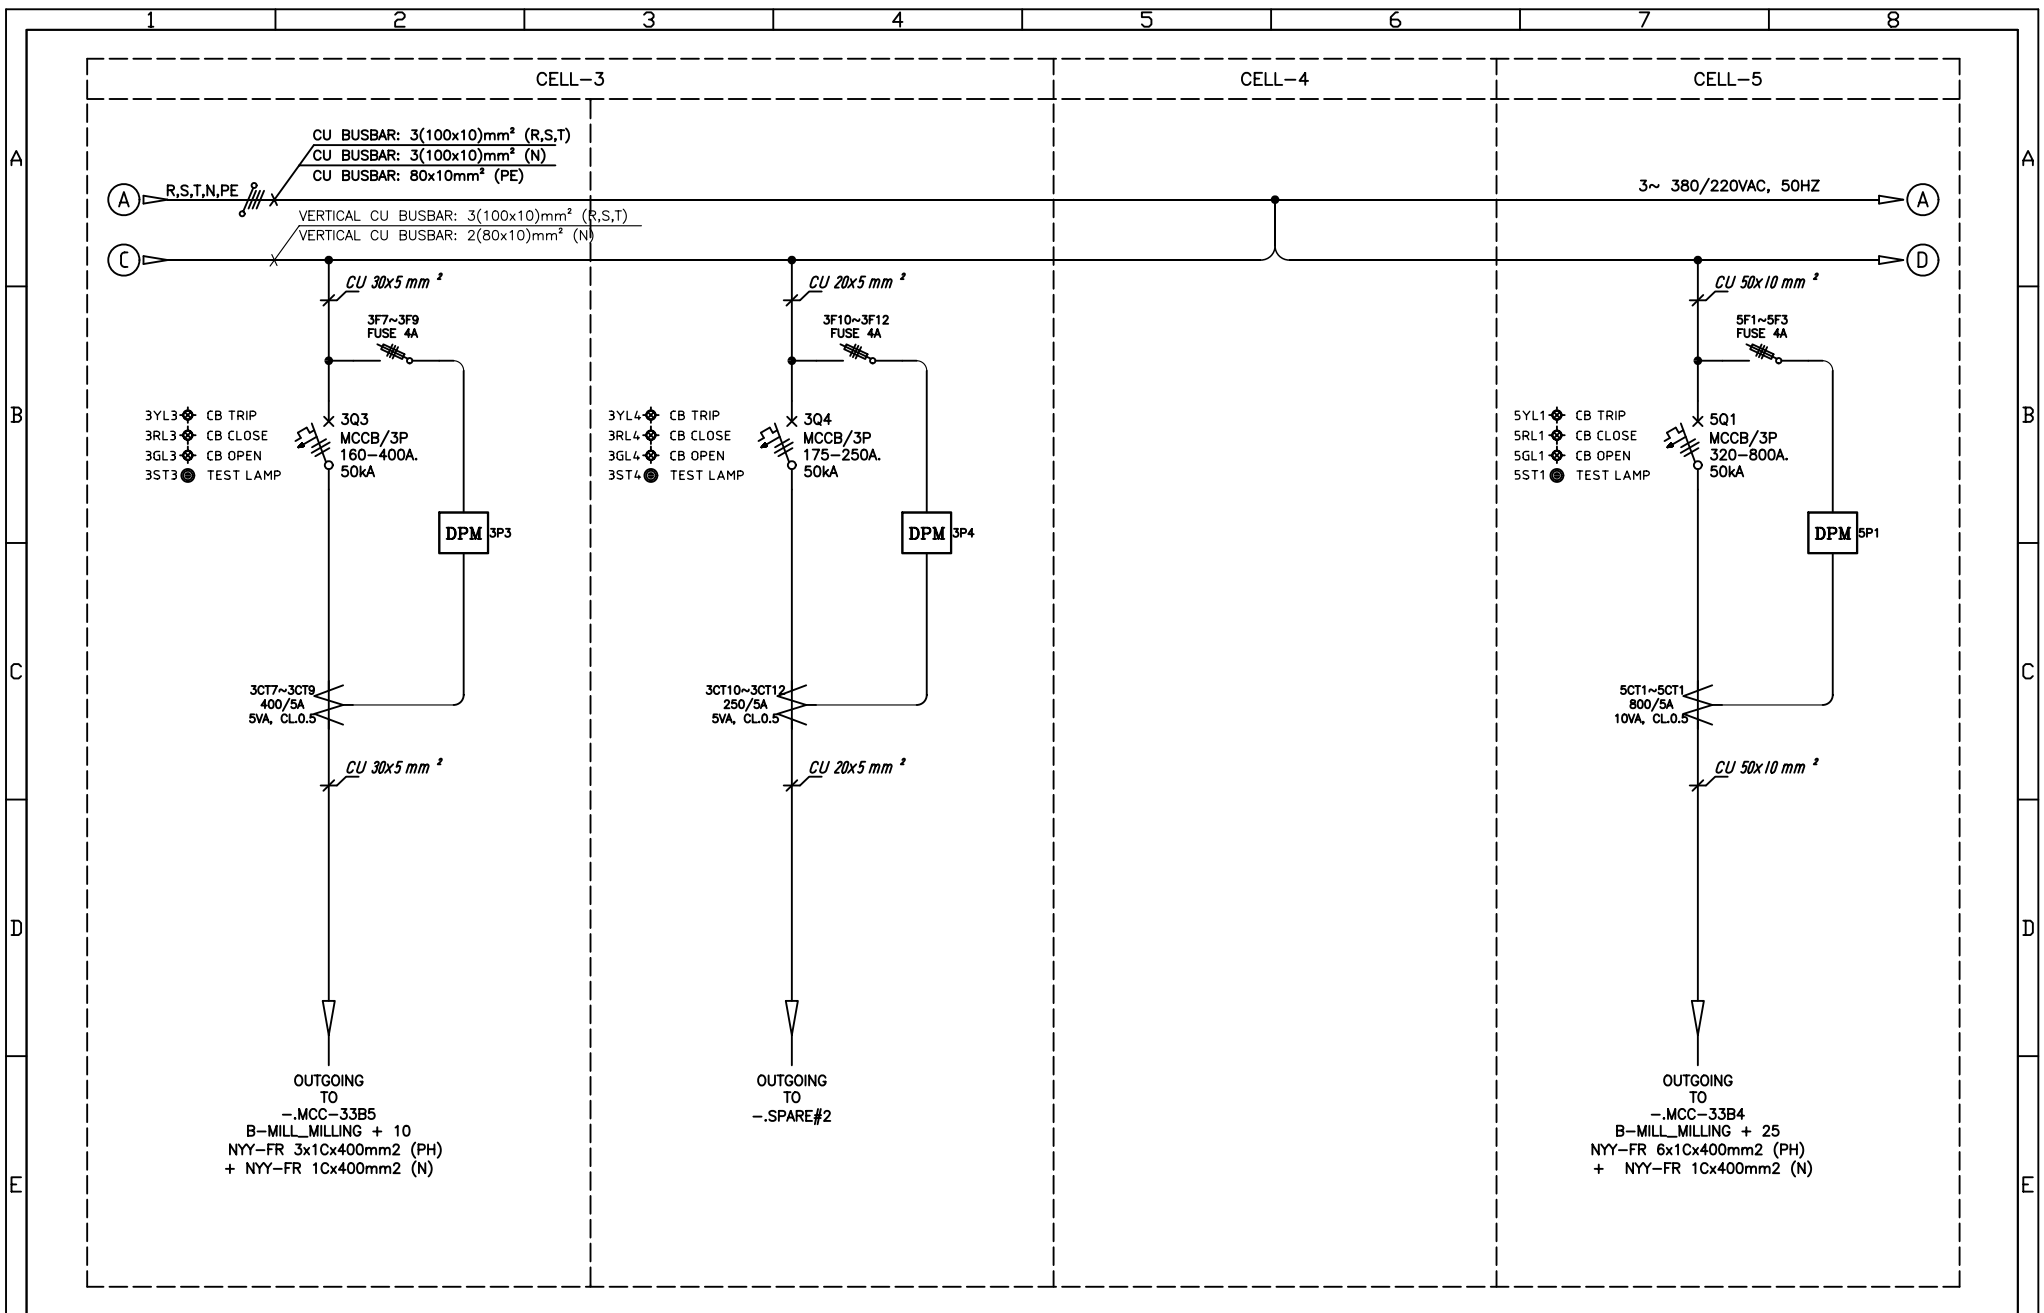

1		2		3		4		5		6		7		8					
 PMElectric Best Value Electrical Solution				PROJECT : WILMAR FLOUR MILL		DRAWING TITLE : SINGLE LINE DIAGRAM LVD-33B (FLOUR MILL B)				DATE 06-07-2020	DRAWN YD	SIGN	VERIFIED SBR	SIGN	DESCRIPTION FOR APPROVAL	REV 1	PAGE 11		
										...	YD		SBR		FOR APPROVAL R1	2			
										NO DR/JO : DR-017/IND.2020	SCALE : NTS	12-08-2020	YD		SBR			FOR APPROVAL R2	3
										NO DWG. : ABB-001	Dimension in mm	25-08-2020	YD		SBR			FOR APPROVAL R3	4
				CUSTOMER : PT. ABB SAKTI INDUSTRI													15		

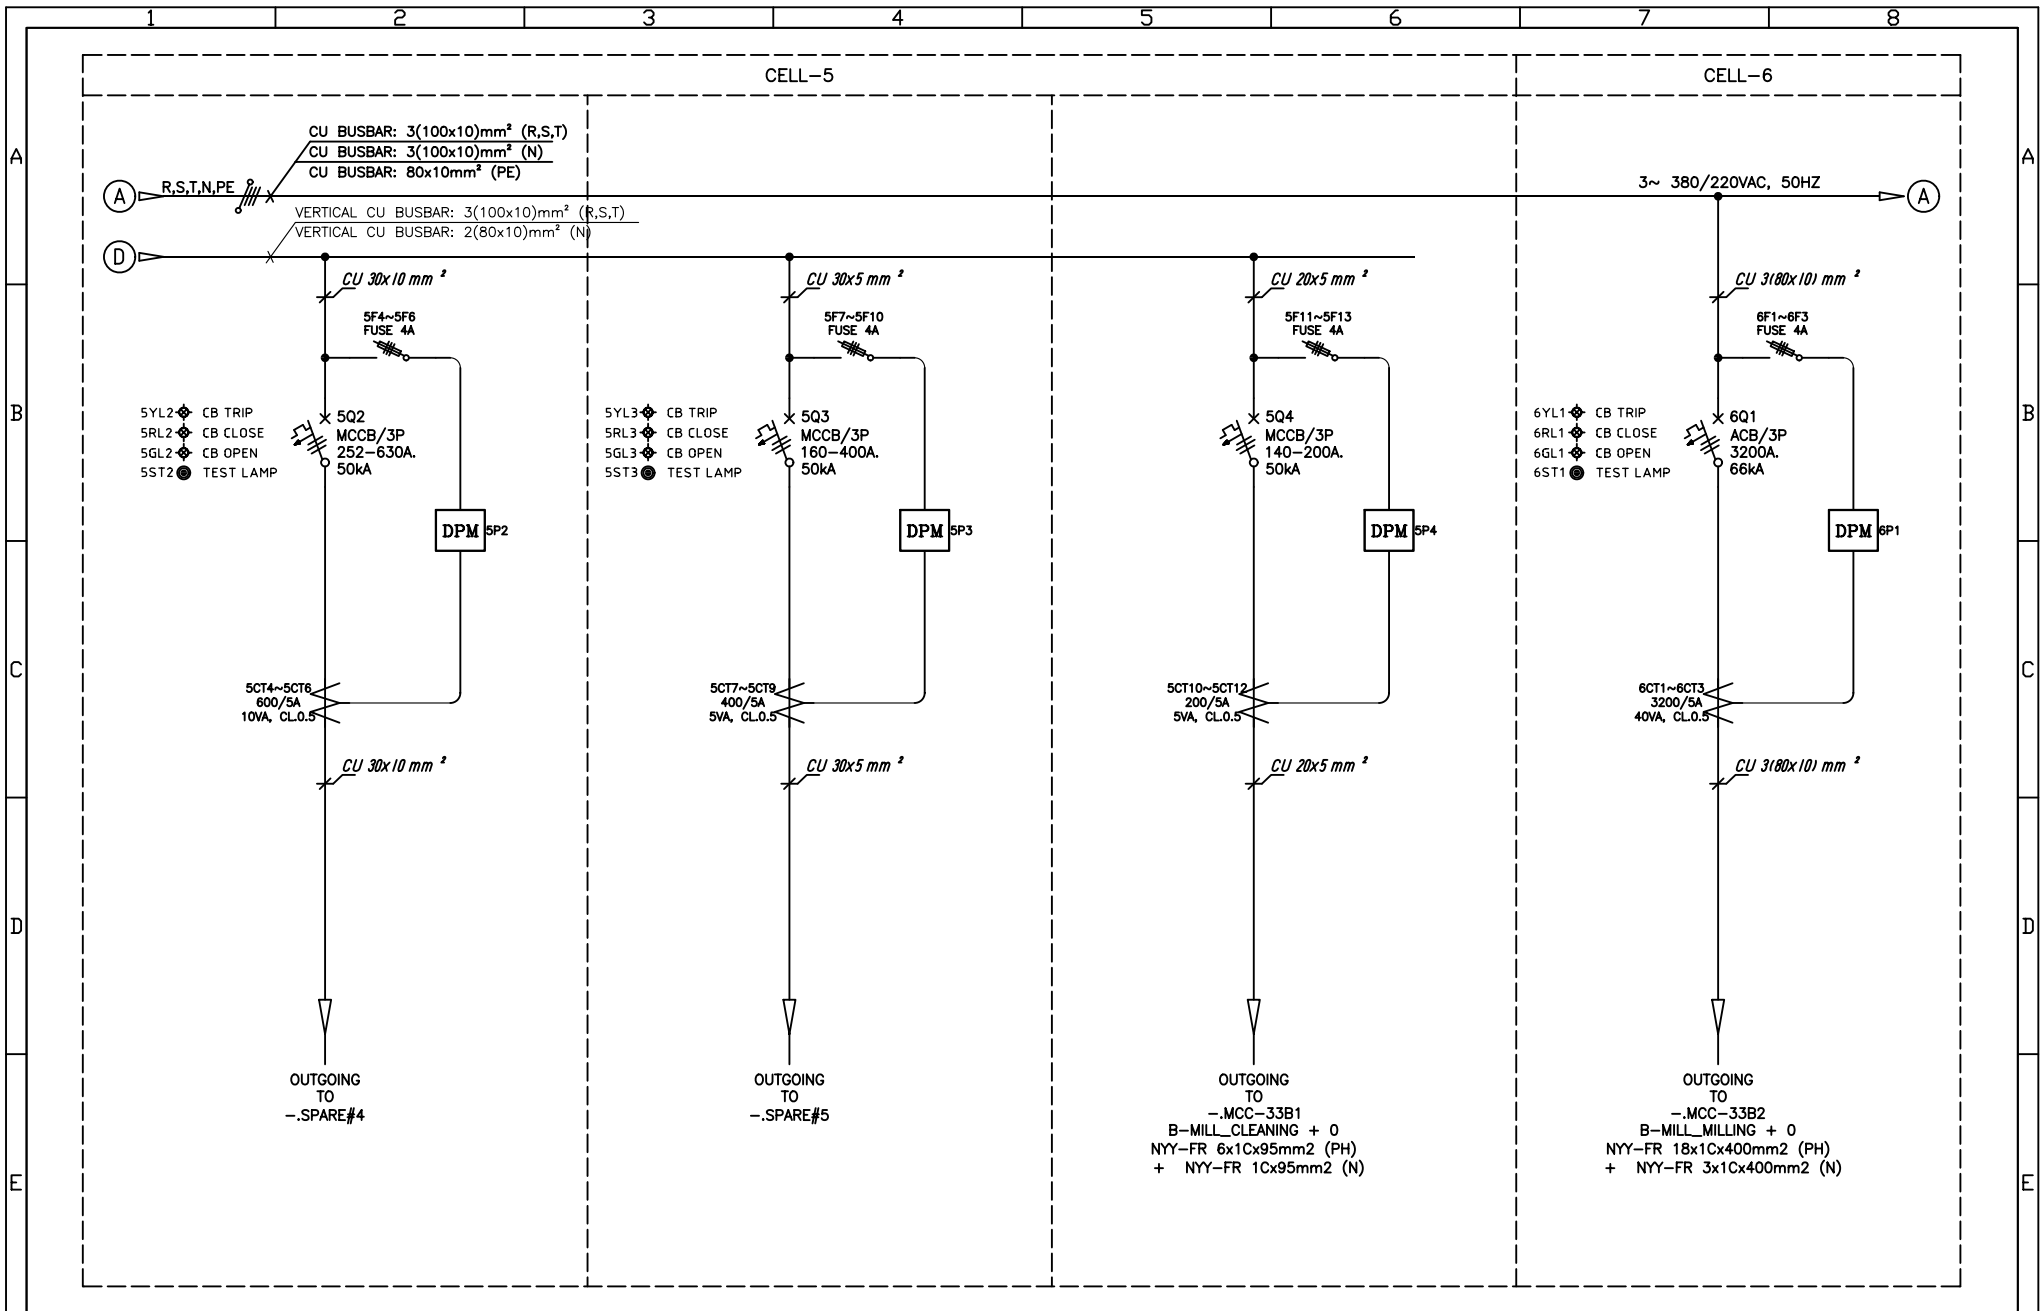

PMElectric Best Value Electrical Solution	PROJECT : WILMAR FLOUR MILL		DRAWING TITLE : SINGLE LINE DIAGRAM LVD-33B (FLOUR MILL B)		DATE	DRAWN	SIGN	VERIFIED	SIGN	DESCRIPTION	REV	PAGE
	CUSTOMER : PT. ABB SAKTI INDUSTRI		NO DR/JO : DR-017/IND.2020		06-07-2020	YD		SBR		FOR APPROVAL R1		12
			NO DWG. : ABB-001		12-08-2020	YD		SBR		FOR APPROVAL R2		15
			Dimension in mm		25-08-2020	YD		SBR		FOR APPROVAL R3		

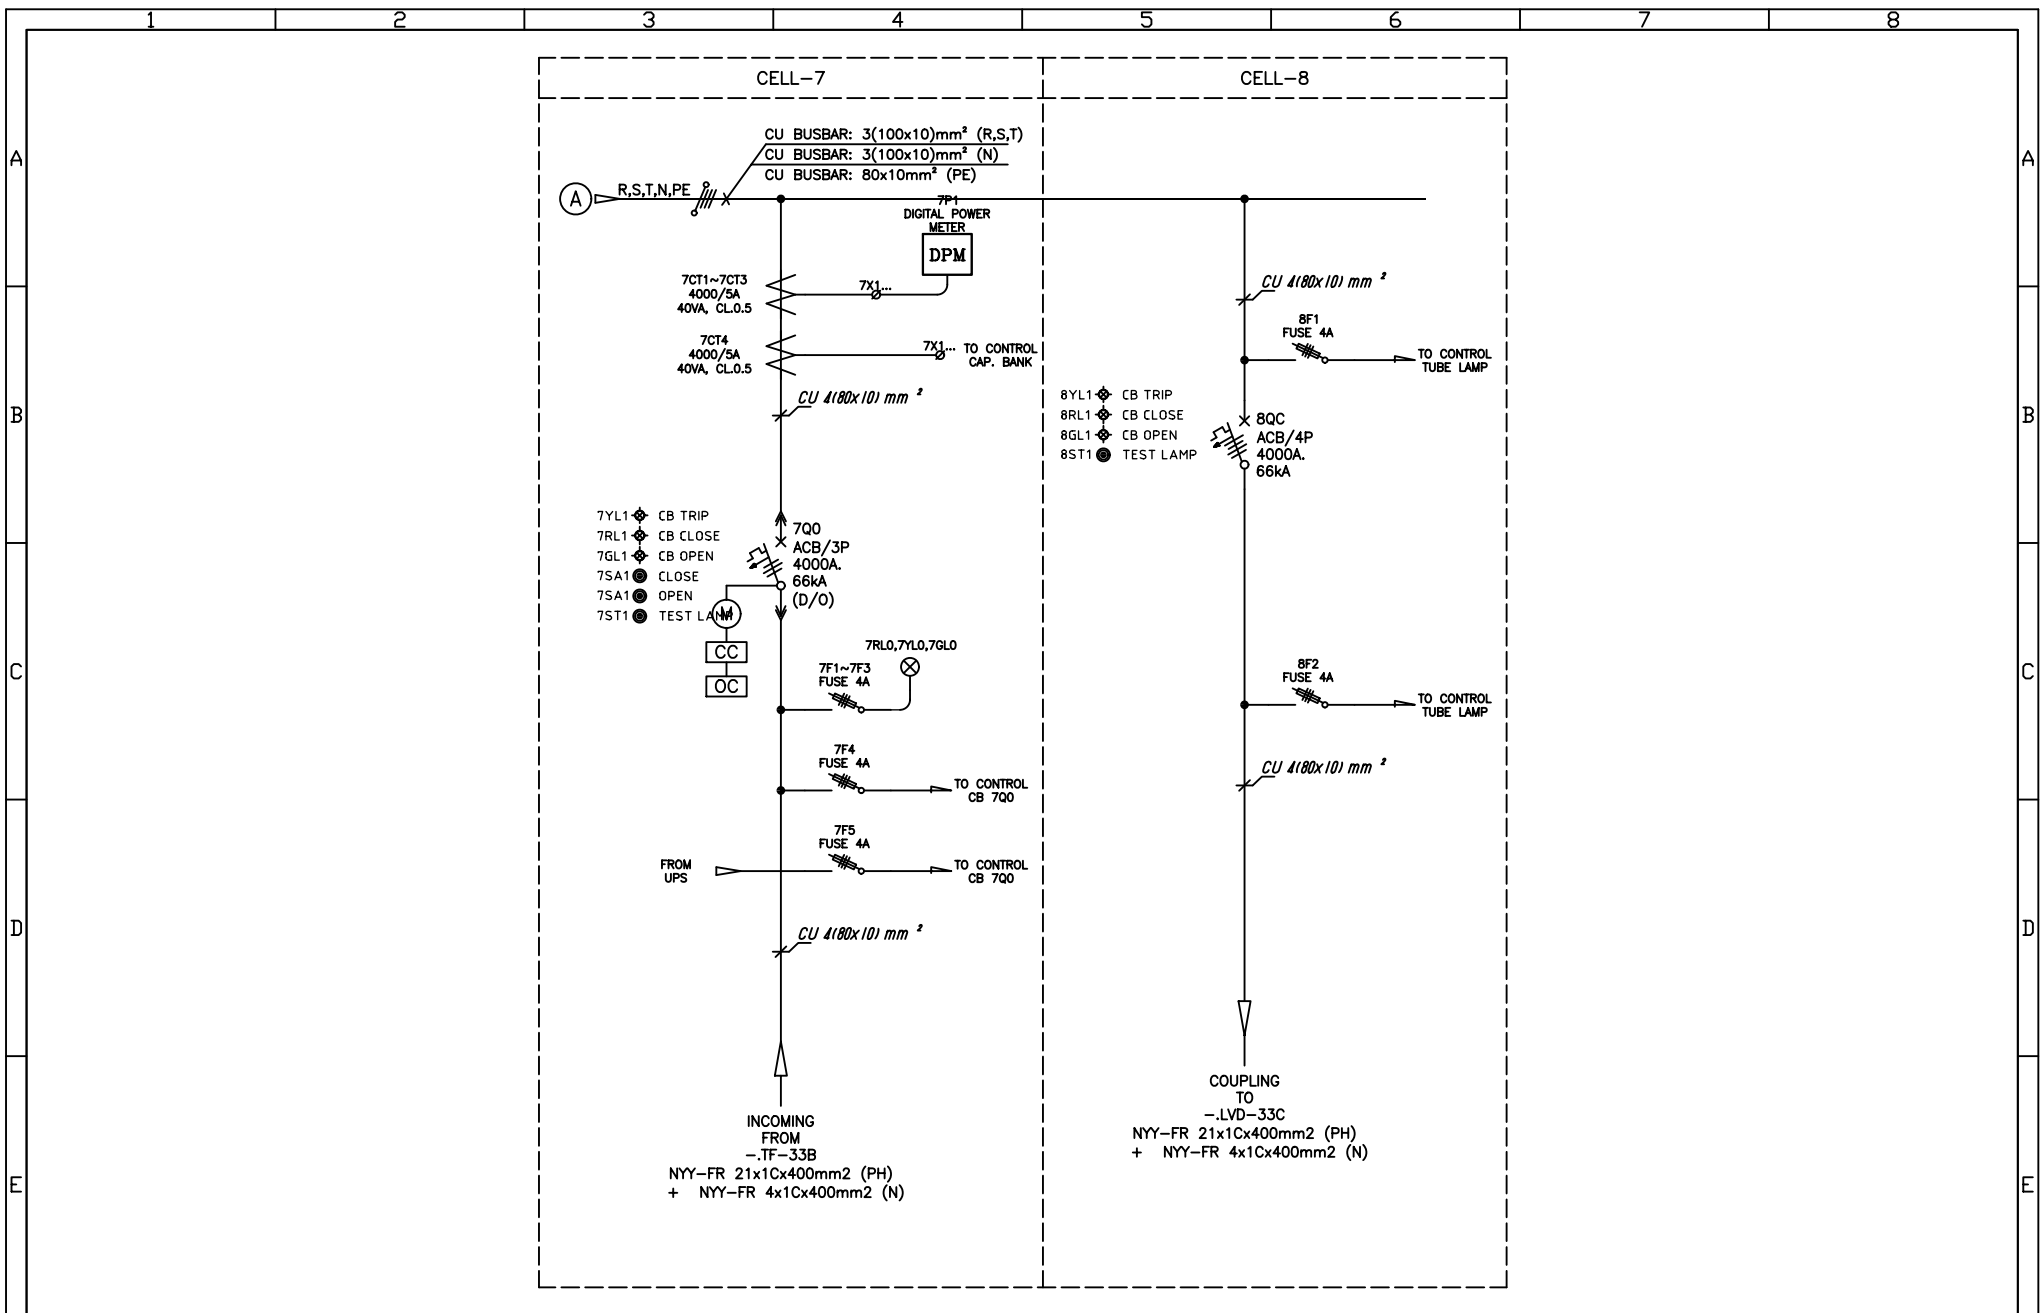

PROJECT :		DRAWING TITLE :		DATE	DRAWN	SIGN	VERIFIED	SIGN	DESCRIPTION	REV	PAGE
WILMAR FLOUR MILL		SINGLE LINE DIAGRAM LVD-33B (FLOUR MILL B)		06-07-2020	YD		SBR		FOR APPROVAL	1	13
CUSTOMER : PT. ABB SAKTI INDUSTRI		NO DR/JO : DR-017/IND.2020		12-08-2020	YD	14	SBR		FOR APPROVAL R1	2	
		NO DWG. : ABB-001		25-08-2020	YD	16	SBR		FOR APPROVAL R2	3	
		SCALE : NTS									15
		Dimension in mm									

1	2	3	4	5	6	7	8
NO	CODE	SPECIFICATION	TYPE	BRAND	QTY	UNIT	REMARK
		~ INCOMING SECTION ~					
1	7Q0	ACB 3P 4000A 66KA, D/O, E4.2N40 4000 EKIP DIP/LI	1SDA072541R1	ABB	1	PC	
2	-	EKIP TOUCH/LSIG	-	ABB	1	PC	
3	-	GEARED MOTOR 220-250V AC/DC, M-E2.2/E6.2	1SDA073725R1	ABB	1	PC	
4	-	SHUNT CLOSING RELEASE 220-240V AC/DC, YC E1.2-6.2	1SDA073687R1	ABB	1	PC	
5	-	SHUNT OPENING RELEASE 220-240V AC/DC, YO E1.2-6.2	1SDA073674R1	ABB	1	PC	
6	-	PADLOCK FOR ACB E2.2-E6.2 (TANPA GEMBOK)	1SDA073803R1	ABB	1	PC	
		~ COUPLING SECTION ~					
7	1QC,8QC	ACB 4P 4000A 66KA, F/T, E4.2N40 4000 EKIP DIP/LI	1SDA071821R1	ABB	2	PCS	
8	-	EKIP DIP/LSI	-	ABB	2	PCS	
9	-	PADLOCK FOR ACB E2.2-E6.2 (TANPA GEMBOK)	1SDA073803R1	ABB	2	PCS	
		~ OUTGOING SECTION ~					
10	6Q1	ACB 3P 3200A 66KA, F/T, E4.2N32 3200 EKIP DIP/LI	1SDA071141R1	ABB	1	PC	
11	-	EKIP DIP/LSI	1SDA070871R1	ABB	1	PC	
12	-	PADLOCK FOR ACB E2.2-E6.2 (TANPA GEMBOK)	1SDA073803R1	ABB	1	PC	
13	2Q1	ACB 3P 1250A 50KA, F/T, E1.2C12 1250 EKIP DIP/LI	1SDA070831R1	ABB	1	PC	
14	-	EKIP DIP/LSI	1SDA070871R1	ABB	1	PC	
15	-	PADLOCK FOR ACB E1.2 (TANPA GEMBOK)	1SDA073800R1	ABB	1	PC	
16	3Q1	ACB 3P 1000A 50KA, F/T, E1.2C10 1000 EKIP DIP/LI	1SDA070791R1	ABB	1	PC	
17	-	EKIP DIP/LSI	1SDA070871R1	ABB	1	PC	
18	-	PADLOCK FOR ACB E1.2 (TANPA GEMBOK)	1SDA073800R1	ABB	1	PC	
19	5Q1	MCCB 3P 320-800A 50KA, T6S PR221DS-LS/I-800	1SDA060278R1	ABB	1	PC	
20	-	RHE NORMAL TRANSMITTED HANDLE, T6, FIXED/PLUGIN	1SDA054929R1	ABB	1	PC	
21	-	AUXILIARY CONTACT, AUX-C 3Q 1SY 250V AC/DC, T4,T5,T6	1SDA054911R1	ABB	1	PC	
22	5Q2	MCCB 3P 252-630A 50KA, T5S PR221DS-LS/I-630	1SDA054404R1	ABB	1	PC	
23	-	RHE NORMAL TRANSMITTED HANDLE, T5, FIXED/PLUGIN	1SDA054929R1	ABB	1	PC	
24	-	AUXILIARY CONTACT, AUX-C 3Q 1SY 250V AC/DC, T4,T5,T6	1SDA054911R1	ABB	1	PC	
25	3Q2~3Q3,5Q3	MCCB 3P 160-400A 50KA, T5S PR221DS-LS/I-400	1SDA054333R1	ABB	3	PCS	
26	-	RHE NORMAL TRANSMITTED HANDLE, T5, FIXED/PLUGIN	1SDA054929R1	ABB	3	PCS	
27	-	AUXILIARY CONTACT, AUX-C 3Q 1SY 250V AC/DC, T4,T5,T6	1SDA054911R1	ABB	3	PCS	
28	3Q4	MCCB 3P 175-250A 50KA, XT3S TMD-250	1SDA068221R1	ABB	1	PC	
29	-	RHE NORMAL TRANSMITTED HANDLE, XT1/XT3, FIXED/PLUGIN	1SDA066479R1	ABB	1	PC	
30	-	AUXILIARY CONTACT, AUX-C 2Q 1SY 250V AC, XT1,XT2,XT3,XT4	1SDA066433R1	ABB	1	PC	
31	5Q4	MCCB 3P 140-200A 50KA, XT3S TMD-200	1SDA068220R1	ABB	1	PC	
32	-	RHE NORMAL TRANSMITTED HANDLE, XT1/XT3, FIXED/PLUGIN	1SDA066479R1	ABB	1	PC	
33	-	AUXILIARY CONTACT, AUX-C 2Q 1SY 250V AC, XT1,XT2,XT3,XT4	1SDA066433R1	ABB	1	PC	
34	2Q2	MCCB 3P 87,5-125A 50KA, XT2S TMA-125	1SDA067559R1	ABB	1	PC	
35	-	RHE NORMAL TRANSMITTED HANDLE, XT2/XT4, FIXED/PLUGIN	1SDA069055R1	ABB	1	PC	
36	-	AUXILIARY CONTACT, AUX-C 2Q 1SY 250V AC, XT1,XT2,XT3,XT4	1SDA066433R1	ABB	1	PC	
37	2Q3~2Q4	MCCB 3P 70-100A 50KA, XT2S TMA-100	1SDA067558R1	ABB	2	PCS	
38	-	RHE NORMAL TRANSMITTED HANDLE, XT2/XT4, FIXED/PLUGIN	1SDA069055R1	ABB	2	PCS	
39	-	AUXILIARY CONTACT, AUX-C 2Q 1SY 250V AC, XT1,XT2,XT3,XT4	1SDA066433R1	ABB	2	PCS	
40	-	-	-	-	-	-	

1		2		3		4		5		6		7		8						
 PMElectric Best Value Electrical Solution				PROJECT :		WILMAR FLOUR MILL		DRAWING TITLE :		PART LIST COMPONENT LVD-33B (FLOUR MILL B)		DATE	DRAWN	SIGN	VERIFIED	SIGN	DESCRIPTION	REV	PAGE	
				CUSTOMER :		PT. ABB SAKTI INDUSTRI		NO DR/JO : DR-017/IND.2020 NO DWG. : ABB-001		SCALE : NTS Dimension in mm		06-07-2020		YD		SBR		FOR APPROVAL	1	14 15
												...-...-...		YD		SBR		FOR APPROVAL R1	1	
												12-08-2020		YD		SBR		FOR APPROVAL R2	1	
												25-08-2020		YD		SBR		FOR APPROVAL R3	1	

1	2	3	4	5	6	7	8
NO	CODE	SPECIFICATION	TYPE	BRAND	QTY	UNIT	REMARK
41	2Q5	MCCB 3P 56-80A 50KA, XT2S TMA-80	1SDA067557R1	ABB	1	PC	
42	-	RHE NORMAL TRANSMITTED HANDLE, XT2/XT4, FIXED/PLUGIN	1SDA069055R1	ABB	1	PC	
43	-	AUXILIARY CONTACT, AUX-C 2Q 1SY 250V AC, XT1,XT2,XT3,XT4	1SDA066433R1	ABB	1	PC	
		- CONTROL, METERING & PROTECTION SECTION -					
44	1F1~1F...	FUSE CARTRIDGE 4A + FUSE CARRIER	RT18-32	PM	49	PCS	
45	1RL0~1RL...	PILOT LAMP 220VAC, LED, Ø22.5mm, RED	AD22-221DS	AXLE/EQ	17	PCS	
46	1YL0~1YL...	PILOT LAMP 220VAC, LED, Ø22.5mm, YELLOW	AD22-221DS	AXLE/EQ	17	PCS	
47	1GL0~1GL...	PILOT LAMP 220VAC, LED, Ø22.5mm, GREEN	AD22-221DS	AXLE/EQ	17	PCS	
48	1SA1~1SA...	PUSH BUTTON, 1 C/O, Ø22.5mm, GREEN	AXP-B235	AXLE/EQ	1	PCS	
49	1SB1~1SB...	PUSH BUTTON, 1 C/O, Ø22.5mm, RED	AXP-B245	AXLE/EQ	1	PCS	
50	1ST1~1ST...	PUSH BUTTON FLUSH, 1 N/O, Ø22mm, BLACK	YW1B-M1E10B	IDEC/EQ	16	PCS	
51	1P1~1P...	DIGITAL POWER METER,MODBUS ETHERNET TCP/IP, M4M20ETHERNET	2CSG204471R4051	ABB	15	PCS	
52	1CT1~1CT...	CURRENT TRANSFORMER 100/5A, 2.5VA, CLASS 0.5, 31.5x11mm	HG30-100	HOWIG/EQ	9	PCS	
53	1CT1~1CT...	CURRENT TRANSFORMER 150/5A, 2.5VA, CLASS 0.5, 31.5x11mm	HG30-150	HOWIG/EQ	3	PCS	
54	1CT1~1CT...	CURRENT TRANSFORMER 200/5A, 5VA, CLASS 0.5, 31.5x11mm	HG30-200	HOWIG/EQ	3	PCS	
55	1CT1~1CT...	CURRENT TRANSFORMER 250/5A, 5VA, CLASS 0.5, 31.5x11mm	HG30-250	HOWIG/EQ	3	PCS	
56	1CT1~1CT...	CURRENT TRANSFORMER 400/5A, 5VA, CLASS 0.5, 42x11mm	HG40-400	HOWIG/EQ	9	PCS	
57	1CT1~1CT...	CURRENT TRANSFORMER 600/5A, 10VA, CLASS 0.5, 51x16mm	HG50-600	HOWIG/EQ	3	PCS	
58	1CT1~1CT...	CURRENT TRANSFORMER 800/5A, 10VA, CLASS 0.5, 82x32.5mm	HG82-800	HOWIG/EQ	3	PCS	
59	1CT1~1CT...	CURRENT TRANSFORMER 1000/5A, 10VA, CLASS 0.5, 82x32.5mm	HG82-1000	HOWIG/EQ	3	PCS	
60	1CT1~1CT...	CURRENT TRANSFORMER 1200/5A, 20VA, CLASS 0.5, 82x32.5mm	HG82-1200	HOWIG/EQ	3	PCS	
61	1CT1~1CT...	CURRENT TRANSFORMER 3200/5A, 40VA, CLASS 0.5, 126x36mm	HG120-3200	HOWIG/EQ	3	PCS	
62	1CT1~1CT...	CURRENT TRANSFORMER 4000/5A, 40VA, CLASS 0.5, 151x133mm	HG150-4000	HOWIG/EQ	4	PCS	
63	1R1~1R...	RELAY 4-CO 10A 220VAC + SOCKET	LY4 + PTF14A-E	OMRON	20	PCS	
64	1X1~1X...	TERMINAL BLOCK, 4mm, 32A, ZS4	1SNK505010R0000	ENTRELEC	300	PCS	
65	-	END SECTION FOR ZS4~ZS25, ES4	1SNK505910R0000	ENTRELEC	20	PCS	
66	-	END STOPER, BM3	1SNK900001R0000	ENTRELEC	40	PCS	
67	DS	LIMIT SWITCH SINGLE POLE 1-CO	-	IMPORT	4	PCS	
68	TUBE LAMP	TUBULAR LAMP LED 4W, 220VAC	31099	PHILIPS	4	PCS	
69	-	WIRING & ACCESORIES	PM	LOCAL	1	LOT	
70	-	CU BUSBAR	PREMIUM	EX-IMPORT	1	LOT	
71	-	BOX PANEL UK: 2200(H) X 400(W) X 1000(D)mm ²	PRO E	ABB	1	UNIT	
72	-	BOX PANEL UK: 2200(H) X 700(W) X 1000(D)mm ²	PRO E	ABB	5	UNIT	
73	-	BOX PANEL UK: 2200(H) X 900(W) X 1000(D)mm ²	PRO E	ABB	2	UNIT	
74							
75							
76							
77							
78							
79							
80							
81							
82							

1		2		3		4		5		6		7		8						
 PMElectric Best Value Electrical Solution				PROJECT :		WILMAR FLOUR MILL		DRAWING TITLE :		PART LIST COMPONENT LVD-33B (FLOUR MILL B)		DATE	DRAWN	SIGN	VERIFIED	SIGN	DESCRIPTION	REV	PAGE	
				CUSTOMER :		PT. ABB SAKTI INDUSTRI		NO DR/JO : DR-017/IND.2020 NO DWG. : ABB-001		SCALE : NTS Dimension in mm		06-07-2020	YD		SBR		FOR APPROVAL	△	15	15
												...	YD	14	SBR		FOR APPROVAL R1	△		
												12-08-2020	YD	16	SBR		FOR APPROVAL R2	△		
												25-08-2020	YD		SBR		FOR APPROVAL R3	△		