




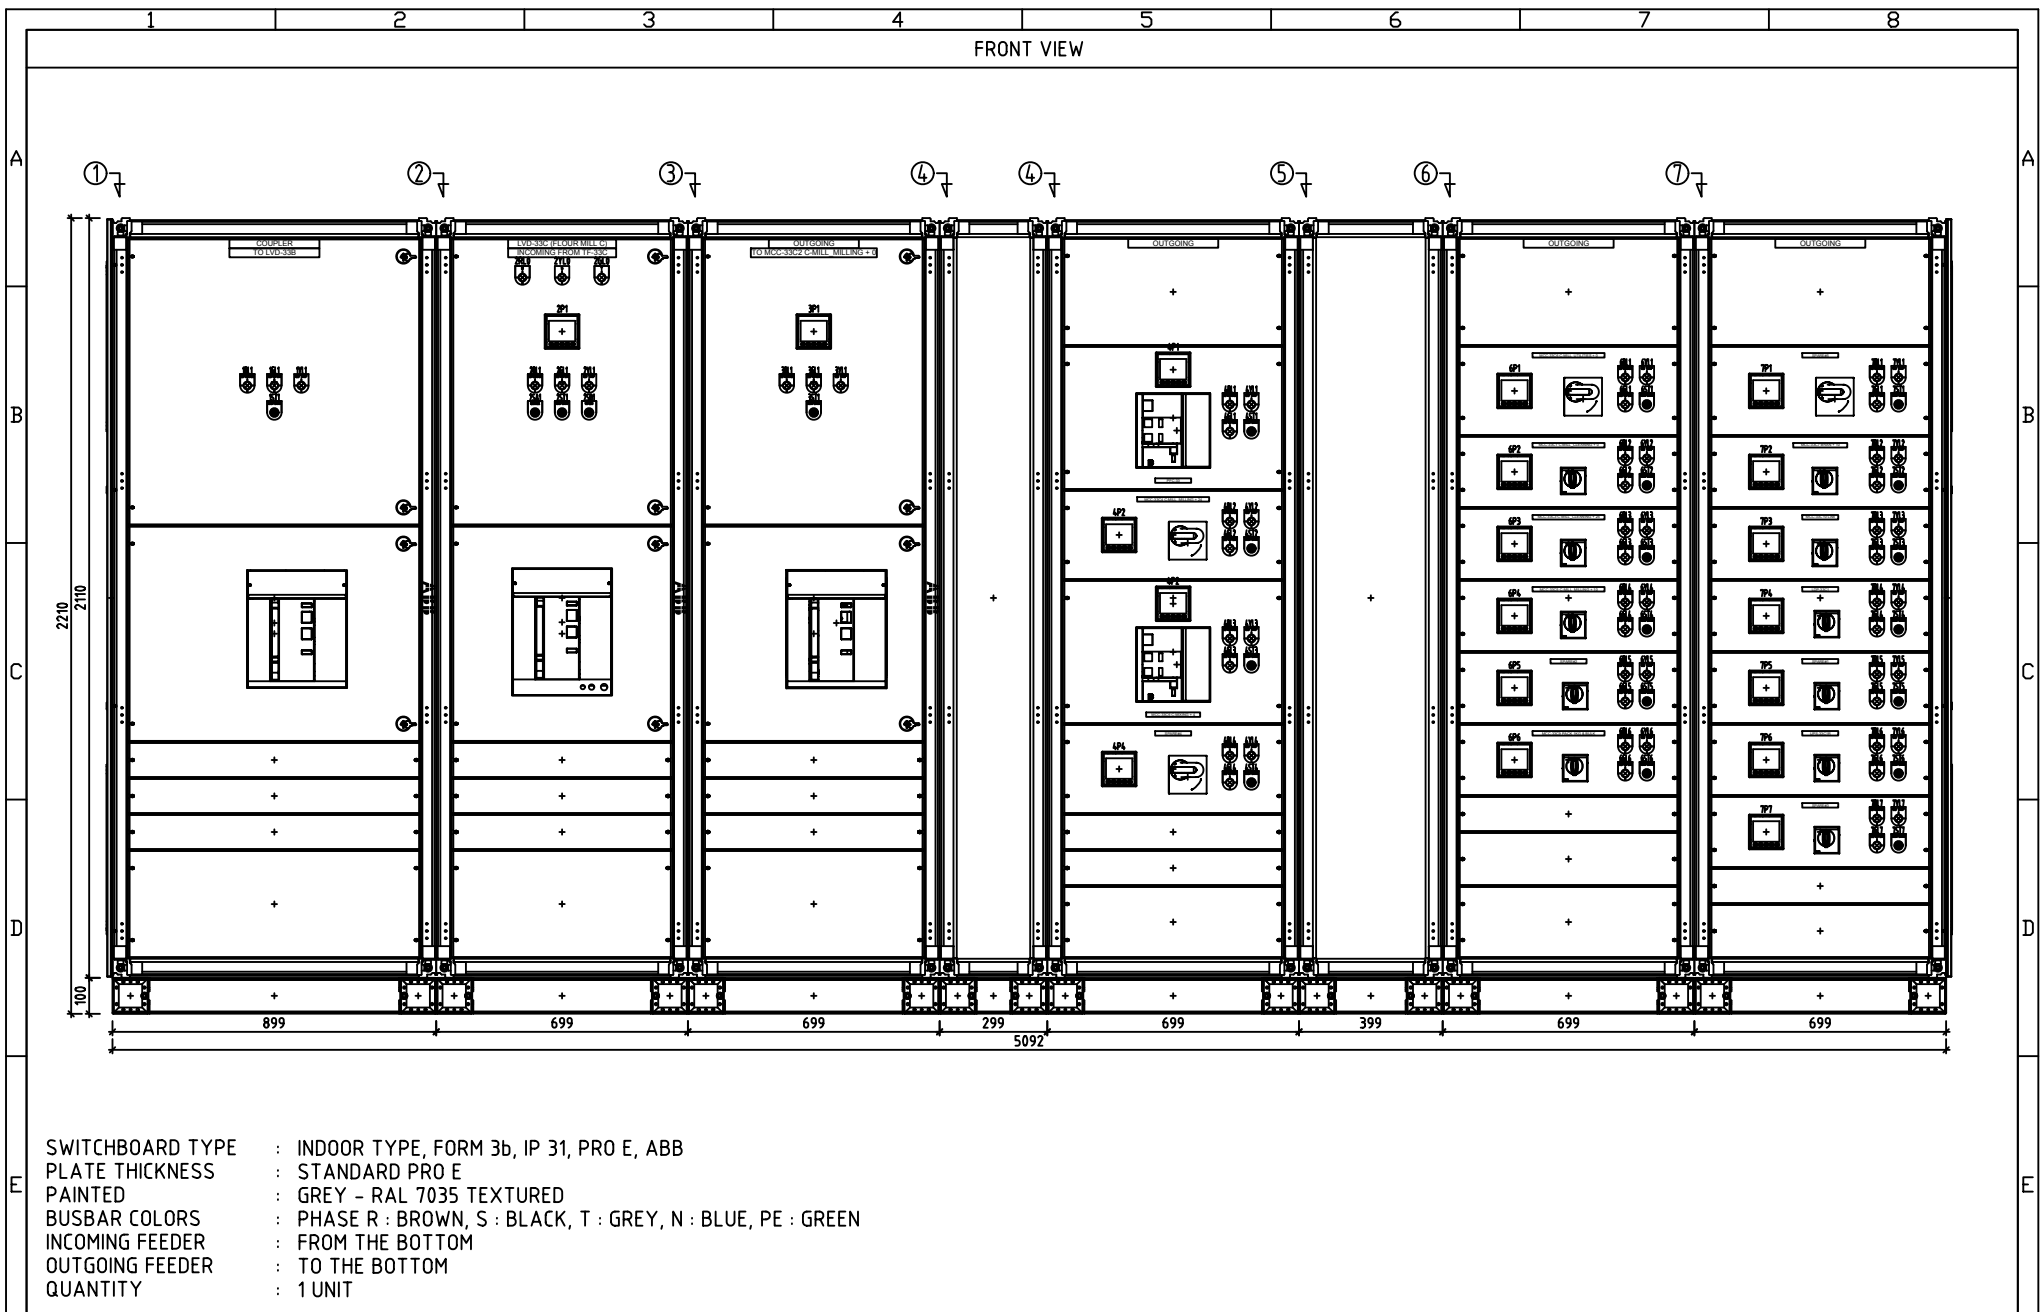



PROJECT :	DRAWING TITLE :	DATE	DRAWN	SIGN	VERIFIED	SIGN	DESCRIPTION	REV	PAGE
WILMAR FLOURMILL	OUTLINE DRAWING LVD-33C (FLOUR MILL C)	07-07-2020	YD		SBR		FOR APPROVAL	1	16
CUSTOMER : PT. ABB SAKTI INDUSTRI	NO DR/JO : DR-017/IND.2020								
	NO DWG. : ABB-002								
	SCALE : 1:21								
	Dimension in mm								


FRONT VIEW (COVER REMOVED)

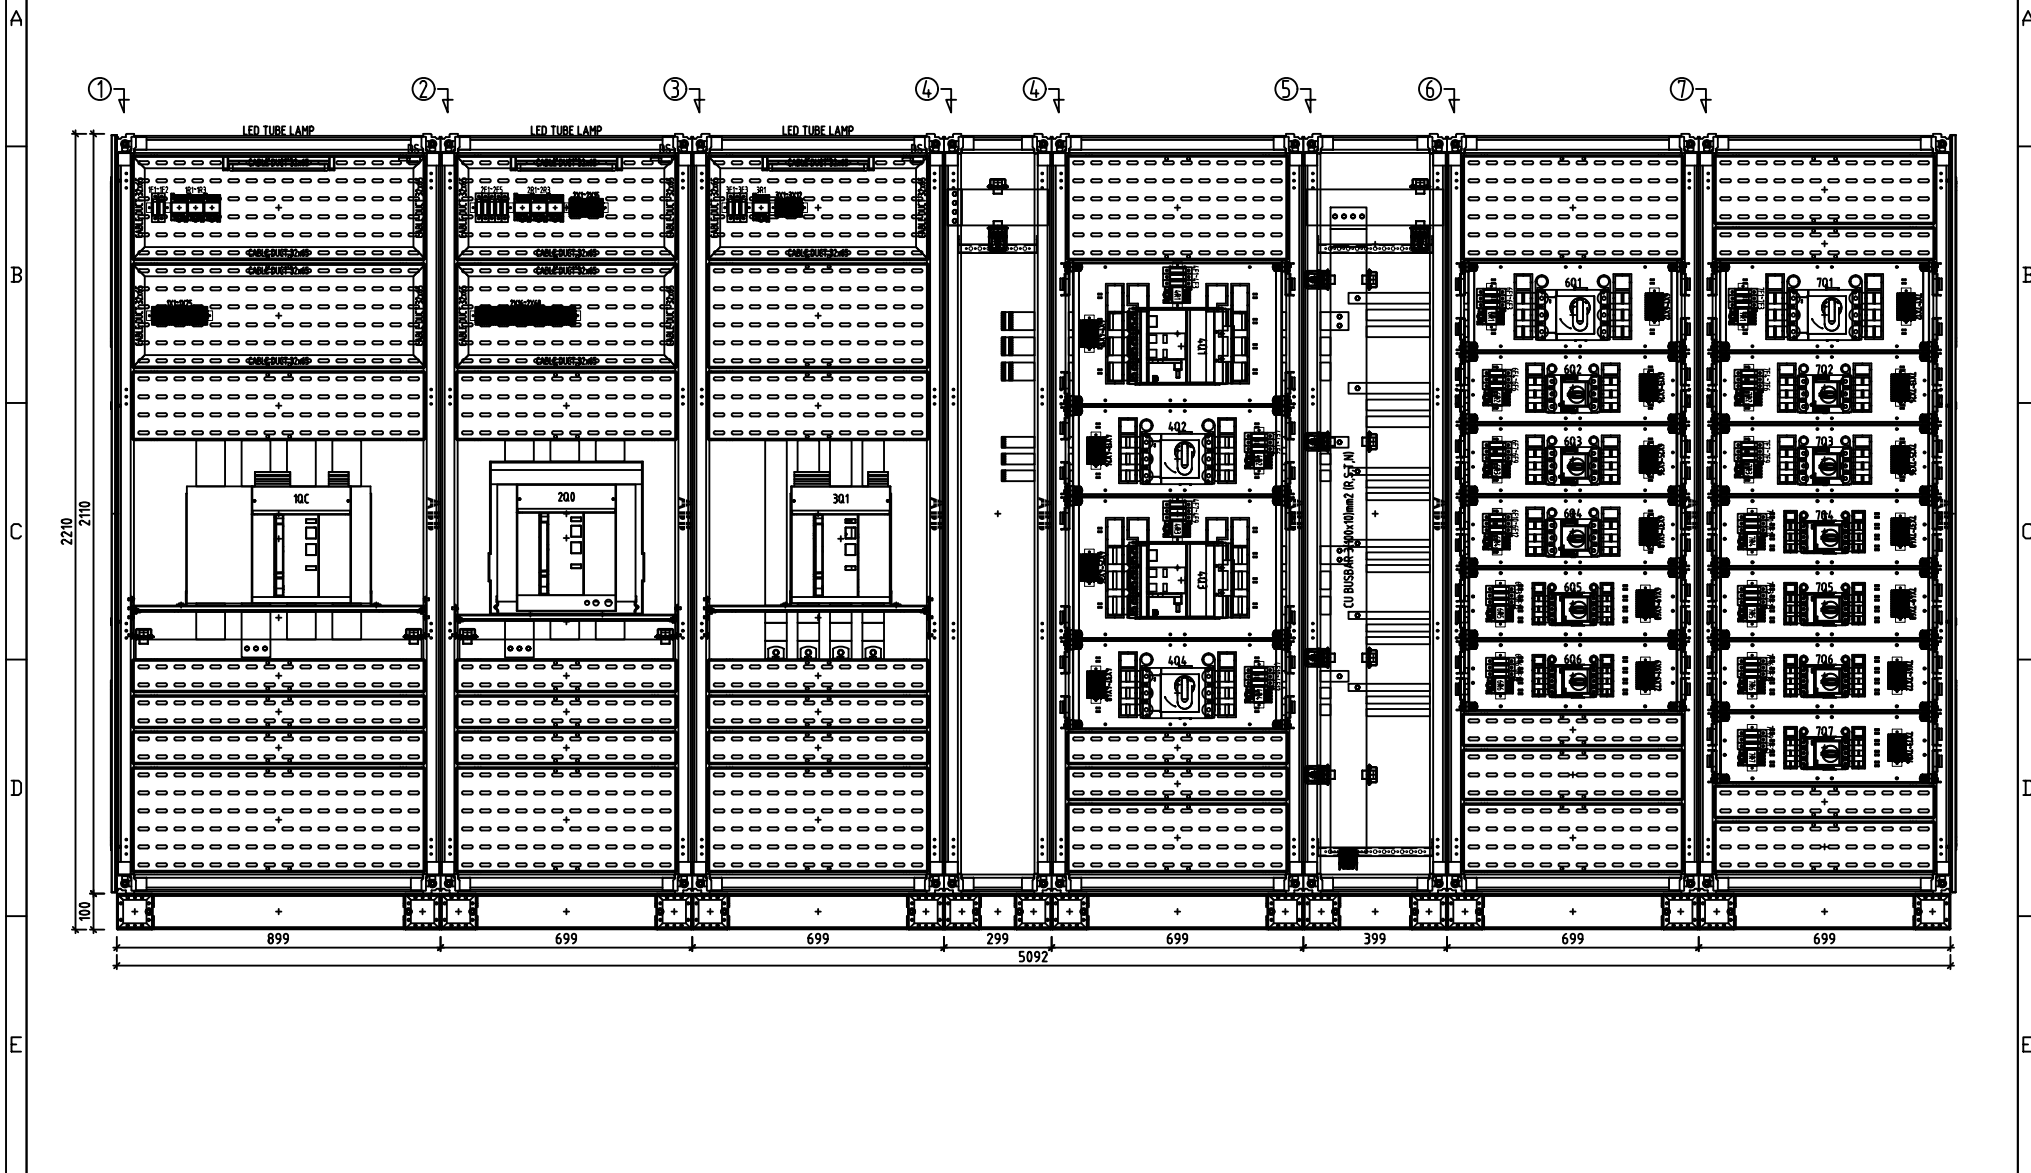

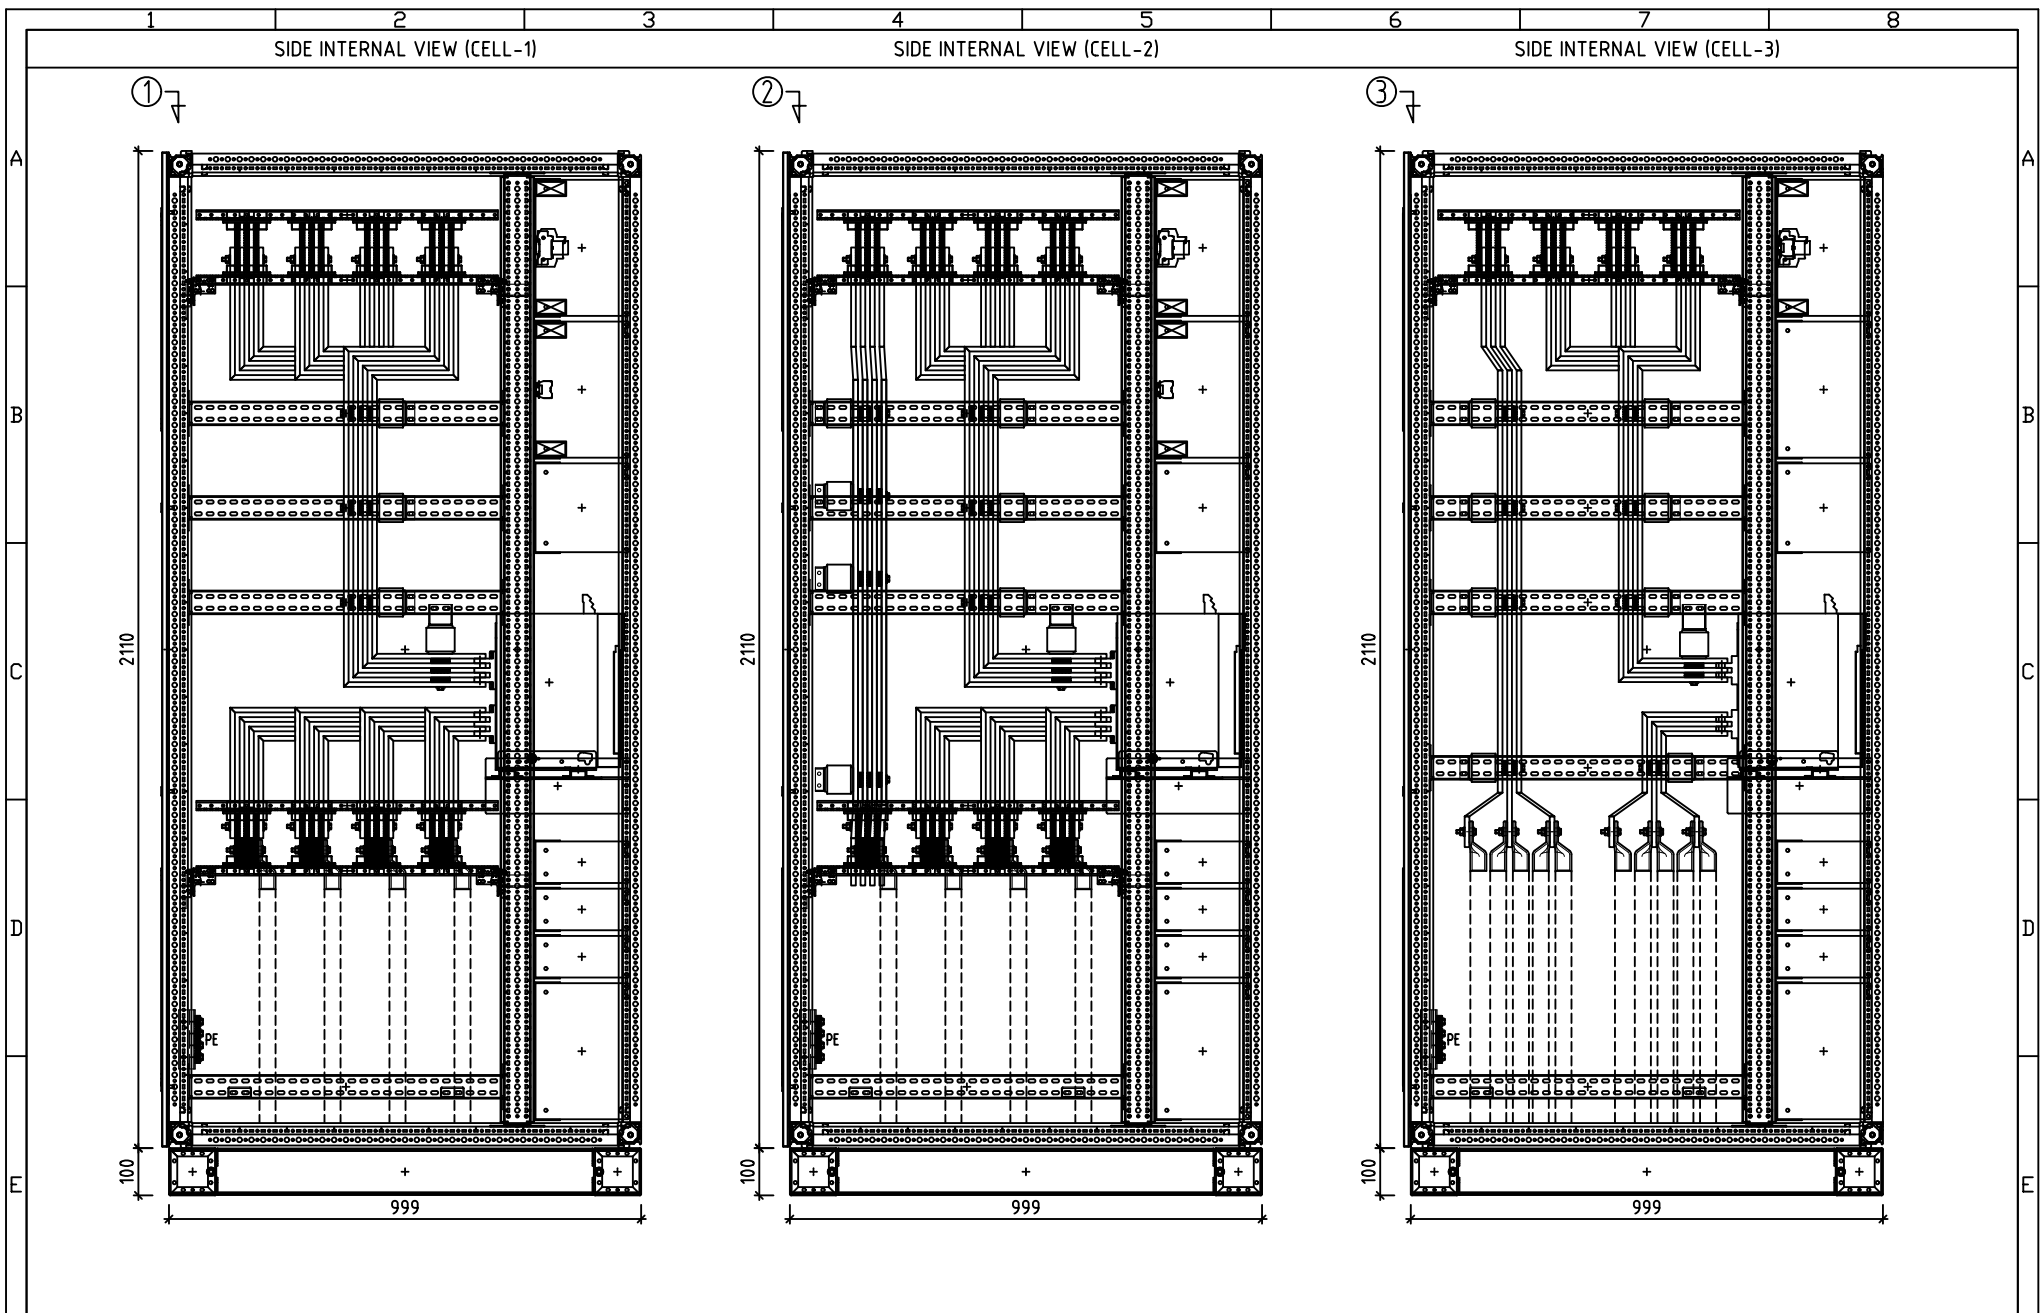


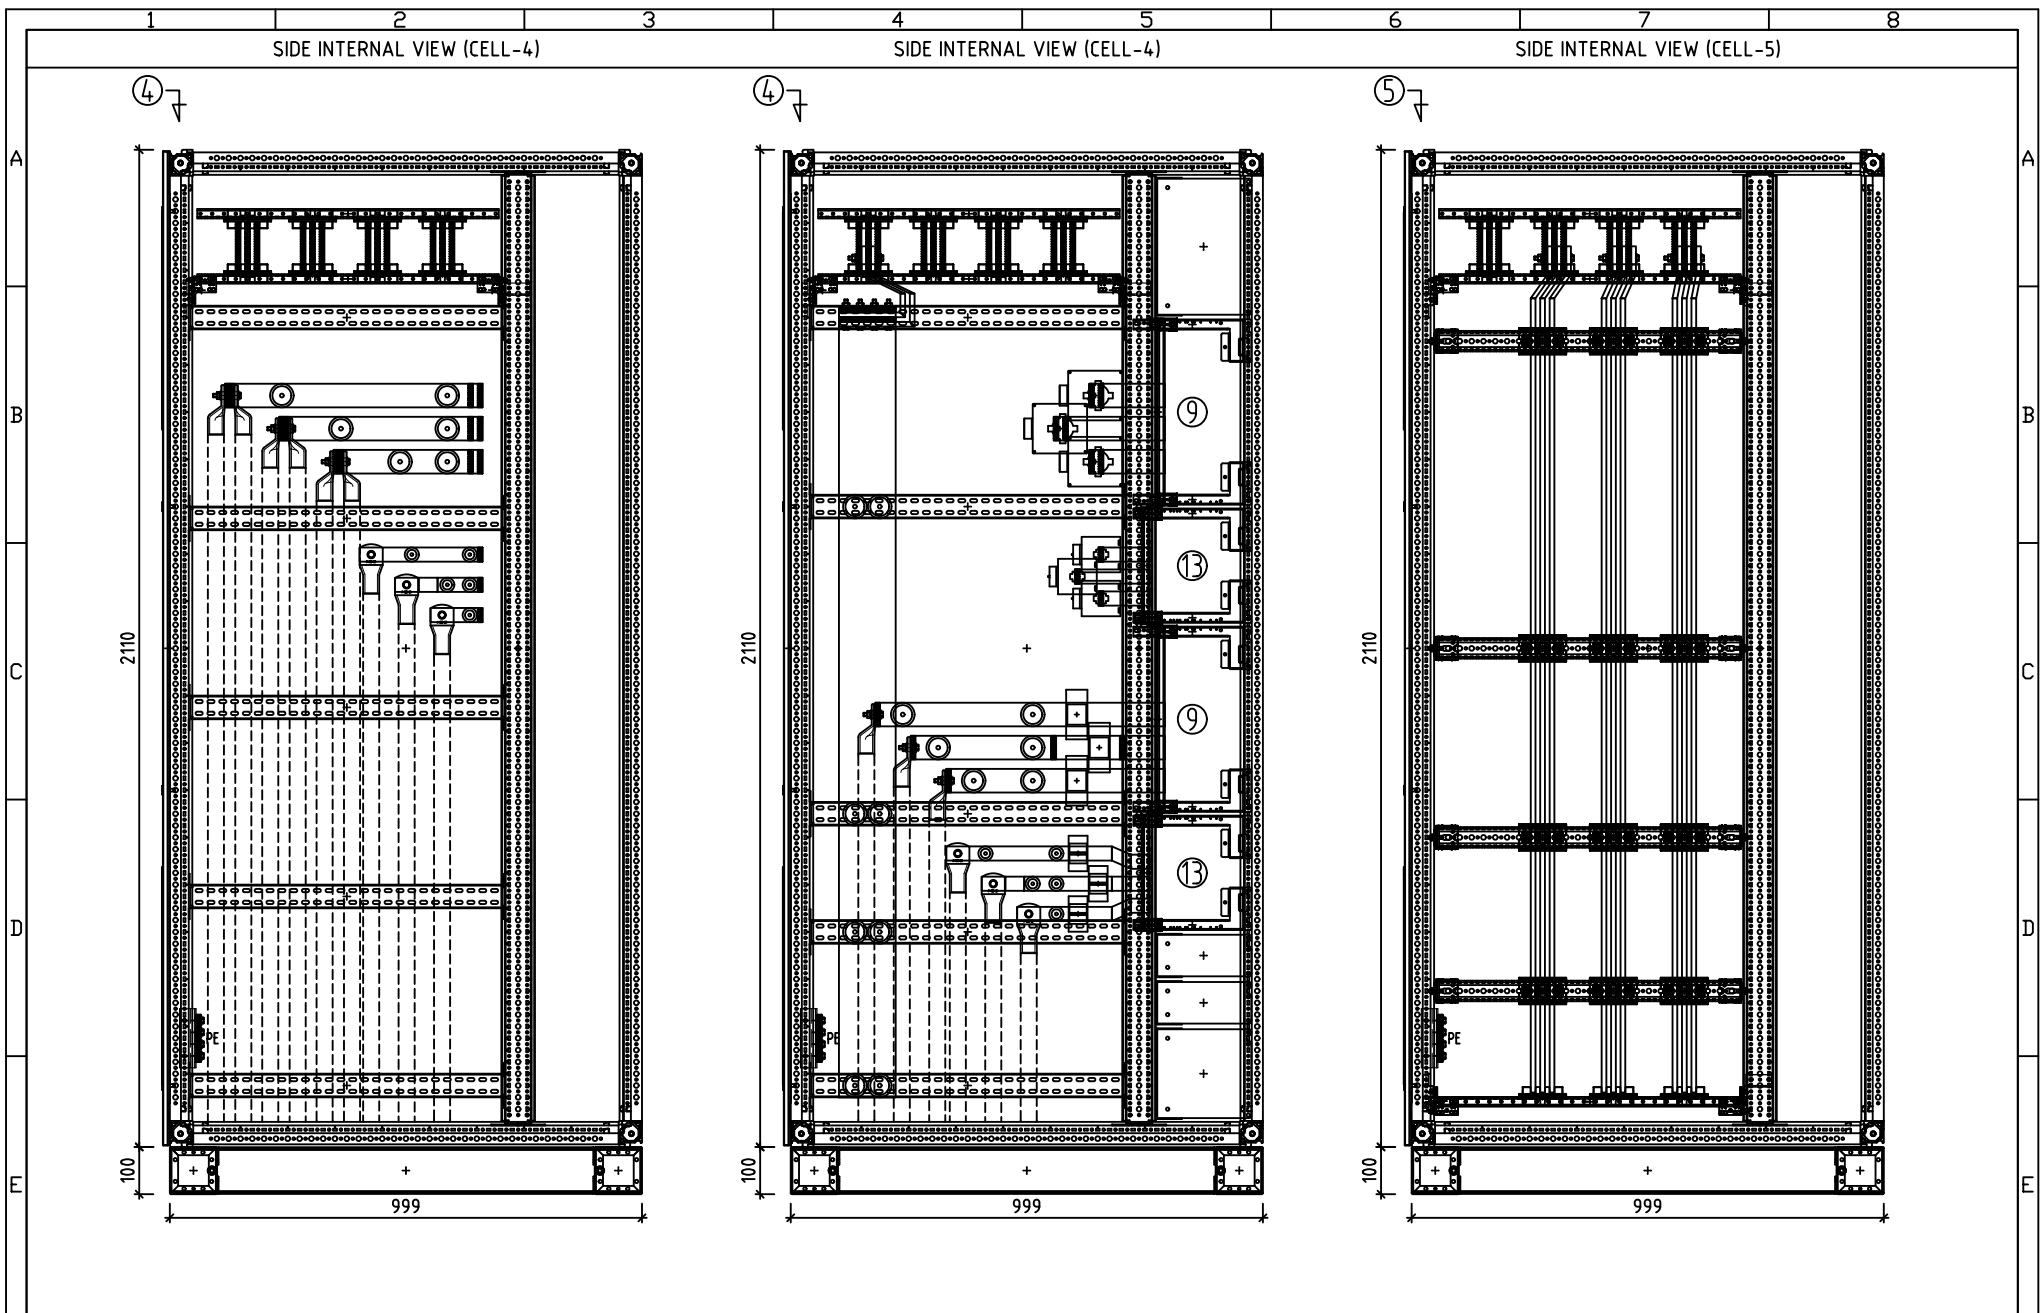

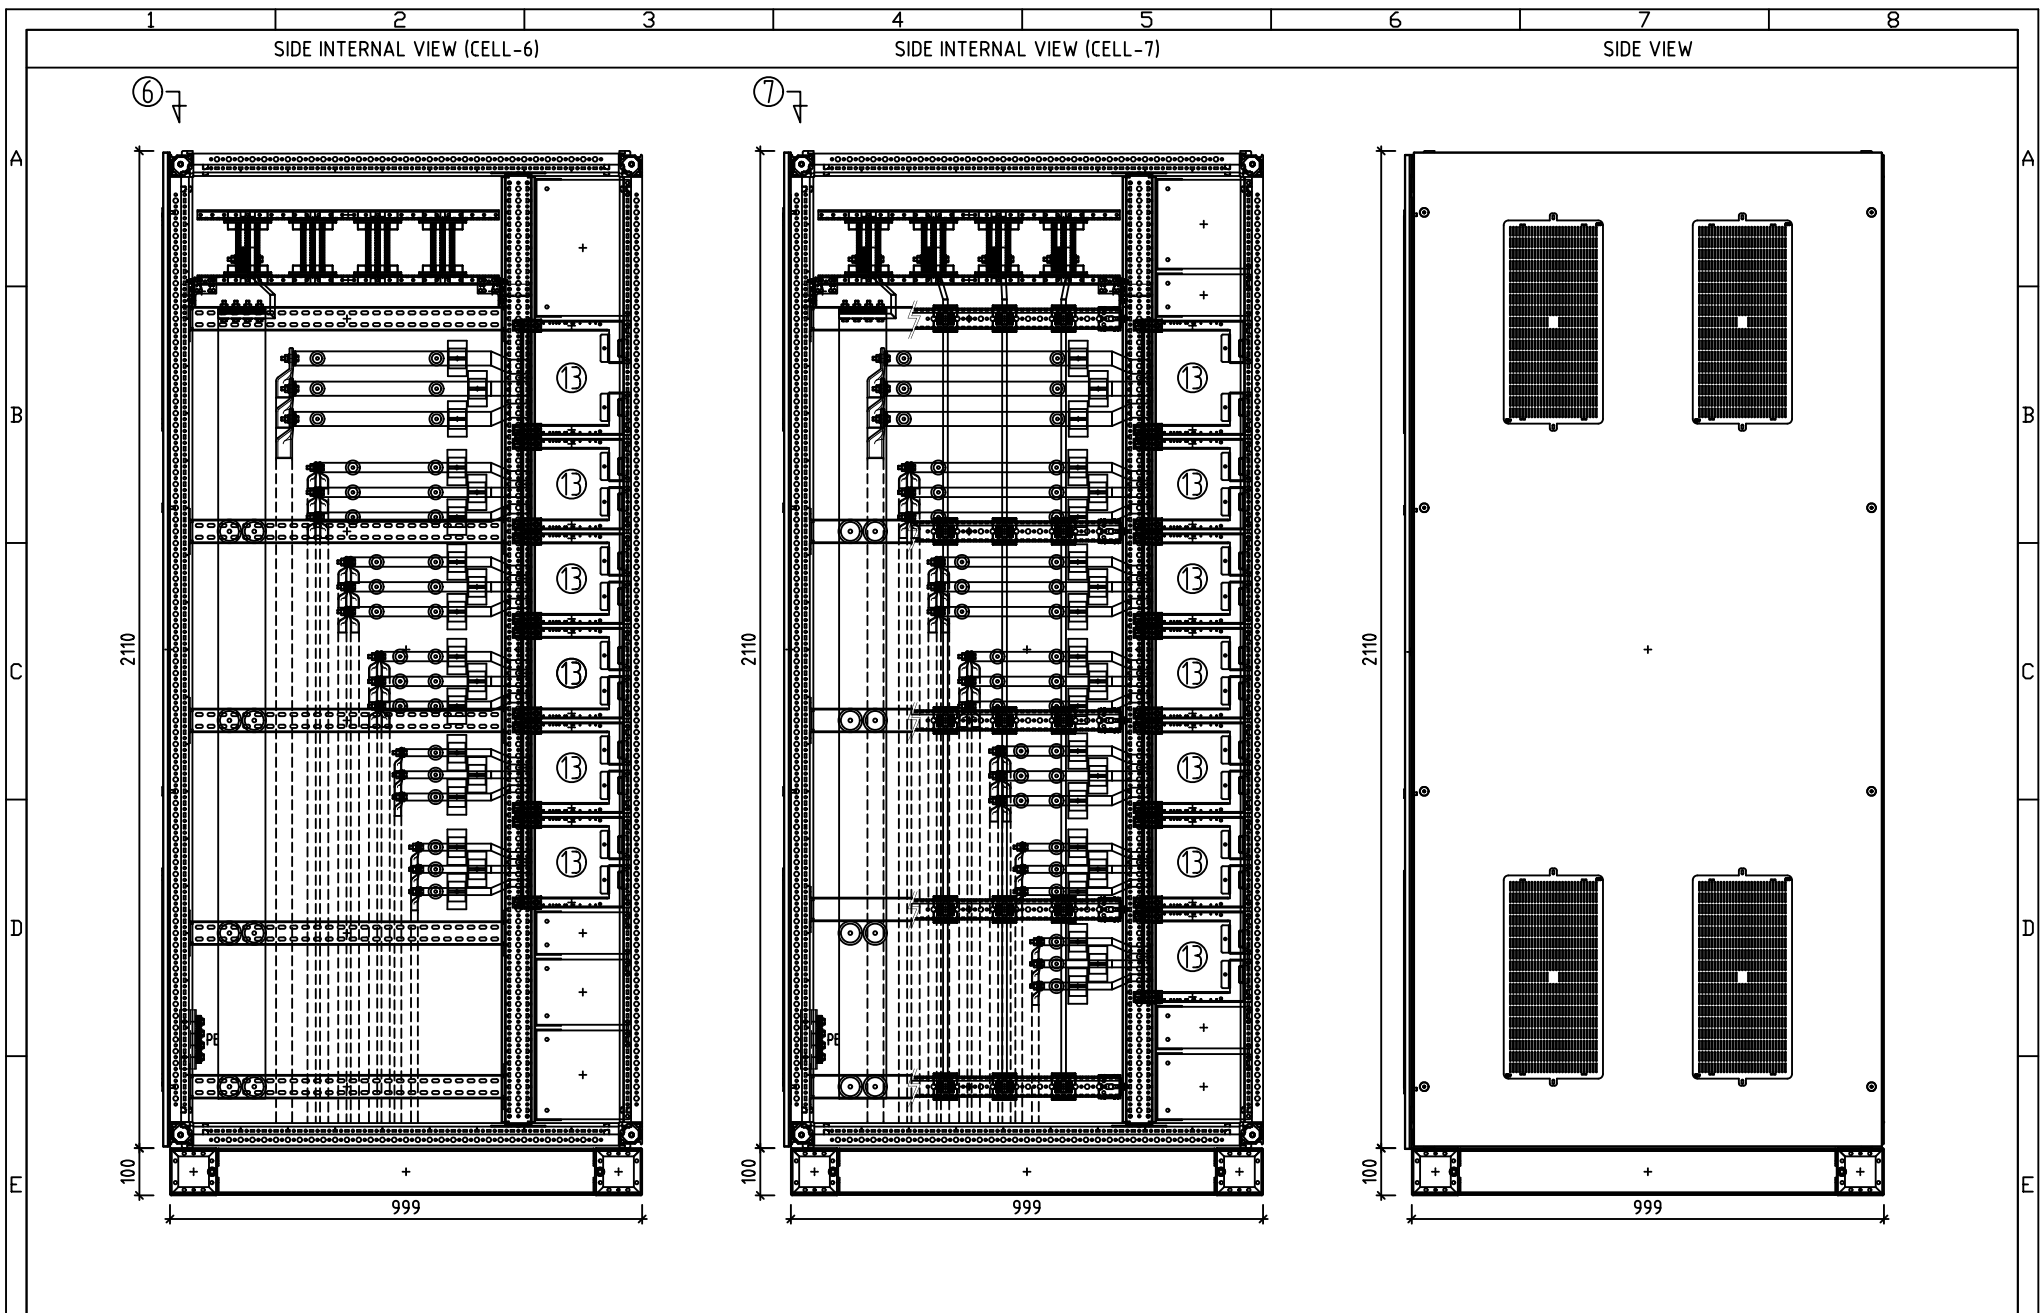


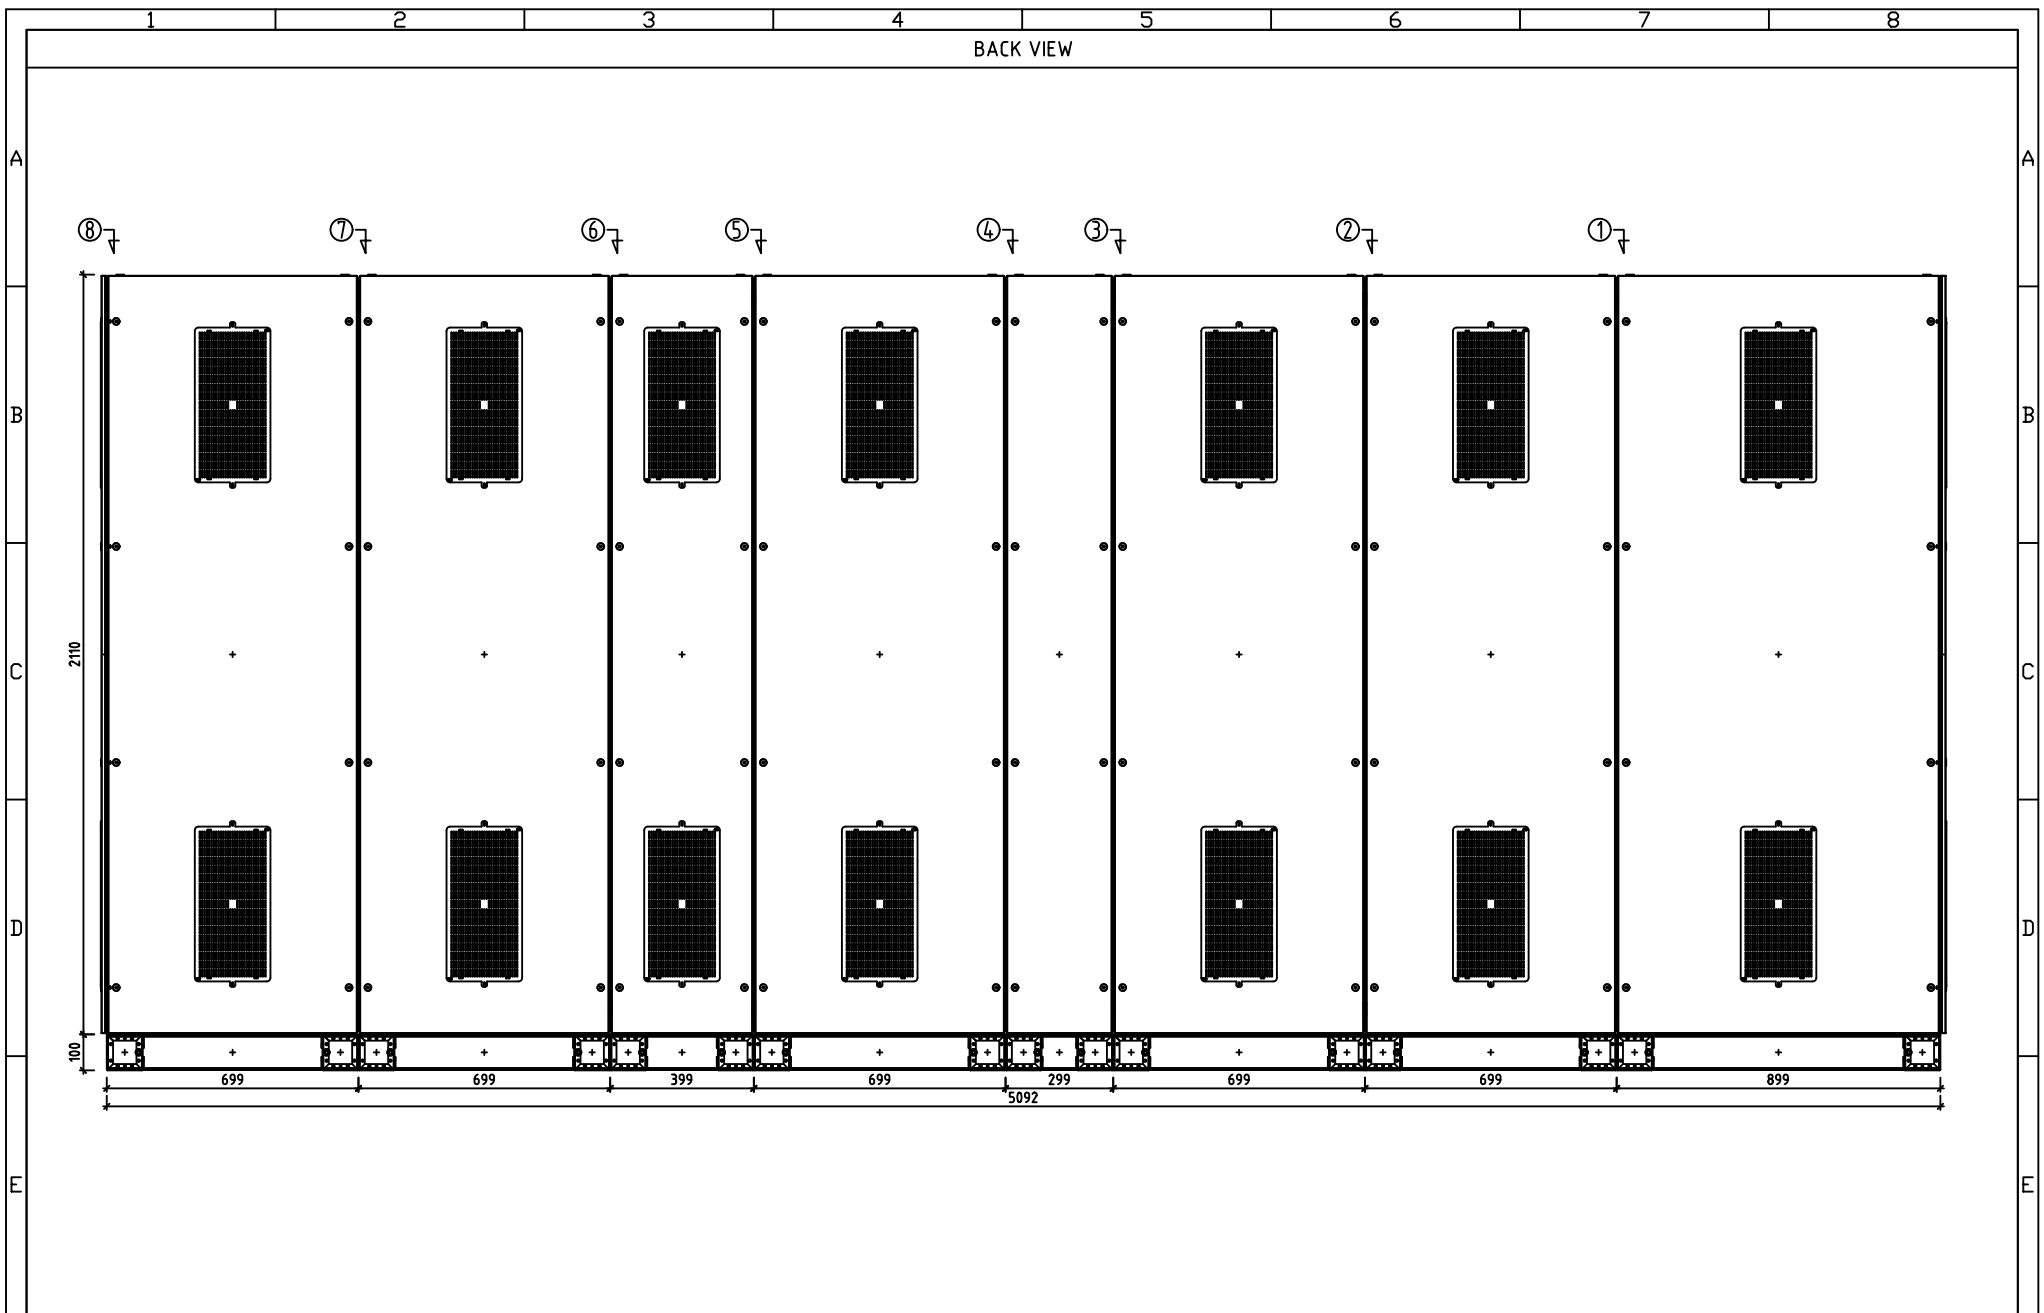


 PMElectric Best Value Electrical Solution	PROJECT :	WILMAR FLOURMILL	DRAWING TITLE :		DATE	DRAWN	SIGN	VERIFIED	SIGN	DESCRIPTION	REV	PAGE 716	
	CUSTOMER :	PT. ABB SAKTI INDUSTRI	OUTLINE DRAWING		07-07-2020	YD		SBR		FOR APPROVAL			
			LVD-33C (FLOUR MILL C)		-	-		-	-	-			
			NO DR/JO : DR-017/IND.2020		SCALE : 1:16	-		-	-	-	-		
			NO DWG. : ABB-002		Dimension in mm	-		-	-	-	-		

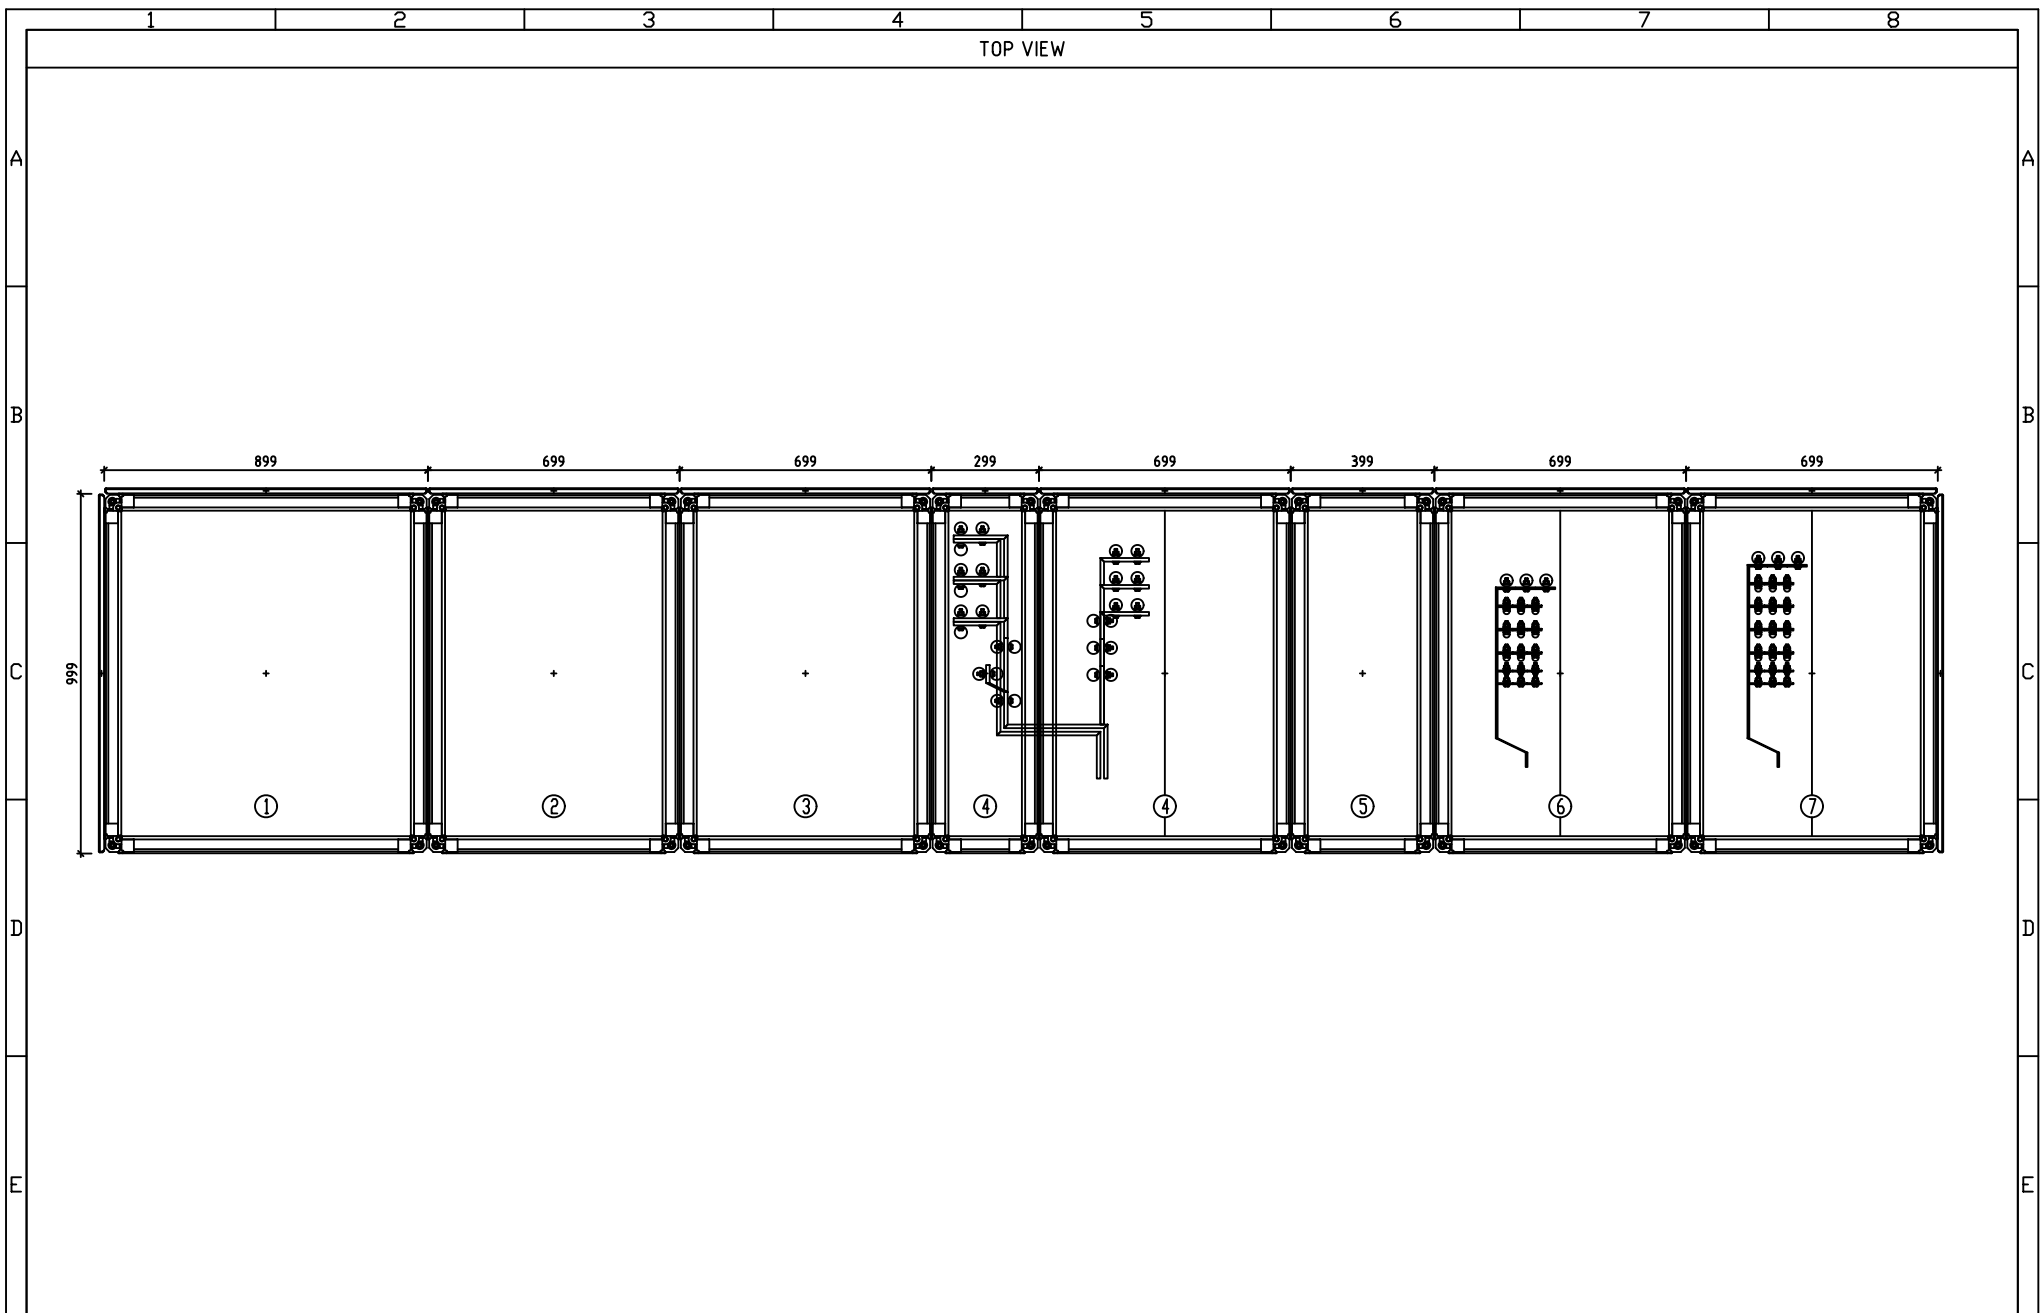


PMElectric Best Value Electrical Solution	PROJECT :	WILMAR FLOURMILL	DRAWING TITLE :		DATE	DRAWN	SIGN	VERIFIED	SIGN	DESCRIPTION	REV	PAGE
	CUSTOMER :	PT. ABB SAKTI INDUSTRI	OUTLINE DRAWING		07-07-2020	YD		SBR		FOR APPROVAL	▲	8
			LVD-33C (FLOUR MILL C)		-	-	Y	-		-	▲	
			NO DR/JO : DR-017/IND.2020	SCALE : 1:16	-	-	SG	-		-	▲	16
			NO DWG. : ABB-002	Dimension in mm	-	-		-		-	▲	

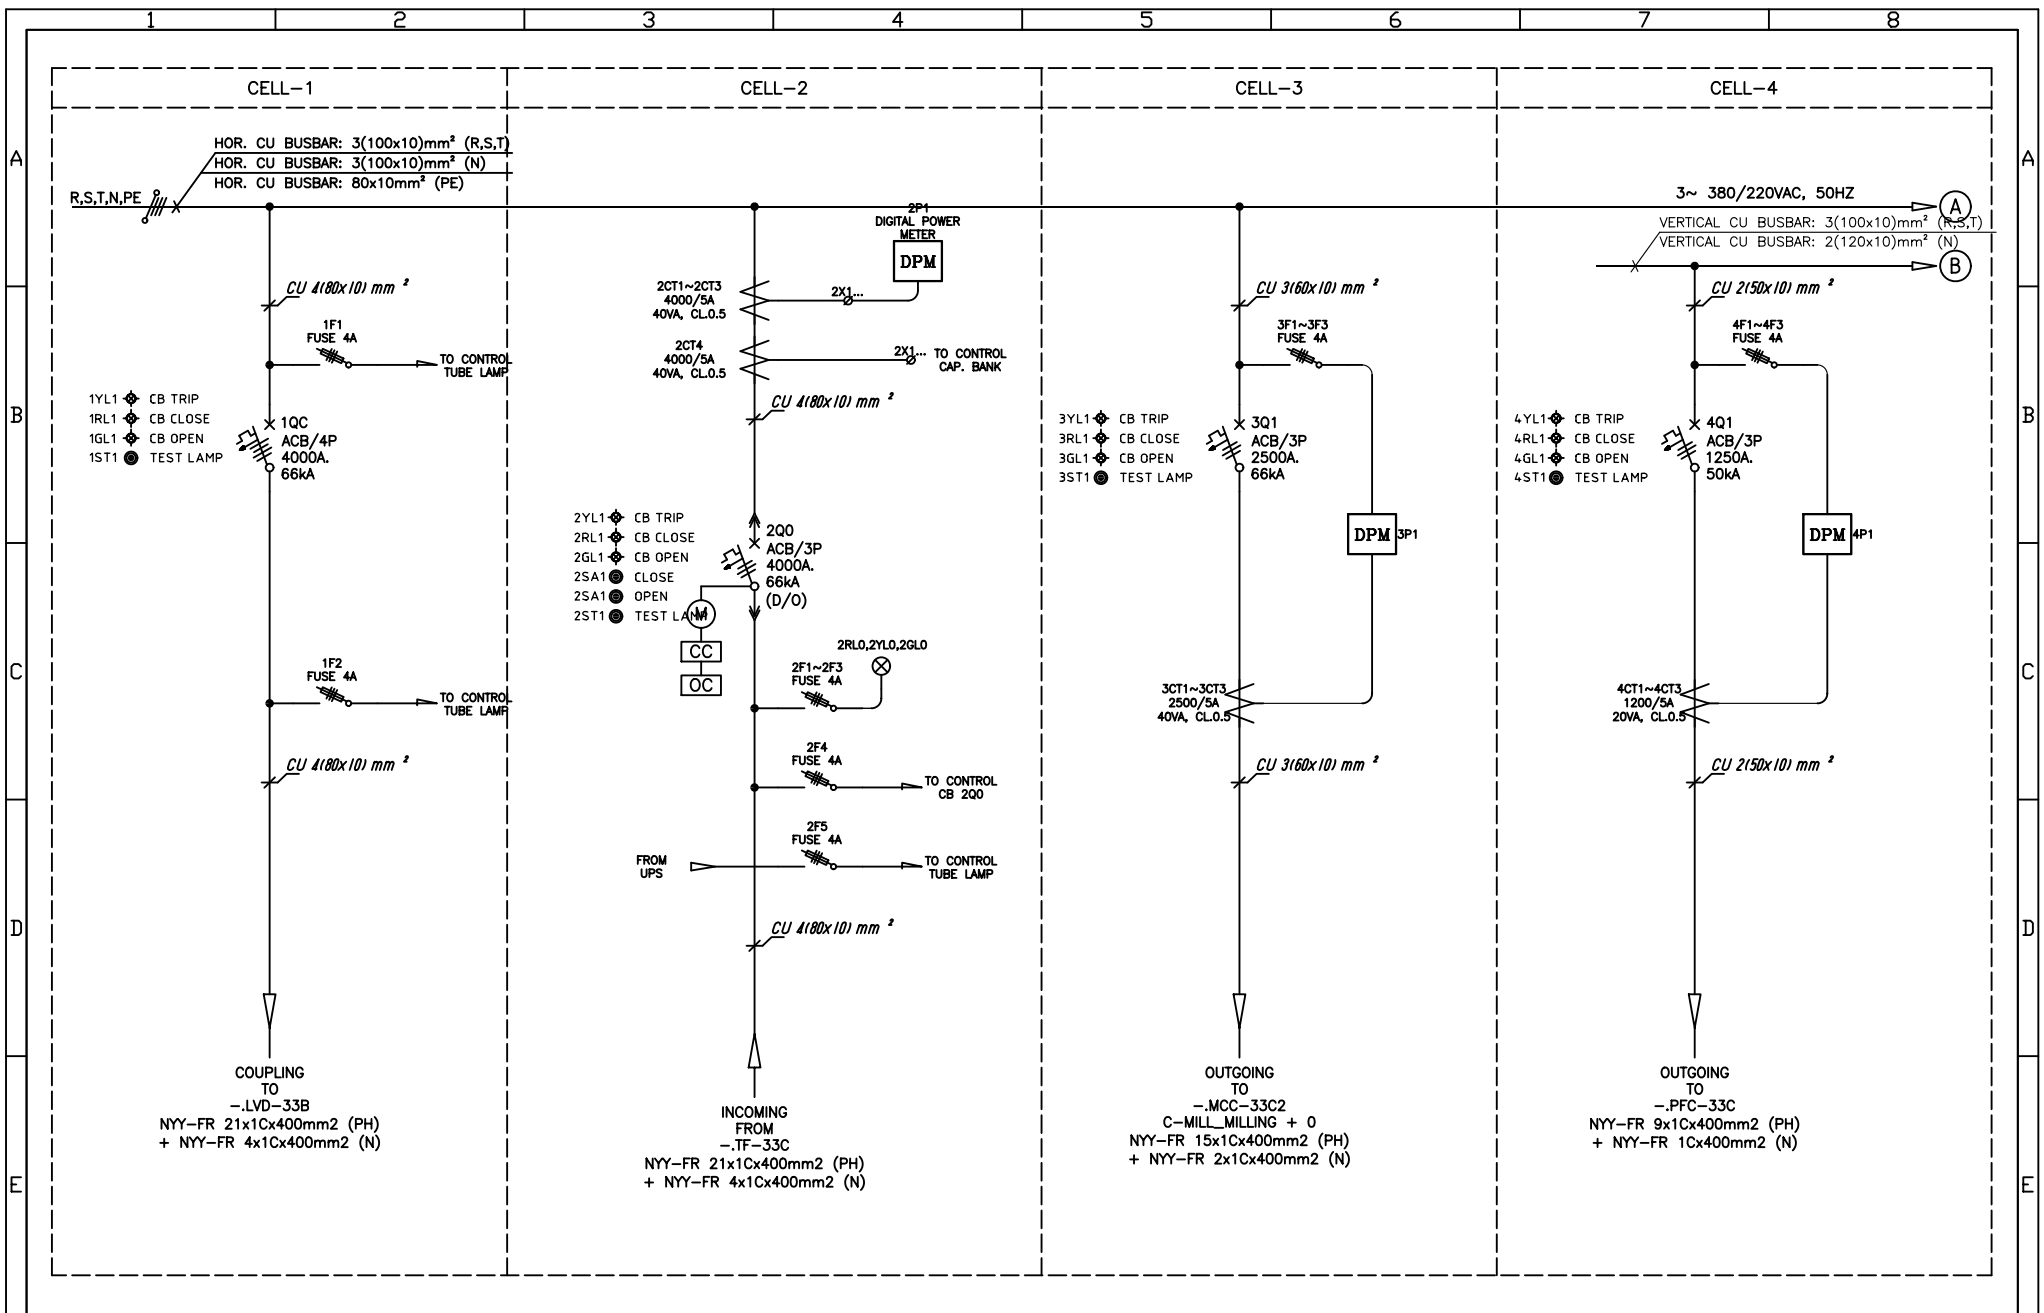


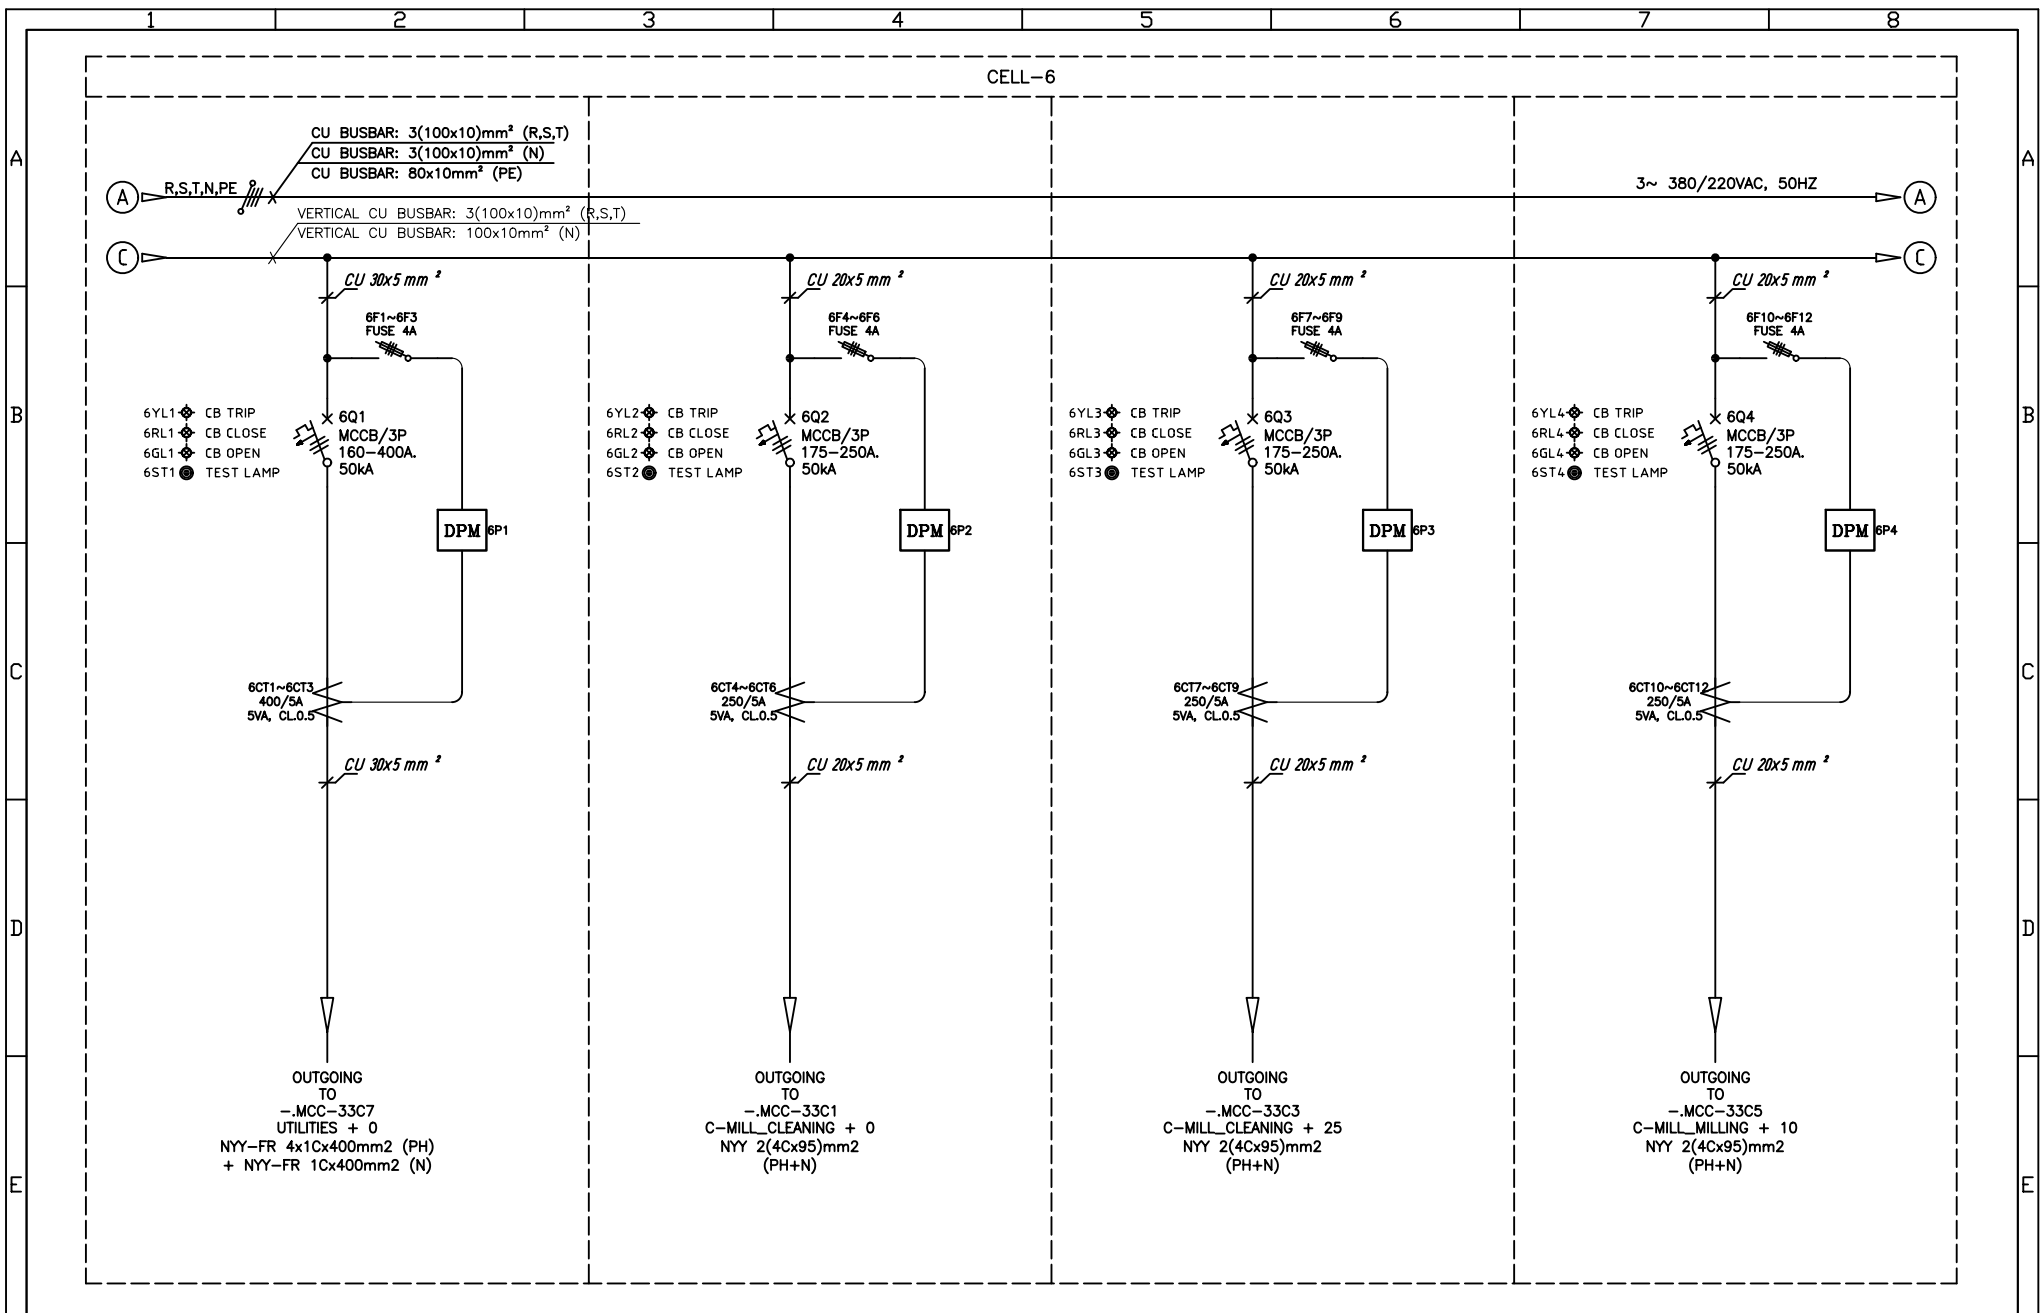


PMElectric Best Value Electrical Solution	PROJECT :	WILMAR FLOURMILL	DRAWING TITLE :	SINGLE LINE DIAGRAM LVD-33C (FLOUR MILL C)	DATE	DRAWN	SIGN	VERIFIED	SIGN	DESCRIPTION	REV	PAGE
	CUSTOMER :	PT. ABB SAKTI INDUSTRI	NO DR/JO :	DR-017/IND.2020	07-07-2020	YD		SBR		FOR APPROVAL	1	11
			SCALE :	NTS								
			NO DWG. :	ABB-002								16

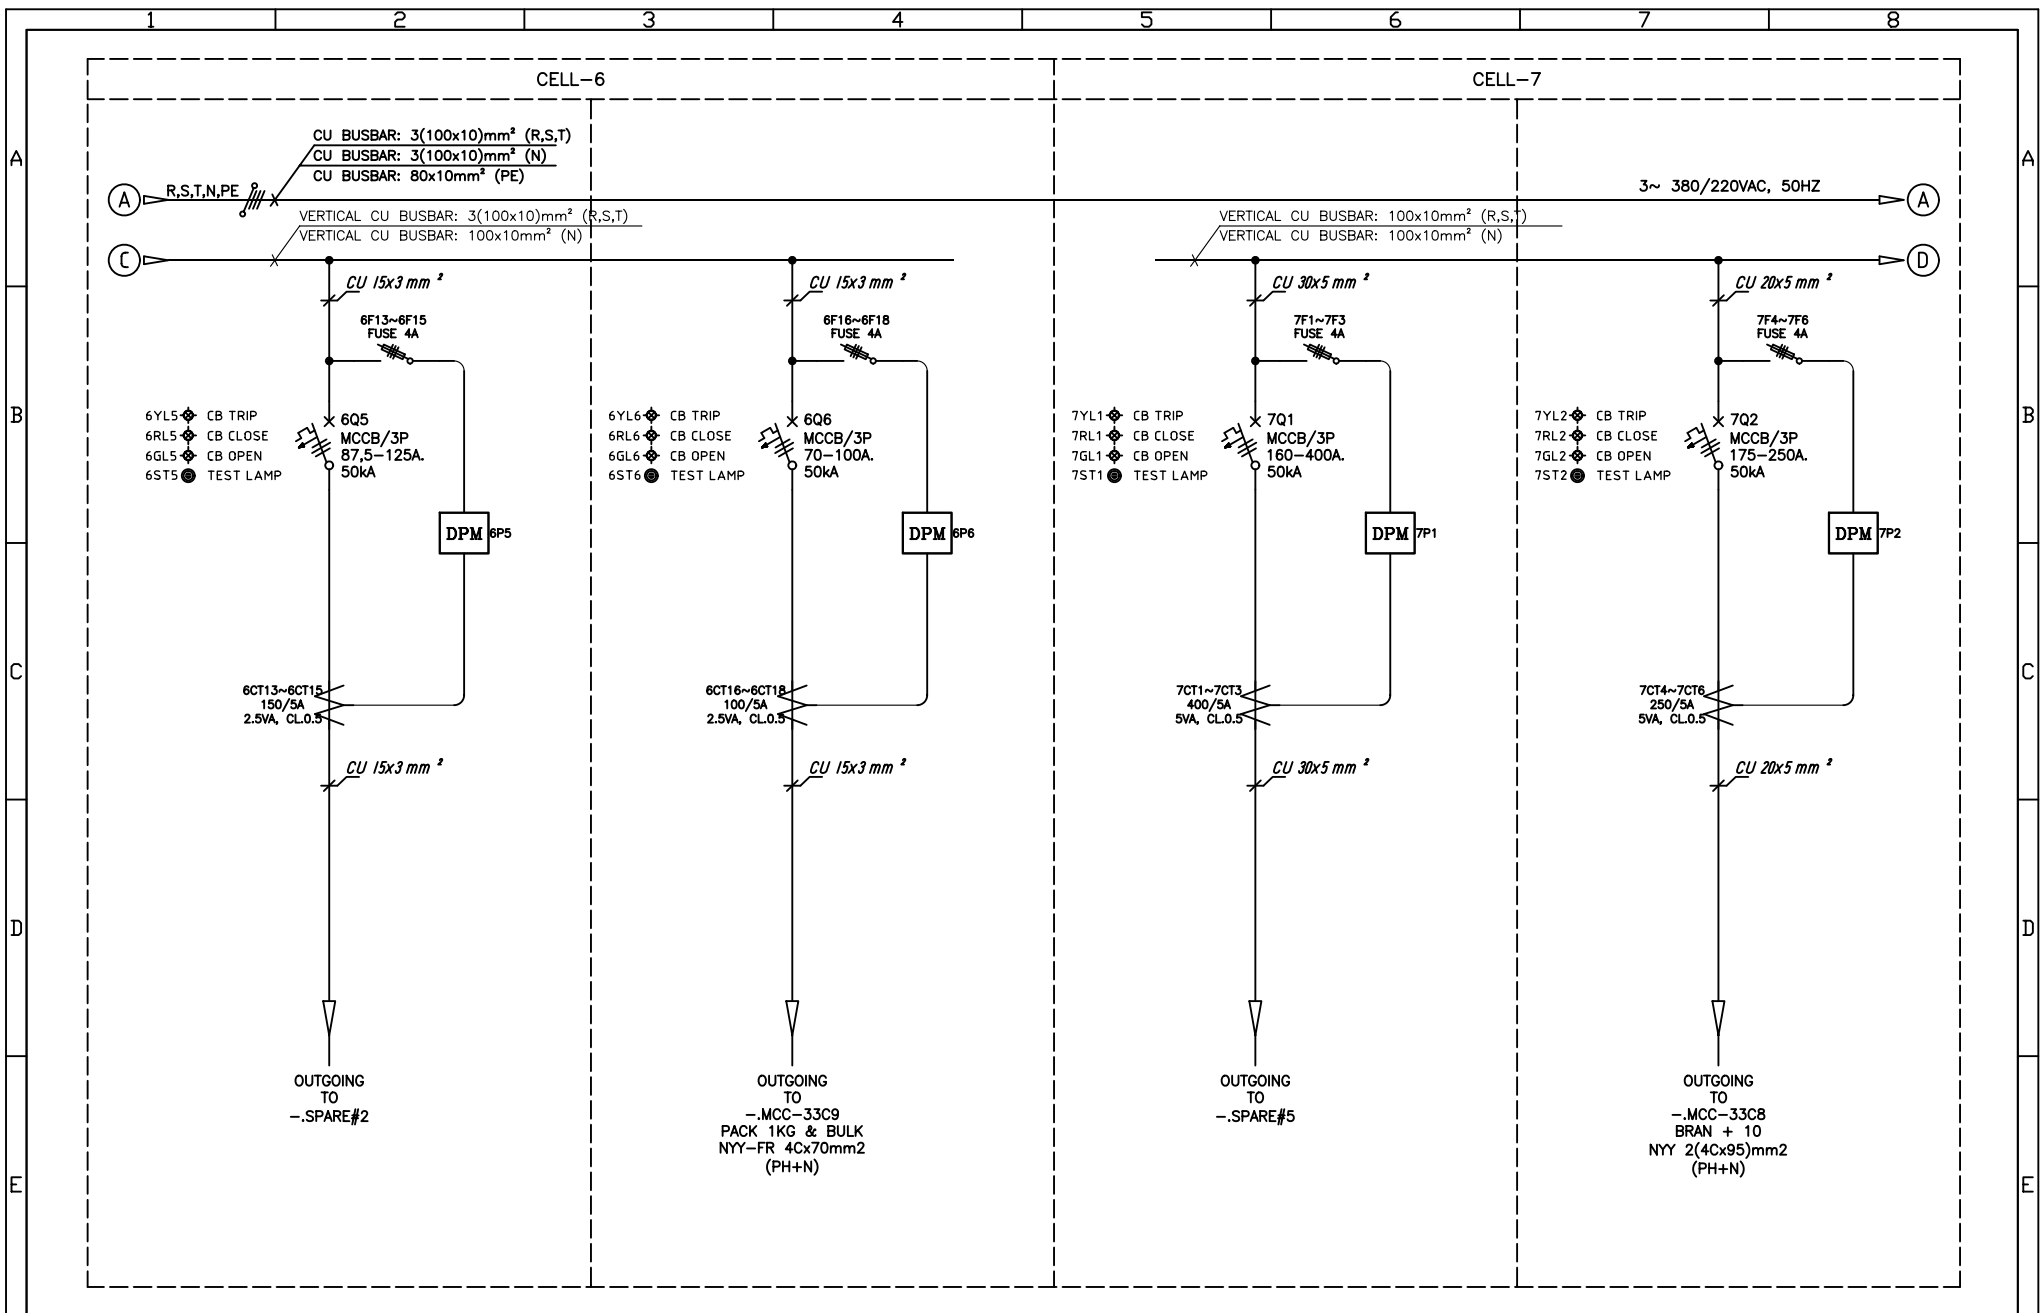

PMElectric Best Value Electrical Solution	PROJECT :	WILMAR FLOURMILL	DRAWING TITLE :	SINGLE LINE DIAGRAM LVD-33C (FLOUR MILL C)	DATE	DRAWN	SIGN	VERIFIED	SIGN	DESCRIPTION	REV	PAGE
	CUSTOMER :	PT. ABB SAKTI INDUSTRI	NO DR/JO :	DR-017/IND.2020	07-07-2020	YD		SBR		FOR APPROVAL	1	12
			SCALE :	NTS								
			NO DWG. :	ABB-002								16

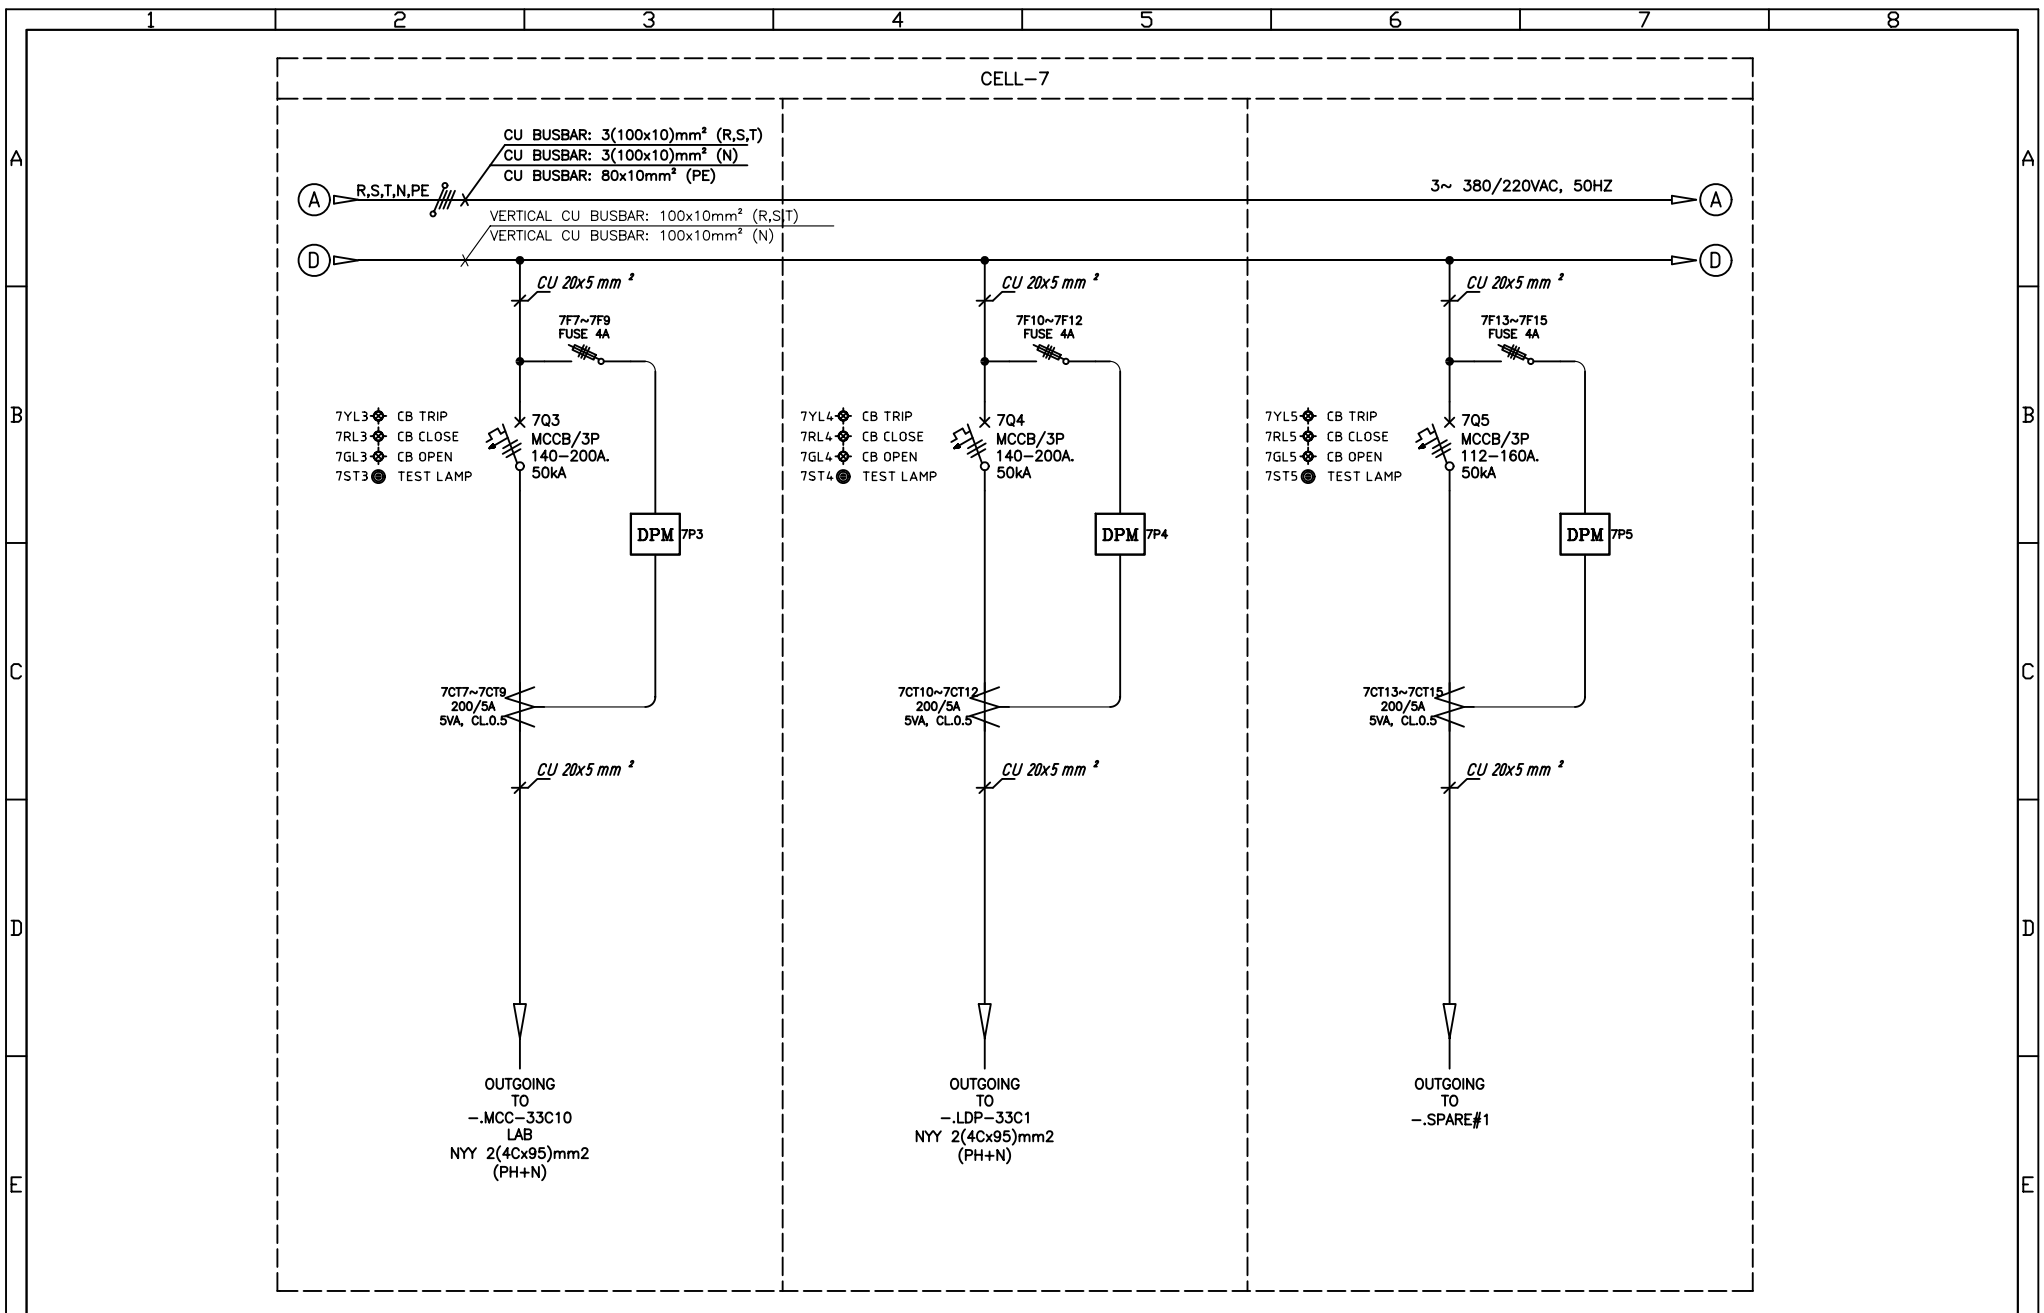

PMElectric Best Value Electrical Solution	PROJECT :	WILMAR FLOURMILL	DRAWING TITLE :	SINGLE LINE DIAGRAM LVD-33C (FLOUR MILL C)	DATE	DRAWN	SIGN	VERIFIED	SIGN	DESCRIPTION	REV	PAGE
	CUSTOMER :	PT. ABB SAKTI INDUSTRI	NO DR/JO : DR-017/IND.2020	SCALE : NTS	07-07-2020	YD		SBR		FOR APPROVAL	1	13
			NO DWG. : ABB-002	Dimension in mm	-	-		-		-	2	16
					-	-		-		-	3	

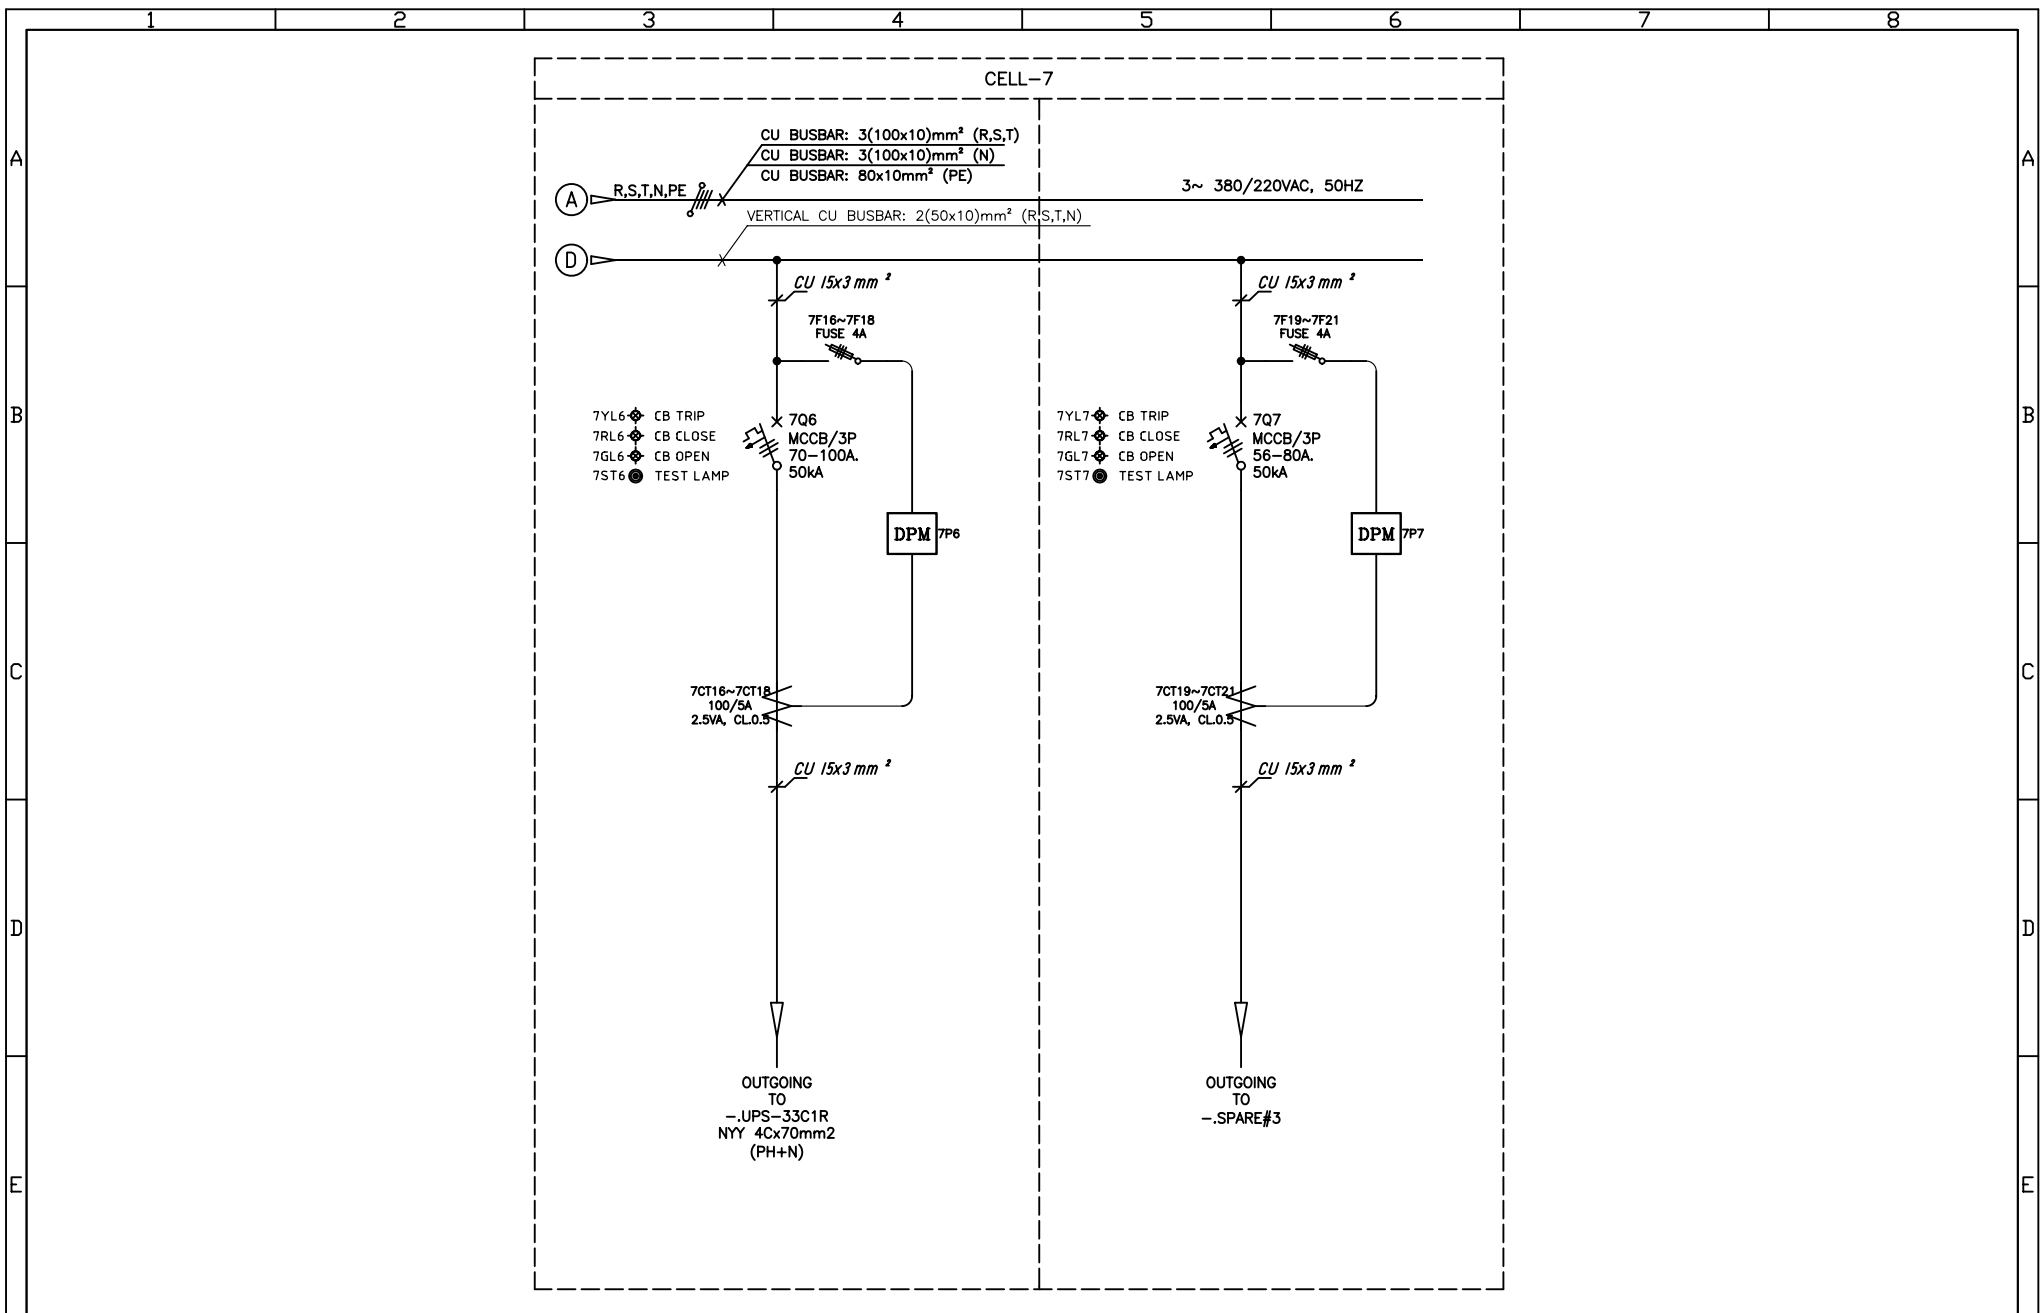

PMElectric Best Value Electrical Solution	PROJECT :	WILMAR FLOURMILL	DRAWING TITLE :	SINGLE LINE DIAGRAM LVD-33C (FLOUR MILL C)	DATE	DRAWN	SIGN	VERIFIED	SIGN	DESCRIPTION	REV	PAGE
	CUSTOMER :	PT. ABB SAKTI INDUSTRI	NO DR/JO :	DR-017/IND.2020	07-07-2020	YD		SBR		FOR APPROVAL	1	14
			NO DWG. :	ABB-002								
				Dimension in mm								16

1	2	3	4	5	6	7	8
NO	CODE	SPECIFICATION	TYPE	BRAND	QTY	UNIT	REMARK
		~ INCOMING SECTION ~					
1	2Q0	ACB 3P 4000A 66KA, D/O, E4.2N40 4000 EKIP DIP/LI	1SDA072541R1	ABB	1	PC	
2	-	EKIP TOUCH/LSIG	-	ABB	1	PC	
3	-	GEARED MOTOR 220-250V AC/DC, M-E2.2/E6.2	1SDA073725R1	ABB	1	PC	
4	-	SHUNT CLOSING RELEASE 220-240V AC/DC, YC E1.2-6.2	1SDA073687R1	ABB	1	PC	
5	-	SHUNT OPENING RELEASE 220-240V AC/DC, YO E1.2-6.2	1SDA073674R1	ABB	1	PC	
6	-	PADLOCK FOR ACB E2.2-E6.2 (TANPA GEMBOK)	1SDA073803R1	ABB	1	PC	
		~ COUPLING SECTION ~					
7	1QC	ACB 4P 4000A 66KA, F/T, E4.2N40 4000 EKIP DIP/LI	1SDA071821R1	ABB	1	PC	
8	-	EKIP DIP/LSI	-	ABB	1	PC	
9	-	PADLOCK FOR ACB E2.2-E6.2 (TANPA GEMBOK)	1SDA073803R1	ABB	1	PC	
		~ OUTGOING SECTION ~					
10	3Q1	ACB 3P 2500A 66KA, F/T, E2.2N25 2500 EKIP DIP/LI	1SDA071061R1	ABB	1	PC	
11	-	EKIP DIP/LSI	1SDA070871R1	ABB	1	PC	
12	-	PADLOCK FOR ACB E2.2-E6.2 (TANPA GEMBOK)	1SDA073803R1	ABB	1	PC	
13	4Q1	ACB 3P 1250A 50KA, F/T, E1.2C12 1250 EKIP DIP/LI	1SDA070831R1	ABB	1	PC	
14	-	EKIP DIP/LSI	1SDA070871R1	ABB	1	PC	
15	-	PADLOCK FOR ACB E1.2 (TANPA GEMBOK)	1SDA073800R1	ABB	1	PC	
16	4Q3	ACB 3P 1000A 50KA, F/T, E1.2C10 1000 EKIP DIP/LI	1SDA070791R1	ABB	1	PC	
17	-	EKIP DIP/LSI	1SDA070871R1	ABB	1	PC	
18	-	PADLOCK FOR ACB E1.2 (TANPA GEMBOK)	1SDA073800R1	ABB	1	PC	
19	4Q2,4Q4	MCCB 3P 252-630A 50KA, T5S PR221DS-LS/I-630	1SDA054404R1	ABB	2	PCS	
20	-	RHE NORMAL TRANSMITTED HANDLE, T5, FIXED/PLUGIN	1SDA054929R1	ABB	2	PCS	
21	-	AUXILIARY CONTACT, AUX-C 3Q 1SY 250V AC/DC, T4,T5,T6	1SDA054911R1	ABB	2	PCS	
22	6Q1,7Q1	MCCB 3P 160-400A 50KA, T5S PR221DS-LS/I-400	1SDA054333R1	ABB	2	PCS	
23	-	RHE NORMAL TRANSMITTED HANDLE, T5, FIXED/PLUGIN	1SDA054929R1	ABB	2	PCS	
24	-	AUXILIARY CONTACT, AUX-C 3Q 1SY 250V AC/DC, T4,T5,T6	1SDA054911R1	ABB	2	PCS	
25	6Q2-6Q4,7Q2	MCCB 3P 175-250A 50KA, XT3S TMD-250	1SDA068221R1	ABB	4	PCS	
26	-	RHE NORMAL TRANSMITTED HANDLE, XT1/XT3, FIXED/PLUGIN	1SDA066479R1	ABB	4	PCS	
27	-	AUXILIARY CONTACT, AUX-C 2Q 1SY 250V AC, XT1,XT2,XT3,XT4	1SDA066433R1	ABB	4	PCS	
28	7Q3-7Q4	MCCB 3P 140-200A 50KA, XT3S TMD-200	1SDA068220R1	ABB	2	PCS	
29	-	RHE NORMAL TRANSMITTED HANDLE, XT1/XT3, FIXED/PLUGIN	1SDA066479R1	ABB	2	PCS	
30	-	AUXILIARY CONTACT, AUX-C 2Q 1SY 250V AC, XT1,XT2,XT3,XT4	1SDA066433R1	ABB	2	PCS	
31	7Q5	MCCB 3P 112-160A 50KA, XT2S TMA-160	1SDA067560R1	ABB	1	PC	
32	-	RHE NORMAL TRANSMITTED HANDLE, XT2/XT4, FIXED/PLUGIN	1SDA069055R1	ABB	1	PC	
33	-	AUXILIARY CONTACT, AUX-C 2Q 1SY 250V AC, XT1,XT2,XT3,XT4	1SDA066433R1	ABB	1	PC	
34	6Q5	MCCB 3P 87,5-125A 50KA, XT2S TMA-125	1SDA067559R1	ABB	1	PC	
35	-	RHE NORMAL TRANSMITTED HANDLE, XT2/XT4, FIXED/PLUGIN	1SDA069055R1	ABB	1	PC	
36	-	AUXILIARY CONTACT, AUX-C 2Q 1SY 250V AC, XT1,XT2,XT3,XT4	1SDA066433R1	ABB	1	PC	
37	6Q6,7Q6	MCCB 3P 70-100A 50KA, XT2S TMA-100	1SDA067558R1	ABB	2	PCS	
38	-	RHE NORMAL TRANSMITTED HANDLE, XT2/XT4, FIXED/PLUGIN	1SDA069055R1	ABB	2	PCS	
39	-	AUXILIARY CONTACT, AUX-C 2Q 1SY 250V AC, XT1,XT2,XT3,XT4	1SDA066433R1	ABB	2	PCS	
40	-	-	-	-	-	-	

1		2		3		4		5		6		7		8	
 PMElectric Best Value Electrical Solution				PROJECT :		DRAWING TITLE :		DATE	DRAWN	SIGN	VERIFIED	SIGN	DESCRIPTION	REV	PAGE
				WILMAR FLOURMILL		PART LIST COMPONENT LVD-33C (FLOUR MILL C)		07-07-2020	YD		SBR		FOR APPROVAL		
								-	-		-		-		
								-	-		-		-		
								-	-		-		-		
				CUSTOMER :		NO DR/JO : DR-017/IND.2020		SCALE : NTS							
				PT. ABB SAKTI INDUSTRI		NO DWG. : ABB-002		Dimension in mm							

1	2	3	4	5	6	7	8
NO	CODE	SPECIFICATION	TYPE	BRAND	QTY	UNIT	REMARK
41	7Q7	MCCB 3P 56-80A 50KA, XT2S TMA-80	1SDA067557R1	ABB	1	PC	
42	-	RHE NORMAL TRANSMITTED HANDLE, XT2/XT4, FIXED/PLUGIN	1SDA069055R1	ABB	1	PC	
43	-	AUXILIARY CONTACT, AUX-C 2Q 1SY 250V AC, XT1,XT2,XT3,XT4	1SDA066433R1	ABB	1	PC	
		- CONTROL, METERING & PROTECTION SECTION -					
44	1F1~1F...	FUSE CARTRIDGE 4A + FUSE CARRIER	RT18-32	PM	61	PCS	
45	1RL0~1RL...	PILOT LAMP 220VAC, LED, Ø22.5mm, RED	AD22-221DS	AXLE/EQ	21	PCS	
46	1YL0~1YL...	PILOT LAMP 220VAC, LED, Ø22.5mm, YELLOW	AD22-221DS	AXLE/EQ	21	PCS	
47	1GL0~1GL...	PILOT LAMP 220VAC, LED, Ø22.5mm, GREEN	AD22-221DS	AXLE/EQ	21	PCS	
48	1SA1~1SA...	PUSH BUTTON, 1 C/O, Ø22.5mm, GREEN	AXP-B235	AXLE/EQ	1	PCS	
49	1SB1~1SB...	PUSH BUTTON, 1 C/O, Ø22.5mm, RED	AXP-B245	AXLE/EQ	1	PCS	
50	1ST1~1ST...	PUSH BUTTON FLUSH, 1 N/O, Ø22mm, BLACK	YW1B-M1E10B	IDEC/EQ	20	PCS	
51	1P1~1P...	DIGITAL POWER METER,MODBUS ETHERNET TCP/IP, M4M20ETHERNET	2CSG204471R4051	ABB	19	PCS	
52	1CT1~1CT...	CURRENT TRANSFORMER 100/5A, 2.5VA, CLASS 0.5, 31.5x11mm	HG30-100	HOWIG/EQ	9	PCS	
53	1CT1~1CT...	CURRENT TRANSFORMER 150/5A, 2.5VA, CLASS 0.5, 31.5x11mm	HG30-150	HOWIG/EQ	3	PCS	
54	1CT1~1CT...	CURRENT TRANSFORMER 200/5A, 5VA, CLASS 0.5, 31.5x11mm	HG30-200	HOWIG/EQ	9	PCS	
55	1CT1~1CT...	CURRENT TRANSFORMER 250/5A, 5VA, CLASS 0.5, 31.5x11mm	HG30-250	HOWIG/EQ	12	PCS	
56	1CT1~1CT...	CURRENT TRANSFORMER 400/5A, 5VA, CLASS 0.5, 42x11mm	HG40-400	HOWIG/EQ	6	PCS	
57	1CT1~1CT...	CURRENT TRANSFORMER 600/5A, 10VA, CLASS 0.5, 51x16mm	HG50-600	HOWIG/EQ	6	PCS	
58	1CT1~1CT...	CURRENT TRANSFORMER 1000/5A, 10VA, CLASS 0.5, 82x32.5mm	HG82-1000	HOWIG/EQ	3	PCS	
59	1CT1~1CT...	CURRENT TRANSFORMER 1200/5A, 20VA, CLASS 0.5, 82x32.5mm	HG82-1200	HOWIG/EQ	3	PCS	
60	1CT1~1CT...	CURRENT TRANSFORMER 2500/5A, 40VA, CLASS 0.5, 126x36mm	HG120-2500	HOWIG/EQ	3	PCS	
61	1CT1~1CT...	CURRENT TRANSFORMER 4000/5A, 40VA, CLASS 0.5, 151x133mm	HG150-4000	HOWIG/EQ	4	PCS	
62	1R1~1R...	RELAY 4-CO 10A 220VAC + SOCKET	LY4 + PTF14A-E	OMRON	24	PCS	
63	1X1~1X...	TERMINAL BLOCK, 4mm, 32A, ZS4	1SNK505010R0000	ENTRELEC	315	PCS	
64	-	END SECTION FOR ZS4~ZS25, ES4	1SNK505910R0000	ENTRELEC	20	PCS	
65	-	END STOPER, BM3	1SNK900001R0000	ENTRELEC	40	PCS	
66	DS	LIMIT SWITCH SINGLE POLE 1-CO	-	IMPORT	3	PCS	
67	TUBE LAMP	TUBULAR LAMP LED 4W, 220VAC	31099	PHILIPS	3	PCS	
68	-	WIRING & ACCESORIES (CABLE C/W FLAME RETARDANT INSULATION)	PM	LOCAL	1	LOT	
69	-	CU BUSBAR C/W FLAME RETARDANT INSULATION	PREMIUM	EX-IMPORT	1	LOT	
70	-	BOX PANEL UK: 2200(H) X 300(W) X 1000(D)mm ²	PRO E	ABB	1	UNIT	
71	-	BOX PANEL UK: 2200(H) X 400(W) X 1000(D)mm ²	PRO E	ABB	1	UNIT	
72	-	BOX PANEL UK: 2200(H) X 700(W) X 1000(D)mm ²	PRO E	ABB	5	UNIT	
73	-	BOX PANEL UK: 2200(H) X 900(W) X 1000(D)mm ²	PRO E	ABB	1	UNIT	
74							
75							
76							
77							
78							
79							
80							
81							
82							

1	2	3	4	5	6	7	8					
 PMElectric Best Value Electrical Solution	PROJECT :	WILMAR FLOURMILL	DRAWING TITLE :		DATE	DRAWN	SIGN	VERIFIED	SIGN	DESCRIPTION	REV	PAGE
			PART LIST COMPONENT		07-07-2020	YD		SBR		FOR APPROVAL		16
			LVD-33C (FLOUR MILL C)		-	-		-		-		
					-	-		-		-		
					-	-		-		-		
	CUSTOMER :	PT. ABB SAKTI INDUSTRI	NO DR/JO : DR-017/IND.2020	SCALE : NTS	-	-		-		-		16
			NO DWG. : ABB-002	Dimension in mm	-	-		-		-		