



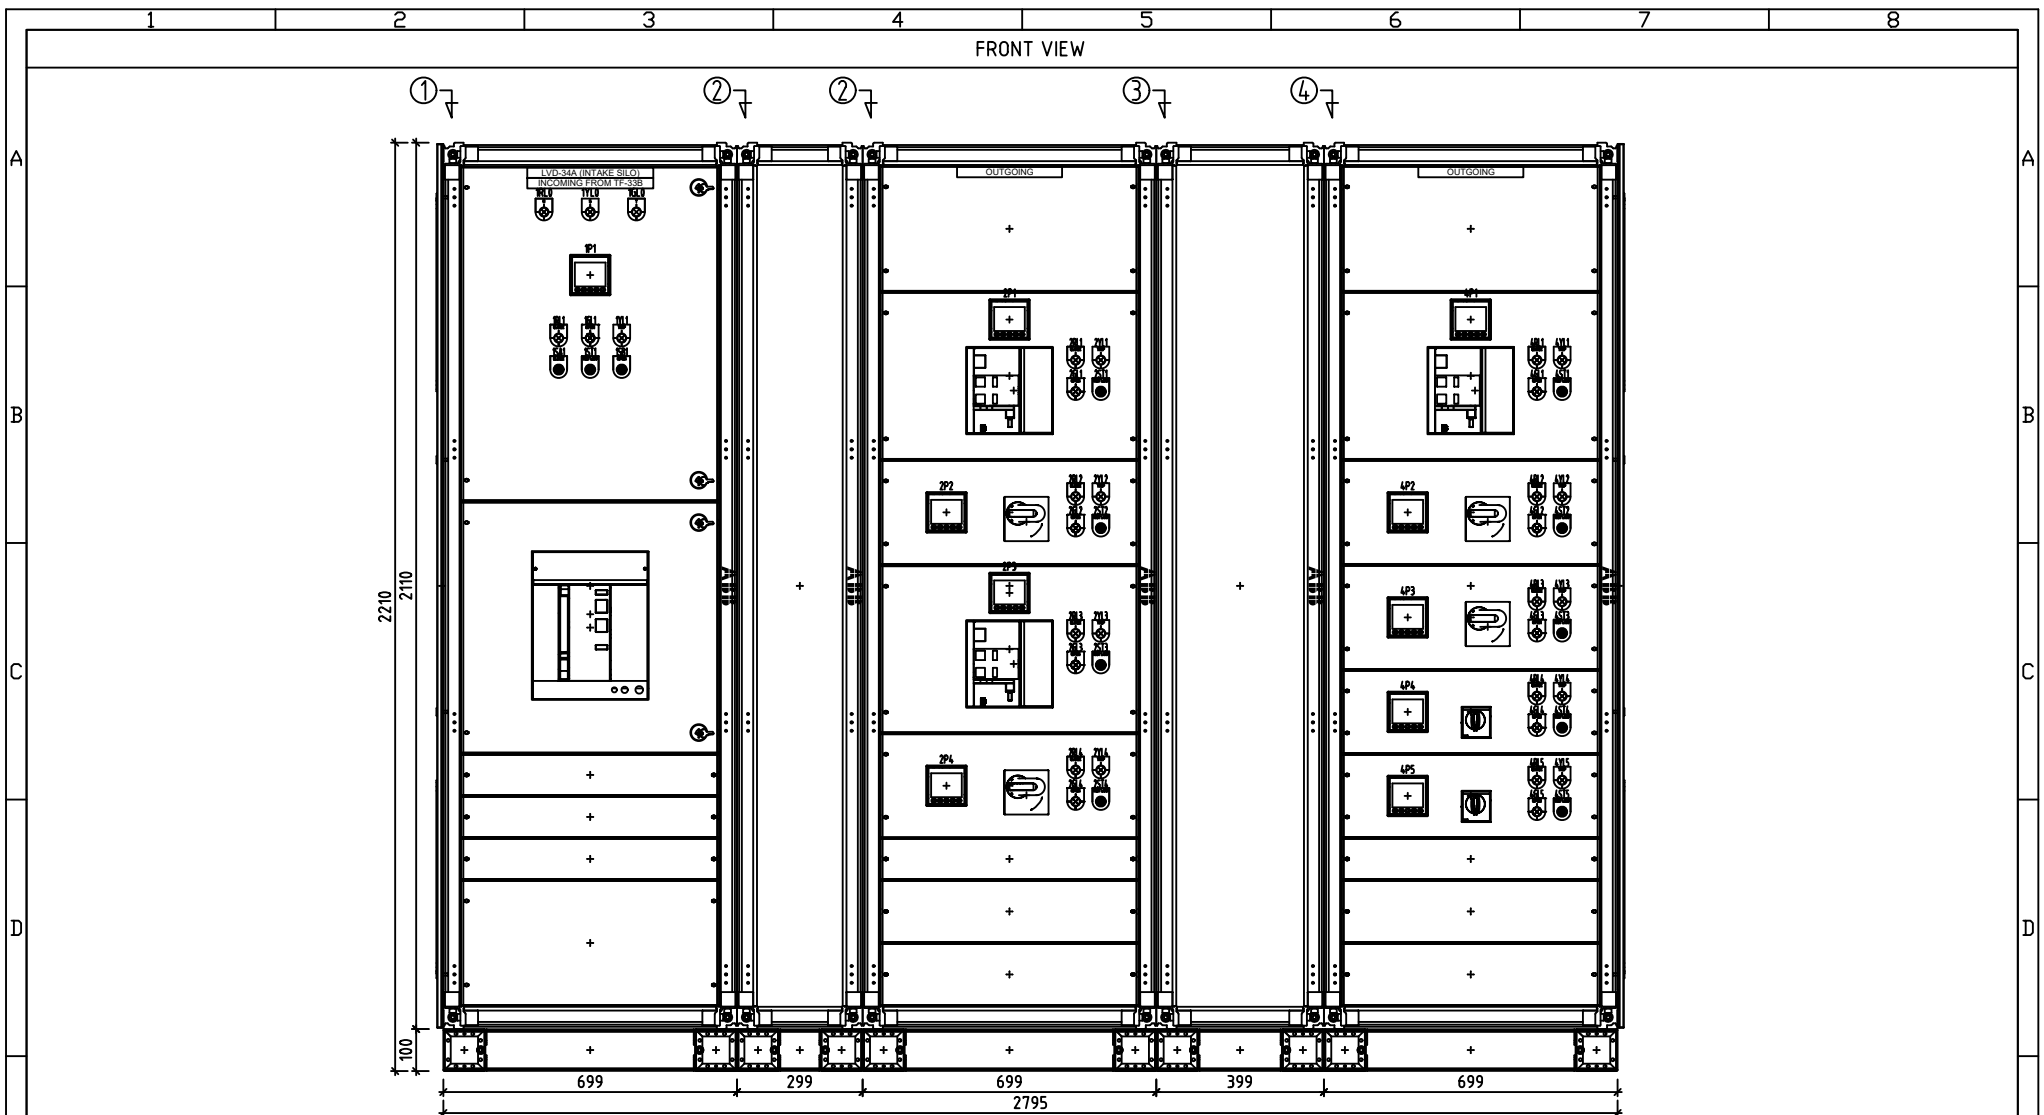



SWITCHBOARD TYPE : INDOOR TYPE, FORM 3b, IP 31, PRO E, ABB
 PLATE THICKNESS : STANDARD PRO E
 PAINTED : GREY - RAL 7035 TEXTURED
 BUSBAR COLORS : PHASE R : BROWN, S : BLACK, T : GREY, N : BLUE, PE : GREEN
 INCOMING FEEDER : FROM THE BOTTOM
 OUTGOING FEEDER : TO THE BOTTOM
 QUANTITY : 1 UNIT


PROJECT :		DRAWING TITLE :		DATE	DRAWN	SIGN	VERIFIED	SIGN	DESCRIPTION	REV	PAGE
WILMAR FLOUR MILL		OUTLINE DRAWING LVD-34A (INTAKE SILO)		07-07-2020	YD		SBR		FOR APPROVAL	1	1
CUSTOMER : PT. ABB SAKTI INDUSTRI		NO DR/JO : DR-017/IND.2020									
		NO DWG. : ABB-003									
		SCALE : 1:18									
		Dimension in mm									

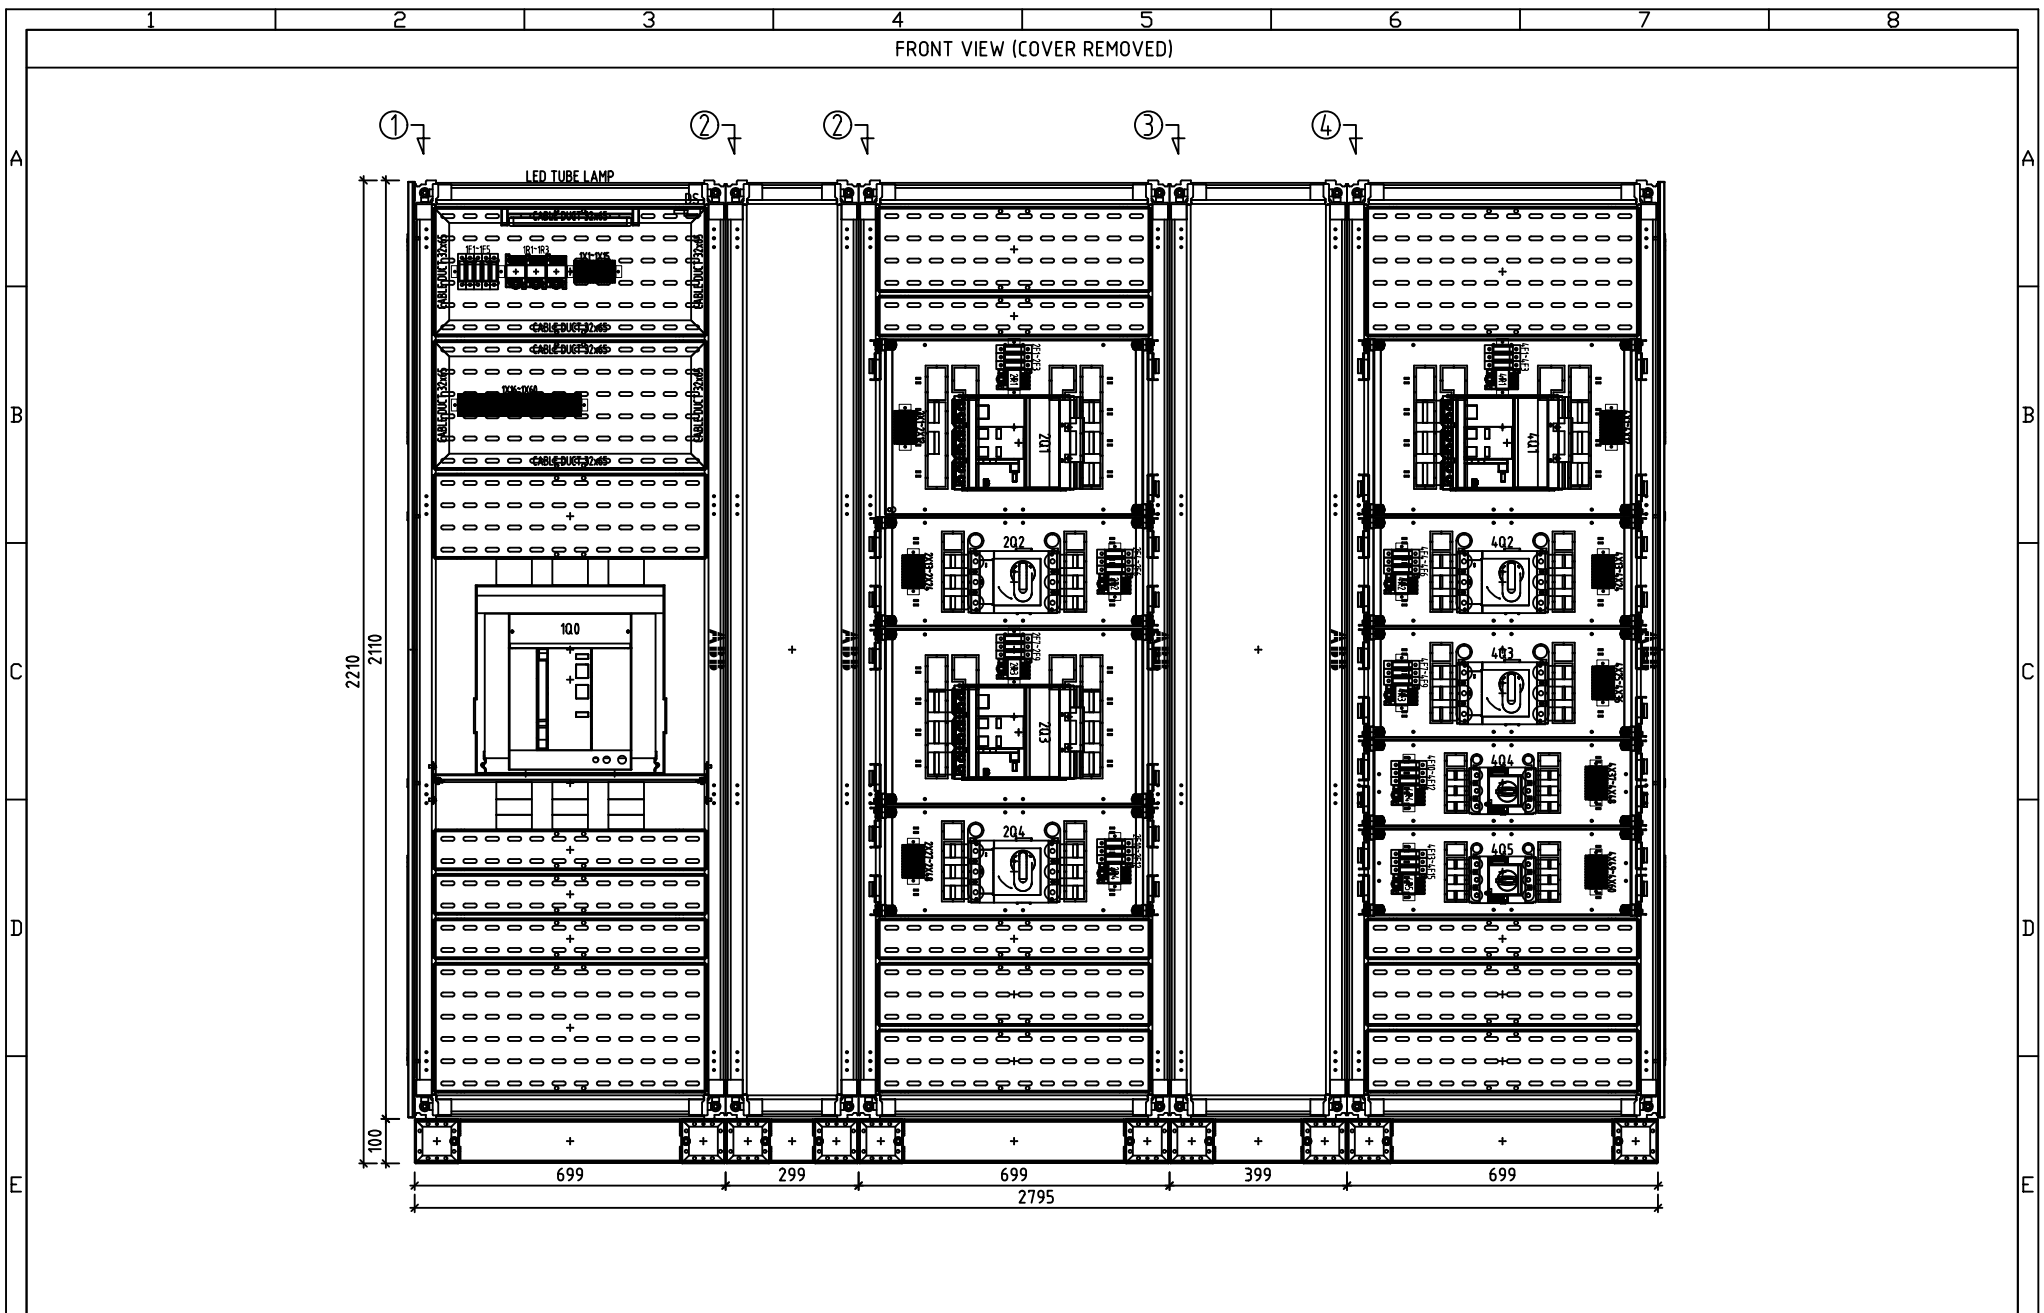


FRONT VIEW (COVER & BLANK PLATE REMOVED)

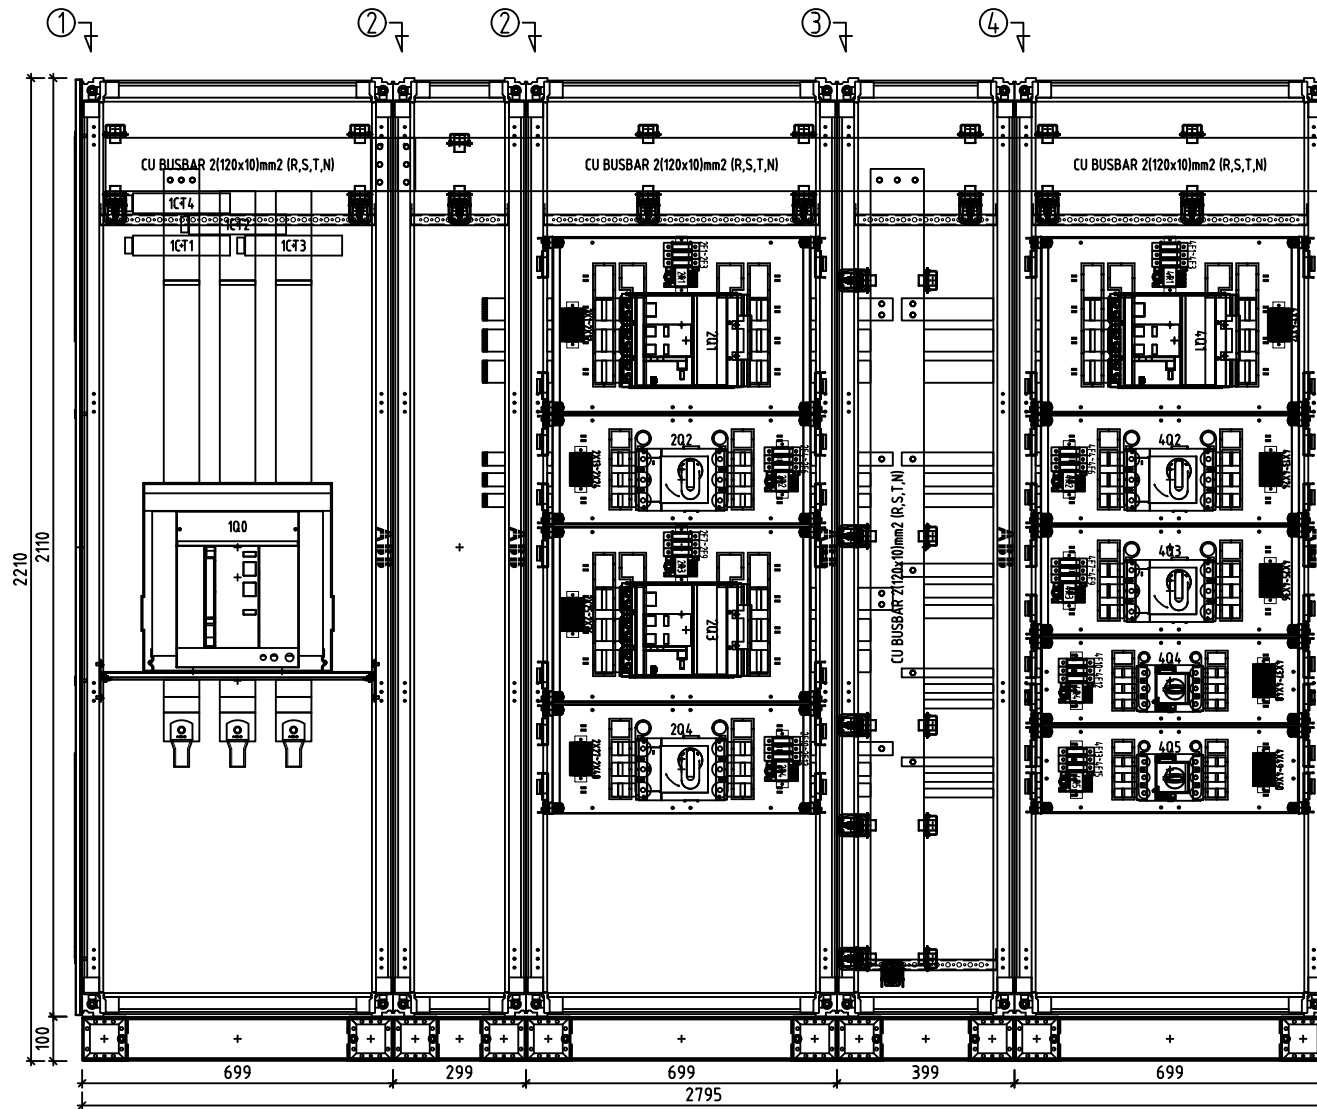

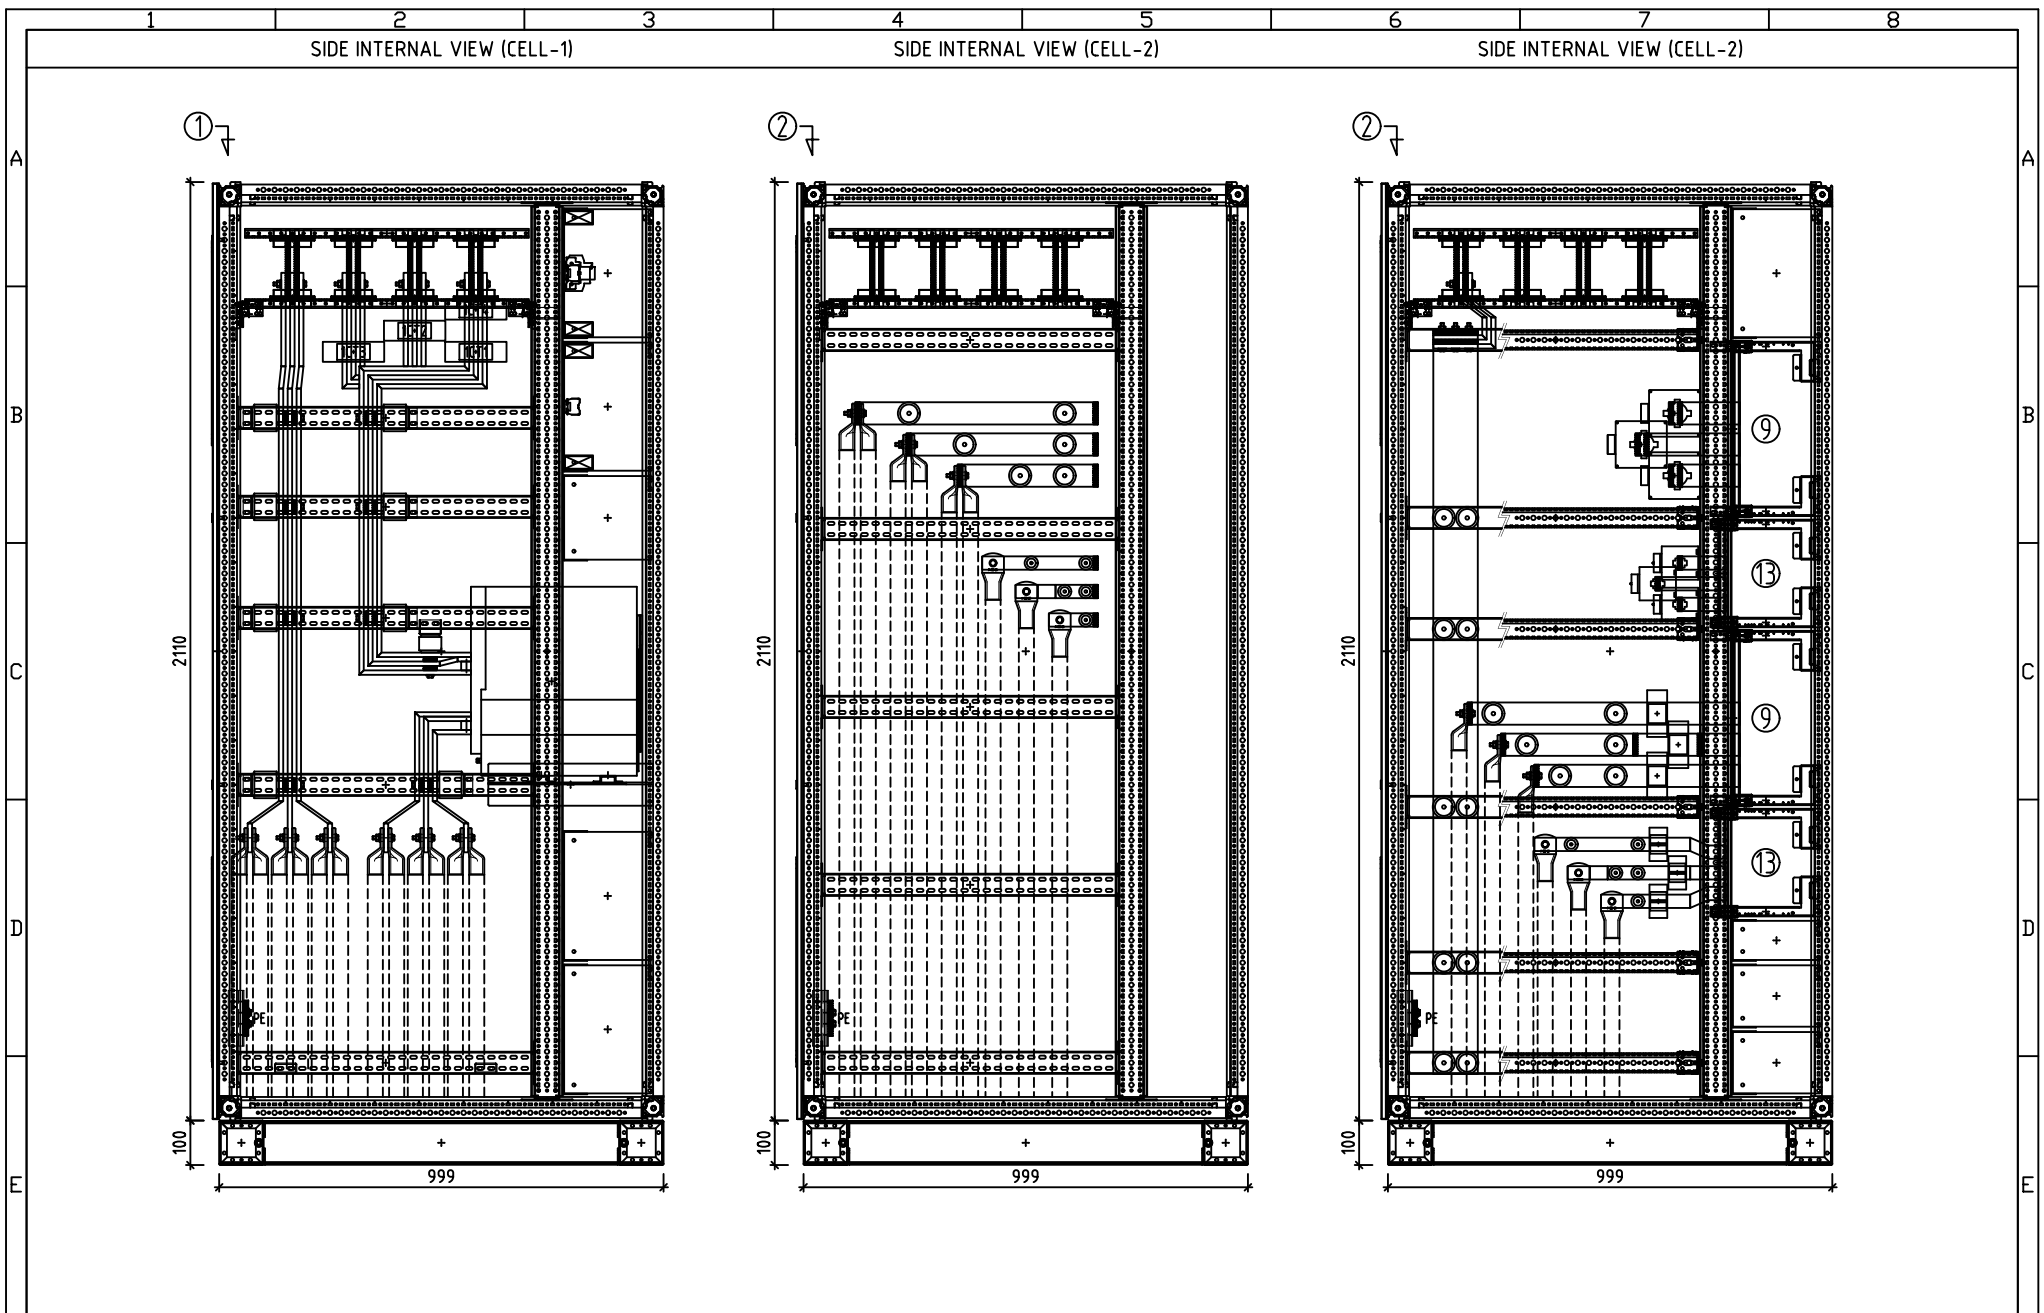


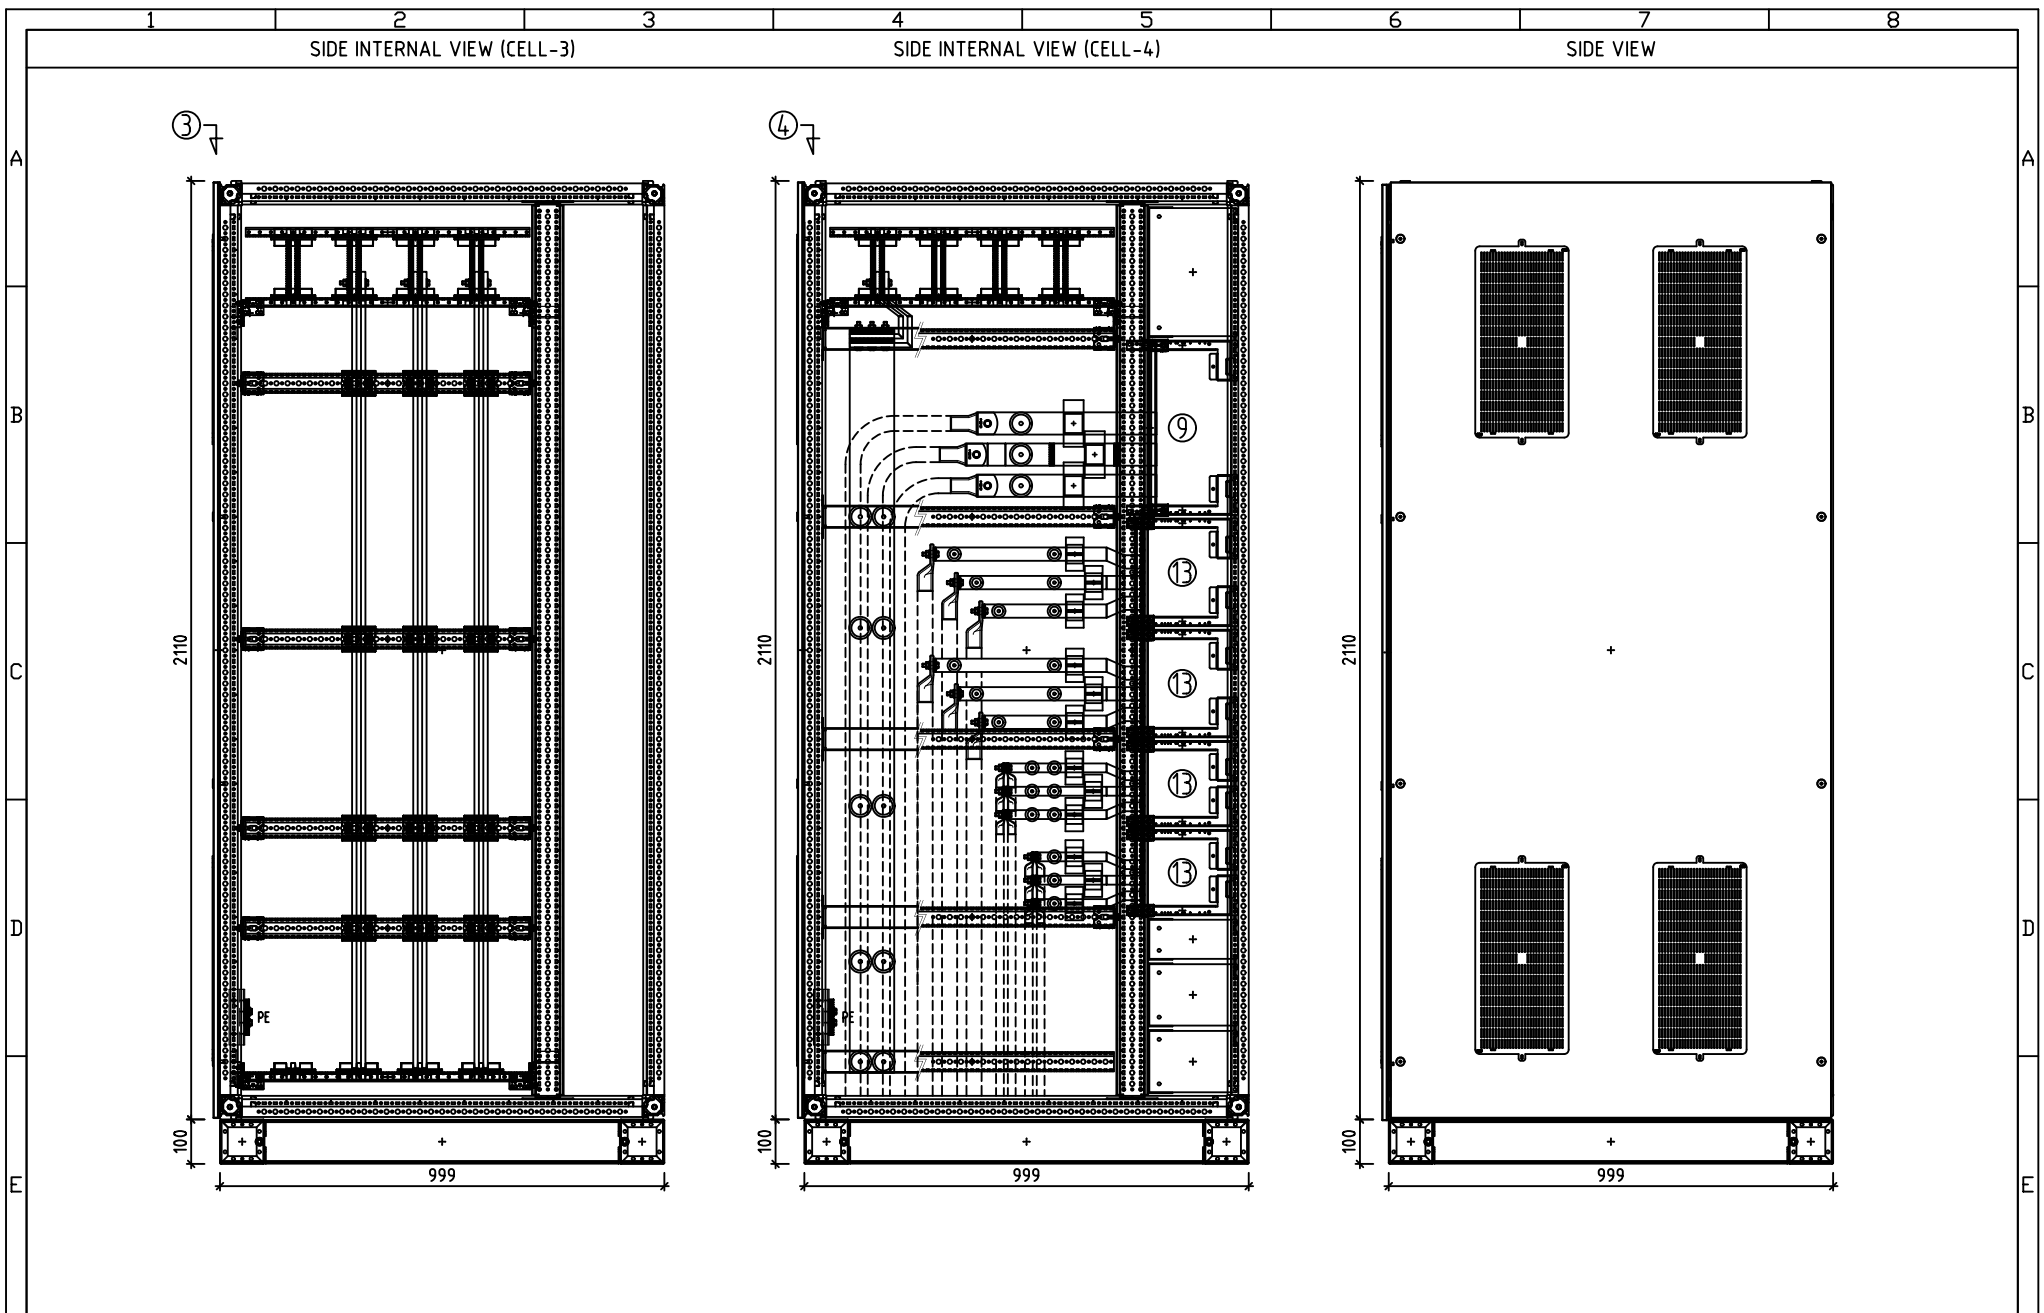


PMElectric Best Value Electrical Solution	PROJECT : WILMAR FLOUR MILL		DRAWING TITLE : OUTLINE DRAWING LVD-34A (INTAKE SILO)		DATE	DRAWN	SIGN	VERIFIED	SIGN	DESCRIPTION	REV	PAGE
	CUSTOMER : PT. ABB SAKTI INDUSTRI		NO DR/JO : DR-017/IND.2020		07-07-2020	YD		SBR		FOR APPROVAL	1	5
			NO DWG. : ABB-003		-	-		-		-	2	
			SCALE : 1:17		-	-		-		-	3	
			Dimension in mm		-	-		-		-	4	10

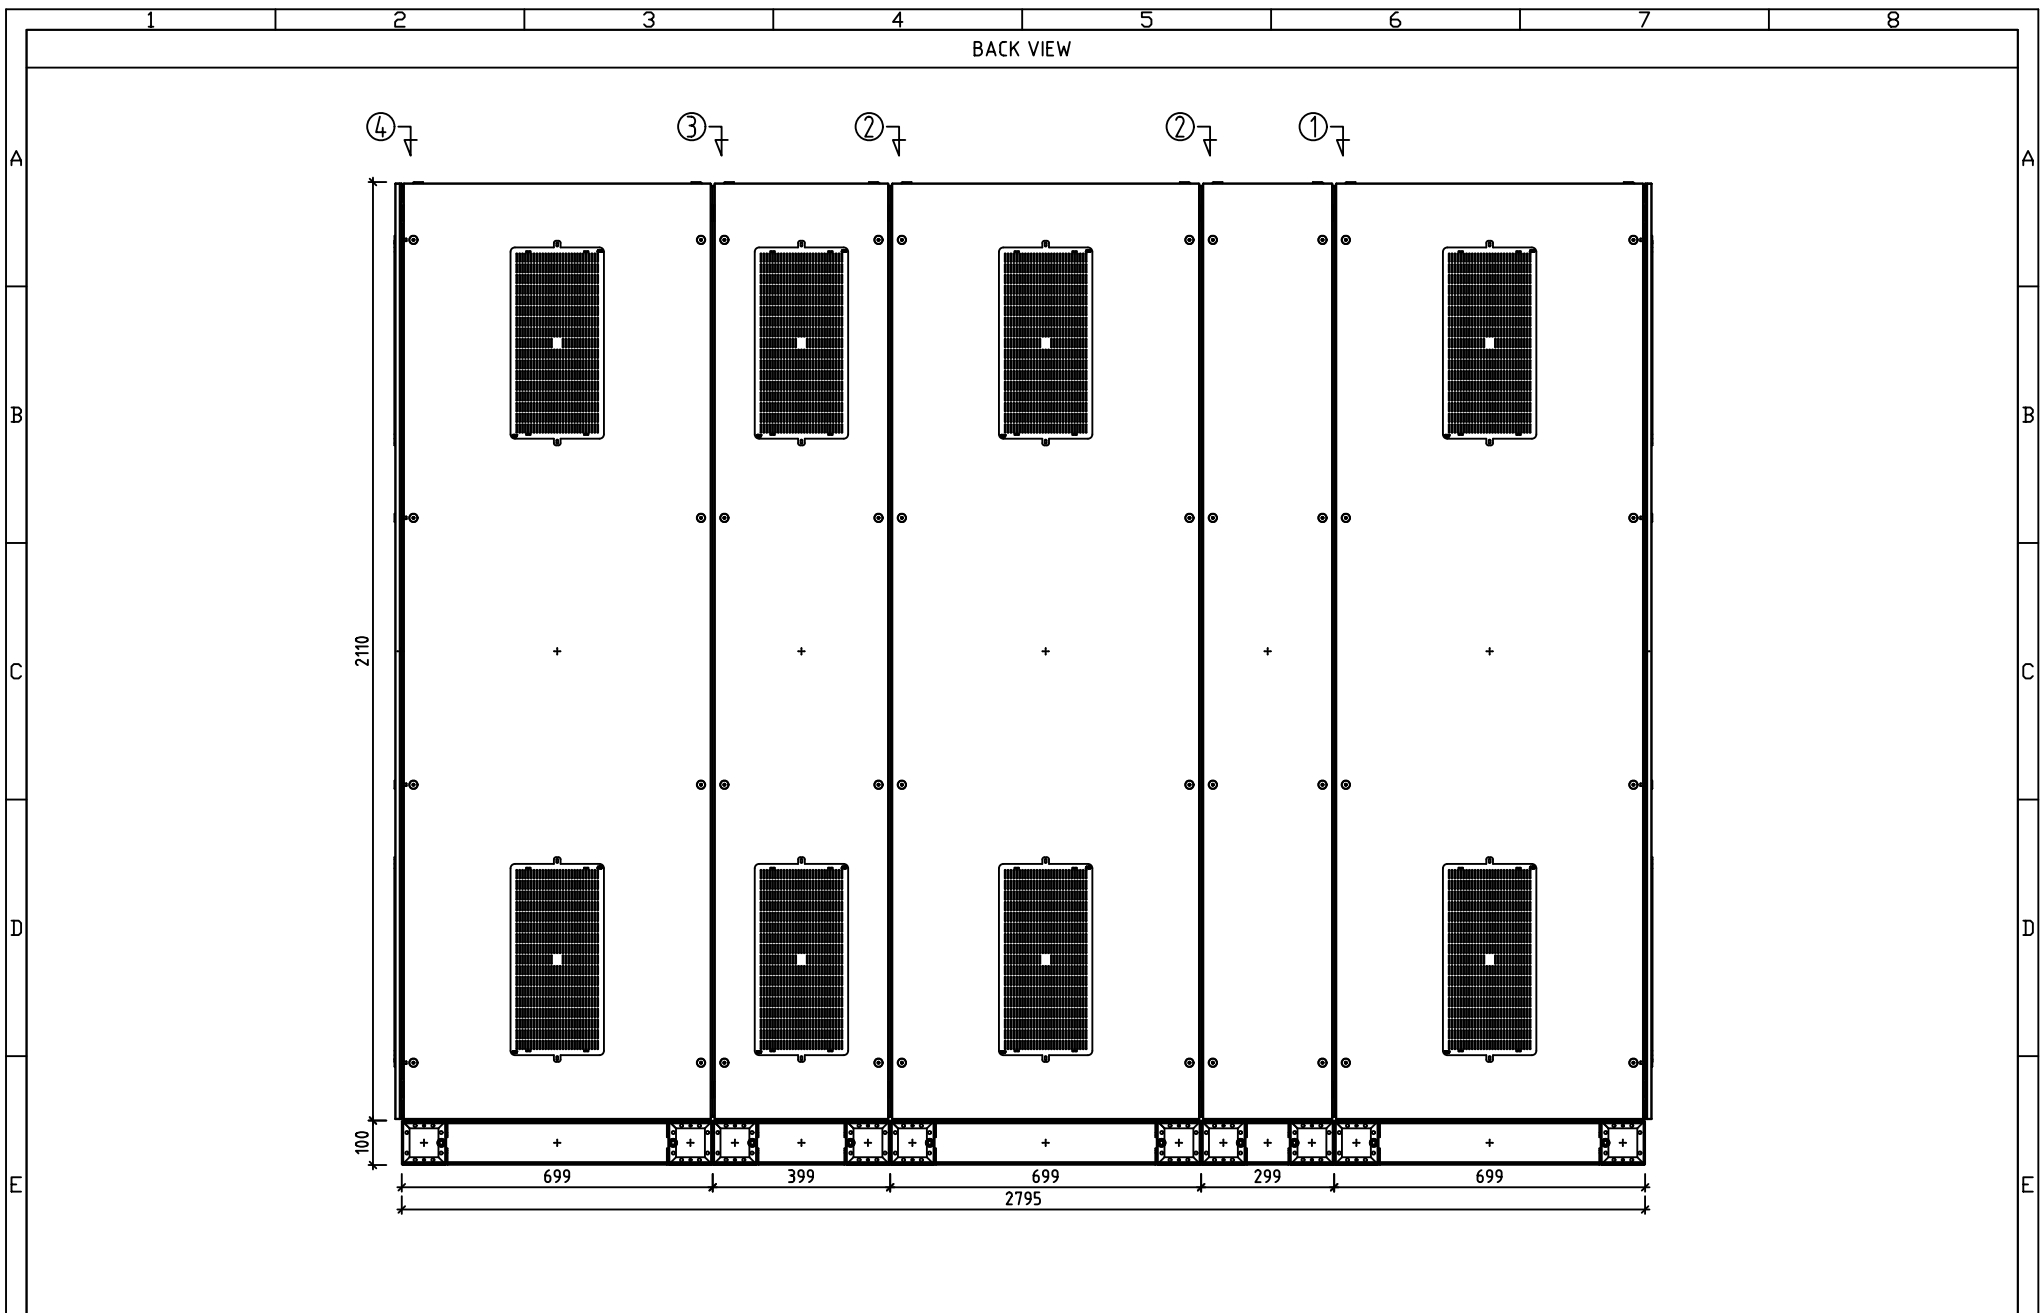



PMElectric Best Value Electrical Solution	PROJECT : WILMAR FLOUR MILL		DRAWING TITLE : OUTLINE DRAWING LVD-34A (INTAKE SILO)		DATE 07-07-2020	DRAWN YD	SIGN	VERIFIED SBR	SIGN	DESCRIPTION FOR APPROVAL	REV	PAGE
	CUSTOMER : PT. ABB SAKTI INDUSTRI		NO DR/JO : DR-017/IND.2020		SCALE : 1:17	-	-	-	-	-	-	6
			NO DWG. : ABB-003		Dimension in mm	-	-	-	-	-	-	10
						-	-	-	-	-	-	
						-	-	-	-	-	-	

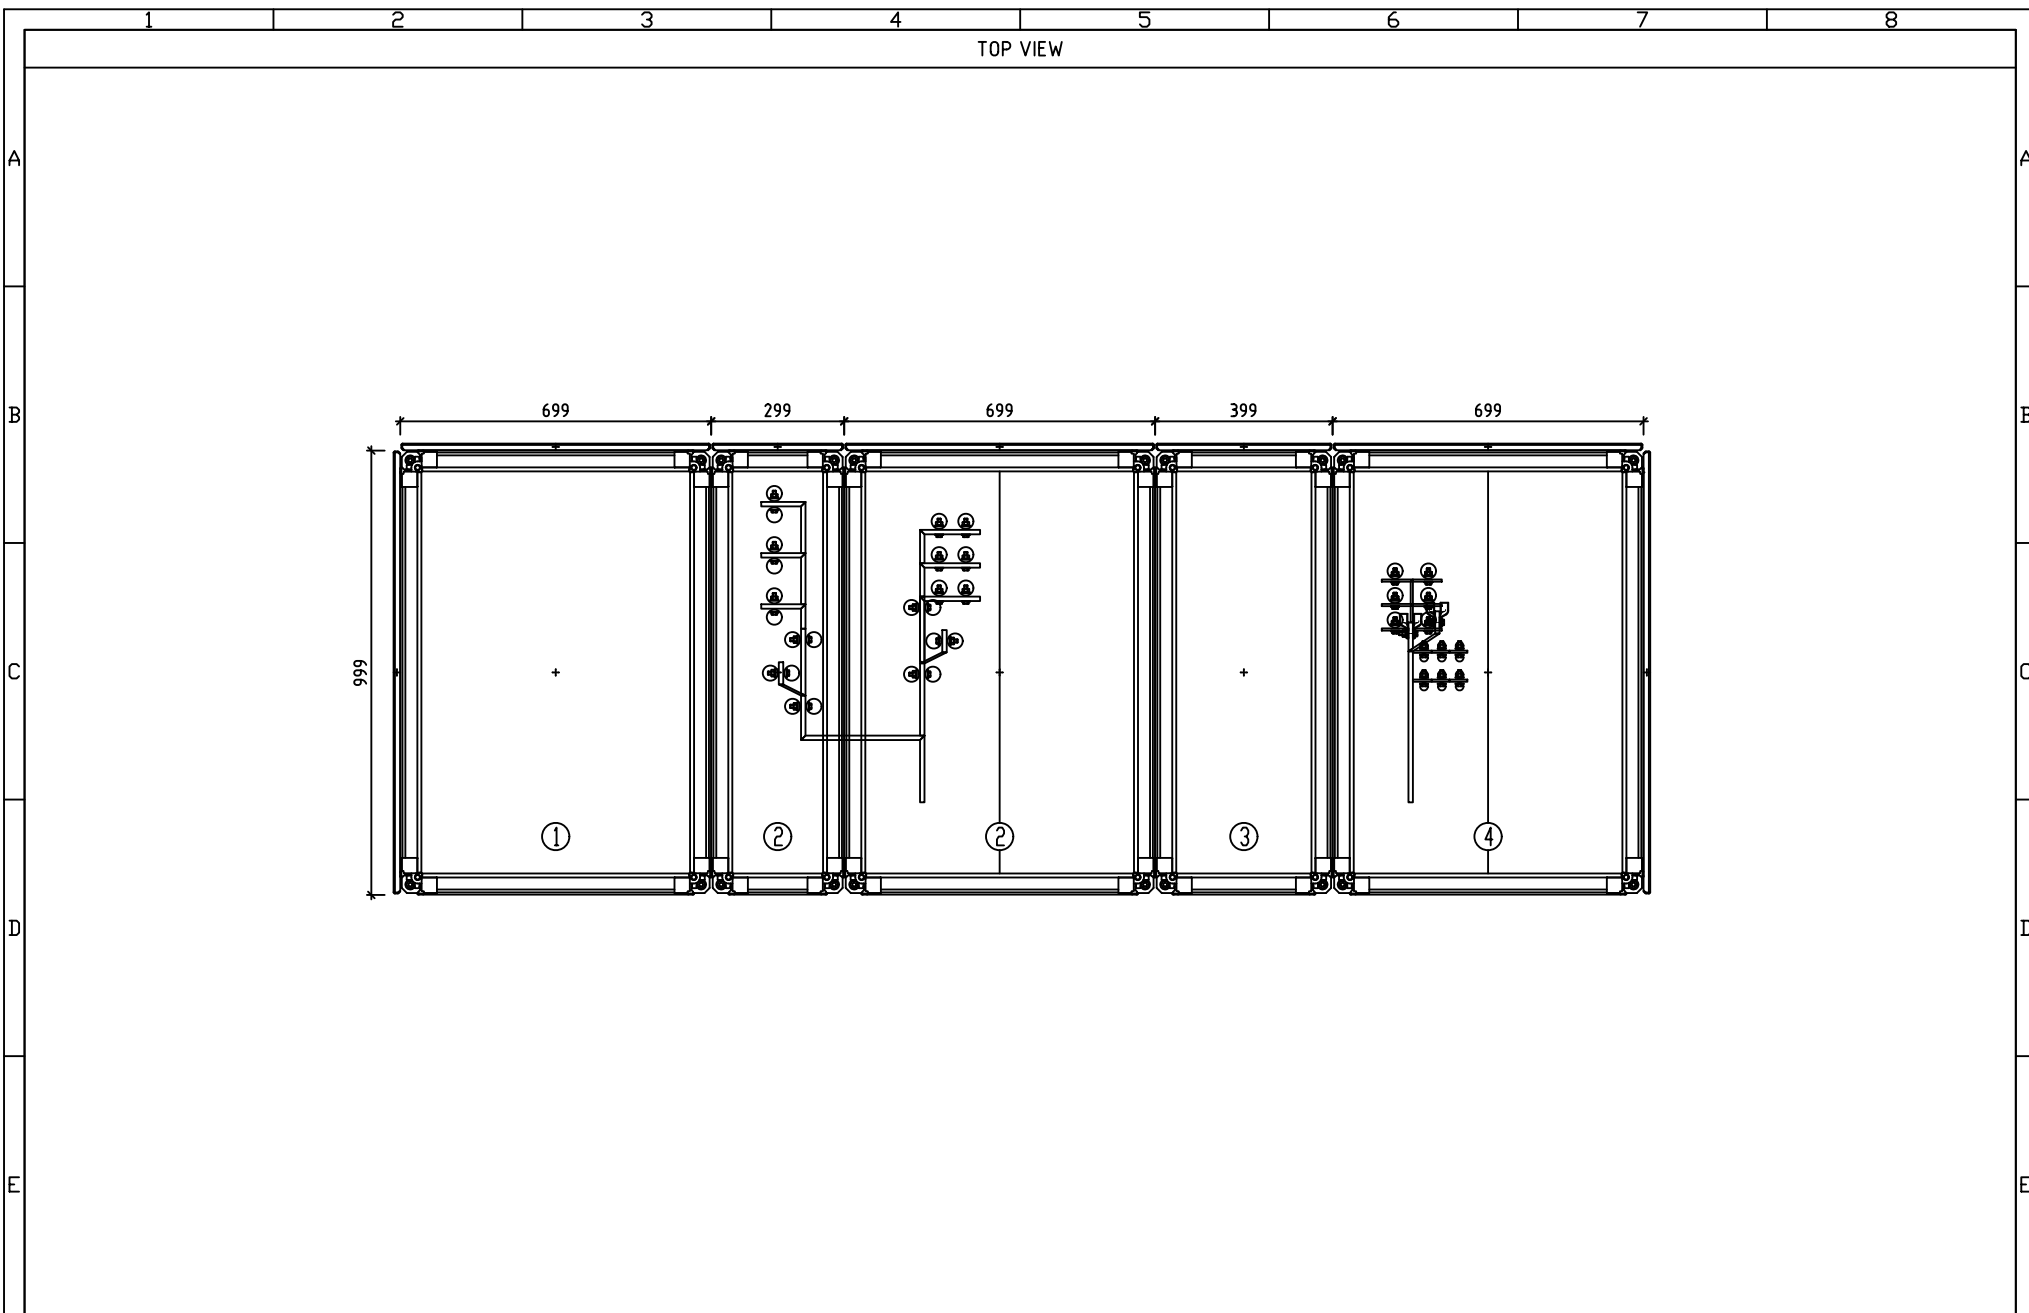

PMElectric Best Value Electrical Solution	PROJECT : WILMAR FLOUR MILL		DRAWING TITLE : OUTLINE DRAWING LVD-34A (INTAKE SILO)		DATE	DRAWN	SIGN	VERIFIED	SIGN	DESCRIPTION	REV	PAGE
	CUSTOMER : PT. ABB SAKTI INDUSTRI		NO DR/JO : DR-017/IND.2020		07-07-2020	YD		SBR		FOR APPROVAL	7	10
			NO DWG. : ABB-003		-	-		-		-		
			SCALE : 1:17		-	-		-		-		
			Dimension in mm		-	-		-		-		

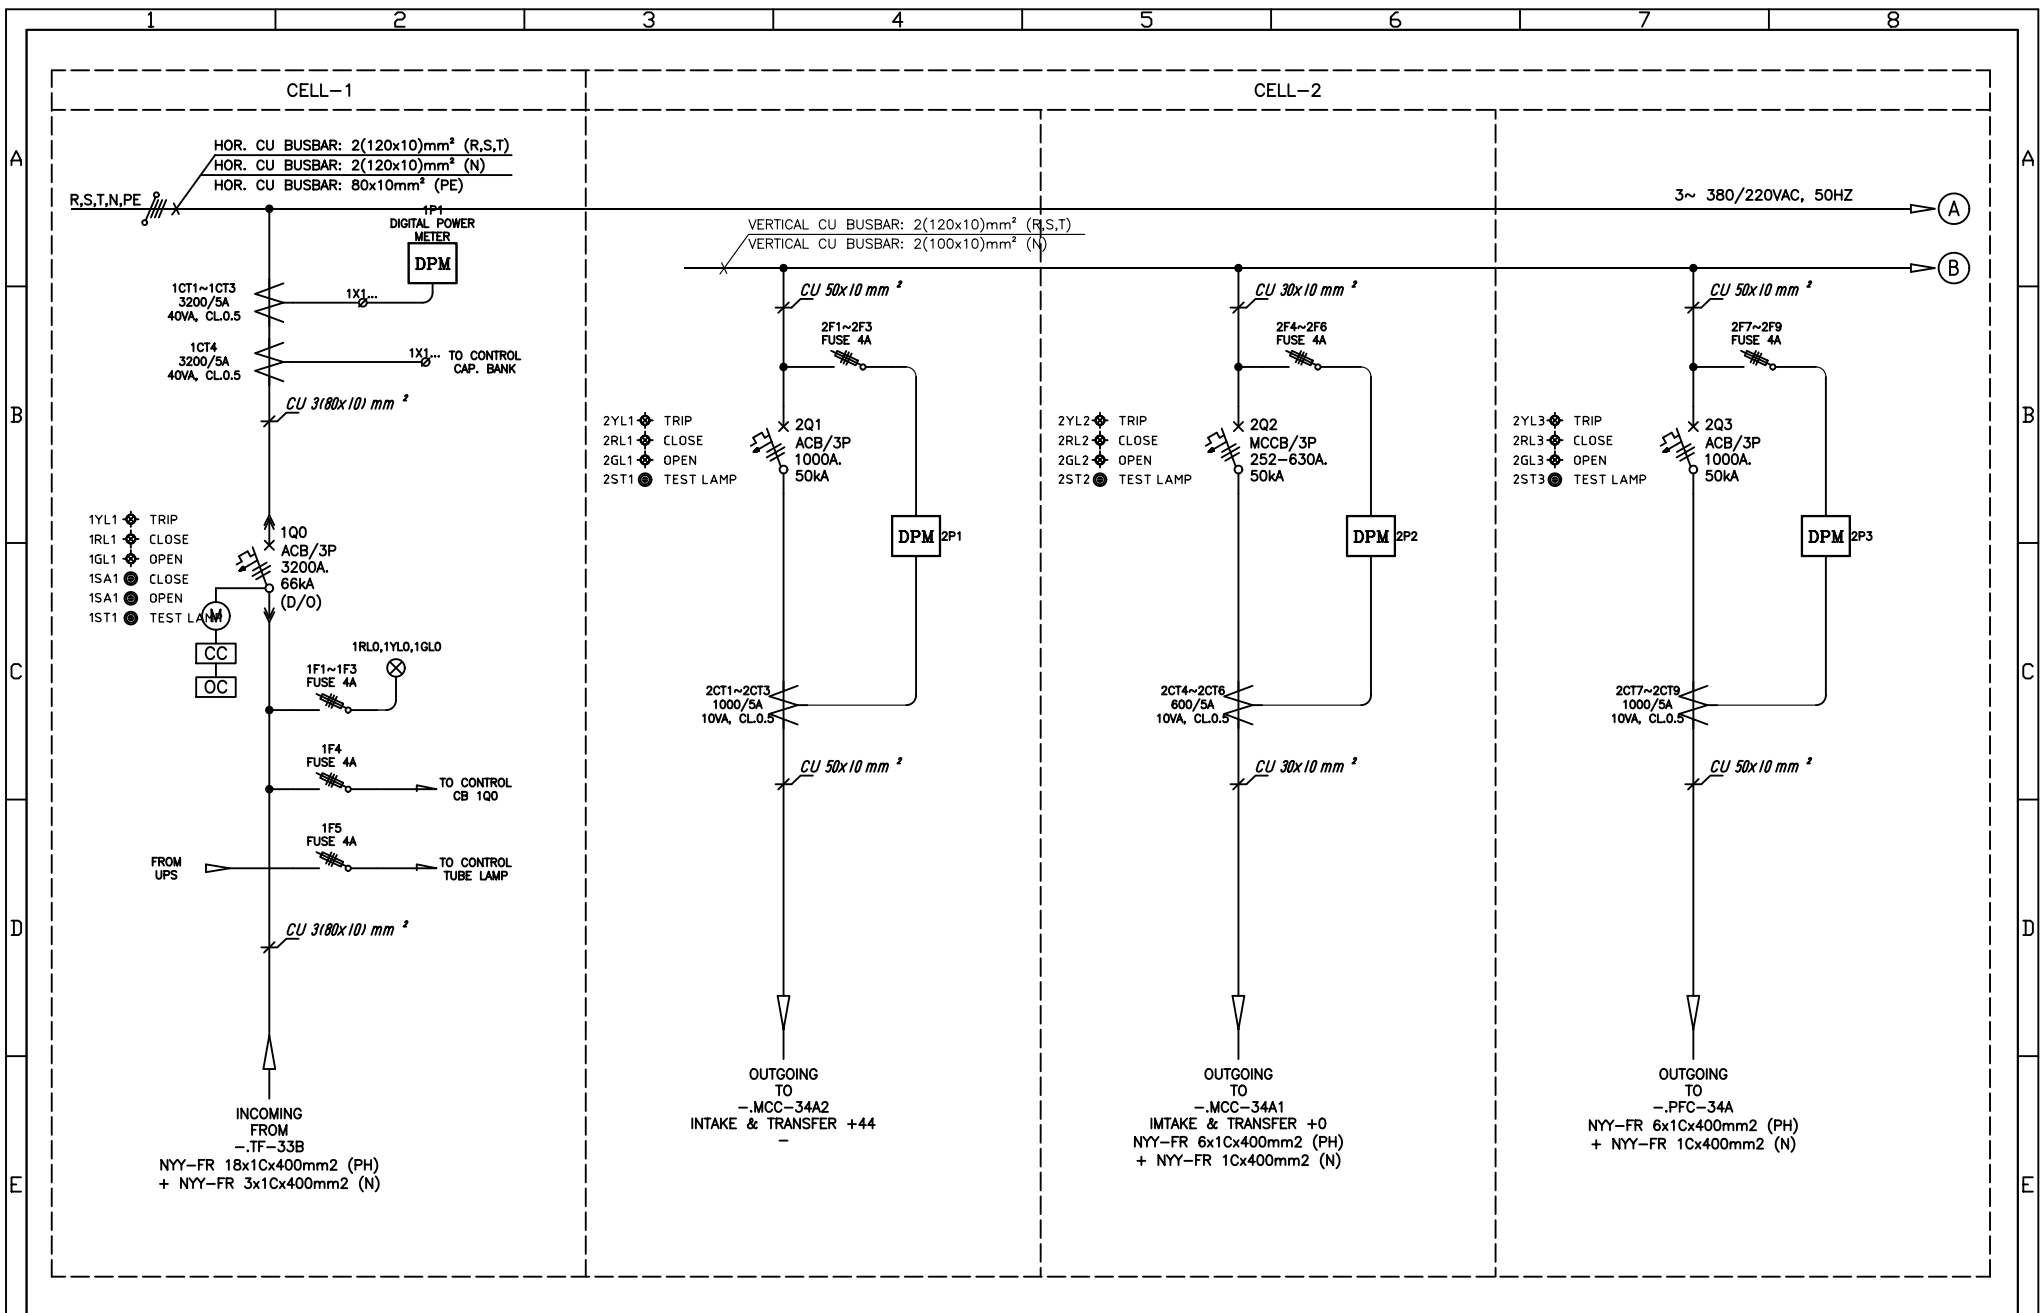

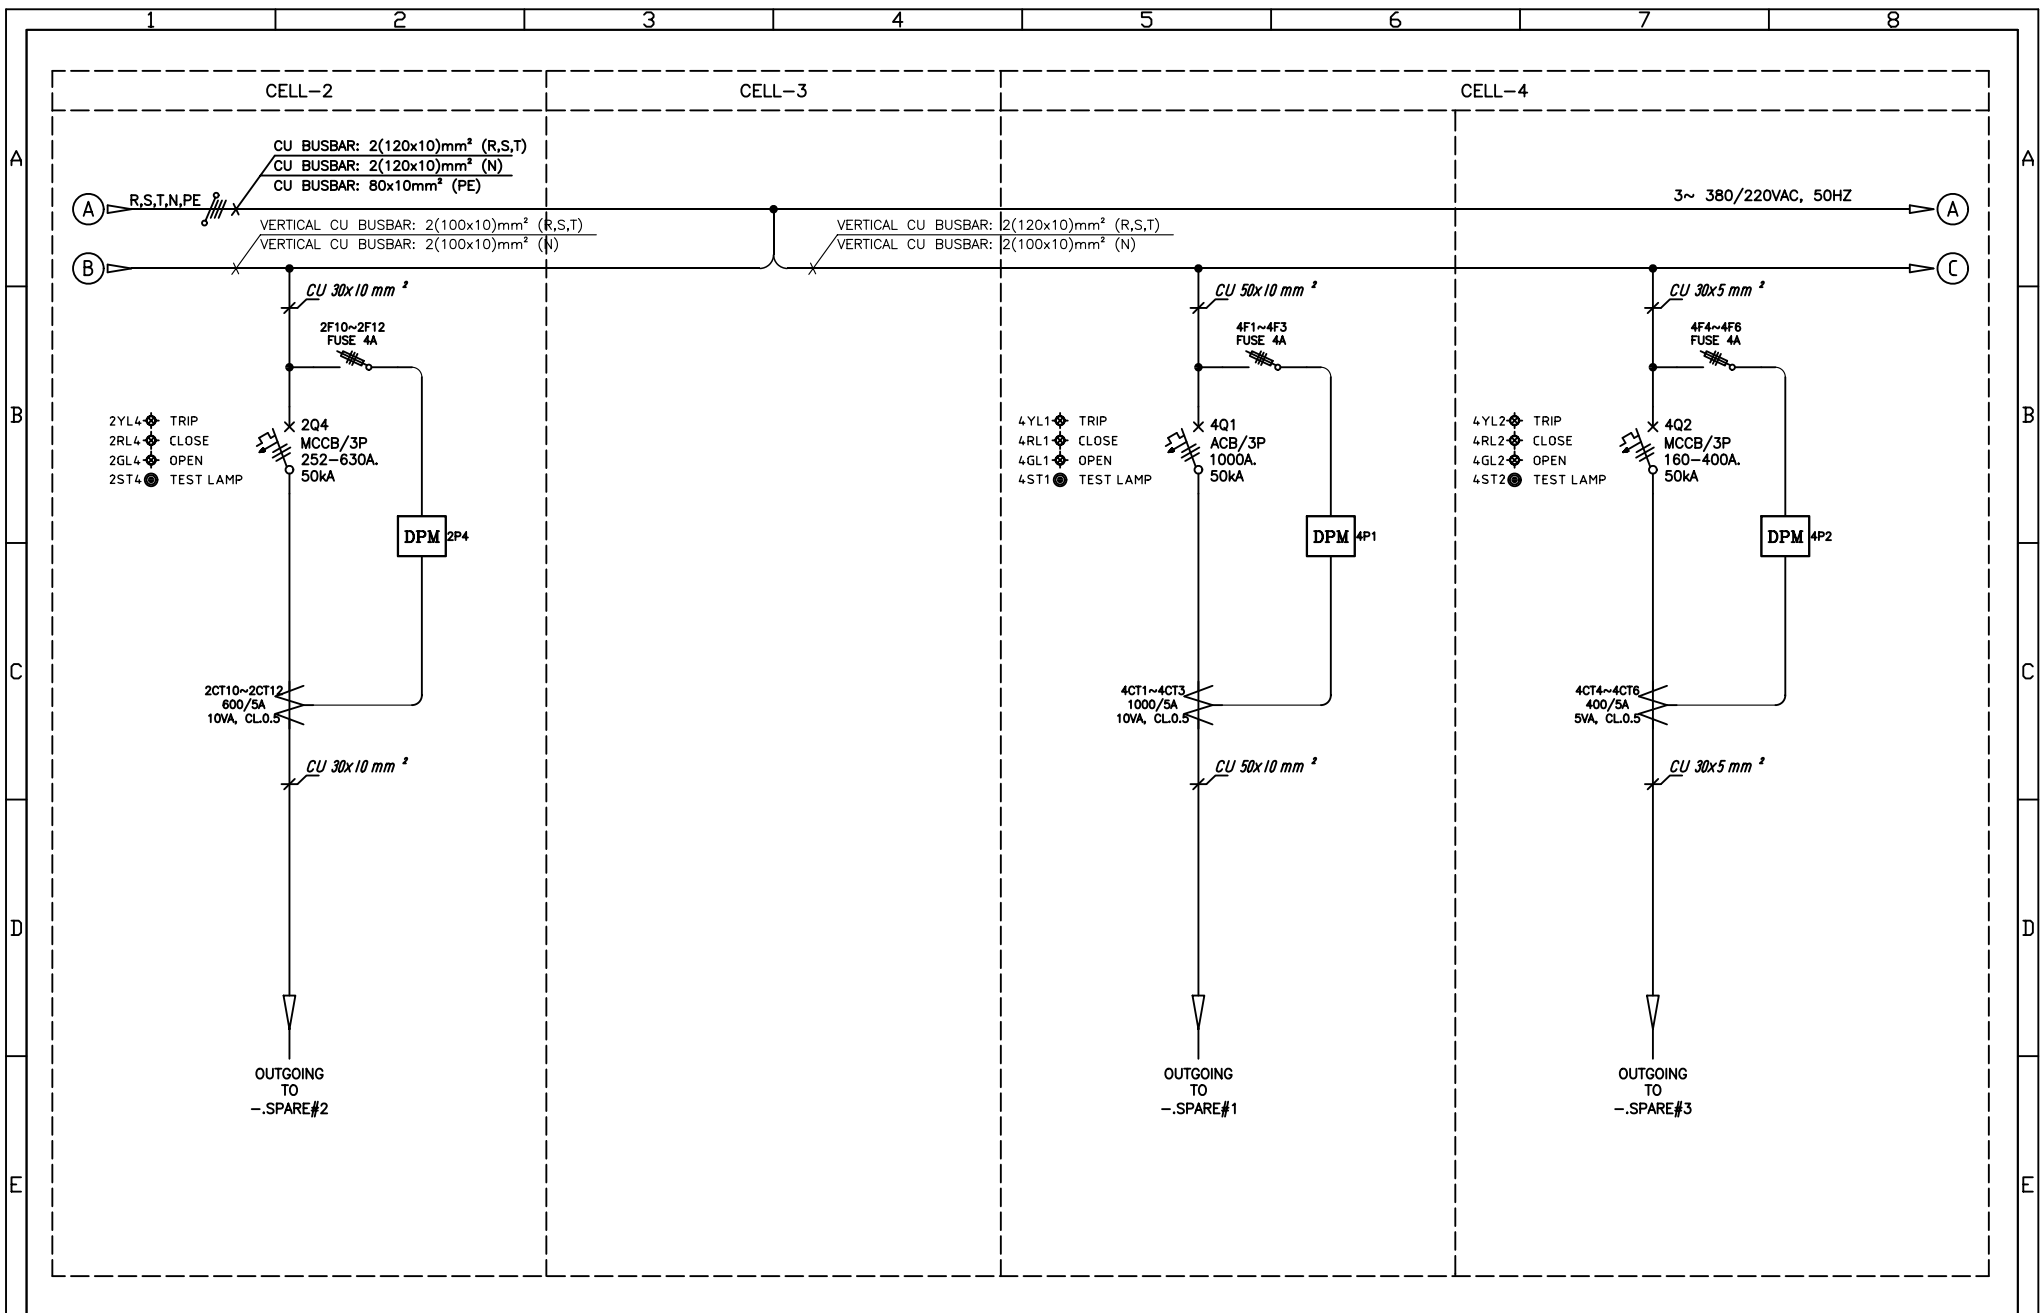

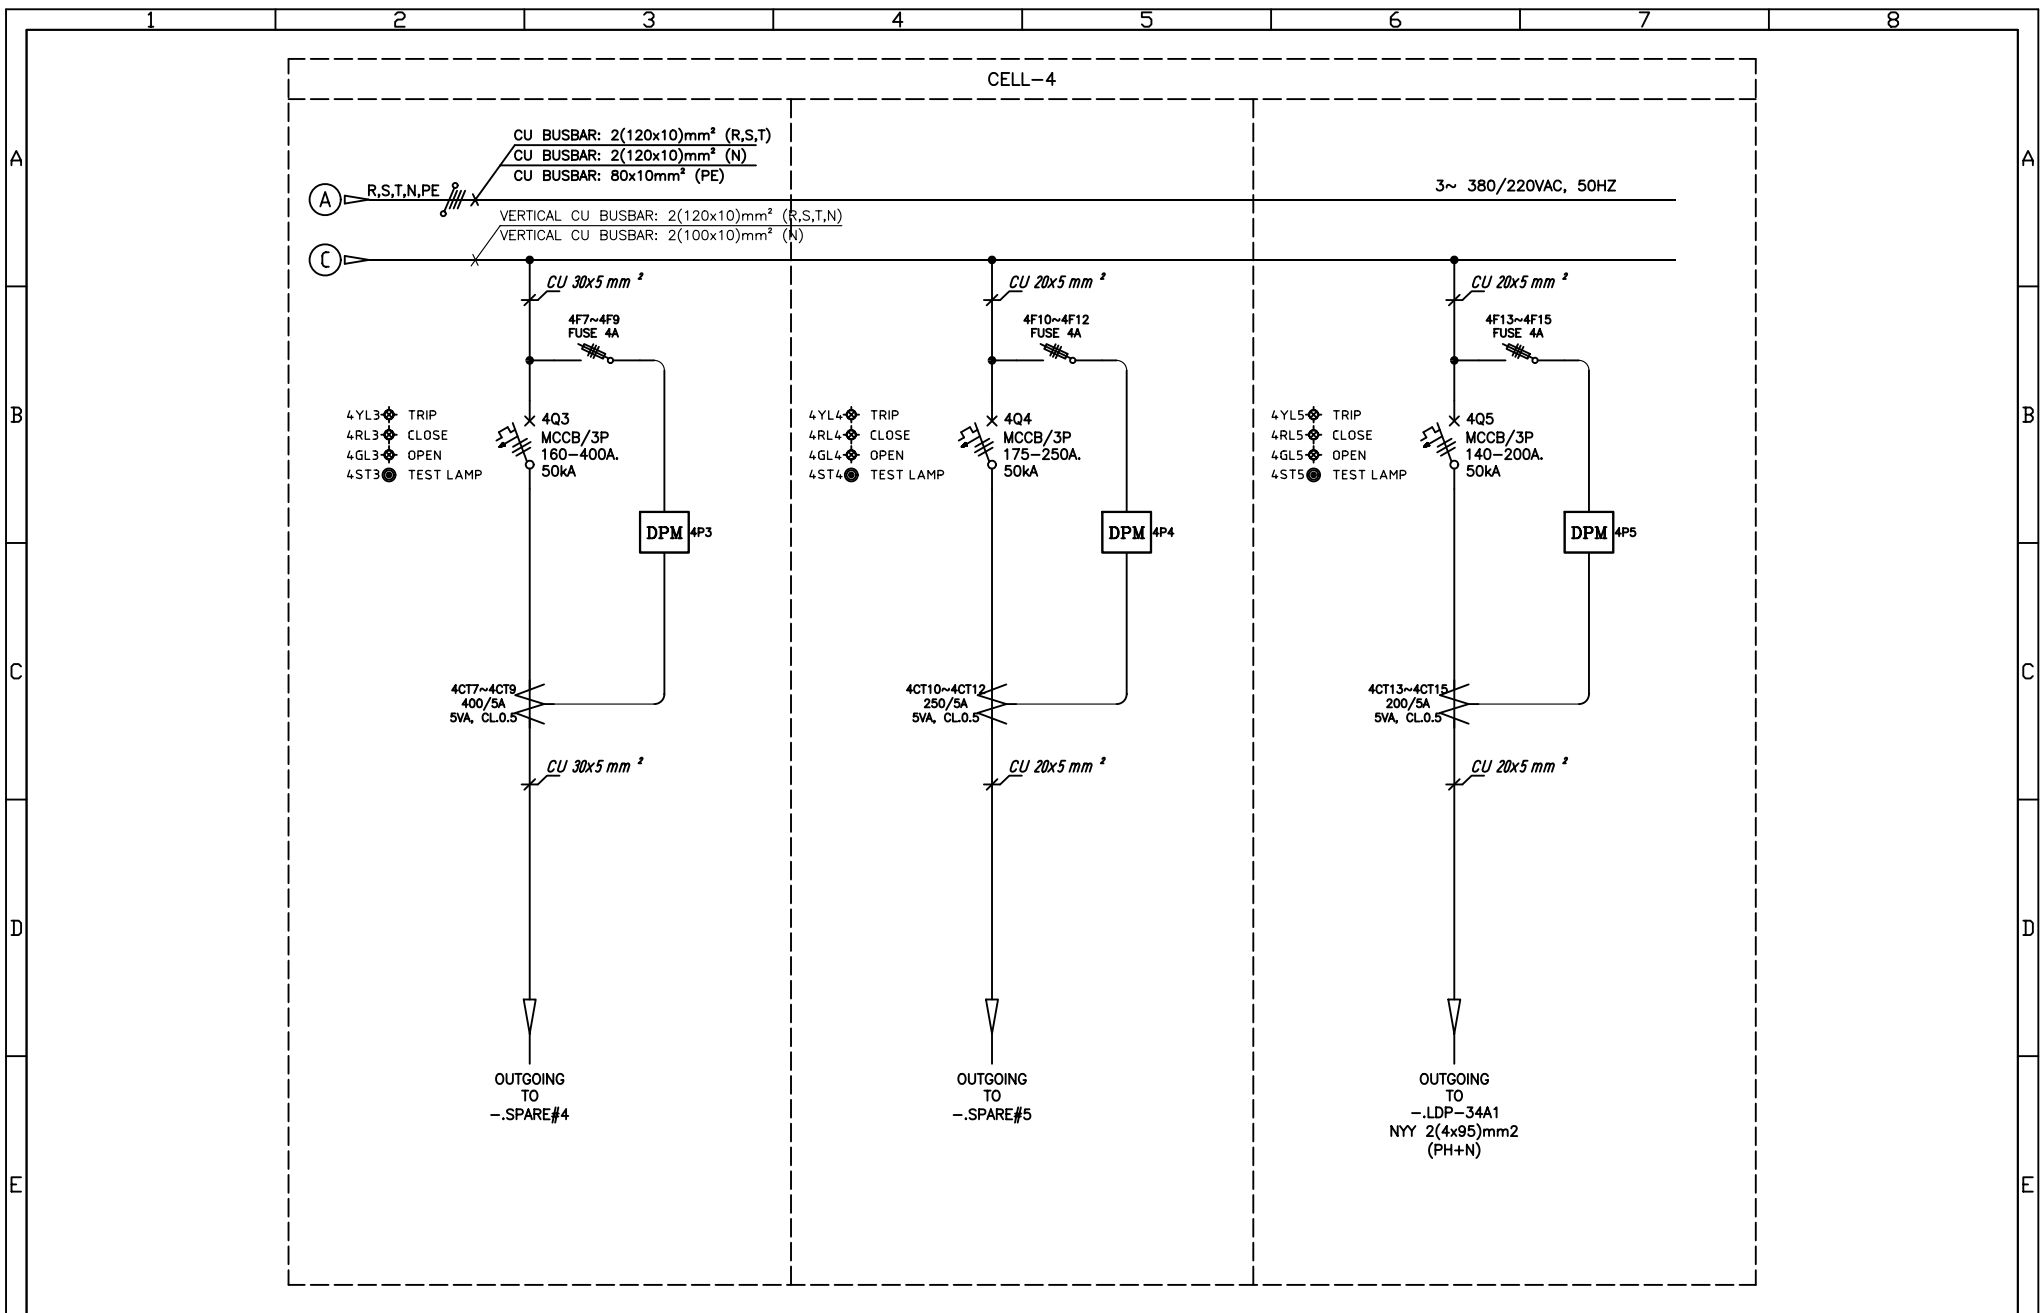

PMElectric Best Value Electrical Solution	PROJECT :	WILMAR FLOUR MILL	DRAWING TITLE :	SINGLE LINE DIAGRAM LVD-34A (INTAKE SILO)	DATE	DRAWN	SIGN	VERIFIED	SIGN	DESCRIPTION	REV	PAGE
	CUSTOMER :	PT. ABB SAKTI INDUSTRI	NO DR/JO : DR-017/IND.2020	SCALE : NTS	07-07-2020	YD		SBR		FOR APPROVAL		10
			NO DWG. : ABB-003	Dimension in mm	-	-		-		-		10
					-	-		-		-		

1	2	3	4	5	6	7	8
NO	CODE	SPECIFICATION	TYPE	BRAND	QTY	UNIT	REMARK
		~ INCOMING SECTION ~					
1	200	ACB 3P 3200A 66KA, D/O, E4.2N32 3200 EKIP DIP/LI	1SDA072491R1	ABB	1	PC	
2	-	EKIP TOUCH/LSIG	-	ABB	1	PC	
3	-	GEARED MOTOR 220-250V AC/DC, M-E2.2/E6.2	1SDA073725R1	ABB	1	PC	
4	-	SHUNT CLOSING RELEASE 220-240V AC/DC, YC E1.2-6.2	1SDA073687R1	ABB	1	PC	
5	-	SHUNT OPENING RELEASE 220-240V AC/DC, YO E1.2-6.2	1SDA073674R1	ABB	1	PC	
6	-	PADLOCK FOR ACB E2.2-E6.2 (TANPA GEMBOK)	1SDA073803R1	ABB	1	PC	
		~ OUTGOING SECTION ~					
7	201,202,401	ACB 3P 1000A 50KA, F/T, E1.2C10 1000 EKIP DIP/LI	1SDA070791R1	ABB	3	PCS	
8	-	EKIP DIP/LSI	1SDA070871R1	ABB	3	PCS	
9	-	PADLOCK FOR ACB E1.2 (TANPA GEMBOK)	1SDA073800R1	ABB	3	PCS	
10	202,204	MCCB 3P 252-630A 50KA, TSS PR22IDS-LS/I-630	1SDA054404R1	ABB	2	PCS	
11	-	RHE NORMAL TRANSMITTED HANDLE, T5, FIXED/PLUGIN	1SDA054929R1	ABB	2	PCS	
12	-	AUXILIARY CONTACT, AUX-C 3Q 1SY 250V AC/DC, T4, T5, T6	1SDA054911R1	ABB	2	PCS	
13	402-403	MCCB 3P 160-400A 50KA, TSS PR22IDS-LS/I-400	1SDA054333R1	ABB	2	PCS	
14	-	RHE NORMAL TRANSMITTED HANDLE, T5, FIXED/PLUGIN	1SDA054929R1	ABB	2	PCS	
15	-	AUXILIARY CONTACT, AUX-C 3Q 1SY 250V AC/DC, T4, T5, T6	1SDA054911R1	ABB	2	PCS	
16	404	MCCB 3P 175-250A 50KA, XT3S TMD-250	1SDA068221R1	ABB	1	PC	
17	-	RHE NORMAL TRANSMITTED HANDLE, XT1/XT3, FIXED/PLUGIN	1SDA066479R1	ABB	1	PC	
18	-	AUXILIARY CONTACT, AUX-C 2Q 1SY 250V AC, XT1,XT2,XT3,XT4	1SDA066433R1	ABB	1	PC	
19	405	MCCB 3P 140-200A 50KA, XT3S TMD-200	1SDA068220R1	ABB	1	PC	
20	-	RHE NORMAL TRANSMITTED HANDLE, XT1/XT3, FIXED/PLUGIN	1SDA066479R1	ABB	1	PC	
21	-	AUXILIARY CONTACT, AUX-C 2Q 1SY 250V AC, XT1,XT2,XT3,XT4	1SDA066433R1	ABB	1	PC	
		~ CONTROL, METERING & PROTECTION SECTION ~					
22	1F1-1F...	FUSE CARTRIDGE 4A + FUSE CARRIER	RT18-32	PM	32	PCS	
23	1RL0-1RL...	PILOT LAMP 220VAC, LED, Ø22.5mm, RED	AD22-22IDS	AXLE/EQ	11	PCS	
24	1YL0-1YL...	PILOT LAMP 220VAC, LED, Ø22.5mm, YELLOW	AD22-22IDS	AXLE/EQ	11	PCS	
25	1GL0-1GL...	PILOT LAMP 220VAC, LED, Ø22.5mm, GREEN	AD22-22IDS	AXLE/EQ	11	PCS	
26	1SA1-1SA...	PUSH BUTTON, 1 C/O, Ø22.5mm, GREEN	AXP-B235	AXLE/EQ	1	PCS	
27	1SB1-1SB...	PUSH BUTTON, 1 C/O, Ø22.5mm, RED	AXP-B245	AXLE/EQ	1	PCS	
28	1ST1-1ST...	PUSH BUTTON FLUSH, 1 N/O, Ø22mm, BLACK	YW1B-ME10B	IDEC/EQ	10	PCS	
29	1P1-1P...	DIGITAL POWER METER,MODBUS ETHERNET TCP/IP, M4M20ETHERNET	2CSG204471R4051	ABB	10	PCS	
30	1CT1-1CT...	CURRENT TRANSFORMER 200/5A, 5VA, CLASS 0.5, 31.5x11mm	HG30-200	HOWIG/EQ	3	PCS	
31	1CT1-1CT...	CURRENT TRANSFORMER 250/5A, 5VA, CLASS 0.5, 31.5x11mm	HG30-250	HOWIG/EQ	3	PCS	
32	1CT1-1CT...	CURRENT TRANSFORMER 400/5A, 5VA, CLASS 0.5, 42x11mm	HG40-400	HOWIG/EQ	6	PCS	
33	1CT1-1CT...	CURRENT TRANSFORMER 600/5A, 10VA, CLASS 0.5, 51x16mm	HG50-600	HOWIG/EQ	6	PCS	
34	1CT1-1CT...	CURRENT TRANSFORMER 1000/5A, 10VA, CLASS 0.5, 82x32.5mm	HG82-1000	HOWIG/EQ	9	PCS	
35	1CT1-1CT...	CURRENT TRANSFORMER 3200/5A, 40VA, CLASS 0.5, 126x36mm	HG120-3200	HOWIG/EQ	4	PCS	
36	1R1-1R...	RELAY 4-CO 10A 220VAC + SOCKET	LY4 + PTF14A-E	QMRON	12	PCS	
37	1X1-1X...	TERMINAL BLOCK, 4mm, 32A, ZS4	1SNK505010R0000	ENTRELEC	175	PCS	
38	-	END SECTION FOR ZS4-ZS25, ES4	1SNK505910R0000	ENTRELEC	20	PCS	
39	-	END STOPER, BM3	1SNK900001R0000	ENTRELEC	40	PCS	
40	DS	LIMIT SWITCH SINGLE POLE 1-CO	-	IMPORT	1	PC	
41	TUBE LAMP	TUBULAR LAMP LED 4W, 220VAC	31099	PHILIPS	1	PC	
42	-	WIRING & ACCESORIES (CABLE C/W FLAME RETARDANT INSULATION)	PM	LOCAL	1	LOT	
43	-	CU BUSBAR C/W FLAME RETARDANT INSULATION	PREMIUM	EX-IMPORT	1	LOT	
44	-	BOX PANEL UK: 2200(H) X 300(W) X 1000(D)mm ²	PRO E	ABB	1	UNIT	
45	-	BOX PANEL UK: 2200(H) X 400(W) X 1000(D)mm ²	PRO E	ABB	1	UNIT	
46	-	BOX PANEL UK: 2200(H) X 700(W) X 1000(D)mm ²	PRO E	ABB	3	UNIT	
47							
48							
49							
50							

1		2		3		4		5		6		7		8						
 PMElectric Best Value Electrical Solution				PROJECT :		WILMAR FLOUR MILL		DRAWING TITLE :		PART LIST COMPONENT LVD-34A (INTAKE SILO)		DATE	DRAWN	SIGN	VERIFIED	SIGN	DESCRIPTION	REV	PAGE	
												07-07-2020	YD			SBR		FOR APPROVAL		11
												-	-			-		-		
												-	-			-		-		
												-	-			-		-		
				CUSTOMER :		PT. ABB SAKTI INDUSTRI		NO DR/JO : DR-017/IND.2020		SCALE : NTS		-	-	-	-	-	-		10	
								NO DWG. : ABB-003		Dimension in mm		-	-	-	-	-	-			