




WE RESERVE ALL RIGHTS IN THIS DOCUMENT AND IN THE INFORMATION CONTAINED THEREIN. REPRODUCTION, USE OR DISCLOSURE TO THIRD PARTIES WITHOUT EXPRESS AUTHORITY IS STRICTLY FORBIDDEN.

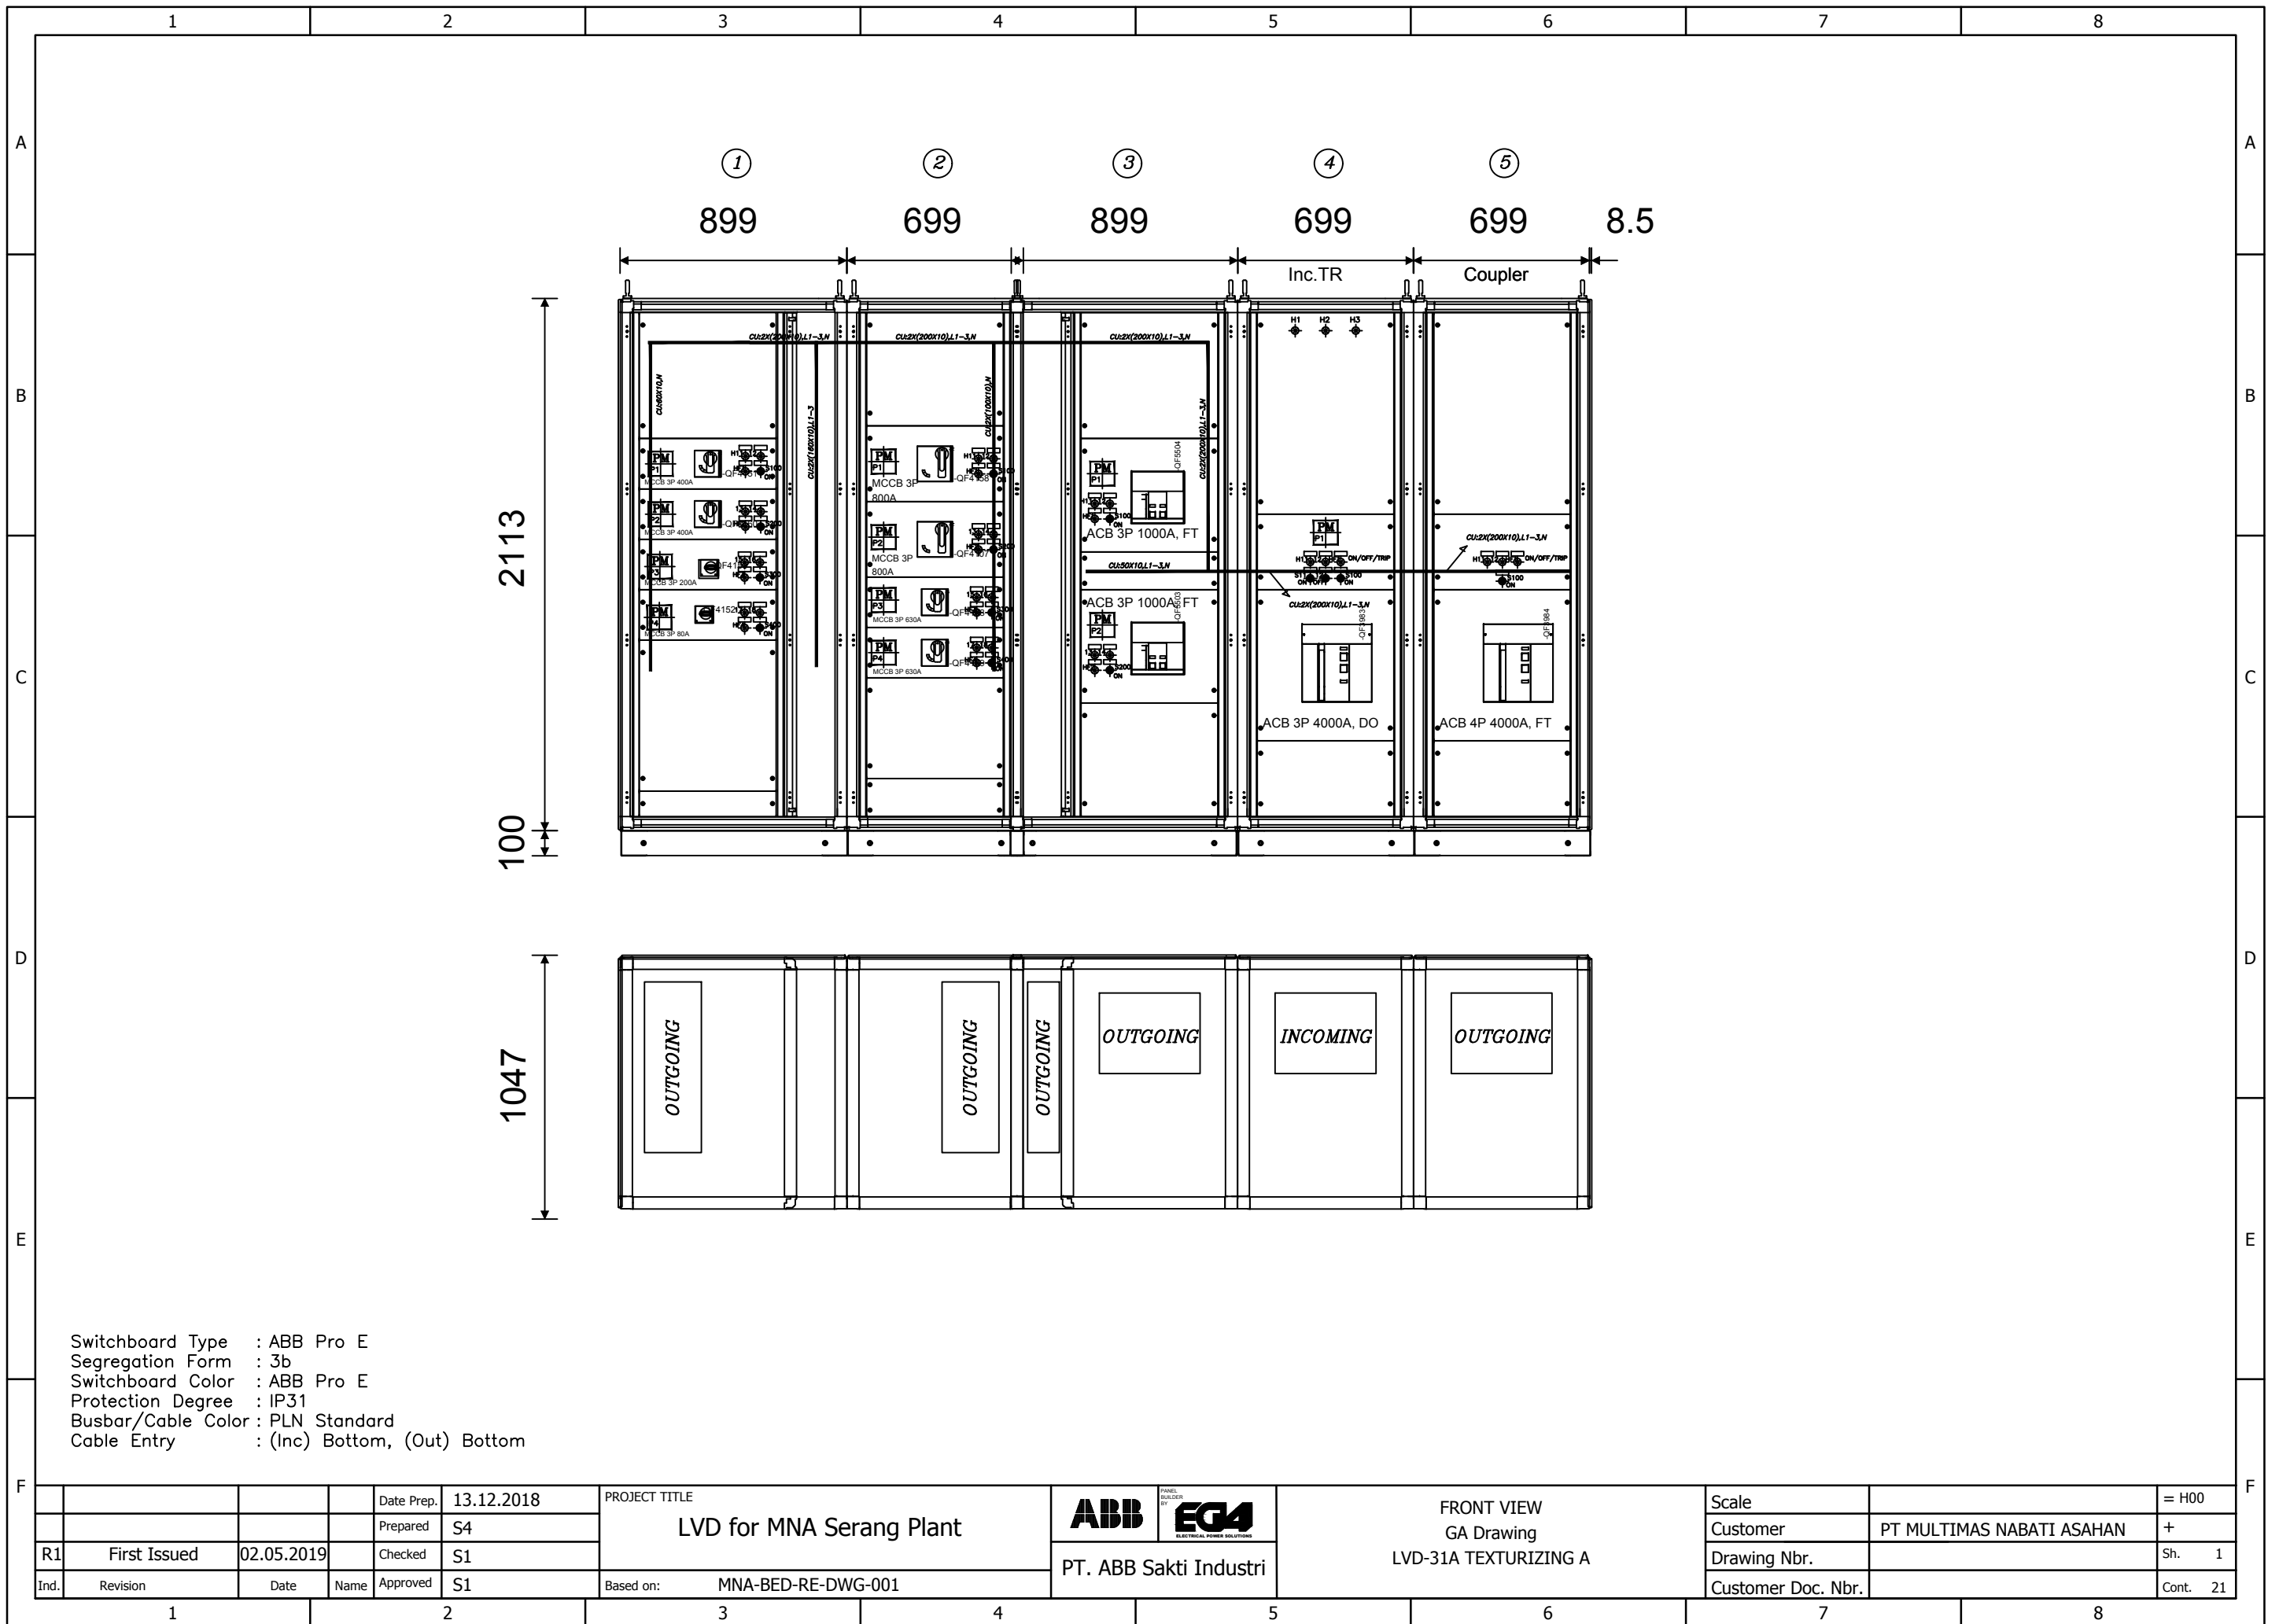

WE RESERVE ALL RIGHTS IN THIS DOCUMENT AND IN THE INFORMATION CONTAINED THEREIN. REPRODUCTION, USE OR DISCLOSURE TO THIRD PARTIES WITHOUT EXPRESS AUTHORITY IS STRICTLY FORBIDDEN.

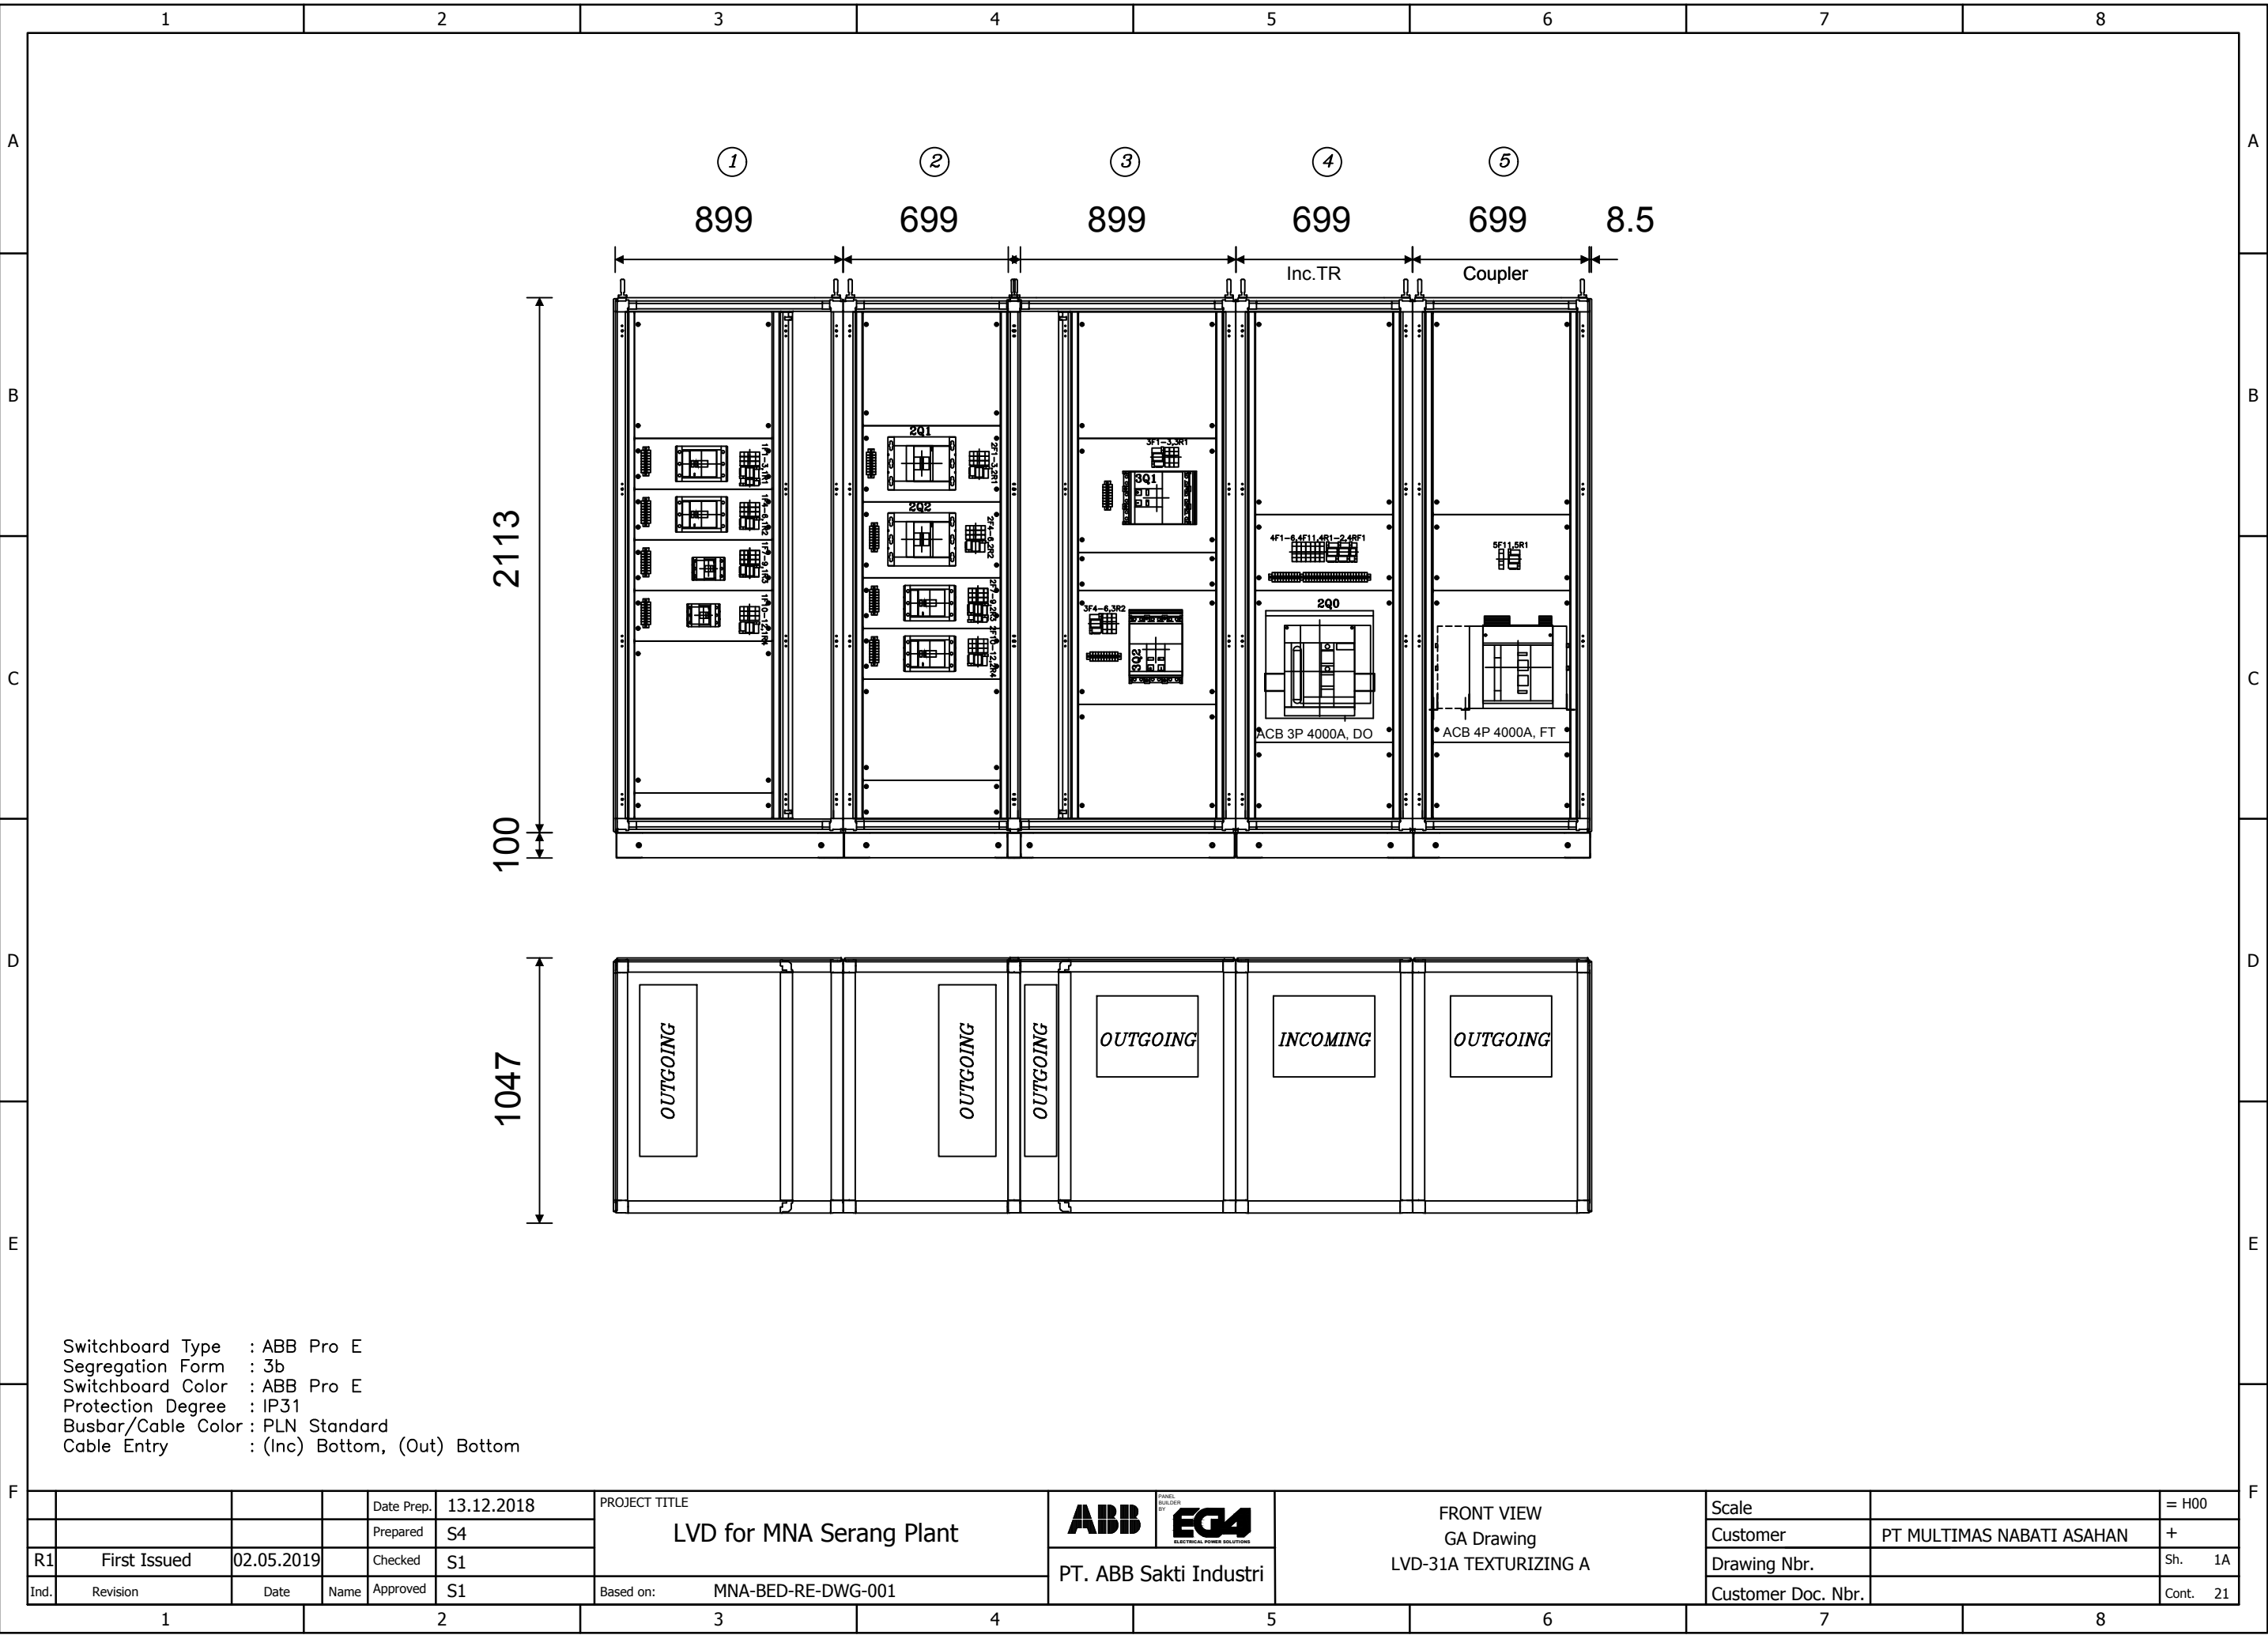

WE RESERVE ALL RIGHTS IN THIS DOCUMENT AND IN THE INFORMATION CONTAINED THEREIN. REPRODUCTION, USE OR DISCLOSURE TO THIRD PARTIES WITHOUT EXPRESS AUTHORITY IS STRICTLY FORBIDDEN.

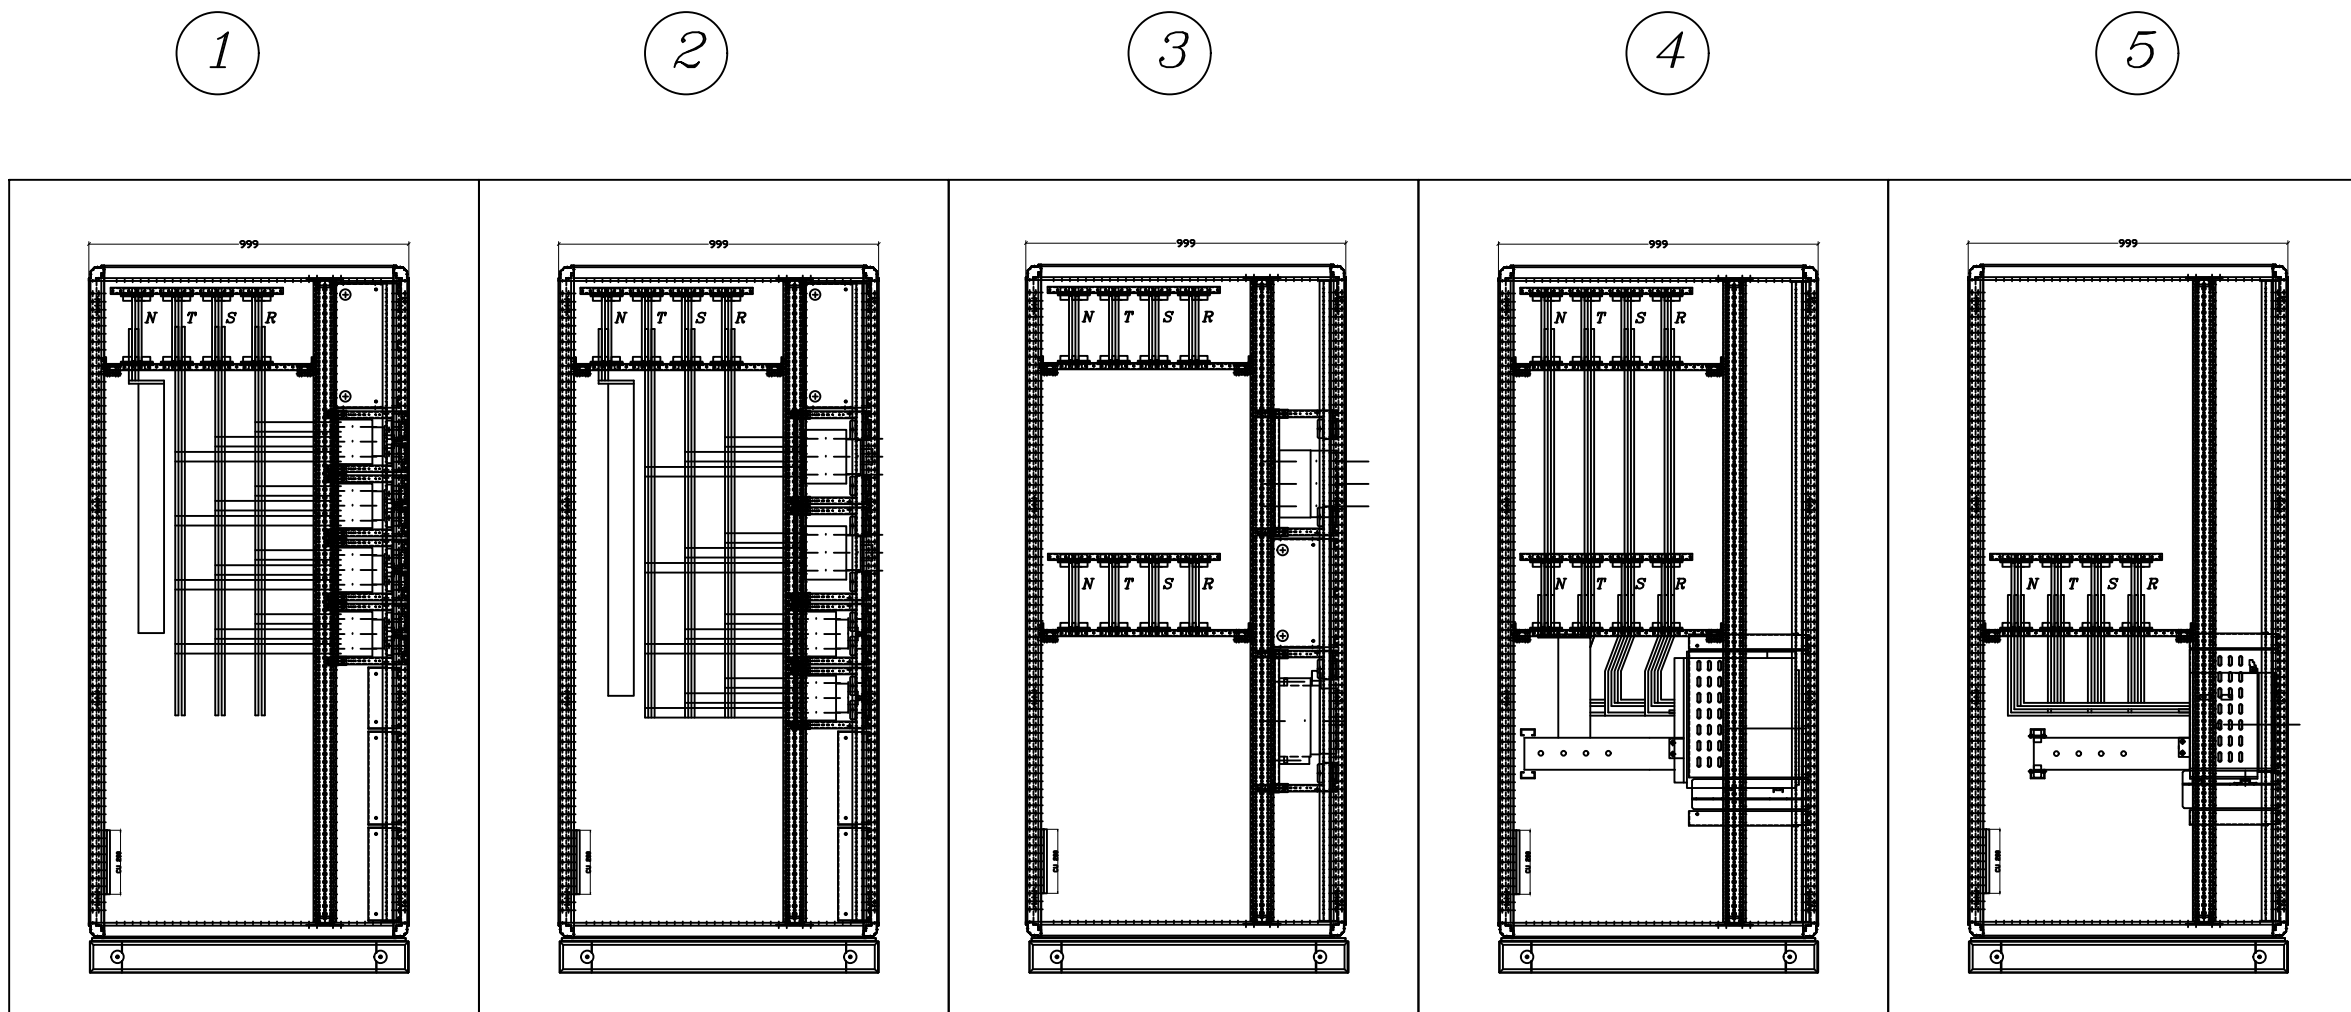


Switchboard Type : ABB Pro E
Segregation Form : 3b
Switchboard Color : ABB Pro E
Protection Degree : IP31
Busbar/Cable Color : PLN Standard
Cable Entry : (Inc) Bottom, (Out) Bottom


				Date Prep.	13.12.2018	PROJECT TITLE LVD for MNA Serang Plant	ABB PANEL BUILDING BY EG4 ELECTRICAL POWER SOLUTIONS PT. ABB Sakti Industri	FRONT VIEW GA Drawing LVD-31A TEXTURIZING A	Scale		= H00
				Prepared	S4				Customer	PT MULTIMAS NABATI ASAHAN	+
R1	First Issued	02.05.2019	Checked	S1					Drawing Nbr.		Sh. 1B
Ind.	Revision	Date	Name	Approved	S1	Based on:	MNA-BED-RE-DWG-001		Customer Doc. Nbr.		Cont. 21

WE RESERVE ALL RIGHTS IN THIS DOCUMENT AND IN THE INFORMATION CONTAINED THEREIN. REPRODUCTION, USE OR DISCLOSURE TO THIRD PARTIES WITHOUT EXPRESS AUTHORITY IS STRICTLY FORBIDDEN.

SIDE VIEW

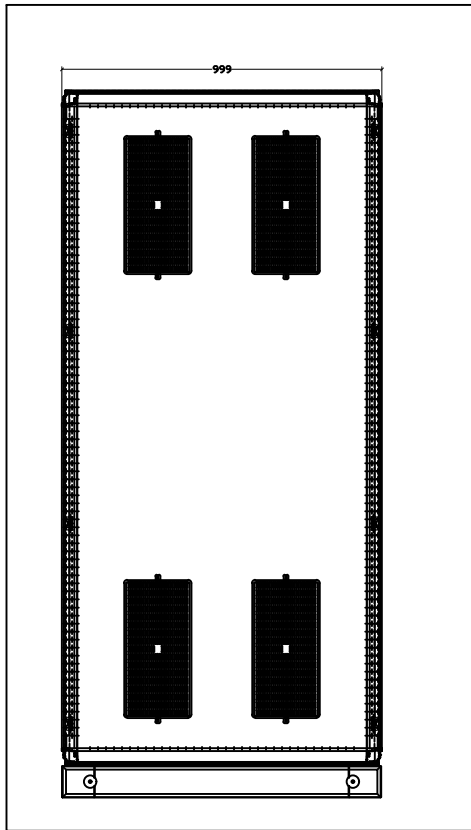


BACK VIEW

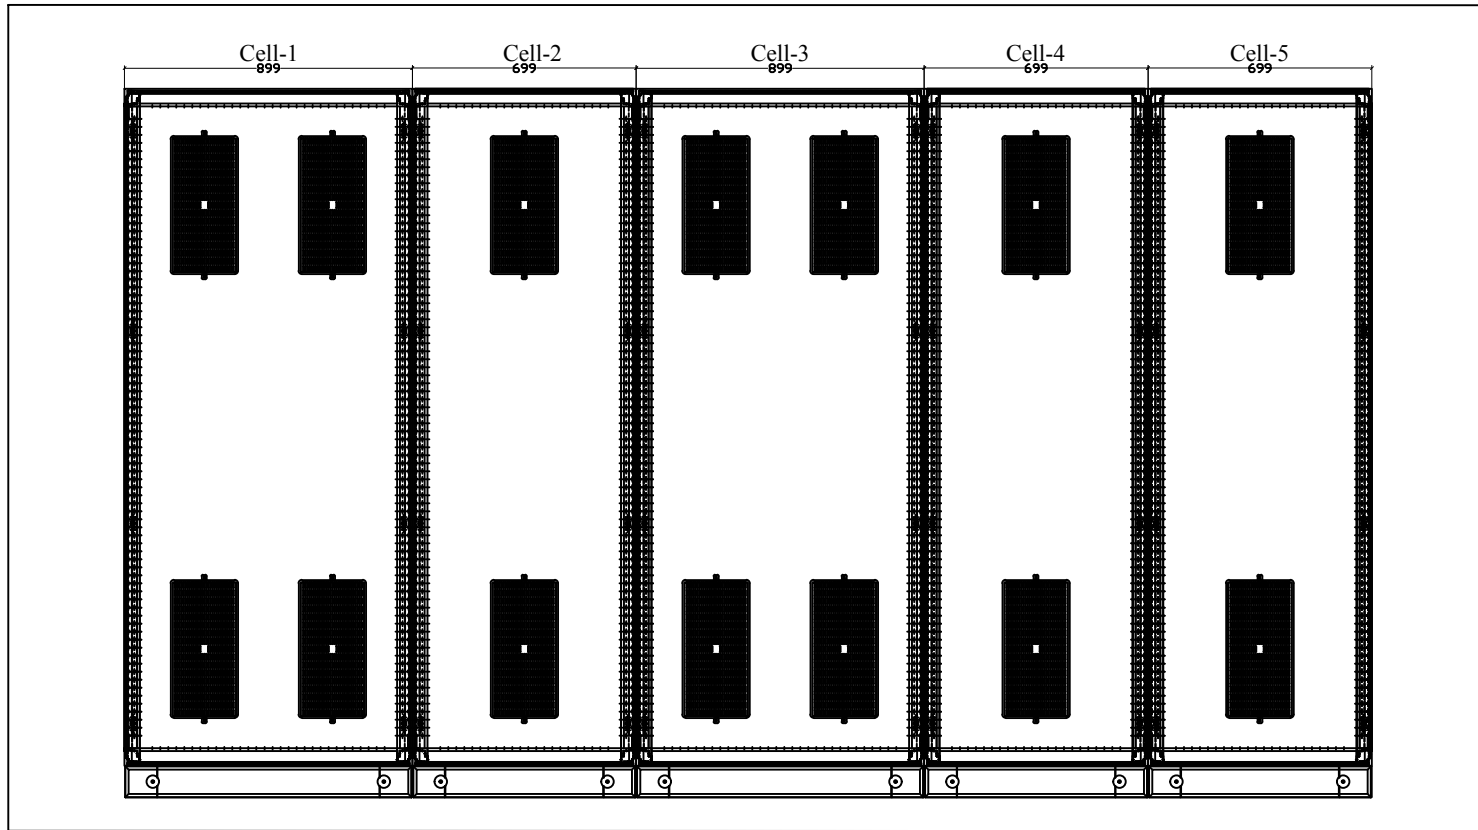

Switchboard Type : ABB Pro E
Segregation Form : 3b
Switchboard Color : ABB Pro E
Protection Degree : IP31
Busbar/Cable Color : PLN Standard
Cable Entry : (Inc) Bottom, (Out) Bottom


				Date Prep.	13.12.2018	PROJECT TITLE LVD for MNA Serang Plant	  PT. ABB Sakti Industri	FRONT VIEW GA Drawing LVD-31A TEXTURIZING A	Scale		= H00
				Prepared	S4				Customer	PT MULTIMAS NABATI ASAHAN	+
R1	First Issued	02.05.2019		Checked	S1				Drawing Nbr.		Sh. 1C
Ind.	Revision	Date	Name	Approved	S1	Based on:	MNA-BED-RE-DWG-001		Customer Doc. Nbr.		Cont. 21


WE RESERVE ALL RIGHTS IN THIS DOCUMENT AND IN THE INFORMATION CONTAINED THEREIN. REPRODUCTION, USE OR DISCLOSURE TO THIRD PARTIES WITHOUT EXPRESS AUTHORITY IS STRICTLY FORBIDDEN.

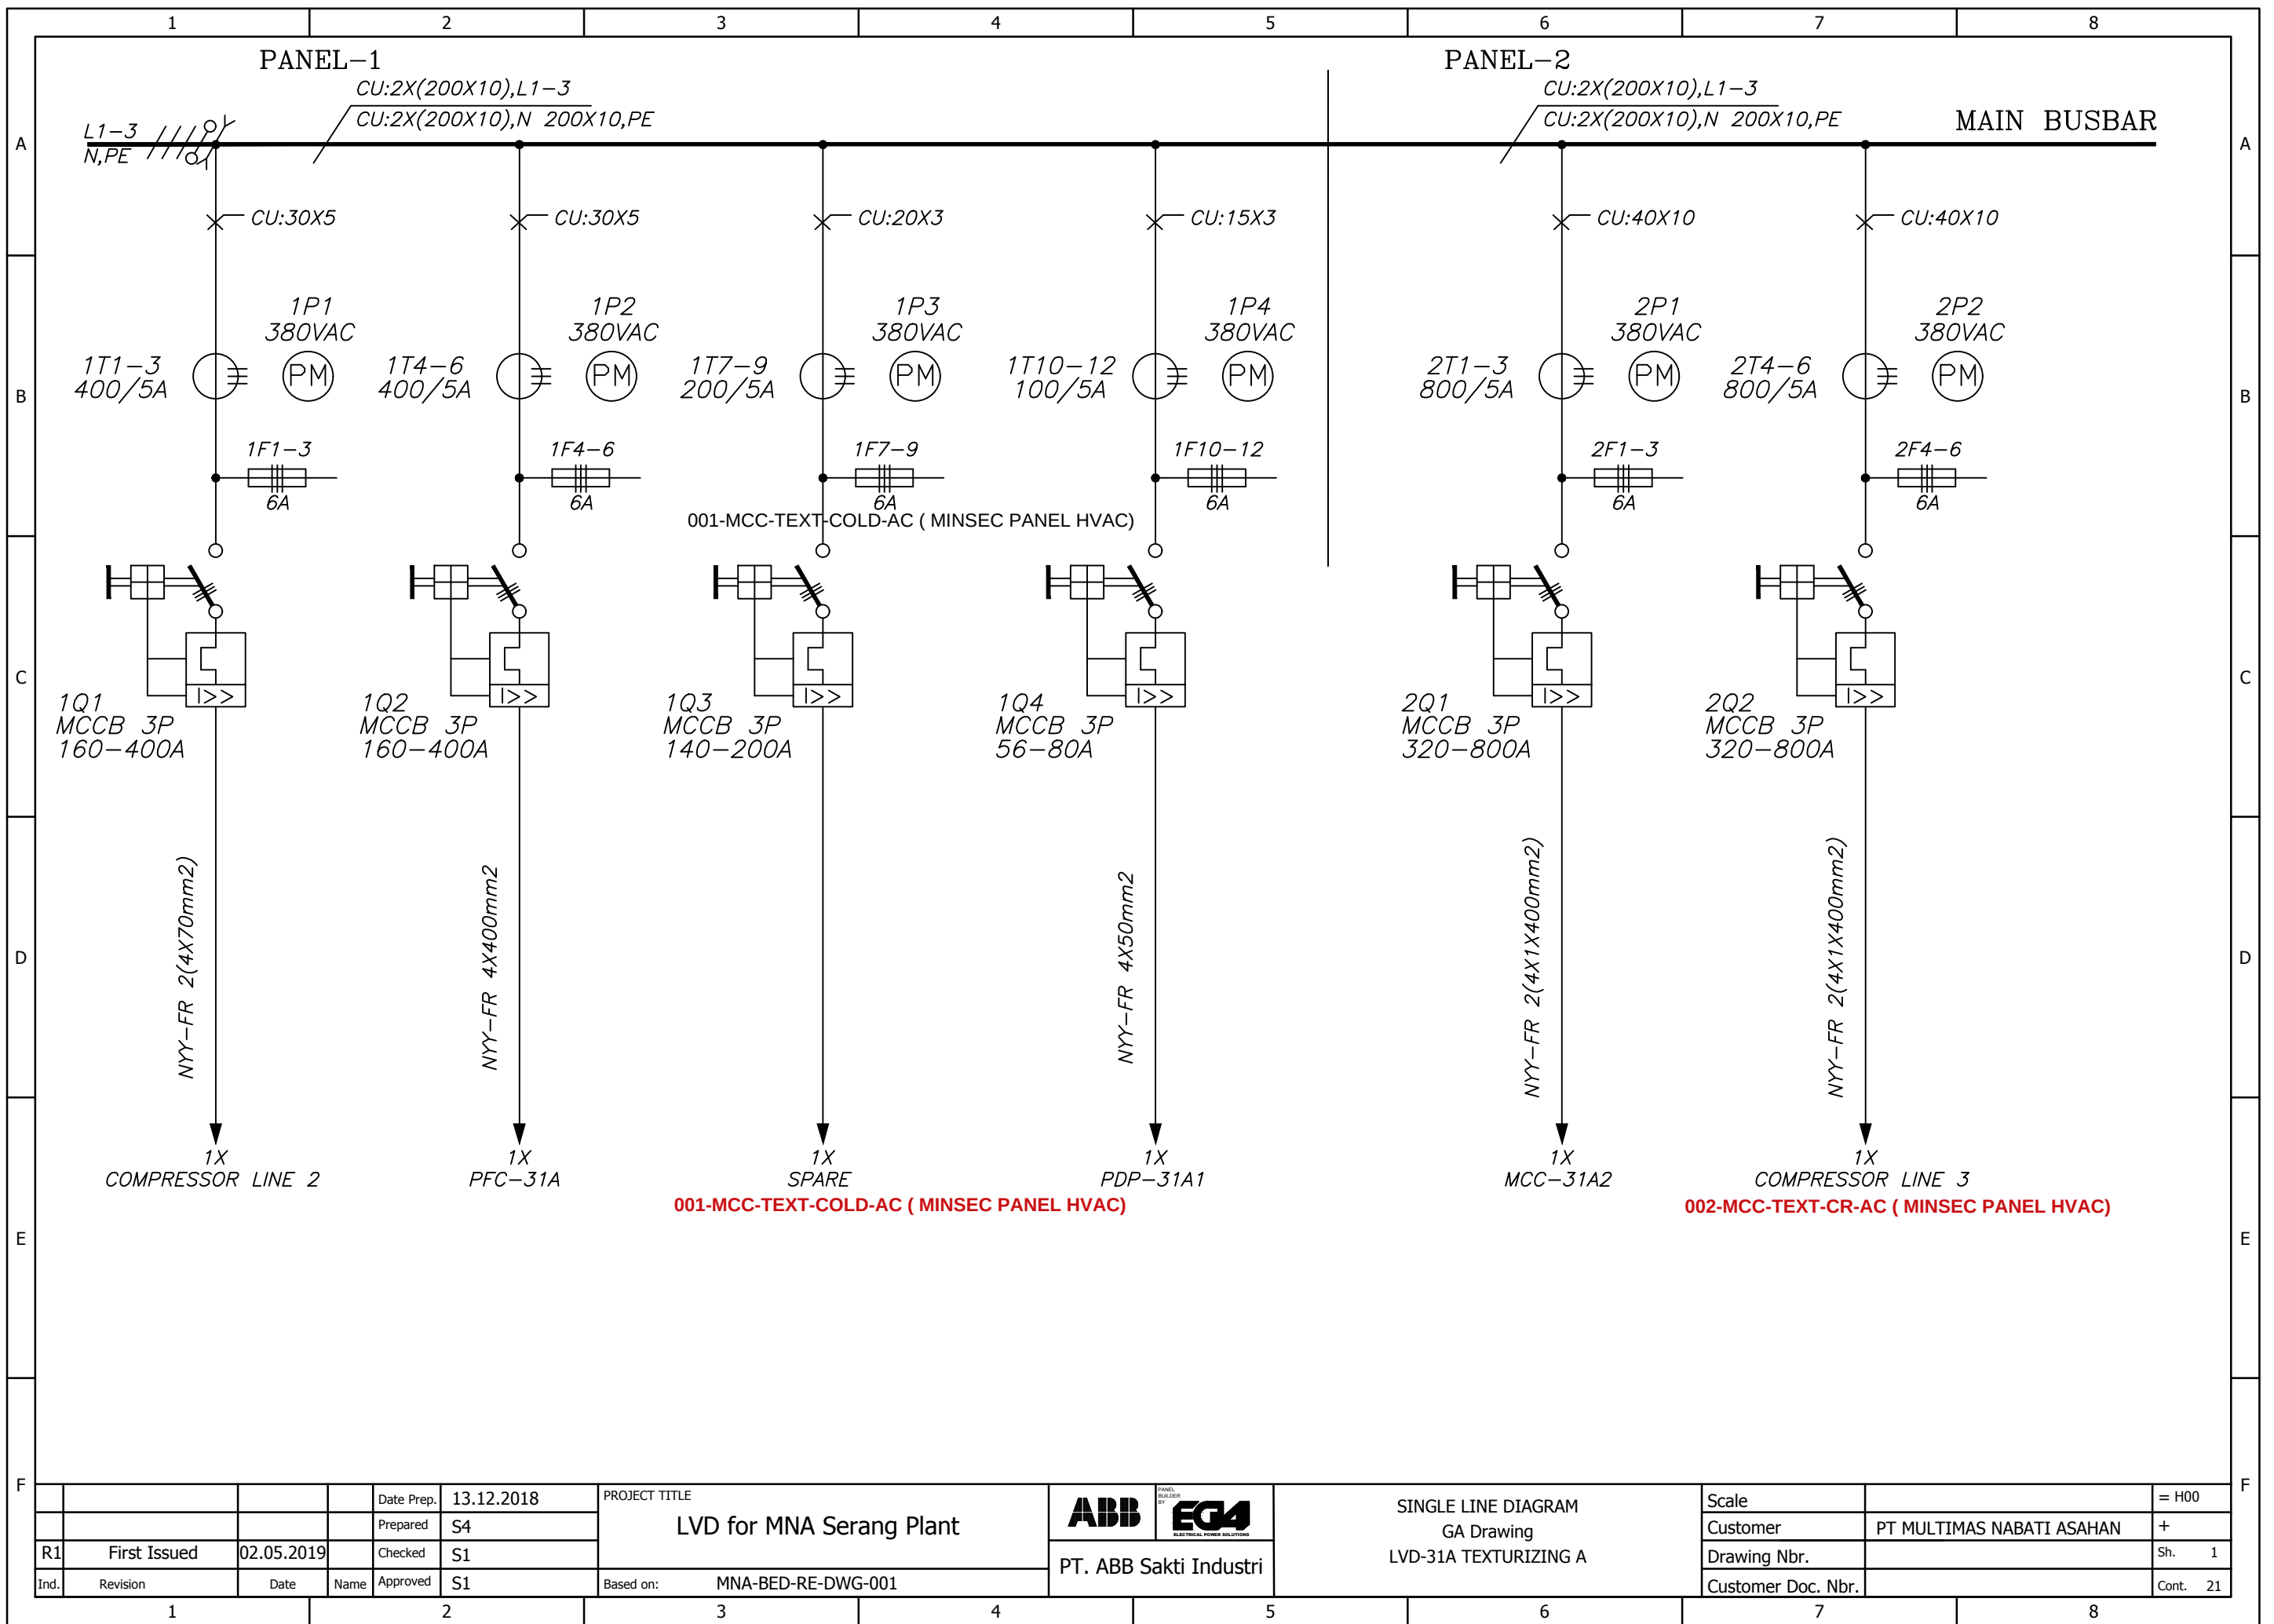


R1		First Issued	02.05.2019	Checked	S1	PROJECT TITLE LVD for MNA Serang Plant	  PT. ABB Sakti Industri	SINGLE LINE DIAGRAM GA Drawing LVD-31A TEXTURIZING A	Scale	= H00
Ind.		Revision	Date	Name	Approved				Customer	PT MULTIMAS NABATI ASAHAN
									Drawing Nbr.	Sh. 1
						Based on:	MNA-BED-RE-DWG-001		Customer Doc. Nbr.	Cont. 21

WE RESERVE ALL RIGHTS IN THIS DOCUMENT AND IN THE INFORMATION CONTAINED THEREIN. REPRODUCTION, USE OR DISCLOSURE TO THIRD PARTIES WITHOUT EXPRESS AUTHORITY IS STRICTLY FORBIDDEN.

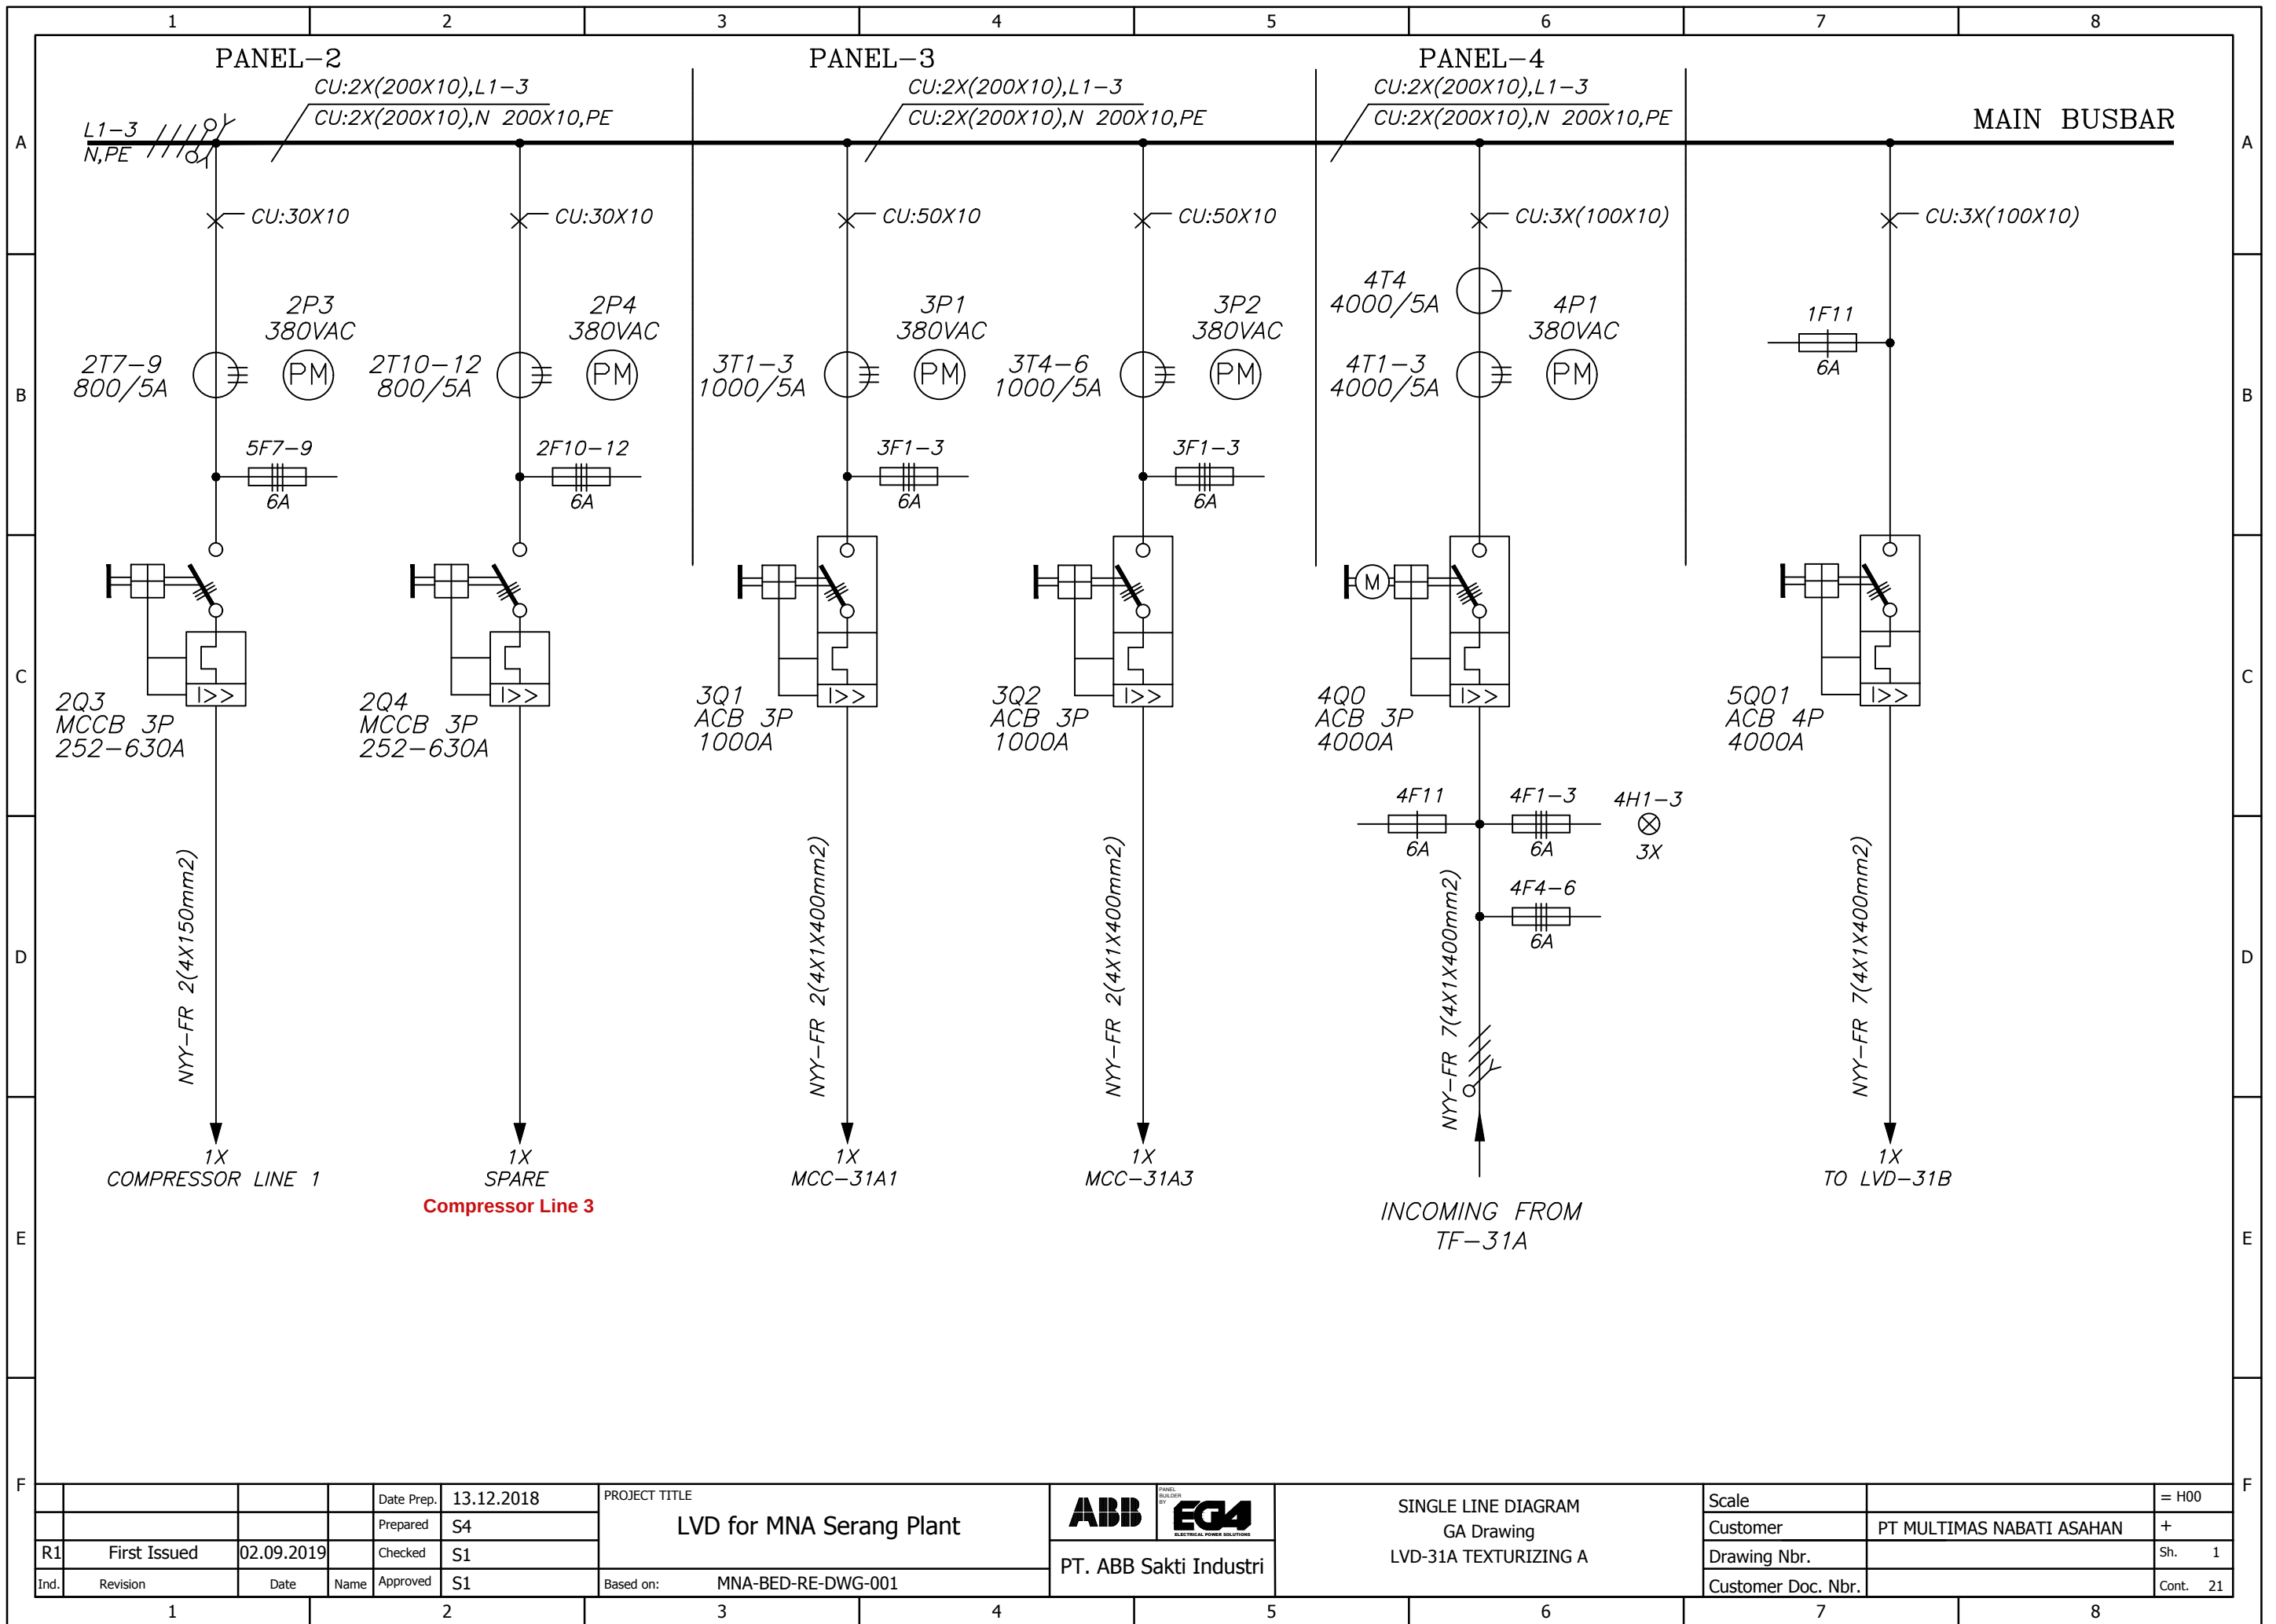


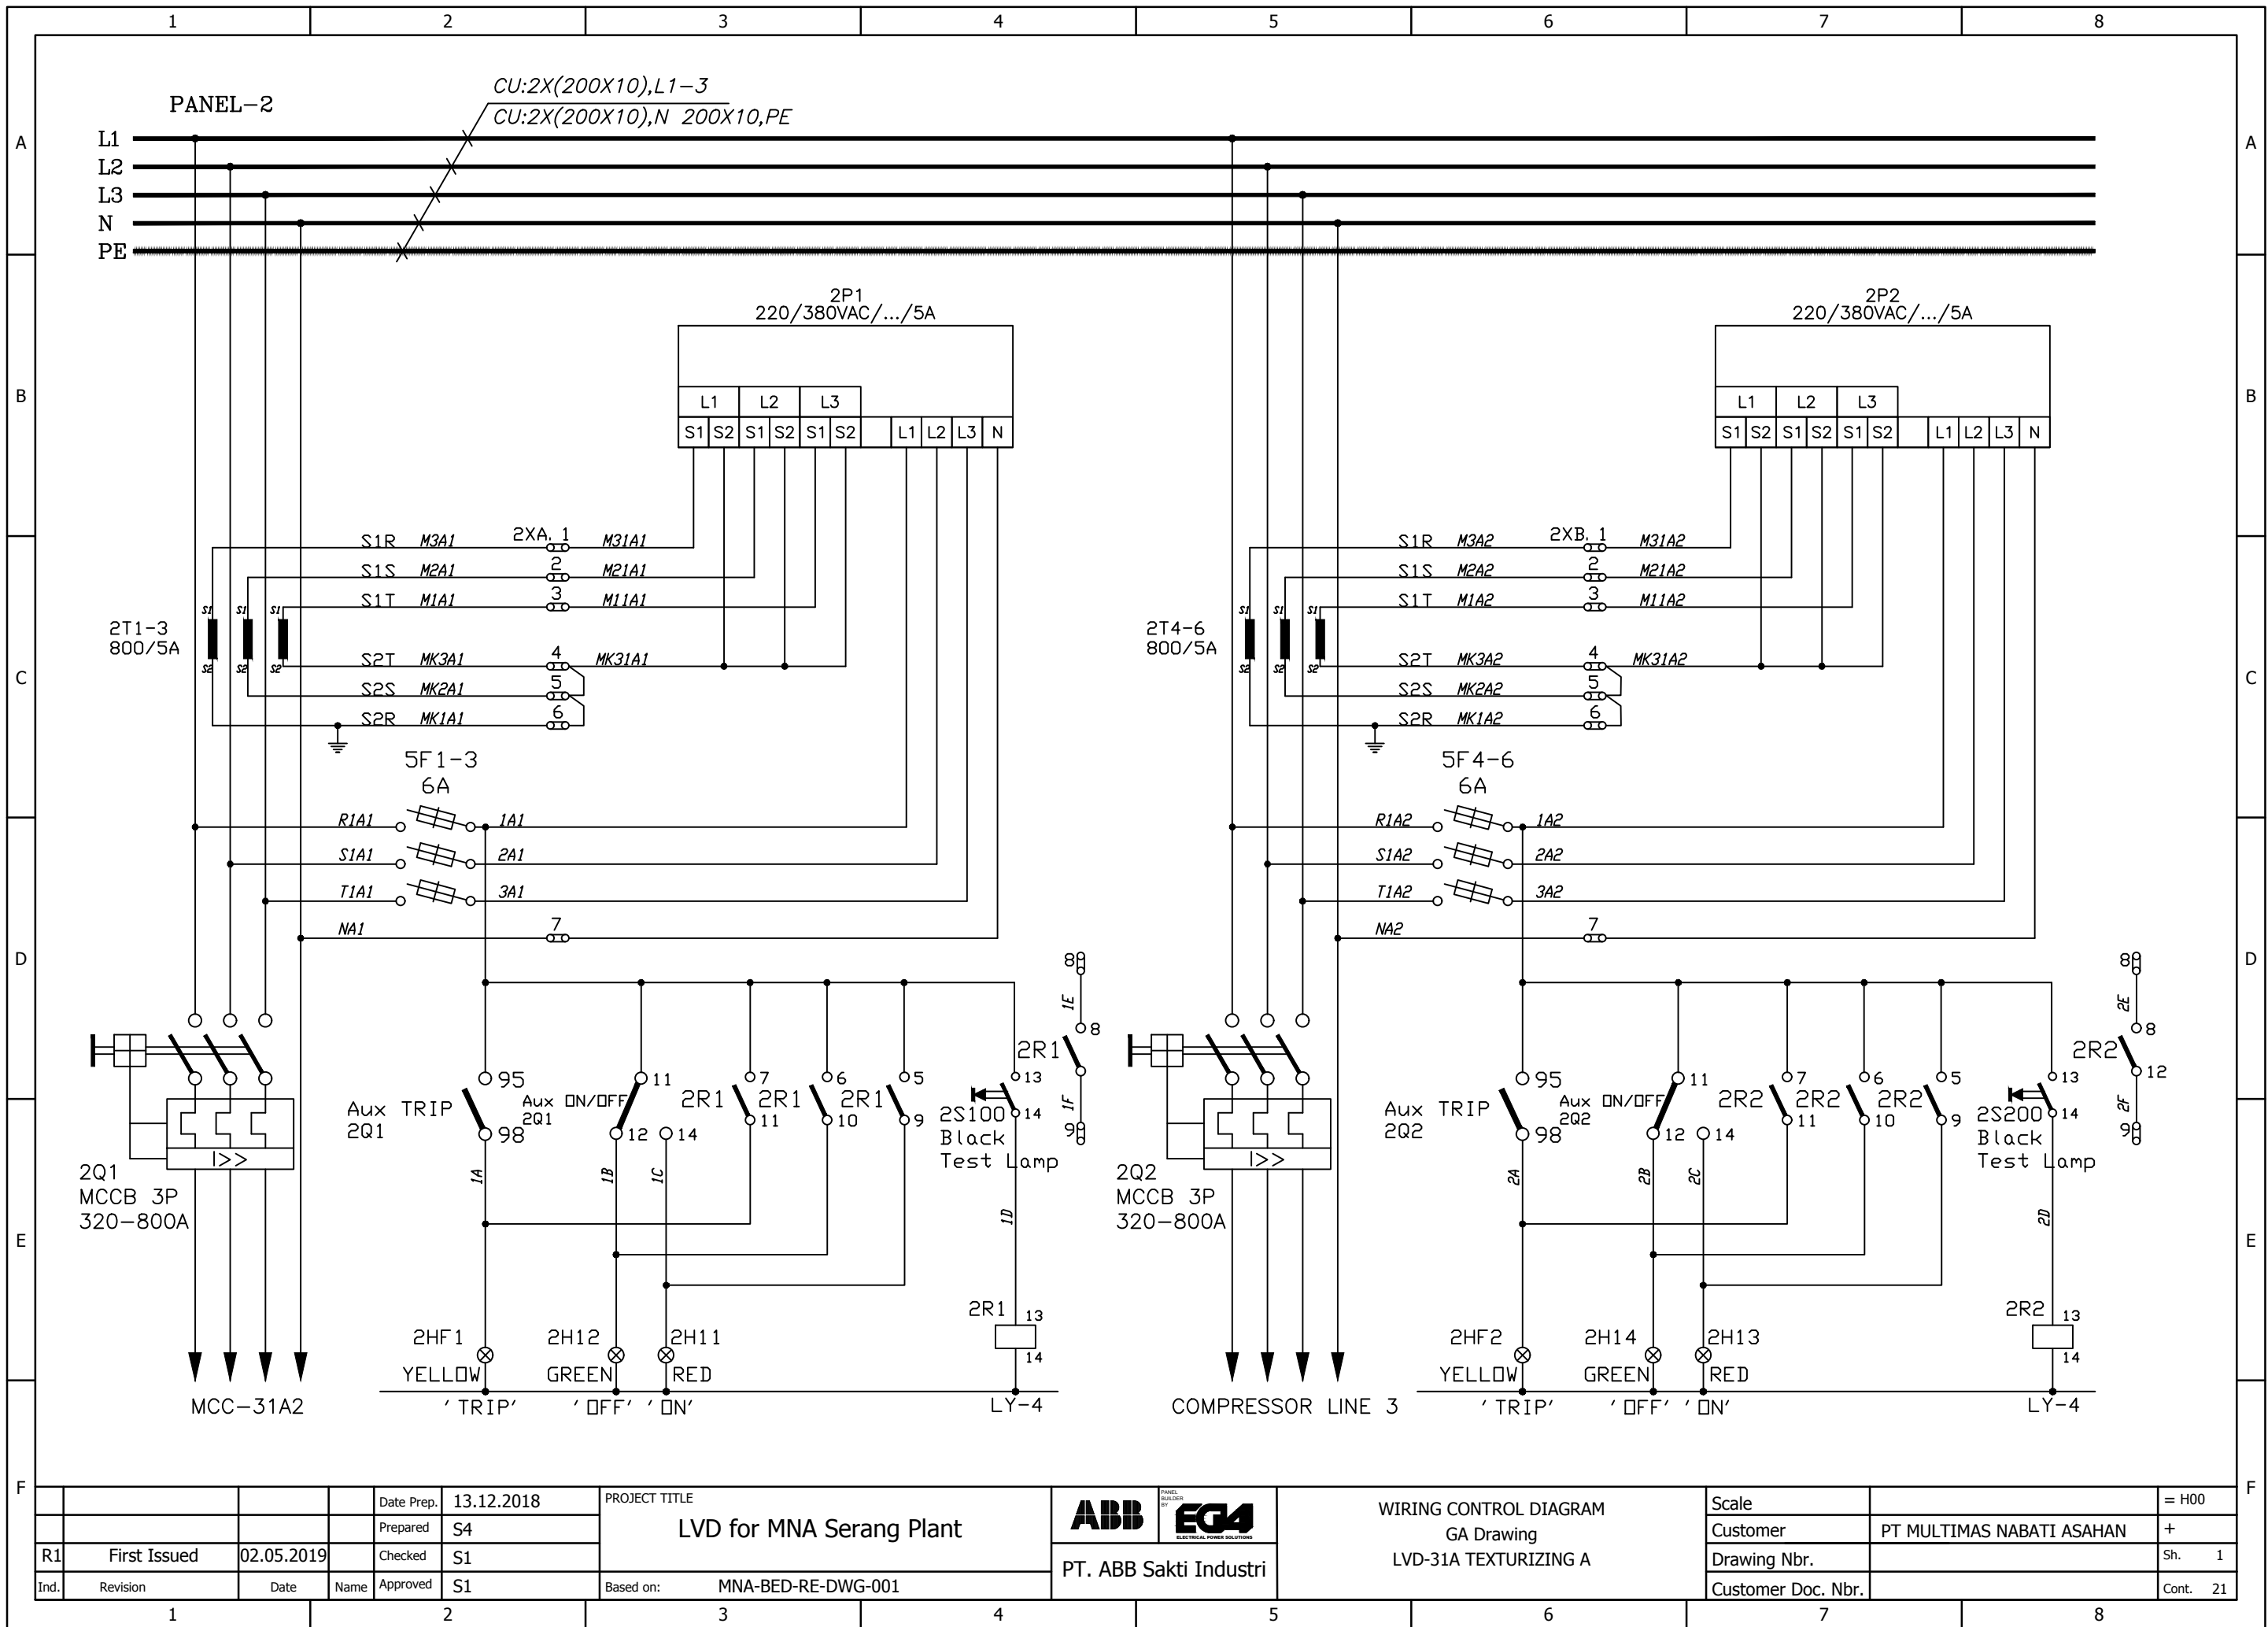

WE RESERVE ALL RIGHTS IN THIS DOCUMENT AND IN THE INFORMATION CONTAINED THEREIN. REPRODUCTION, USE OR DISCLOSURE TO THIRD PARTIES WITHOUT EXPRESS AUTHORITY IS STRICTLY FORBIDDEN.

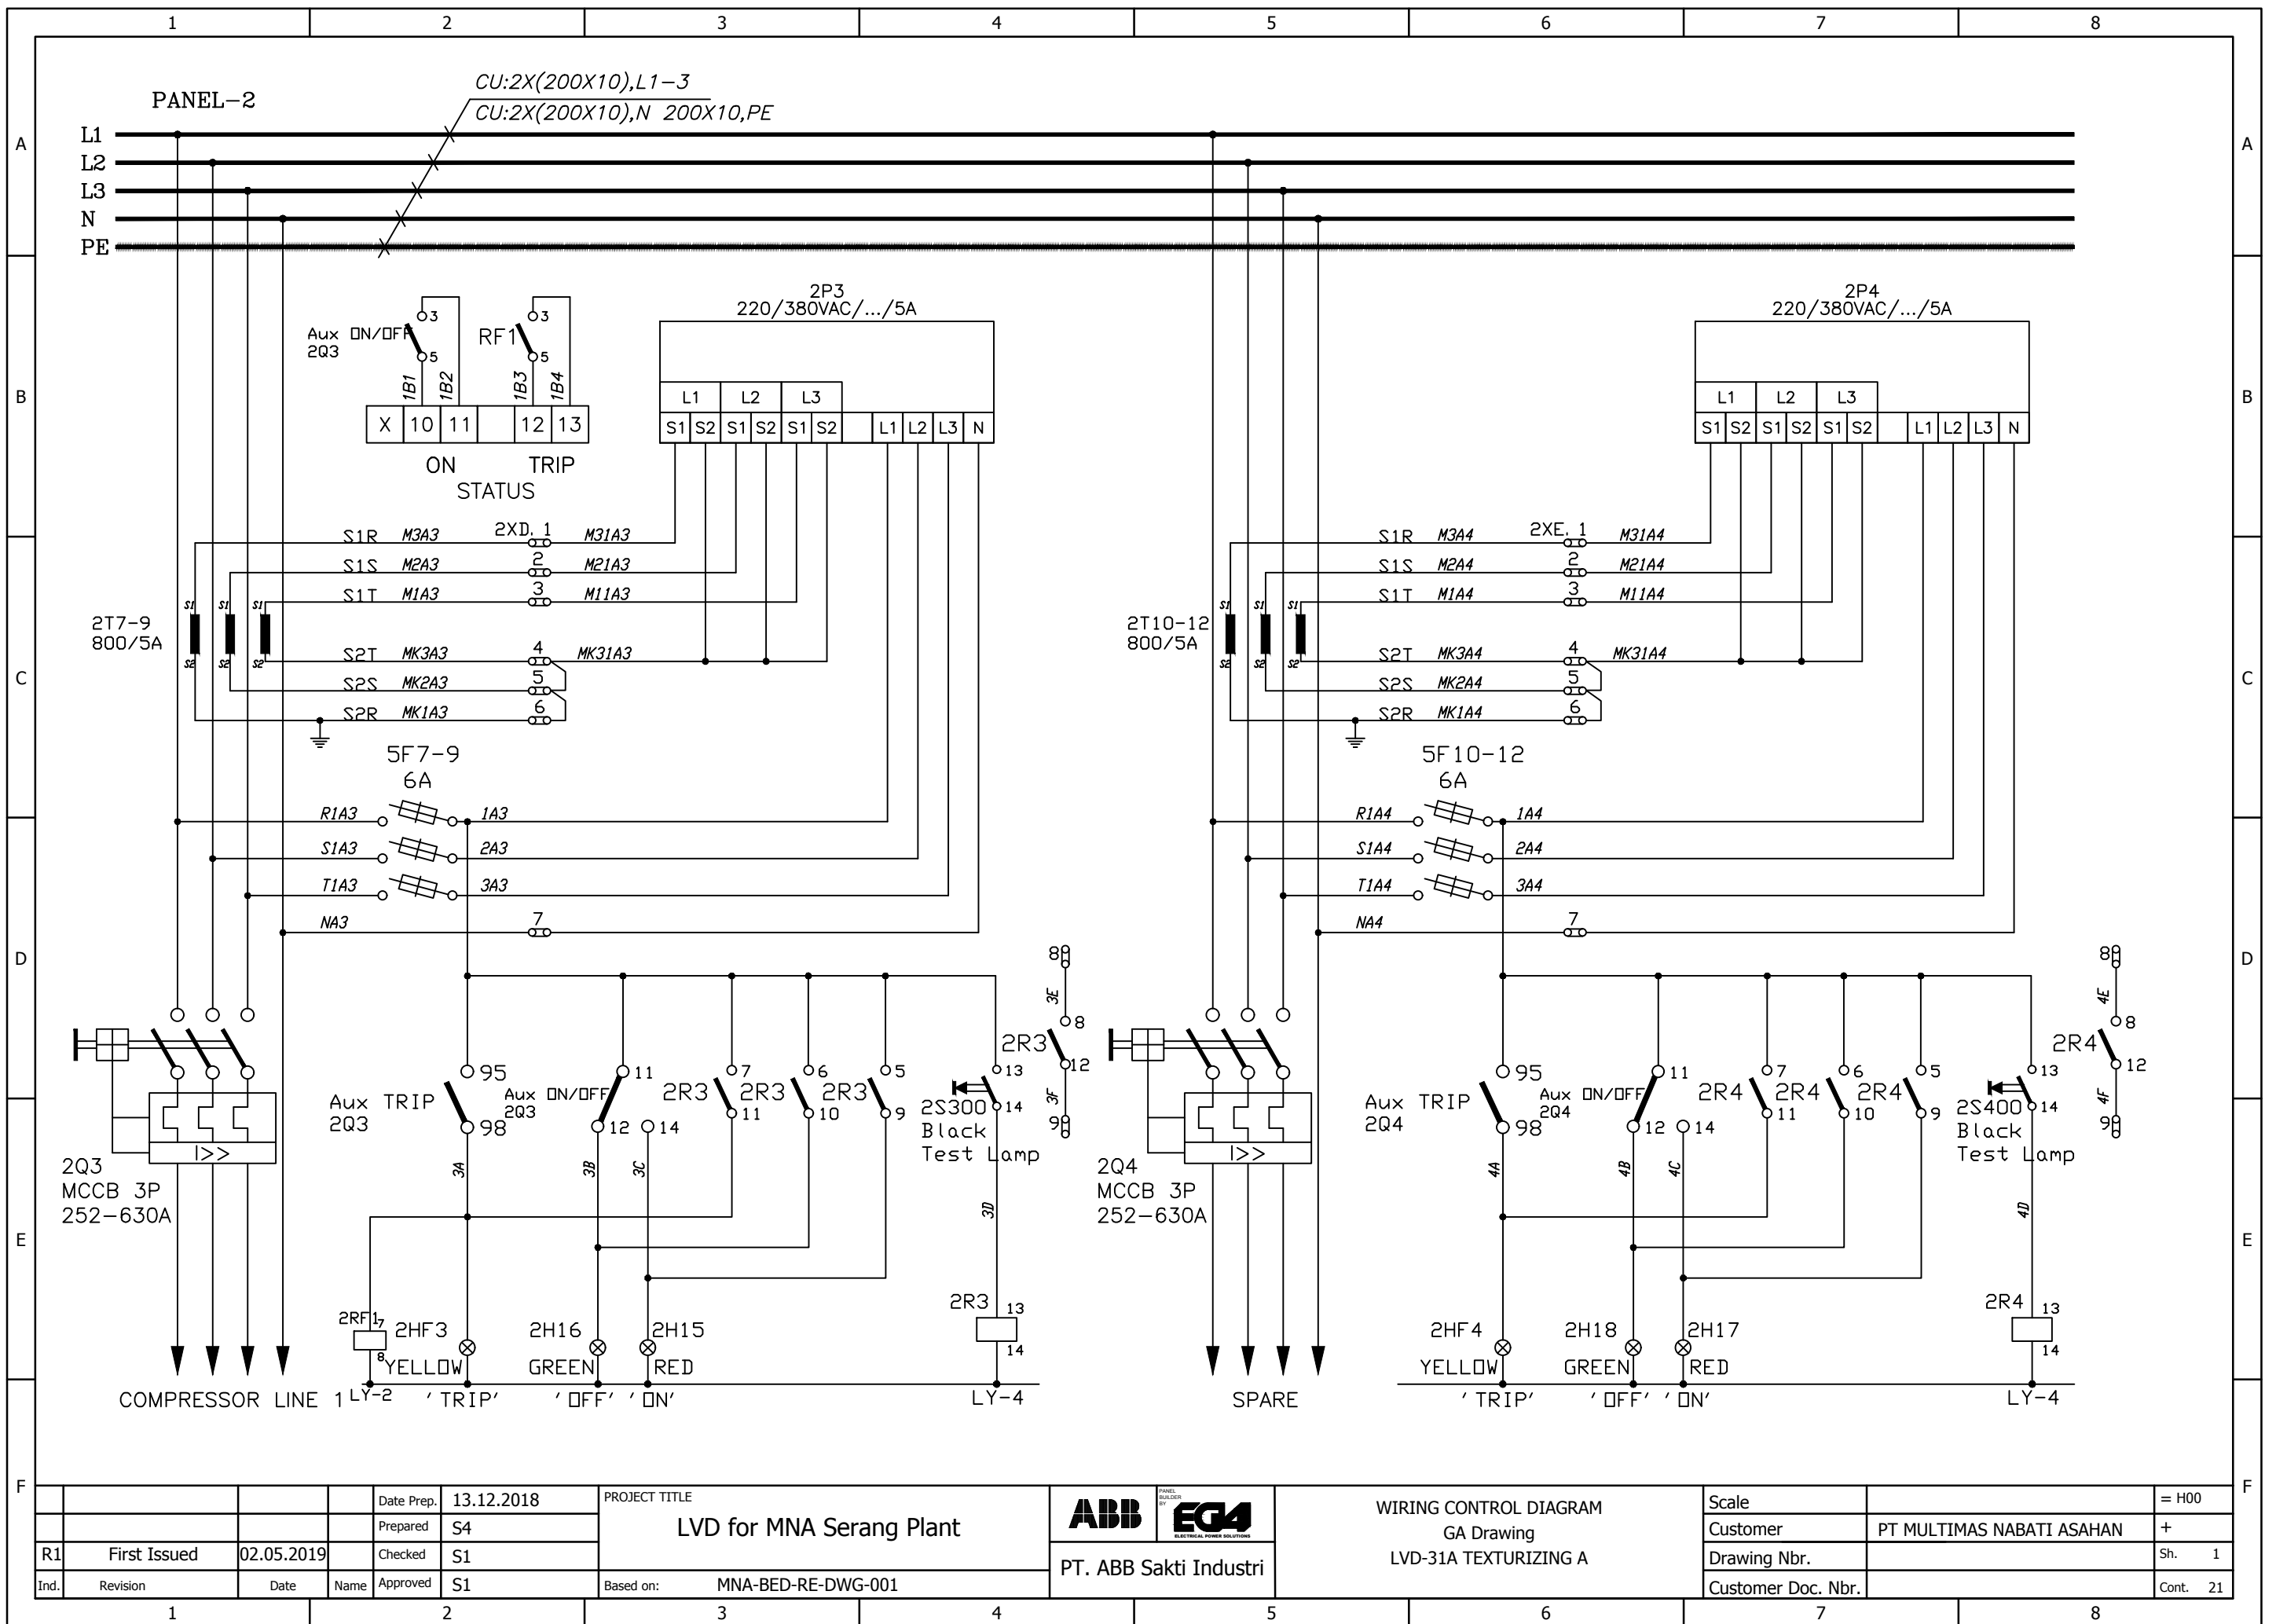


WE RESERVE ALL RIGHTS IN THIS DOCUMENT AND IN THE INFORMATION CONTAINED THEREIN. REPRODUCTION, USE OR DISCLOSURE TO THIRD PARTIES WITHOUT EXPRESS AUTHORITY IS STRICTLY FORBIDDEN.

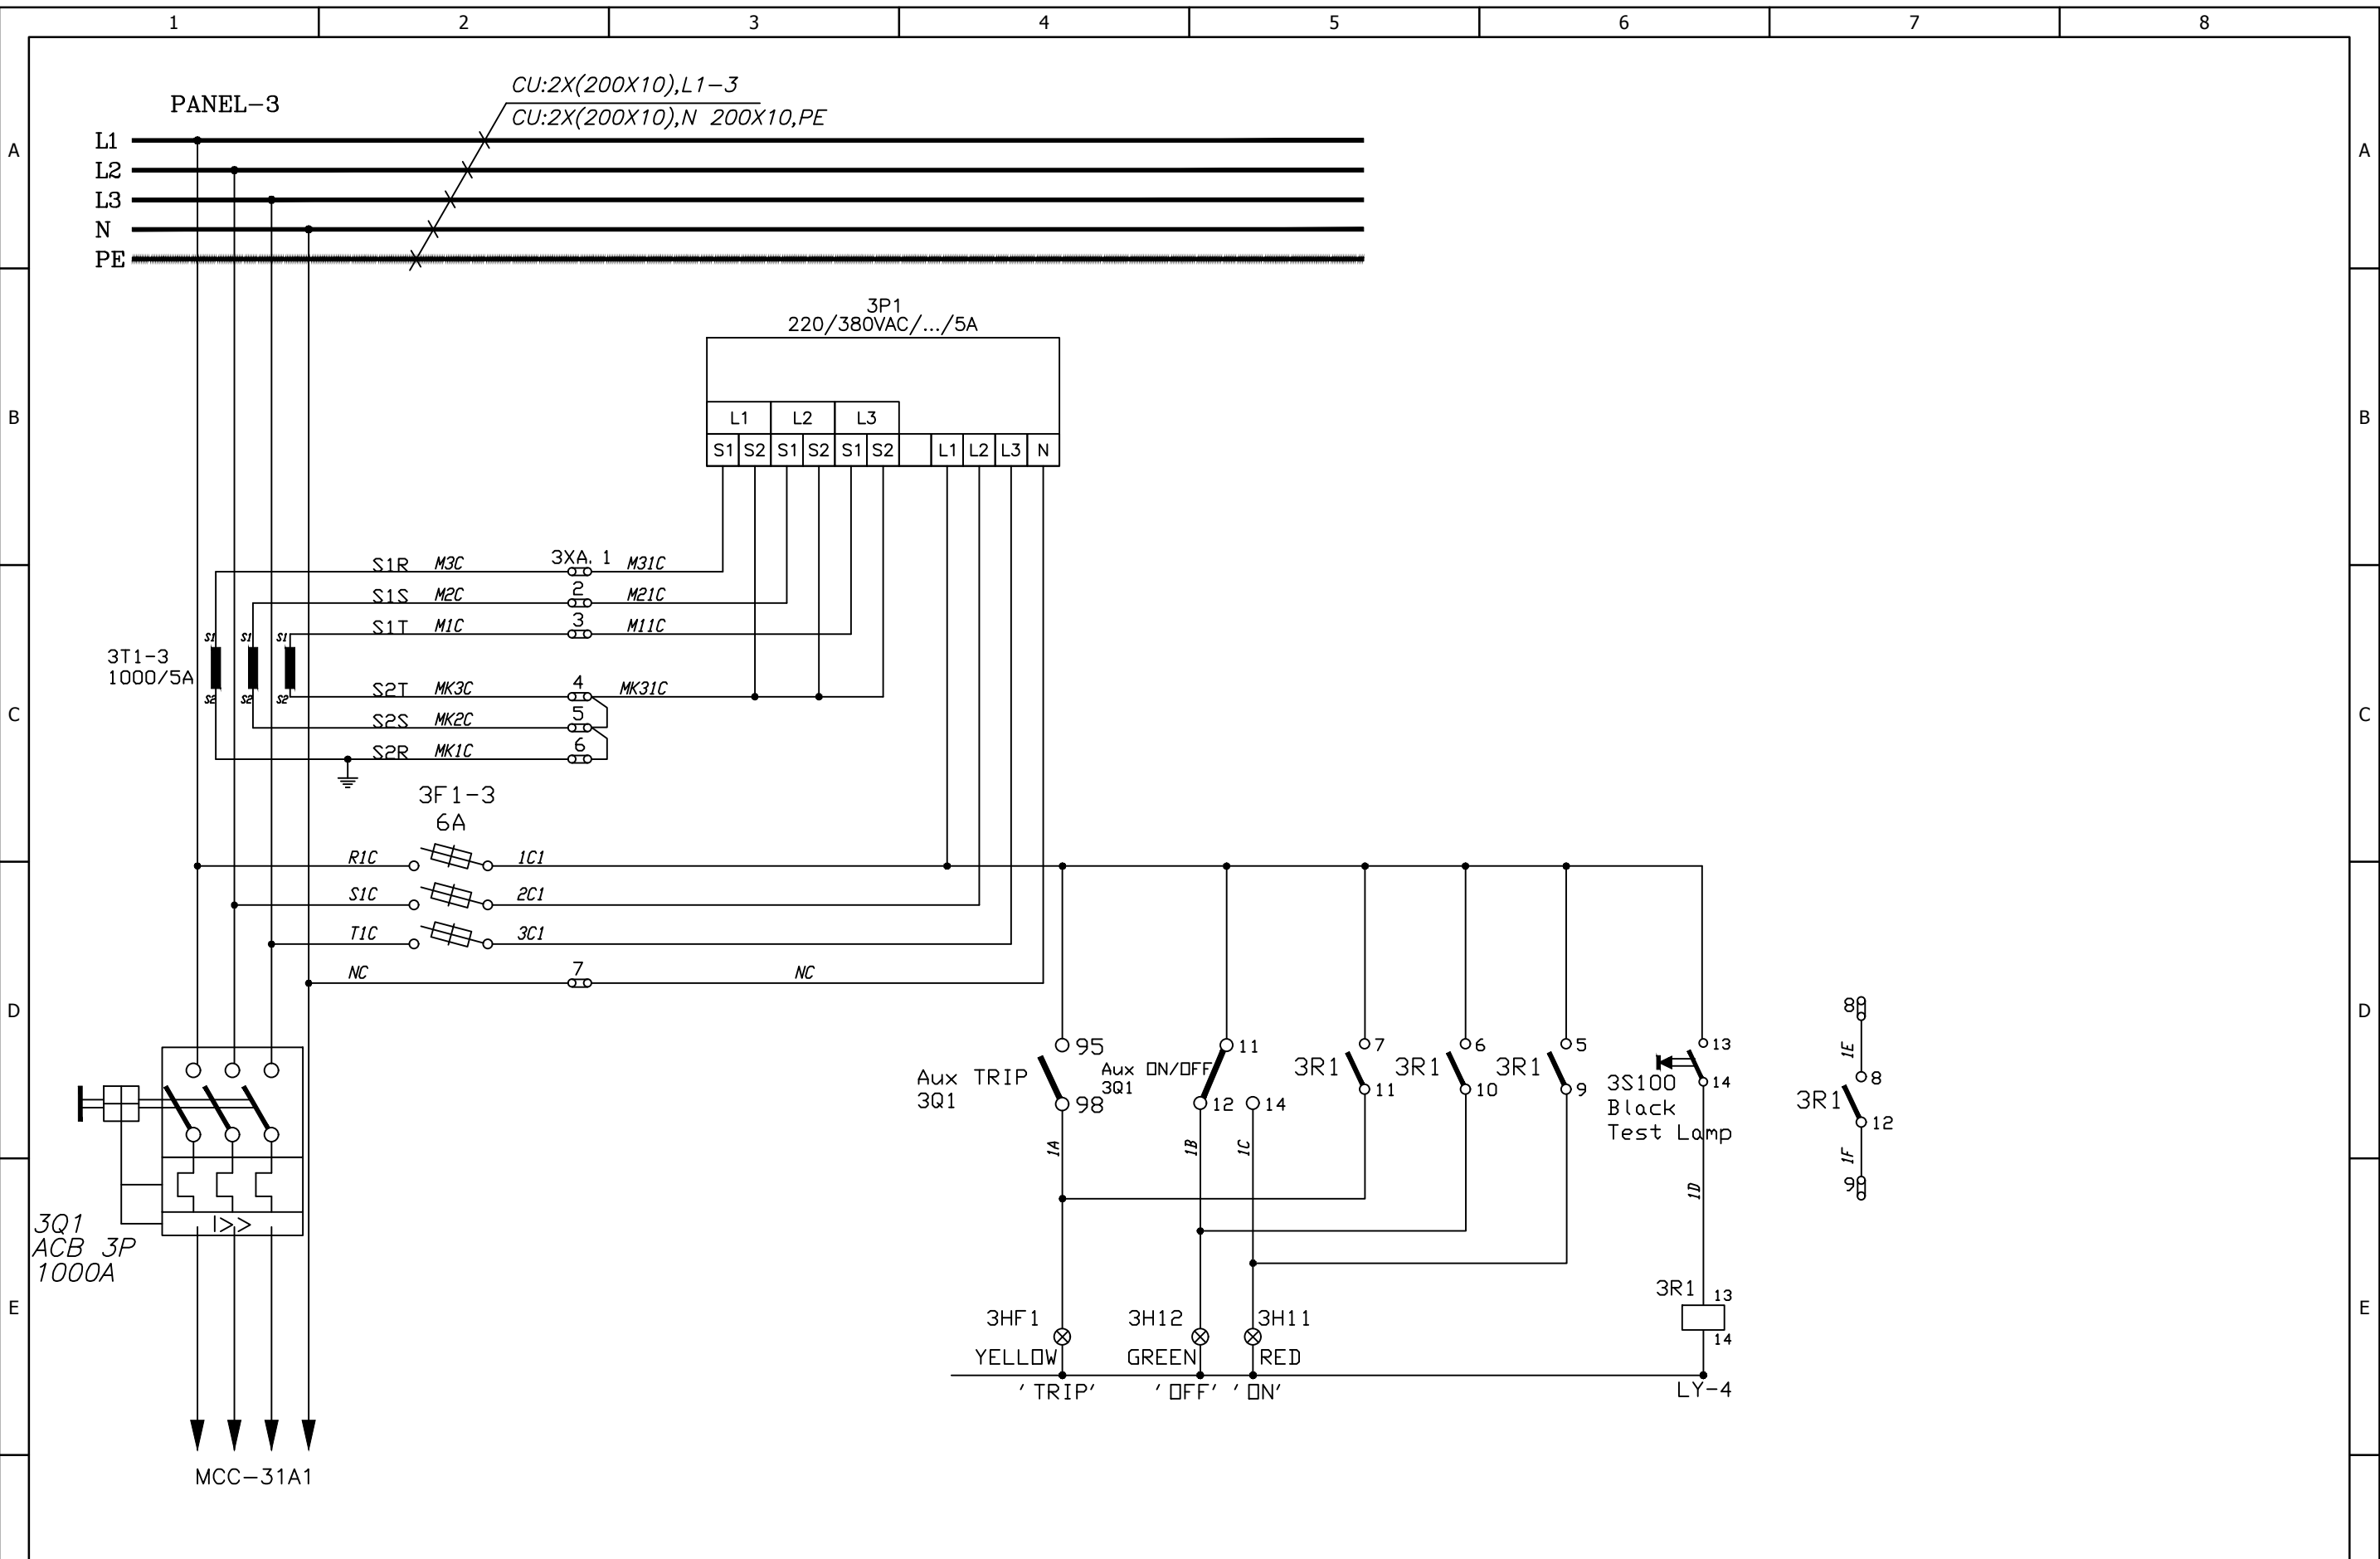


Ind.		Revision	Date	Name	Approved	Based on:	MNA-BED-RE-DWG-001		PT. ABB Sakti Industri		WIRING CONTROL DIAGRAM GA Drawing LVD-31A TEXTURIZING A		Scale	= H00	
R1		First Issued	02.05.2019		Checked	S1							Customer	PT MULTIMAS NABATI ASAHAN	
													Drawing Nbr.	Sh. 1	
													Customer Doc. Nbr.	Cont. 21	

WE RESERVE ALL RIGHTS IN THIS DOCUMENT AND IN THE INFORMATION CONTAINED THEREIN. REPRODUCTION, USE OR DISCLOSURE TO THIRD PARTIES WITHOUT EXPRESS AUTHORITY IS STRICTLY FORBIDDEN.

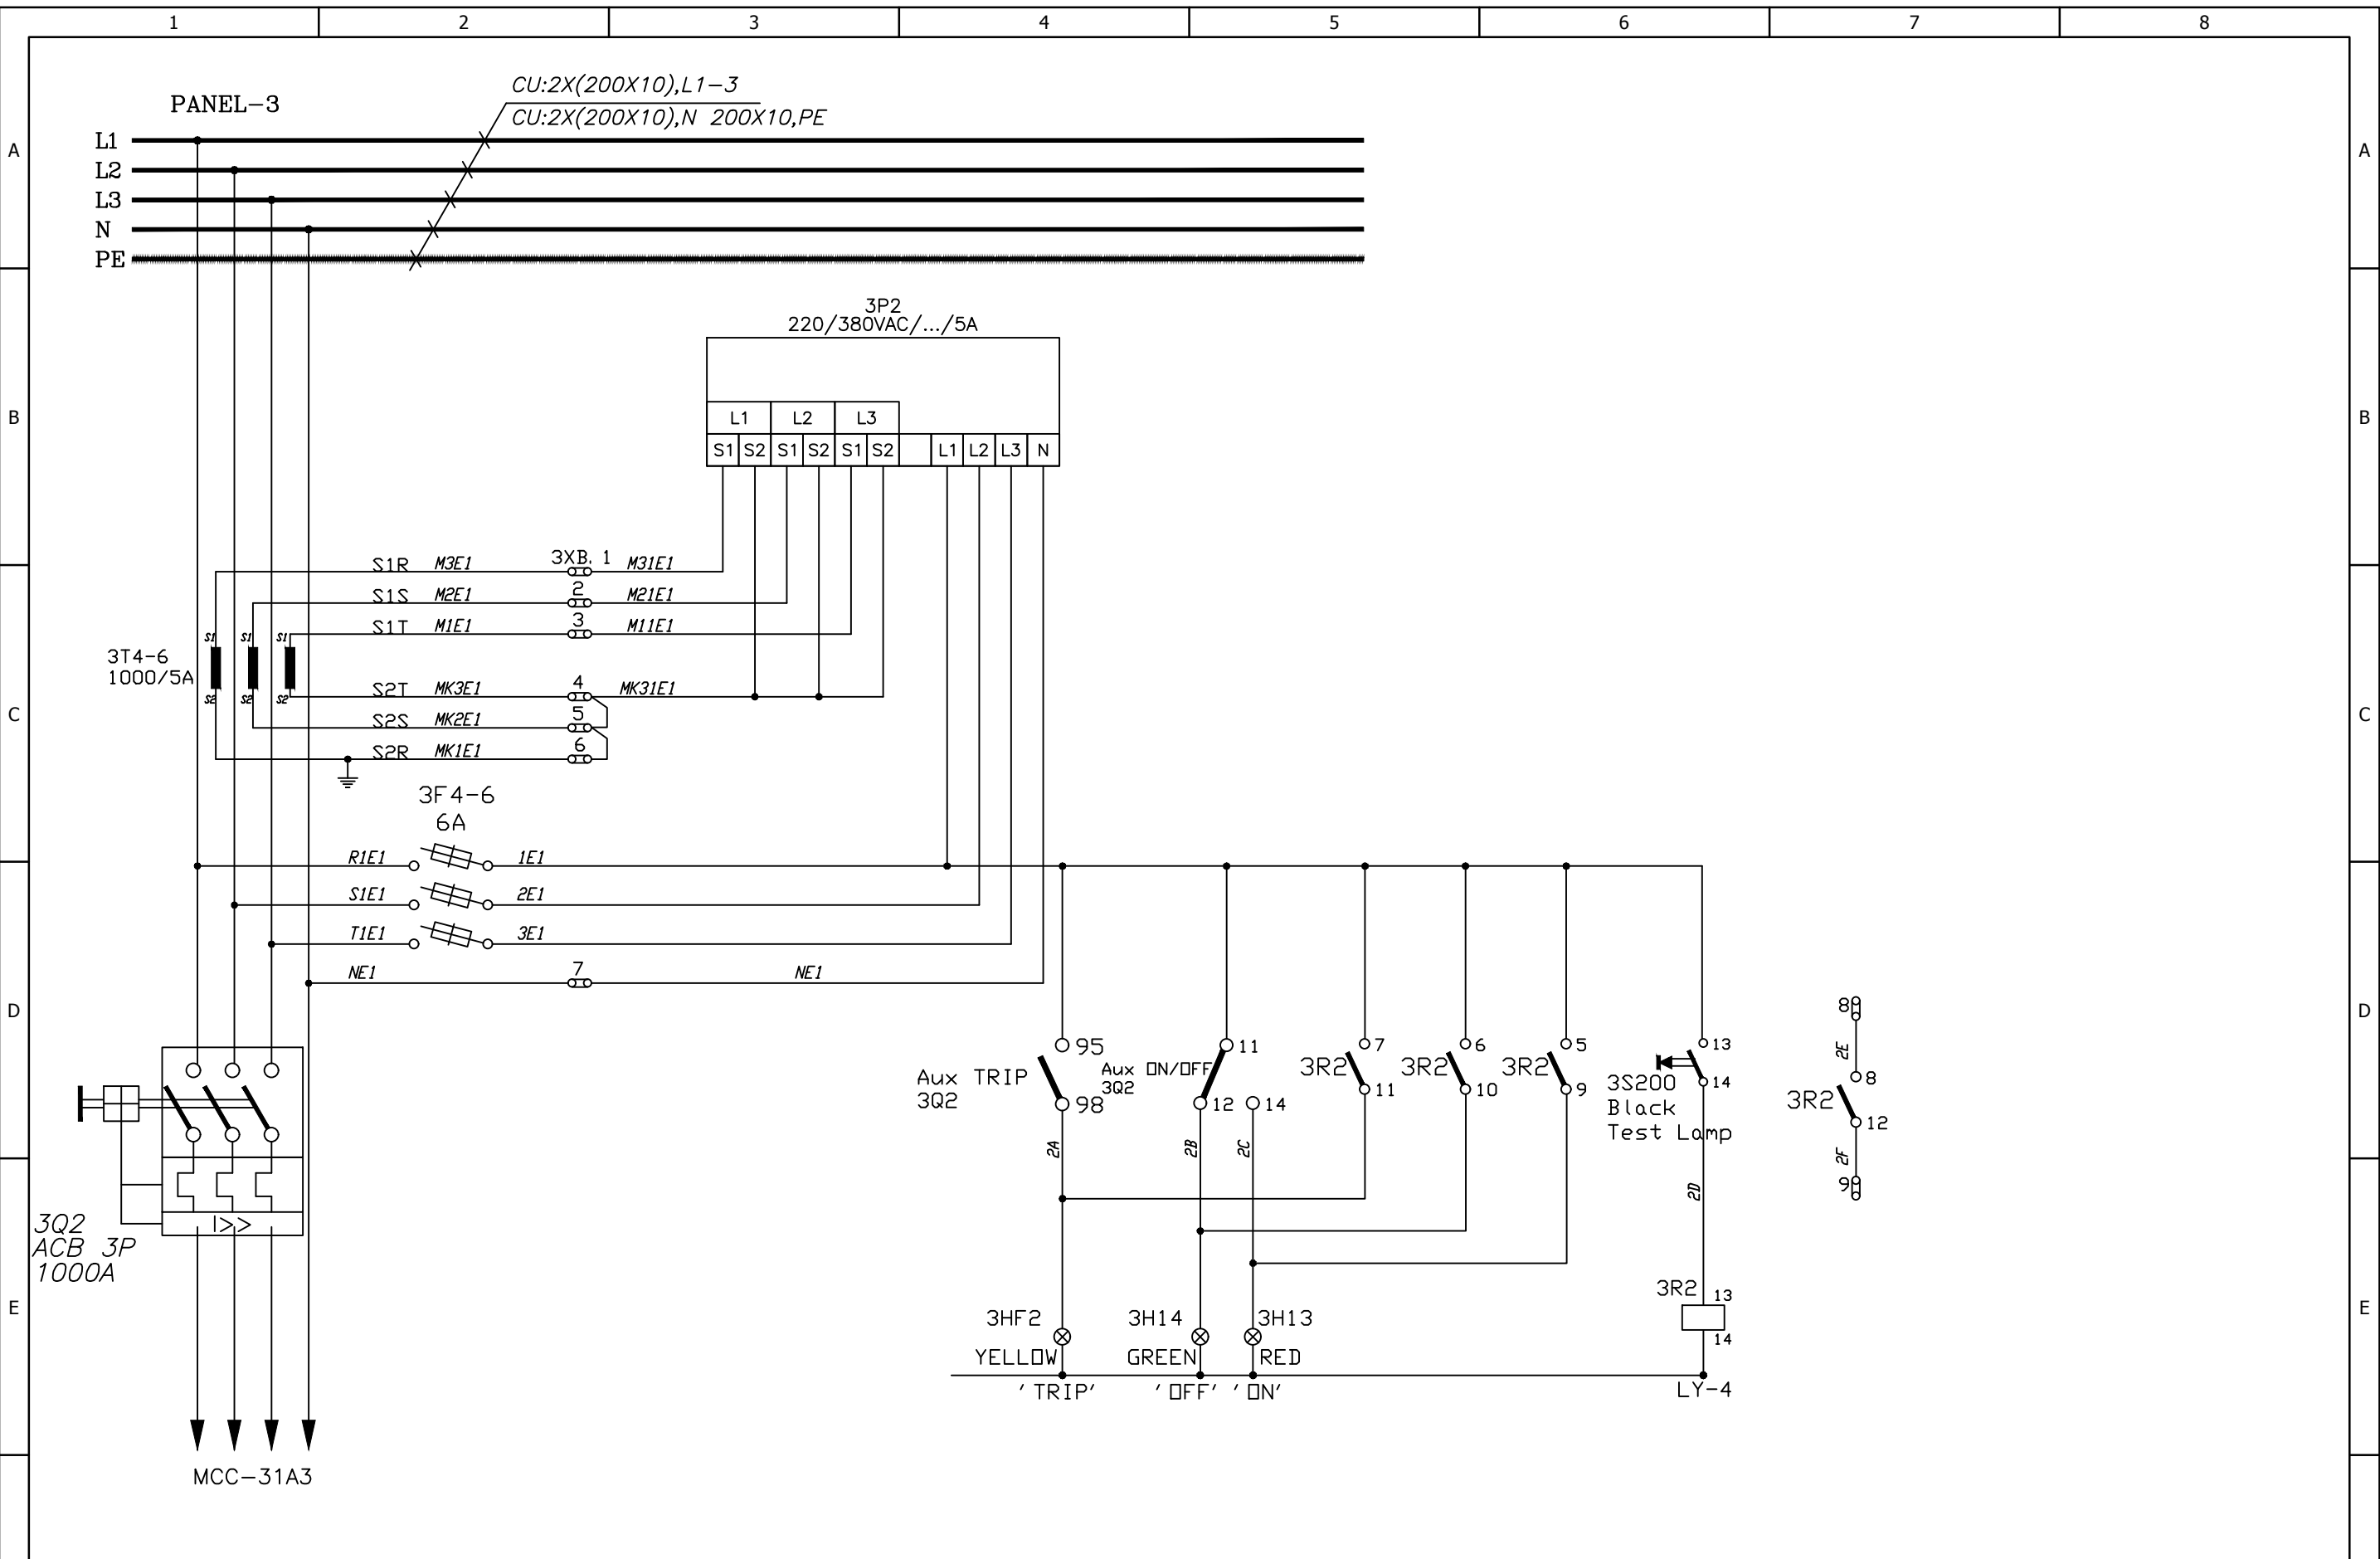


Ind.		Revision	Date	Name	Approved	Based on:	MNA-BED-RE-DWG-001		PT. ABB Sakti Industri		WIRING CONTROL DIAGRAM GA Drawing LVD-31A TEXTURIZING A		Scale	= H00	
R1		First Issued	02.05.2019		Checked	S1							Customer	PT MULTIMAS NABATI ASAHAN	
													Drawing Nbr.	Sh. 1	
													Customer Doc. Nbr.	Cont. 21	


WE RESERVE ALL RIGHTS IN THIS DOCUMENT AND IN THE INFORMATION CONTAINED THEREIN. REPRODUCTION, USE OR DISCLOSURE TO THIRD PARTIES WITHOUT EXPRESS AUTHORITY IS STRICTLY FORBIDDEN.

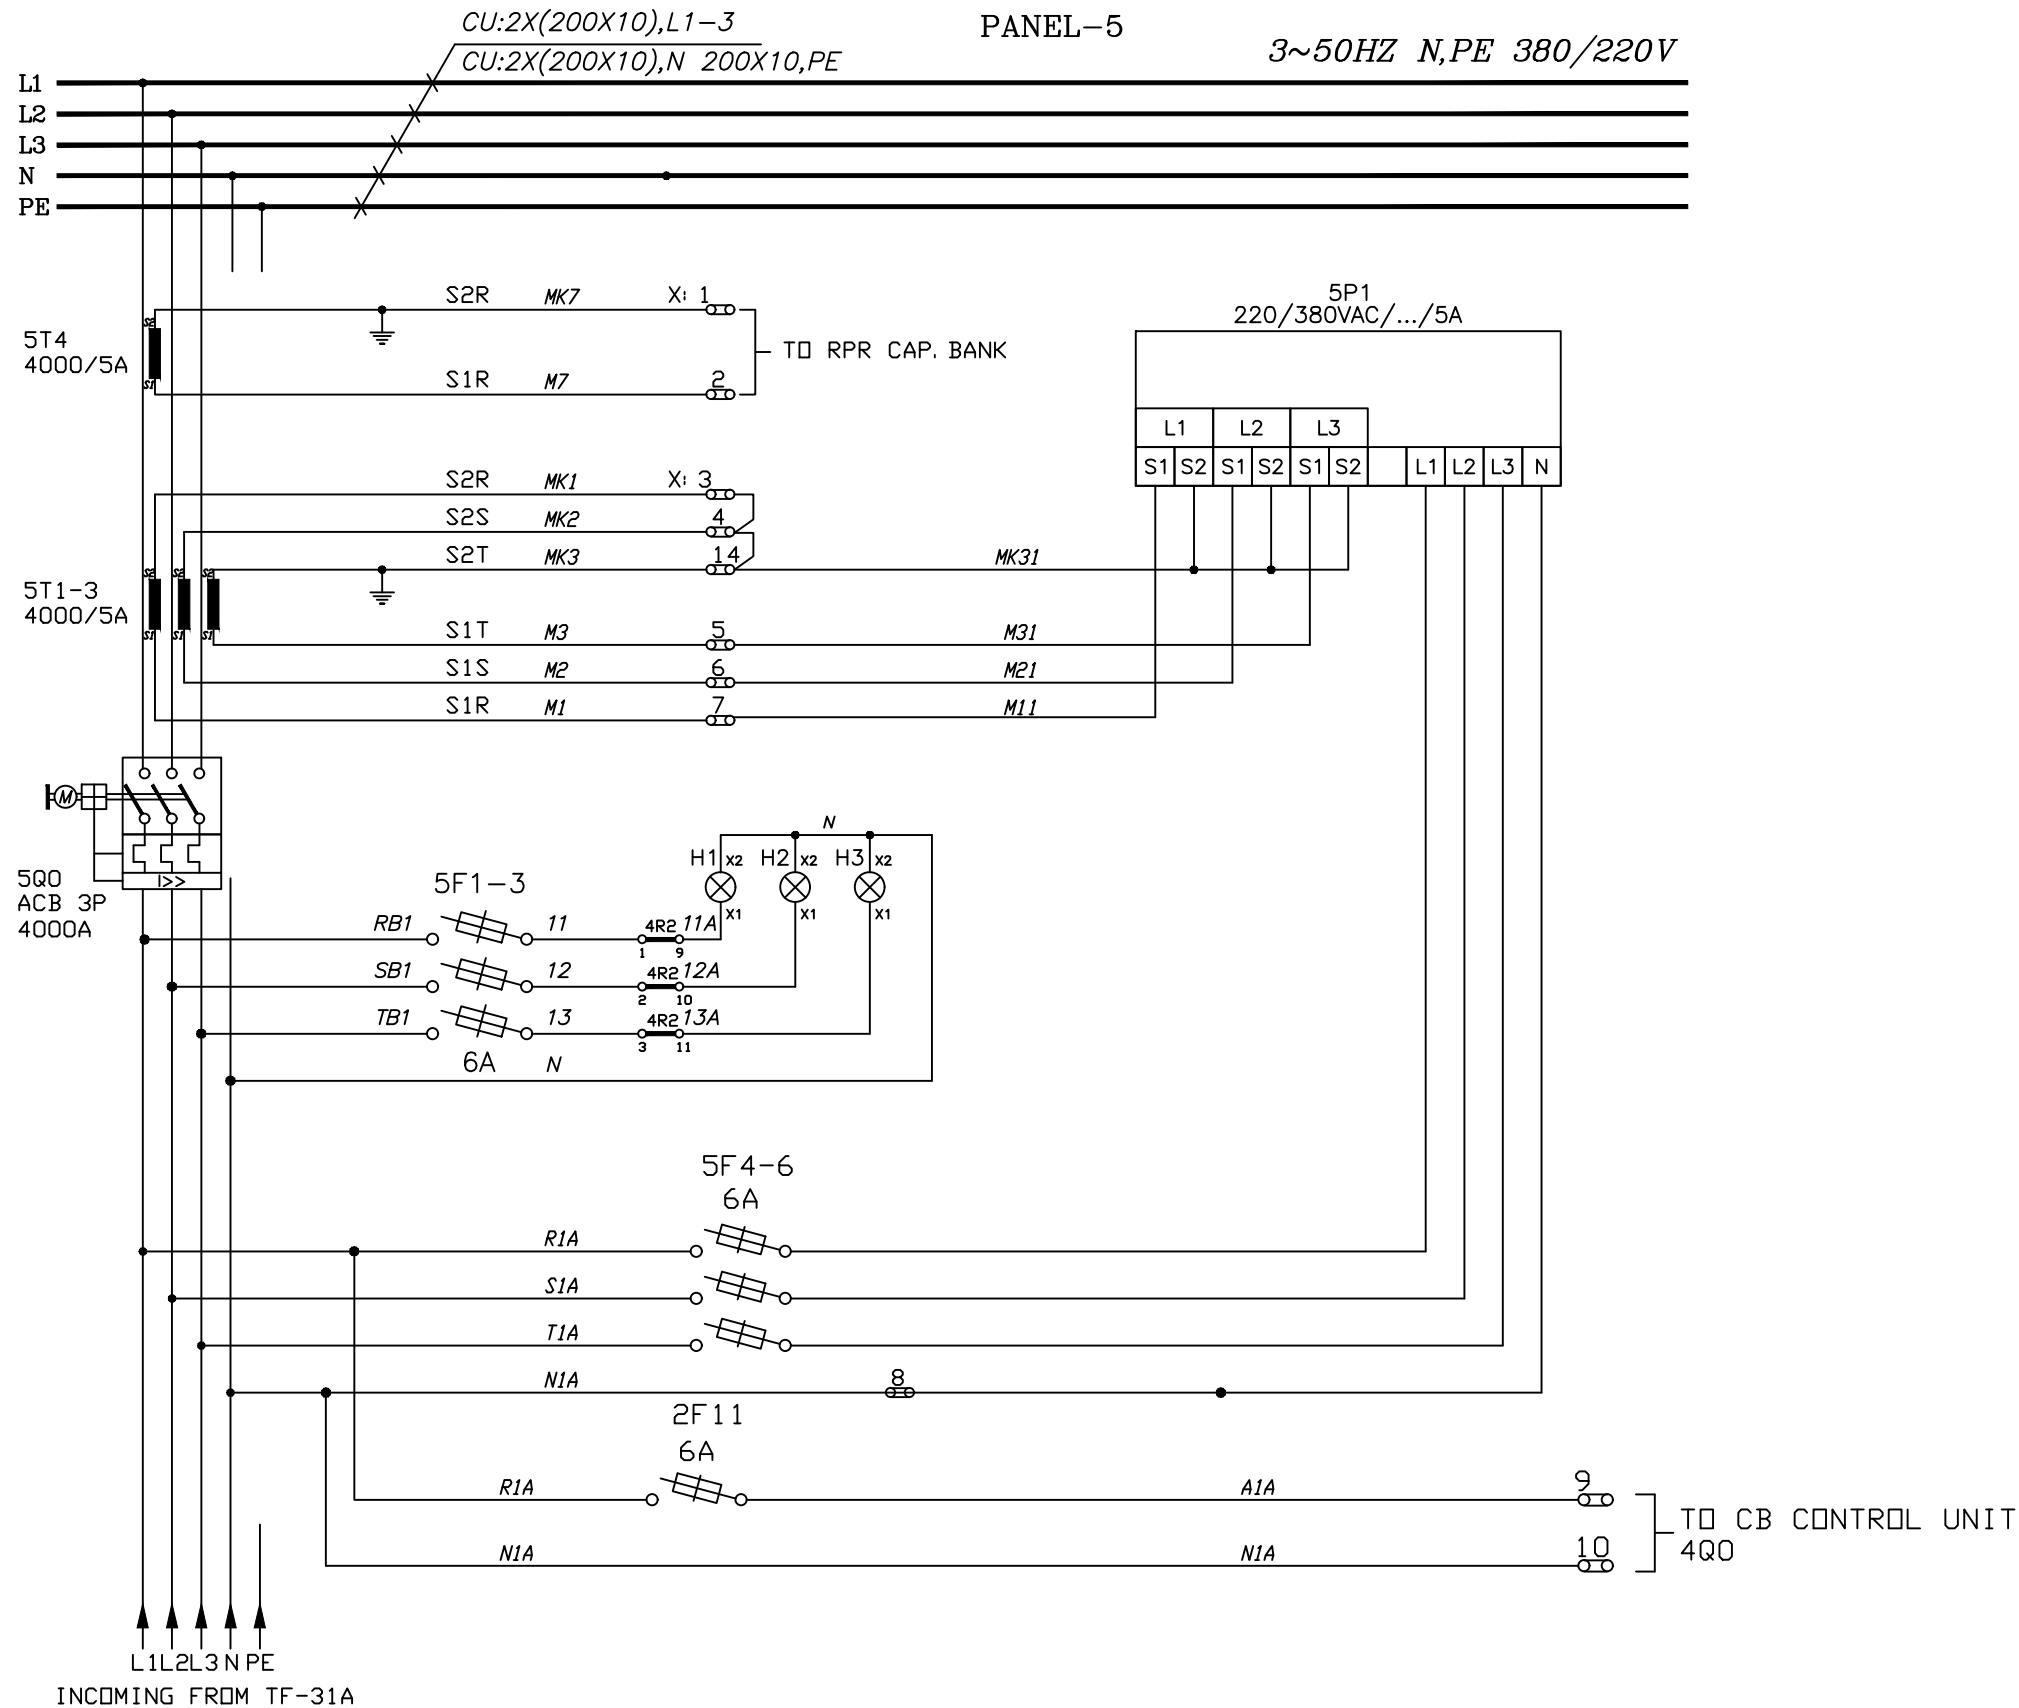


			Date Prep.	13.12.2018	PROJECT TITLE LVD for MNA Serang Plant			WIRING CONTROL DIAGRAM GA Drawing LVD-31A TEXTURIZING A	Scale		= H00
			Prepared	S4					Customer	PT MULTIMAS NABATI ASAHAN	+
R1	First Issued	02.05.2019	Checked	S1		PT. ABB Sakti Industri	Drawing Nbr.			Sh.	1
Ind.	Revision	Date	Name	Approved	S1	Based on:	MNA-BED-RE-DWG-001	Customer Doc. Nbr.		Cont.	21

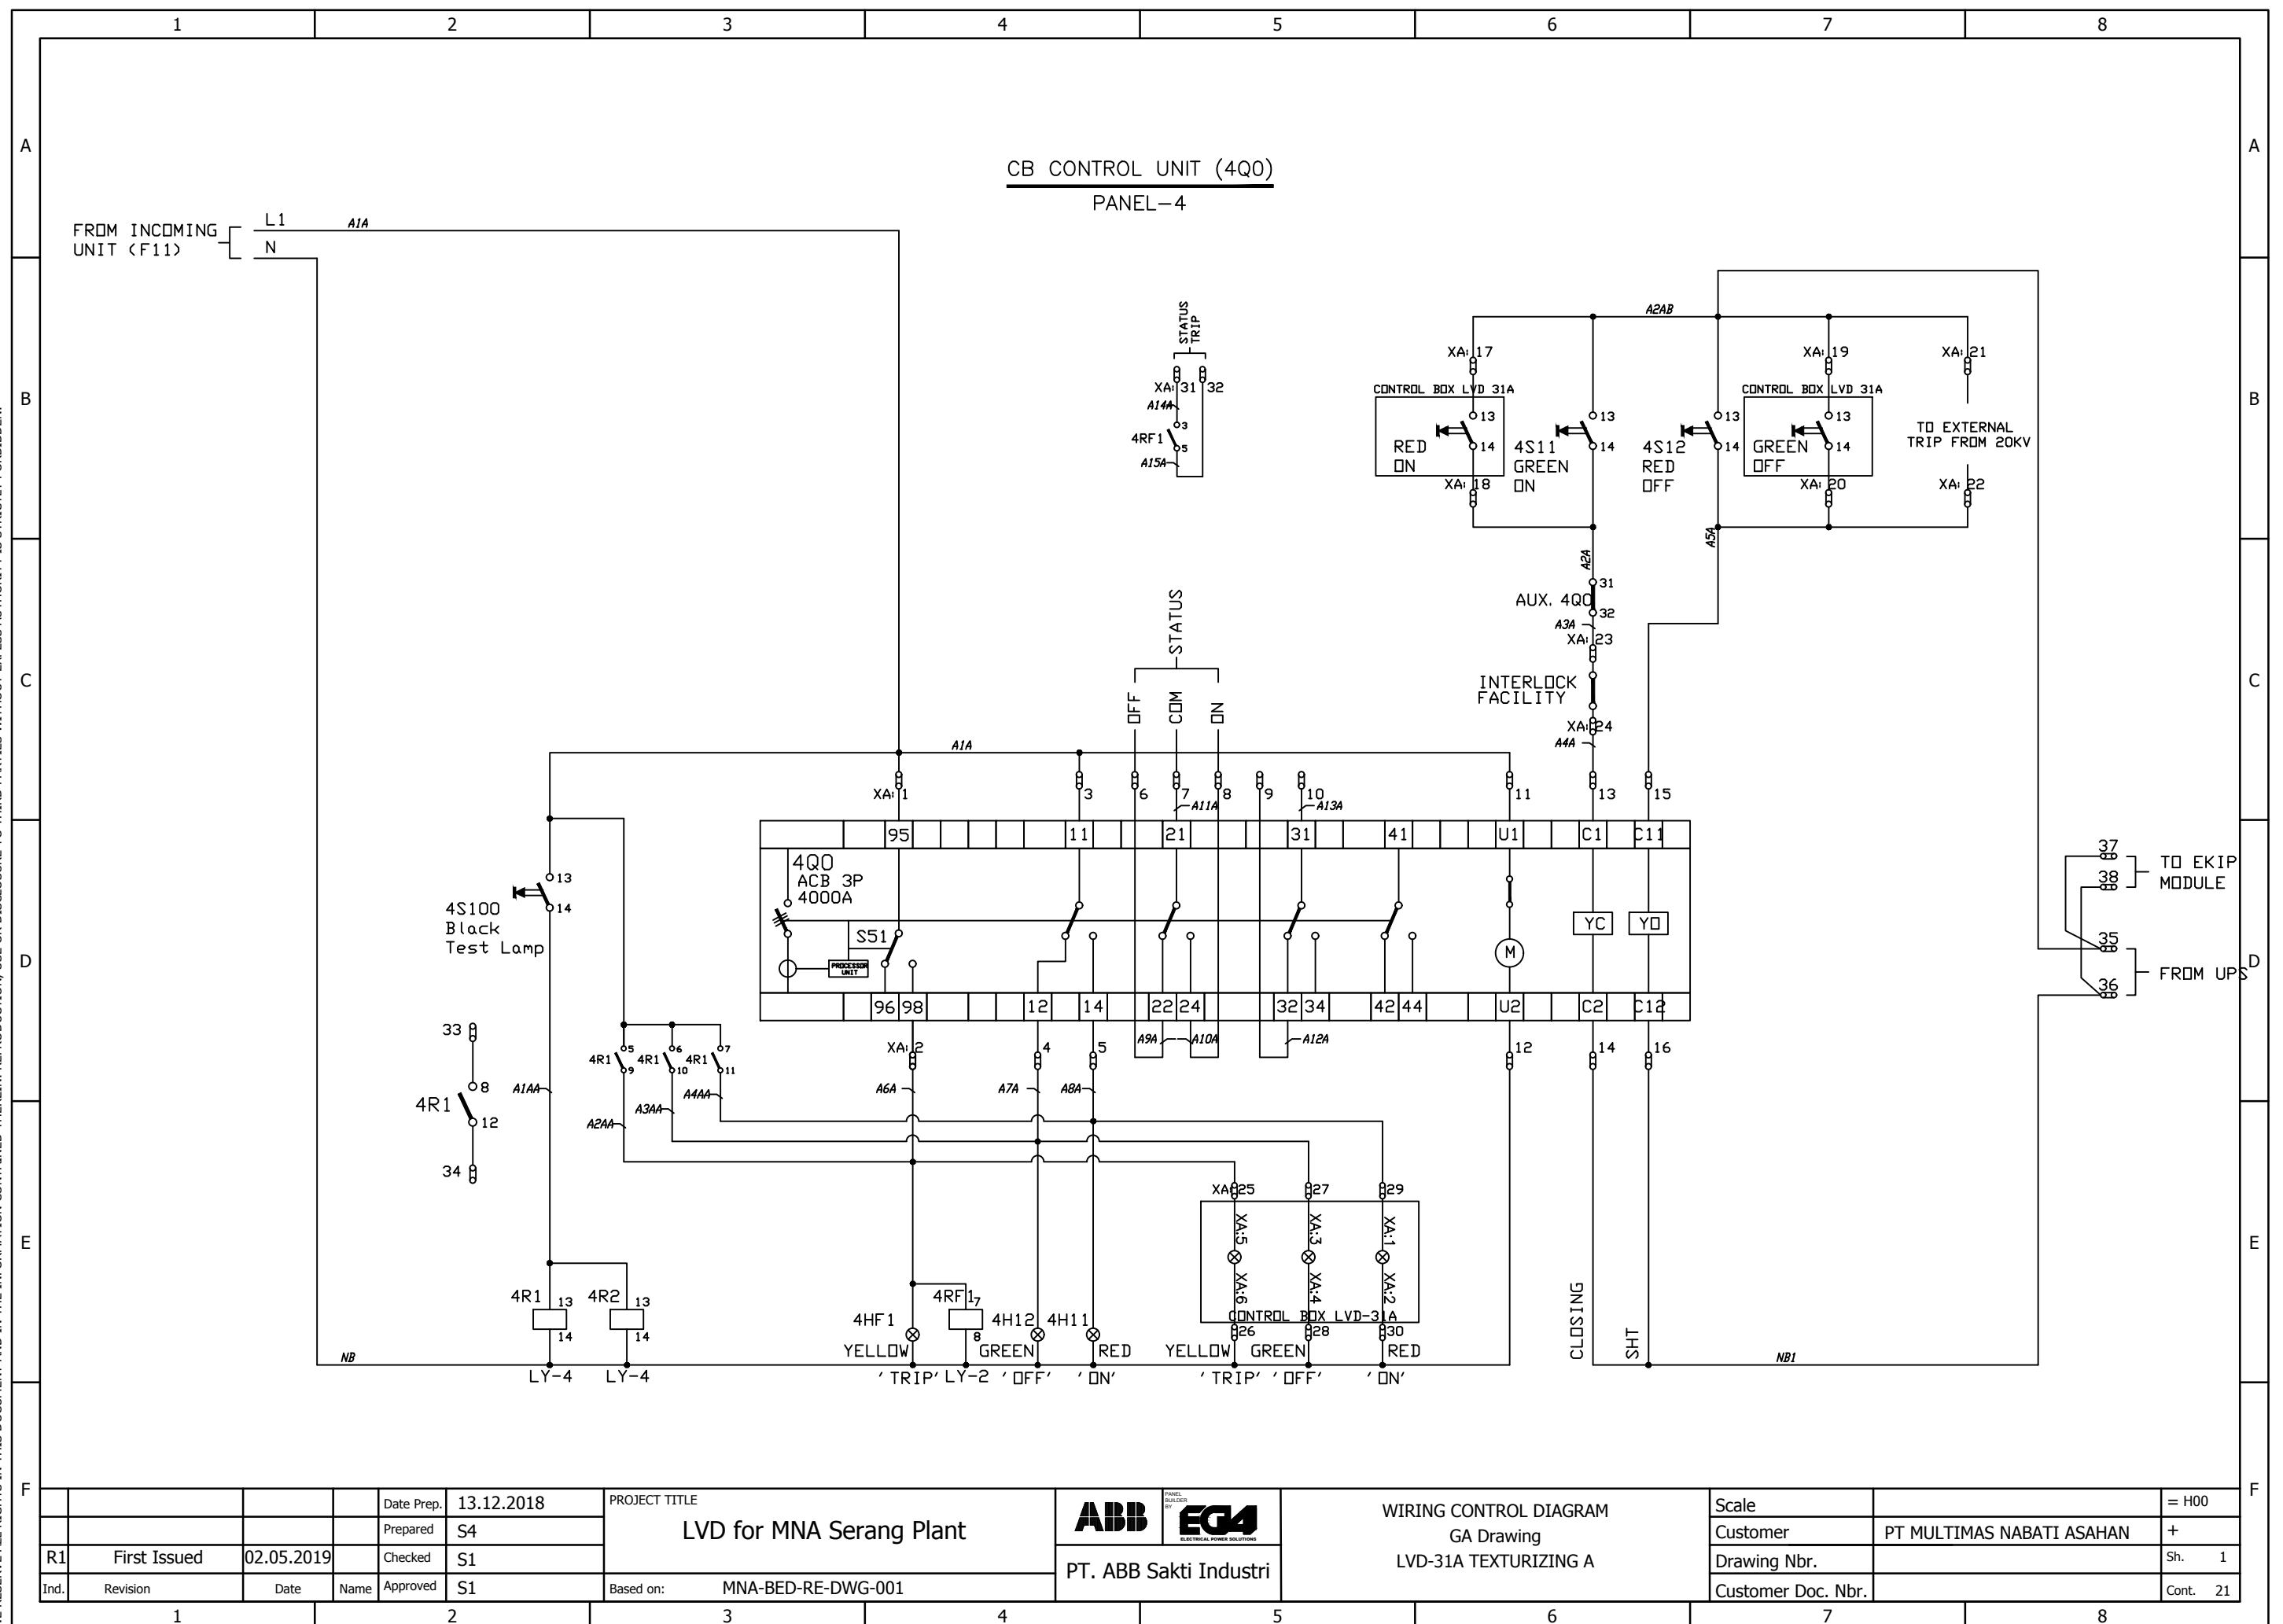

WE RESERVE ALL RIGHTS IN THIS DOCUMENT AND IN THE INFORMATION CONTAINED THEREIN. REPRODUCTION, USE OR DISCLOSURE TO THIRD PARTIES WITHOUT EXPRESS AUTHORITY IS STRICTLY FORBIDDEN.

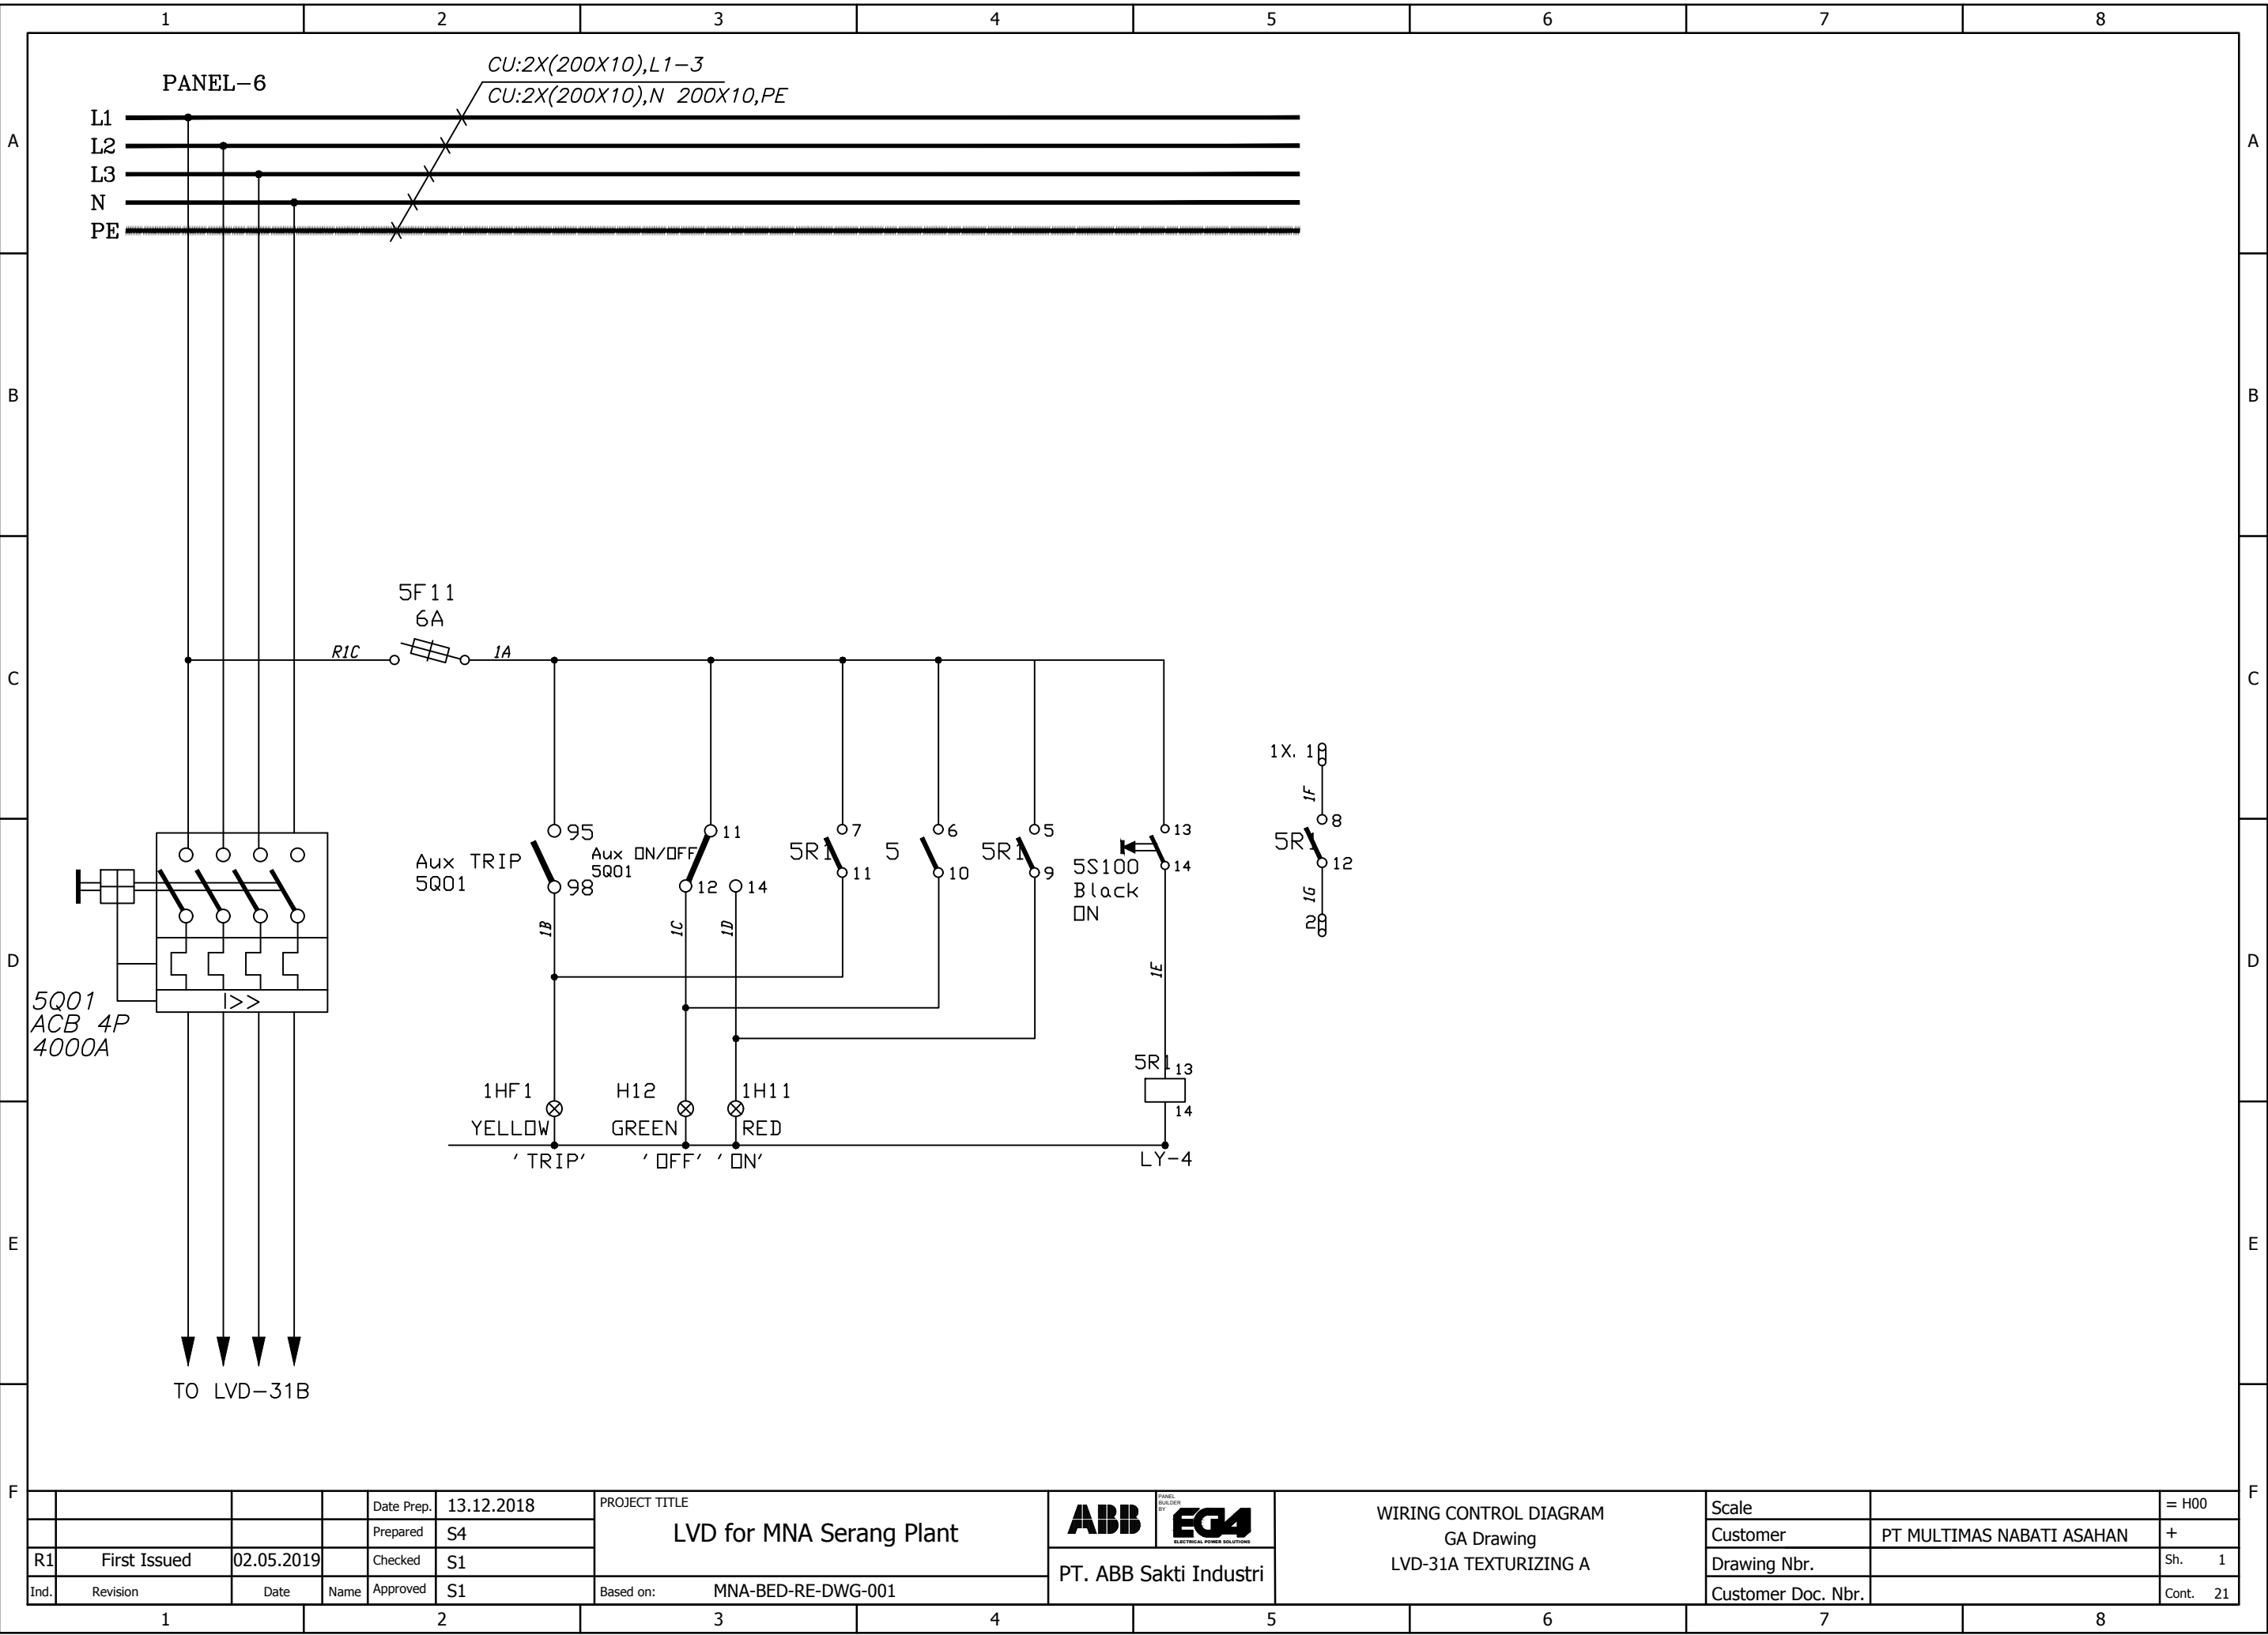

WE RESERVE ALL RIGHTS IN THIS DOCUMENT AND IN THE INFORMATION CONTAINED THEREIN. REPRODUCTION, USE OR DISCLOSURE TO THIRD PARTIES WITHOUT EXPRESS AUTHORITY IS STRICTLY FORBIDDEN.

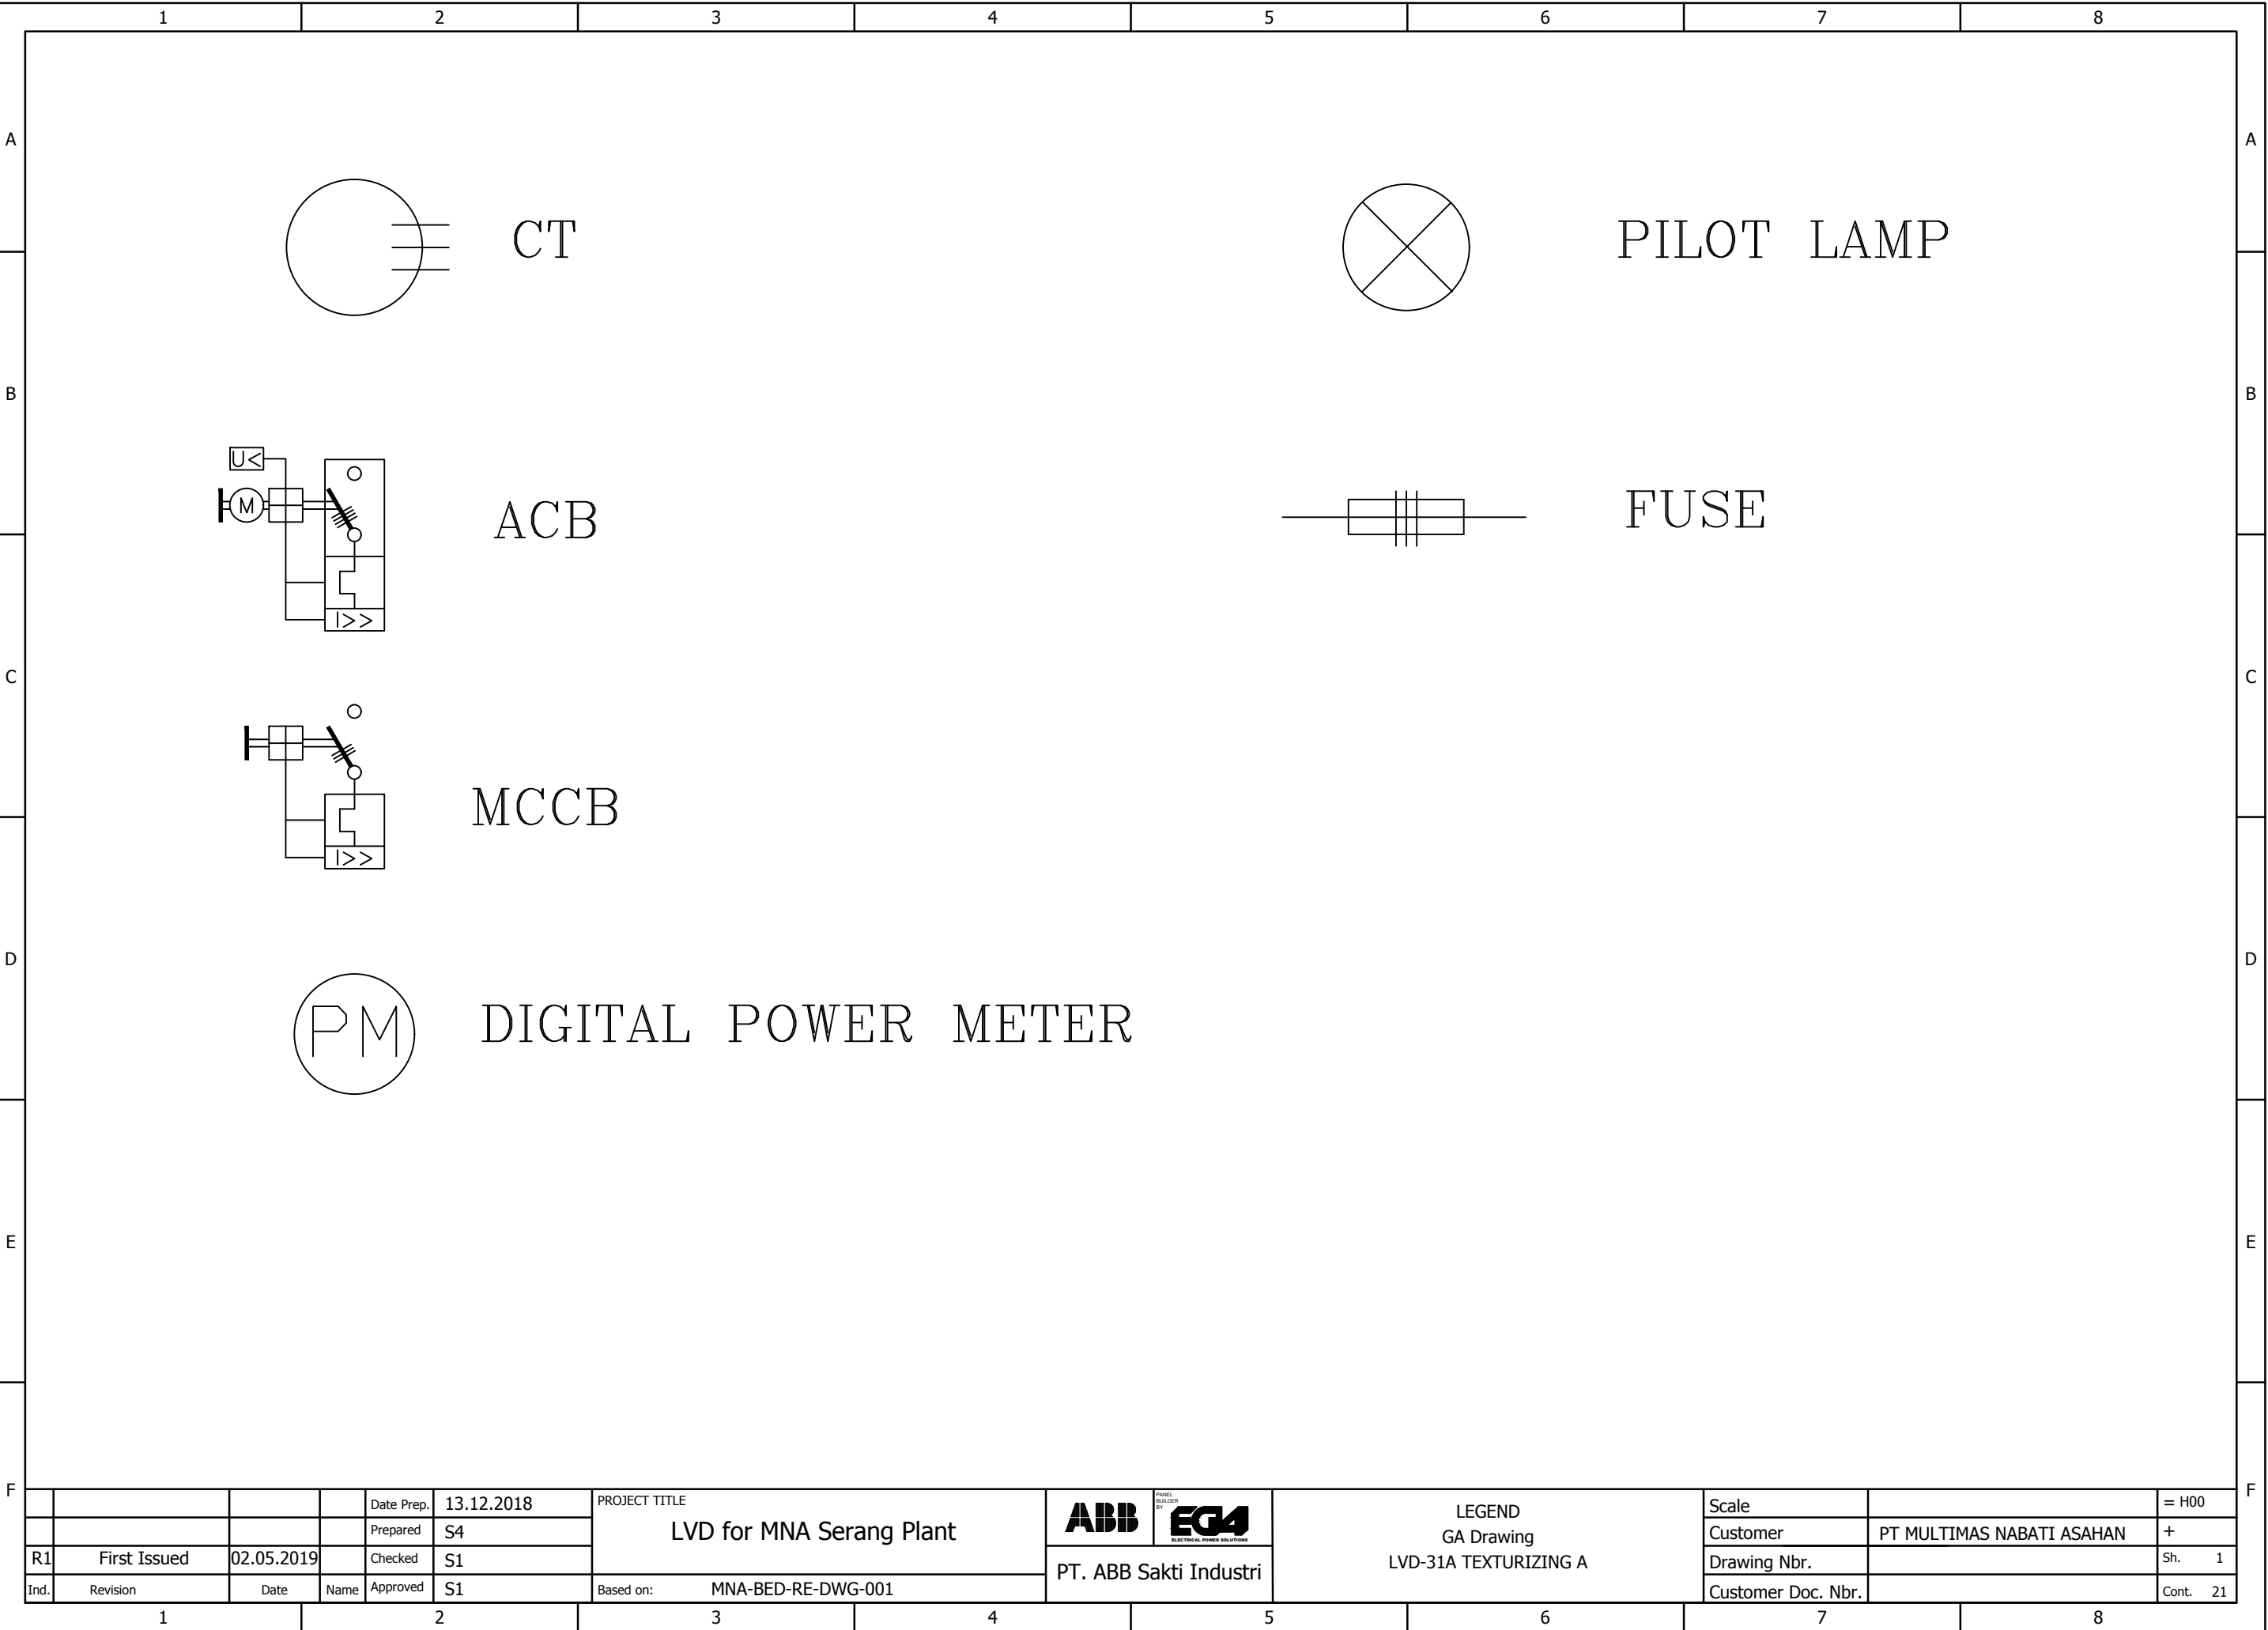

WE RESERVE ALL RIGHTS IN THIS DOCUMENT AND IN THE INFORMATION CONTAINED THEREIN. REPRODUCTION, USE OR DISCLOSURE TO THIRD PARTIES WITHOUT EXPRESS AUTHORITY IS STRICTLY FORBIDDEN.

	1	2	3	4	5	6	7	8
A	N O	DESCRIPTION	TECHNICAL DATA	QTY	DESIGNATION			
		OUTGOING						
B	1	Fuse Carrier 6A	AXLE	30	1F1-12 ; 2F1-12 ; 3F1-6			
	2	Pilot Lamp (LED) 220Vac/50Hz, Red	AXLE	10	1,2H12,14,16,18 ; 3H12,14			
	3	Pilot Lamp (LED) 220Vac/50Hz, Yellow	AXLE	10	1,2HF1-4 ; 3HF1-2			
	4	Pilot Lamp (LED) 220Vac/50Hz, Green	AXLE	10	1,3H11,13,15,17 ; 3H11,13			
	5	DIGITAL POWER METER (*)	ABB, M2M ETHERNET	10	1,2P1-4 ; 3P1-2			
	6	CT 1000/5A CL.0.5 10VA	Howig, HG 82-1000	6	3T1-6			
	7	CT 800/5A CL.1 10VA	Howig, HG 50I-800	12	2T1-12			
C	8	CT 400/5A CL.1 5VA	Howig, HG 40I-400	6	1T1-6			
	9	CT 200/5A CL.1 5VA	Howig, HG 30I-200	3	1T7-9			
	10	CT 100/5A CL.1 2.5VA	Howig, HG 30I-100	3	1T10-12			
	11	ACB 3P 1000A, 66KA, FT, Ekip Dip LI (*)	ABB, E1.2N10 F/T	2	3Q1-2			
	12	+ Padlocks For E1.2 (*)	ABB,	2	-			
	13	MCCB 3P 320-800A, 70KA (*)	ABB, T6H 800 PR221DS-LS/I	2	2Q1-2			
	14	+ Auxiliary Contact For T5-T6 (*)	ABB, Aux-C 3Q 1SY	2	-			
D	15	+ Extended Rotary Handles For T5 (*)	ABB, RHE	2	-			
	16	MCCB 3P 252-630A, 70KA (*)	ABB, T5H PR221DS-LS/I-630	2	2Q3-4			
	17	+ Auxiliary Contact For T5-T6 (*)	ABB, Aux-C 3Q 1SY	2	-			
	18	+ Extended Rotary Handles For T5 (*)	ABB, RHE	2	-			
	19	MCCB 3P 160-400A, 70KA (*)	ABB, T5H PR221DS-LS/I-400	2	1Q1-2			
	20	+ Auxiliary Contact For T5-T6 (*)	ABB, Aux-C 3Q 1SY	2	-			
	21	+ Extended Rotary Handles For T5 (*)	ABB, RHE	2	-			
E	22							
	23							
	24							
	25							
	26							
F								

WE RESERVE ALL RIGHTS IN THIS DOCUMENT AND IN THE INFORMATION CONTAINED THEREIN. REPRODUCTION, USE OR DISCLOSURE TO THIRD PARTIES WITHOUT EXPRESS AUTHORITY IS STRICTLY FORBIDDEN.

1		2		3		4		5		6		7		8		
A	N O		DESCRIPTION		TECHNICAL DATA		QTY		DESIGNATION							
			OUTGOING													
B	1	MCCB 3P 140-200A, 70KA (*)		ABB, XT4H TMA 200		1		1Q3								
	2	+ Auxiliary Contact For XT2/XT4 (*)		ABB, Aux-C 2Q 1SY		1		-								
	3	+ Extended Rotary Handles For XT2/XT4 (*)		ABB, RHE		1		-								
	4	MCCB 3P 56-80A, 70KA (*)		ABB, XT2H TMA-80		1		1Q4								
	5	+ Auxiliary Contact For XT2/XT4 (*)		ABB, Aux-C 2Q 1SY		1		-								
	6	+ Extended Rotary Handles For XT2/XT4 (*)		ABB, RHE		1		-								
C	7	Control Relay 220Vac		Omron, LY-4		10		1,2R1-4 ; 3R1-2								
	8	Control Relay 220Vac		Omron, LY-2		2		1,2RF1								
	9	Push Button Test Lamp , 1NO, Black		Ega		10		1,2S100-400 ; 3S100-200								
	10															
	11															
	12															
	13															
	14															
	15															
	16															
D	17															
	18															
	19															
	20															
	21															
	22															
E	23															
	24															
	25															
	26															
F				Date Prep.	13.12.2018	PROJECT TITLE LVD for MNA Serang Plant		ABB PANEL BUILDER BY EG4 ELECTRICAL POWER SOLUTIONS	COMPONENT LIST GA Drawing LVD-31A TEXTURIZING A		Scale		= H00			
				Prepared	S4						Customer		PT MULTIMAS NABATI ASAHAN		+	
	R1	First Issued	02.05.2019		Checked						S1	Drawing Nbr.				Sh. 1
	Ind.	Revision	Date	Name	Approved	S1	Based on: MNA-BED-RE-DWG-001				Customer Doc. Nbr.		Cont. 21			
	1		2		3		4		5		6		7		8	