




WE RESERVE ALL RIGHTS IN THIS DOCUMENT AND IN THE INFORMATION CONTAINED THEREIN. REPRODUCTION, USE OR DISCLOSURE TO THIRD PARTIES WITHOUT EXPRESS AUTHORITY IS STRICTLY FORBIDDEN.

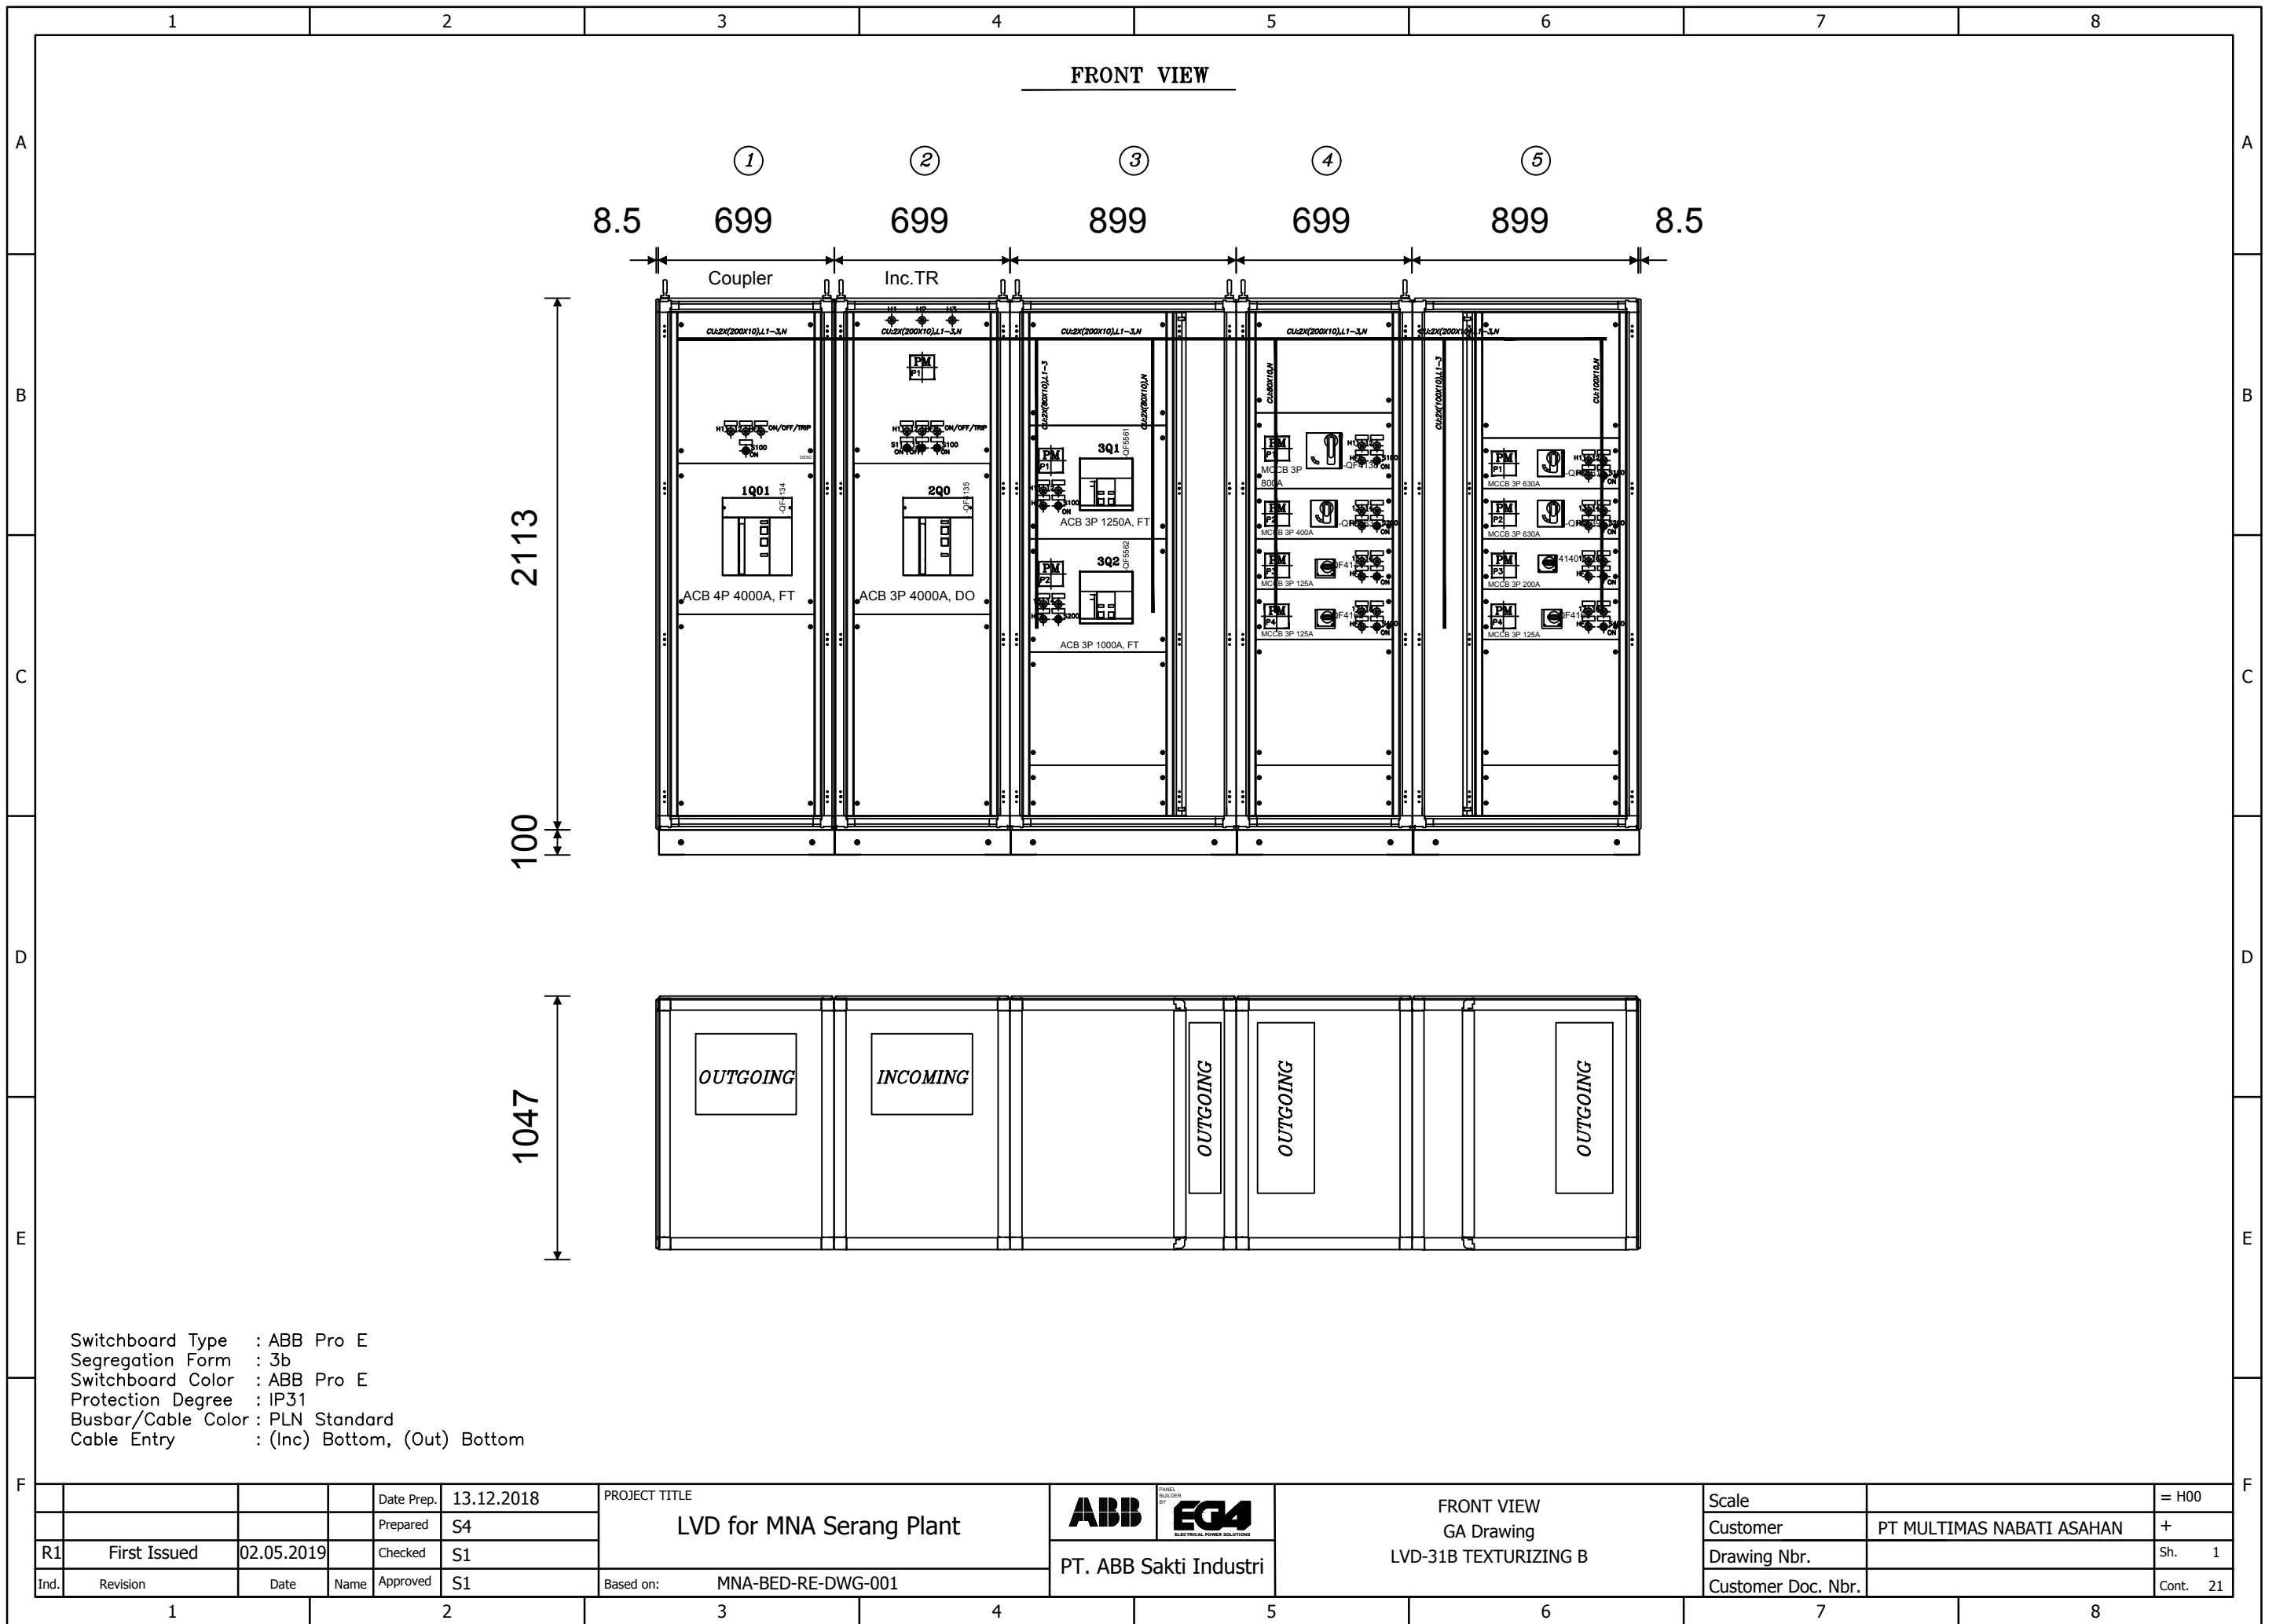

WE RESERVE ALL RIGHTS IN THIS DOCUMENT AND IN THE INFORMATION CONTAINED THEREIN. REPRODUCTION, USE OR DISCLOSURE TO THIRD PARTIES WITHOUT EXPRESS AUTHORITY IS STRICTLY FORBIDDEN.

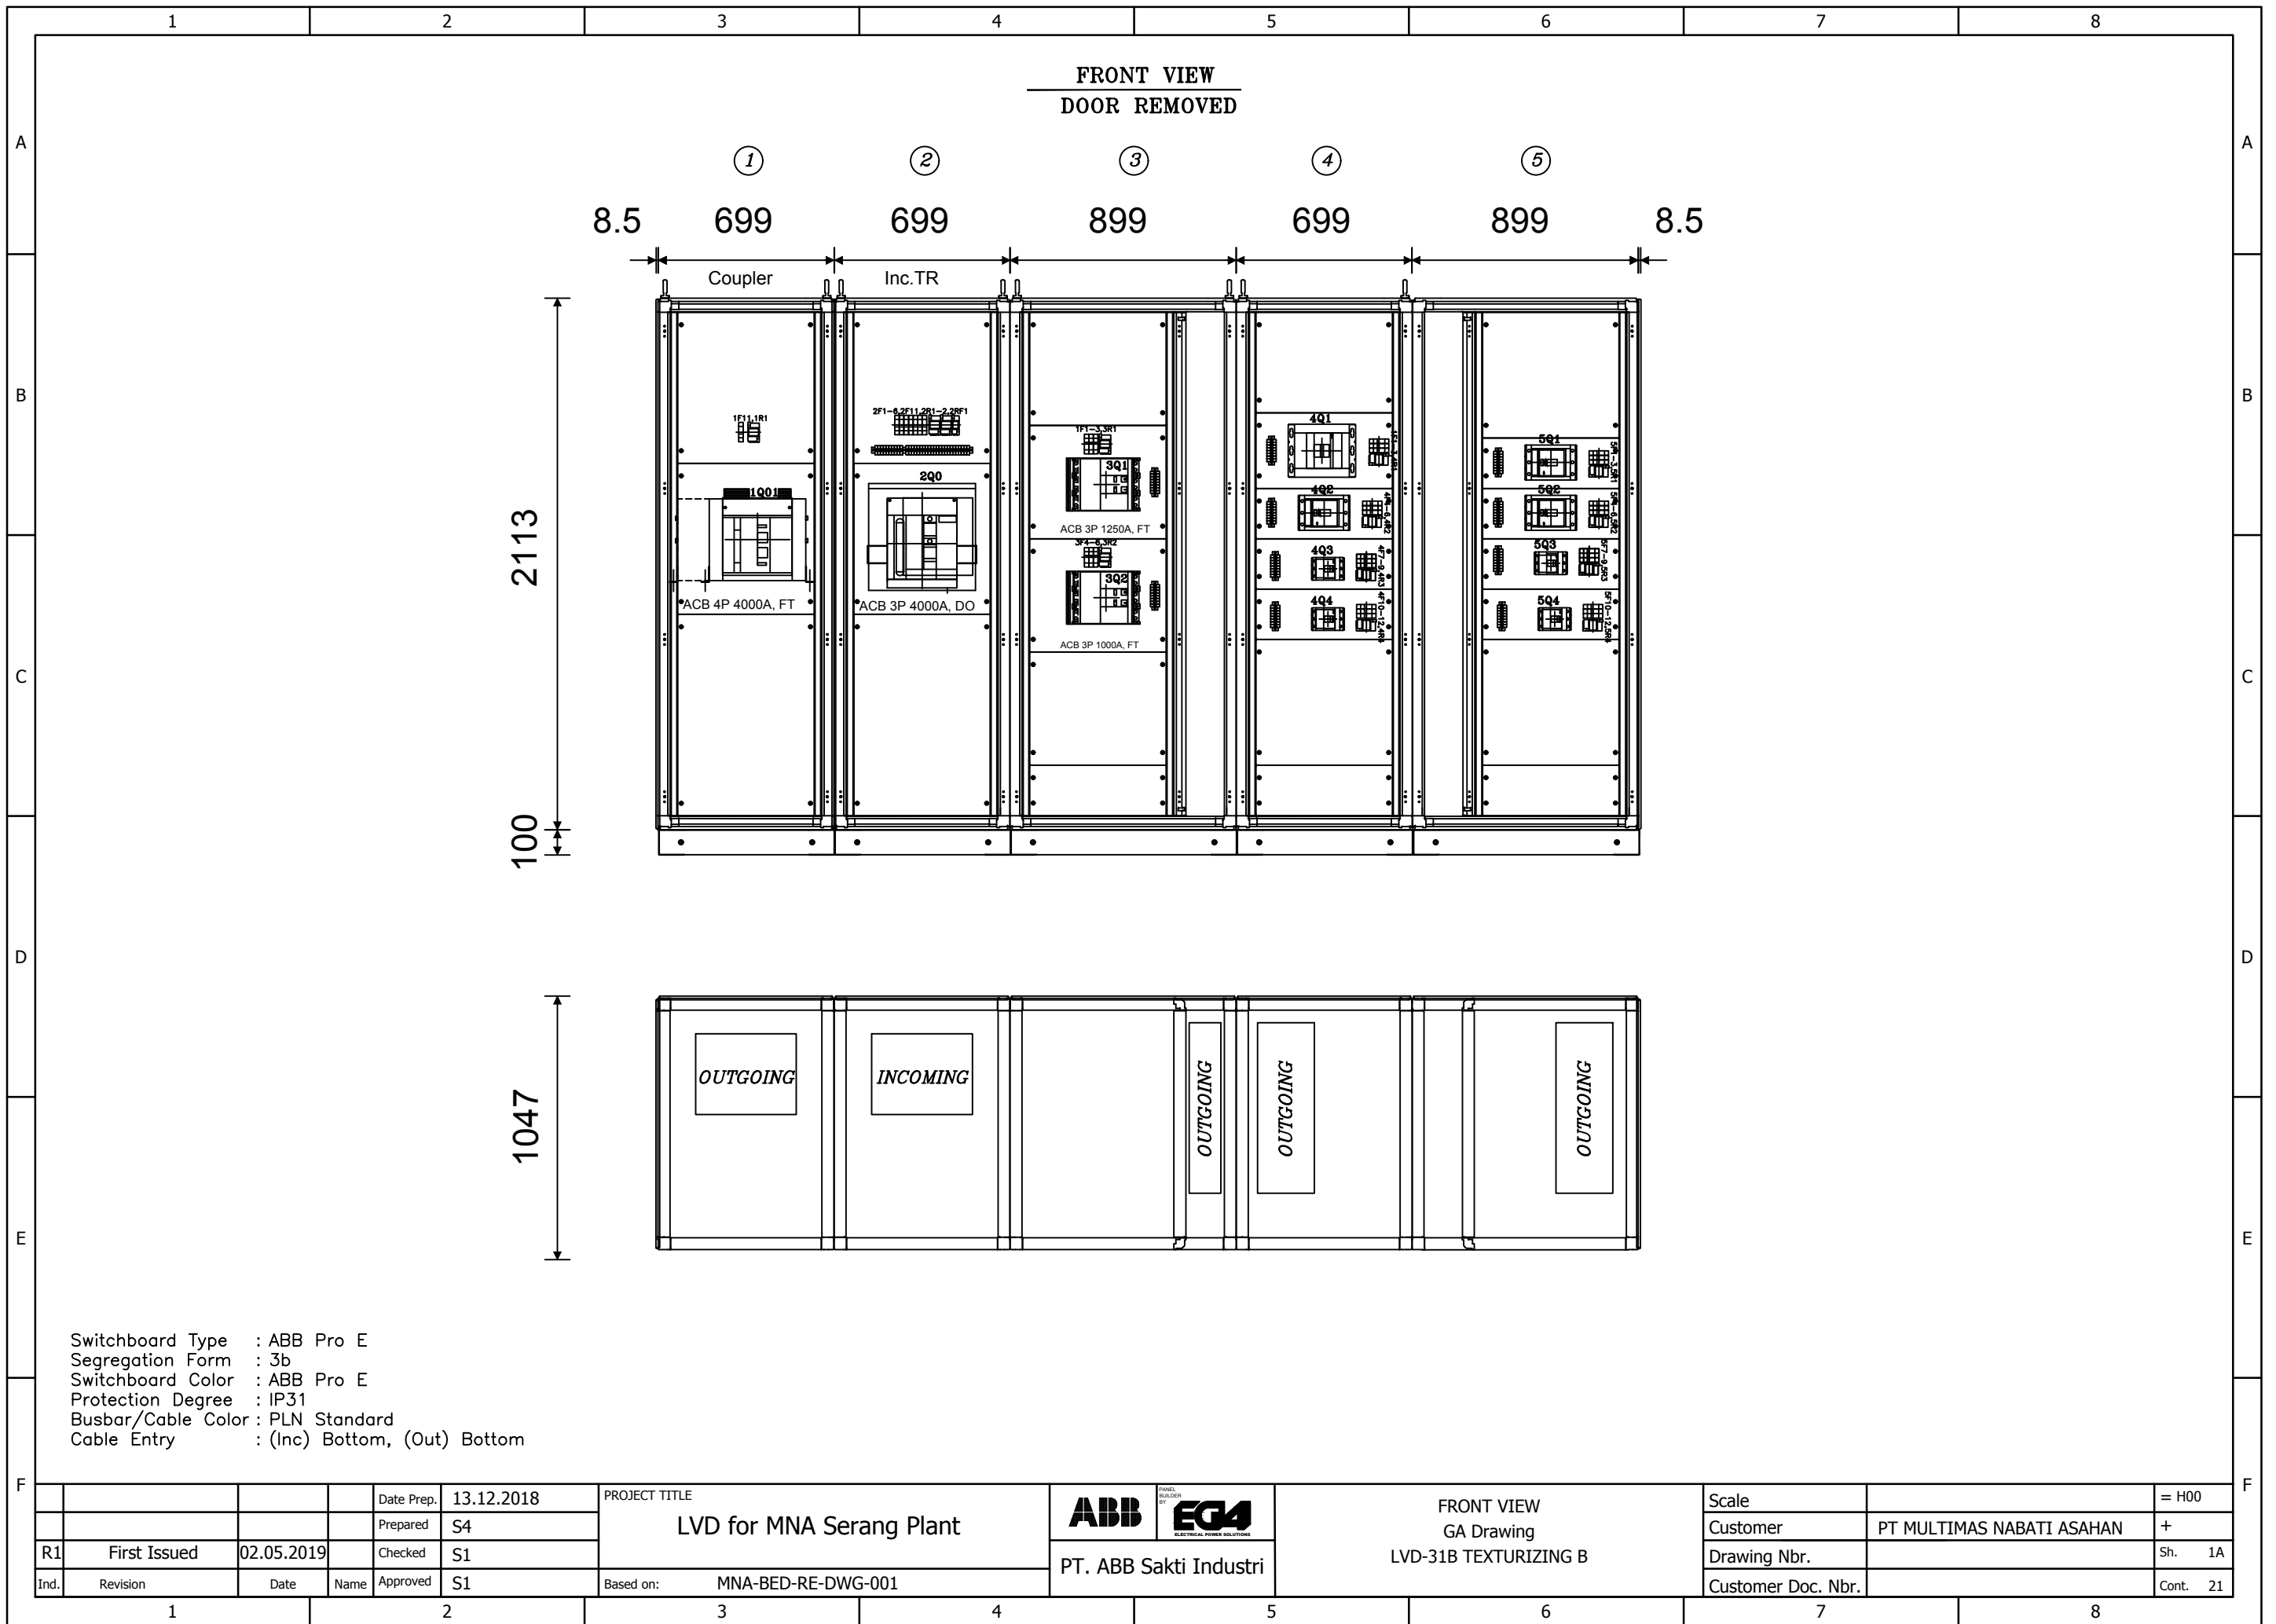


WE RESERVE ALL RIGHTS IN THIS DOCUMENT AND IN THE INFORMATION CONTAINED THEREIN. REPRODUCTION, USE OR DISCLOSURE TO THIRD PARTIES WITHOUT EXPRESS AUTHORITY IS STRICTLY FORBIDDEN.

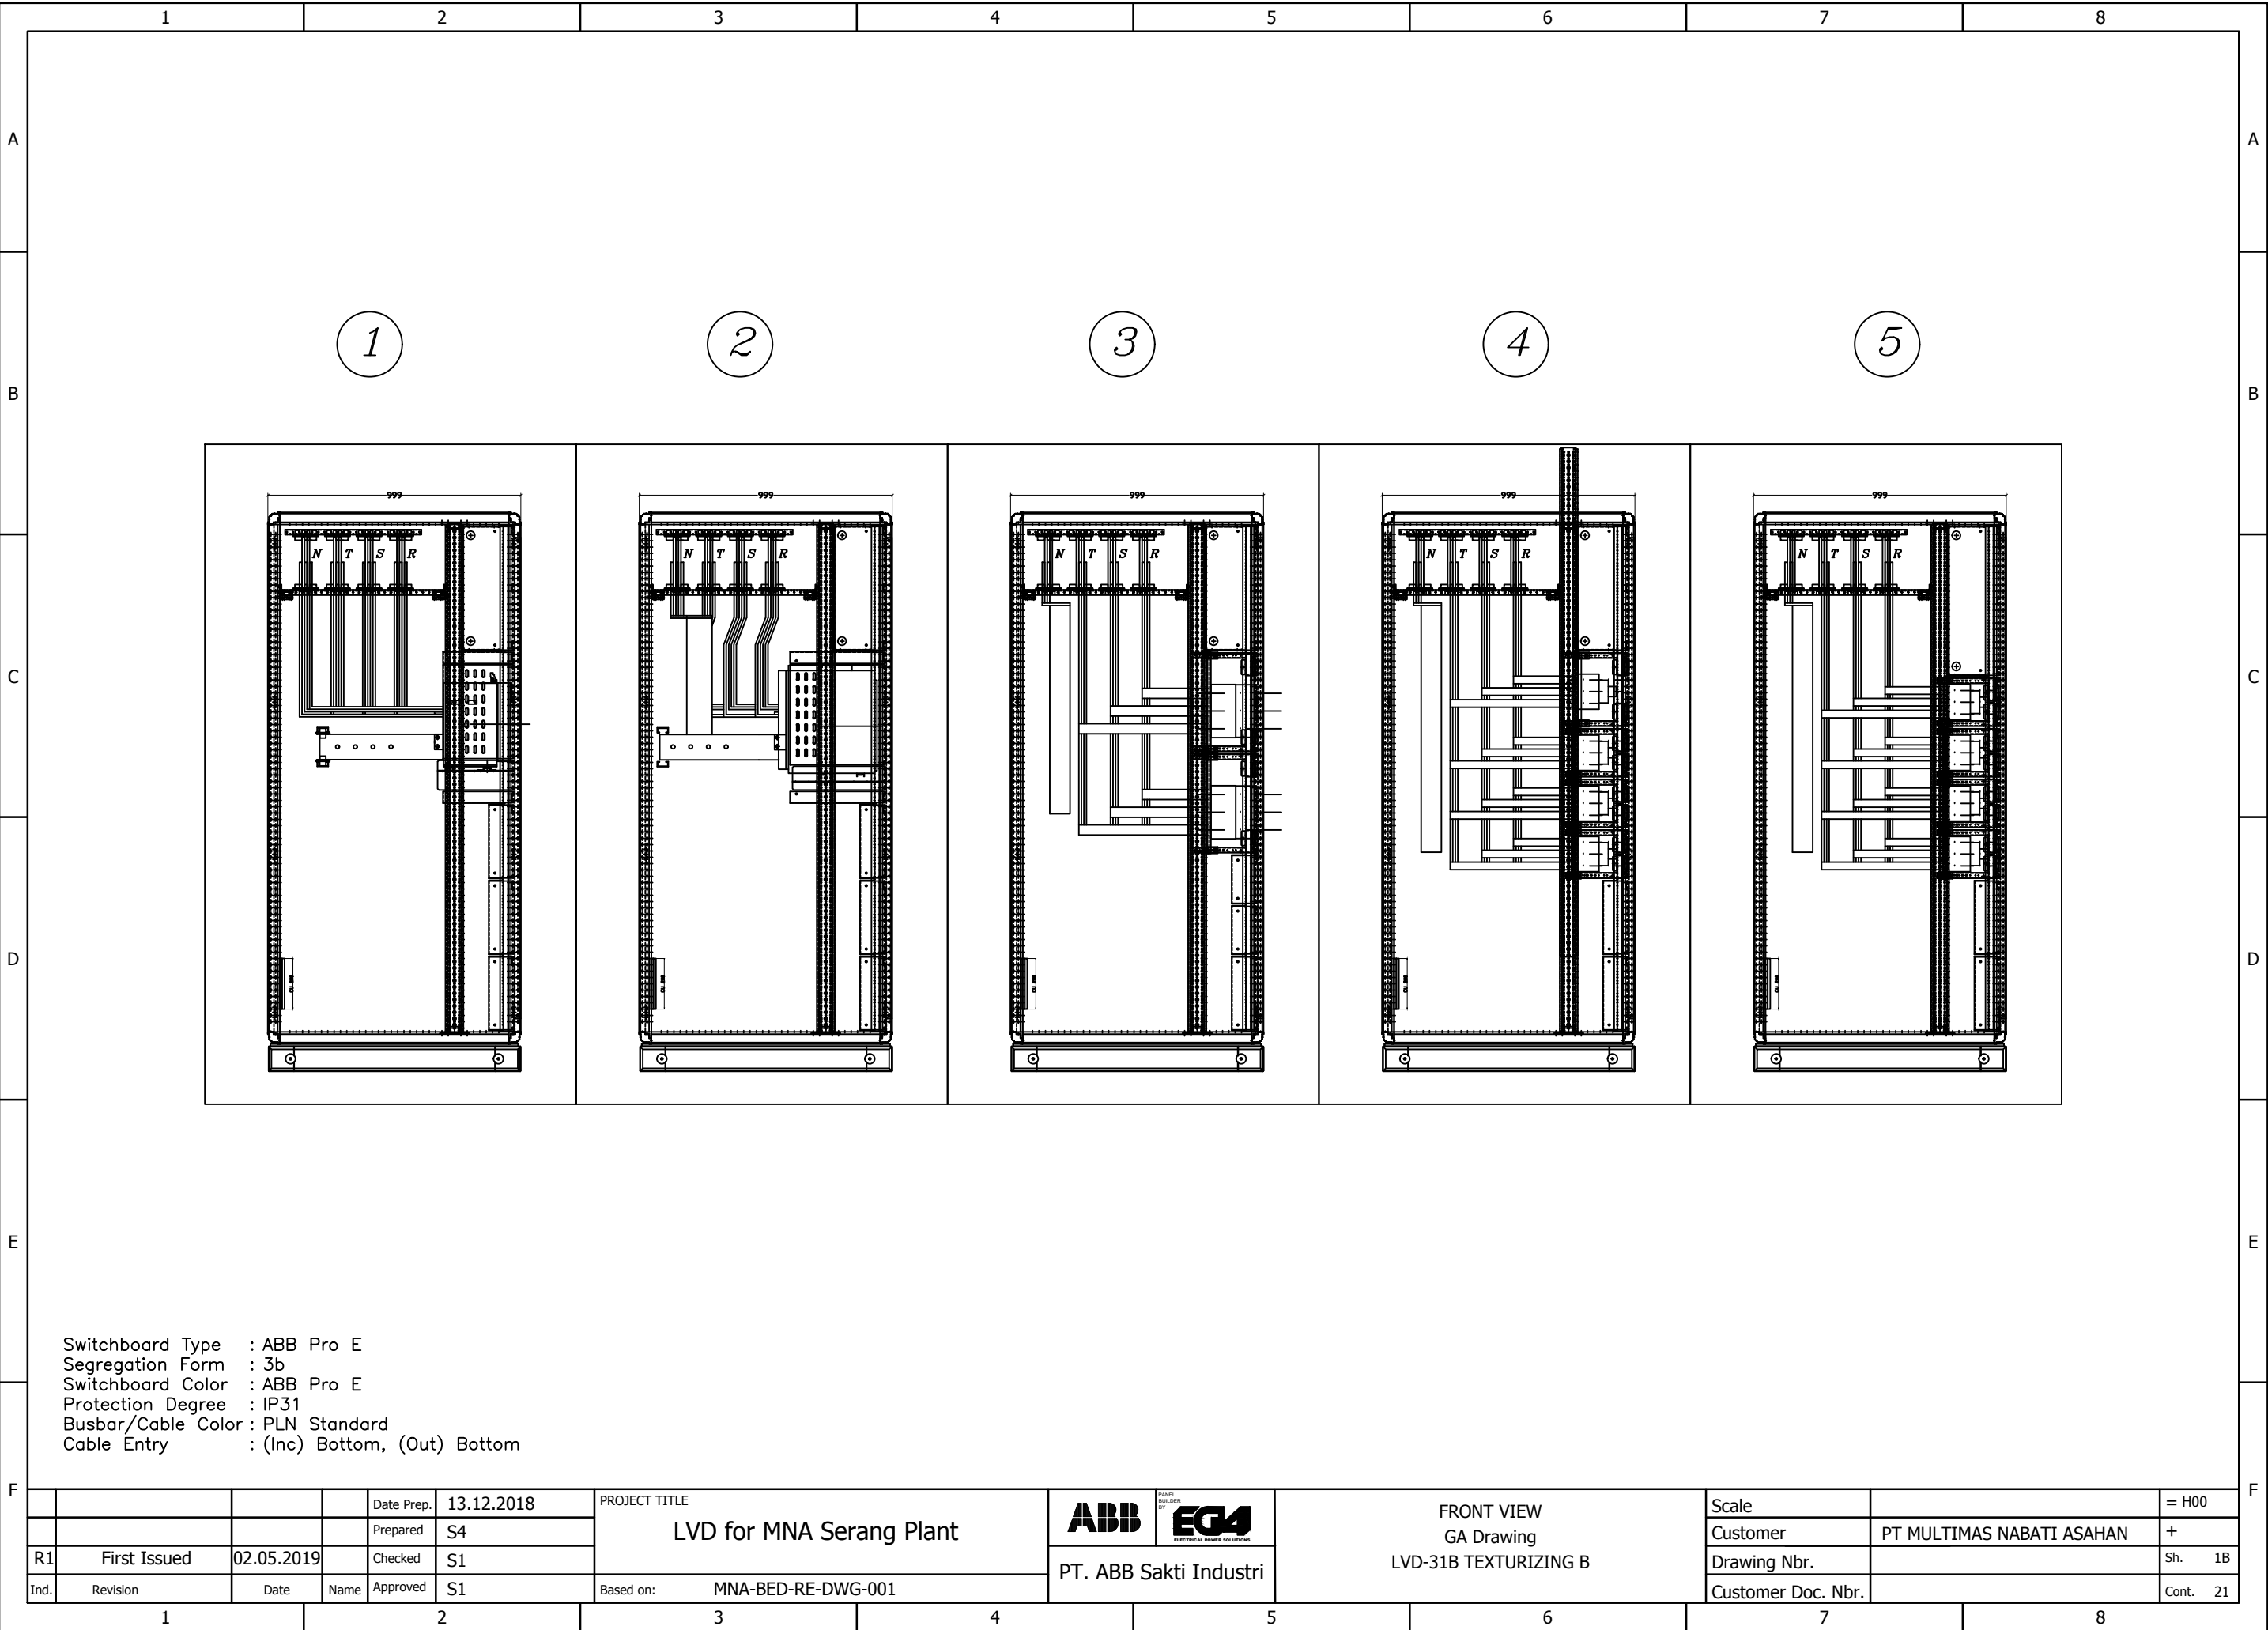


WE RESERVE ALL RIGHTS IN THIS DOCUMENT AND IN THE INFORMATION CONTAINED THEREIN. REPRODUCTION, USE OR DISCLOSURE TO THIRD PARTIES WITHOUT EXPRESS AUTHORITY IS STRICTLY FORBIDDEN.

SIDE VIEW

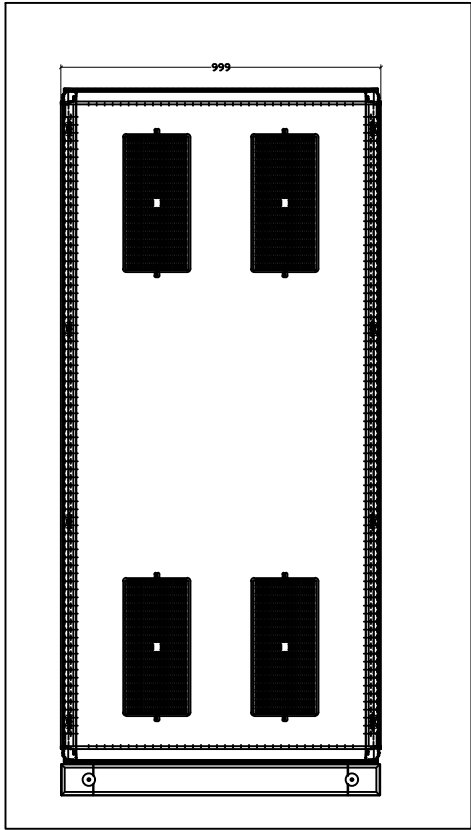


BACK VIEW

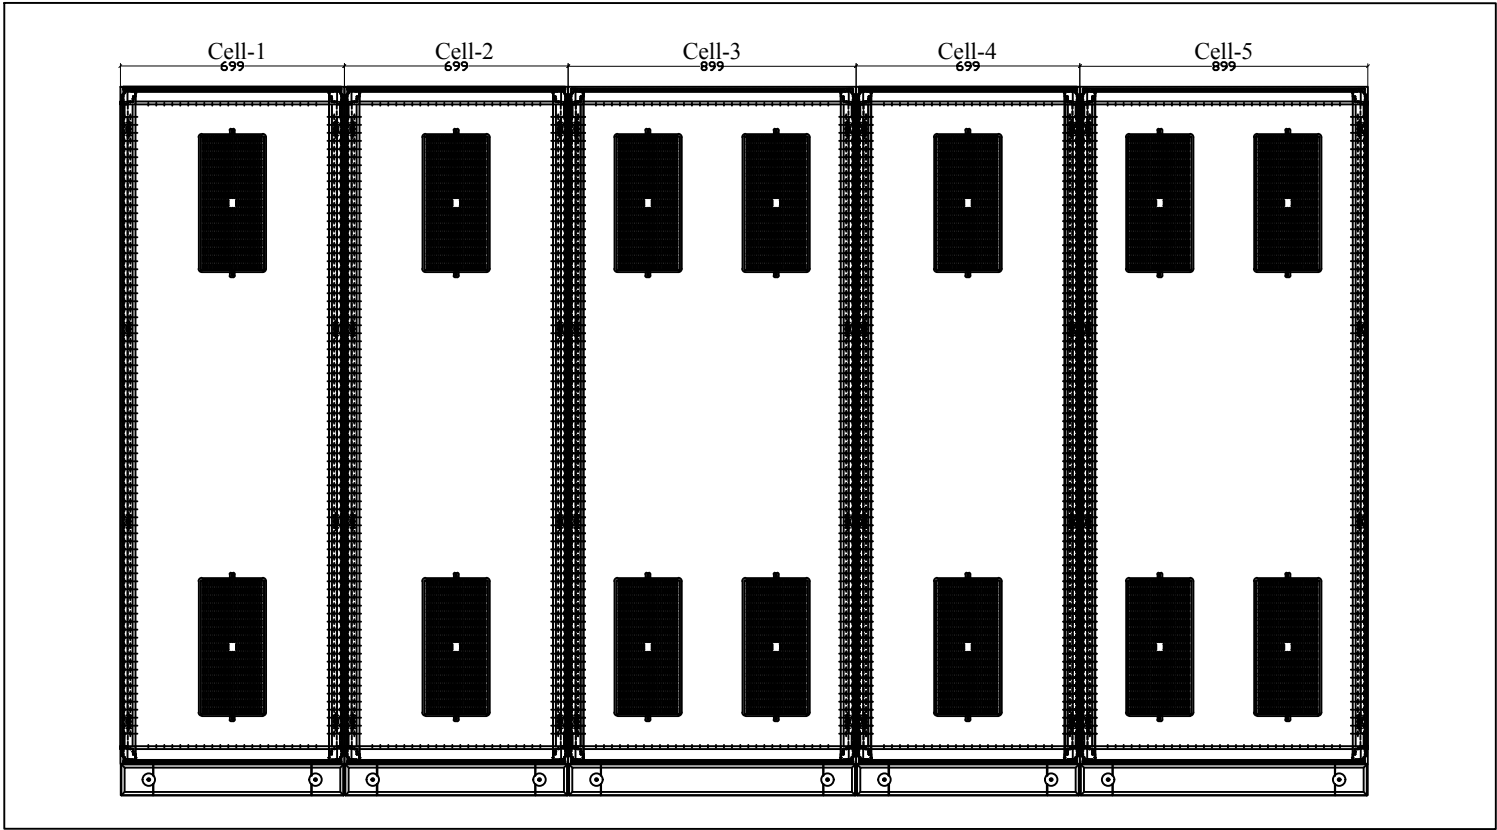


Switchboard Type : ABB Pro E
Segregation Form : 3b
Switchboard Color : ABB Pro E
Protection Degree : IP31
Busbar/Cable Color : PLN Standard
Cable Entry : (Inc) Bottom, (Out) Bottom


				Date Prep.	13.12.2018	PROJECT TITLE LVD for MNA Serang Plant	ABB EG4 PT. ABB Sakti Industri	FRONT VIEW GA Drawing LVD-31B TEXTURIZING B	Scale		= H00
				Prepared	S4				Customer	PT MULTIMAS NABATI ASAHAN	+
R1	First Issued	02.05.2019		Checked	S1				Drawing Nbr.		Sh. 1C
Ind.	Revision	Date	Name	Approved	S1	Based on:	MNA-BED-RE-DWG-001		Customer Doc. Nbr.		Cont. 21

WE RESERVE ALL RIGHTS IN THIS DOCUMENT AND IN THE INFORMATION CONTAINED THEREIN. REPRODUCTION, USE OR DISCLOSURE TO THIRD PARTIES WITHOUT EXPRESS AUTHORITY IS STRICTLY FORBIDDEN.

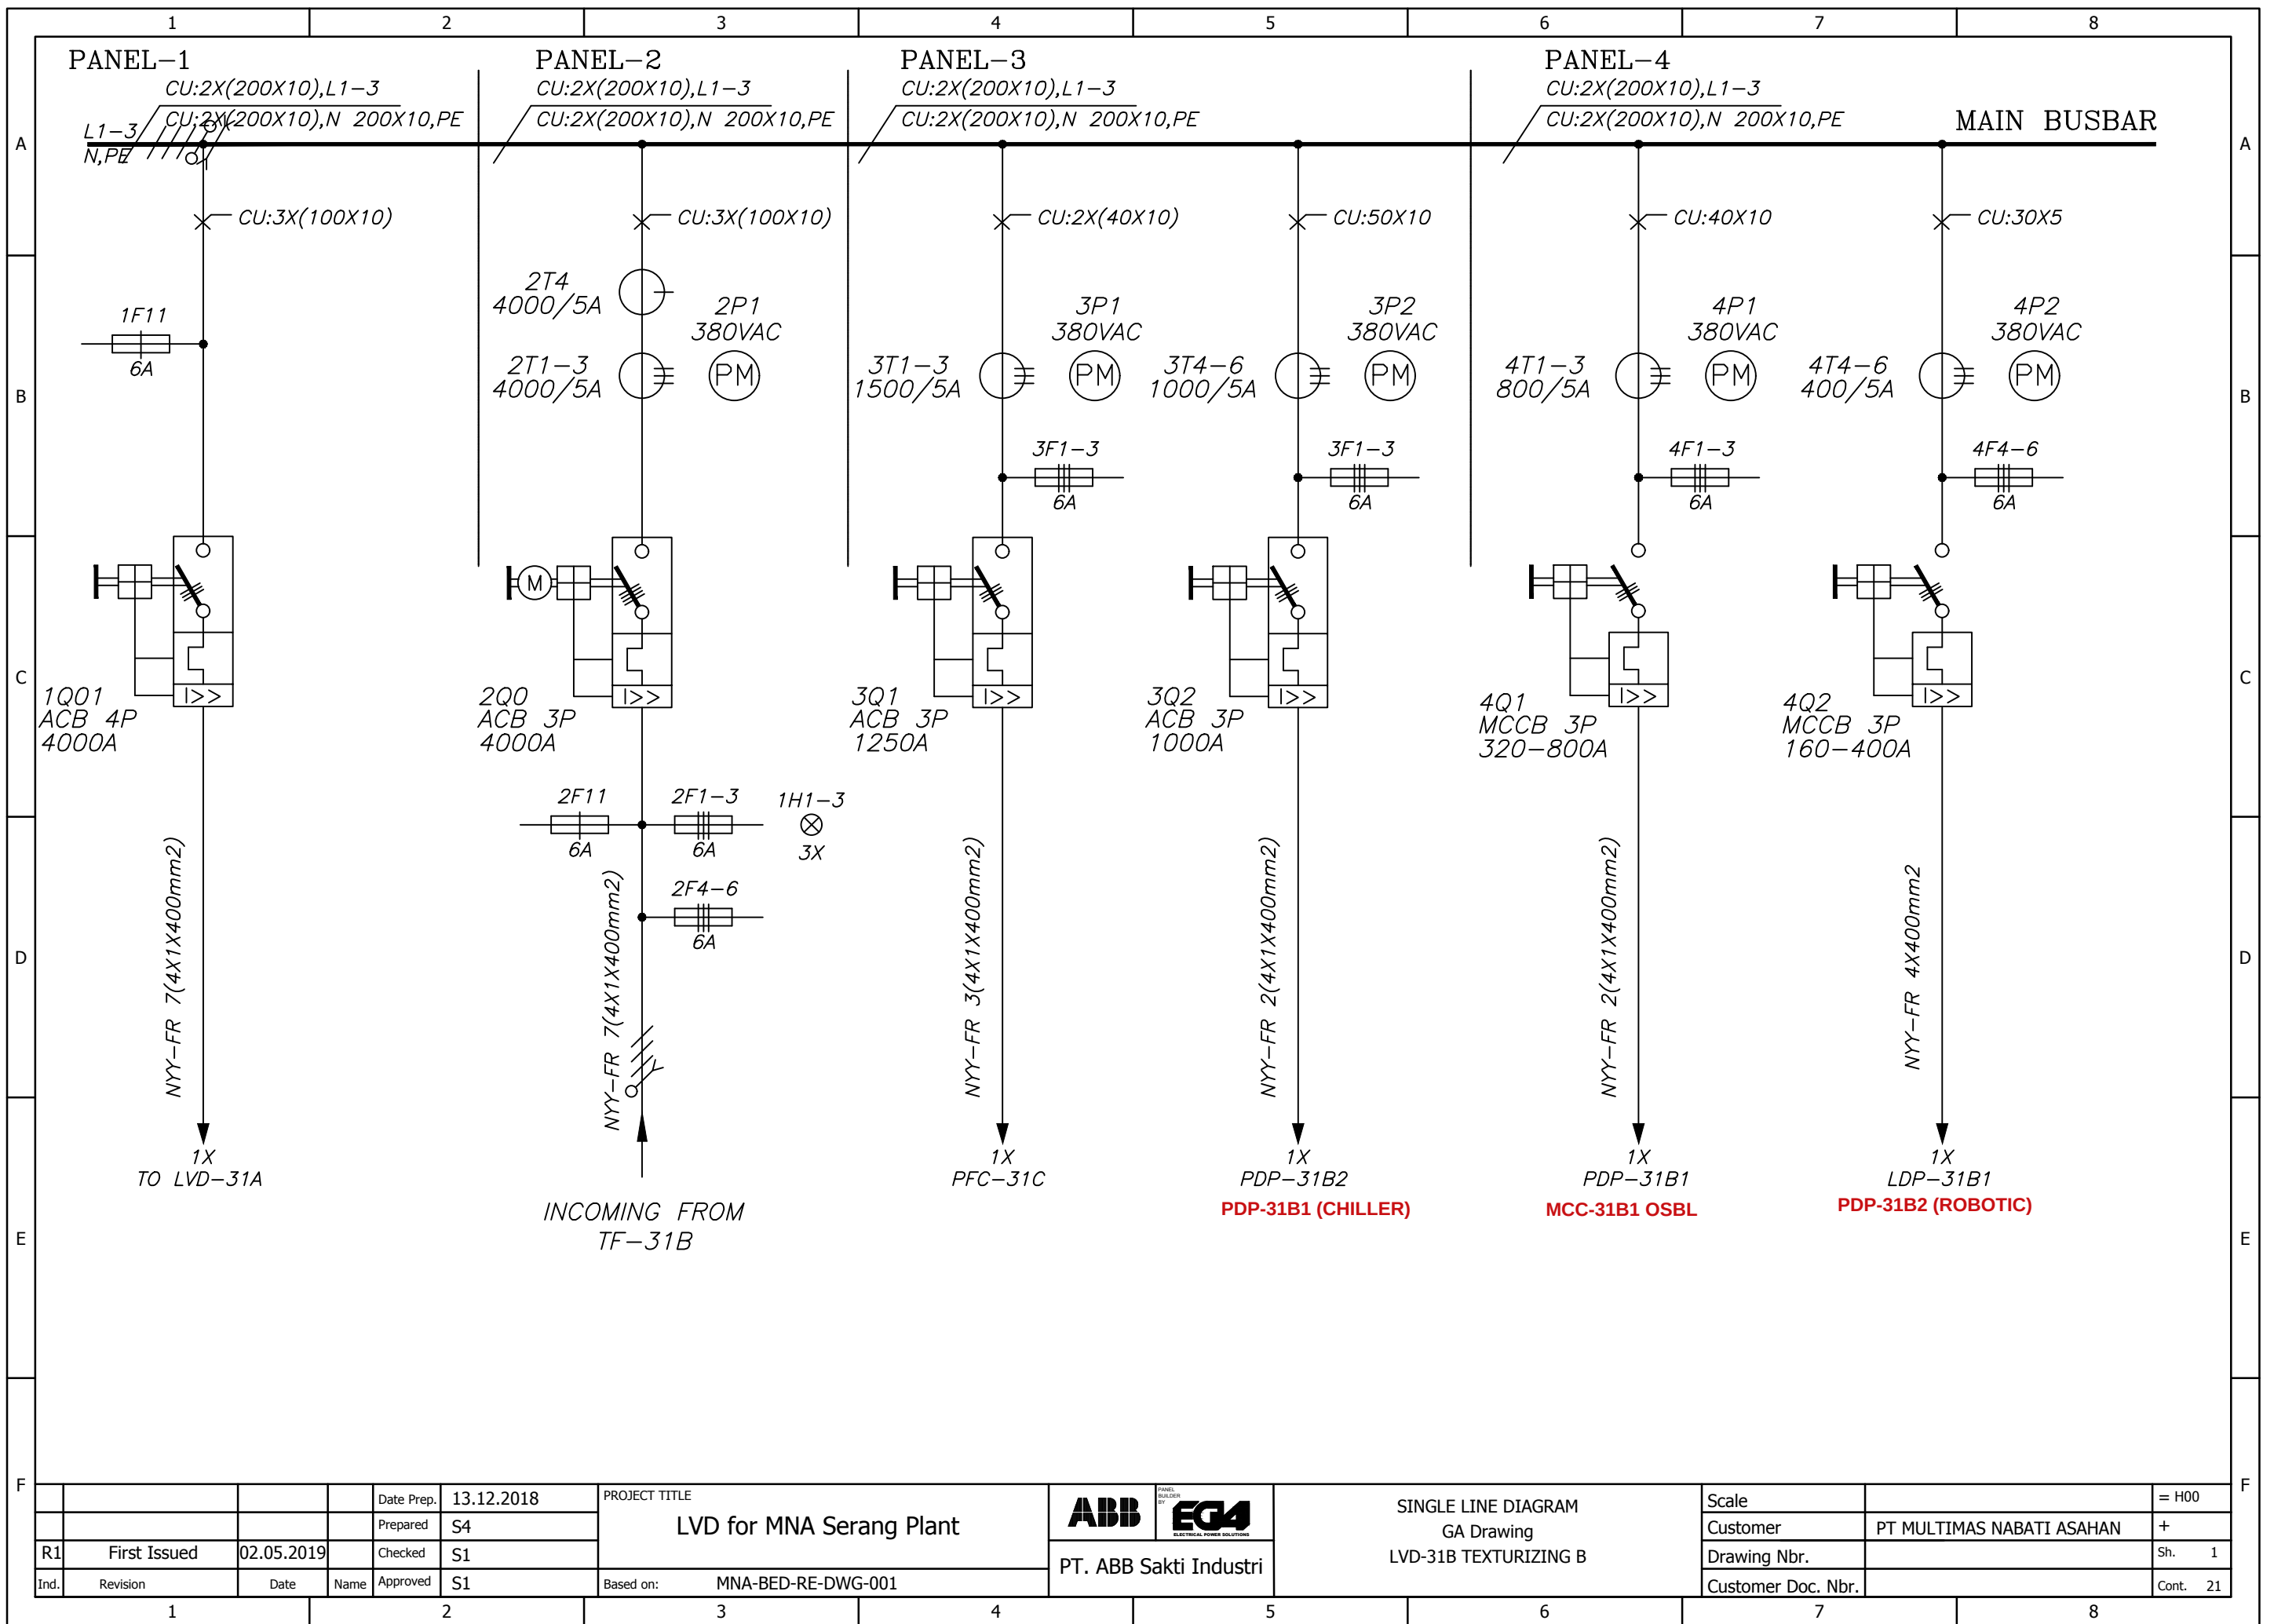


WE RESERVE ALL RIGHTS IN THIS DOCUMENT AND IN THE INFORMATION CONTAINED THEREIN. REPRODUCTION, USE OR DISCLOSURE TO THIRD PARTIES WITHOUT EXPRESS AUTHORITY IS STRICTLY FORBIDDEN.

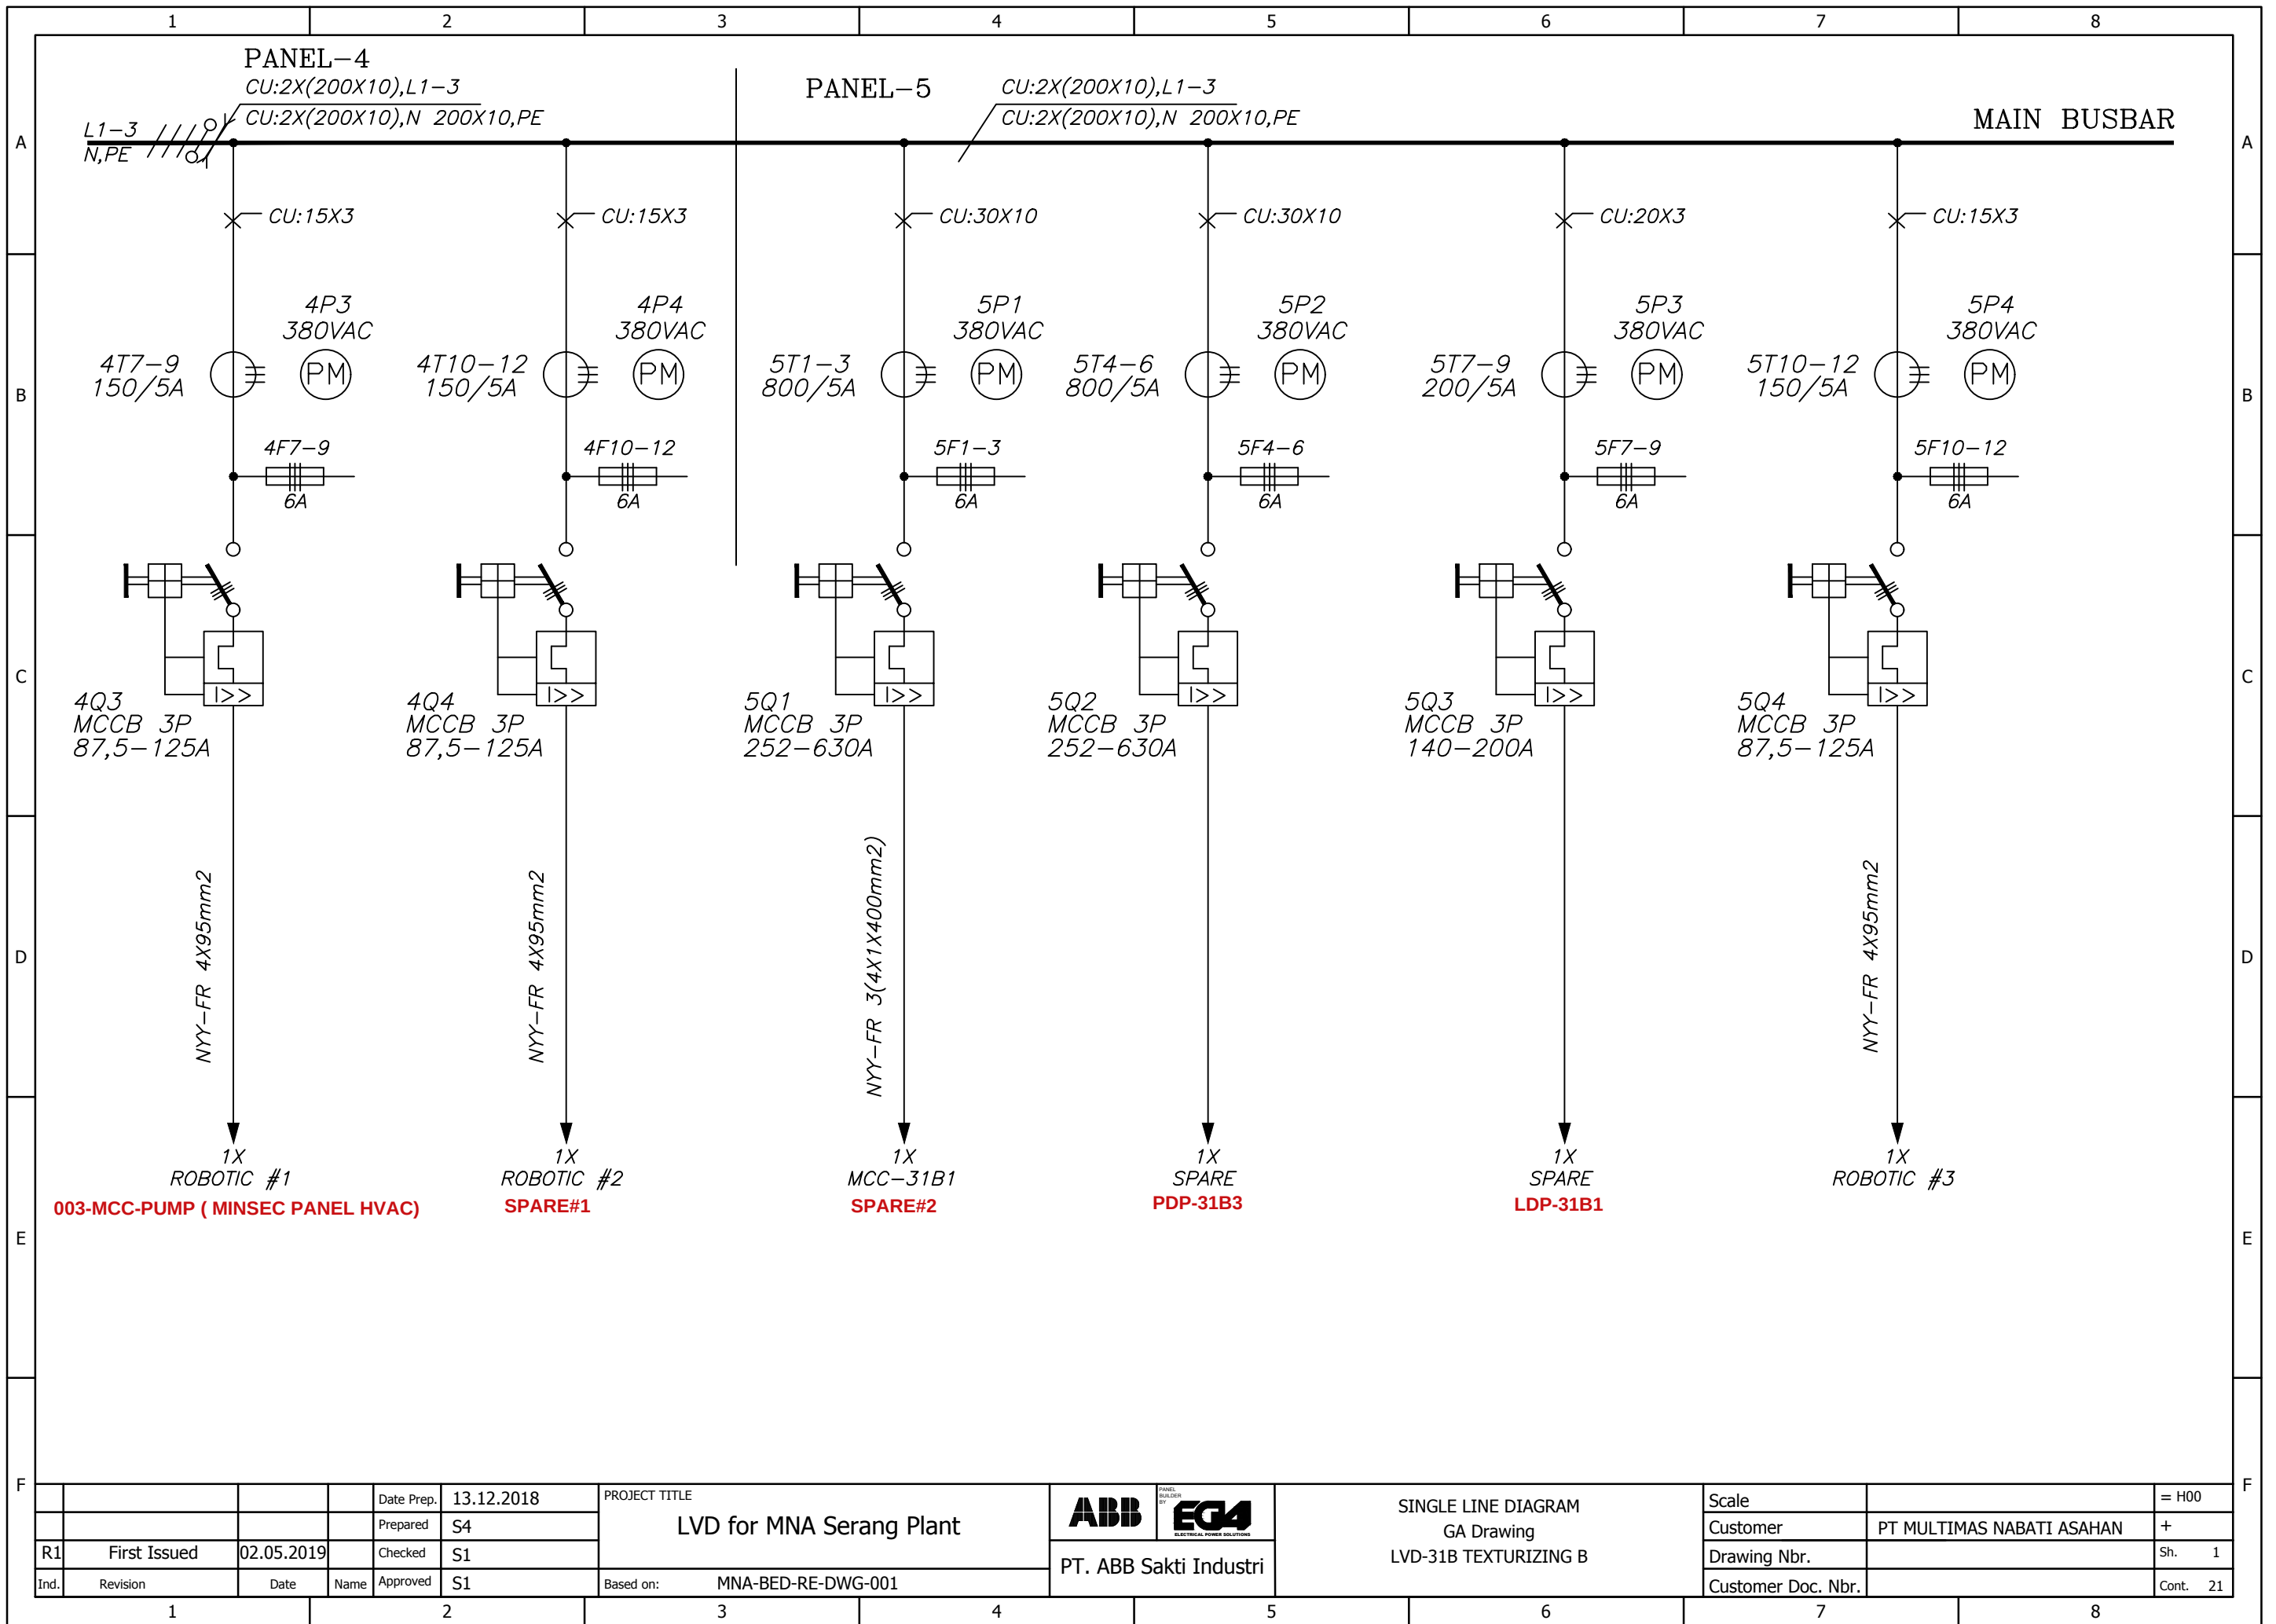

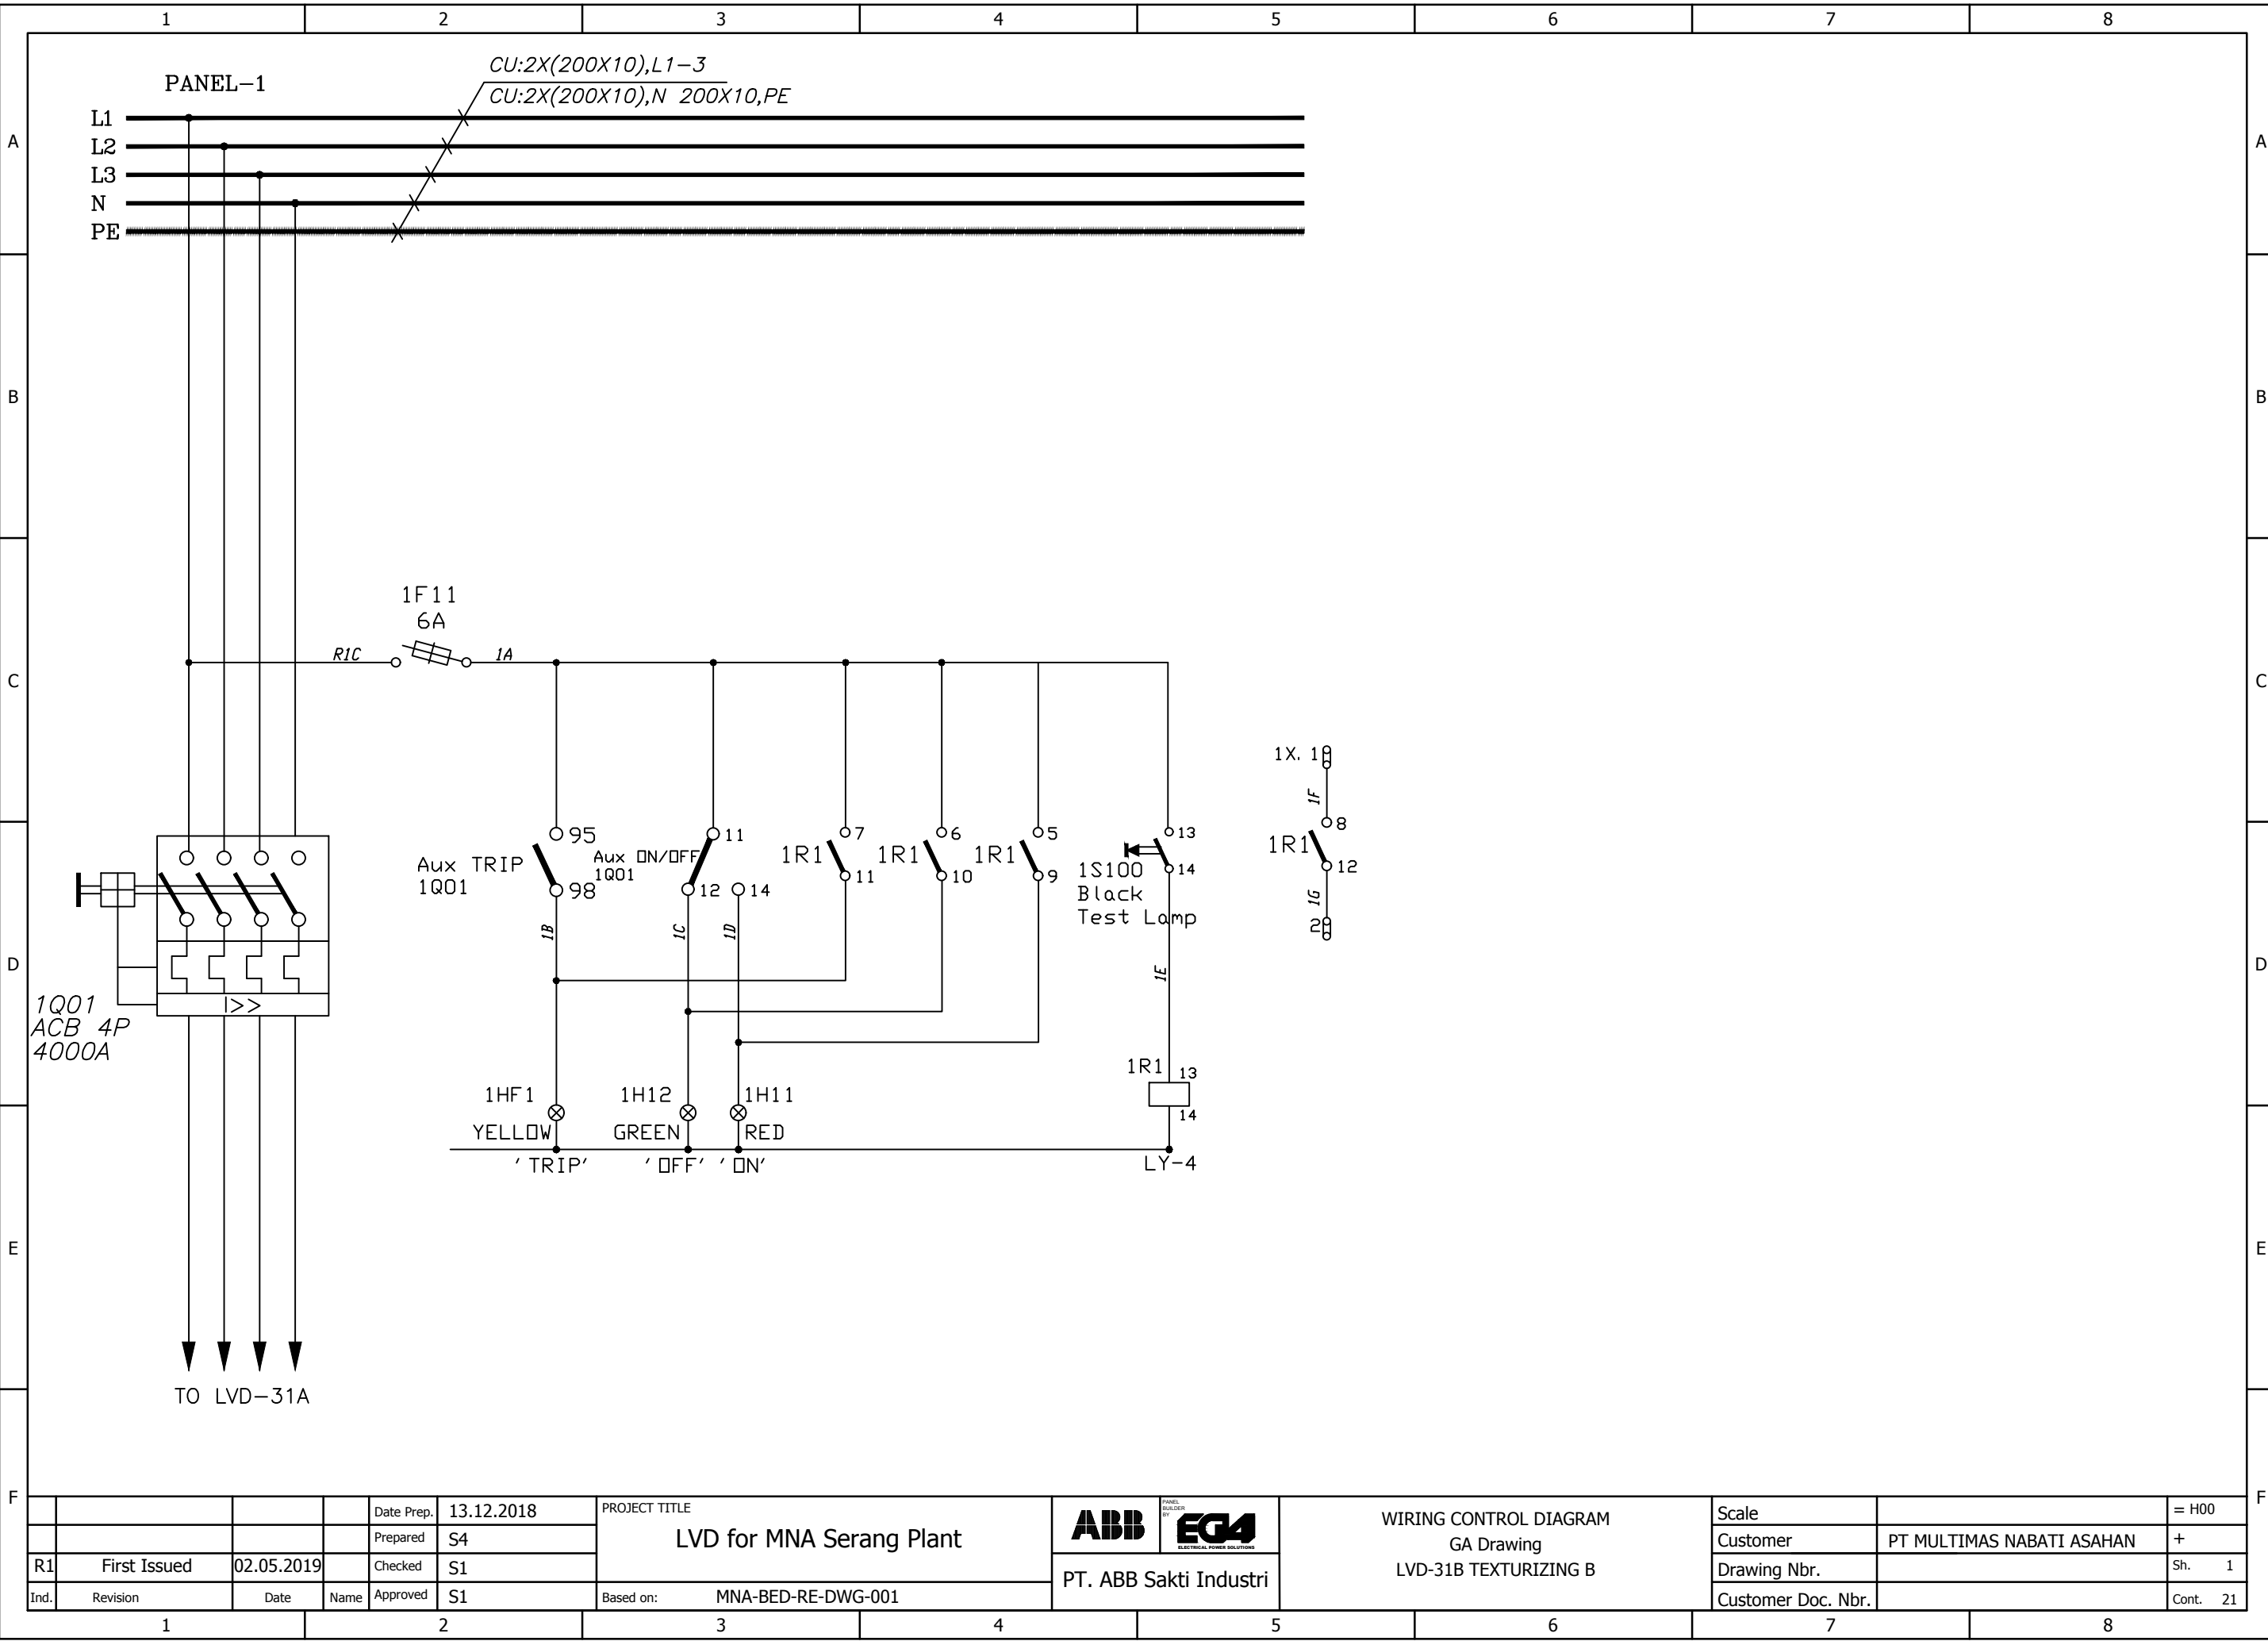


			Date Prep.	13.12.2018	PROJECT TITLE LVD for MNA Serang Plant	 	WIRING CONTROL DIAGRAM GA Drawing LVD-31B TEXTURIZING B	Scale		= H00
			Prepared	S4				Customer	PT MULTIMAS NABATI ASAHAN	+
R1	First Issued	02.05.2019	Checked	S1				Drawing Nbr.		Sh. 1
Ind.	Revision	Date	Name	Approved	S1	Based on: MNA-BED-RE-DWG-001	PT. ABB Sakti Industri	Customer Doc. Nbr.		Cont. 21


WE RESERVE ALL RIGHTS IN THIS DOCUMENT AND IN THE INFORMATION CONTAINED THEREIN. REPRODUCTION, USE OR DISCLOSURE TO THIRD PARTIES WITHOUT EXPRESS AUTHORITY IS STRICTLY FORBIDDEN.

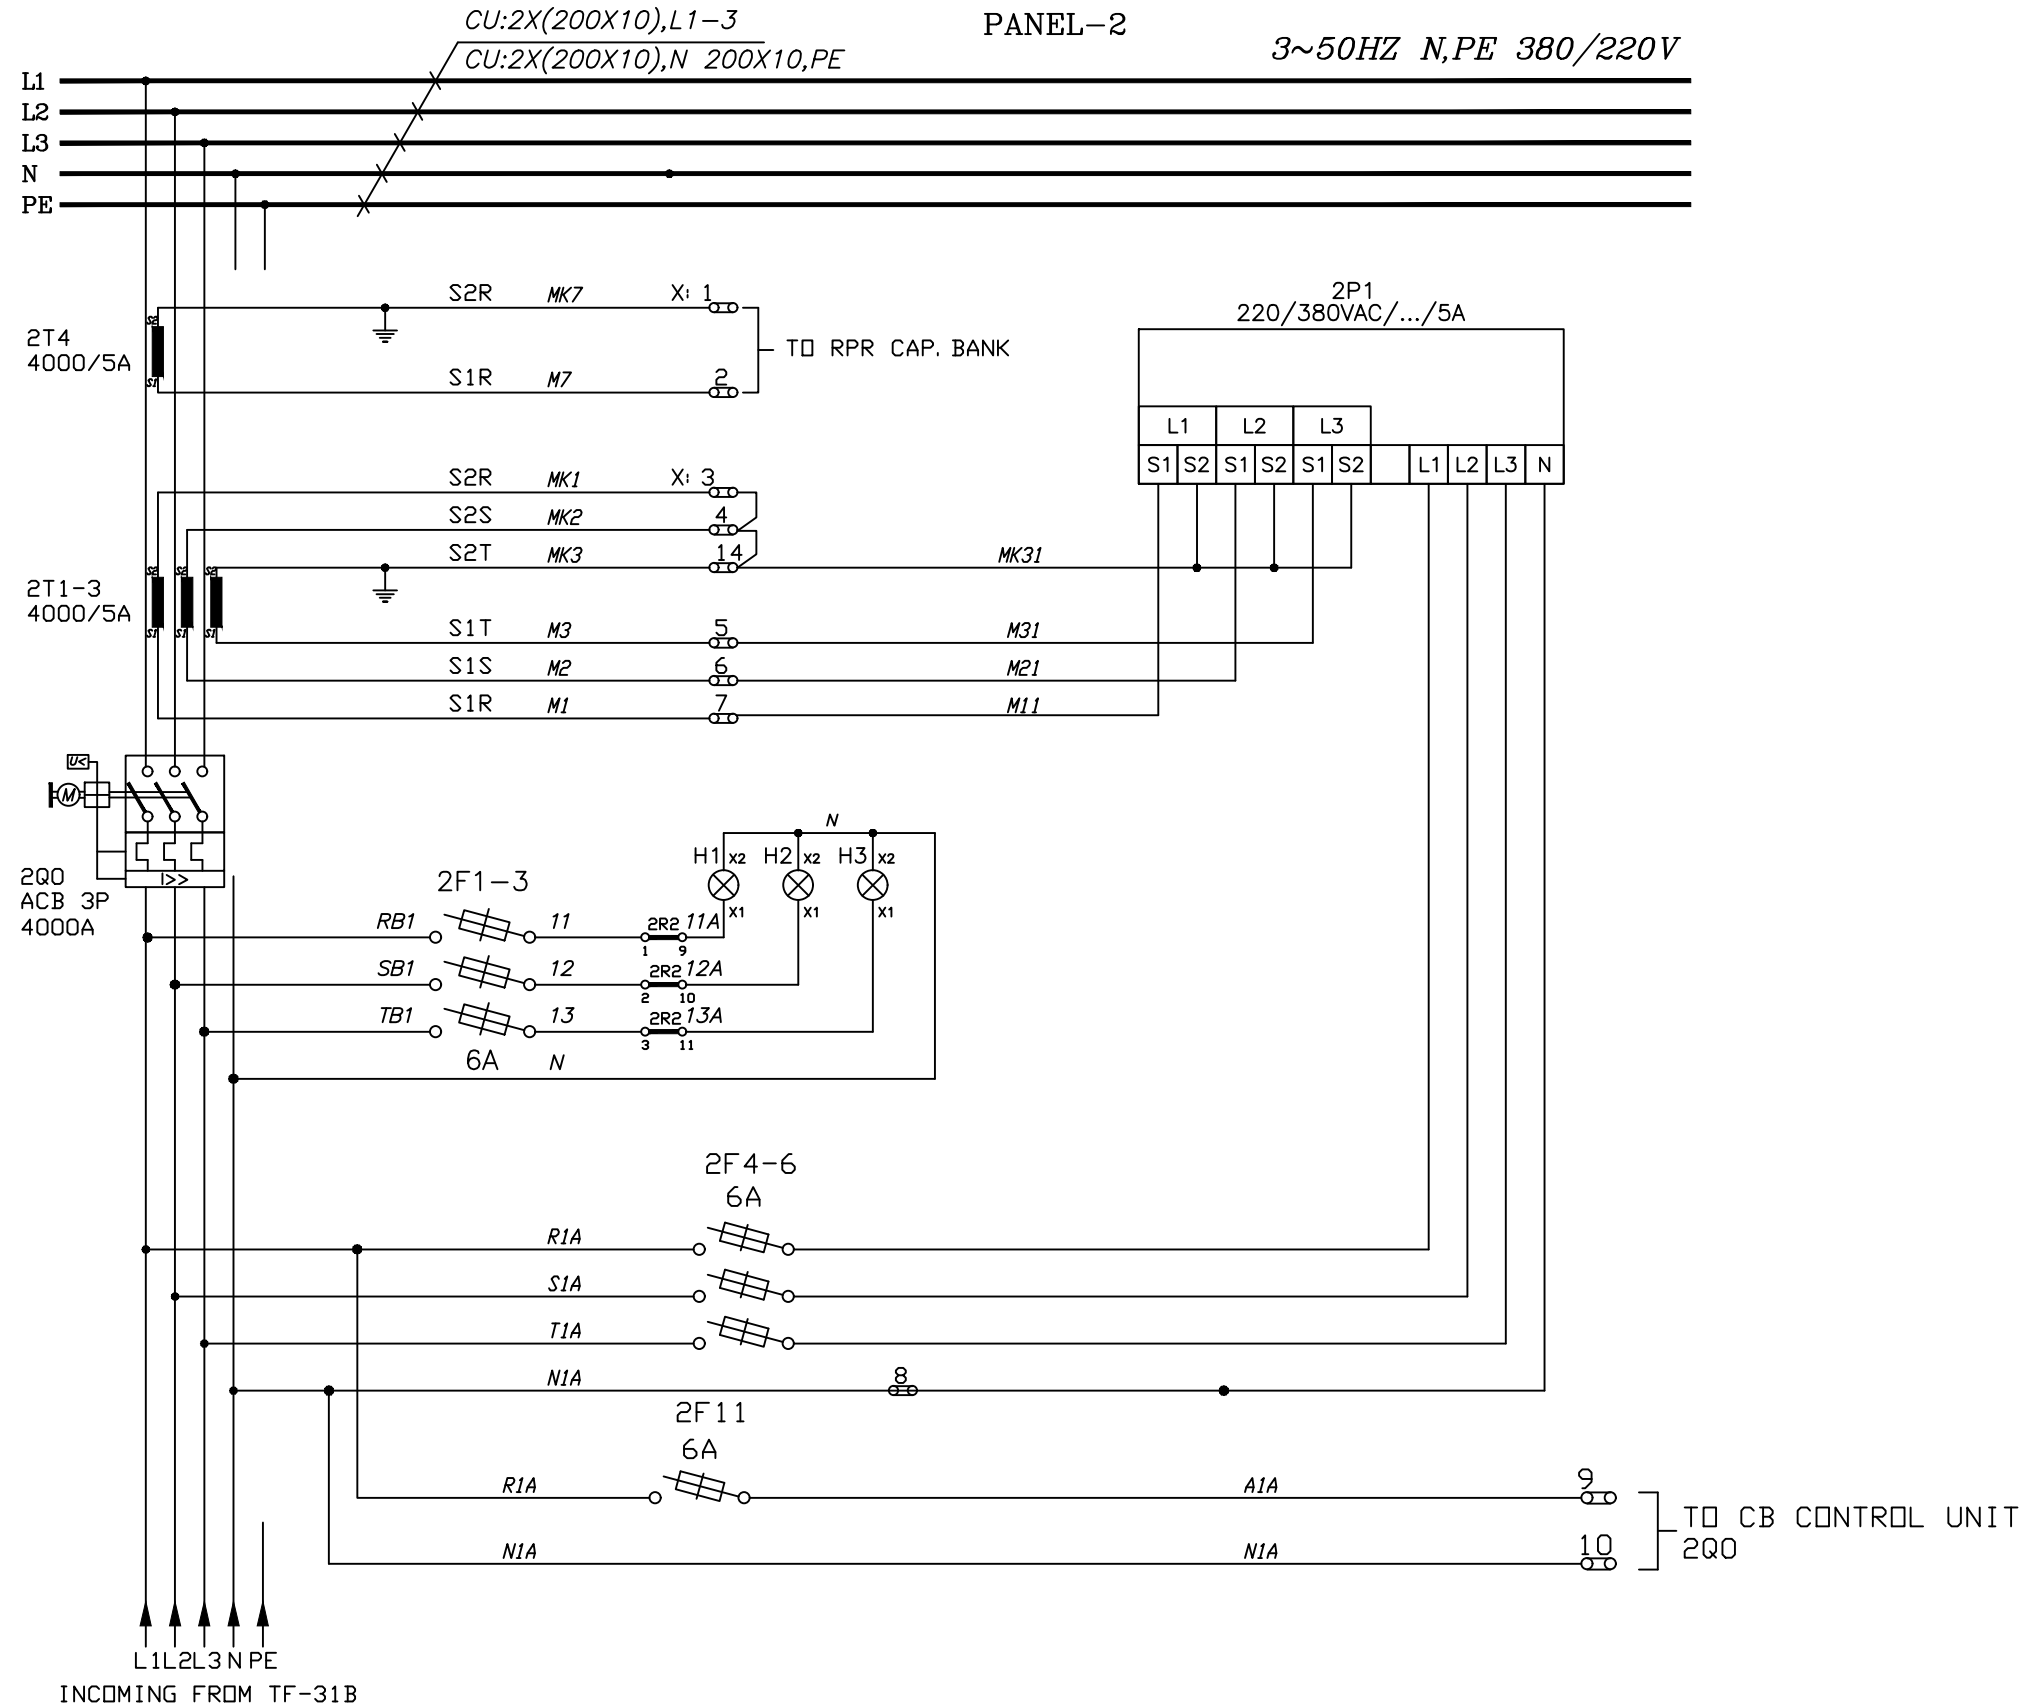

				Date Prep.	13.12.2018	PROJECT TITLE LVD for MNA Serang Plant	  PT. ABB Sakti Industri	WIRING CONTROL DIAGRAM GA Drawing LVD-31B TEXTURIZING B	Scale		= H00
				Prepared	S4				Customer	PT MULTIMAS NABATI ASAHAN	+
R1	First Issued	02.05.2019		Checked	S1				Drawing Nbr.		Sh. 1
Ind.	Revision	Date	Name	Approved	S1	Based on:	MNA-BED-RE-DWG-001		Customer Doc. Nbr.		Cont. 21

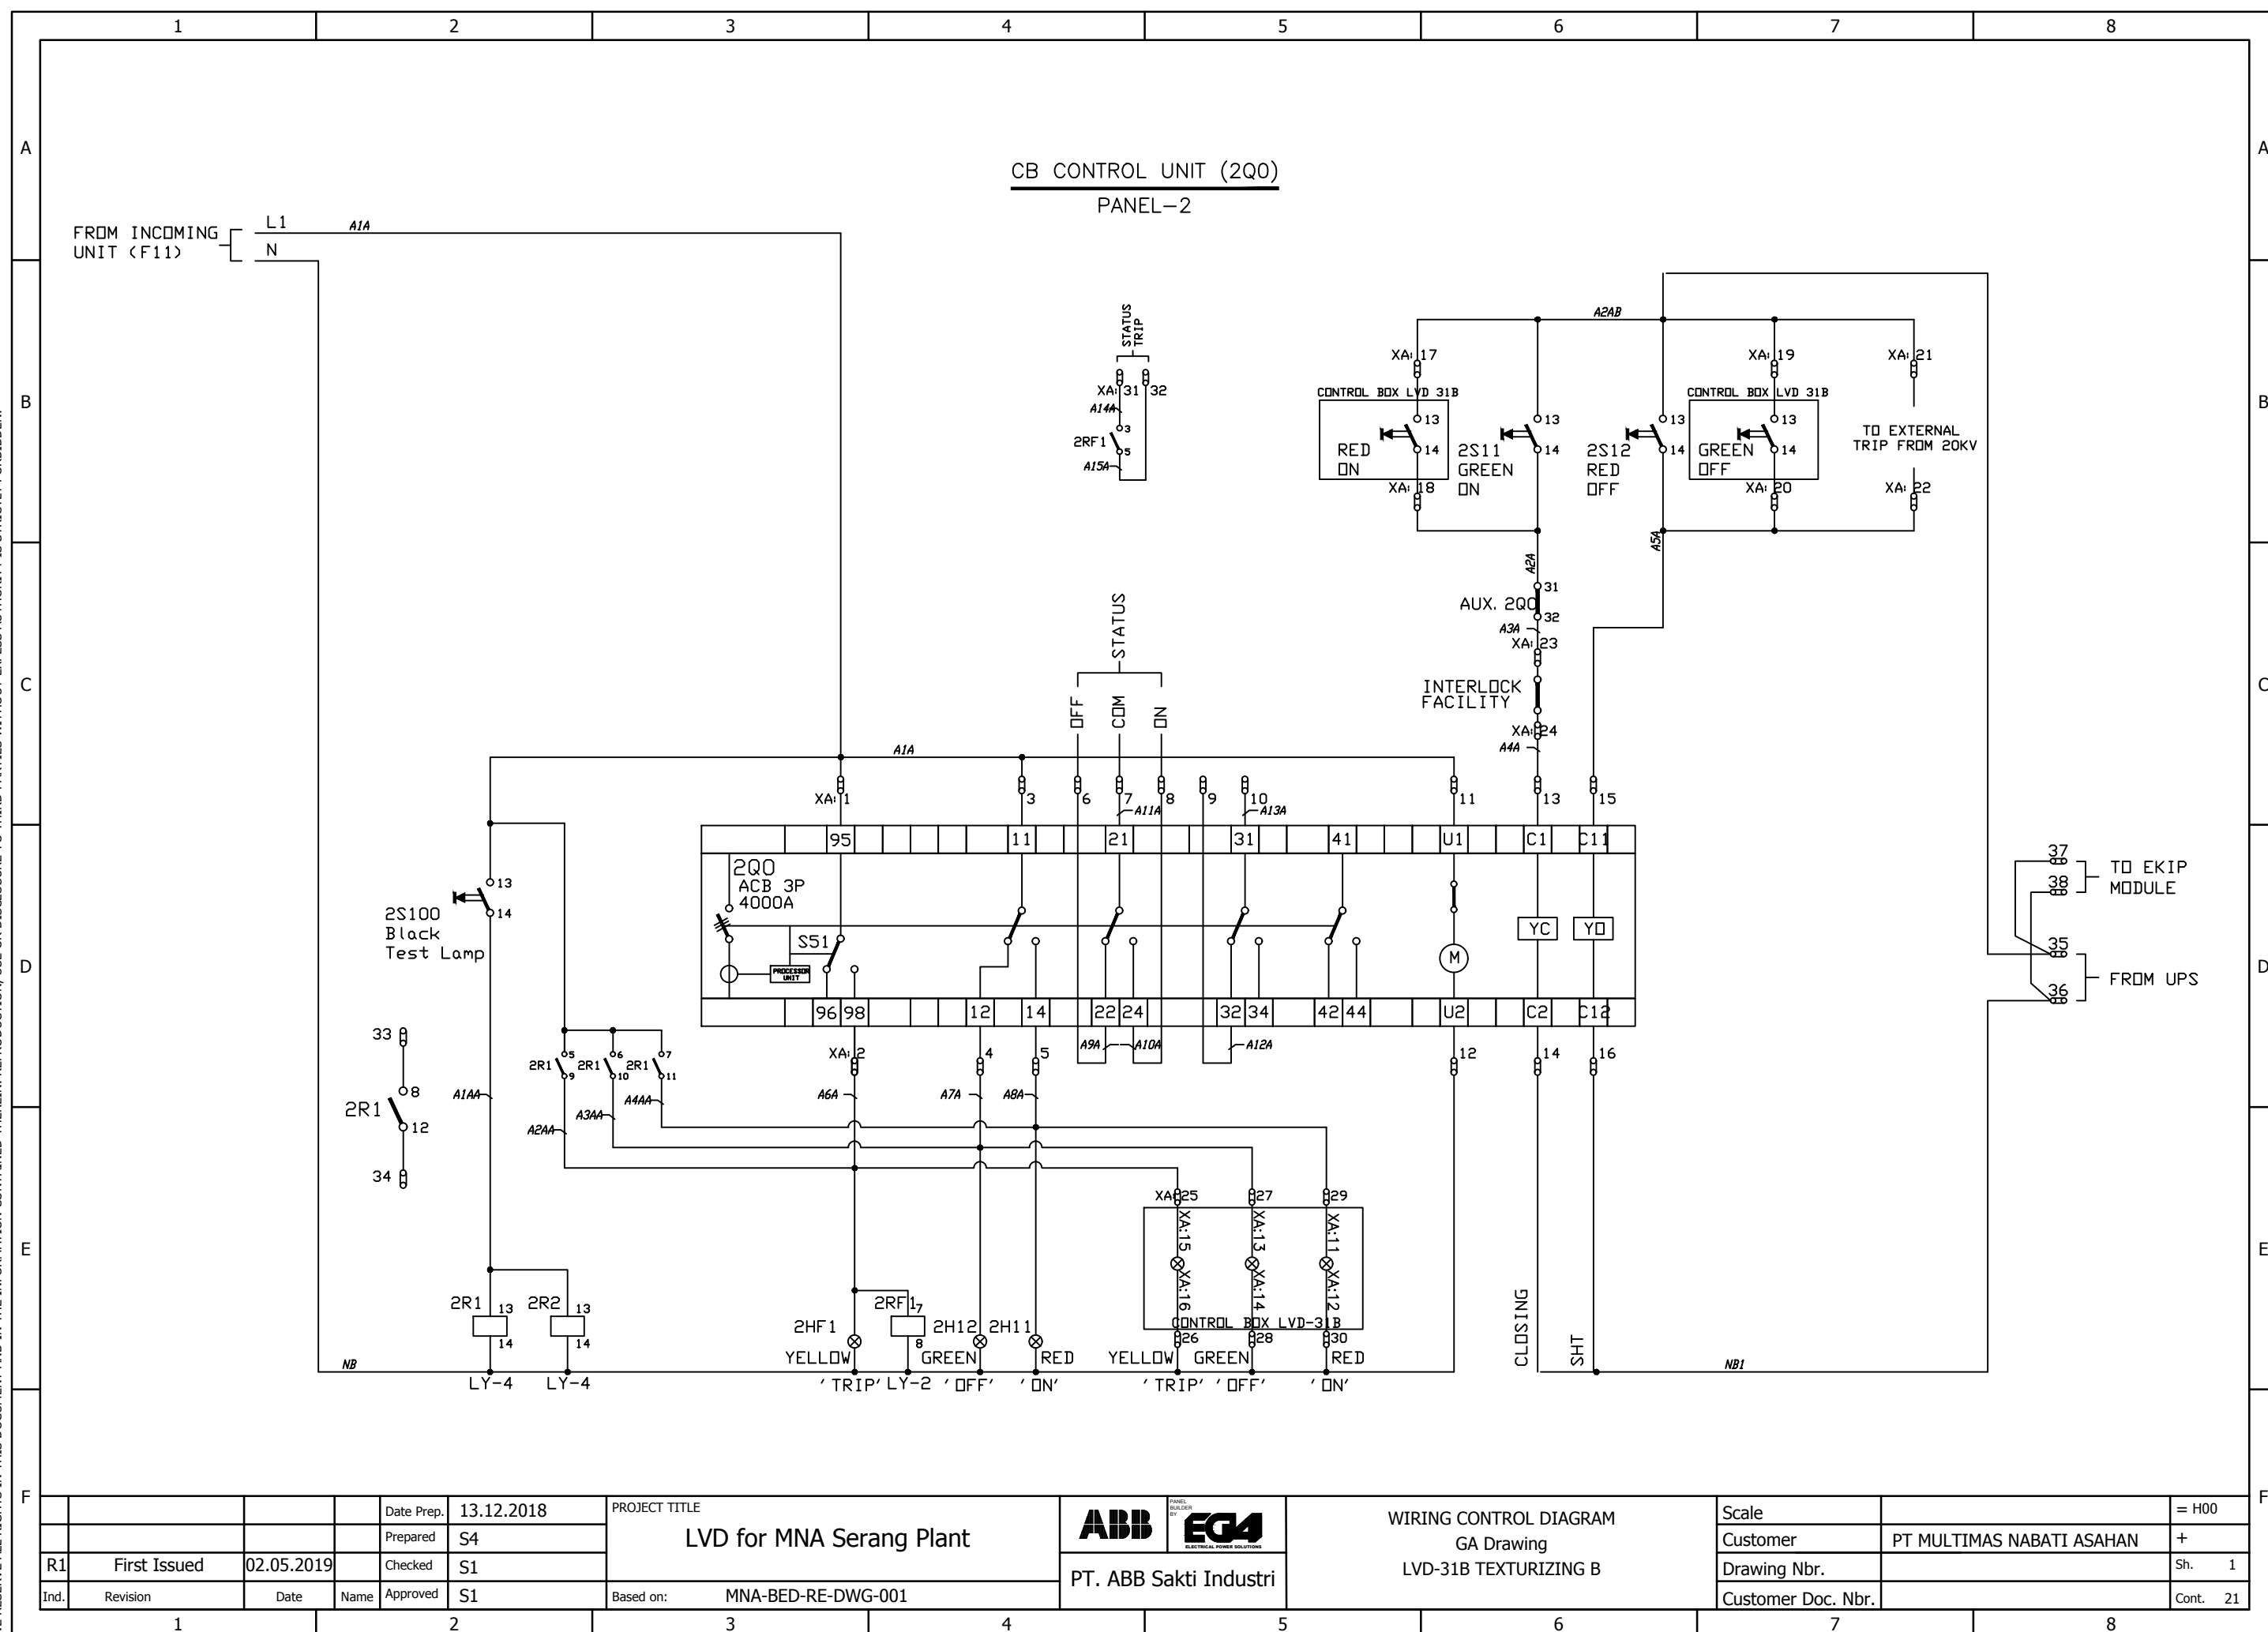


WE RESERVE ALL RIGHTS IN THIS DOCUMENT AND IN THE INFORMATION CONTAINED THEREIN. REPRODUCTION, USE OR DISCLOSURE TO THIRD PARTIES WITHOUT EXPRESS AUTHORITY IS STRICTLY FORBIDDEN.

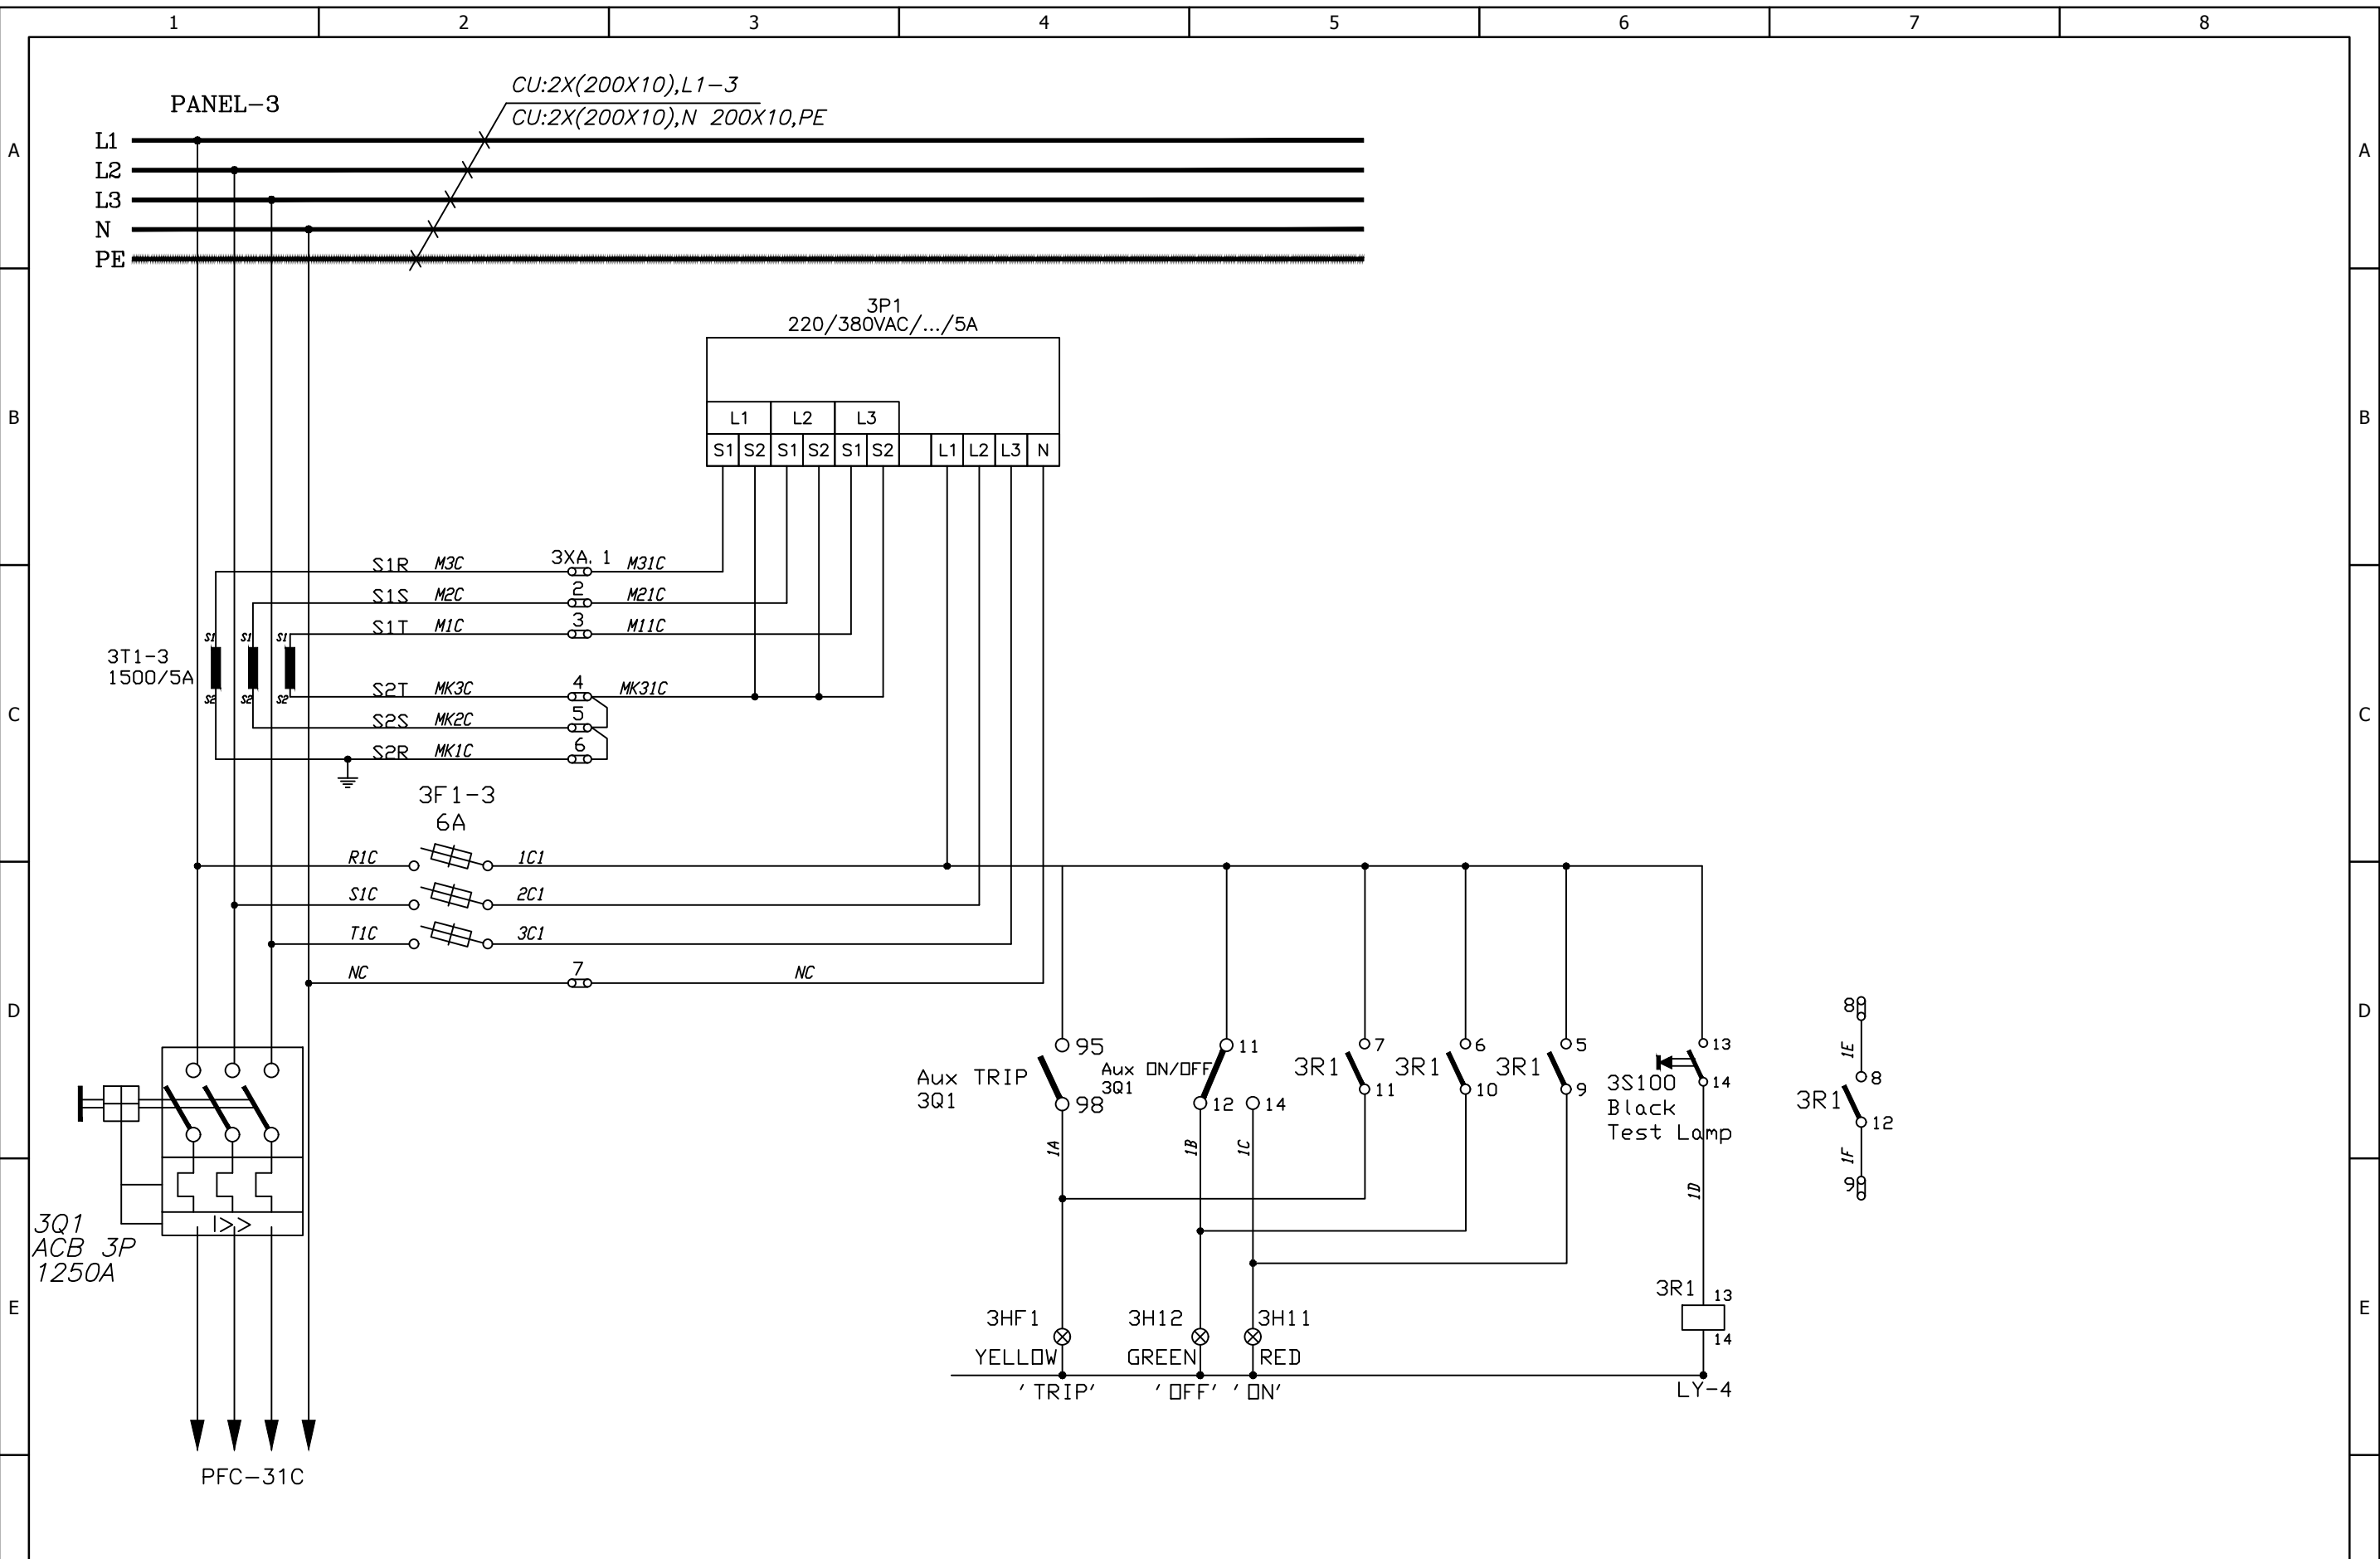


				Date Prep.	13.12.2018	PROJECT TITLE LVD for MNA Serang Plant	ABB PANEL BUILDER BY EG4 ELECTRICAL POWER SOLUTIONS	WIRING CONTROL DIAGRAM GA Drawing LVD-31B TEXTURIZING B	Scale		= H00						
			Prepared	S4	Customer				PT MULTIMAS NABATI ASAHAN	+							
R1	First Issued	02.05.2019	Checked	S1	Drawing Nbr.					Sh. 1							
Ind.	Revision	Date	Name	Approved	S1	Based on: MNA-BED-RE-DWG-001	PT. ABB Sakti Industri		Customer Doc. Nbr.		Cont. 21						
1			2			3		4		5		6		7		8	


WE RESERVE ALL RIGHTS IN THIS DOCUMENT AND IN THE INFORMATION CONTAINED THEREIN. REPRODUCTION, USE OR DISCLOSURE TO THIRD PARTIES WITHOUT EXPRESS AUTHORITY IS STRICTLY FORBIDDEN.

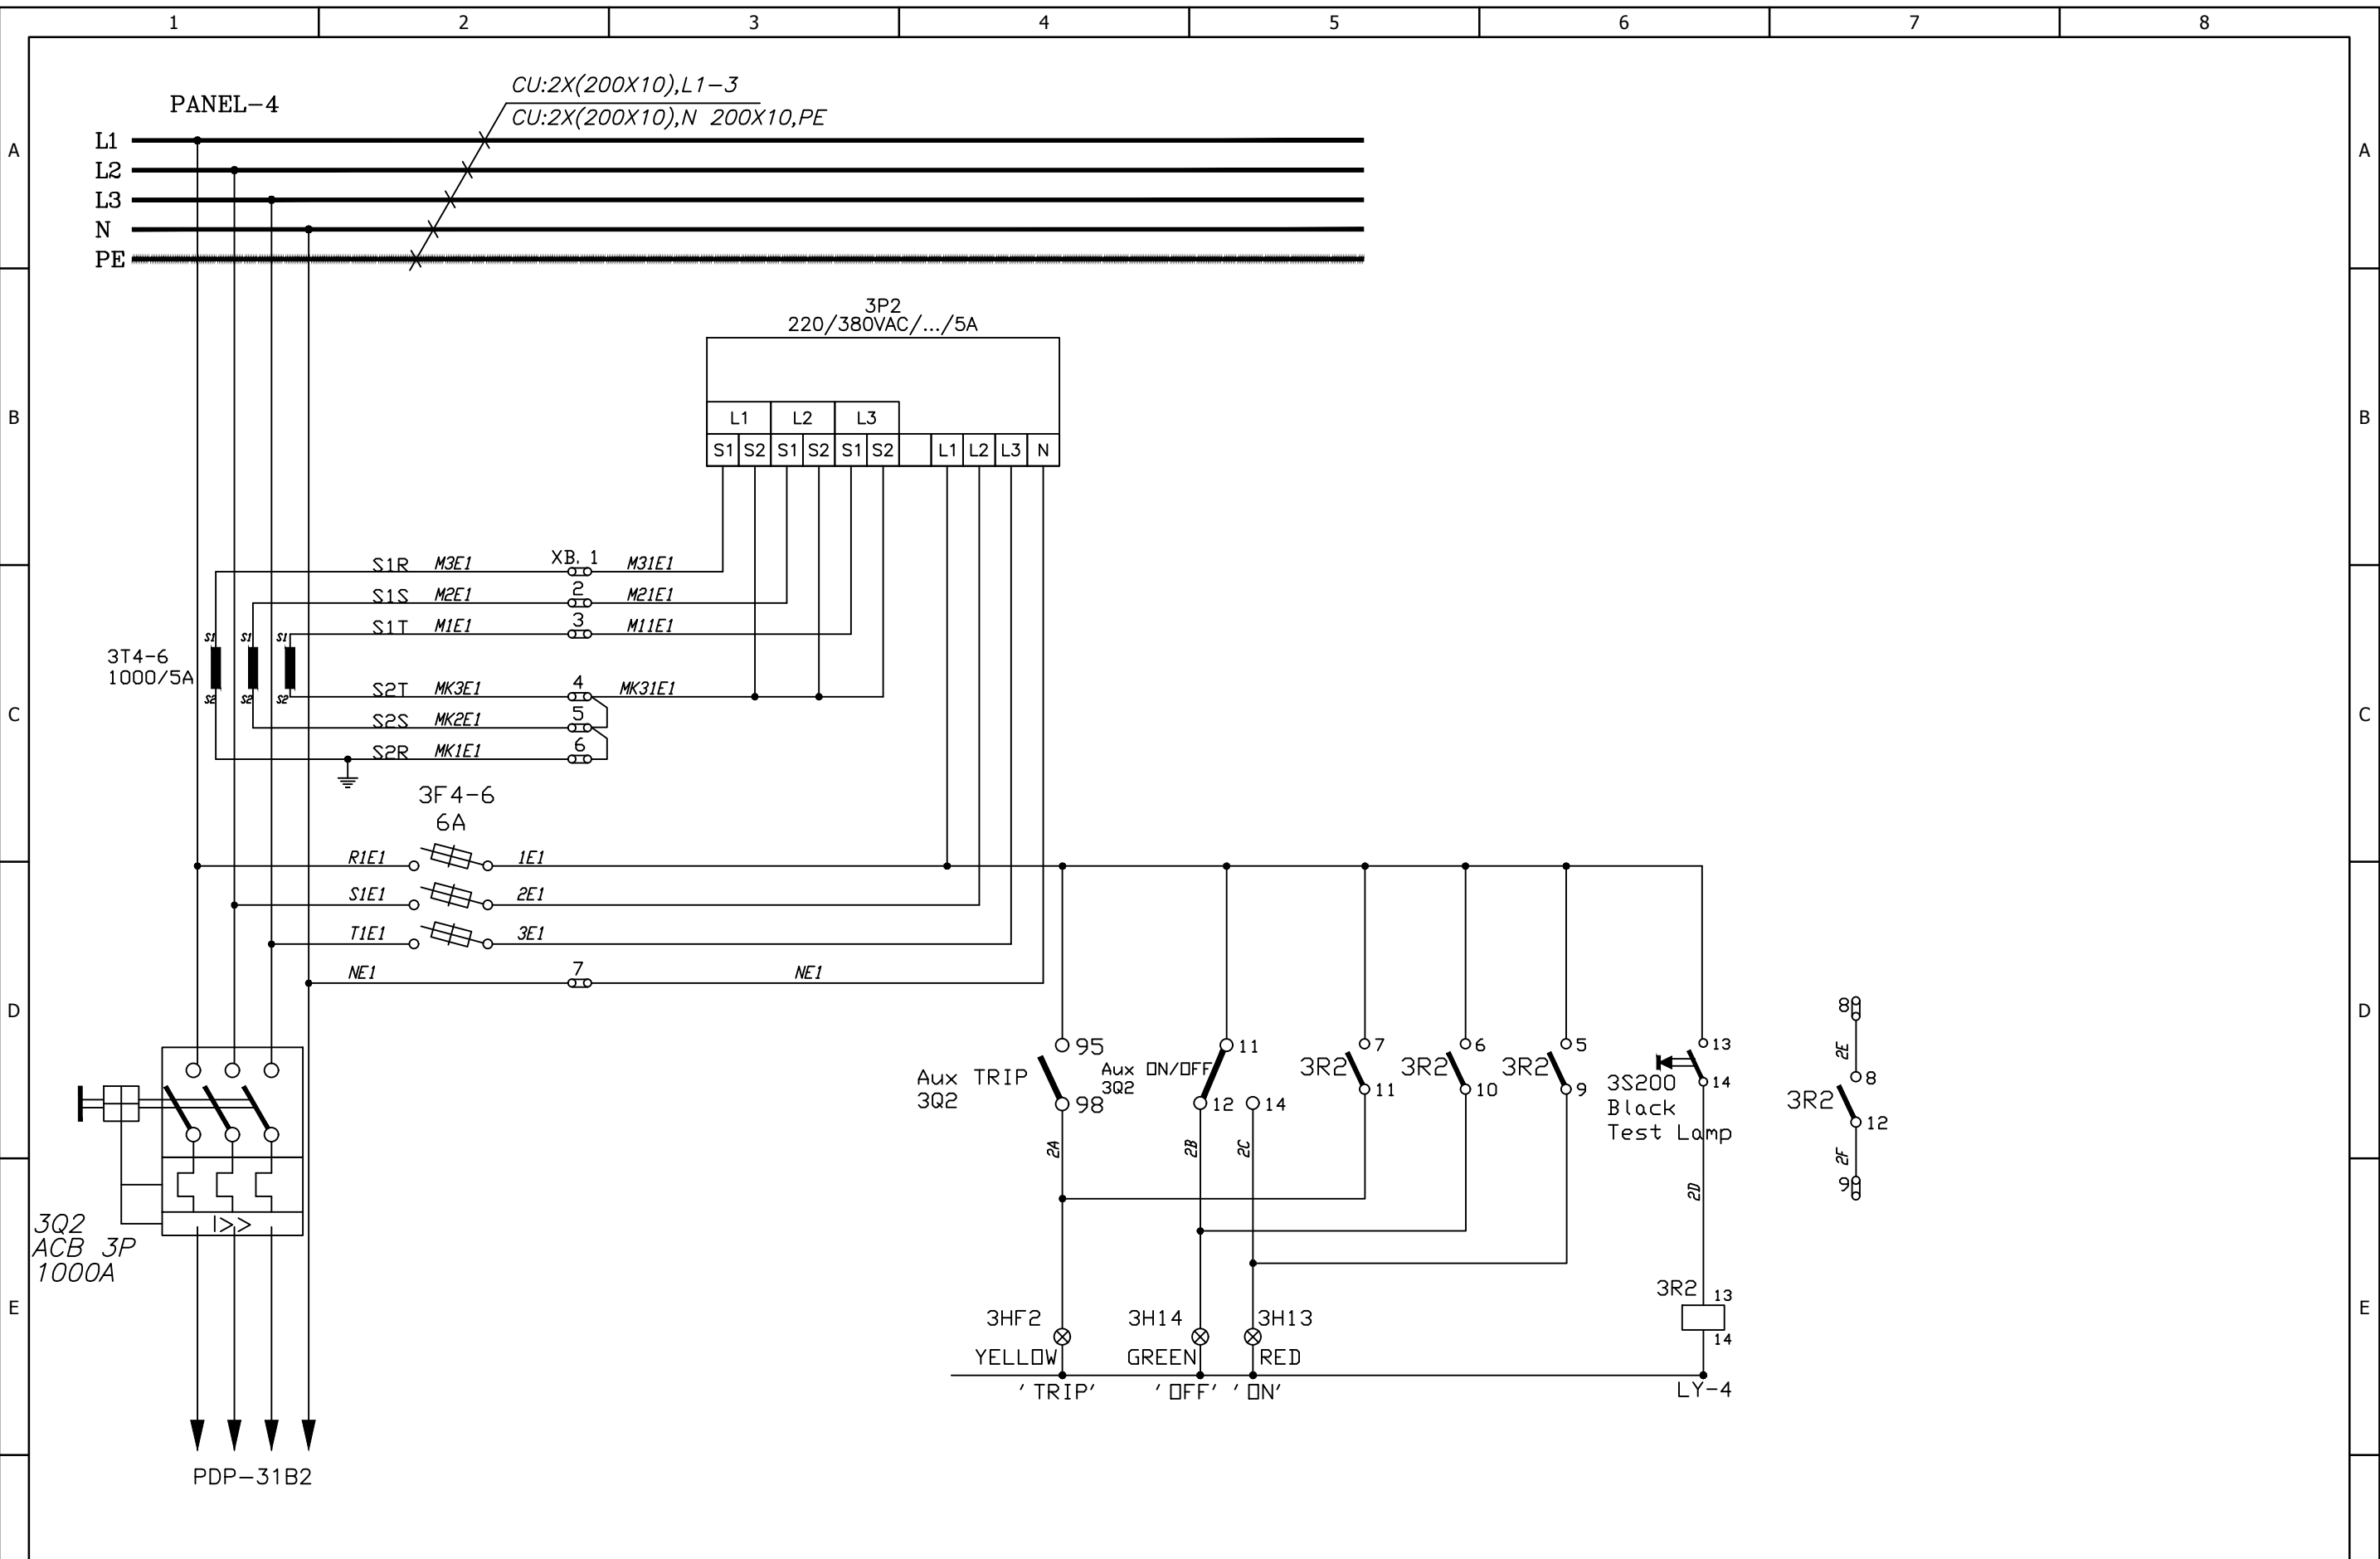


				Date Prep.	13.12.2018	PROJECT TITLE LVD for MNA Serang Plant	  PT. ABB Sakti Industri	WIRING CONTROL DIAGRAM GA Drawing LVD-31B TEXTURIZING B	Scale		= H00
			Prepared	S4	Customer				PT MULTIMAS NABATI ASAHAN	+	
R1	First Issued	02.05.2019		Checked	S1				Drawing Nbr.		Sh. 1
Ind.	Revision	Date	Name	Approved	S1	Based on: MNA-BED-RE-DWG-001		Customer Doc. Nbr.		Cont. 21	
1			2			3	4	5	6	7	8

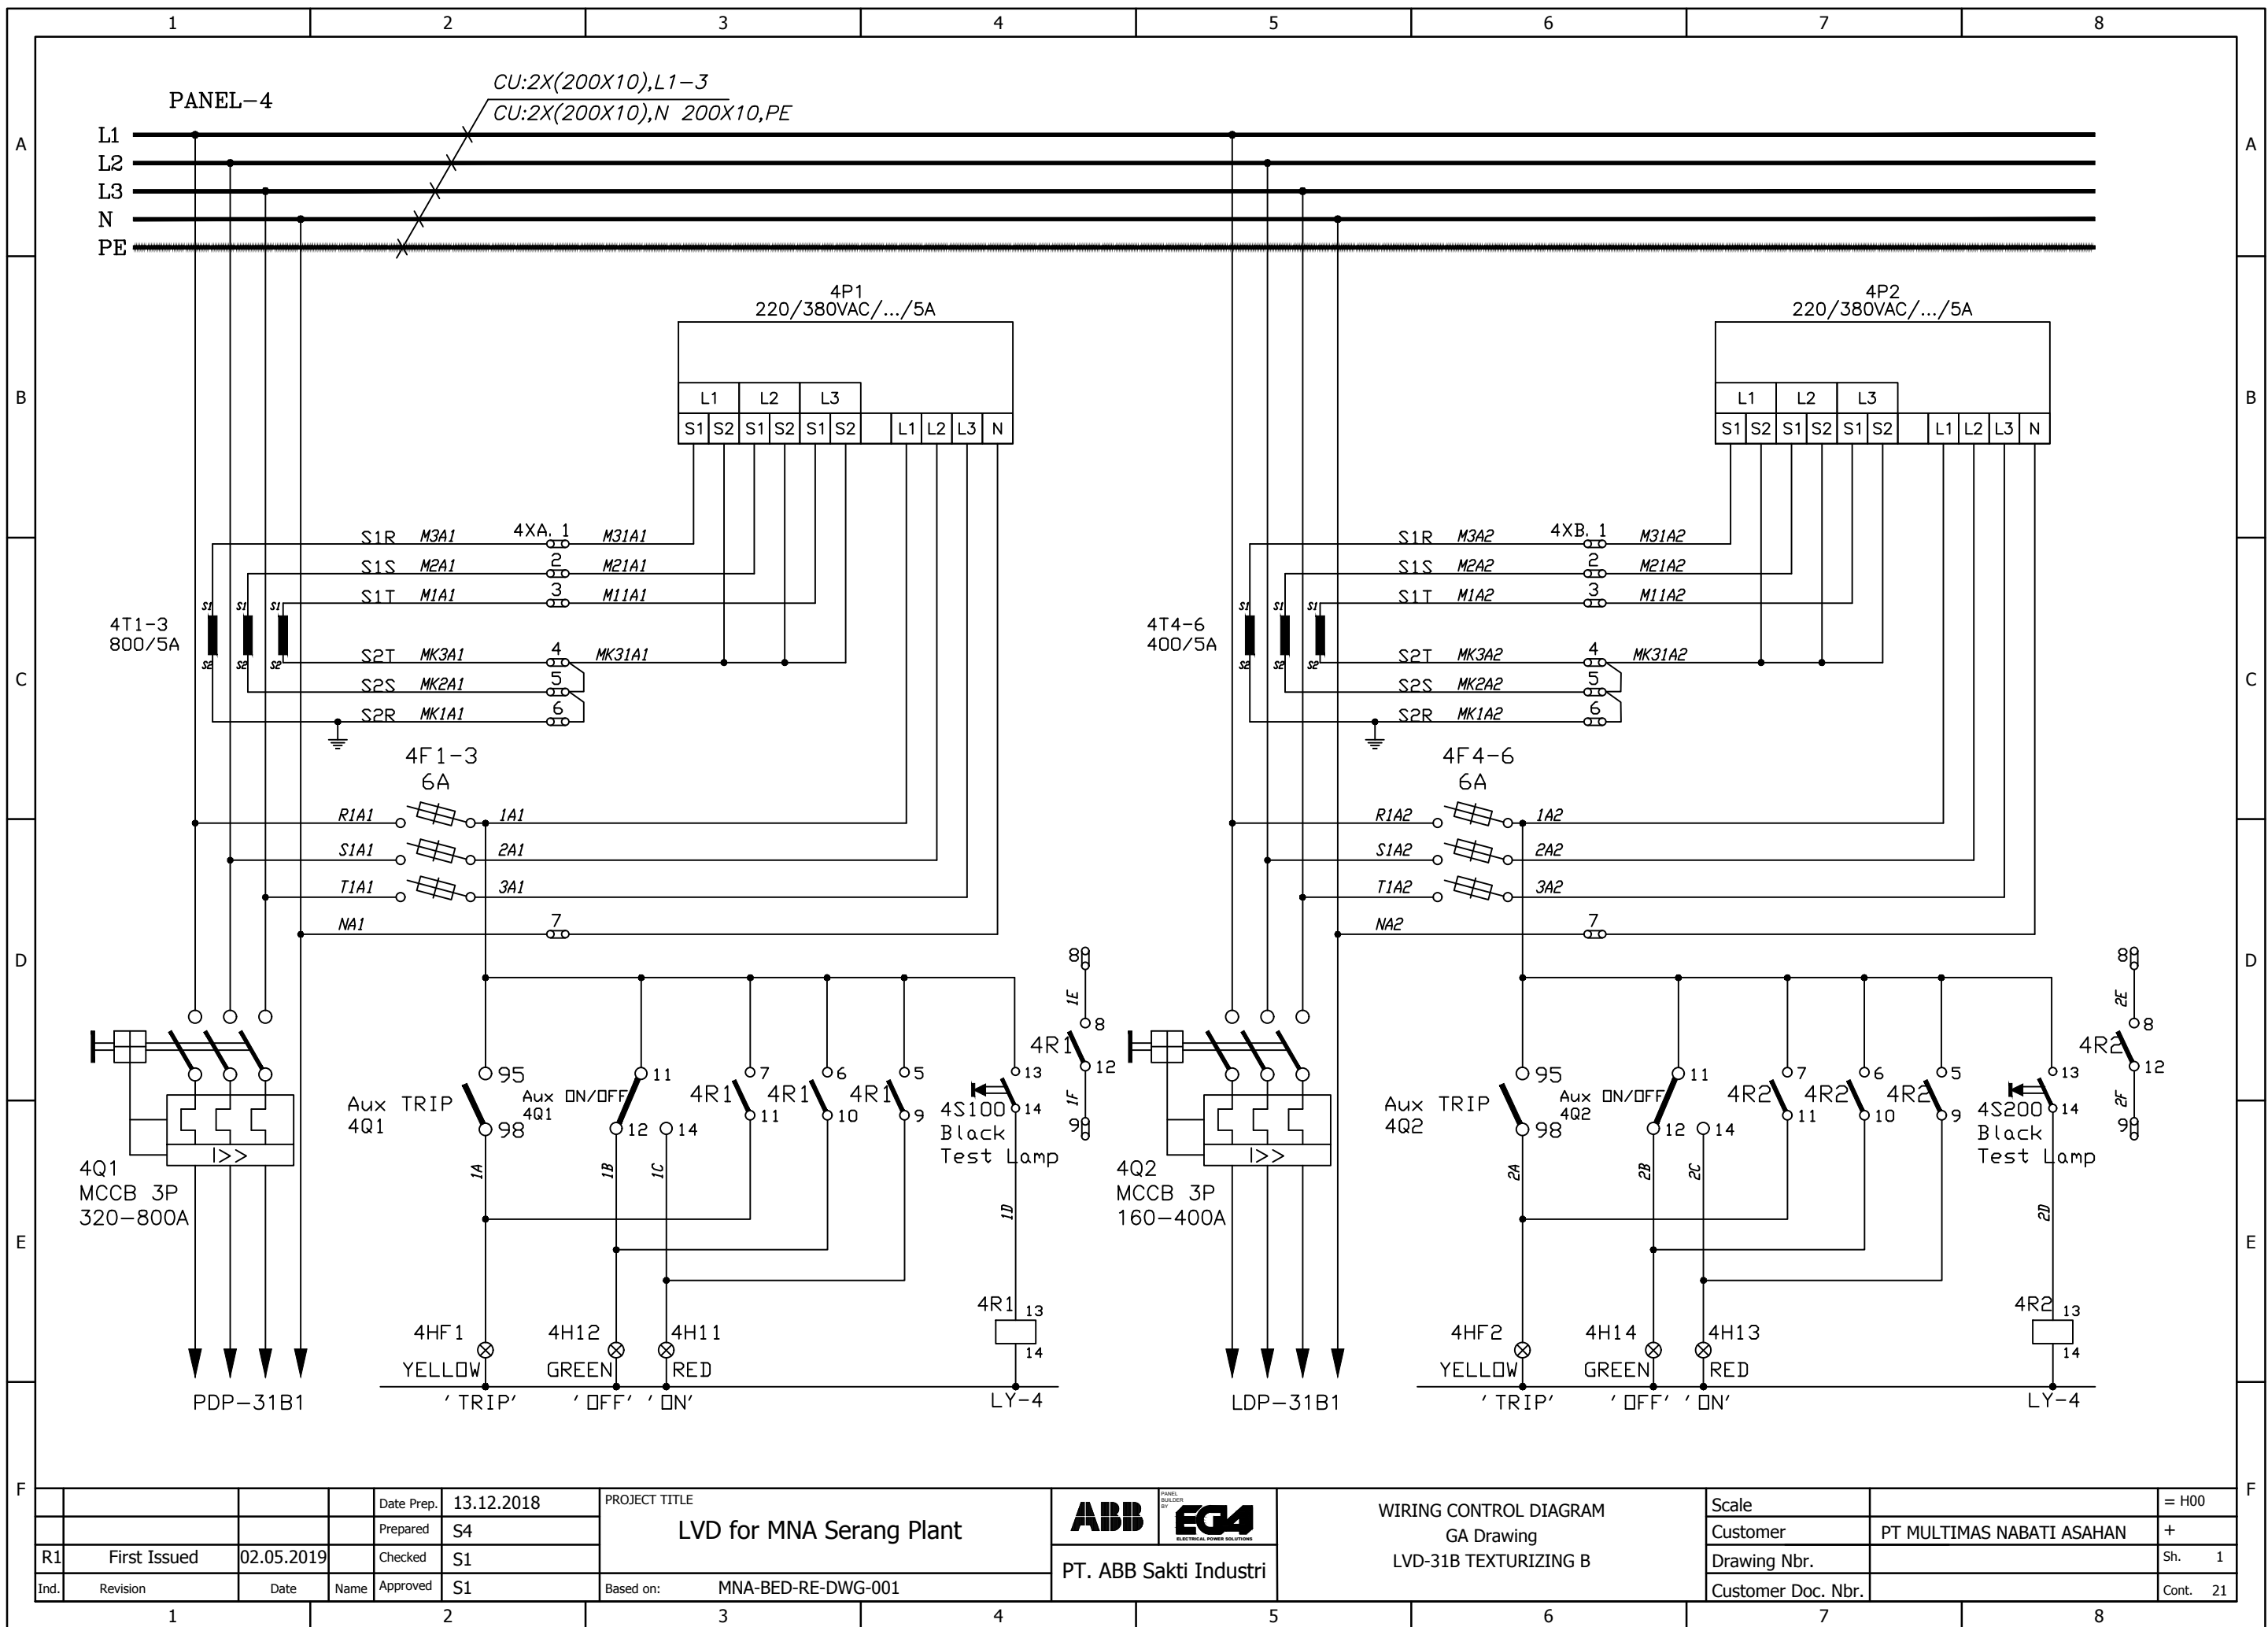

WE RESERVE ALL RIGHTS IN THIS DOCUMENT AND IN THE INFORMATION CONTAINED THEREIN. REPRODUCTION, USE OR DISCLOSURE TO THIRD PARTIES WITHOUT EXPRESS AUTHORITY IS STRICTLY FORBIDDEN.

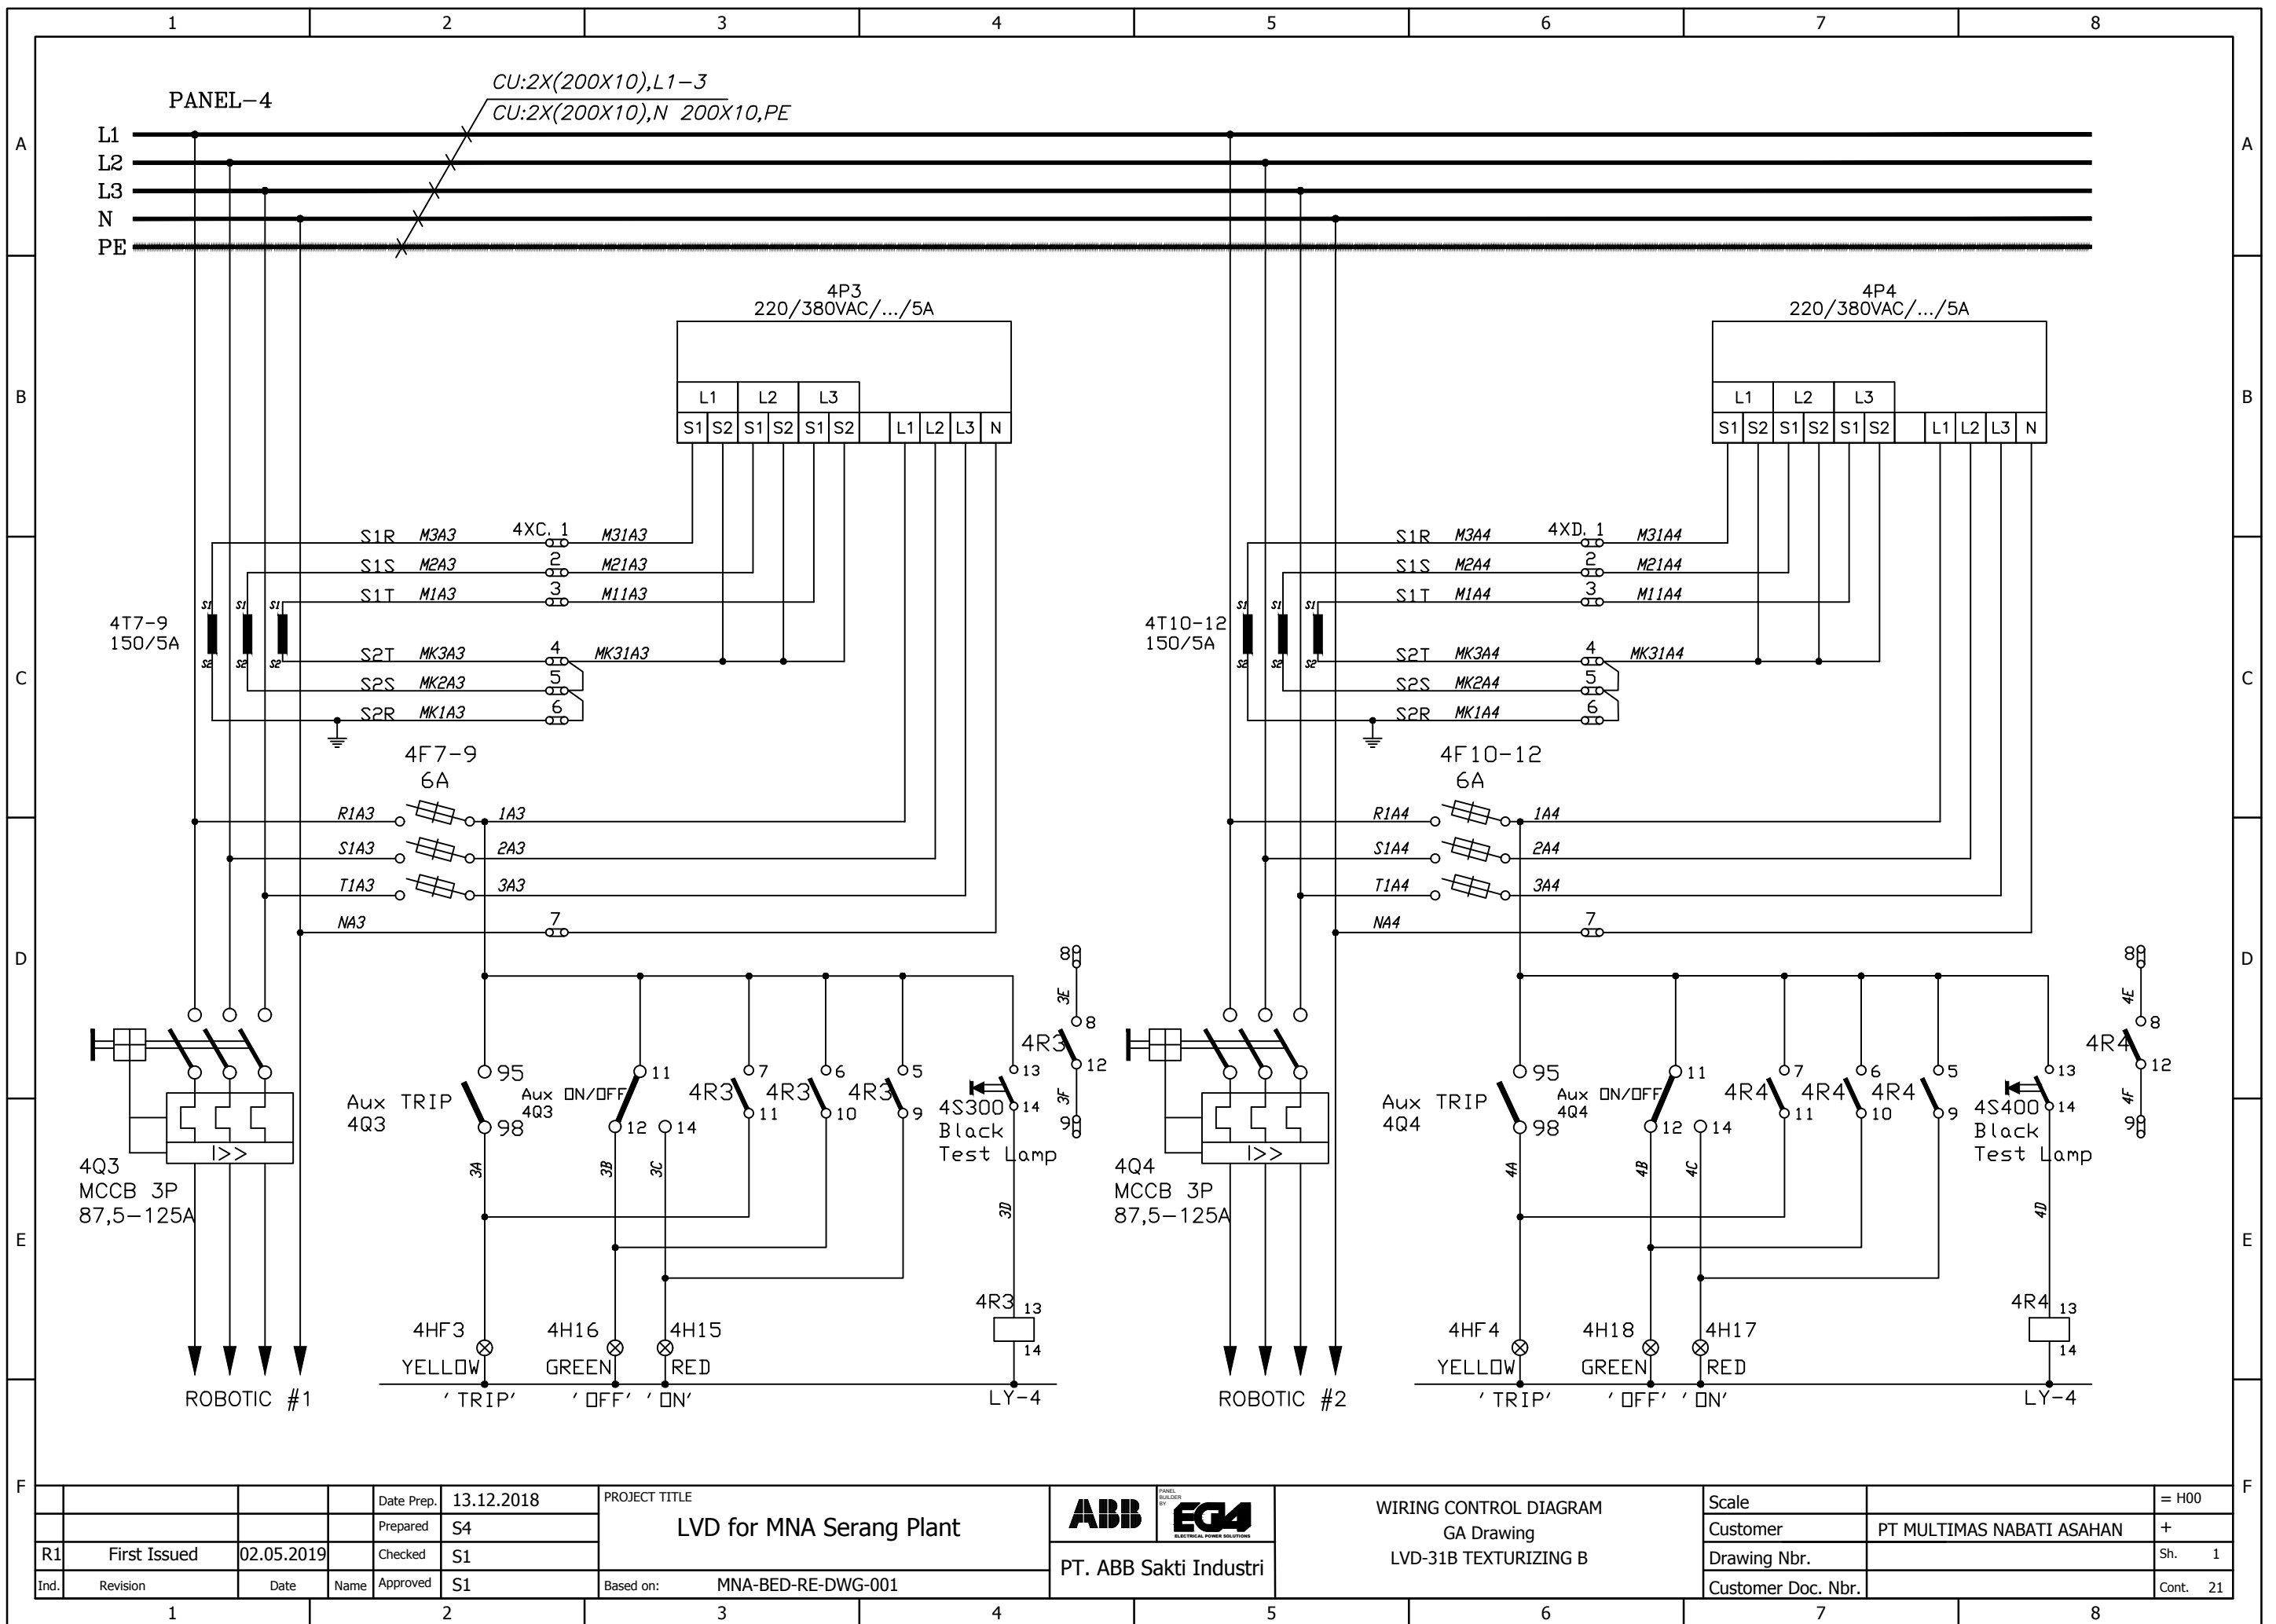

WE RESERVE ALL RIGHTS IN THIS DOCUMENT AND IN THE INFORMATION CONTAINED THEREIN. REPRODUCTION, USE OR DISCLOSURE TO THIRD PARTIES WITHOUT EXPRESS AUTHORITY IS STRICTLY FORBIDDEN.

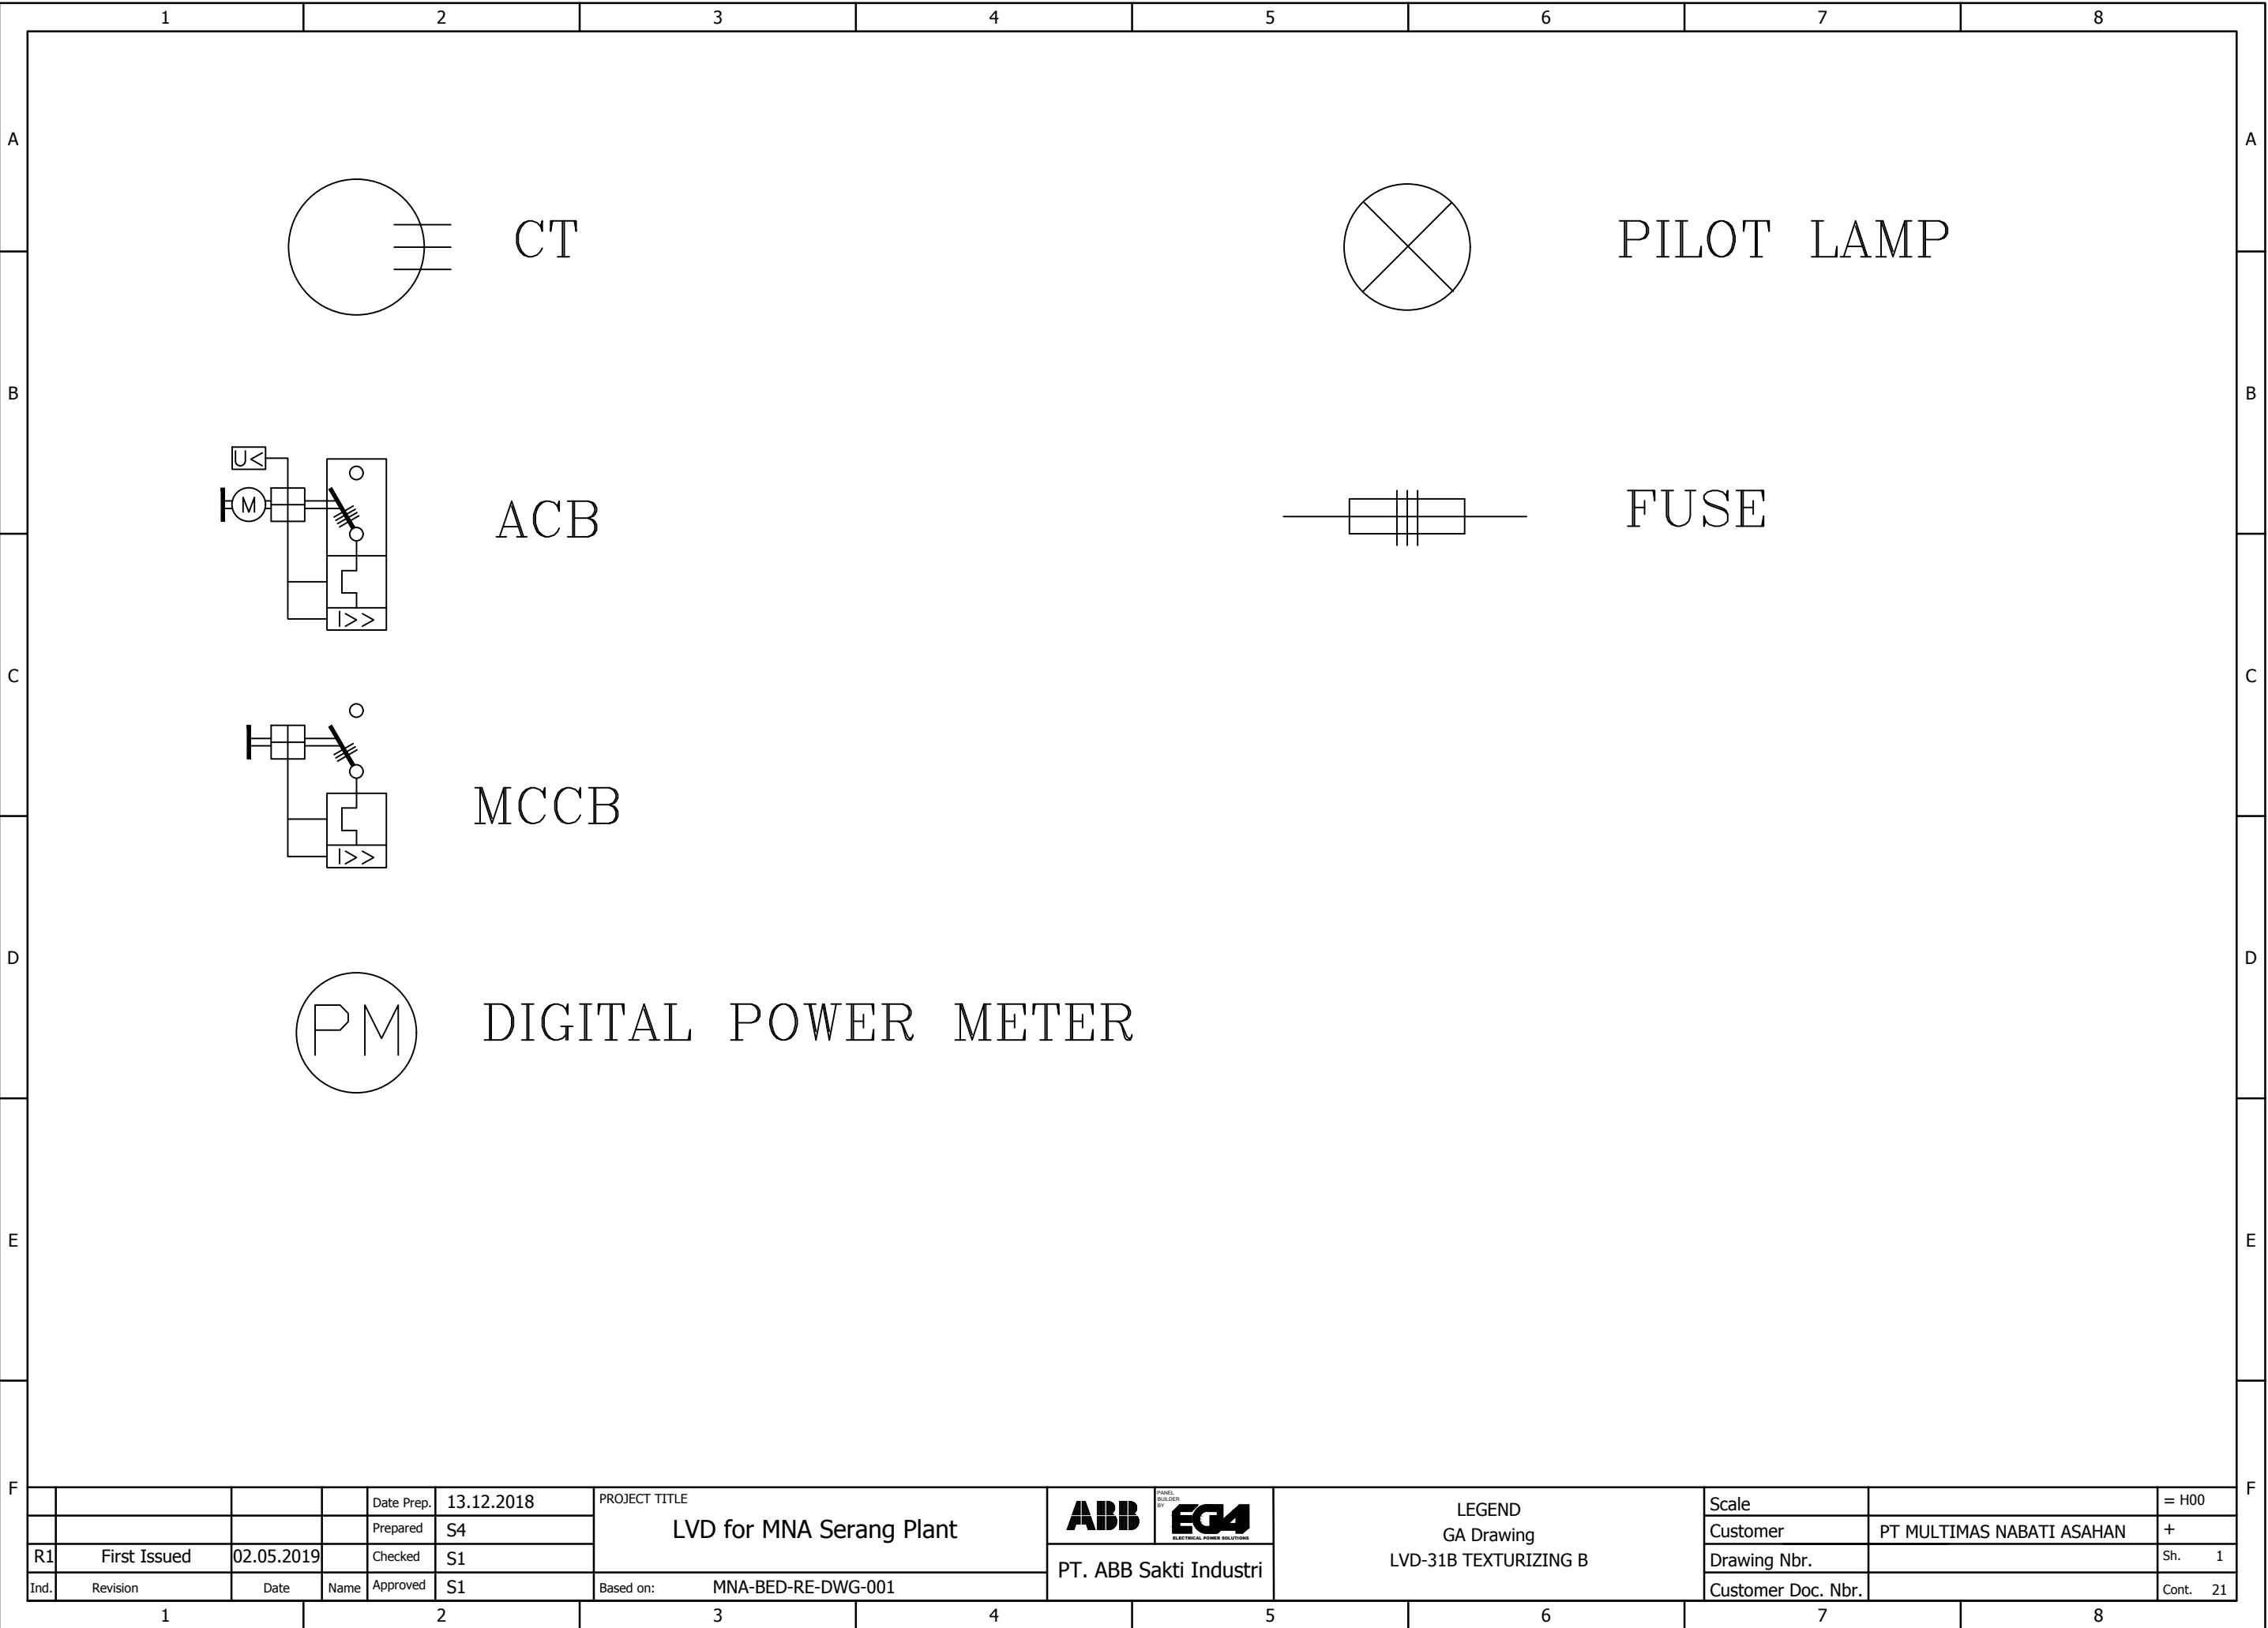

PROJECT TITLE
LVD for MNA Serang Plant



LEGEND
GA Drawing
LVD-31B TEXTURIZING B

Scale		= H00
Customer	PT MULTIMAS NABATI ASAHAN	+
Drawing Nbr.		Sh. 1
Customer Doc. Nbr.		Cont. 21

WE RESERVE ALL RIGHTS IN THIS DOCUMENT AND IN THE INFORMATION CONTAINED THEREIN. REPRODUCTION, USE OR DISCLOSURE TO THIRD PARTIES WITHOUT EXPRESS AUTHORITY IS STRICTLY FORBIDDEN.

1		2		3		4		5		6		7		8		
A	N O	DESCRIPTION			TECHNICAL DATA			QTY	DESIGNATION						A	
		INCOMING														
B	1	Fuse Carrier 6A			AXLE/Setara			7	2F11,2F1-6						B	
	2	Pilot Lamp (LED) 220Vac/50Hz, Red			AXLE/Setara			2	2H1,11							
	3	Pilot Lamp (LED) 220Vac/50Hz, Yellow			AXLE/Setara			2	2H2,HF1							
	4	Pilot Lamp (LED) 220Vac/50Hz, Green			AXLE/Setara			2	2H3,12							
	5	DIGITAL POWER METER (*)			ABB, M2M ETHERNET			1	2P1							
	6	CT 4000/5A CL.0.5 40VA			Howig, HG 120-4000			4	2T1-4							
	7	ACB 3P 4000A, 66KA, DO, Ekip Touch LSIG (*)			ABB, E4.2N40 D/O			1	2Q0							
C	8	+ Shunt Trip Release (Y0) (*)			ABB, Y0			1	-						C	
	9	+ Motor (M) + Closing Release (YC) For E2.2-E6.2 (*)			ABB, M+YC			1	-							
	10	+ Padlocks For E2.2-E6.2 (*)			ABB,			1	-							
	11	+ Ekip Com Protocol IEC 61850 (*)			ABB,			1	-							
	12	Control Relay 220Vac			Omron, LY-2			1	2RF1							
	13	Control Relay 220Vac			Omron, LY-4			2	2R1-2							
	14	Push Button On, 1NO, Green			Ega			1	2S11							
D	15	Push Button Off, 1NO, Red			Ega			1	2S12						D	
	16	Push Button Test Lamp , 1NO, Black			Ega			1	2S100							
	17															
	18	COUPLER														
	19	Fuse Carrier 6A			AXLE/Setara			1	1F11							
	20	Pilot Lamp (LED) 220Vac/50Hz, Red			AXLE/Setara			1	1H11							
	21	Pilot Lamp (LED) 220Vac/50Hz, Yellow			AXLE/Setara			1	1HF1							
E	22	Pilot Lamp (LED) 220Vac/50Hz, Green			AXLE/Setara			1	1H12						E	
	23	ACB 4P 4000A, 66KA, FT, Ekip Dip LI (*)			ABB, E4.2N40 F/T			1	1Q01							
	24	+ Padlocks For E2.2-E6.2 (*)			ABB,			1	-							
	25	Push Button Test Lamp , 1NO, Black			Ega			1	1S100							
	26	Control Relay 220Vac			Omron, LY-4			1	-							
	F					Date Prep.	13.12.2018	PROJECT TITLE LVD for MNA Serang Plant			  PT. ABB Sakti Industri	COMPONENT LIST		Scale		
					Prepared	S4	GA Drawing					Customer	PT MULTIMAS NABATI ASAHAN	+		
R1		First Issued	02.05.2019		Checked	S1	LVD-31B TEXTURIZING B					Drawing Nbr.		Sh. 1		
Ind.		Revision		Date	Name	Approved	S1	Based on:	MNA-BED-RE-DWG-001	Customer Doc. Nbr.		Cont. 21				
1		2		3		4		5		6		7		8		

