


				Date Prep.	13.12.2018	PROJECT TITLE LVD for MNA Serang Plant	ABB PANEL BUILDER BY EG4 ELECTRICAL POWER SOLUTIONS	FRONT VIEW GA Drawing LVD-32A TANKFARM WICA	Scale		= H00
			Prepared	S4	Customer				PT MULTIMAS NABATI ASAHAN	+	
R1	First Issued	02.05.2019		Checked	S1				Drawing Nbr.		Sh. 1
Ind.	Revision	Date	Name	Approved	S1	Based on: MNA-BED-RE-DWG-001	PT. ABB Sakti Industri	Customer Doc. Nbr.		Cont. 21	

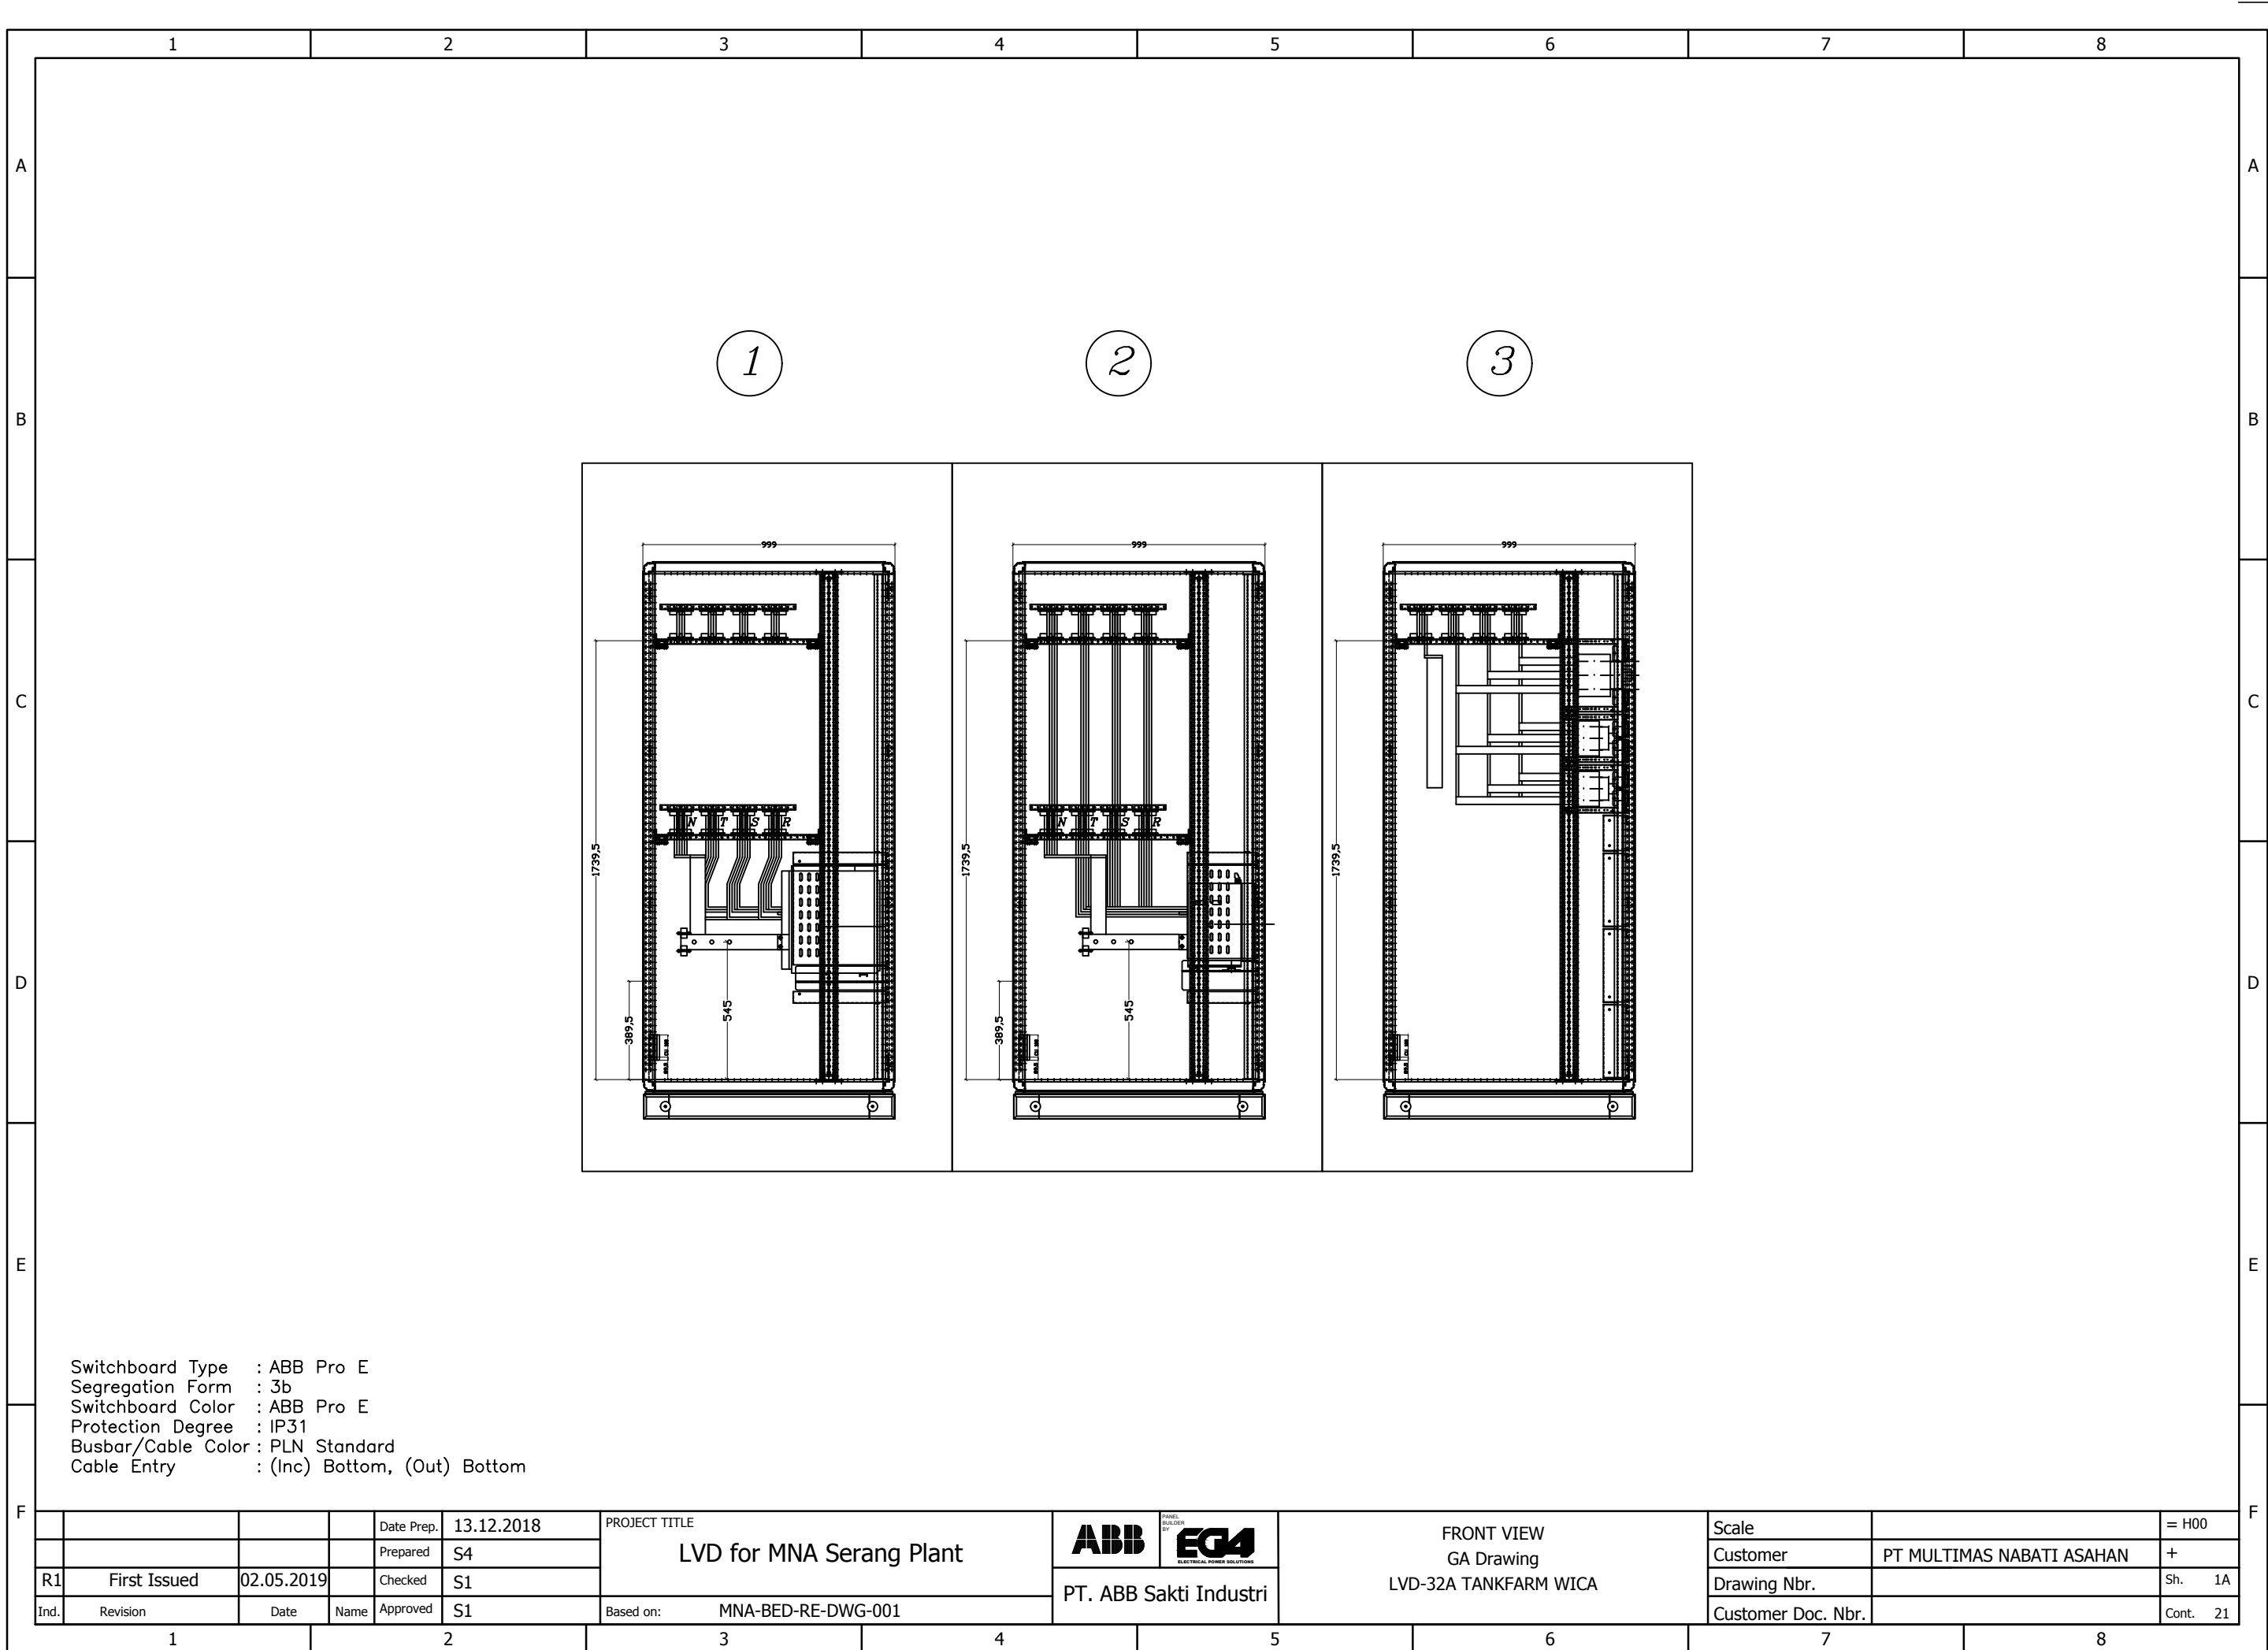

1		2		3		4		5		6		7		8	
A														A	
B														B	
C														C	
D														D	
E														E	
F														F	

				Date Prep. 13.12.2018		PROJECT TITLE LVD for MNA Serang Plant		ABB PANEL BUILDER BY EG4 ELECTRICAL POWER SOLUTIONS PT. ABB Sakti Industri		FRONT VIEW		Scale		= H00			
				Prepared S4						GA Drawing		Customer		PT MULTIMAS NABATI ASAHAN		+	
R1		First Issued		02.05.2019						Checked S1		LVD-32A TANKFARM WICA		Drawing Nbr.		Sh. 1A	
Ind.		Revision		Date		Name		Approved S1		Based on: MNA-BED-RE-DWG-001		Customer Doc. Nbr.		Cont. 21			

1		2		3		4		5		6		7		8	
A														A	
B														B	
C														C	
D														D	
E														E	
F														F	

1

2

3

Switchboard Type : ABB Pro E
Segregation Form : 3b
Switchboard Color : ABB Pro E
Protection Degree : IP31
Busbar/Cable Color : PLN Standard
Cable Entry : (Inc) Bottom, (Out) Bottom

1		2		3		4		5		6		7		8	
A															
B															
C															
D															
E															
F															

1

2

3

<

WE RESERVE ALL RIGHTS IN THIS DOCUMENT AND IN THE INFORMATION CONTAINED THEREIN. REPRODUCTION, USE OR DISCLOSURE TO THIRD PARTIES WITHOUT EXPRESS AUTHORITY IS STRICTLY FORBIDDEN.

12345678

A

B


C

D


E

F

SIDE VIEW

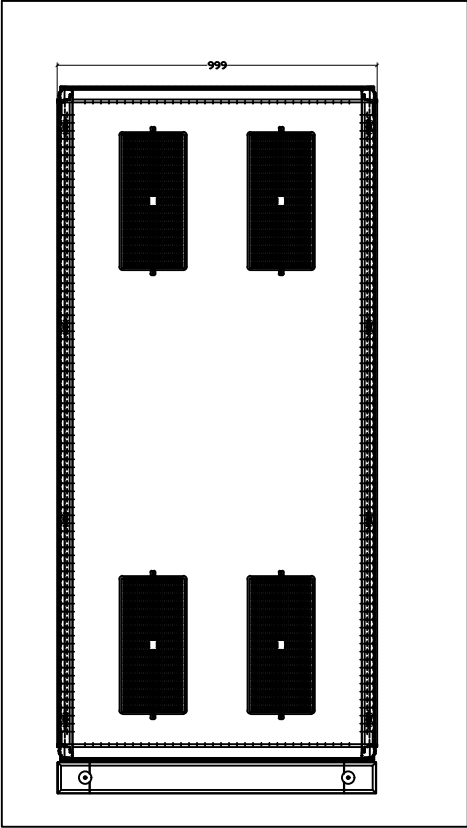

BACK VIEW

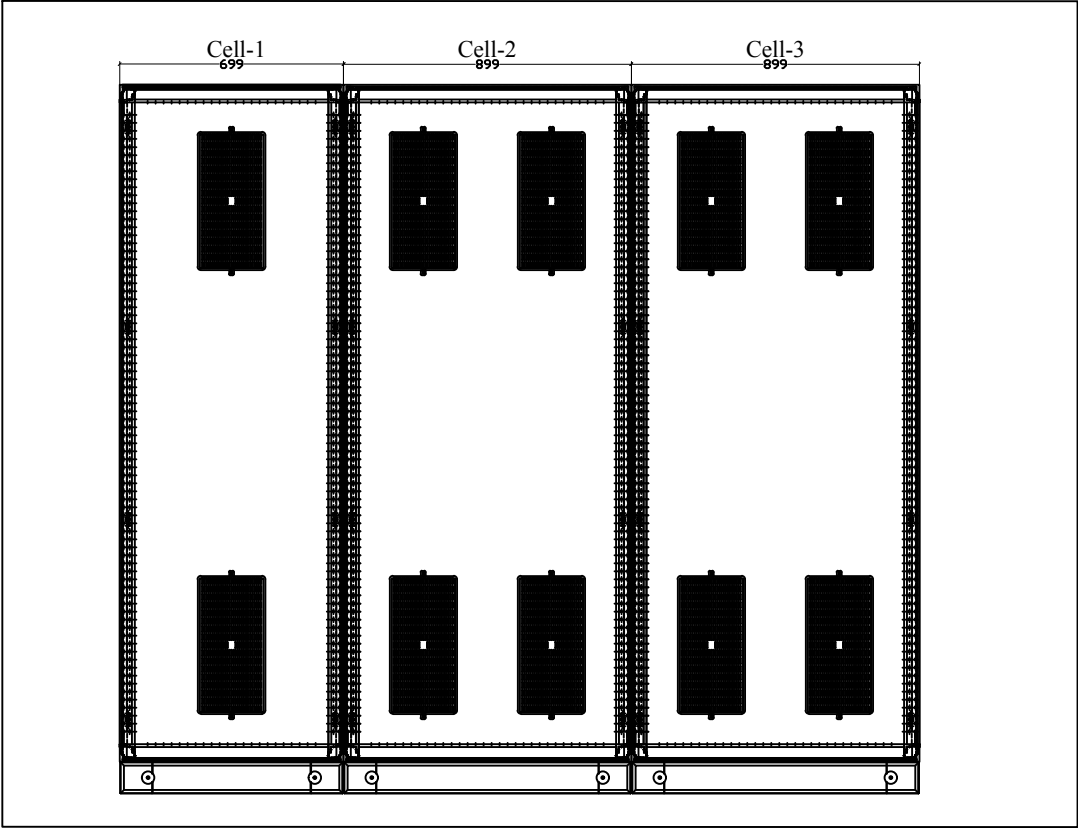


Switchboard Type : ABB Pro E
Segregation Form : 3b
Switchboard Color : ABB Pro E
Protection Degree : IP31
Busbar/Cable Color : PLN Standard
Cable Entry : (Inc) Bottom, (Out) Bottom


				Date Prep.	13.12.2018	PROJECT TITLE LVD for MNA Serang Plant	ABB PANEL BUILDING BY EG4 ELECTRICAL POWER SOLUTIONS PT. ABB Sakti Industri	FRONT VIEW	Scale		= H00
				Prepared	S4			GA Drawing	Customer	PT MULTIMAS NABATI ASAHAN	+
R1	First Issued	02.05.2019		Checked	S1			LVD-32A TANKFARM WICA	Drawing Nbr.		Sh. 1B
Ind.	Revision	Date	Name	Approved	S1	Based on: MNA-BED-RE-DWG-001		Customer Doc. Nbr.		Cont. 21	

12345678

WE RESERVE ALL RIGHTS IN THIS DOCUMENT AND IN THE INFORMATION CONTAINED THEREIN. REPRODUCTION, USE OR DISCLOSURE TO THIRD PARTIES WITHOUT EXPRESS AUTHORITY IS STRICTLY FORBIDDEN.

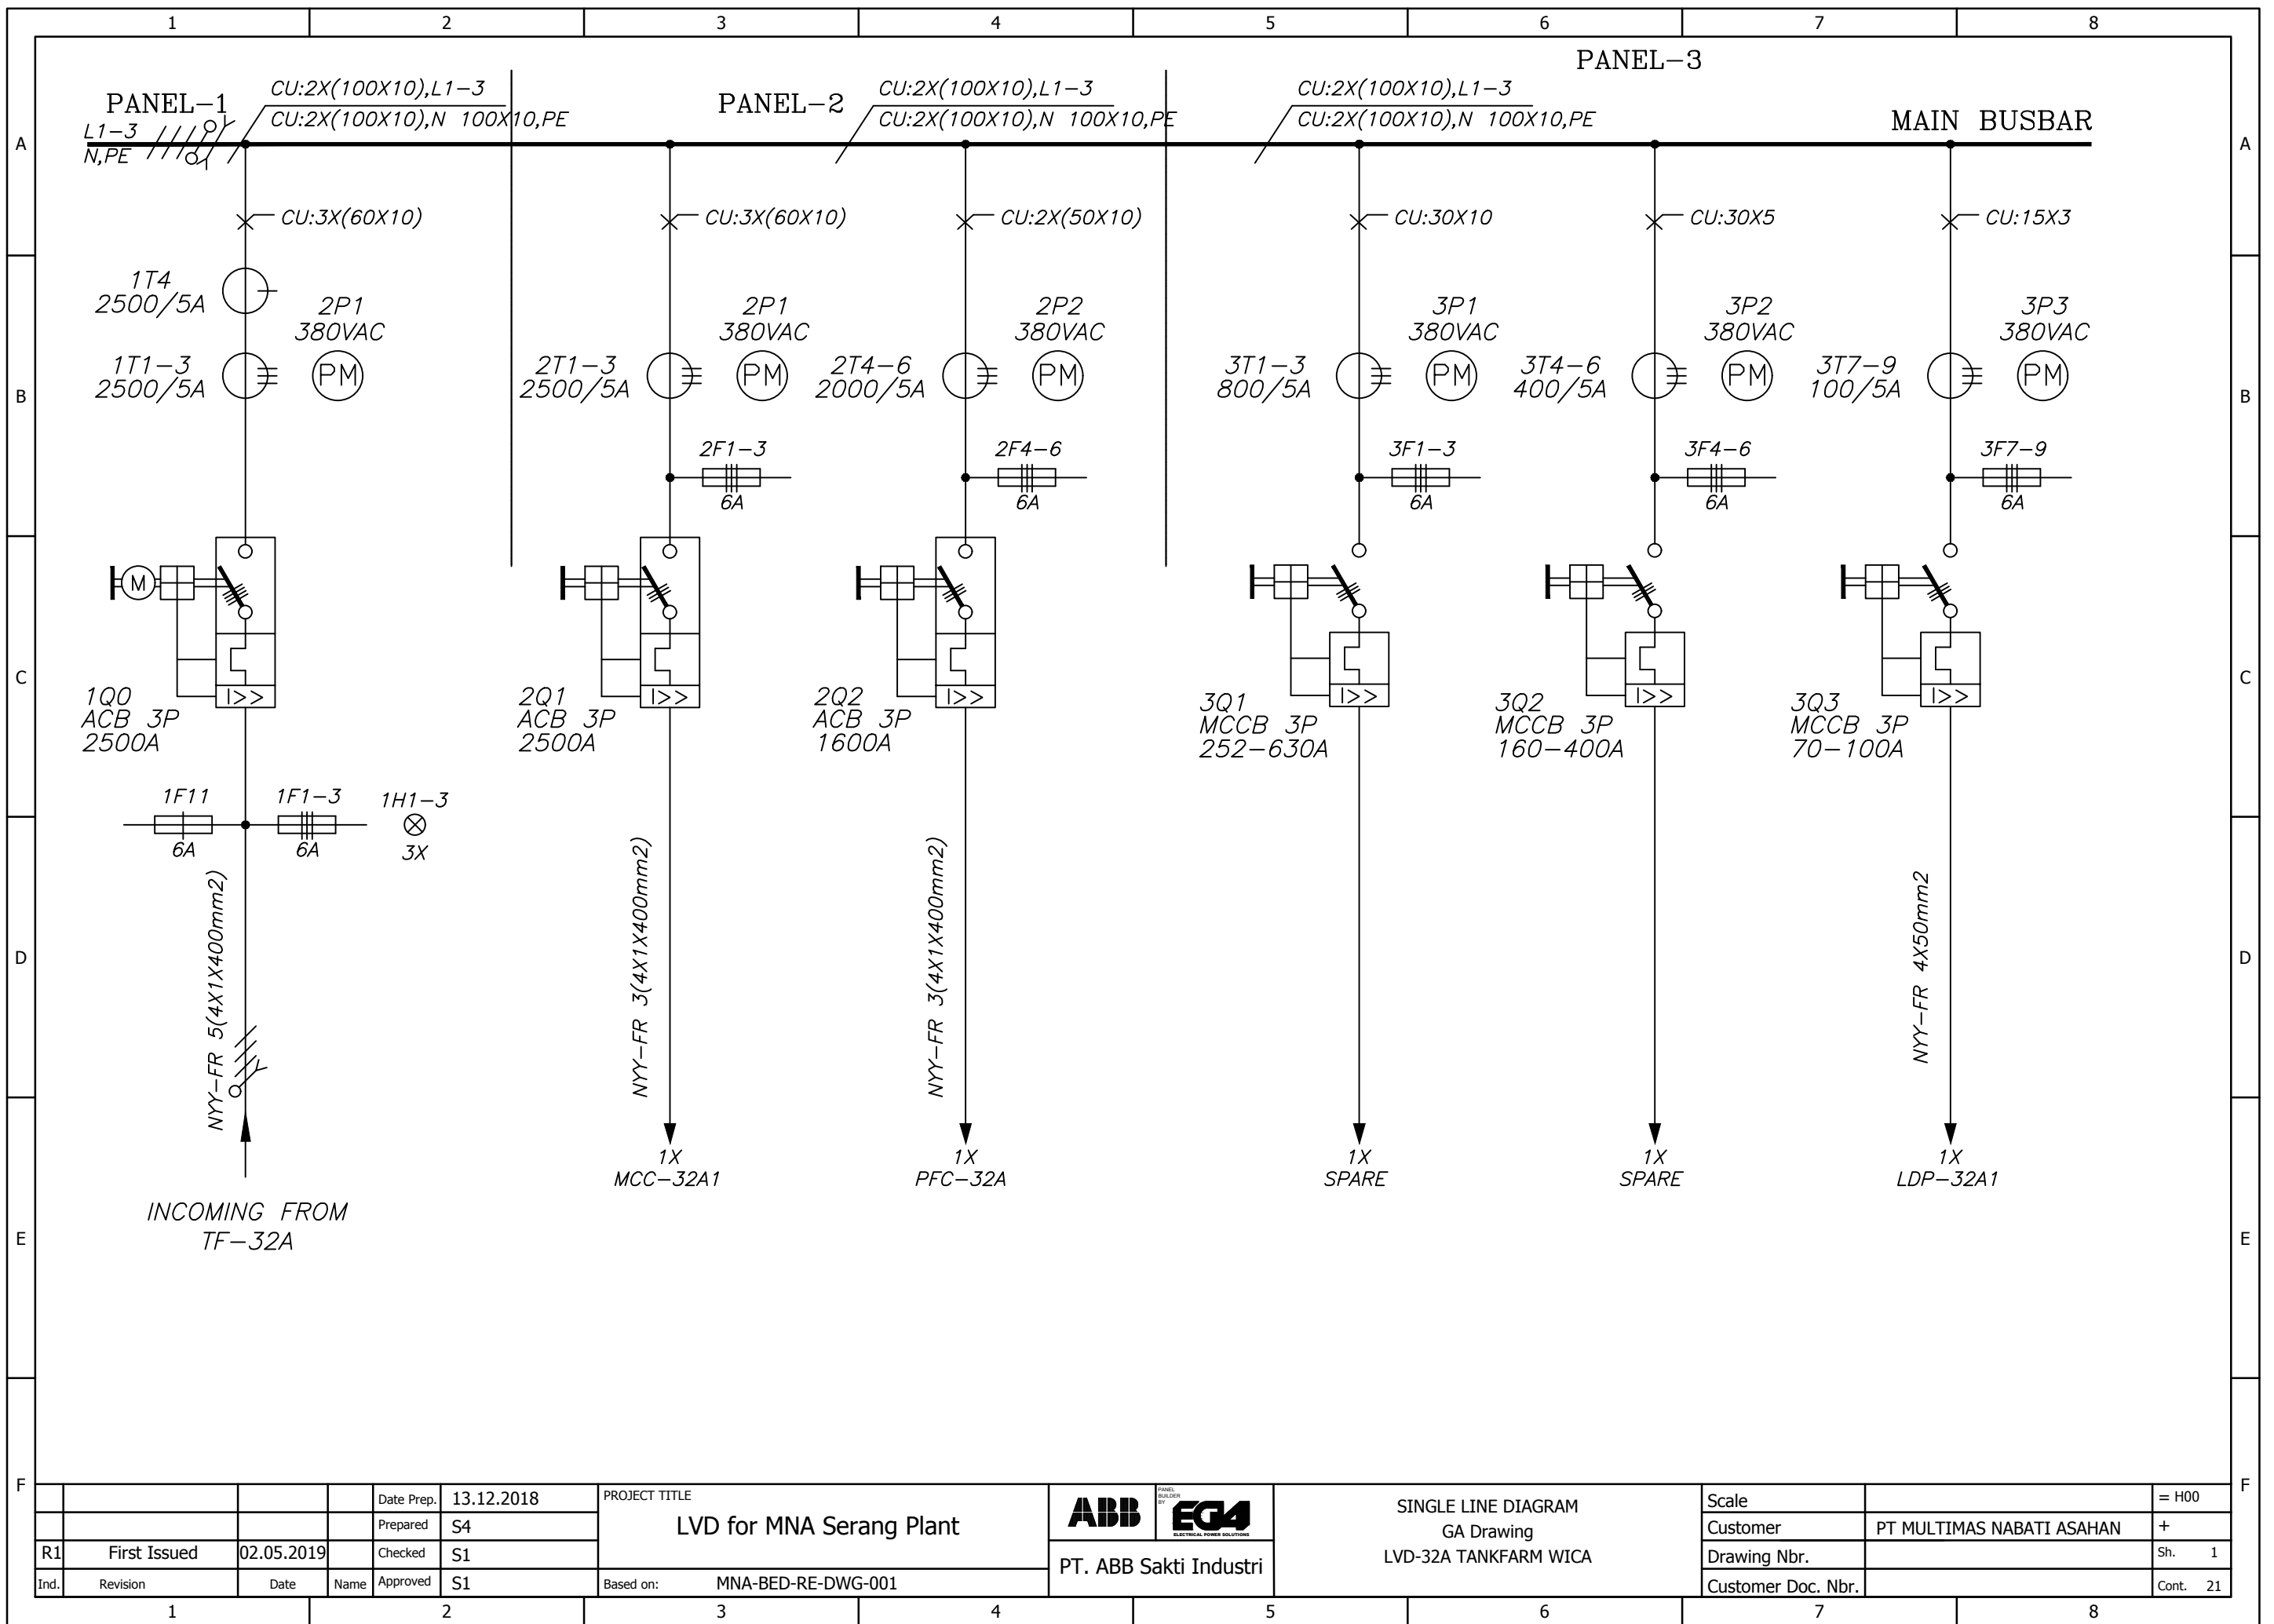

WE RESERVE ALL RIGHTS IN THIS DOCUMENT AND IN THE INFORMATION CONTAINED THEREIN. REPRODUCTION, USE OR DISCLOSURE TO THIRD PARTIES WITHOUT EXPRESS AUTHORITY IS STRICTLY FORBIDDEN.

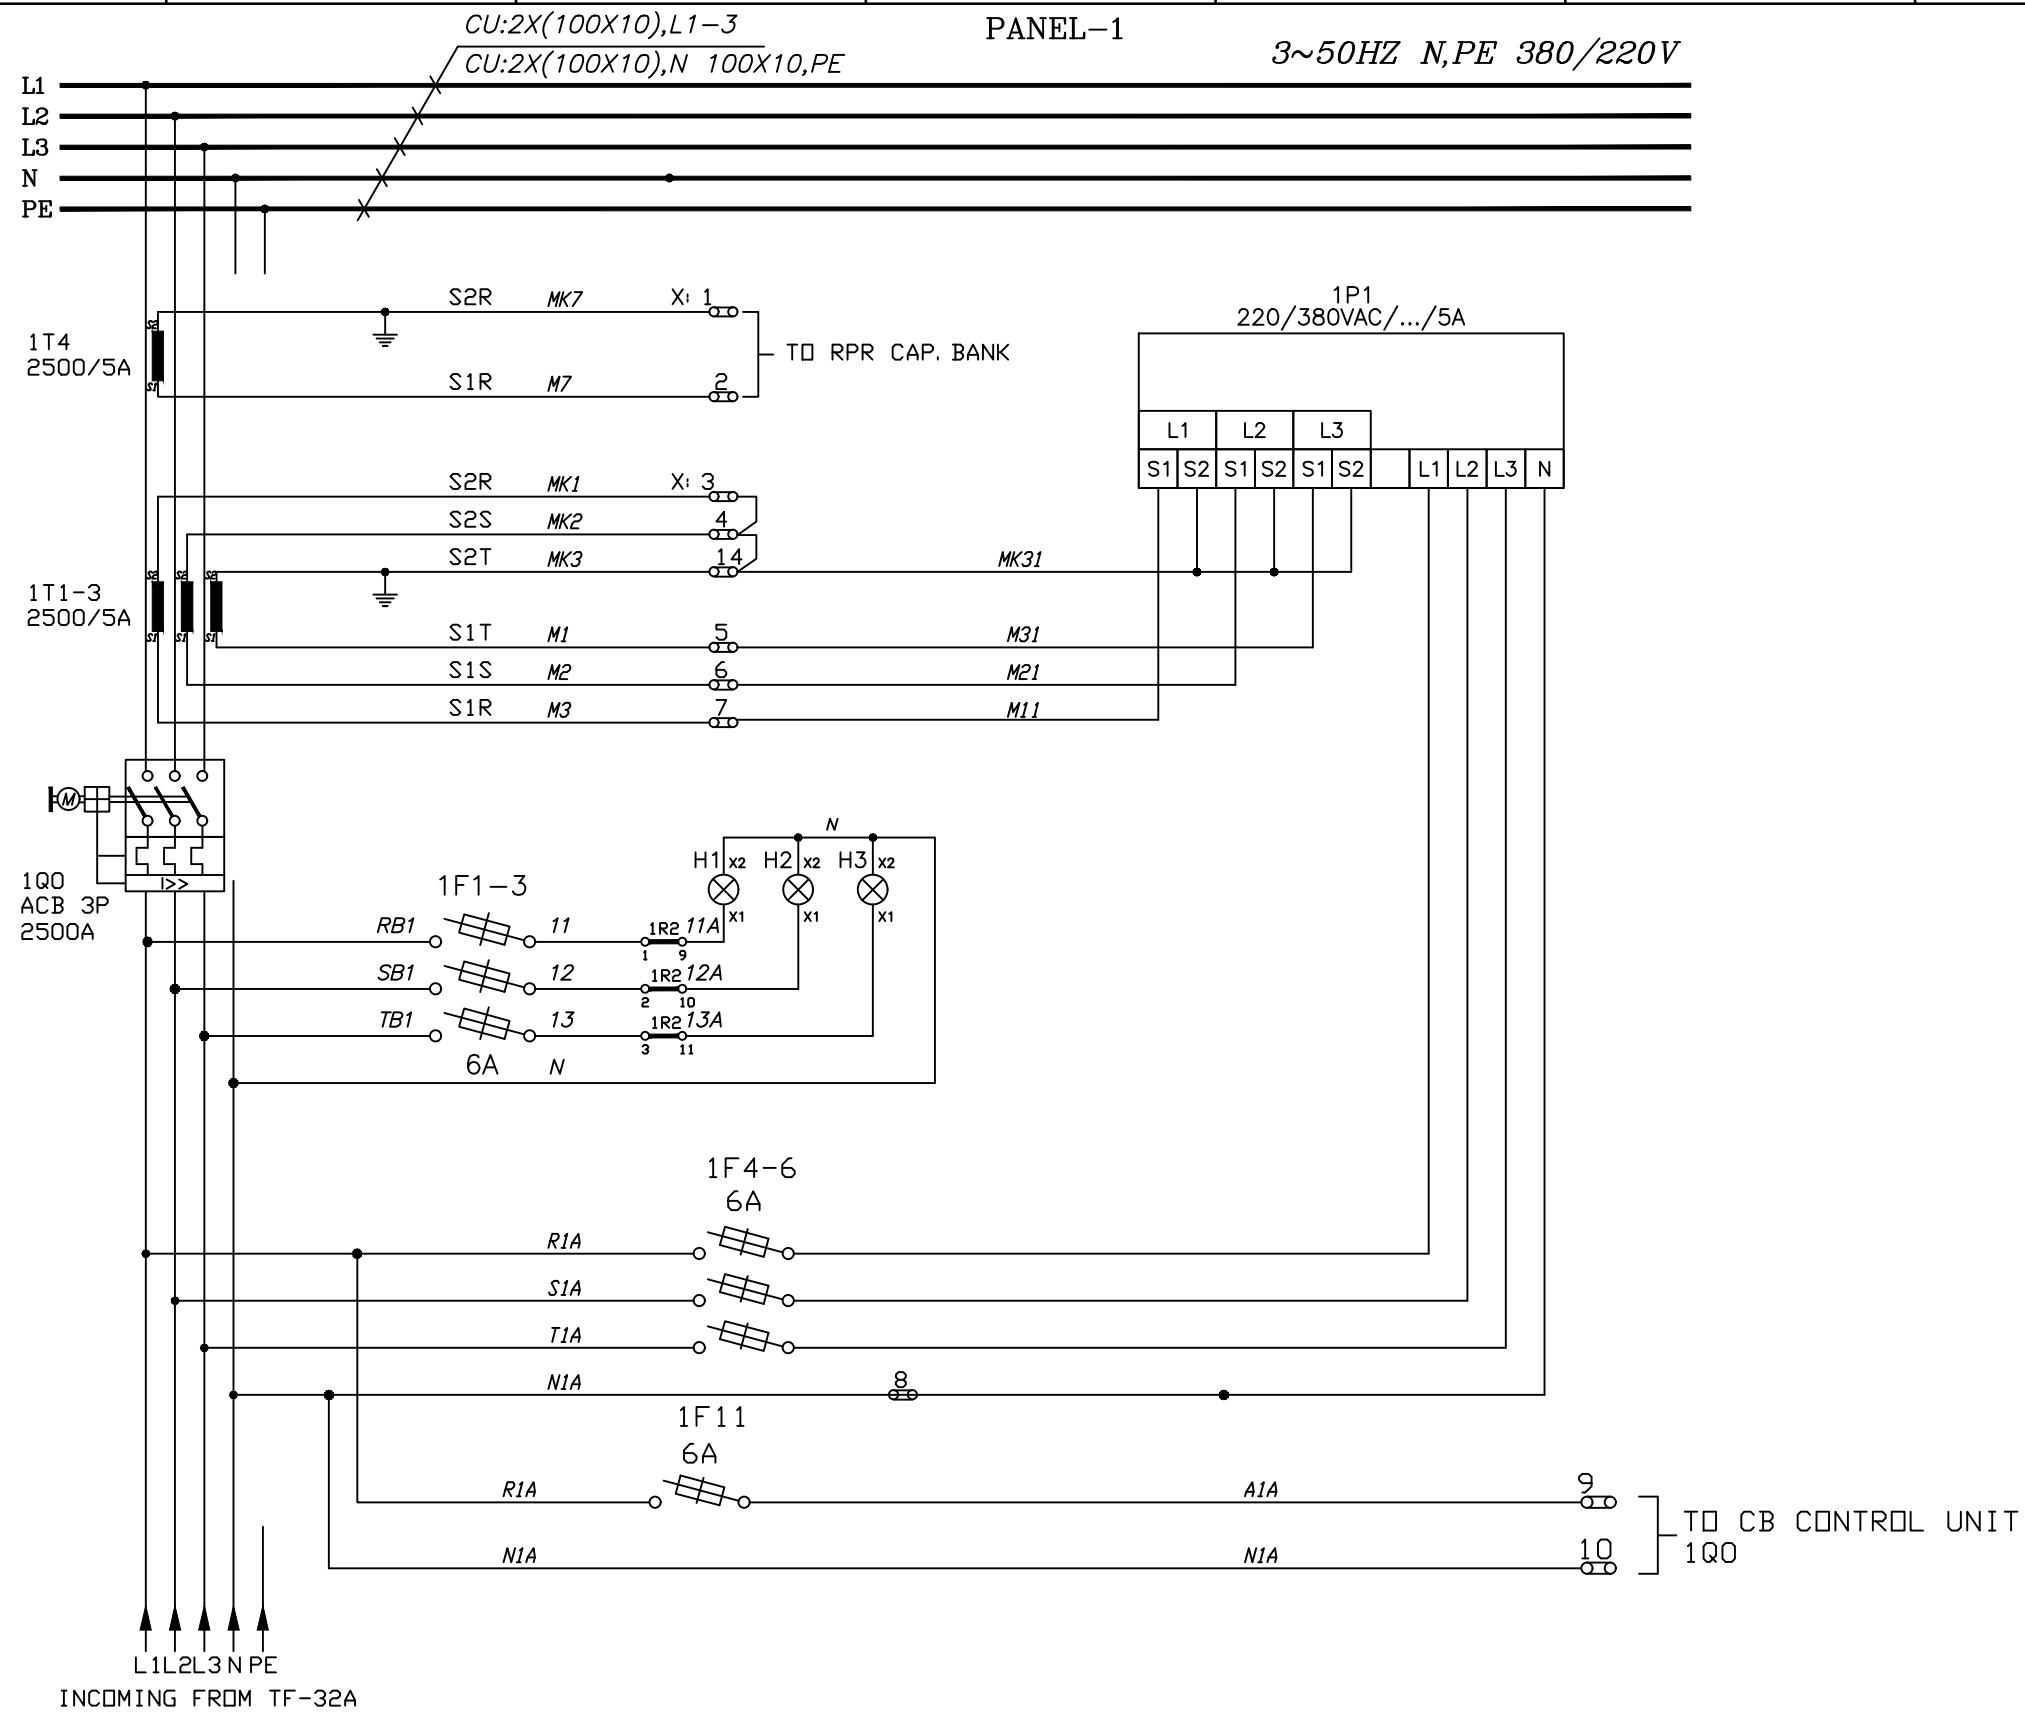

				Date Prep.	13.12.2018	PROJECT TITLE LVD for MNA Serang Plant	ABB PANEL BUILDER BY EG4 ELECTRICAL POWER SOLUTIONS PT. ABB Sakti Industri	WIRING CONTROL DIAGRAM GA Drawing LVD-32A TANKFARM WICA	Scale		= H00
				Prepared	S4				Customer	PT MULTIMAS NABATI ASAHAN	+
R1	First Issued	02.05.2019		Checked	S1				Drawing Nbr.		Sh. 1
Ind.	Revision	Date	Name	Approved	S1	Based on:	MNA-BED-RE-DWG-001		Customer Doc. Nbr.		Cont. 21

1

2

3

4


5

6


7

8

WE RESERVE ALL RIGHTS IN THIS DOCUMENT AND IN THE INFORMATION CONTAINED THEREIN. REPRODUCTION, USE OR DISCLOSURE TO THIRD PARTIES WITHOUT EXPRESS AUTHORITY IS STRICTLY FORBIDDEN.

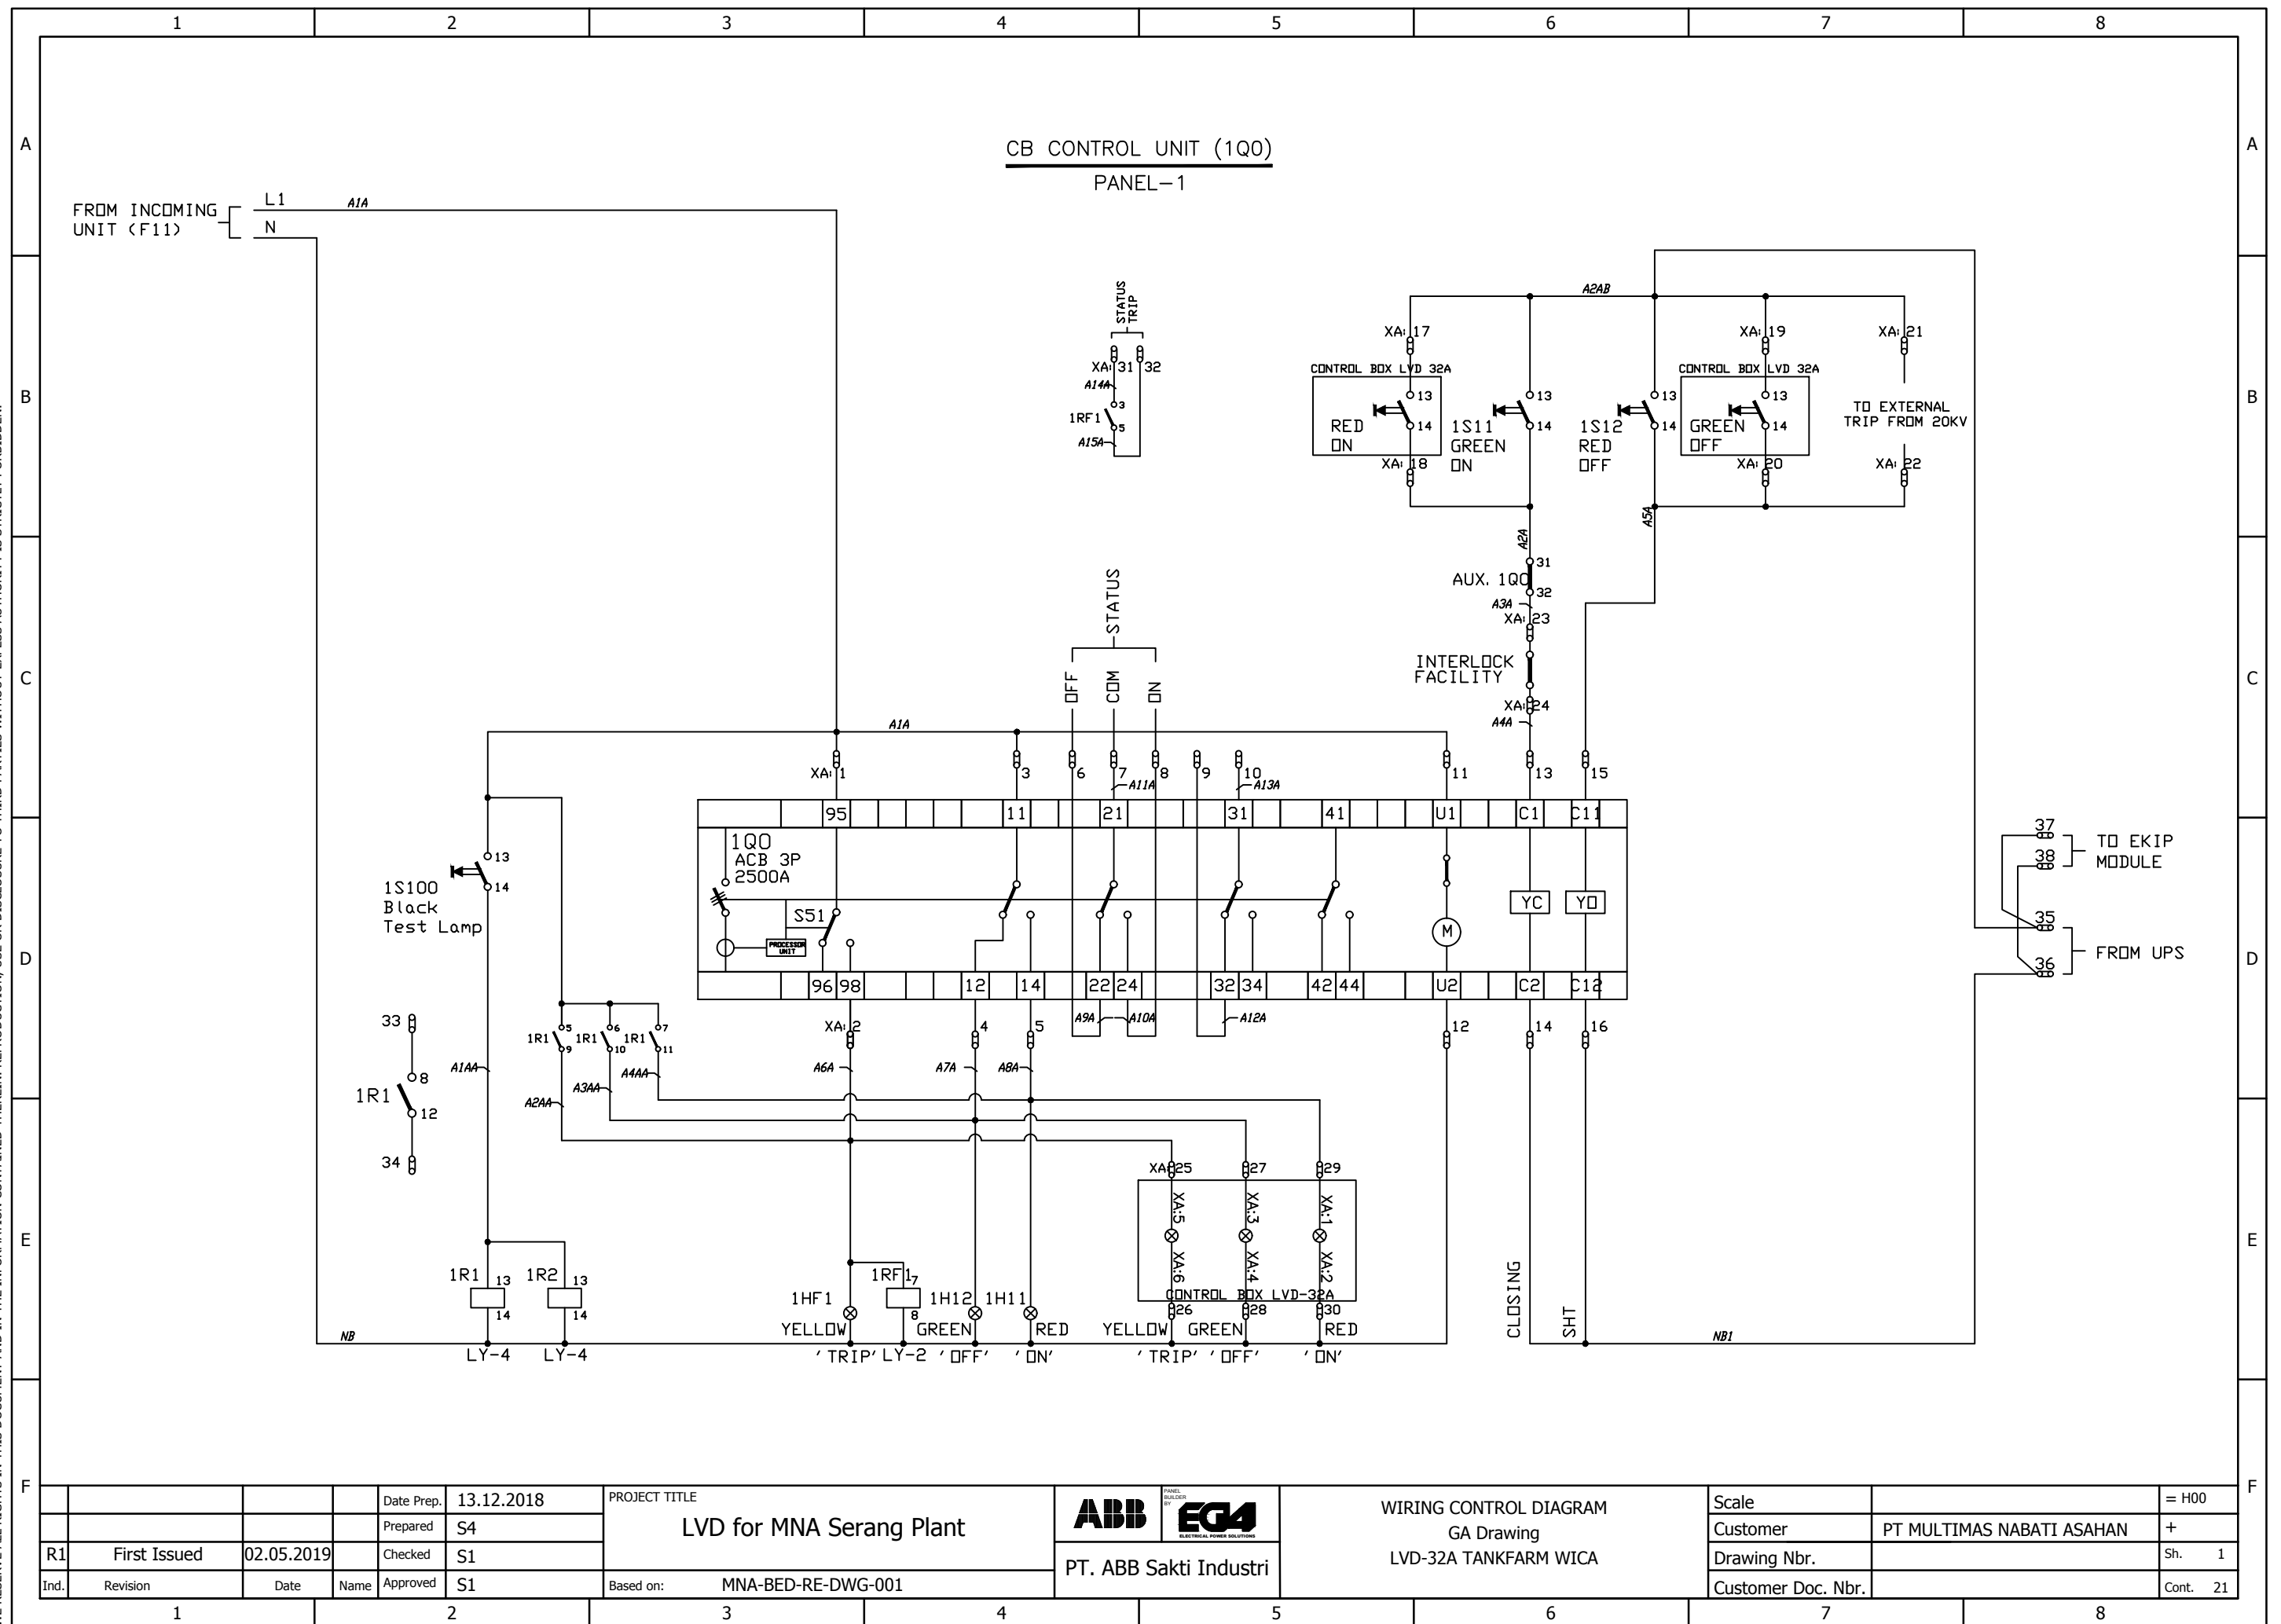


WE RESERVE ALL RIGHTS IN THIS DOCUMENT AND IN THE INFORMATION CONTAINED THEREIN. REPRODUCTION, USE OR DISCLOSURE TO THIRD PARTIES WITHOUT EXPRESS AUTHORITY IS STRICTLY FORBIDDEN.

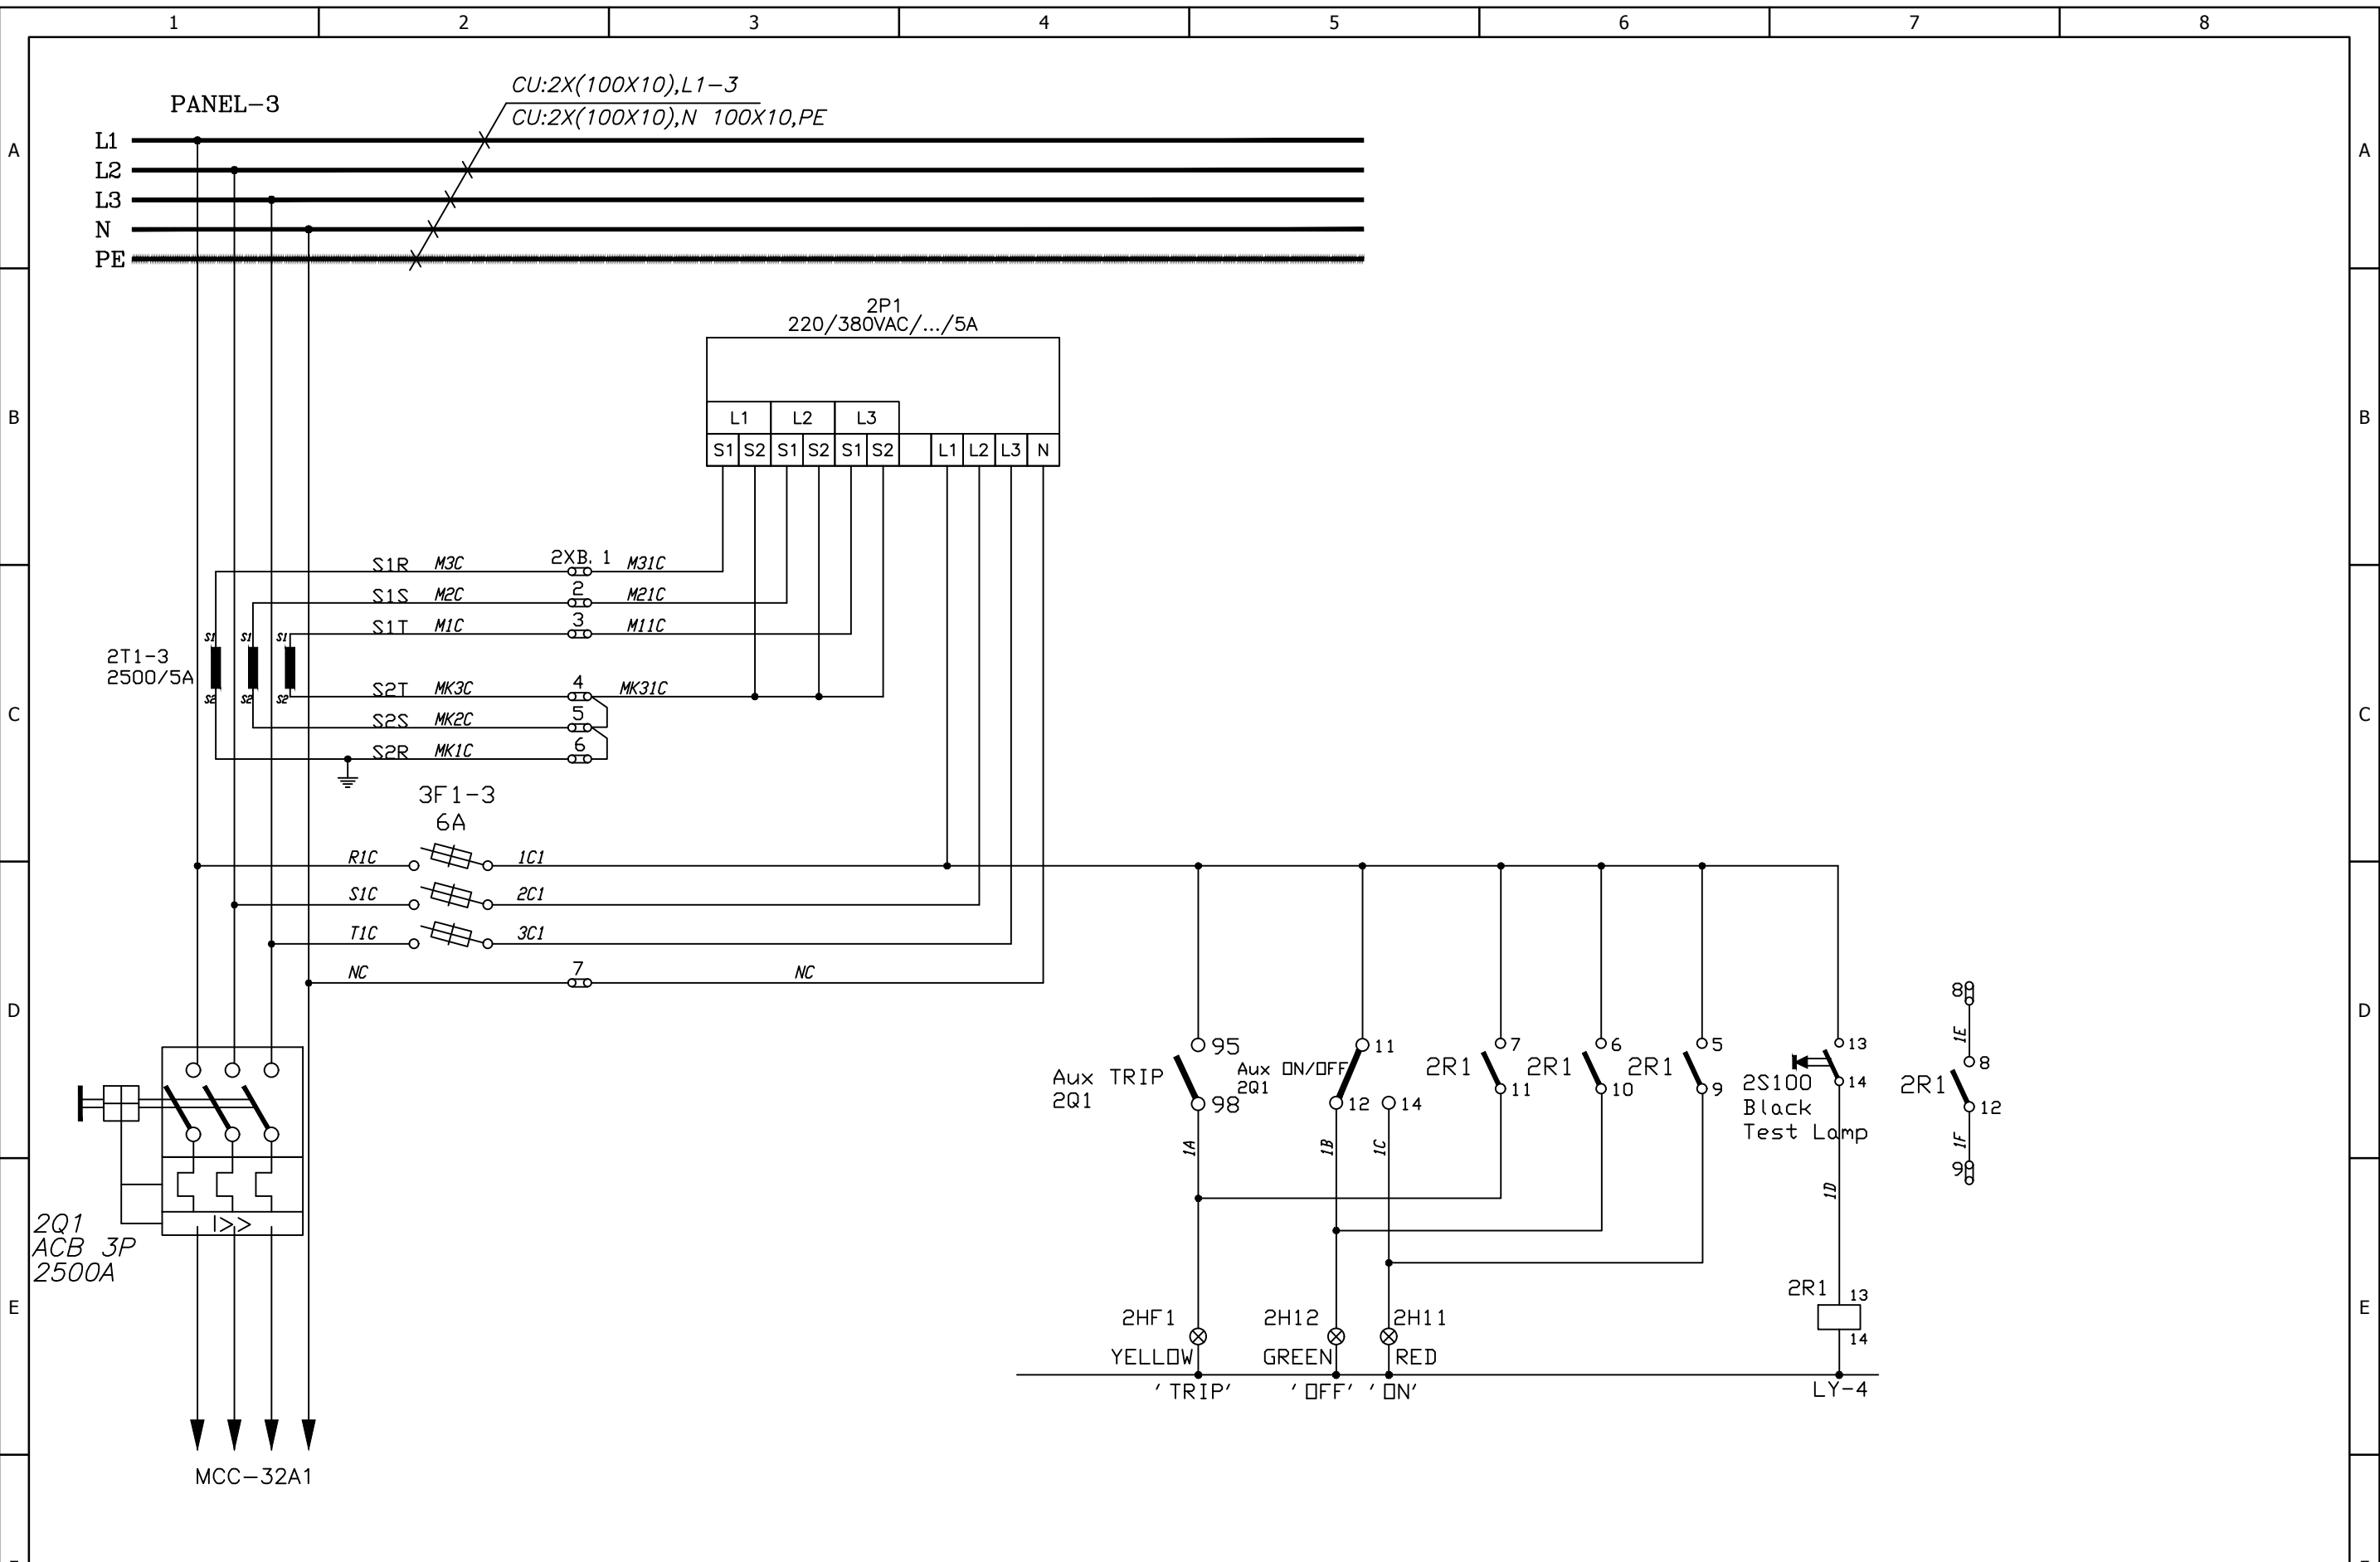


R1		First Issued	02.05.2019	Checked	S1	PROJECT TITLE LVD for MNA Serang Plant Based on: MNA-BED-RE-DWG-001	ABB PANEL BUILDING BY EG4 ELECTRICAL POWER SOLUTIONS PT. ABB Sakti Industri	WIRING CONTROL DIAGRAM GA Drawing LVD-32A TANKFARM WICA	Scale	= H00
Ind.		Revision	Date	Name	Approved				Customer	PT MULTIMAS NABATI ASAHAN
									Drawing Nbr.	Sh. 1
									Customer Doc. Nbr.	Cont. 21

WE RESERVE ALL RIGHTS IN THIS DOCUMENT AND IN THE INFORMATION CONTAINED THEREIN. REPRODUCTION, USE OR DISCLOSURE TO THIRD PARTIES WITHOUT EXPRESS AUTHORITY IS STRICTLY FORBIDDEN.

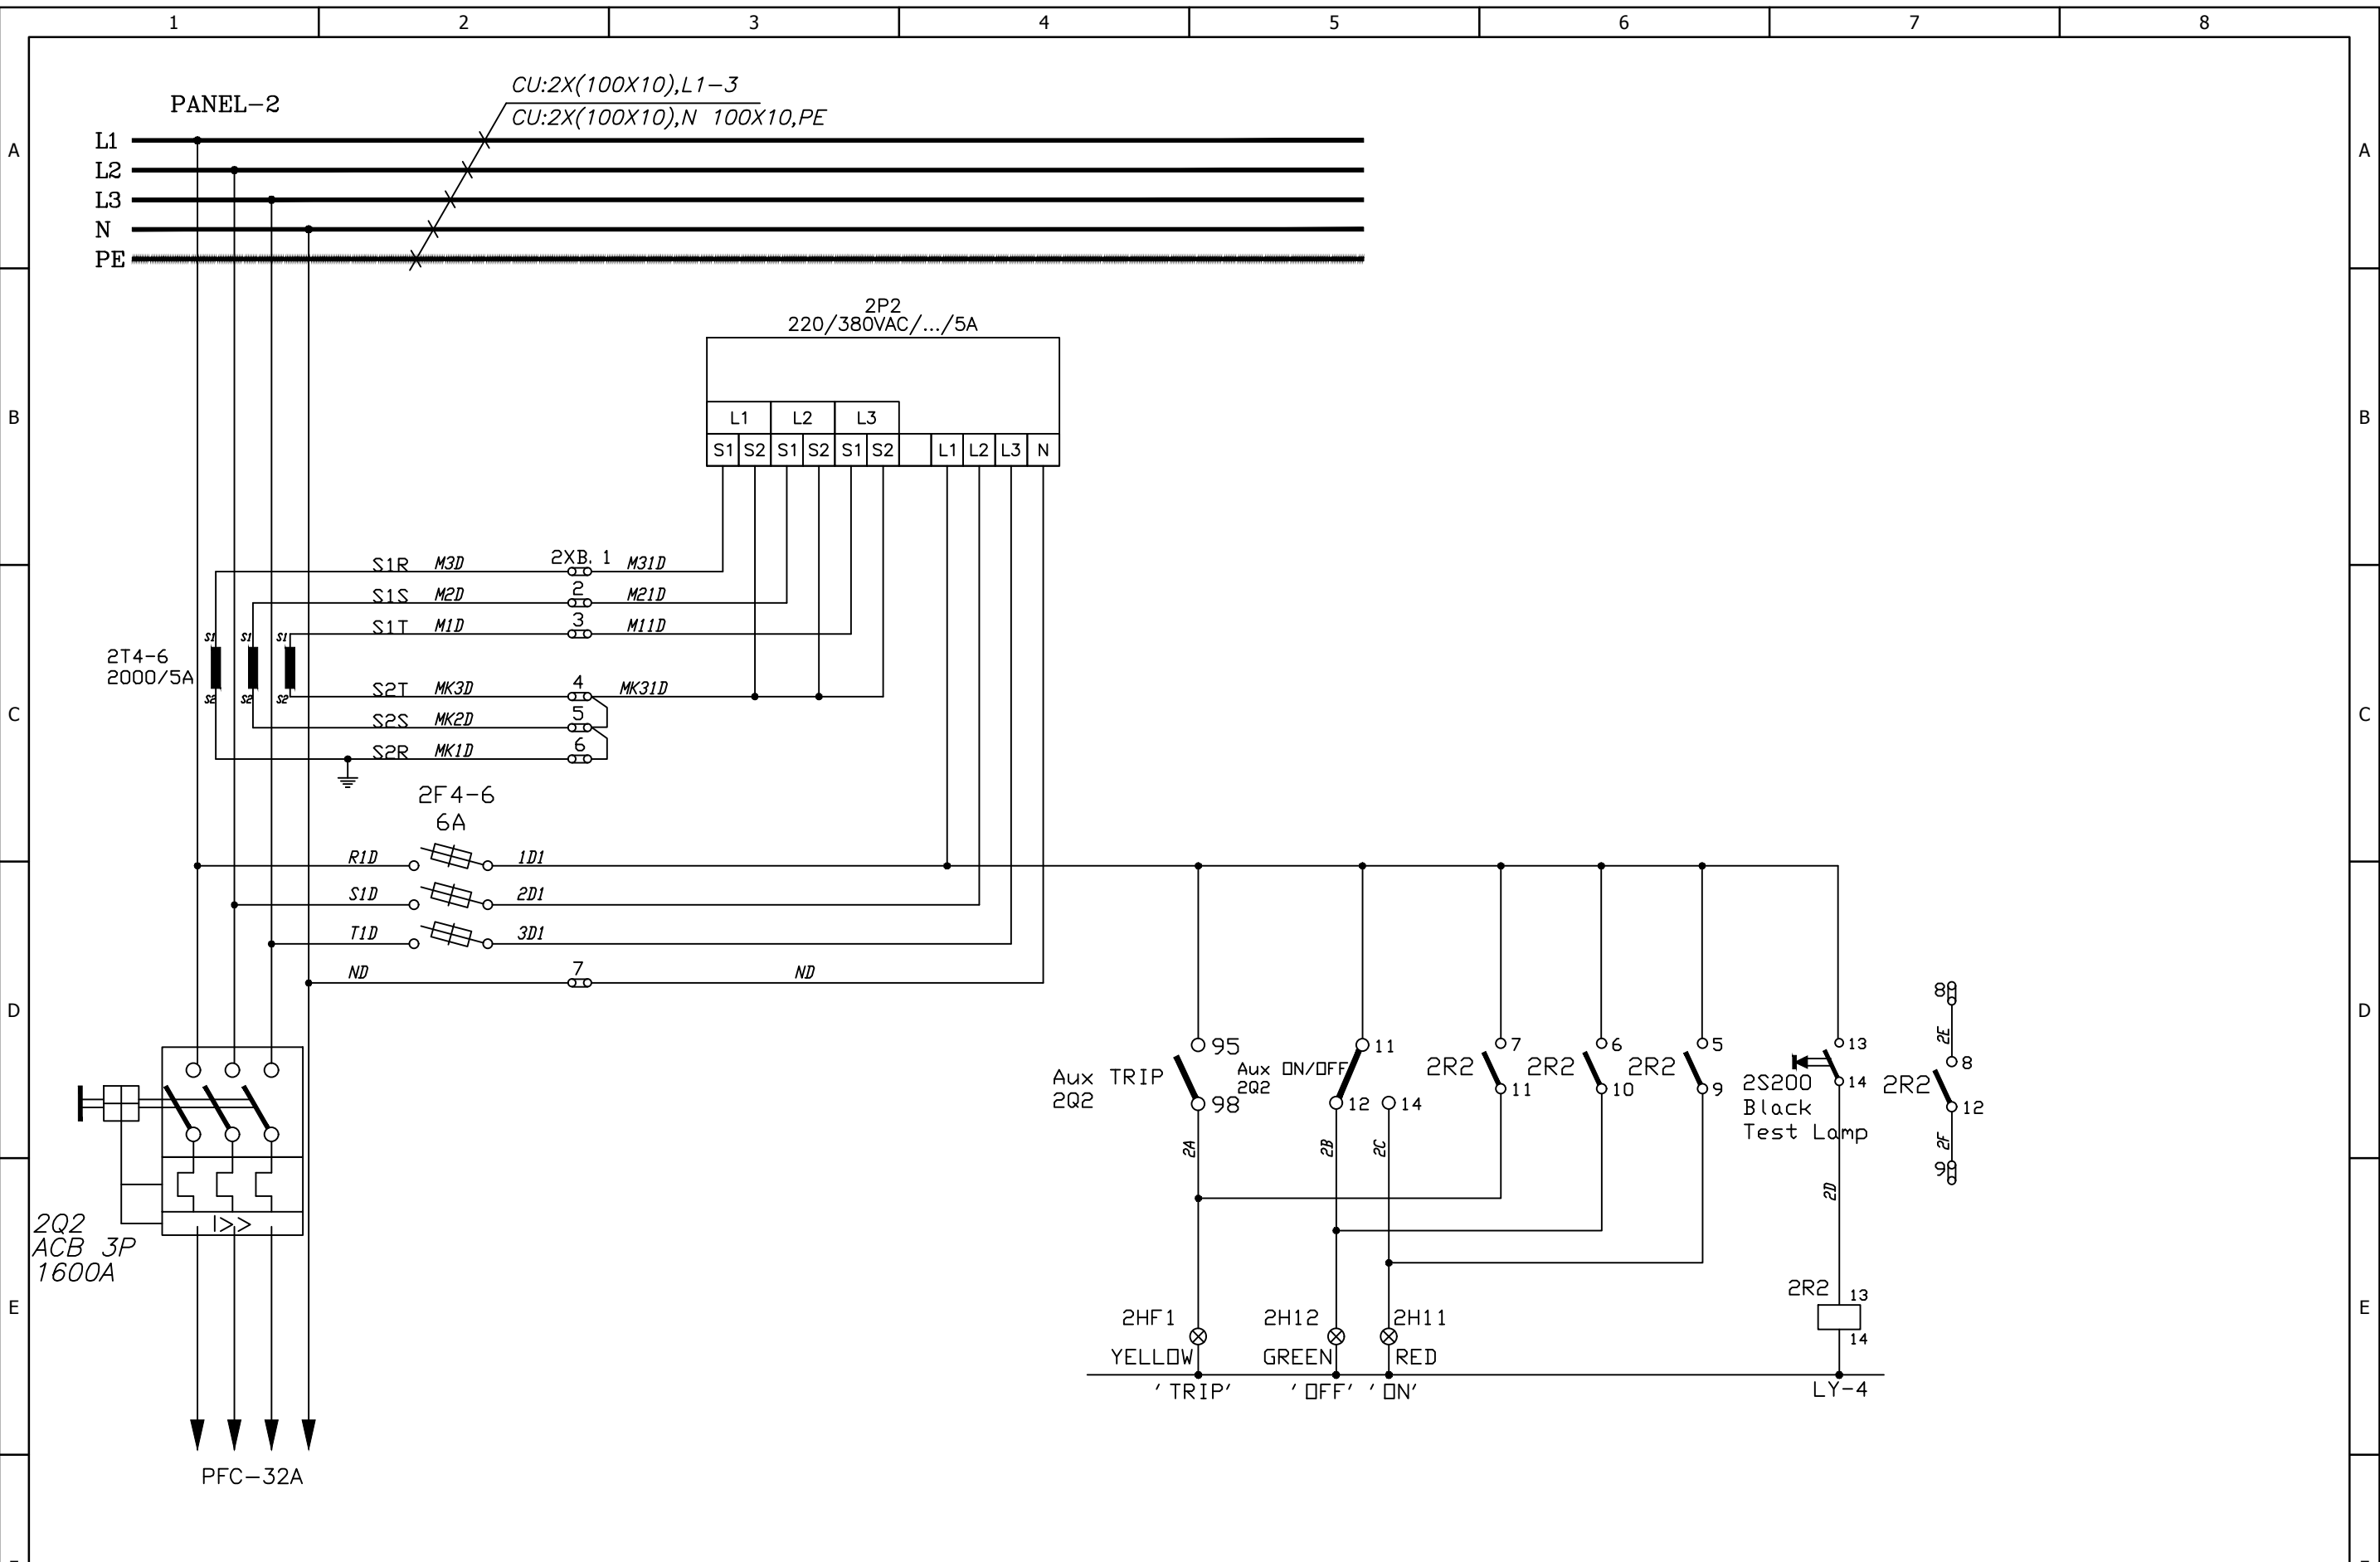


R1		First Issued	02.05.2019	Checked	S1	PROJECT TITLE LVD for MNA Serang Plant Based on: MNA-BED-RE-DWG-001	ABB EG4 PT. ABB Sakti Industri	WIRING CONTROL DIAGRAM GA Drawing LVD-32A TANKFARM WICA	Scale	= H00
Ind.		Revision	Date	Name	Approved				Customer	PT MULTIMAS NABATI ASAHAN
									Drawing Nbr.	Sh. 1
									Customer Doc. Nbr.	Cont. 21


WE RESERVE ALL RIGHTS IN THIS DOCUMENT AND IN THE INFORMATION CONTAINED THEREIN. REPRODUCTION, USE OR DISCLOSURE TO THIRD PARTIES WITHOUT EXPRESS AUTHORITY IS STRICTLY FORBIDDEN.

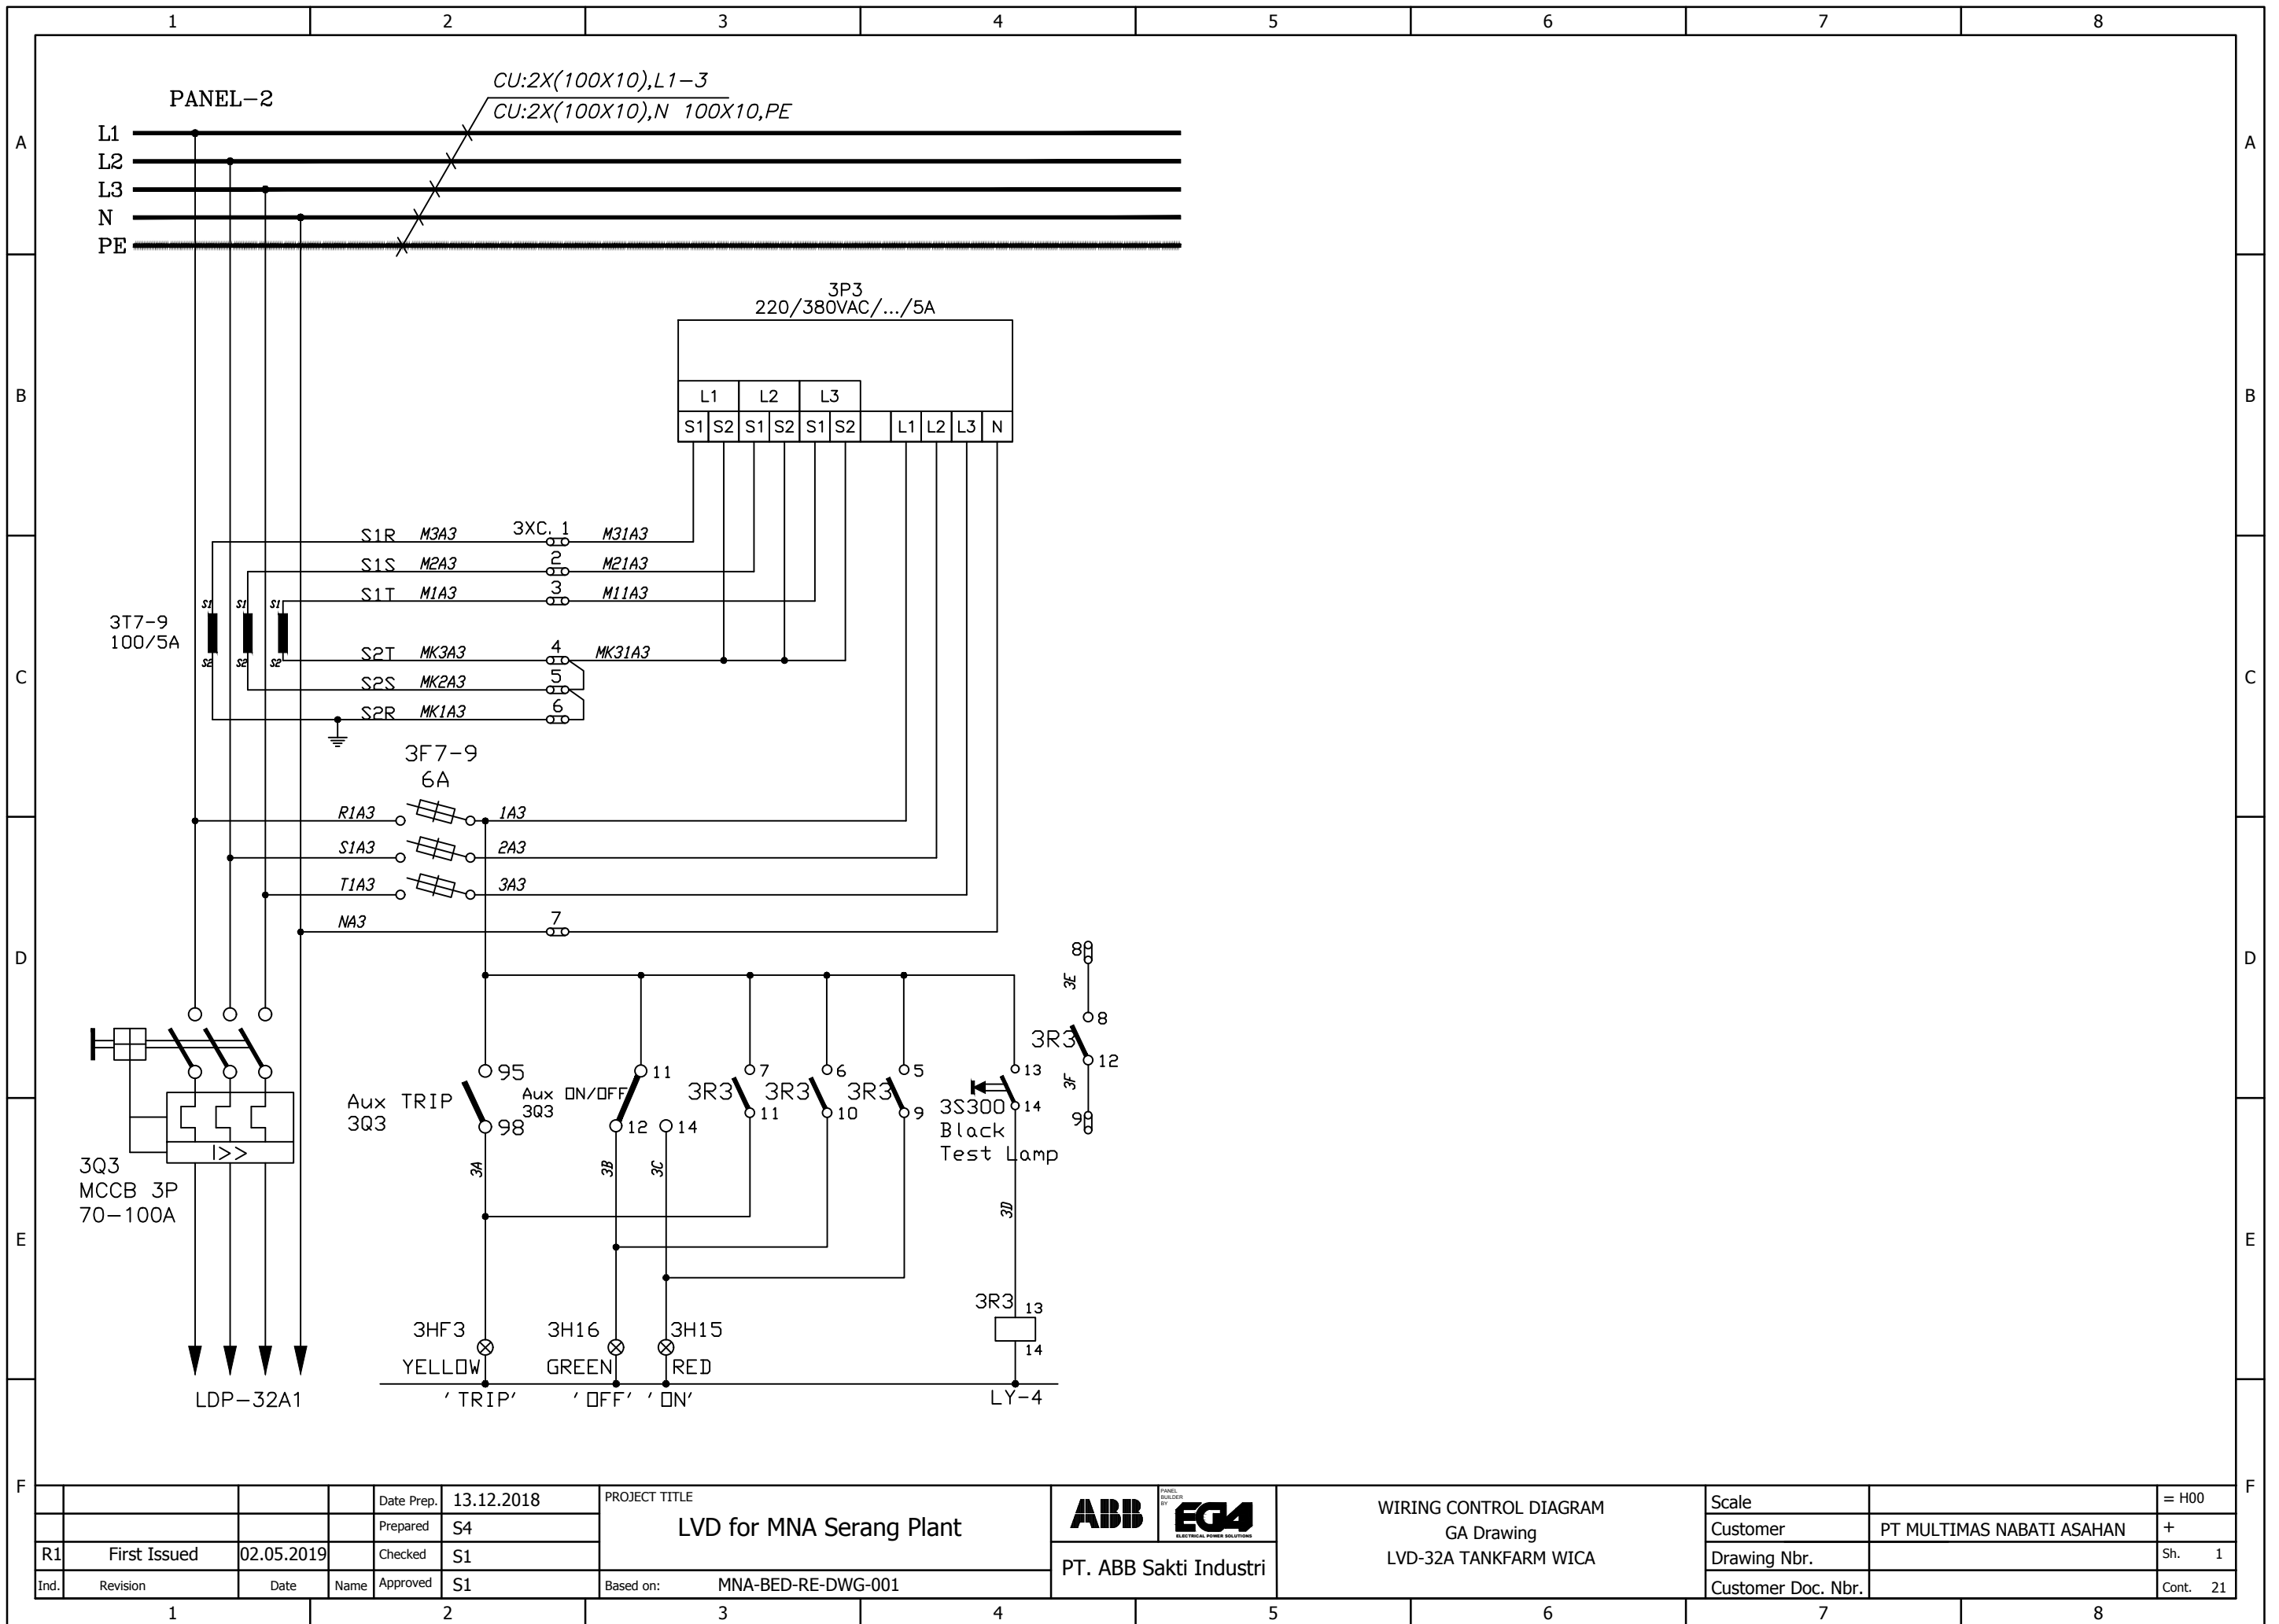


WE RESERVE ALL RIGHTS IN THIS DOCUMENT AND IN THE INFORMATION CONTAINED THEREIN. REPRODUCTION, USE OR DISCLOSURE TO THIRD PARTIES WITHOUT EXPRESS AUTHORITY IS STRICTLY FORBIDDEN.

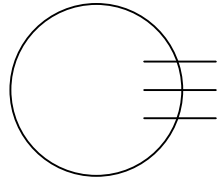


CT

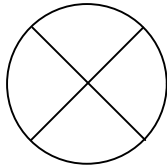


PILOT LAMP

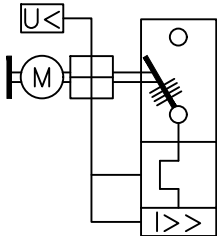

ACB

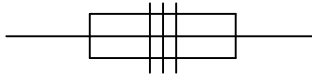

FUSE

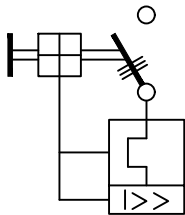

MCCB



DIGITAL POWER METER

				Date Prep.	13.12.2018	PROJECT TITLE LVD for MNA Serang Plant	ABB PANEL BUILDER BY EG4 ELECTRICAL POWER SOLUTIONS PT. ABB Sakti Industri	LEGEND GA Drawing LVD-32A TANKFARM WICA	Scale		= H00
				Prepared	S4				Customer	PT MULTIMAS NABATI ASAHAN	+
R1	First Issued	02.05.2019		Checked	S1				Drawing Nbr.		Sh. 1
Ind.	Revision	Date	Name	Approved	S1	Based on:	MNA-BED-RE-DWG-001		Customer Doc. Nbr.		Cont. 21

WE RESERVE ALL RIGHTS IN THIS DOCUMENT AND IN THE INFORMATION CONTAINED THEREIN. REPRODUCTION, USE OR DISCLOSURE TO THIRD PARTIES WITHOUT EXPRESS AUTHORITY IS STRICTLY FORBIDDEN.

1		2		3		4		5		6		7		8	
A	N O	DESCRIPTION			TECHNICAL DATA			QTY	DESIGNATION						A
		INCOMING													
B	1	Fuse Carrier 6A			AXLE/Setara			7	1F11,1F1-6						B
	2	Pilot Lamp (LED) 220Vac/50Hz, Red			AXLE/Setara			2	1H1,12						
	3	Pilot Lamp (LED) 220Vac/50Hz, Yellow			AXLE/Setara			2	1H2,HF1						
	4	Pilot Lamp (LED) 220Vac/50Hz, Green			AXLE/Setara			2	1H3,H11						
	5	DIGITAL POWER METER (*)			ABB, M2M ETHERNET			1	1P1						
	6	CT 2500/5A CL.0.5 40VA			Howig, HG 120-2500			4	1T1-4						
	7	ACB 3P 2500A, 66KA, DO, Ekip Touch LSIG (*)			ABB, E2.2N25 D/O			1	1Q0						
C	8	+ Shunt Trip Release (Y0) (*)			ABB, Y0			1	-						C
	9	+ Motor (M) + Closing Release (YC) For E2.2-E6.2 (*)			ABB, M+YC			1	-						
	10	+ Padlocks For E2.2-E6.2 (*)			ABB,			1	-						
	11	+ Ekip Com Protocol IEC 61850 (*)			ABB,			1	-						
	12	Push Button On, 1NO, Green			Ega			1	S11						
	13	Push Button Off, 1NO, Red			Ega			1	S12						
	14	Control Relay 220Vac			Omron, LY-2			1	1RF1						
D	15	Control Relay 220Vac			Omron, LY-4			2	1R1-2						D
	16	Push Button On, 1NO, Black			Ega			1	1S100						
	17														
	18	OUTGOING													
	19	Fuse Carrier 6A			AXLE			15	2F1-6 ; 3F1-9						
	20	Pilot Lamp (LED) 220Vac/50Hz, Red			AXLE			5	2H11,13 ; 3H11,13,15						
	21	Pilot Lamp (LED) 220Vac/50Hz, Yellow			AXLE			5	2HF1-2 ; 3HF1-3						
E	22	Pilot Lamp (LED) 220Vac/50Hz, Green			AXLE			5	2H12,14 ; 3H12,14,16						E
	23	DIGITAL POWER METER (*)			ABB, M2M ETHERNET			5	2P1-2 ; 3P1-3						
	24	CT 2500/5A CL.0.5 40VA			Howig, HG 120-2500			3	2T1-3						
	25	CT 2000/5A CL.0.5 20VA			Howig, HG 82-2000			3	2T4-6						
	26														
F					Date Prep.	13.12.2018	PROJECT TITLE LVD for MNA Serang Plant		ABB PANEL BUILDER BY EG4 ELECTRICAL POWER SOLUTIONS	COMPONENT LIST GA Drawing LVD-32A TANKFARM WICA		Scale		= H00	F
					Prepared	S4						Customer	PT MULTIMAS NABATI ASAHAN	+	
	R1	First Issued	02.05.2019		Checked	S1						Drawing Nbr.		Sh. 1	
	Ind.	Revision		Date	Name	Approved	S1	Based on:	MNA-BED-RE-DWG-001	Customer Doc. Nbr.		Cont. 21			
	1		2		3		4		5		6		7		

WE RESERVE ALL RIGHTS IN THIS DOCUMENT AND IN THE INFORMATION CONTAINED THEREIN. REPRODUCTION, USE OR DISCLOSURE TO THIRD PARTIES WITHOUT EXPRESS AUTHORITY IS STRICTLY FORBIDDEN.

1		2		3		4		5		6		7		8		
A	N O	DESCRIPTION				TECHNICAL DATA		QTY	DESIGNATION						A	
		OUTGOING														
B	1	CT 800/5A CL.1 10VA				Howig, HG 50I-800		3	3T1-3						B	
	2	CT 400/5A CL.1 5VA				Howig, HG 40I-400		3	3T4-6							
	3	CT 100/5A CL.1 2.5VA				Howig, HG 30I-100		3	3T7-9							
	4	ACB 3P 2500A, 66KA, FT, Ekip Dip LI (*)				ABB, E2.2N25 F/T		1	2Q1							
	5	+ Padlocks For E2.2 (*)				ABB,		1	-							
	6	ACB 3P 1600A, 66KA, FT, Ekip Dip LI (*)				ABB, E1.2N16 F/T		1	2Q2							
	7	+ Padlocks For E1.2 (*)				ABB,		1	-							
C	8	MCCB 3P 252-630A, 70KA (*)				ABB, T5H PR221DS-LS/I-630		1	3Q1						C	
	9	+ Auxiliary Contact For T5-T6 (*)				ABB, Aux-C 3Q 1SY		1	-							
	10	+ Extended Rotary Handles For T5 (*)				ABB, RHE		1	-							
	11	MCCB 3P 160-400A, 70KA (*)				ABB, T5H PR221DS-LS/I-400		1	3Q2							
	12	+ Auxiliary Contact For T5-T6 (*)				ABB, Aux-C 3Q 1SY		1	-							
	13	+ Extended Rotary Handles For T5 (*)				ABB, RHE		1	-							
	14	MCCB 3P 70-100A, 70KA (*)				ABB, XT2H TMA-100		1	3Q4							
D	15	+ Auxiliary Contact For XT2/XT4 (*)				ABB, Aux-C 2Q 1SY		1	-						D	
	16	+ Extended Rotary Handles For XT2/XT4 (*)				ABB, RHE		1	-							
	17	Control Relay 220Vac				Omron, LY-4		5	2R1-2,3R1-3							
	18	Push Button Test Lamp , 1NO, Black				Ega		5	2S100-200 ; 3S100-300							
	19															
	20															
	21															
E	22														E	
	23															
	24															
	25															
	26															
F					Date Prep.	13.12.2018	PROJECT TITLE LVD for MNA Serang Plant		ABB PANEL BUILDER BY EG4 ELECTRICAL POWER SOLUTIONS PT. ABB Sakti Industri		COMPONENT LIST GA Drawing LVD-32A TANKFARM WICA		Scale		= H00	F
					Prepared	S4							Customer	PT MULTIMAS NABATI ASAHAN	+	
	R1	First Issued	02.05.2019		Checked	S1							Drawing Nbr.		Sh.	
	Ind.	Revision	Date	Name	Approved	S1	Based on:	MNA-BED-RE-DWG-001				Customer Doc. Nbr.		Cont.	21	
	1		2		3		4		5		6		7		8	