


WE RESERVE ALL RIGHTS IN THIS DOCUMENT AND IN THE INFORMATION CONTAINED THEREIN. REPRODUCTION, USE OR DISCLOSURE TO THIRD PARTIES WITHOUT EXPRESS AUTHORITY IS STRICTLY FORBIDDEN.

1		2		3		4		5		6		7		8	
A	
B	
C	
D	
E	
F	
UniSec Medium Voltage Switchgear PT MULTIMAS NABATI ASAHAN MVD-34 20kV FlourMill SCHEMATIC DIAGRAM SBC-W OUTGOING H03	
<table><tr><td colspan="2"></td><td colspan="2"></td><td colspan="2">Date Prep.</td><td colspan="2">15.11.2018</td><td colspan="2">PROJECT TITLE</td><td colspan="2">ABB</td><td colspan="2">EPMV</td><td colspan="2">COVER SHEET</td><td colspan="2">Scale</td><td colspan="2">NTS</td><td colspan="2">= H03</td></tr><tr><td colspan="2"></td><td colspan="2"></td><td colspan="2">Prepared</td><td colspan="2">YR</td><td colspan="2">MV Switchgear for MNA Serang Plant</td><td colspan="2"></td><td colspan="2"></td><td colspan="2">MVD-34 20kV FlourMill</td><td colspan="2">Customer</td><td colspan="2">PT WILMAR NABATI INDONESIA</td><td colspan="2">& 306</td></tr><tr><td colspan="2">00</td><td colspan="2">Issued for Approval</td><td colspan="2">22.02.19</td><td colspan="2">YR</td><td colspan="2">Checked</td><td colspan="2">AW</td><td colspan="2"></td><td colspan="2">SCHEMATIC DIAGRAM</td><td colspan="2">Drawing Nbr.</td><td colspan="2">18.042-WNI-306.02</td><td colspan="2">Sh. 1</td></tr><tr><td colspan="2">Ind.</td><td colspan="2">Revision</td><td colspan="2">Date</td><td colspan="2">Name</td><td colspan="2">Approved</td><td colspan="2">AI</td><td colspan="2">Based on:</td><td colspan="2">BE318043</td><td colspan="2">PT. ABB Sakti Industri</td><td colspan="2">SBC-W OUTGOING</td><td colspan="2">Customer Doc. Nbr.</td><td colspan="2">Cont. 27</td></tr></table>																				Date Prep.		15.11.2018		PROJECT TITLE		ABB		EPMV		COVER SHEET		Scale		NTS		= H03						Prepared		YR		MV Switchgear for MNA Serang Plant						MVD-34 20kV FlourMill		Customer		PT WILMAR NABATI INDONESIA		& 306		00		Issued for Approval		22.02.19		YR		Checked		AW				SCHEMATIC DIAGRAM		Drawing Nbr.		18.042-WNI-306.02		Sh. 1		Ind.		Revision		Date		Name		Approved		AI		Based on:		BE318043		PT. ABB Sakti Industri		SBC-W OUTGOING		Customer Doc. Nbr.		Cont. 27	
				Date Prep.		15.11.2018		PROJECT TITLE		ABB		EPMV		COVER SHEET		Scale		NTS		= H03	
				Prepared		YR		MV Switchgear for MNA Serang Plant						MVD-34 20kV FlourMill		Customer		PT WILMAR NABATI INDONESIA		& 306	
00		Issued for Approval		22.02.19		YR		Checked		AW				SCHEMATIC DIAGRAM		Drawing Nbr.		18.042-WNI-306.02		Sh. 1	
Ind.		Revision		Date		Name		Approved		AI		Based on:		BE318043		PT. ABB Sakti Industri		SBC-W OUTGOING		Customer Doc. Nbr.		Cont. 27	
1		2		3		4		5		6		7		8	


WE RESERVE ALL RIGHTS IN THIS DOCUMENT AND IN THE INFORMATION CONTAINED THEREIN. REPRODUCTION, USE OR DISCLOSURE TO THIRD PARTIES WITHOUT EXPRESS AUTHORITY IS STRICTLY FORBIDDEN.

	1	2	3	4	5	6	7	8					
A	SHEET INDEX								A				
	PAGE			PAGE NAME				REVISION					
	==MVD-34=H03&306/1			COVER SHEET				00					
	==MVD-34=H03&306/2			Index of Sheet				00					
	==MVD-34=H03&306/3			REFERENCE DESIGNATIONS				00					
	==MVD-34=H03&306/4			REFERENCE DESIGNATIONS				00					
	==MVD-34=H03&306/5			REFERENCE DESIGNATIONS				00					
	==MVD-34=H03&306/6			REFERENCE DESIGNATIONS				00					
	==MVD-34=H03&306/7			DISTRIBUTION OF AUXILIARY CIRCUITS				00					
	==MVD-34=H03&306/8			AUXILIARY SUPPLY CIRCUIT				00					
		==MVD-34=H03&306/9			CIRCUIT BREAKER CONTROL				00				
==MVD-34=H03&306/10			AUXILIARY MOTOR & RELAY				00						
==MVD-34=H03&306/11			DIGITAL INPUT/OUPUT RELAY				00						
==MVD-34=H03&306/12			SPARE CONTACT				00						
==MVD-34=H03&306/13			CURRENT TRANSFOMER				00						
==MVD-34=H03&306/14			VOLTAGE TRANSFORMER				00						
		==MVD-34=H03&306/15			LV DOOR LAYOUT				00				
	==MVD-34=H03&306/16			LV BOX LAYOUT				00					
	==MVD-34=H03&306/17			PART LIST				00					
	==MVD-34=H03&306/18			Terminal diagram ==MVD-34=H03+-XDA									
	==MVD-34=H03&306/19			Terminal diagram ==MVD-34=H03+-XDB1									
	==MVD-34=H03&306/20			Terminal diagram ==MVD-34=H03+-XDC1									
	==MVD-34=H03&306/21			Terminal diagram ==MVD-34=H03+-XDC2									
	==MVD-34=H03&306/22			Terminal diagram ==MVD-34=H03+-XDI									
	==MVD-34=H03&306/23			Terminal diagram ==MVD-34=H03+-XDI2									
	==MVD-34=H03&306/24			Terminal diagram ==MVD-34=H03+-XDI3									
	==MVD-34=H03&306/25			Terminal diagram ==MVD-34=H03+-XDI6									
	==MVD-34=H03&306/26			Terminal diagram ==MVD-34=H03+-XDV									
	==MVD-34=H03&306/27			Terminal diagram ==MVD-34=H03+-XDX									
										E			
								F					
				Date Prep.	15.11.2018	PROJECT TITLE		ABB	EPMV	Index of Sheet MVD-34 20kV FlourMill SCHEMATIC DIAGRAM SBC-W OUTGOING	Scale	NTS	= H03
				Prepared	YR	MV Switchgear for MNA Serang Plant					Customer	PT WILMAR NABATI INDONESIA	& 306
00	Issued for Approval	22.02.19	YR	Checked	AW			PT. ABB Sakti Industri			Drawing Nbr.	18.042-WNI-306.02	Sh. 2
Ind.	Revision	Date	Name	Approved	AI	Based on: BE318043				Customer Doc. Nbr.		Cont. 27	
	1	2	3	4	5	6	7	8					


WE RESERVE ALL RIGHTS IN THIS DOCUMENT AND IN THE INFORMATION CONTAINED THEREIN. REPRODUCTION, USE OR DISCLOSURE TO THIRD PARTIES WITHOUT EXPRESS AUTHORITY IS STRICTLY FORBIDDEN.

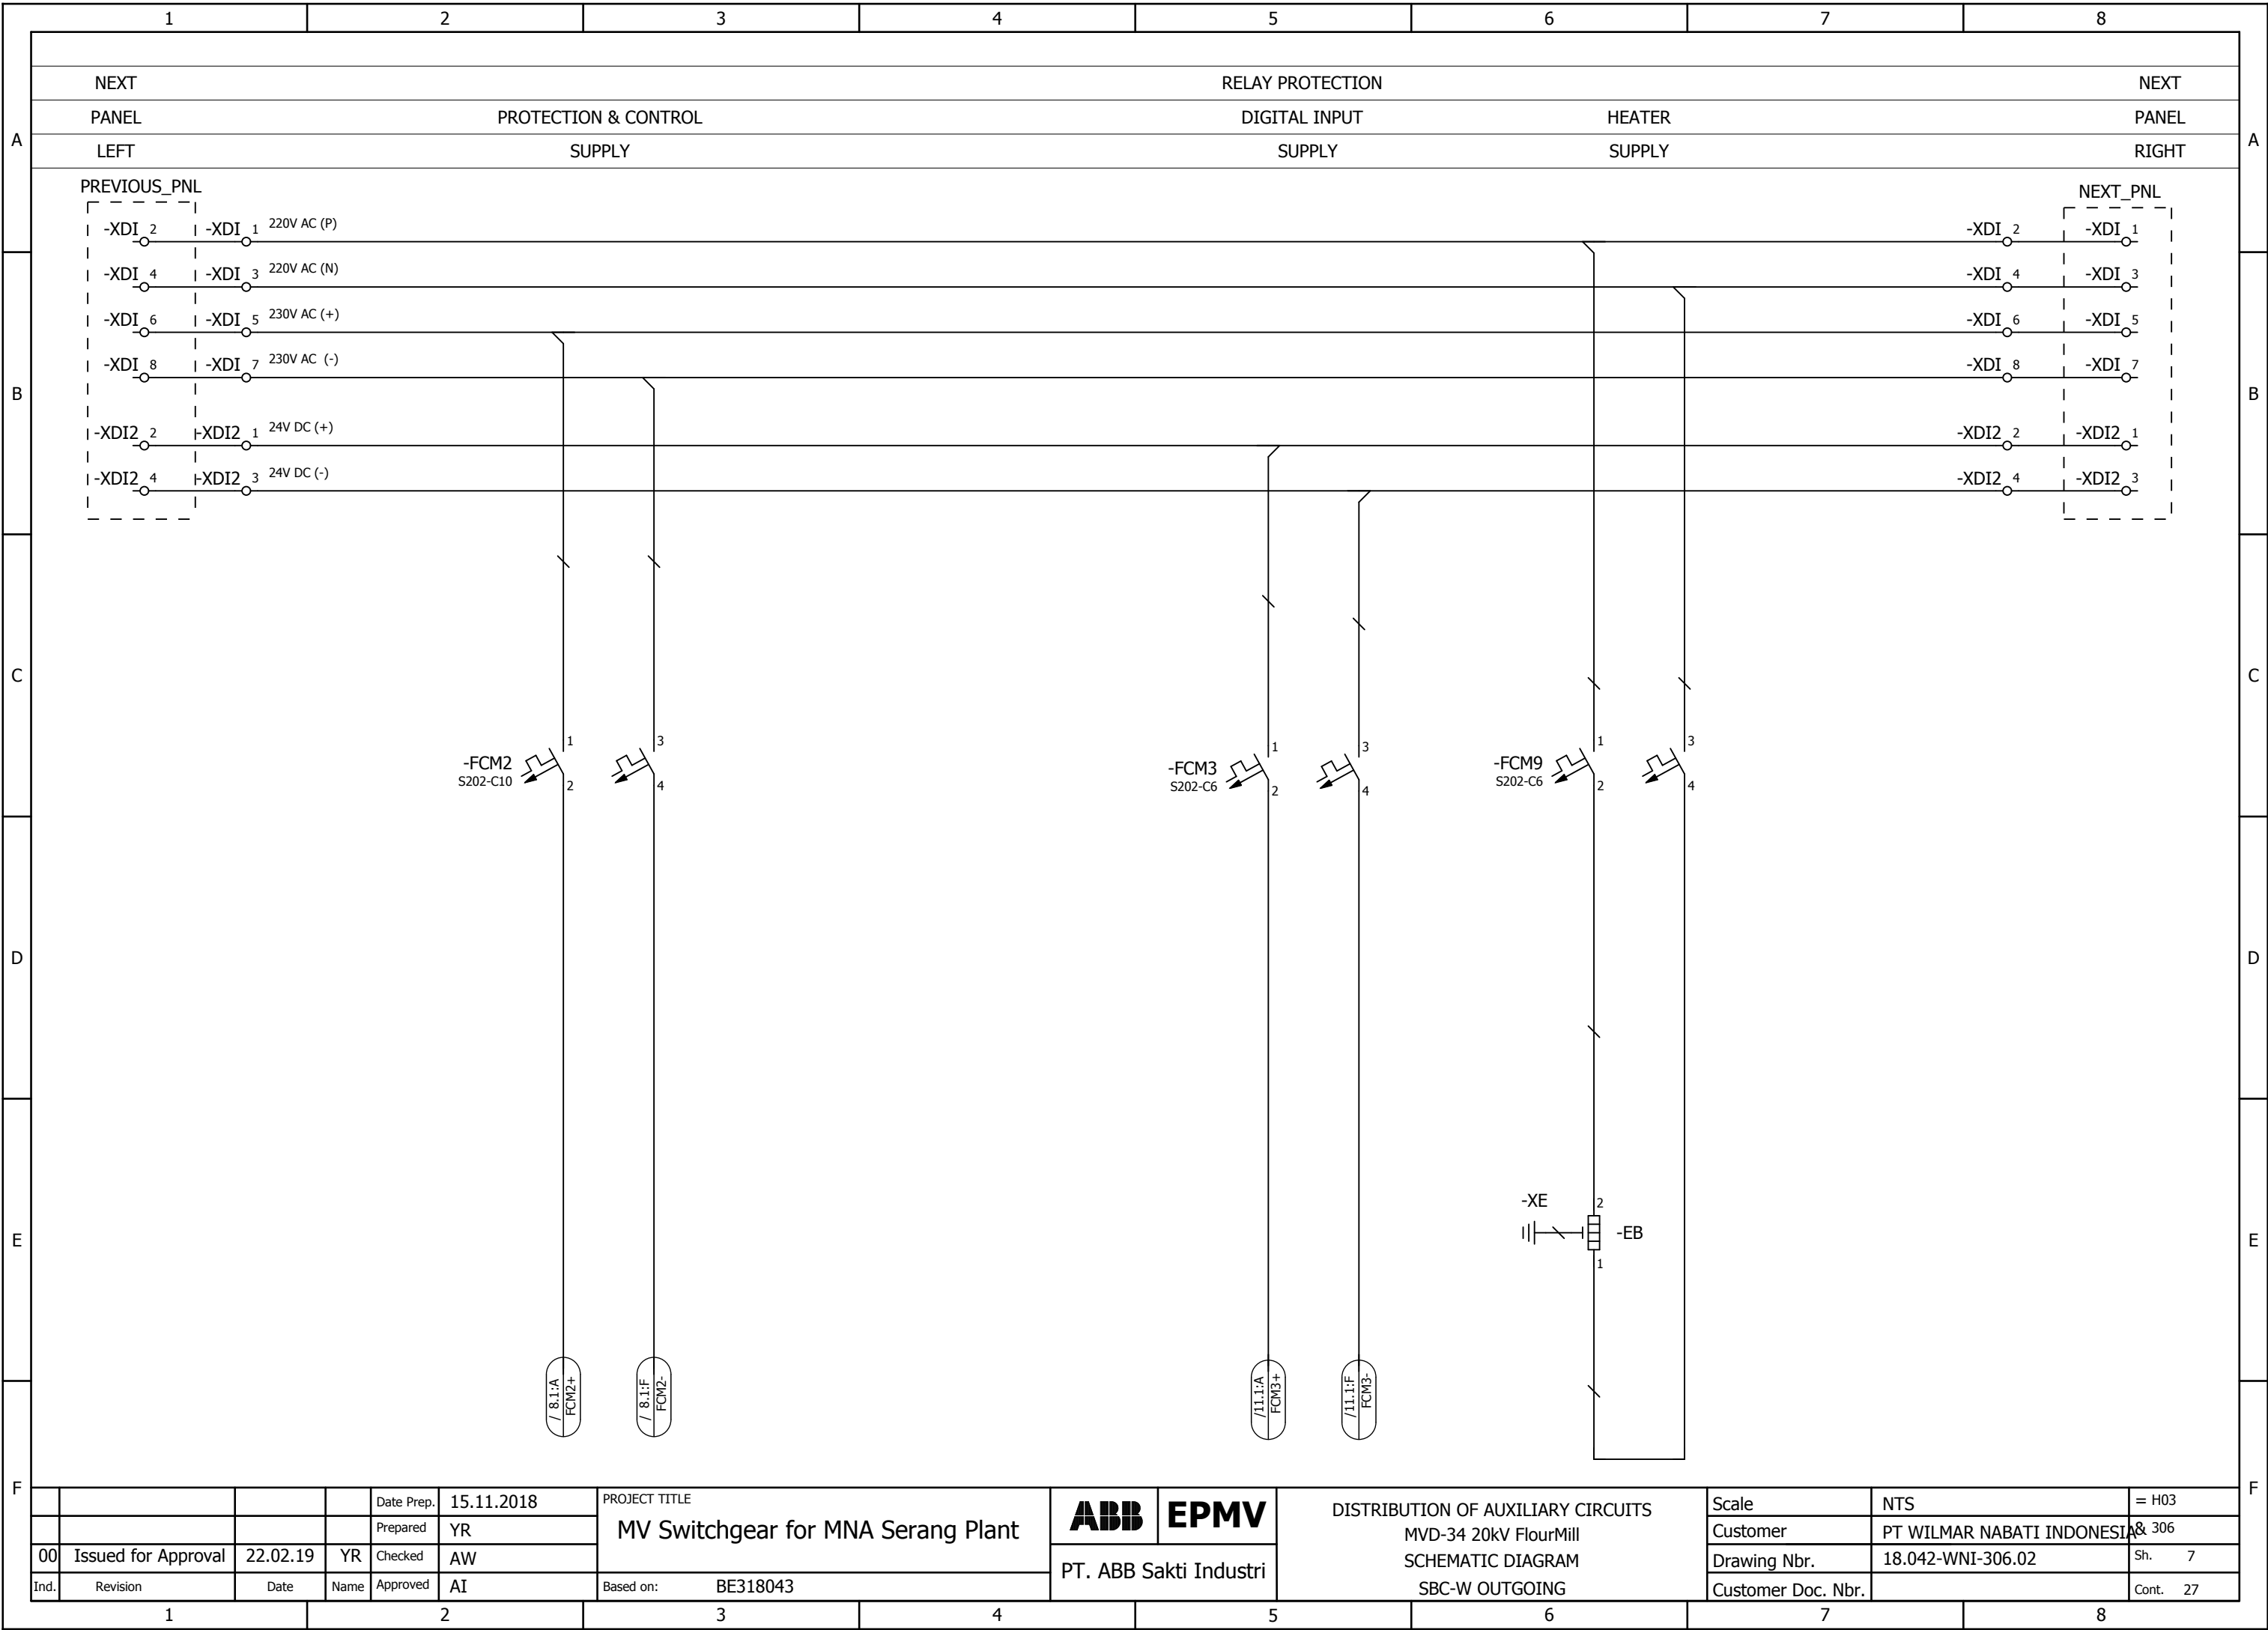


WE RESERVE ALL RIGHTS IN THIS DOCUMENT AND IN THE INFORMATION CONTAINED THEREIN. REPRODUCTION, USE OR DISCLOSURE TO THIRD PARTIES WITHOUT EXPRESS AUTHORITY IS STRICTLY FORBIDDEN.

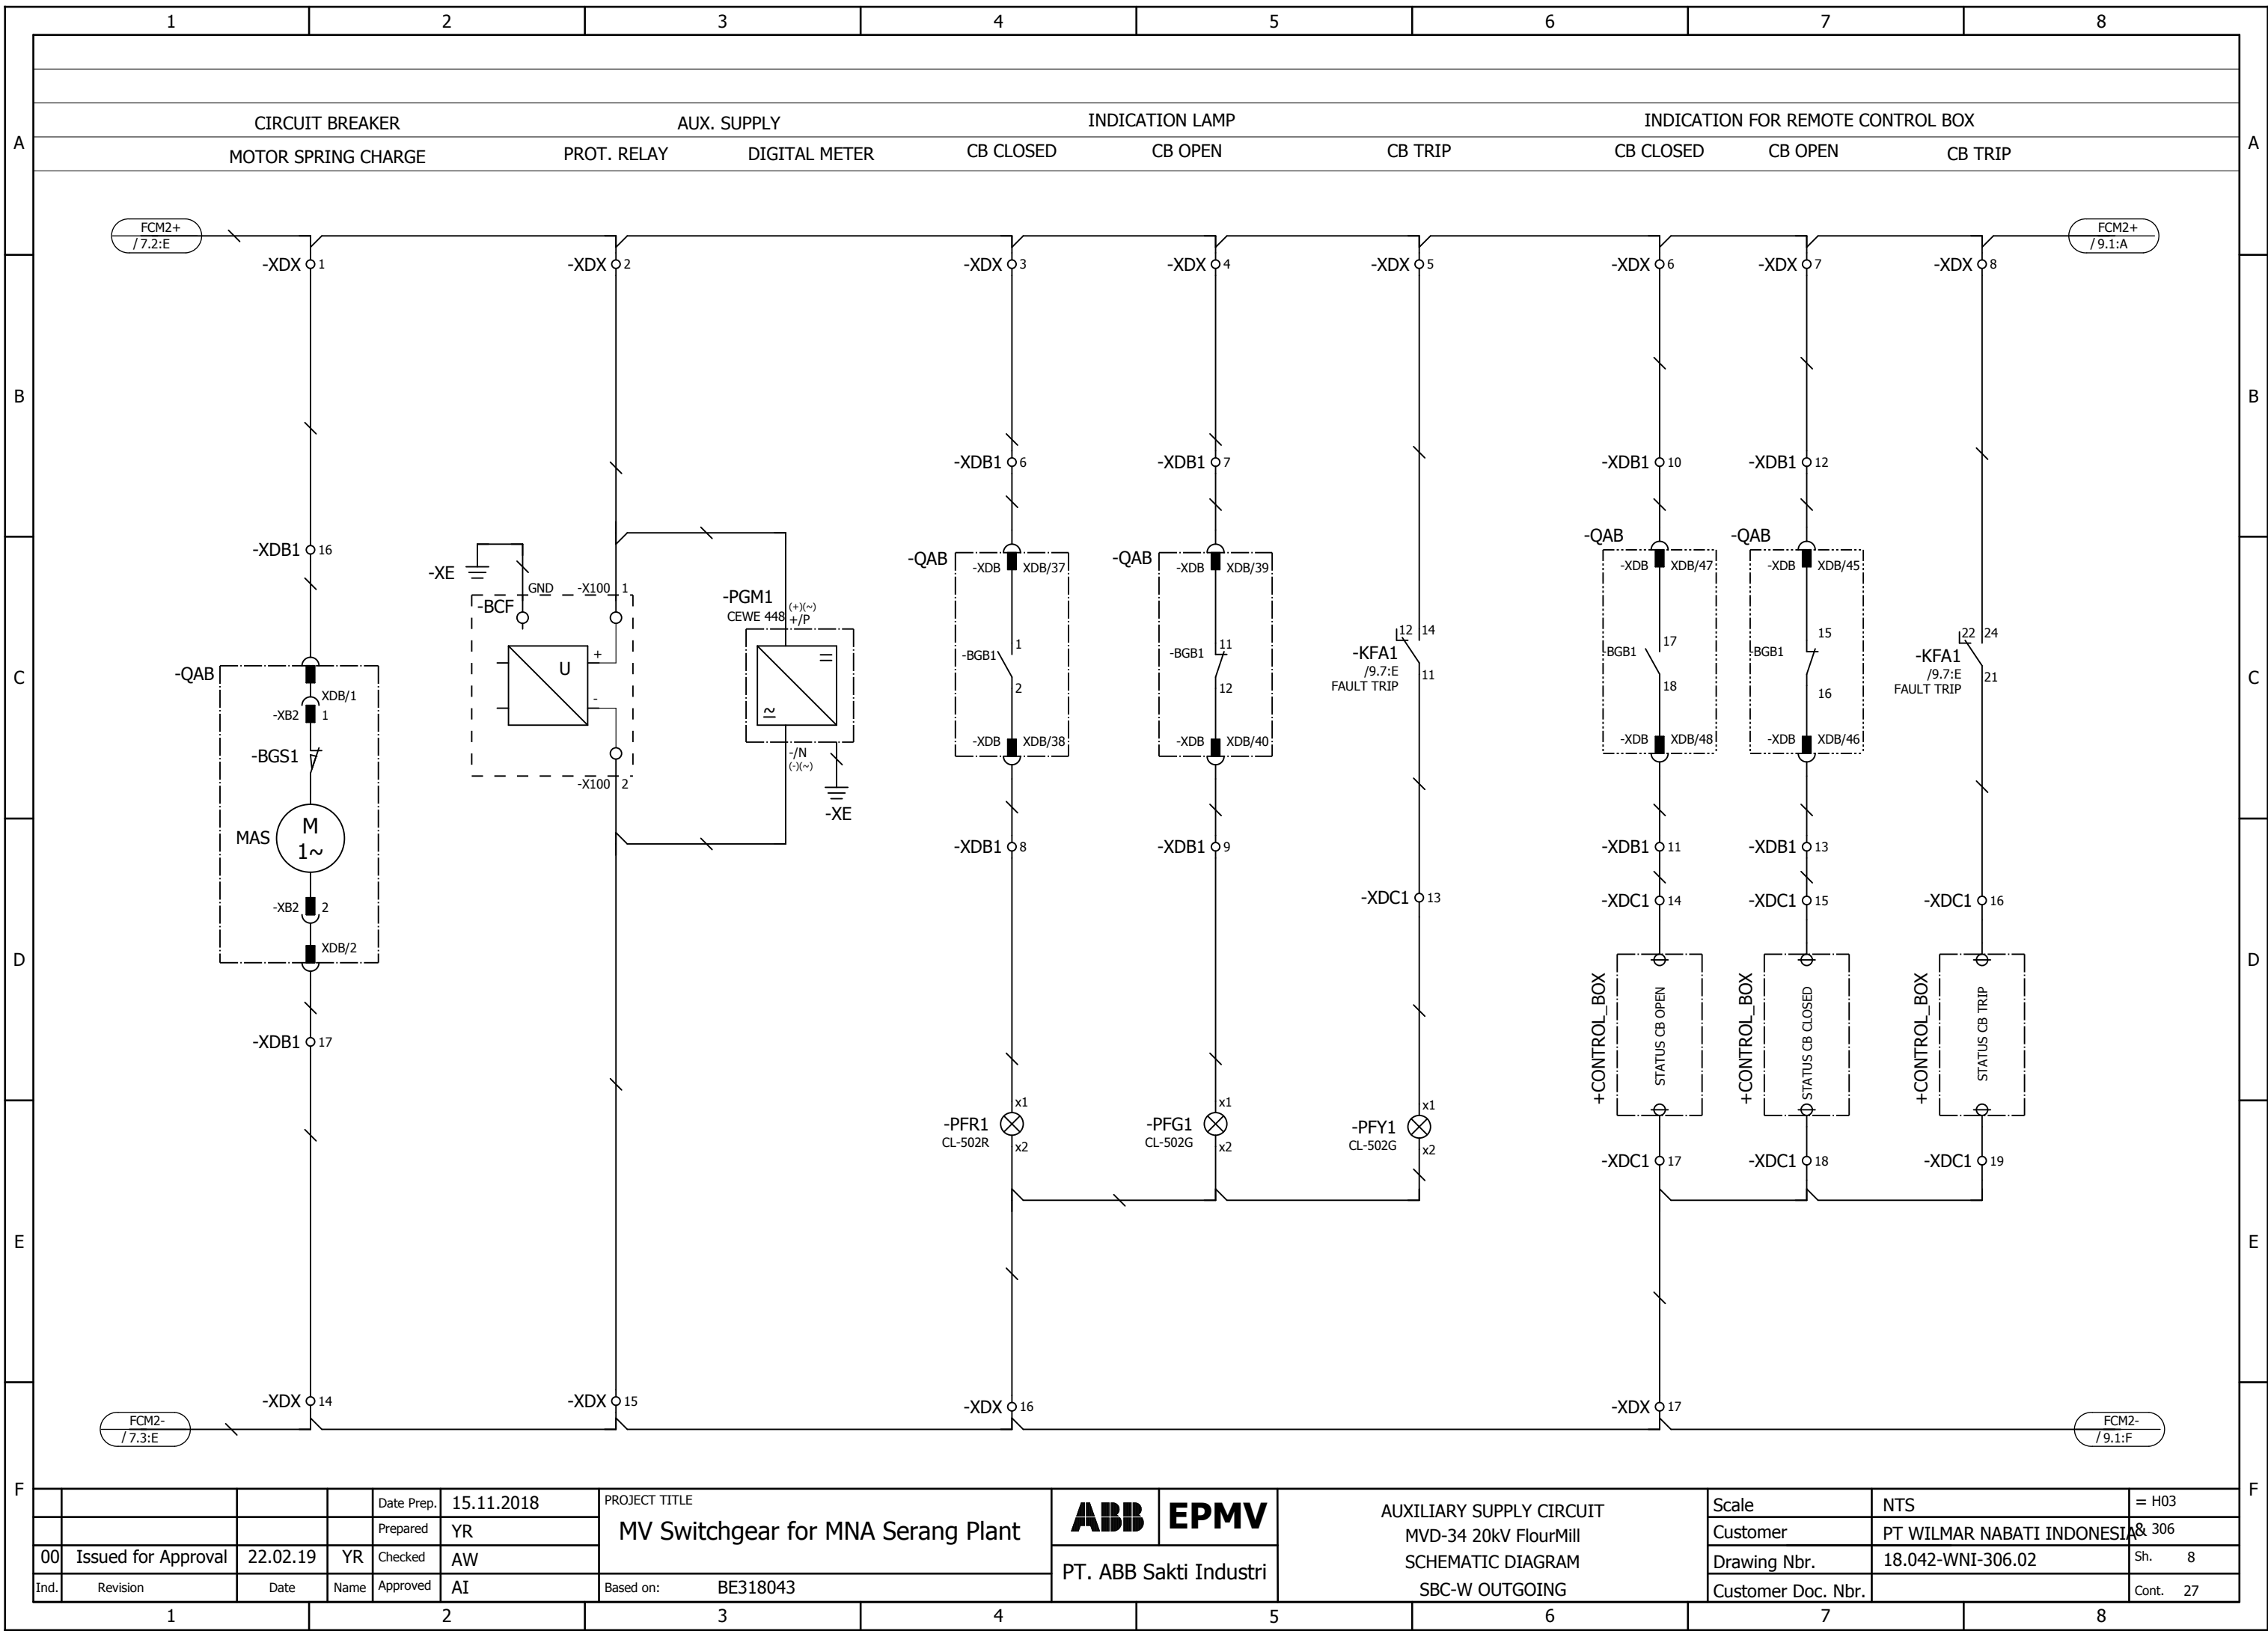


				Date Prep.	15.11.2018	PROJECT TITLE MV Switchgear for MNA Serang Plant	ABB	EPMV	AUXILIARY SUPPLY CIRCUIT MVD-34 20kV FlourMill SCHEMATIC DIAGRAM SBC-W OUTGOING	Scale	NTS	= H03
				Prepared	YR					Customer	PT WILMAR NABATI INDONESIA	& 306
00	Issued for Approval	22.02.19	YR	Checked	AW		Drawing Nbr.	18.042-WNI-306.02		Sh. 8		
Ind.	Revision	Date	Name	Approved	AI	Based on:	BE318043	PT. ABB Sakti Industri		Customer Doc. Nbr.		Cont. 27

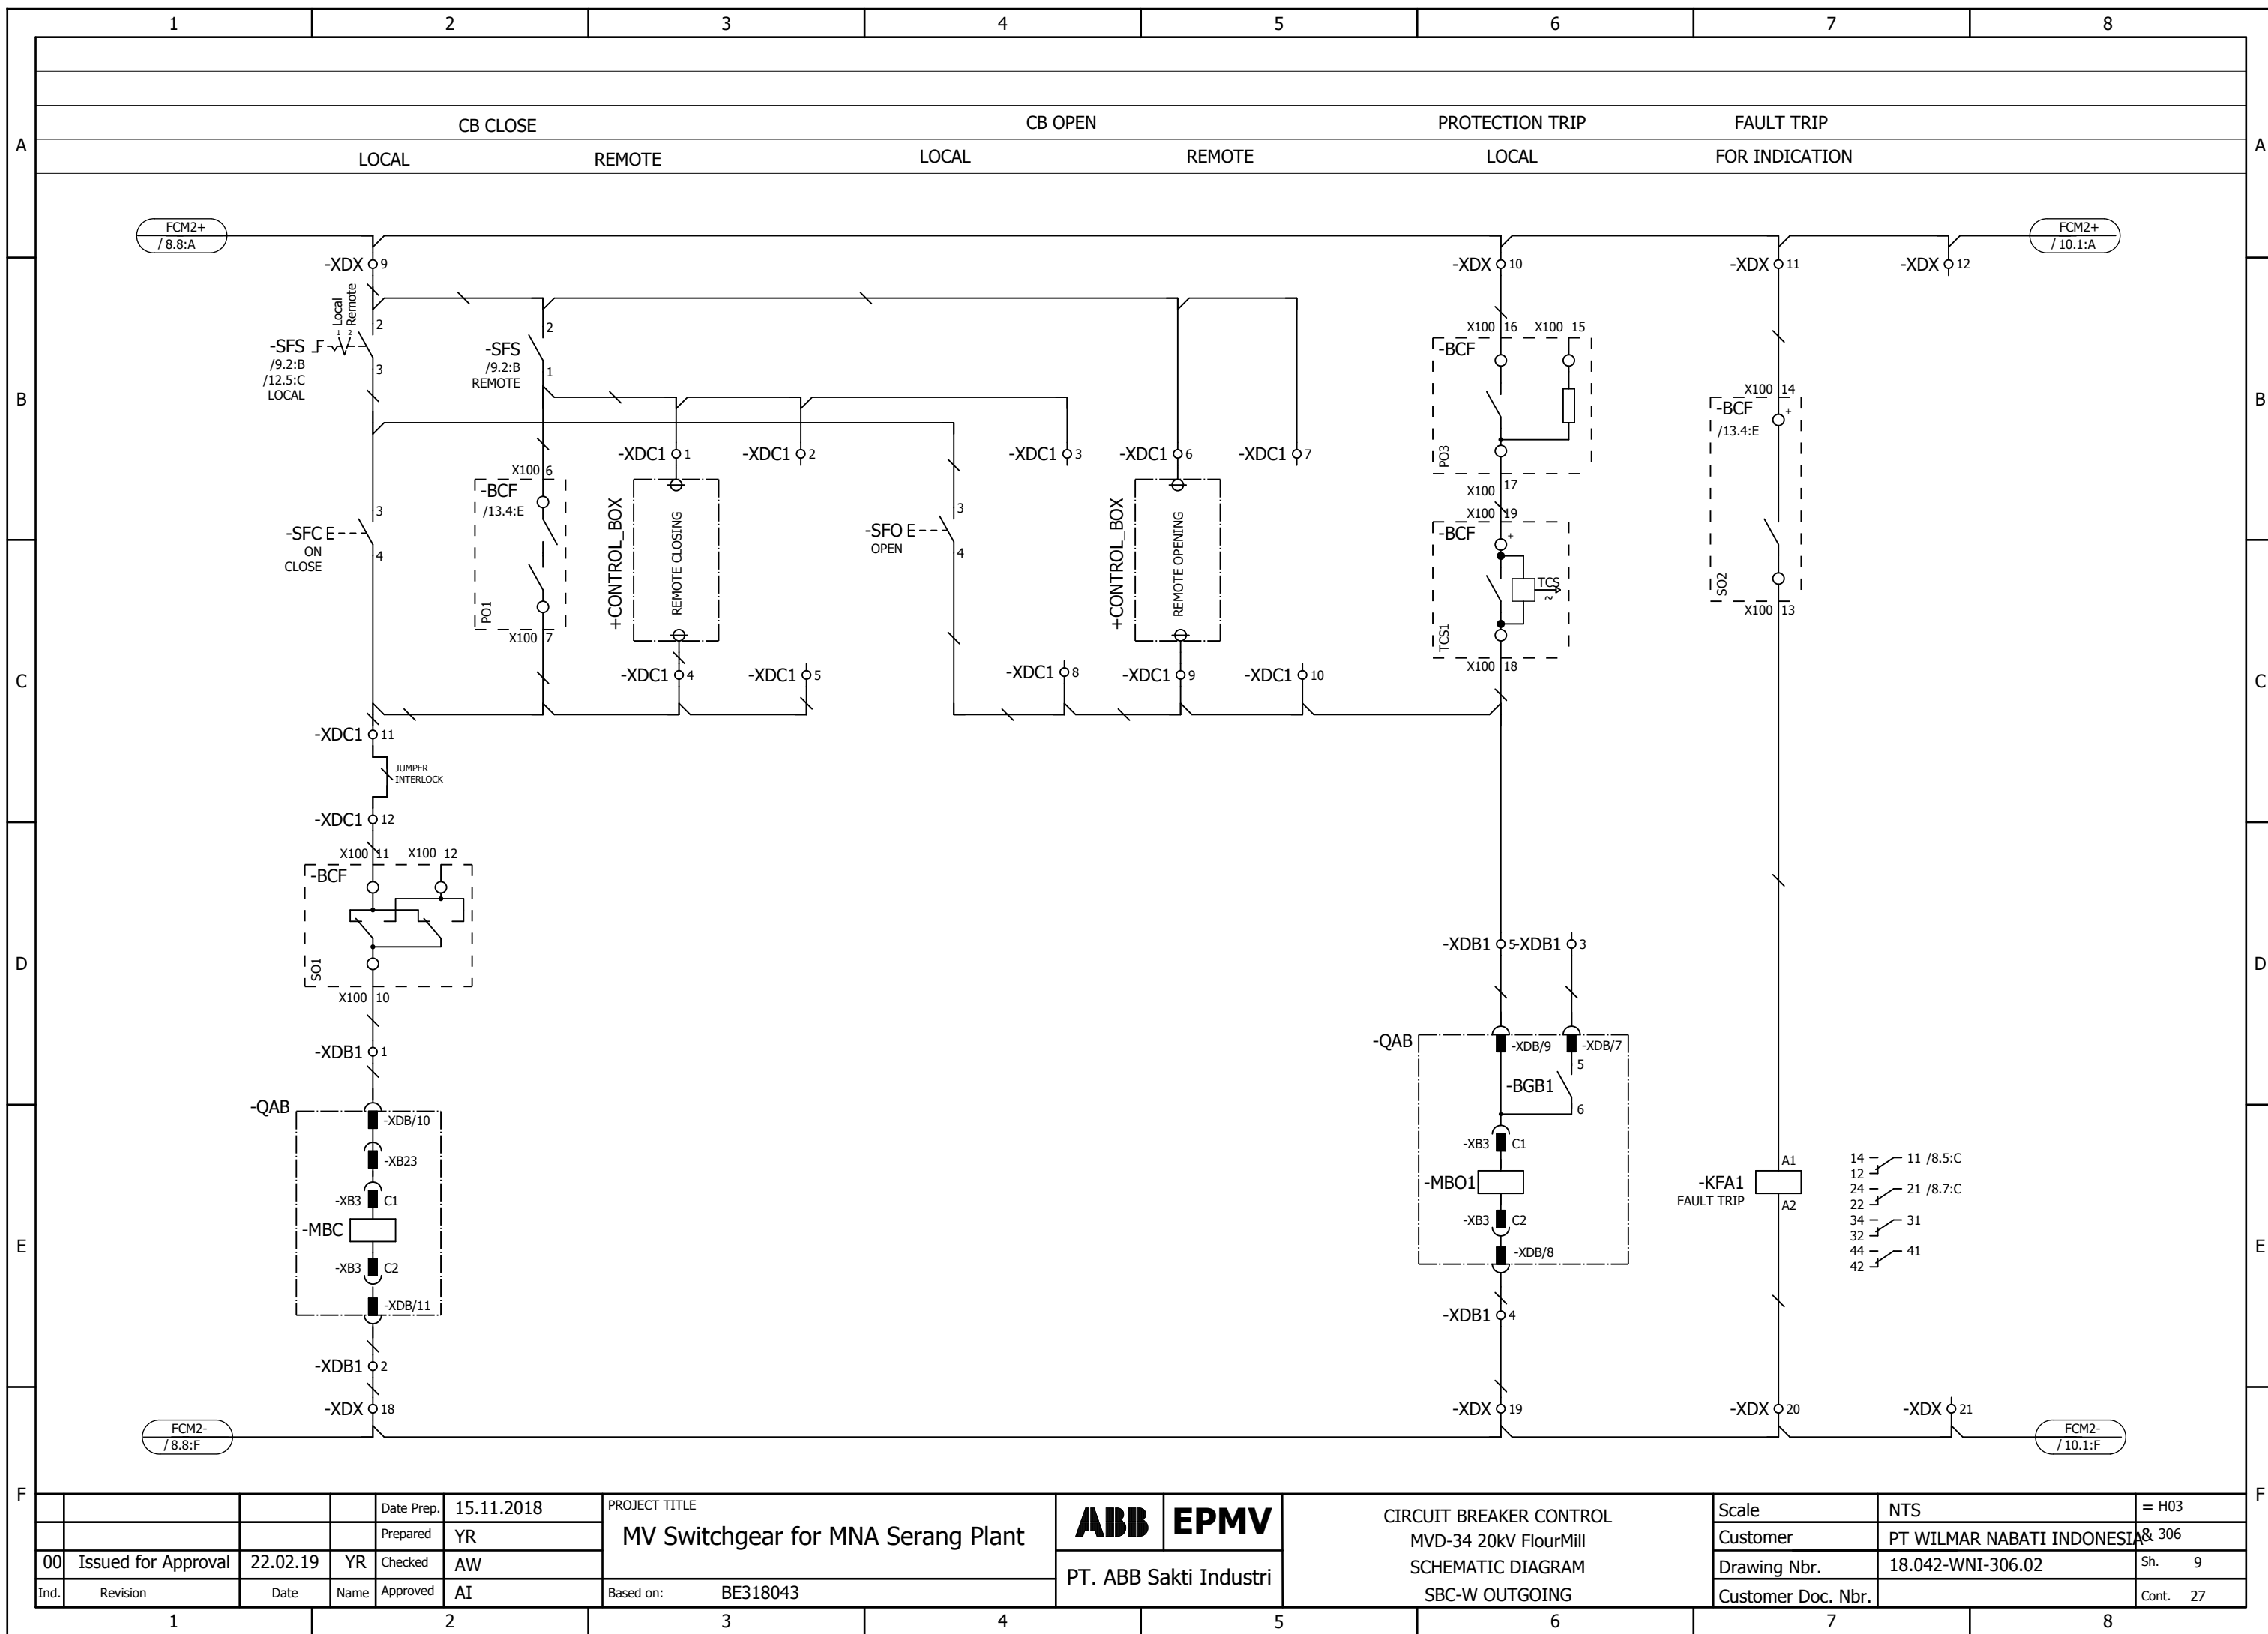


				Date Prep.	15.11.2018	PROJECT TITLE MV Switchgear for MNA Serang Plant			AUXILIARY MOTOR & RELAY MVD-34 20kV FlourMill SCHEMATIC DIAGRAM SBC-W OUTGOING	Scale	NTS	= H03
				Prepared	YR					Customer	PT WILMAR NABATI INDONESIA	& 306
00	Issued for Approval	22.02.19	YR	Checked	AW		PT. ABB Sakti Industri	Drawing Nbr.		18.042-WNI-306.02	Sh. 10	
Ind.	Revision	Date	Name	Approved	AI	Based on: BE318043		Customer Doc. Nbr.			Cont. 27	

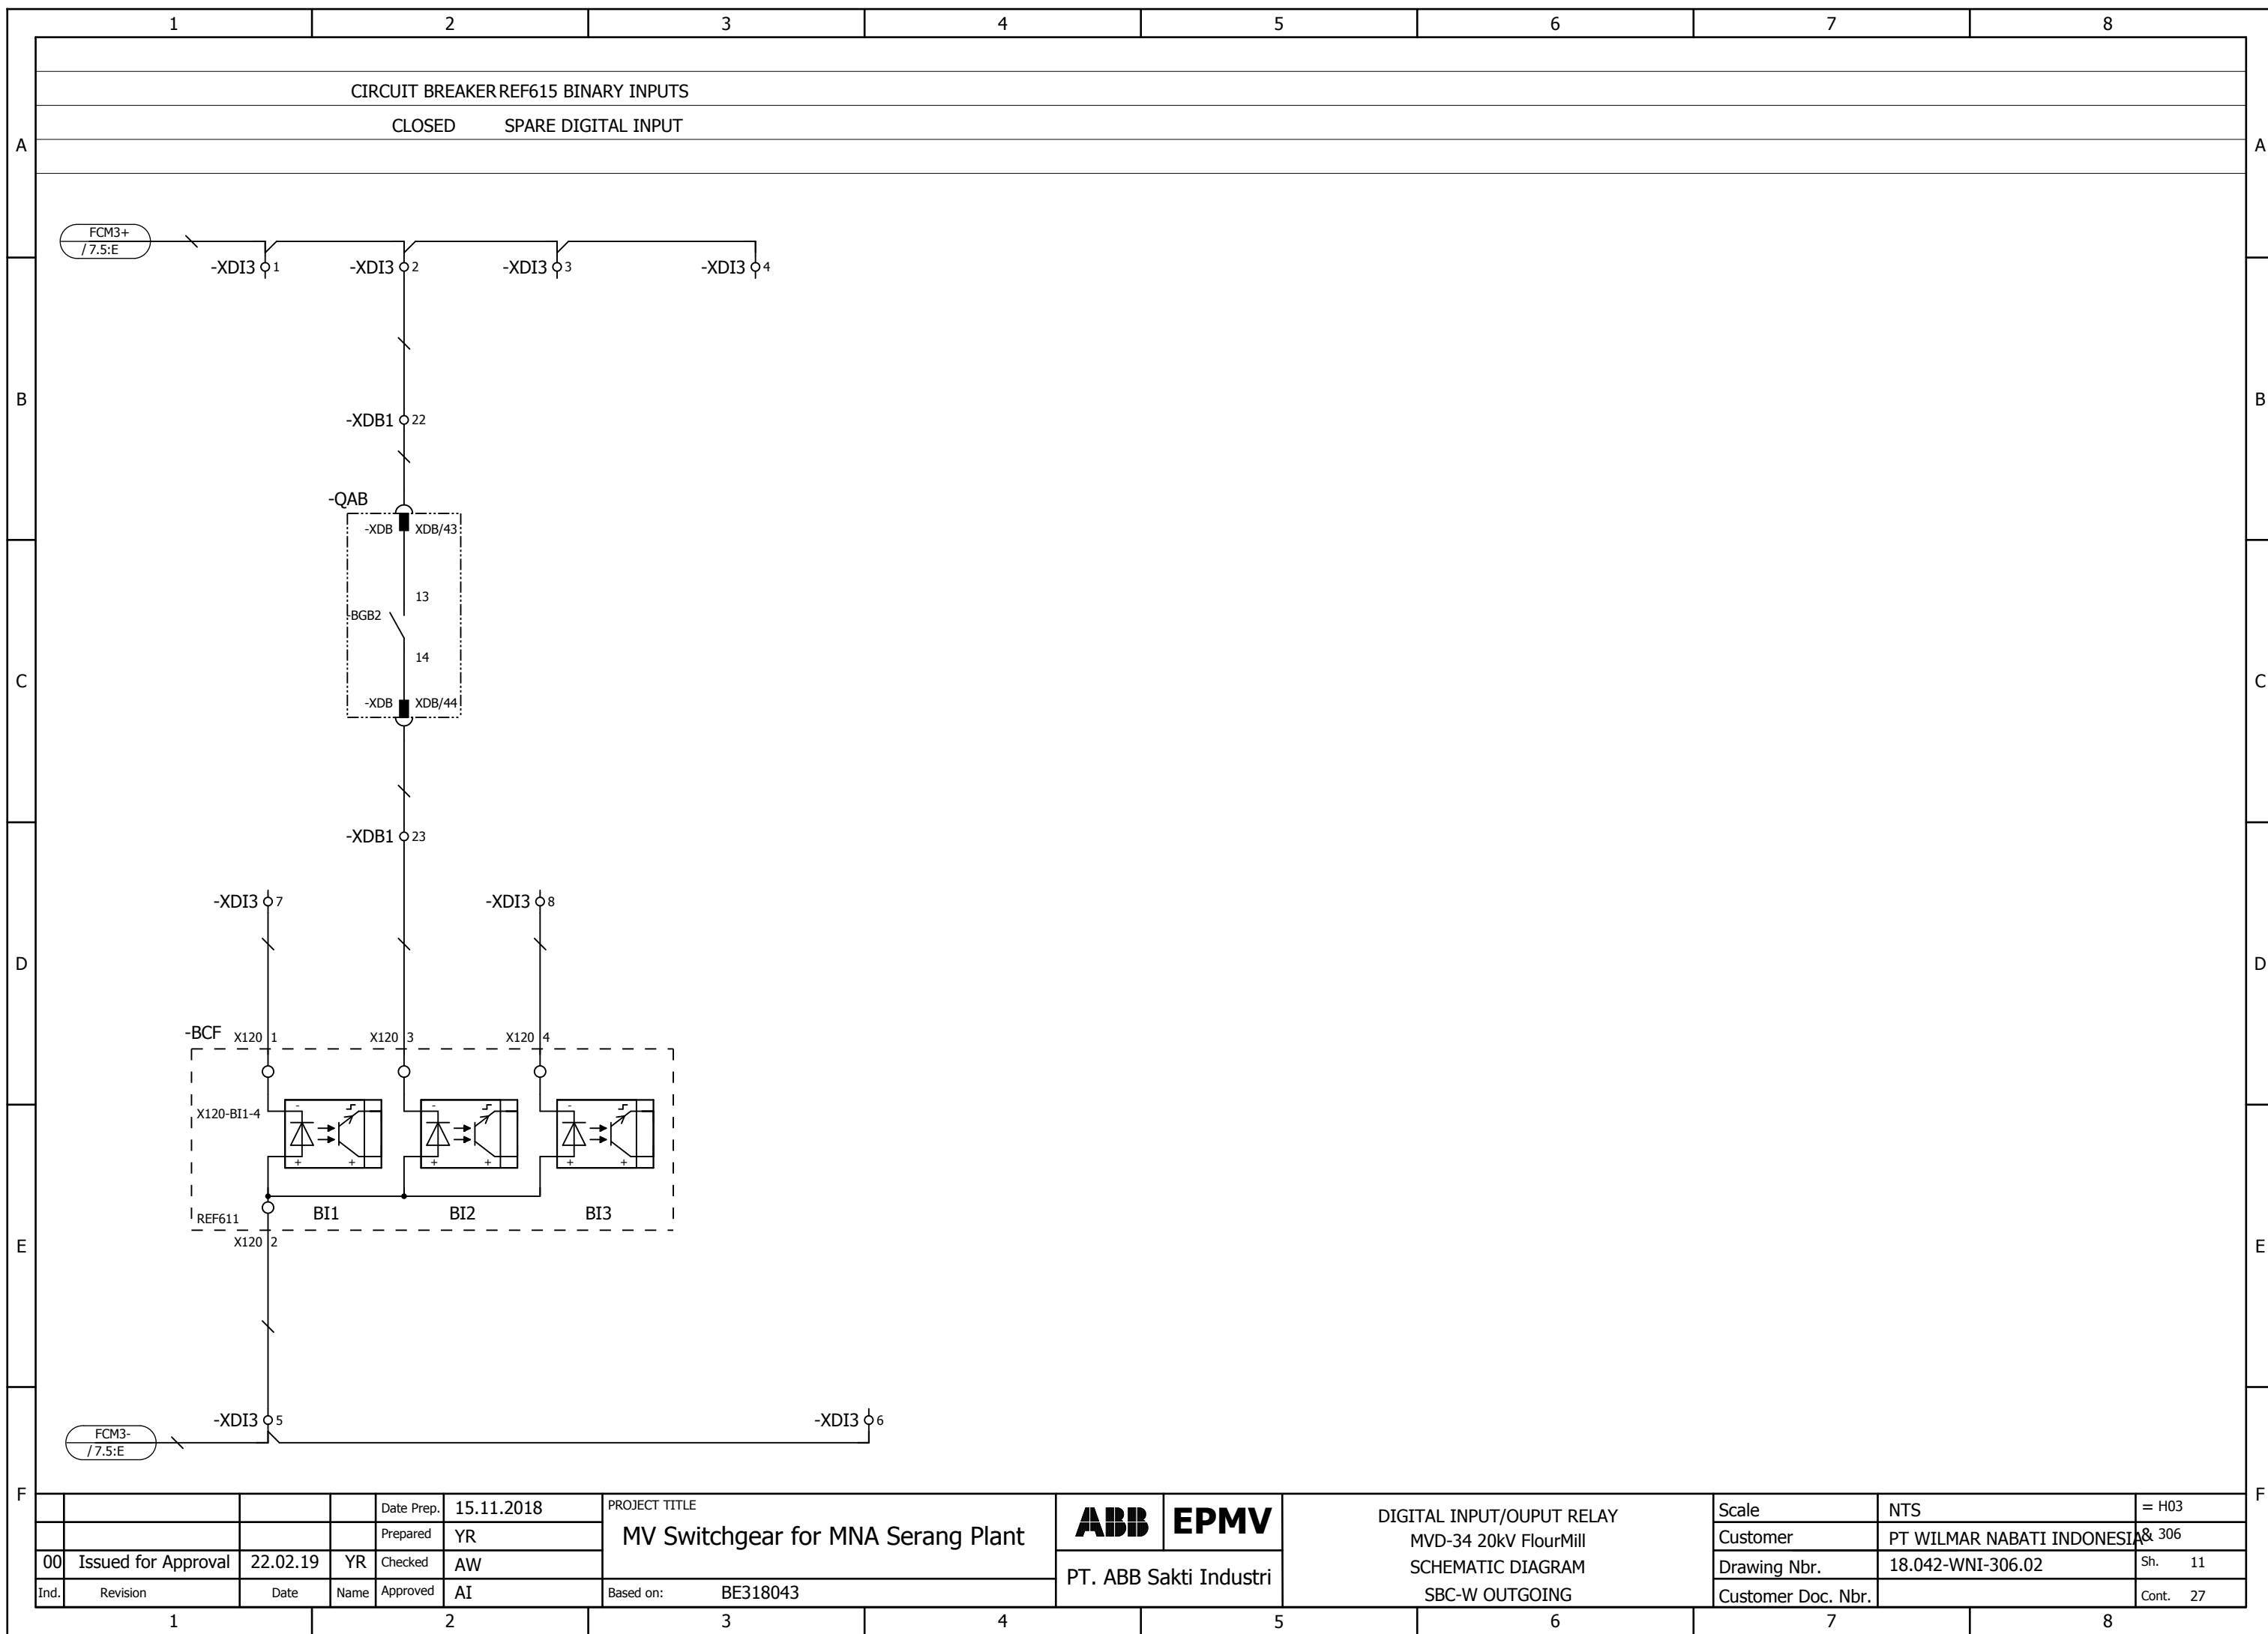


WE RESERVE ALL RIGHTS IN THIS DOCUMENT AND IN THE INFORMATION CONTAINED THEREIN. REPRODUCTION, USE OR DISCLOSURE TO THIRD PARTIES WITHOUT EXPRESS AUTHORITY IS STRICTLY FORBIDDEN.

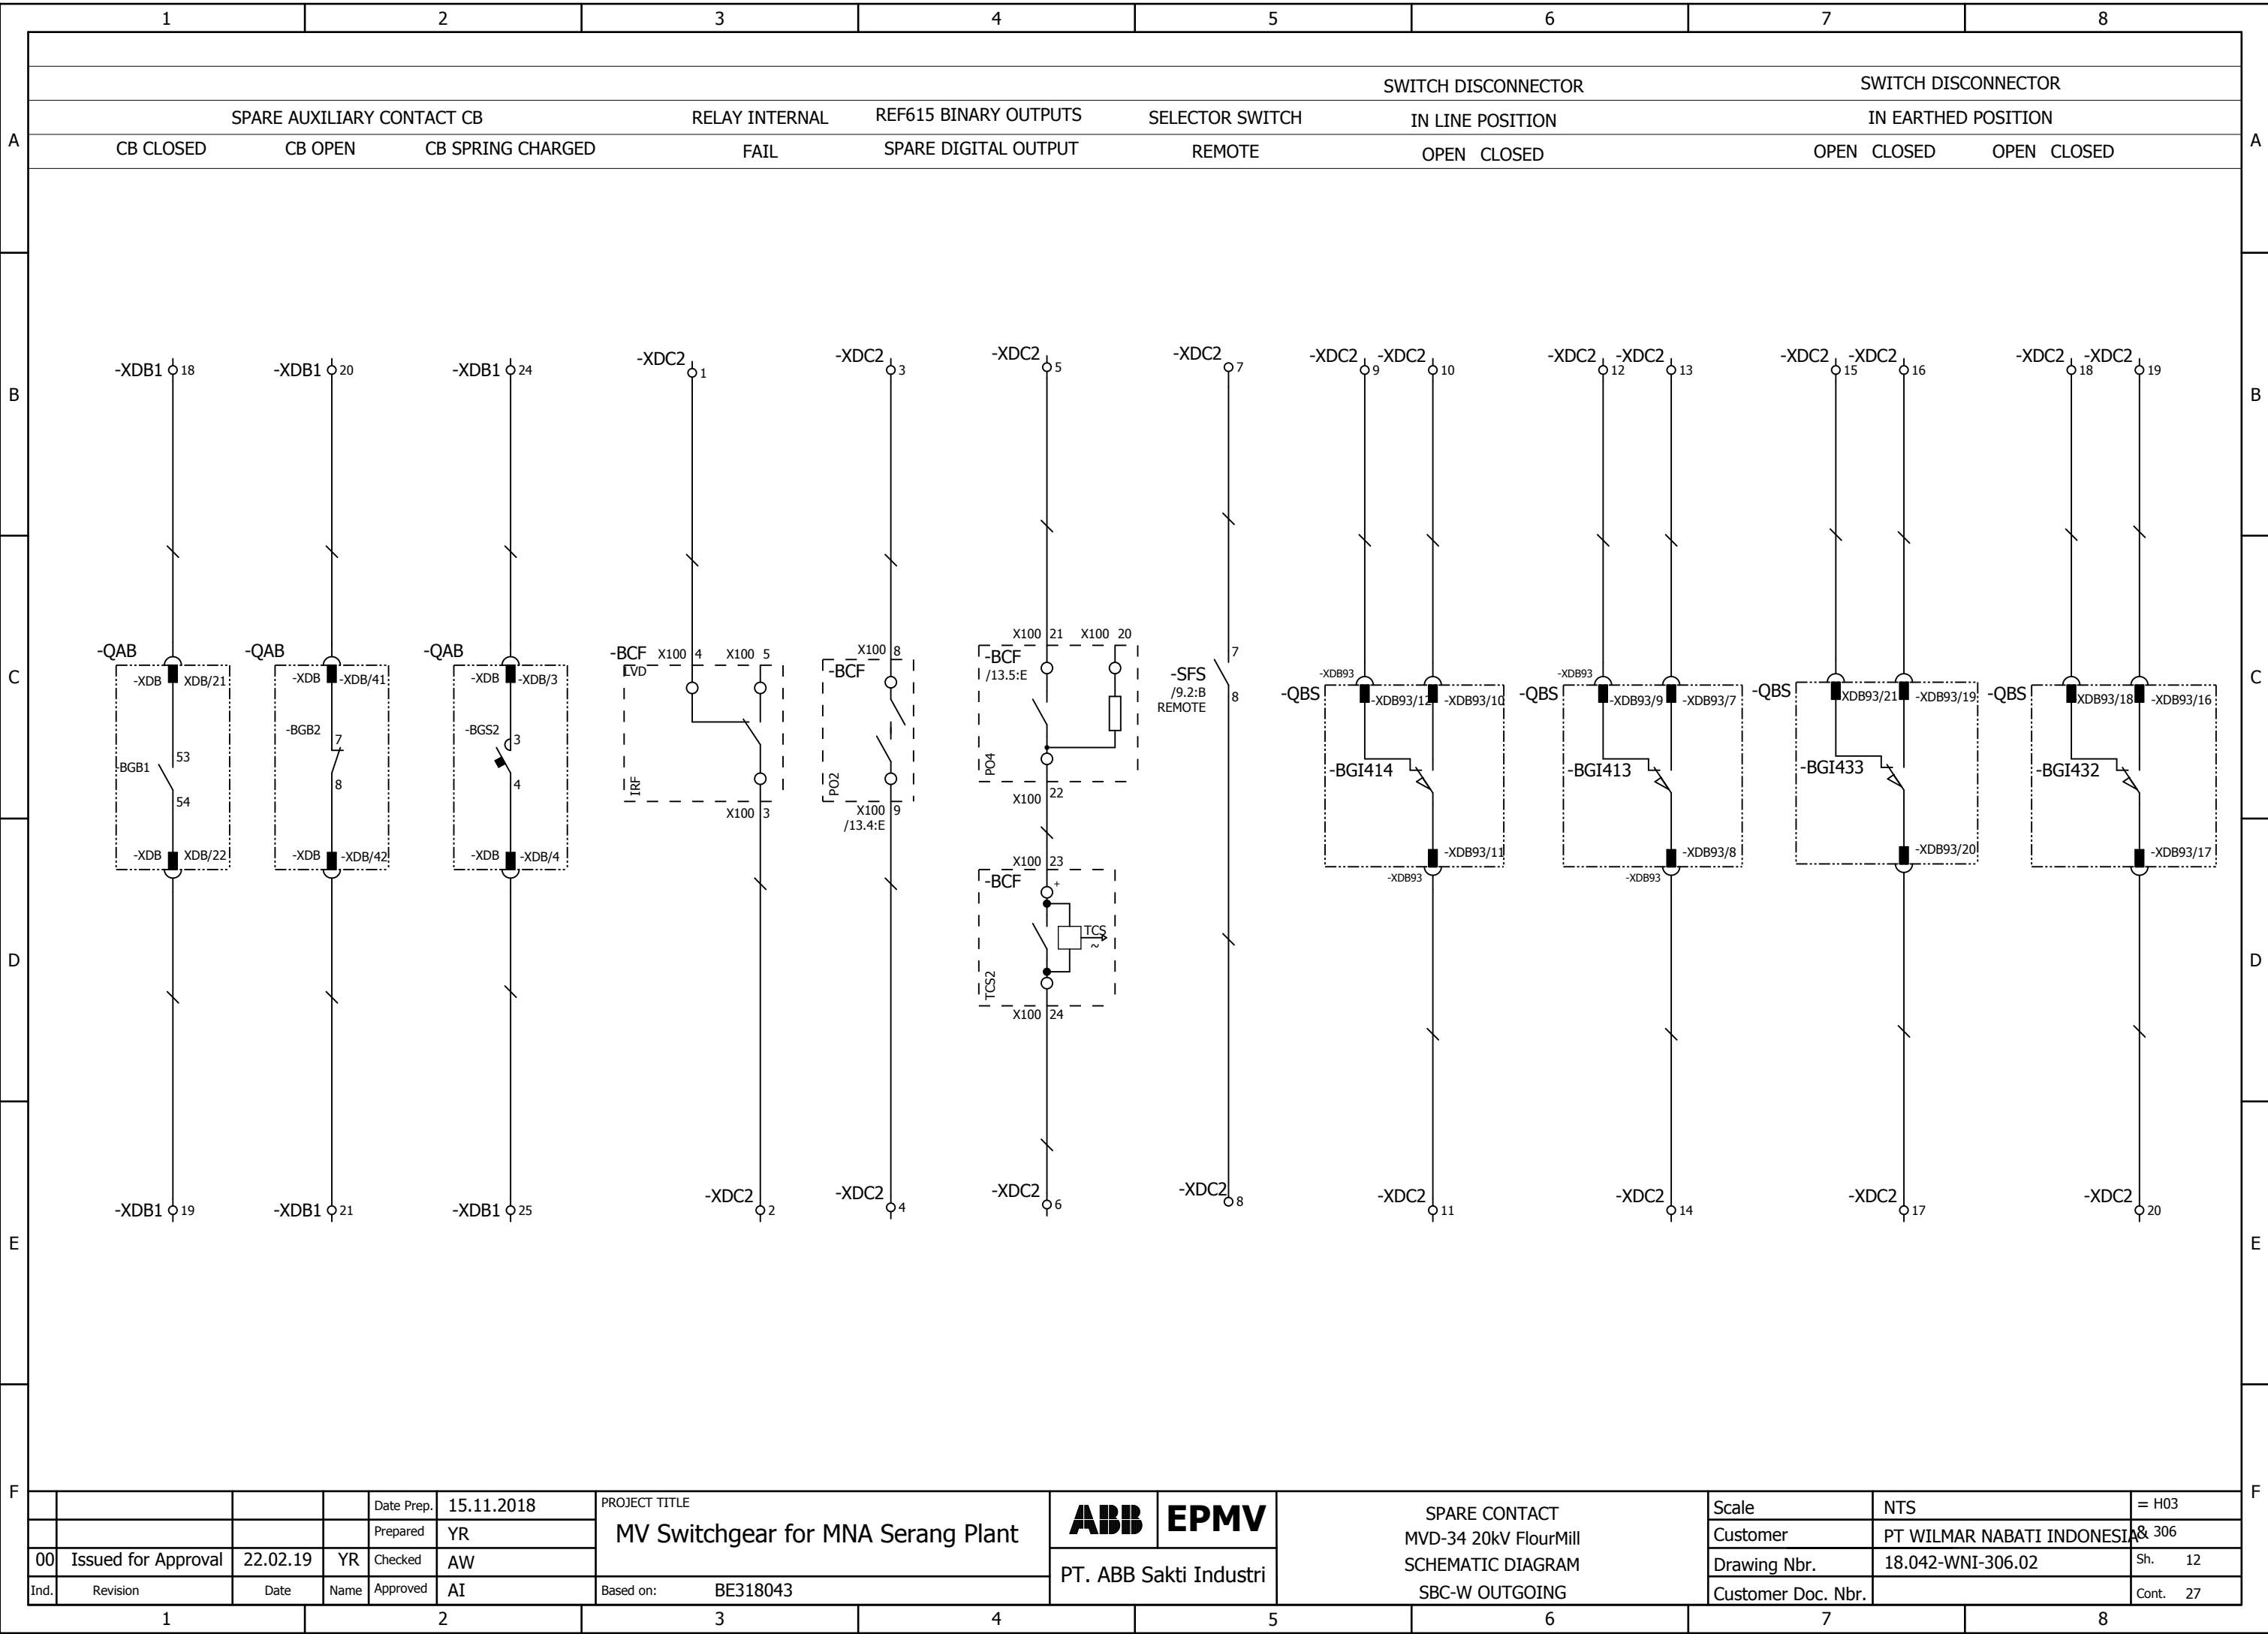

WE RESERVE ALL RIGHTS IN THIS DOCUMENT AND IN THE INFORMATION CONTAINED THEREIN. REPRODUCTION, USE OR DISCLOSURE TO THIRD PARTIES WITHOUT EXPRESS AUTHORITY IS STRICTLY FORBIDDEN.

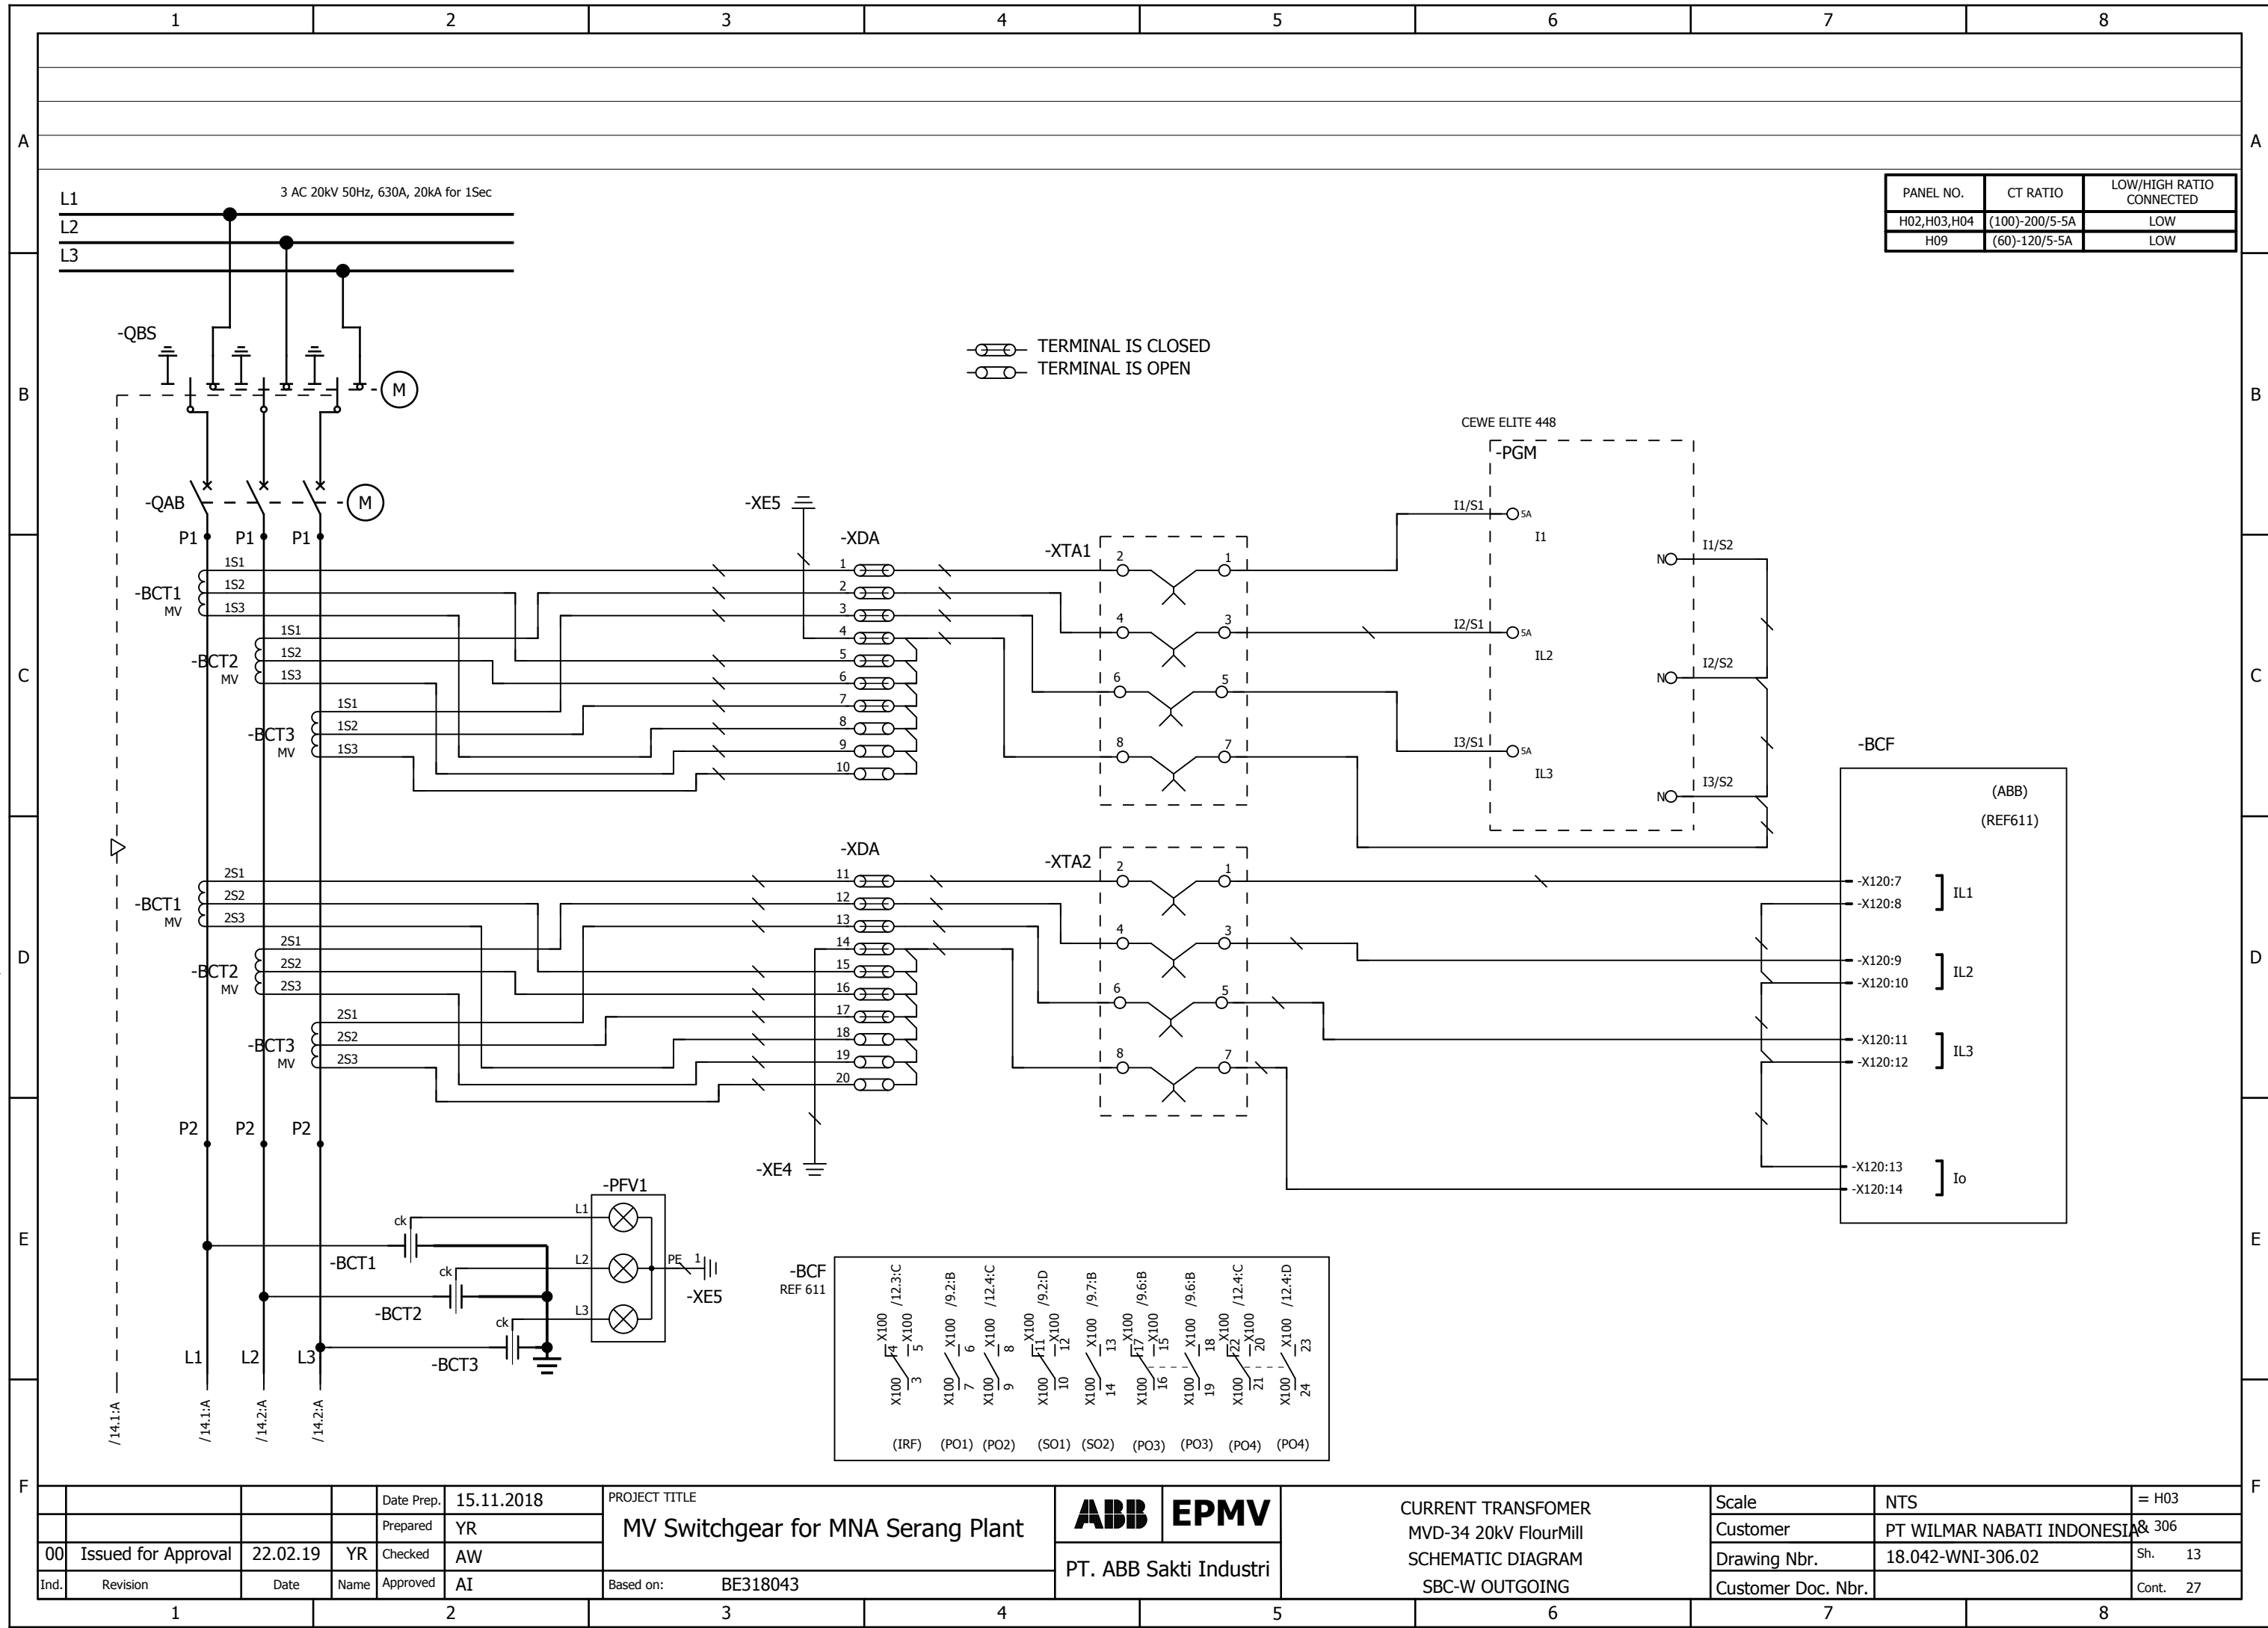


WE RESERVE ALL RIGHTS IN THIS DOCUMENT AND IN THE INFORMATION CONTAINED THEREIN. REPRODUCTION, USE OR DISCLOSURE TO THIRD PARTIES WITHOUT EXPRESS AUTHORITY IS STRICTLY FORBIDDEN.

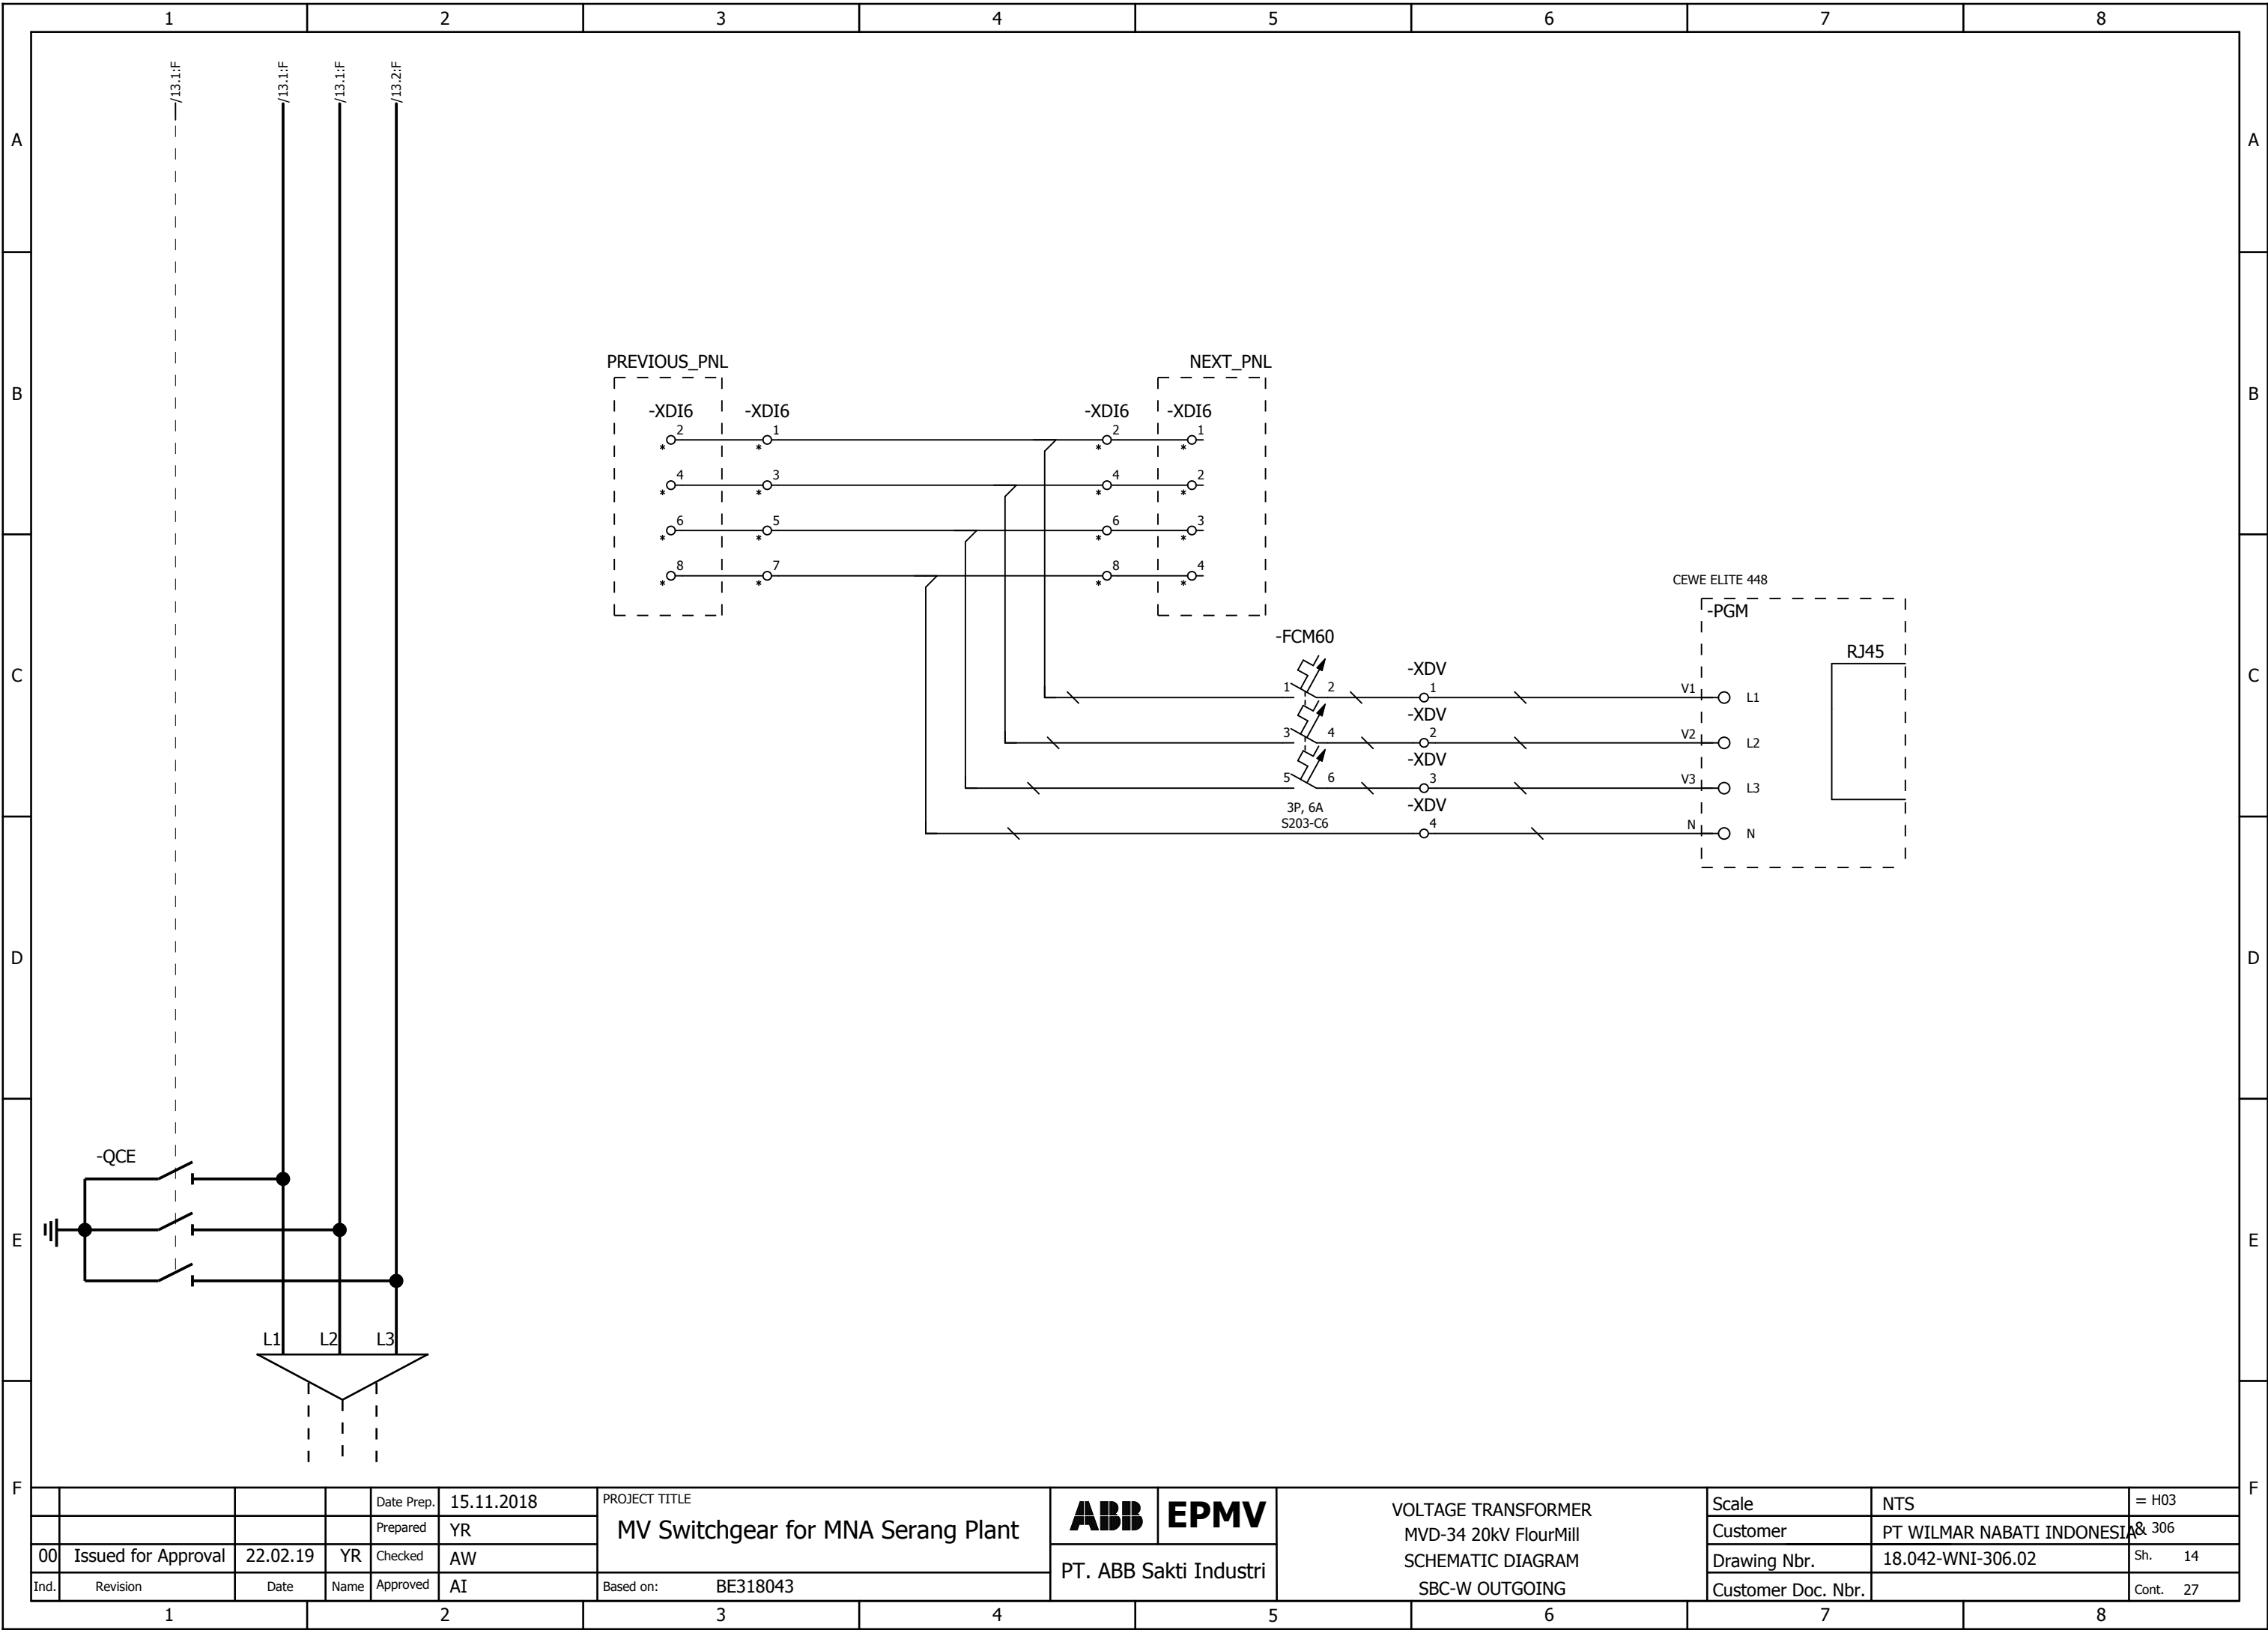

00	Issued for Approval	22.02.19	YR	Date Prep.	15.11.2018	PROJECT TITLE	MV Switchgear for MNA Serang Plant	ABB EPMV	VOLTAGE TRANSFORMER MVD-34 20kV FlourMill SCHEMATIC DIAGRAM SBC-W OUTGOING	Scale	NTS	= H03
				Prepared	YR							
				Checked	AW							
				Approved	AI							
Ind.	Revision	Date	Name	Approved	AI	Based on:	BE318043	PT. ABB Sakti Industri		Customer	PT WILMAR NABATI INDONESIA	Sh. 14
										Drawing Nbr.	18.042-WNI-306.02	Cont. 27
										Customer Doc. Nbr.		

No.	EQUIPMENT DESCRIPTION	ENGRAVING
1	-SFS (LOCAL-OFF-REMOTE SELECTOR SWITCH, K&N)	-SFS, LOCAL-OFF-REMOTE
2	-SFC (PUSH BUTTON CB CLOSE, GREEN, ABB)	-SFC, CB CLOSE
3	-SFO (PUSH BUTTON CB OPEN, RED, ABB)	-SFO, CB OPEN
4	-PFY1 (LAMP INDICATION FOR CB TRIP, YELLOW, ABB)	-PFY1, CB TRIP
5	-PFR1 (LAMP INDICATION FOR CB CLOSE, RED, ABB)	-PFR1, CB CLOSE
6	-PFG1 (LAMP INDICATION FOR CB OPEN, GREEN, ABB)	-PFG1, CB OPEN
7	-PGJ (DIGITAL MEASUREMENT, CEWE 448)	-PGJ, DIGITAL MEASUREMENT
8	-BCF (FEEDER PROTECTION RELAY, REF615J, ABB)	-BCF, RELAY PROTECTION
9	-XTA1, XTA2 (TEST BLOCK , YONGSUNG)	-XTA, CURRENT TEST BLOCK

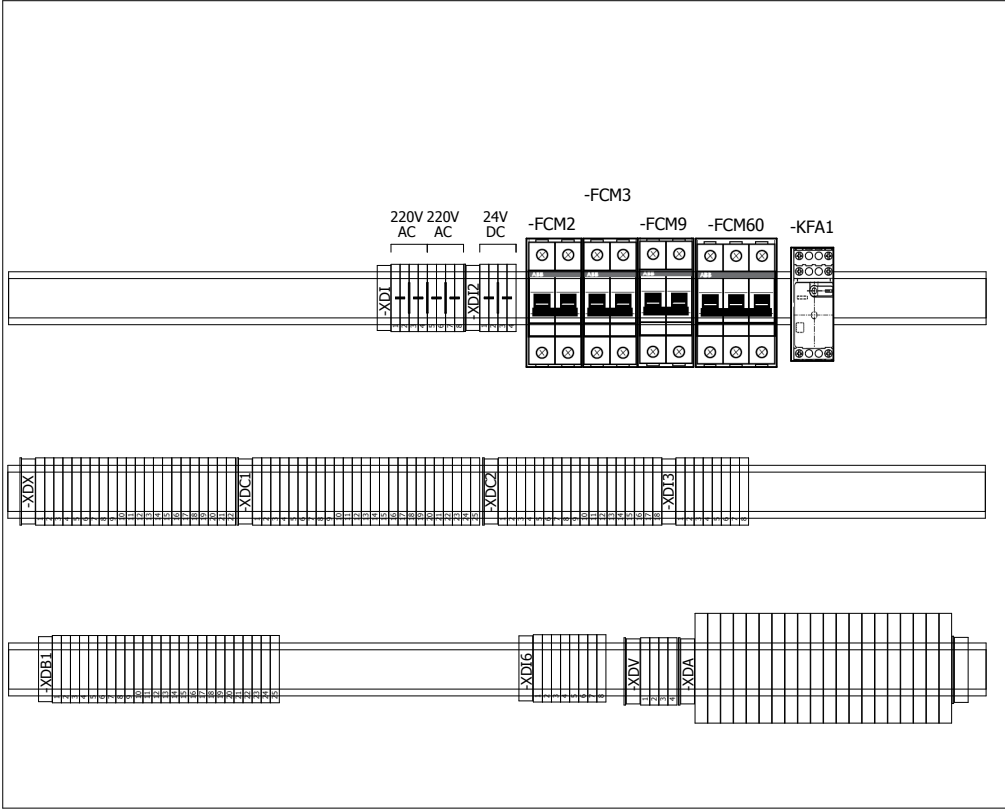[illegible]

				Date Prep.	15.11.2018	PROJECT TITLE MV Switchgear for MNA Serang Plant	ABB	EPMV	LV BOX LAYOUT MVD-34 20kV FlourMill SCHEMATIC DIAGRAM SBC-W OUTGOING	Scale	NTS	= H03
				Prepared	YR							Customer
00	Issued for Approval	22.02.19	YR	Checked	AW					Drawing Nbr.	18.042-WNI-306.02	Sh. 16
Ind.	Revision	Date	Name	Approved	AI	Based on: BE318043	PT. ABB Sakti Industri			Customer Doc. Nbr.		Cont. 27

Carry over: 0.00

[illegible]

				Date Prep.	15.11.2018	PROJECT TITLE MV Switchgear for MNA Serang Plant	ABB	EPMV	PART LIST MVD-34 20kV FlourMill SCHEMATIC DIAGRAM SBC-W OUTGOING	Scale	NTS	= H03
				Prepared	YR					Customer	PT WILMAR NABATI INDONESIA	& 306
00	Issued for Approval	22.02.19	YR	Checked	AW		PT. ABB Sakti Industri	Drawing Nbr.		18.042-WNI-306.02	Sh. 17	
Ind.	Revision	Date	Name	Approved	AI	Based on: BE318043		Customer Doc. Nbr.			Cont. 27	

[illegible]

[illegible]

F		E		D		C		B		A		
Ind. Revision Date Name Approved		REMARK		CABLE	EQUIPMENT	Wire No	Terminal number	TYPE	WIRE NO.	EQUIPMENT	CABLE	REMARK
==MVD-34=H03+-XDI2												
REMARK: ☆ INTERPANEL LIGHT BUS, OFFERED TOGETHER WITH PANELS. △ OUTGOING CONTROL CABLE (Supply by Customer). ● BRIDGE BAR. ✕ PARTITION PLATE. (TEST JUMPER.												

Date Prep.		15.11.2018		PROJECT TITLE		MV Switchgear for MNA Serang Plant		ABB EPMV		Terminal diagram ==MVD-34=H03+-XDI2		Scale		= H03			
Prepared		YR										Customer		PT WILMAR NABATI INDONESIA		Sh. 23	
Checked		AW										Drawing Nbr.				Cont. 27	
Based on:		BE318043		PT. ABB Sakti Industri													

[illegible]

[illegible]

[illegible]

F				E		D		C		B		A	
</													