



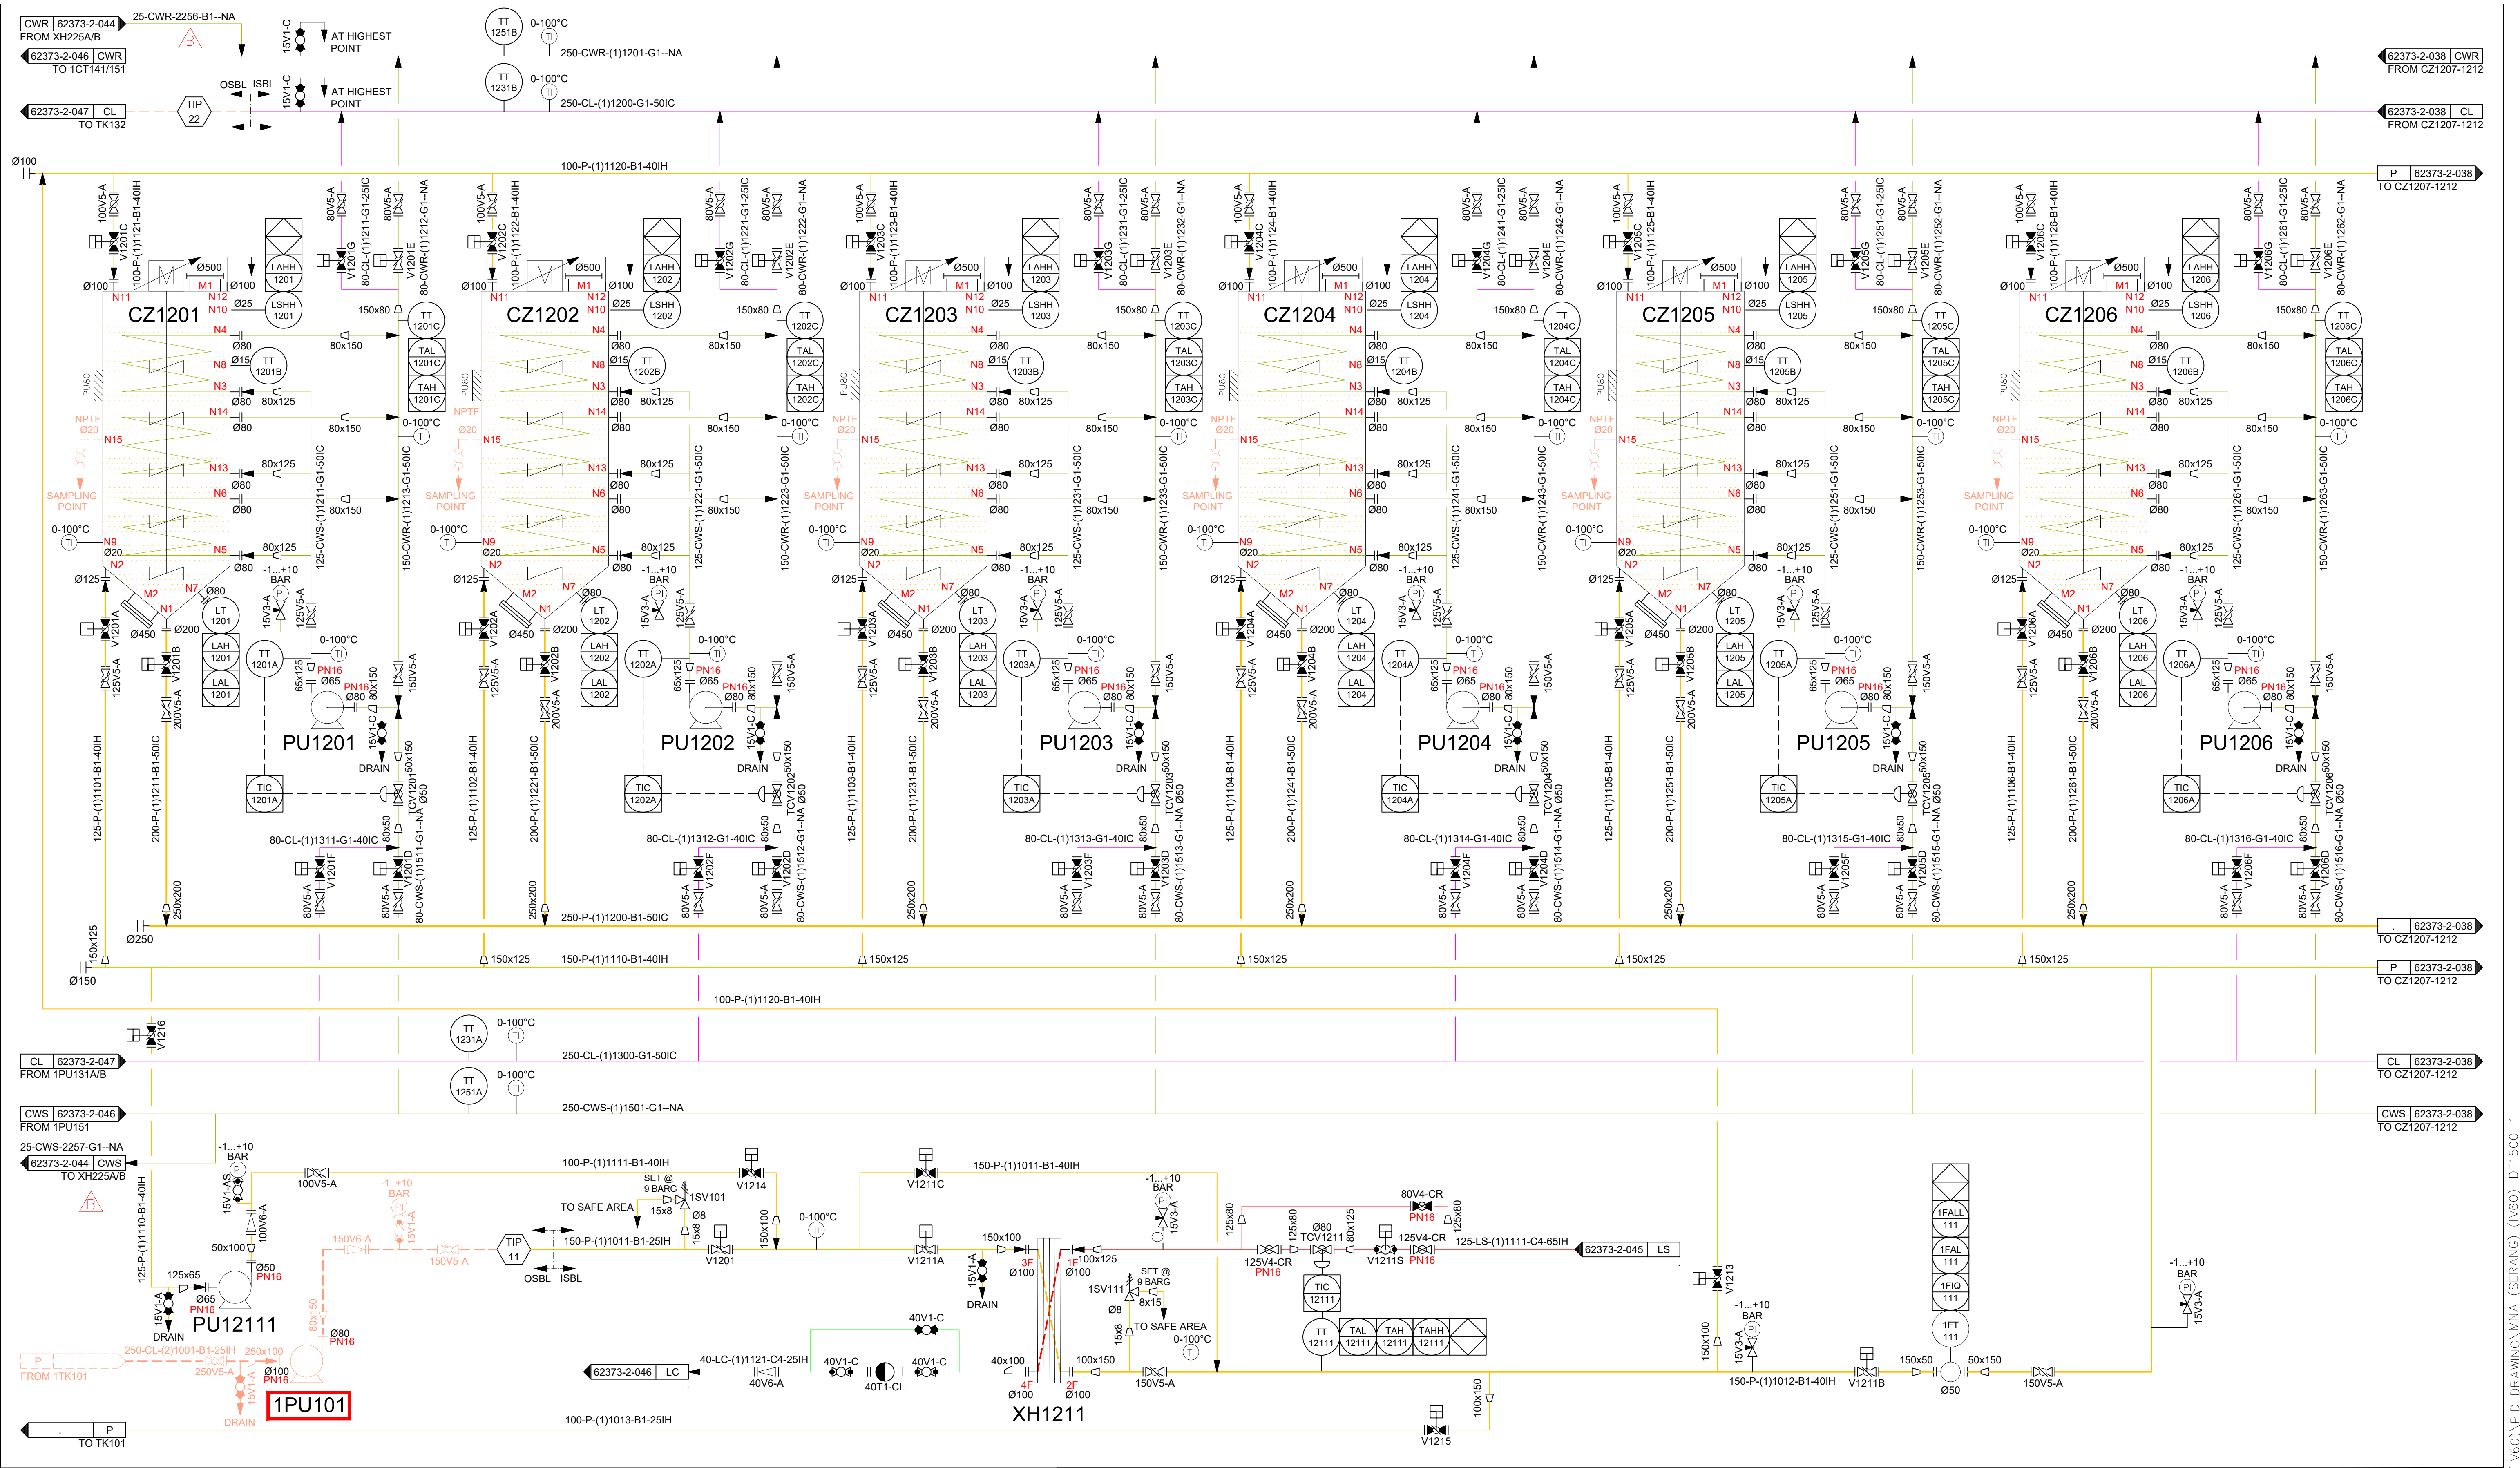


NOTES									This drawing is the property of LUPICO Technologies Pte Ltd and is for internal use only. It is to be used for reference only and is not to be reproduced or utilized in any form without prior written authorization of LUPICO Technologies Pte Ltd.	Customer PT. MULTIMAS NABATI ASAHAN (SERANG)		
											Scale : N.T.S.	
											Date : 010318	
											Drawn By : DZHAFRI	
											Checked :	
				2.	REVISED AS SHOWN 	041018	DZF			Project Name		
				1.	REVISED AS SHOWN 	180718	DZF			1,500MTD DRY FRACTIONATION PLANT (IV60)		
				NO.	DESCRIPTION	DATE	BY	CHK'D		Sheet No. : Or		
				REVISIONS						Drawing No. 62373-2-037		
										Rev. B		


This drawing is the property of IPICO Technologies Pte Ltd. Total or partial reproduction or utilization of this document is forbidden without prior written authorization of IPICO Technologies Pte Ltd.

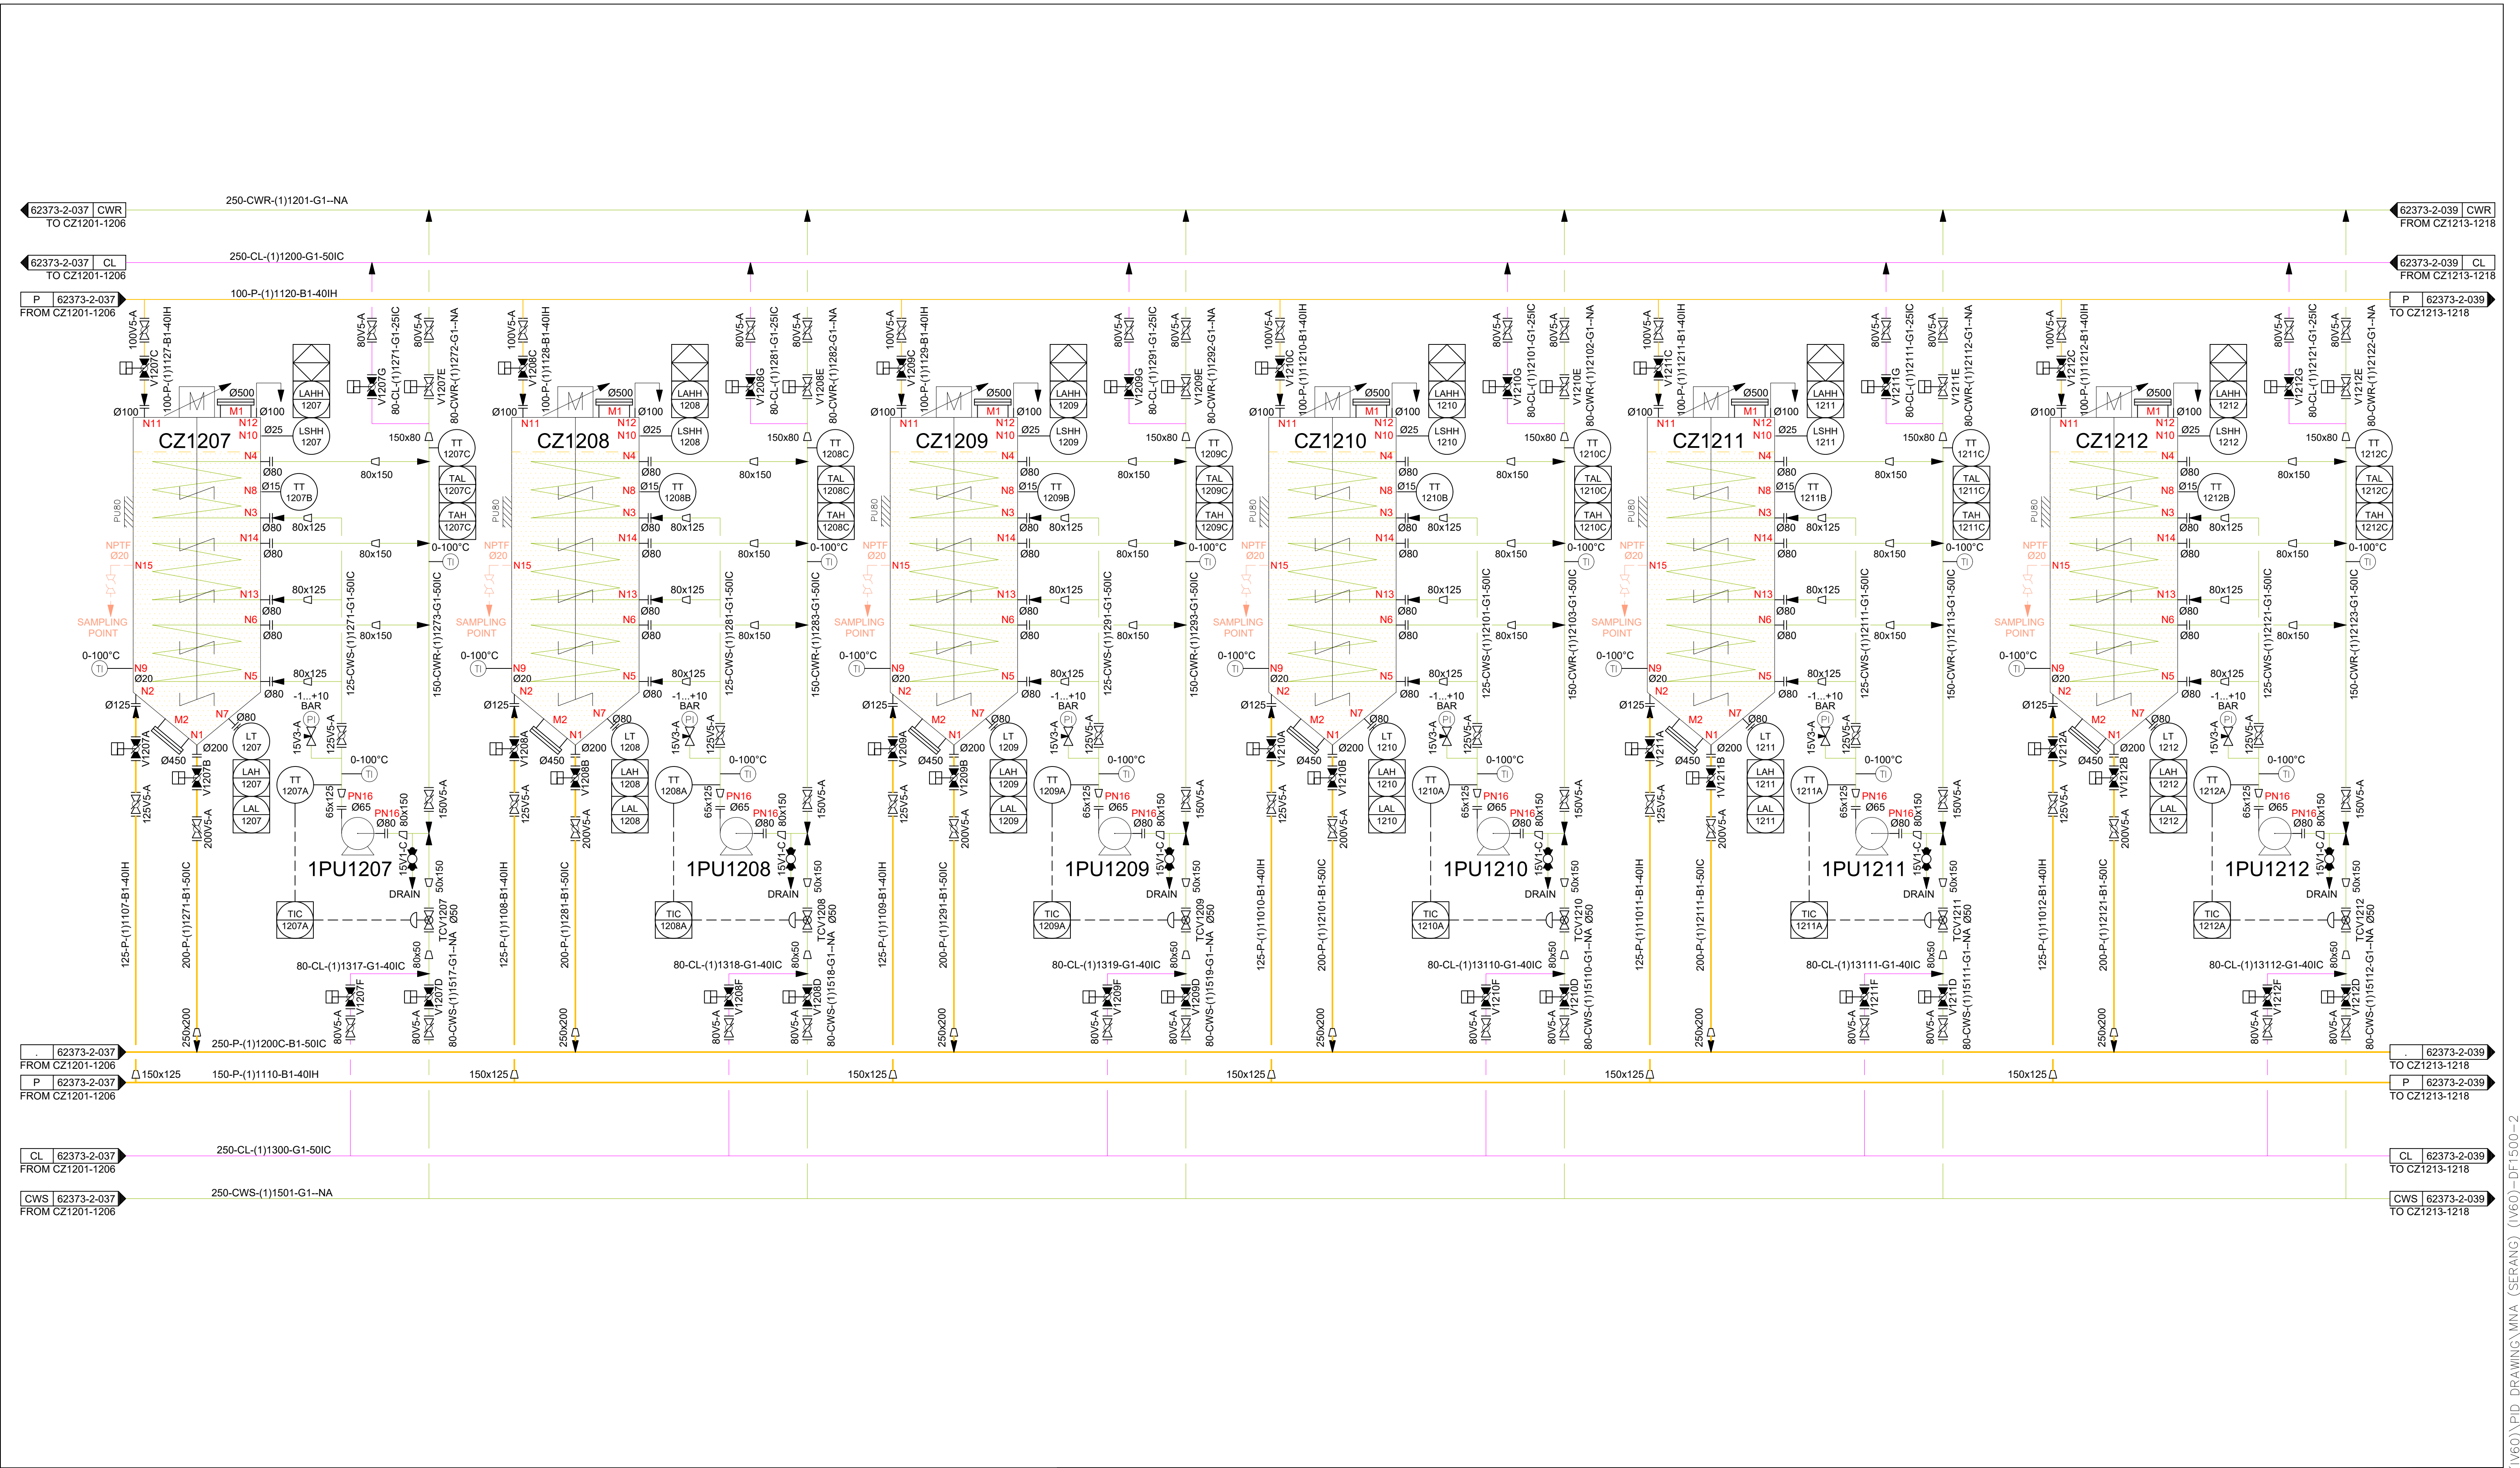


NOTES									This drawing is the property of LUPICO Technologies Pte Ltd and is for the use of the client only. It is to be used for the project and not for any other purpose. It is to be kept confidential and not to be distributed to any other person without prior written authorization of LUPICO Technologies Pte Ltd.	Customer PT. MULTIMAS NABATI ASAHAN (SERANG)			
										 lipico	Scale :	N.T.S.	
											Date :	020318	
											Drawn By :	DZHAFRI	
											Checked :		
										Project Name	Approved :		
										1,500MTD DRY FRACTIONATION PLANT (IV60)	Sheet No. : Of		
										PIPING & INSTRUMENTATION DIAGRAM FOR CRYSTALLIZATION (PART 2)	Drawing No.	Rev.	
											62373-2-038		

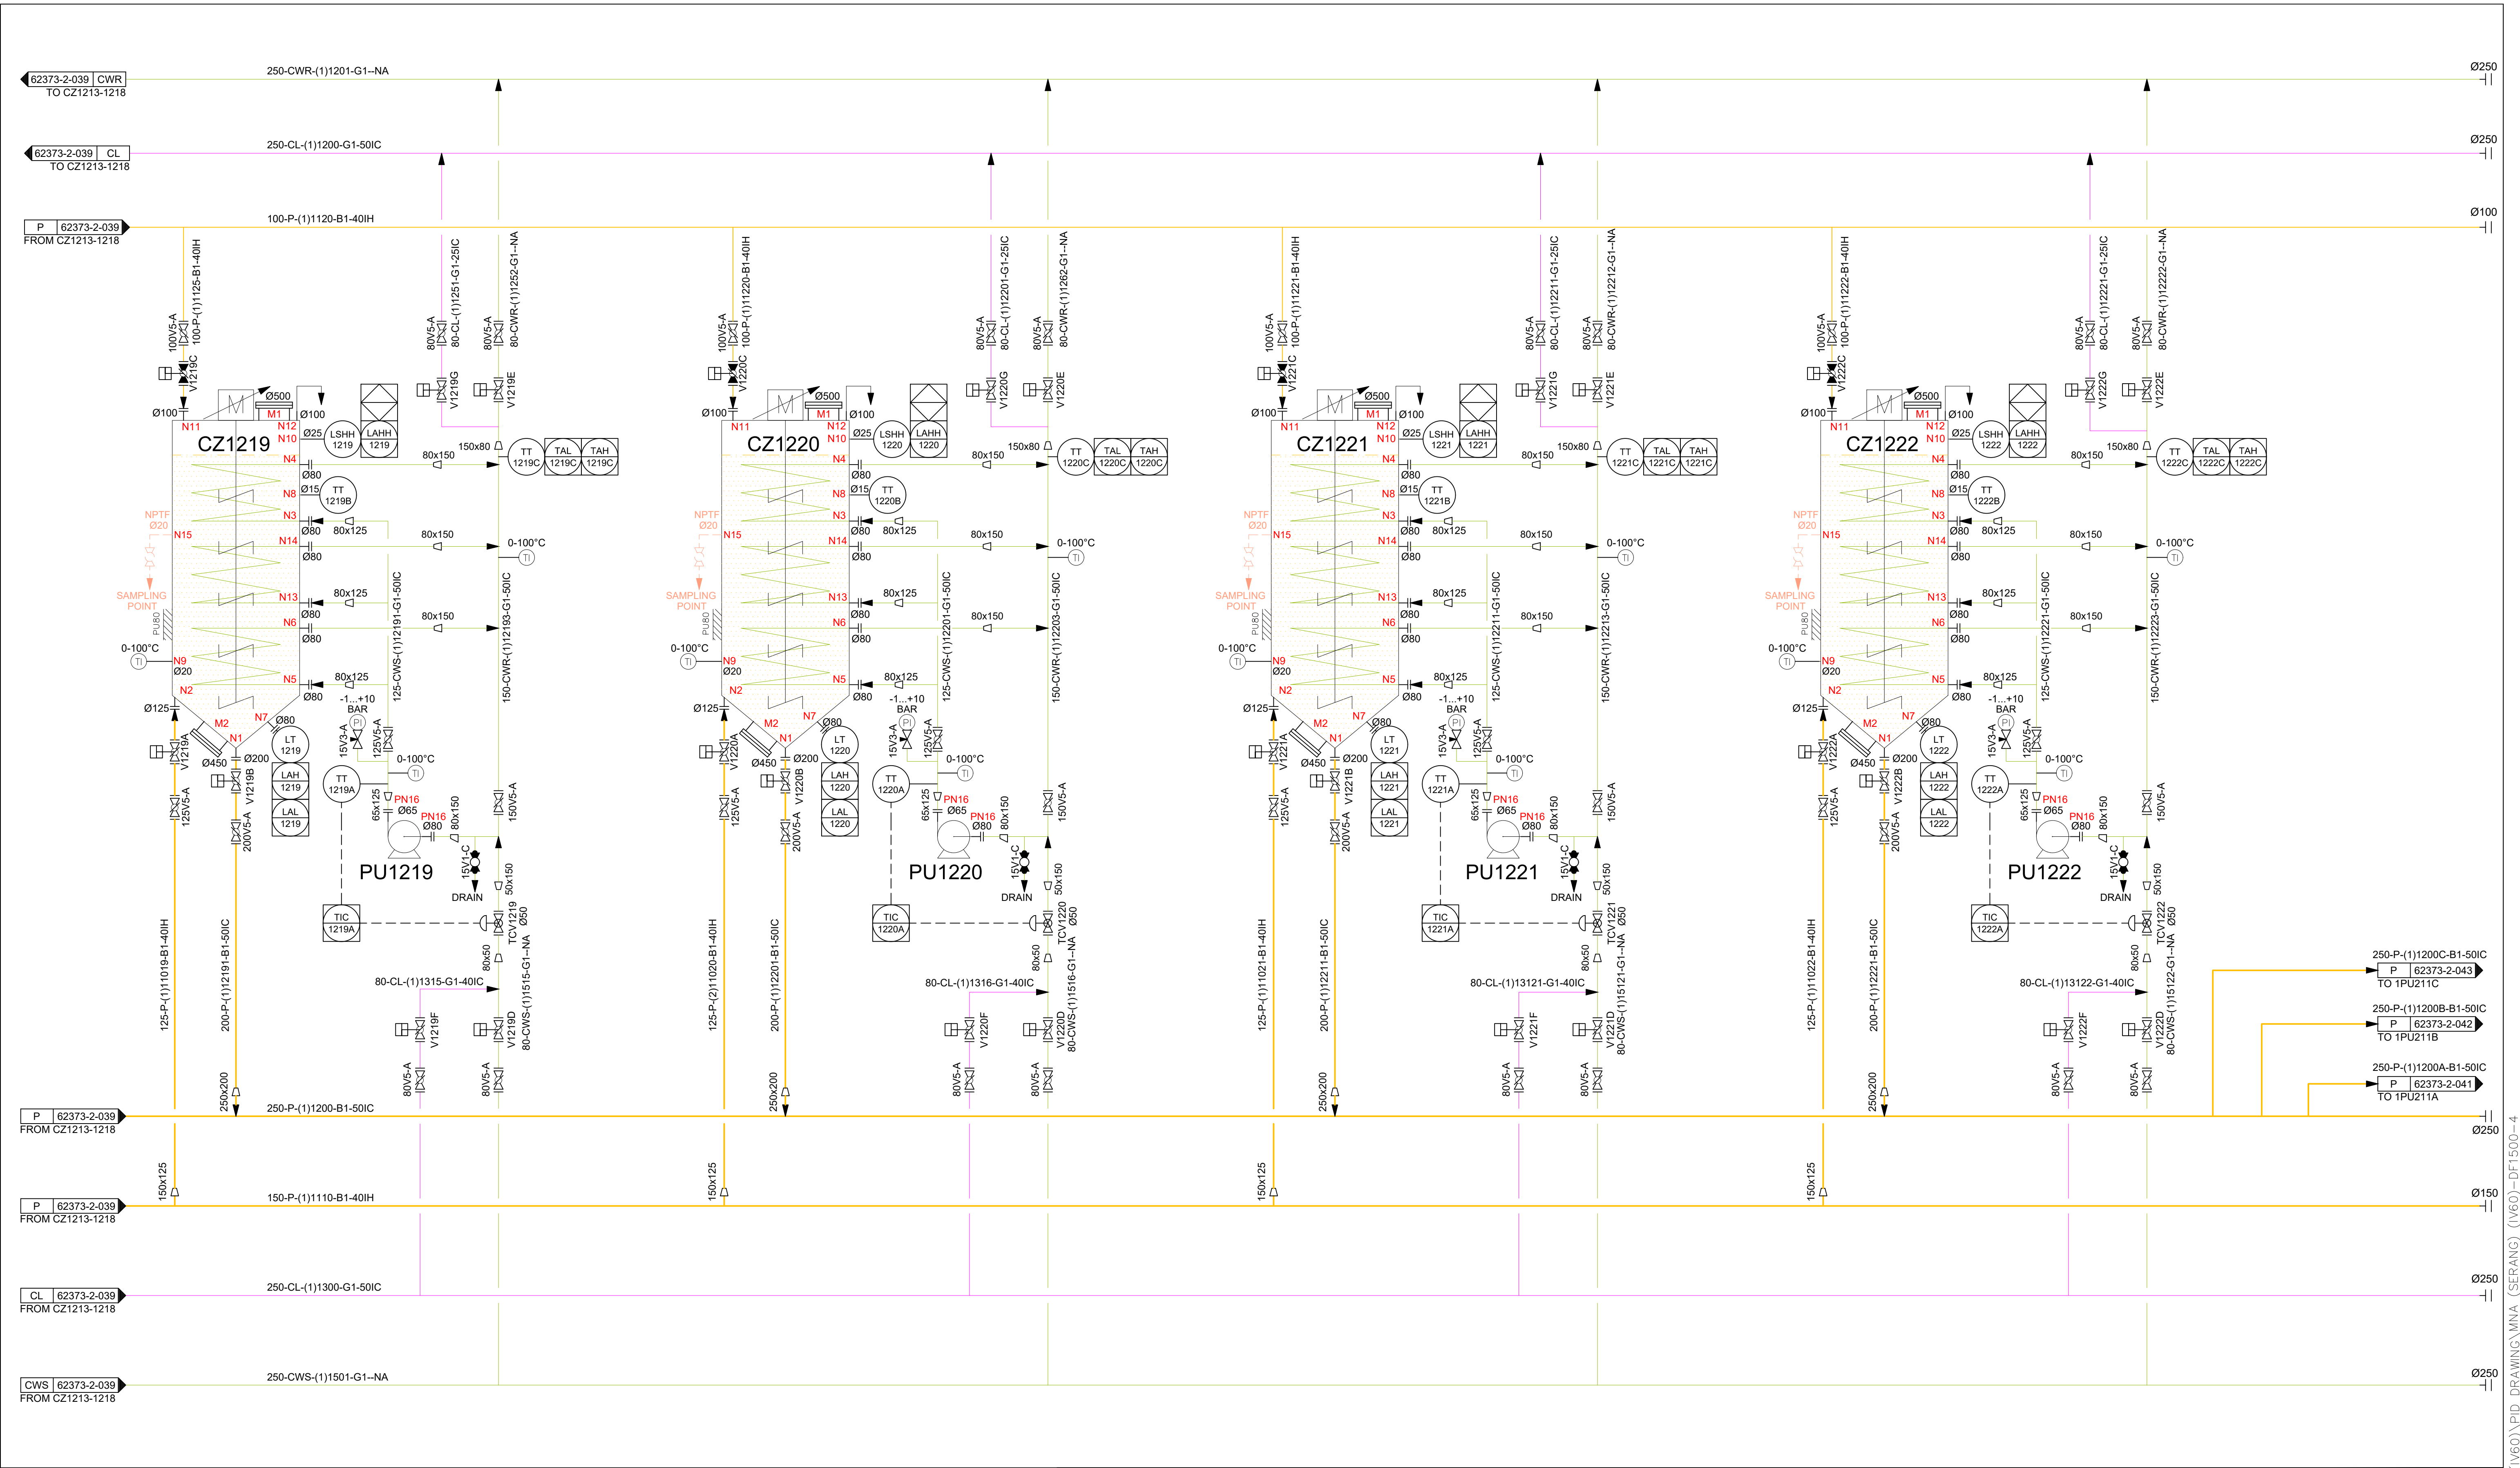

NOTES										This drawing is the property of LUPICO Technologies Pte Ltd total or partial reproduction or utilization of this document is forbidden without prior written authorization of LUPICO Technologies Pte Ltd.	Customer PT. MULTIMAS NABATI ASAHAN (SERANG)								
												Scale :	N.T.S.						
												Date :	010318						
												Drawn By :	DZHAFRI						
												Checked :							
												Approved :							
																Project Name	1,500MTD DRY FRACTIONATION PLANT (IV60)		
																	Sheet No. : Of		
																	Drawing No.	62373-2-040	Rev.
																	PIPING & INSTRUMENTATION DIAGRAM FOR CRYSTALLIZATION SECTION (PART 4)		

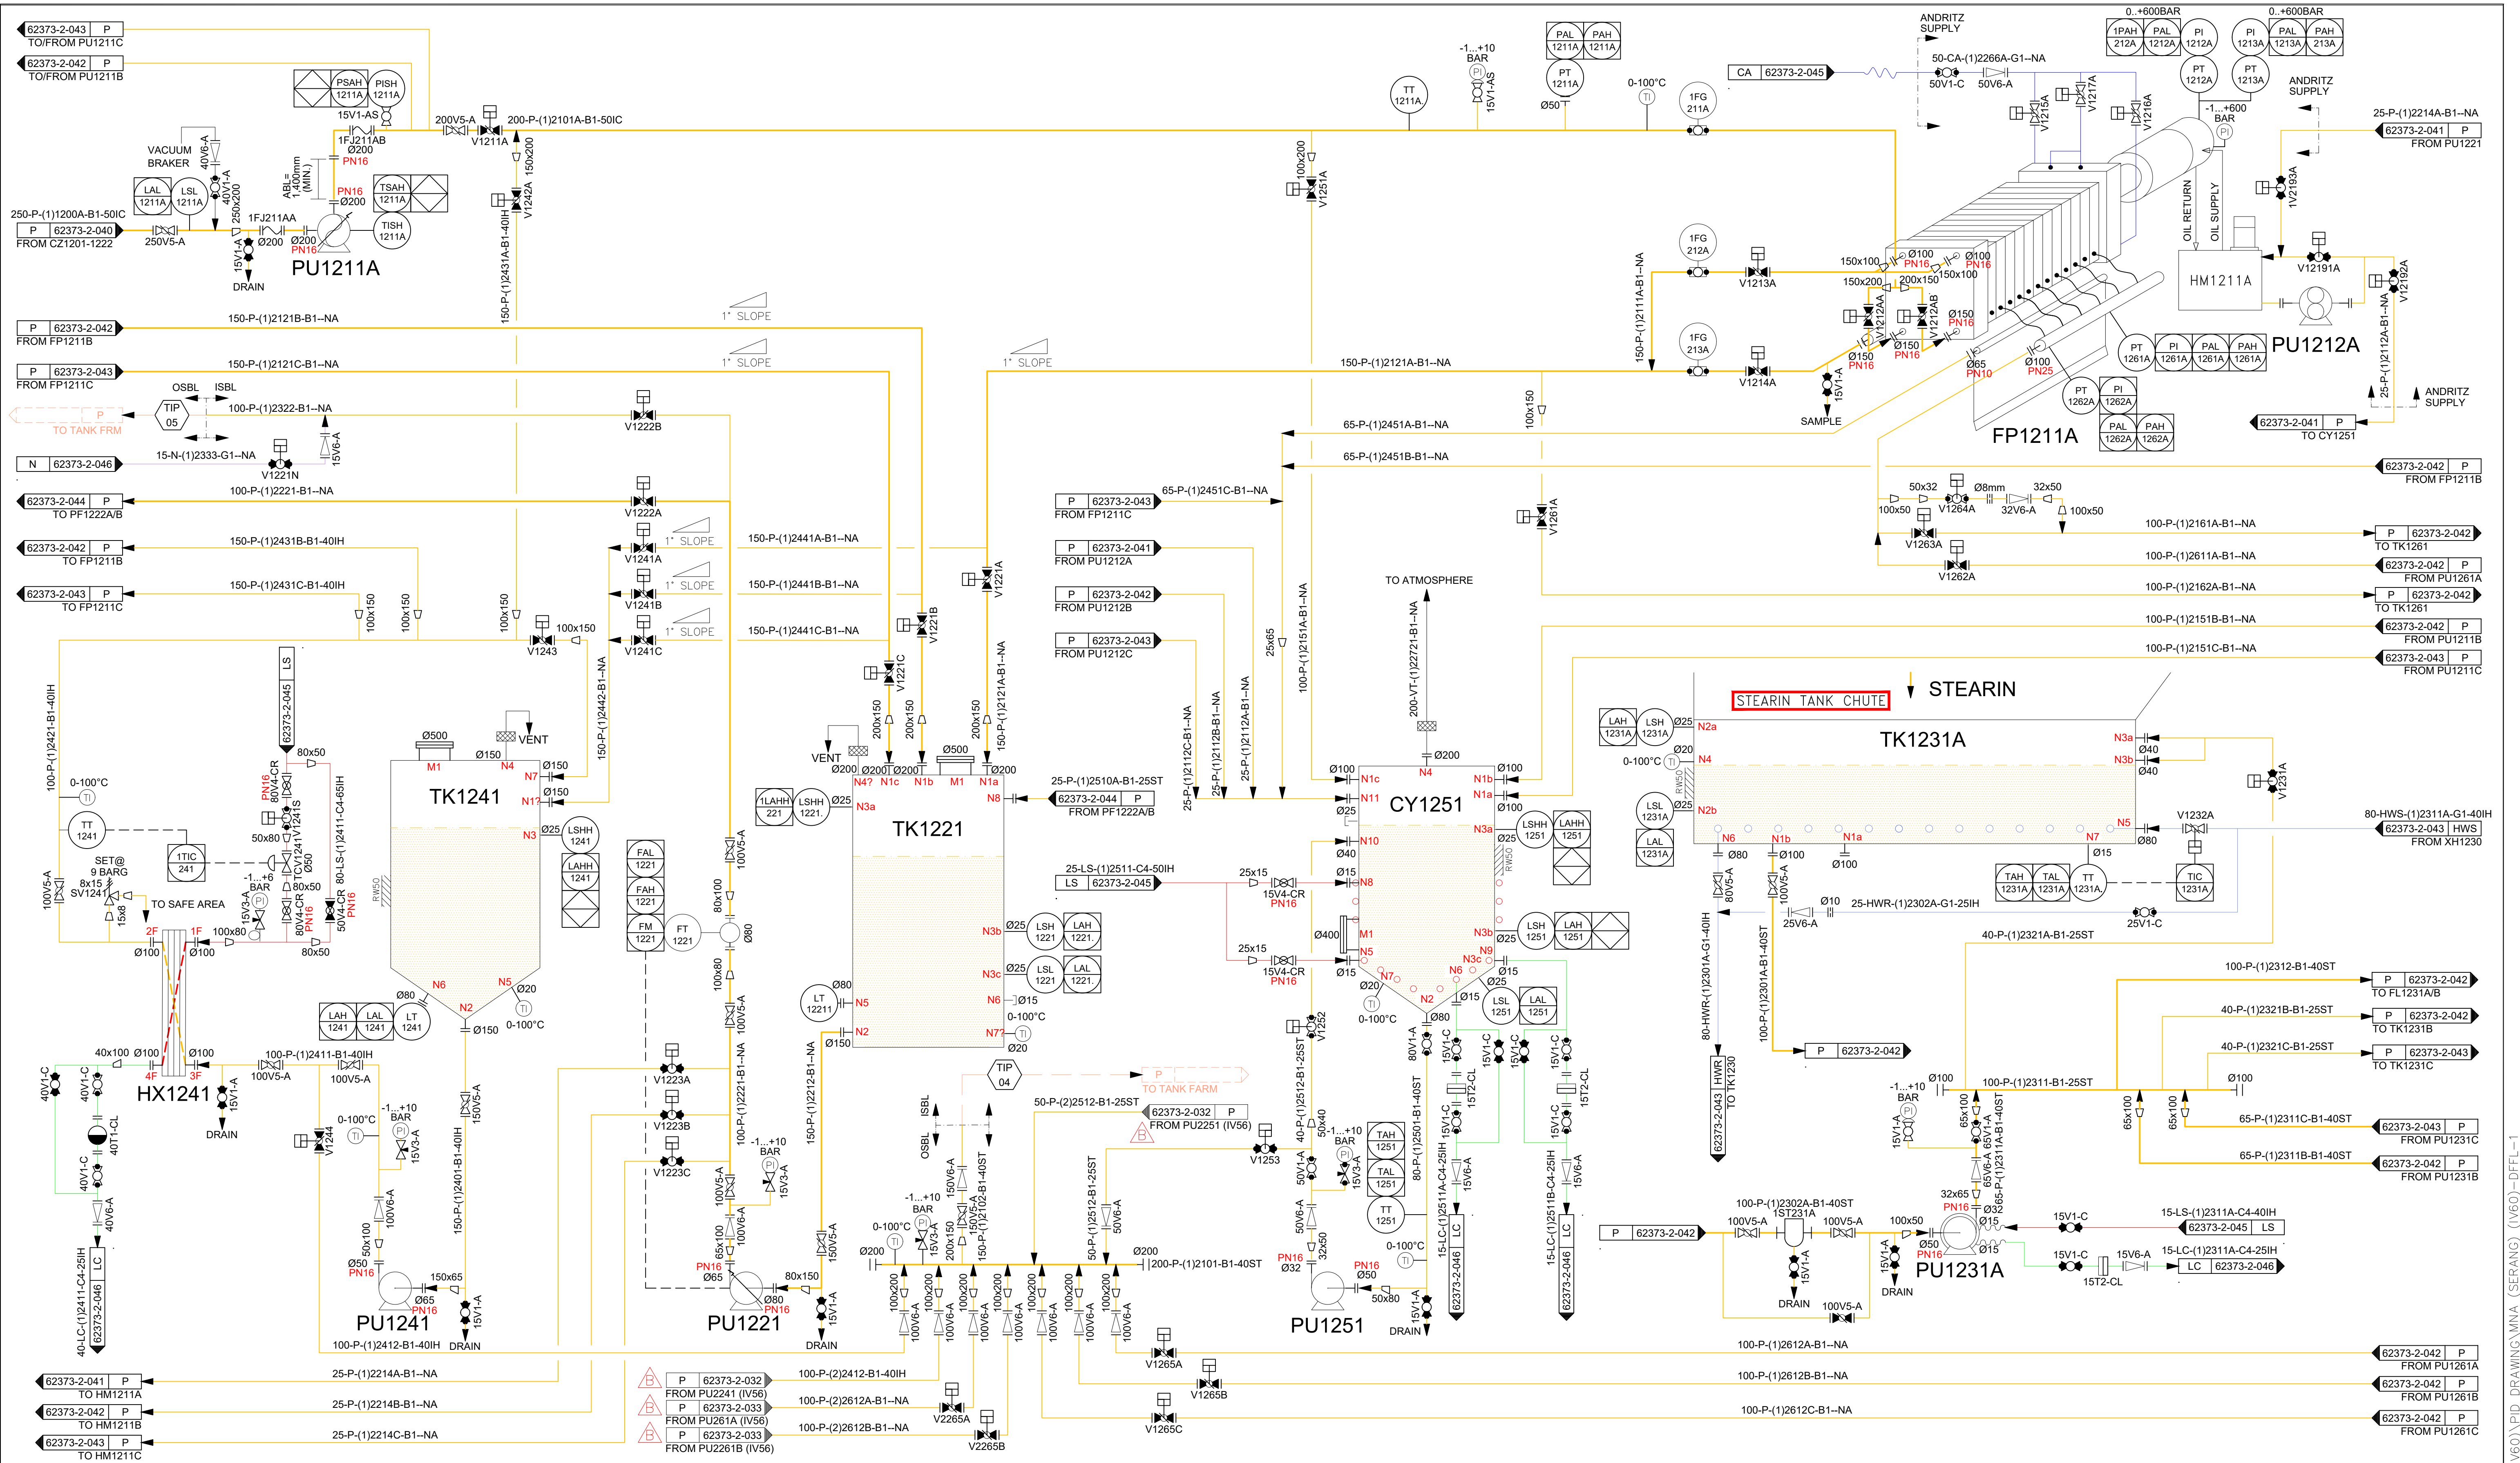

NOTES										This drawing is the property of LIPICO Technologies Pte Ltd. Total or partial reproduction or utilization of this document is forbidden without prior written authorization of LIPICO Technologies Pte Ltd.	Customer PT. MULTIMAS NABATI ASAHAN (SERANG)				
													Scale : N.T.S.		
													Date : 080318		
													Drawn By : DZHAFRI		
													Checked :		
											Project Name		Approved :		
											1,500MTD DRY FRACTIONATION PLANT (IV60)		Sheet No. : Or		
											PIPING & INSTRUMENTATION DIAGRAM FOR FILTRATION SECTION (PART 1)		Drawing No. 62373-2-041		Rev. B

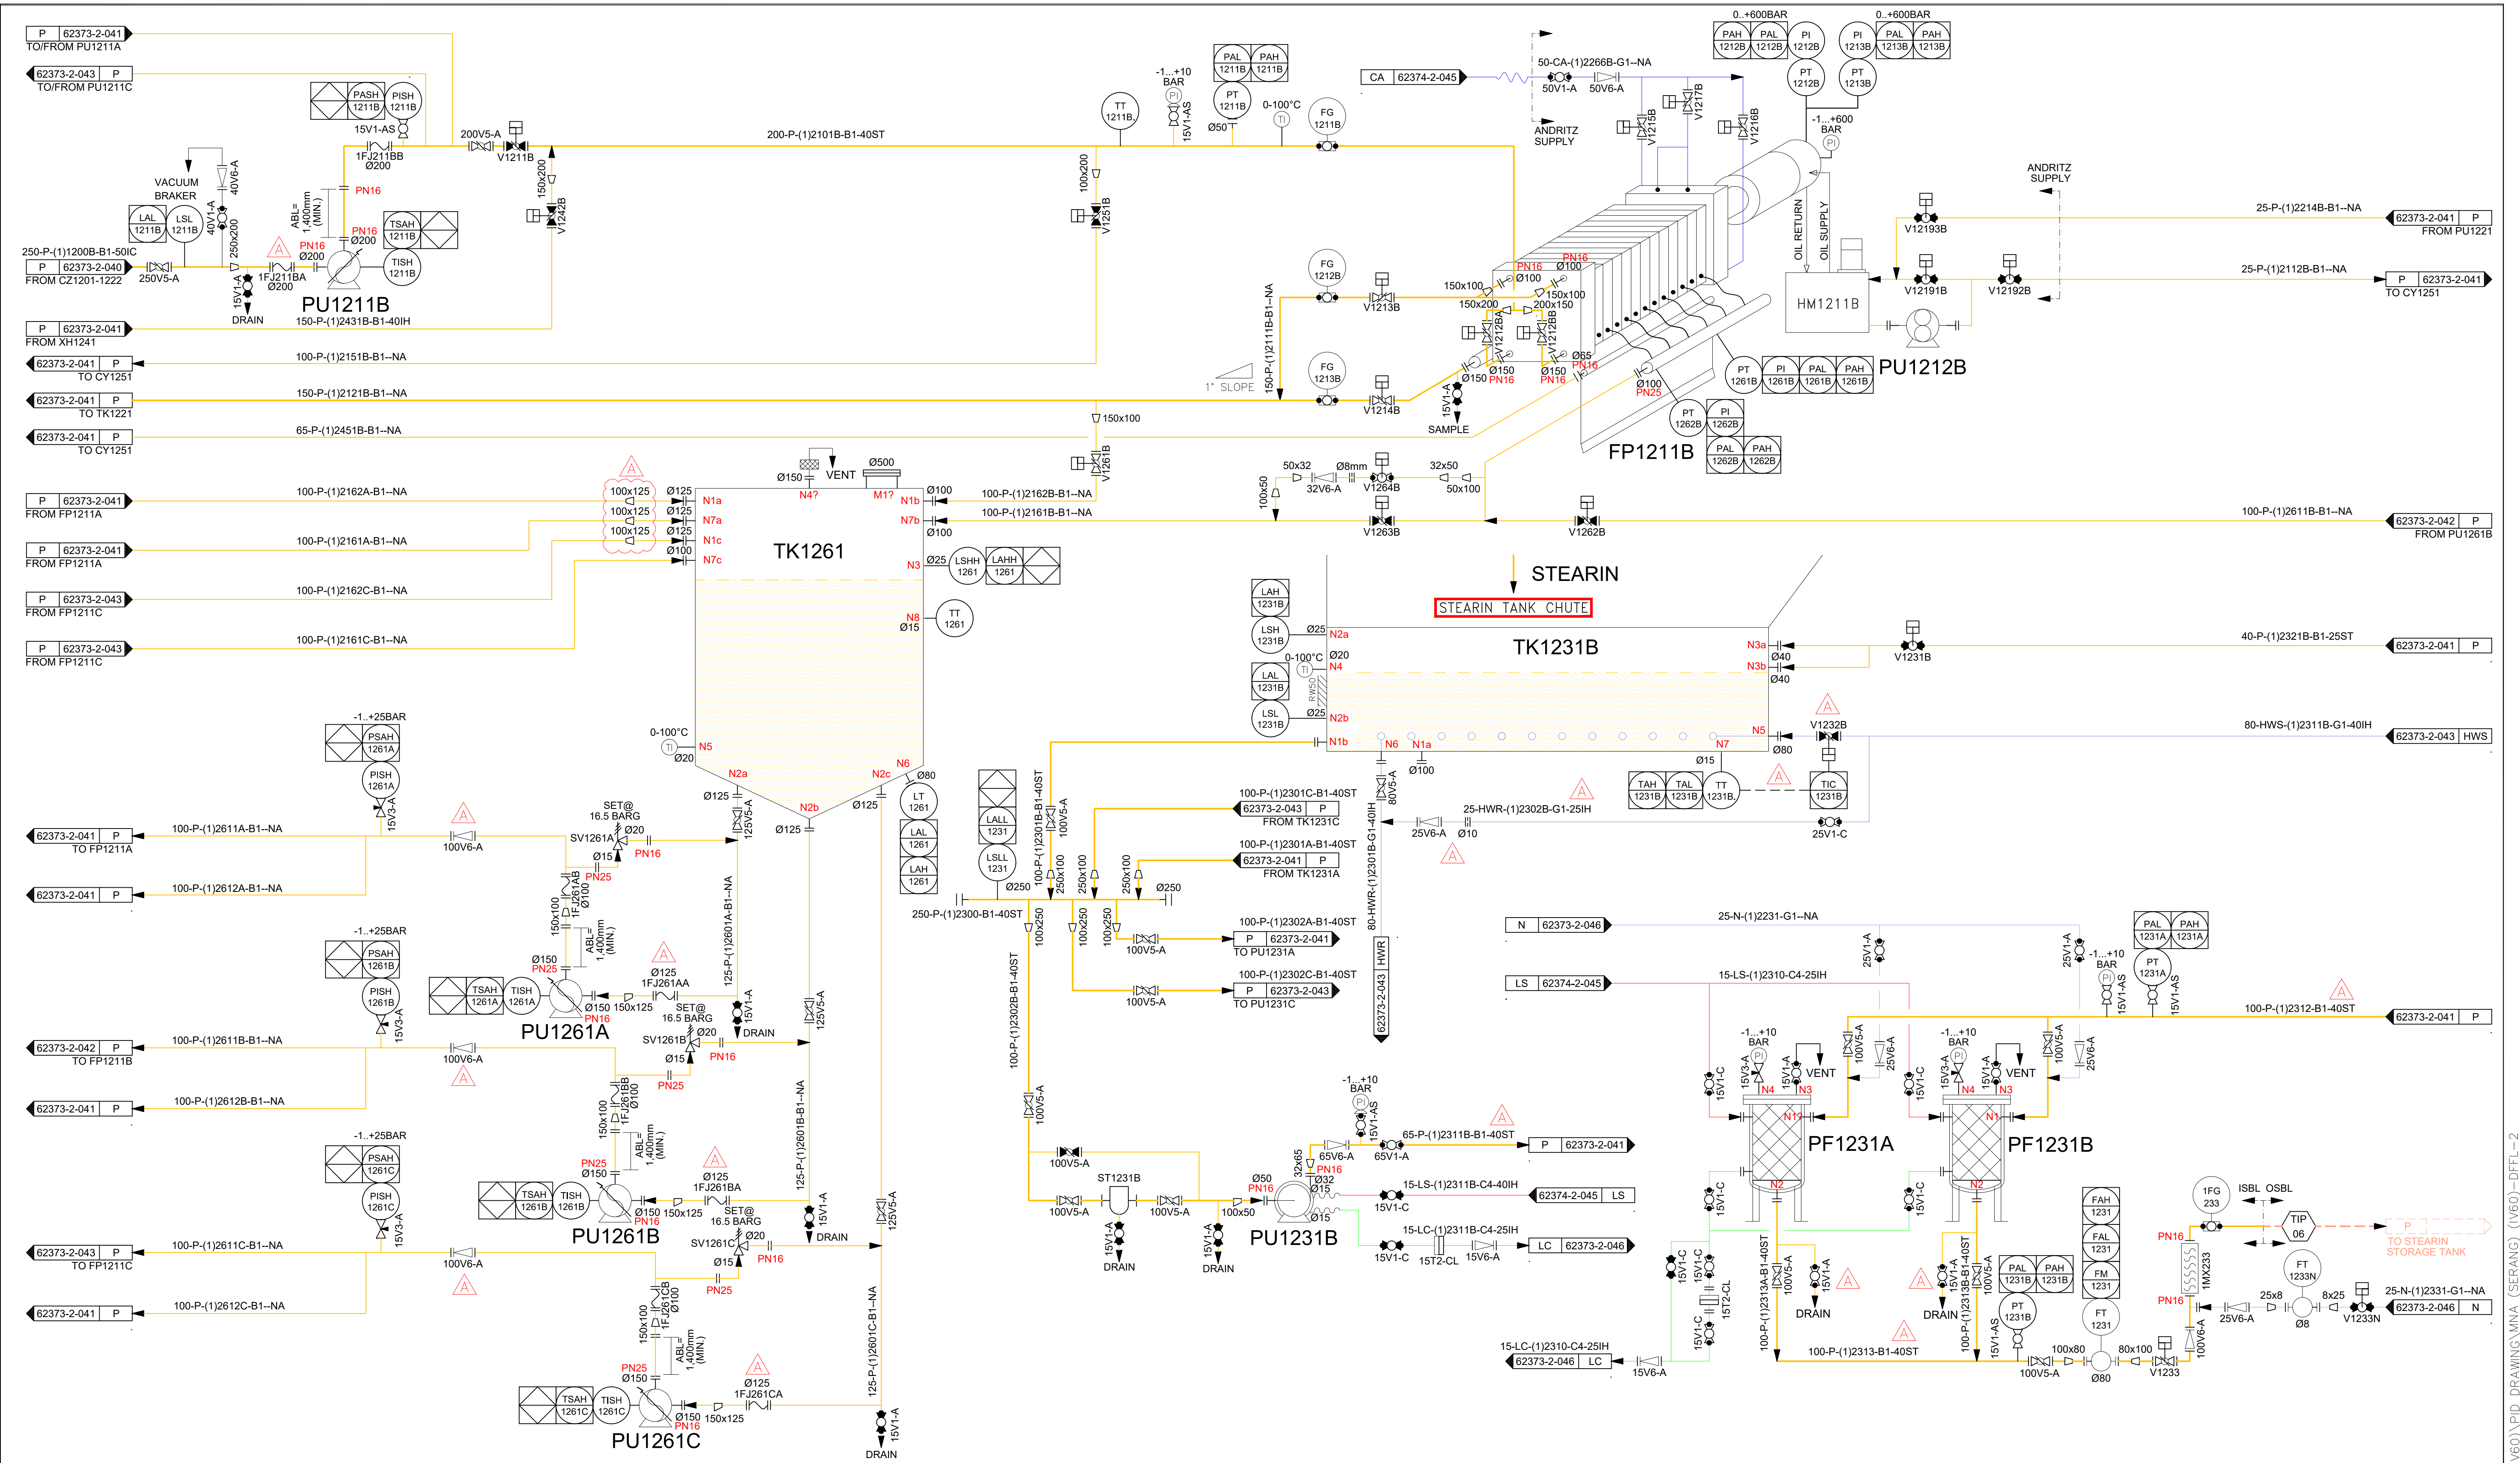


NOTES

NO.	DESCRIPTION	DATE	BY	CHK'D
1.	REVISED AS SHOWN	040918	DZF	JONATHAN
REVISIONS				

This drawing is the property of UPRCO Technologies Pte Ltd. Total or partial reproduction or utilization of this document is forbidden without prior written authorization of UPRCO Technologies Pte Ltd.

Customer PT. MULTIMAS NABATI ASAHAN (SERANG)	
	Scale : N.T.S.
Date : 080318	Drawn By : DZHAFRI
Checked :	Approved :
Project Name 1,500MTD DRY FRACTIONATION PLANT (IV60)	Sheet No. : Of
PIPING & INSTRUMENTATION DIAGRAM FOR FILTRATION SECTION (PART 2)	Drawing No. 62373-2-042 Rev. A

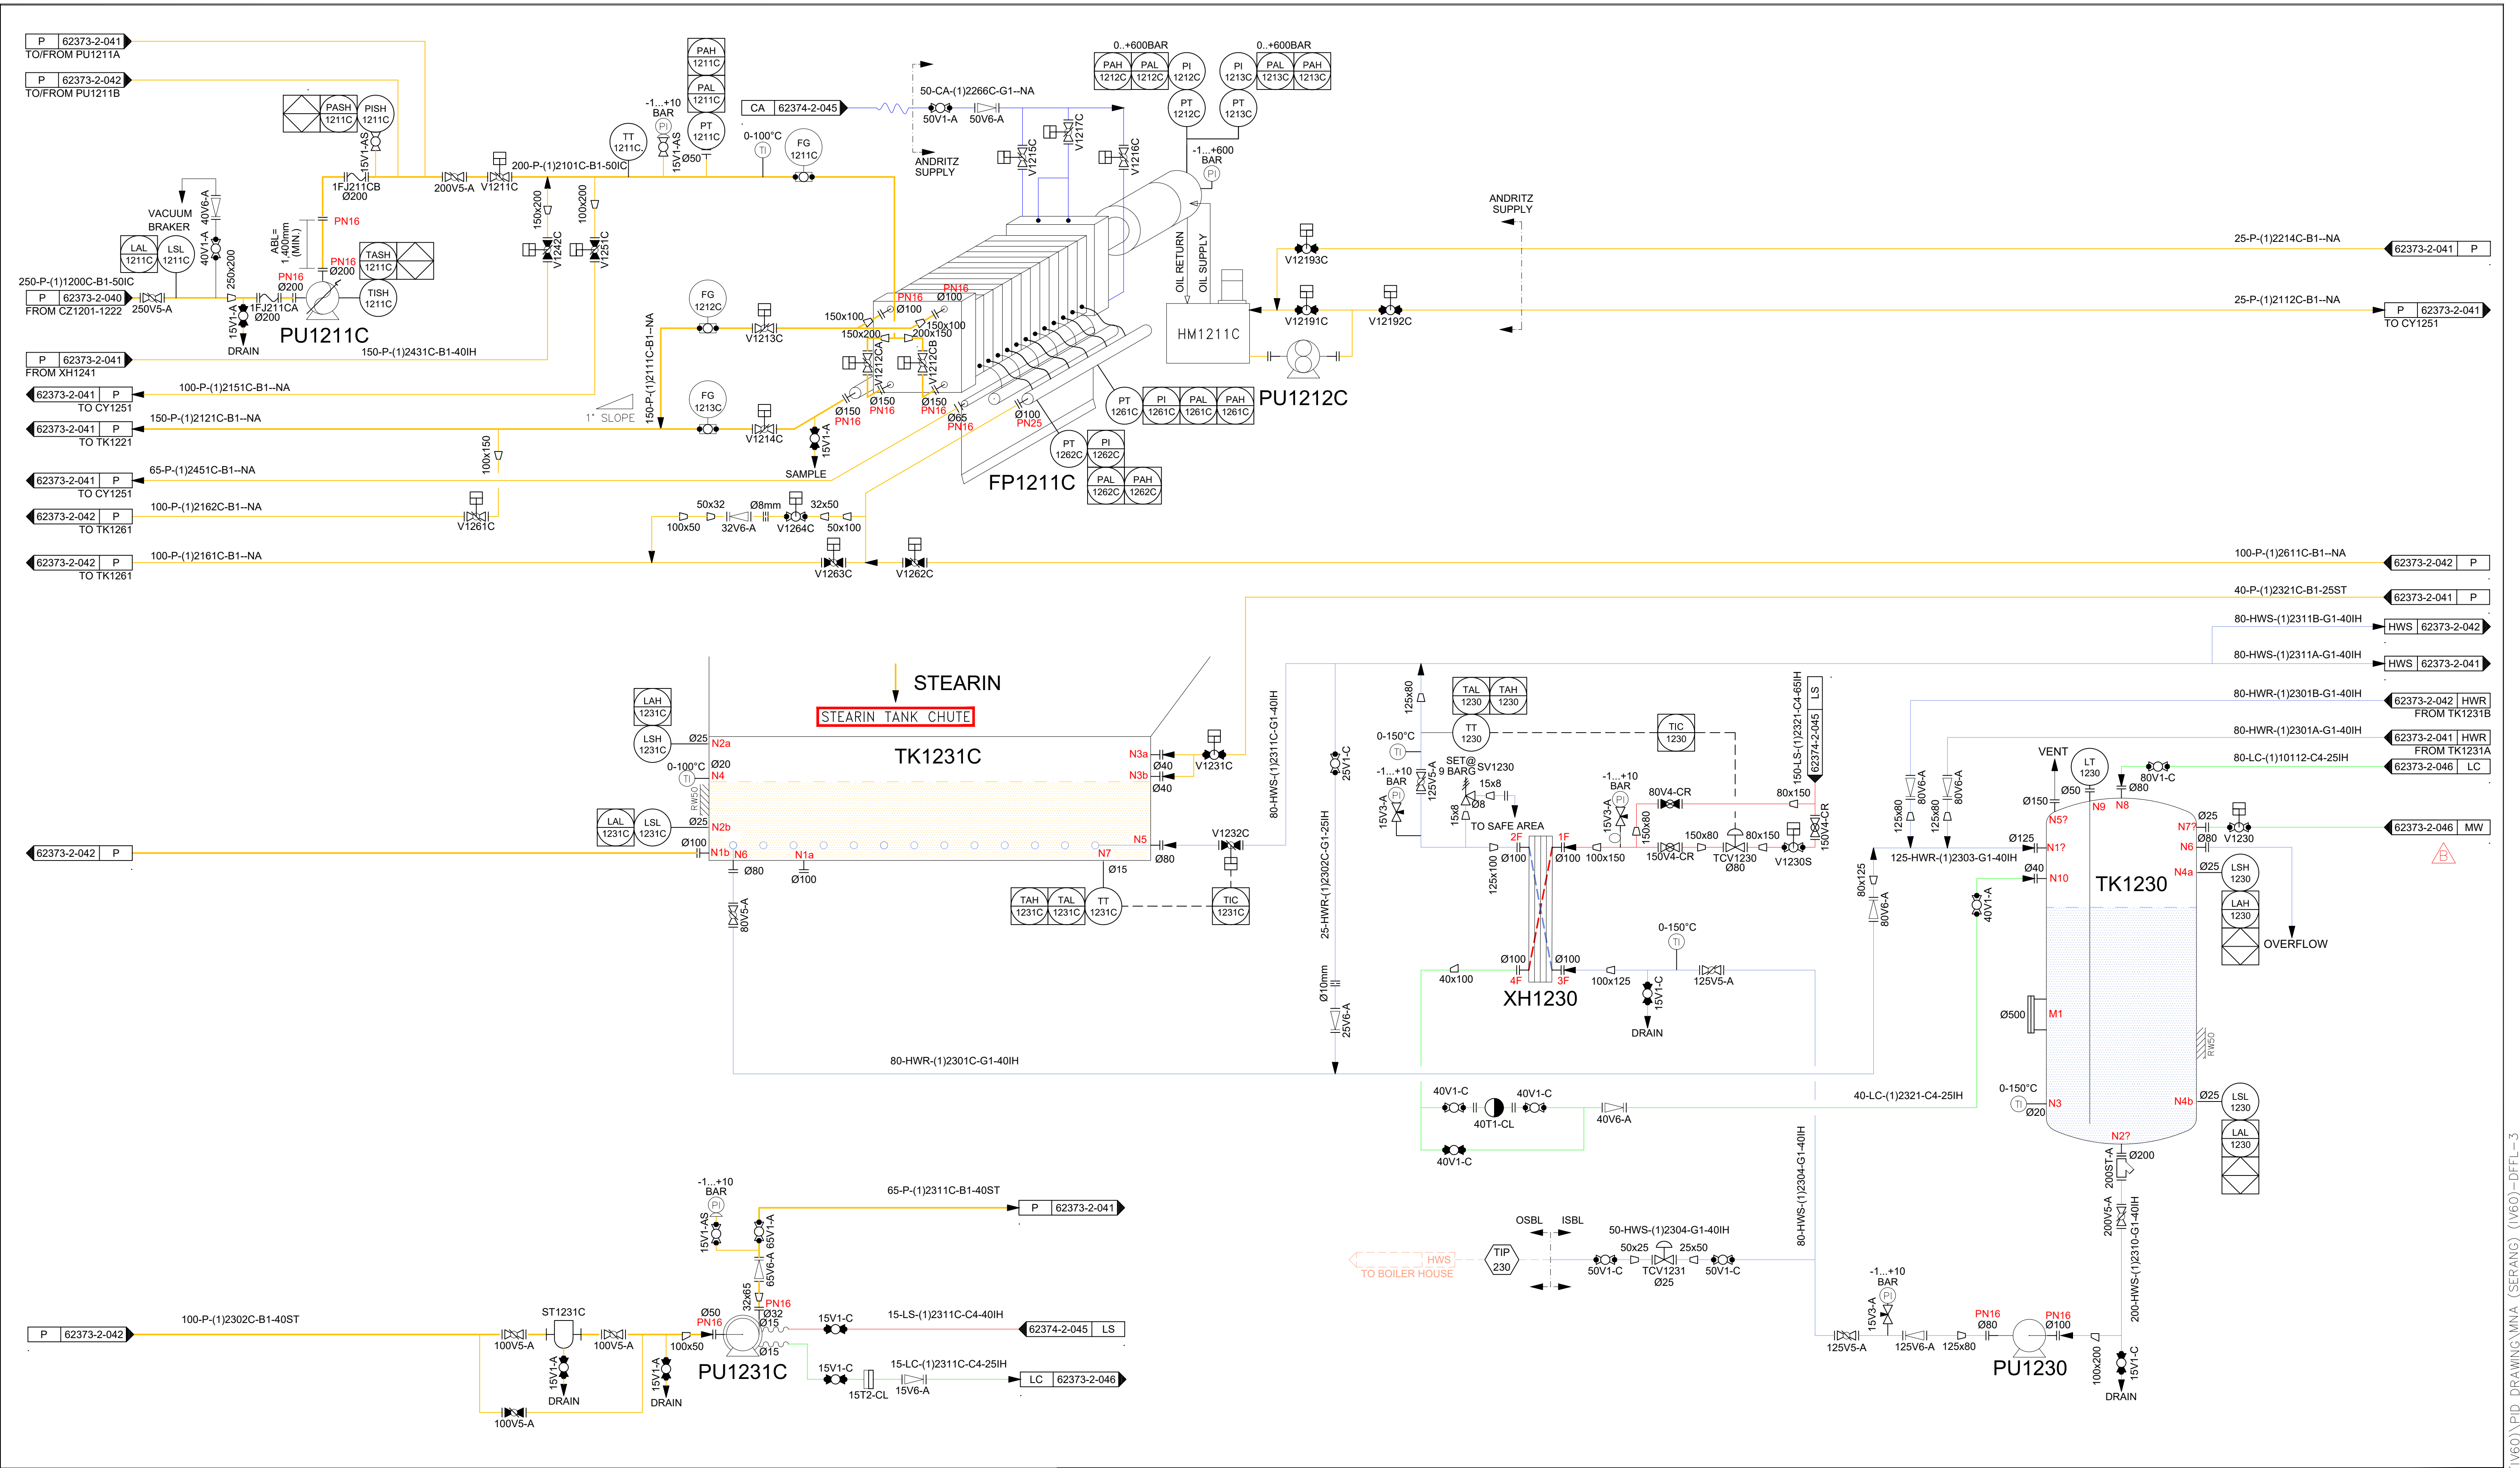


NOTES

NO.	DESCRIPTION	DATE	BY	CHK'D
2.	REVISED AS SHOWN 	041018	DZF	JONATHAN
1.	REVISED AS SHOWN 	040918	DZF	JONATHAN
REVISIONS				

This drawing is the property of UPRCO Technologies Pte Ltd. Total or partial reproduction or utilization of this document is forbidden without prior written authorization of UPRCO Technologies Pte Ltd.

Customer PT. MULTIMAS NABATI ASAHAN (SERANG)		Scale : N.T.S.
		Date : 080318
		Drawn By : DZHAFRI
Project Name 1,500MTD DRY FRACTIONATION PLANT (IV60)		Checked :
PIPING & INSTRUMENTATION DIAGRAM FOR FILTRATION SECTION (PART 3)		Approved :
		Sheet No. : Of
		Drawing No. 62373-2-043
		Rev. B

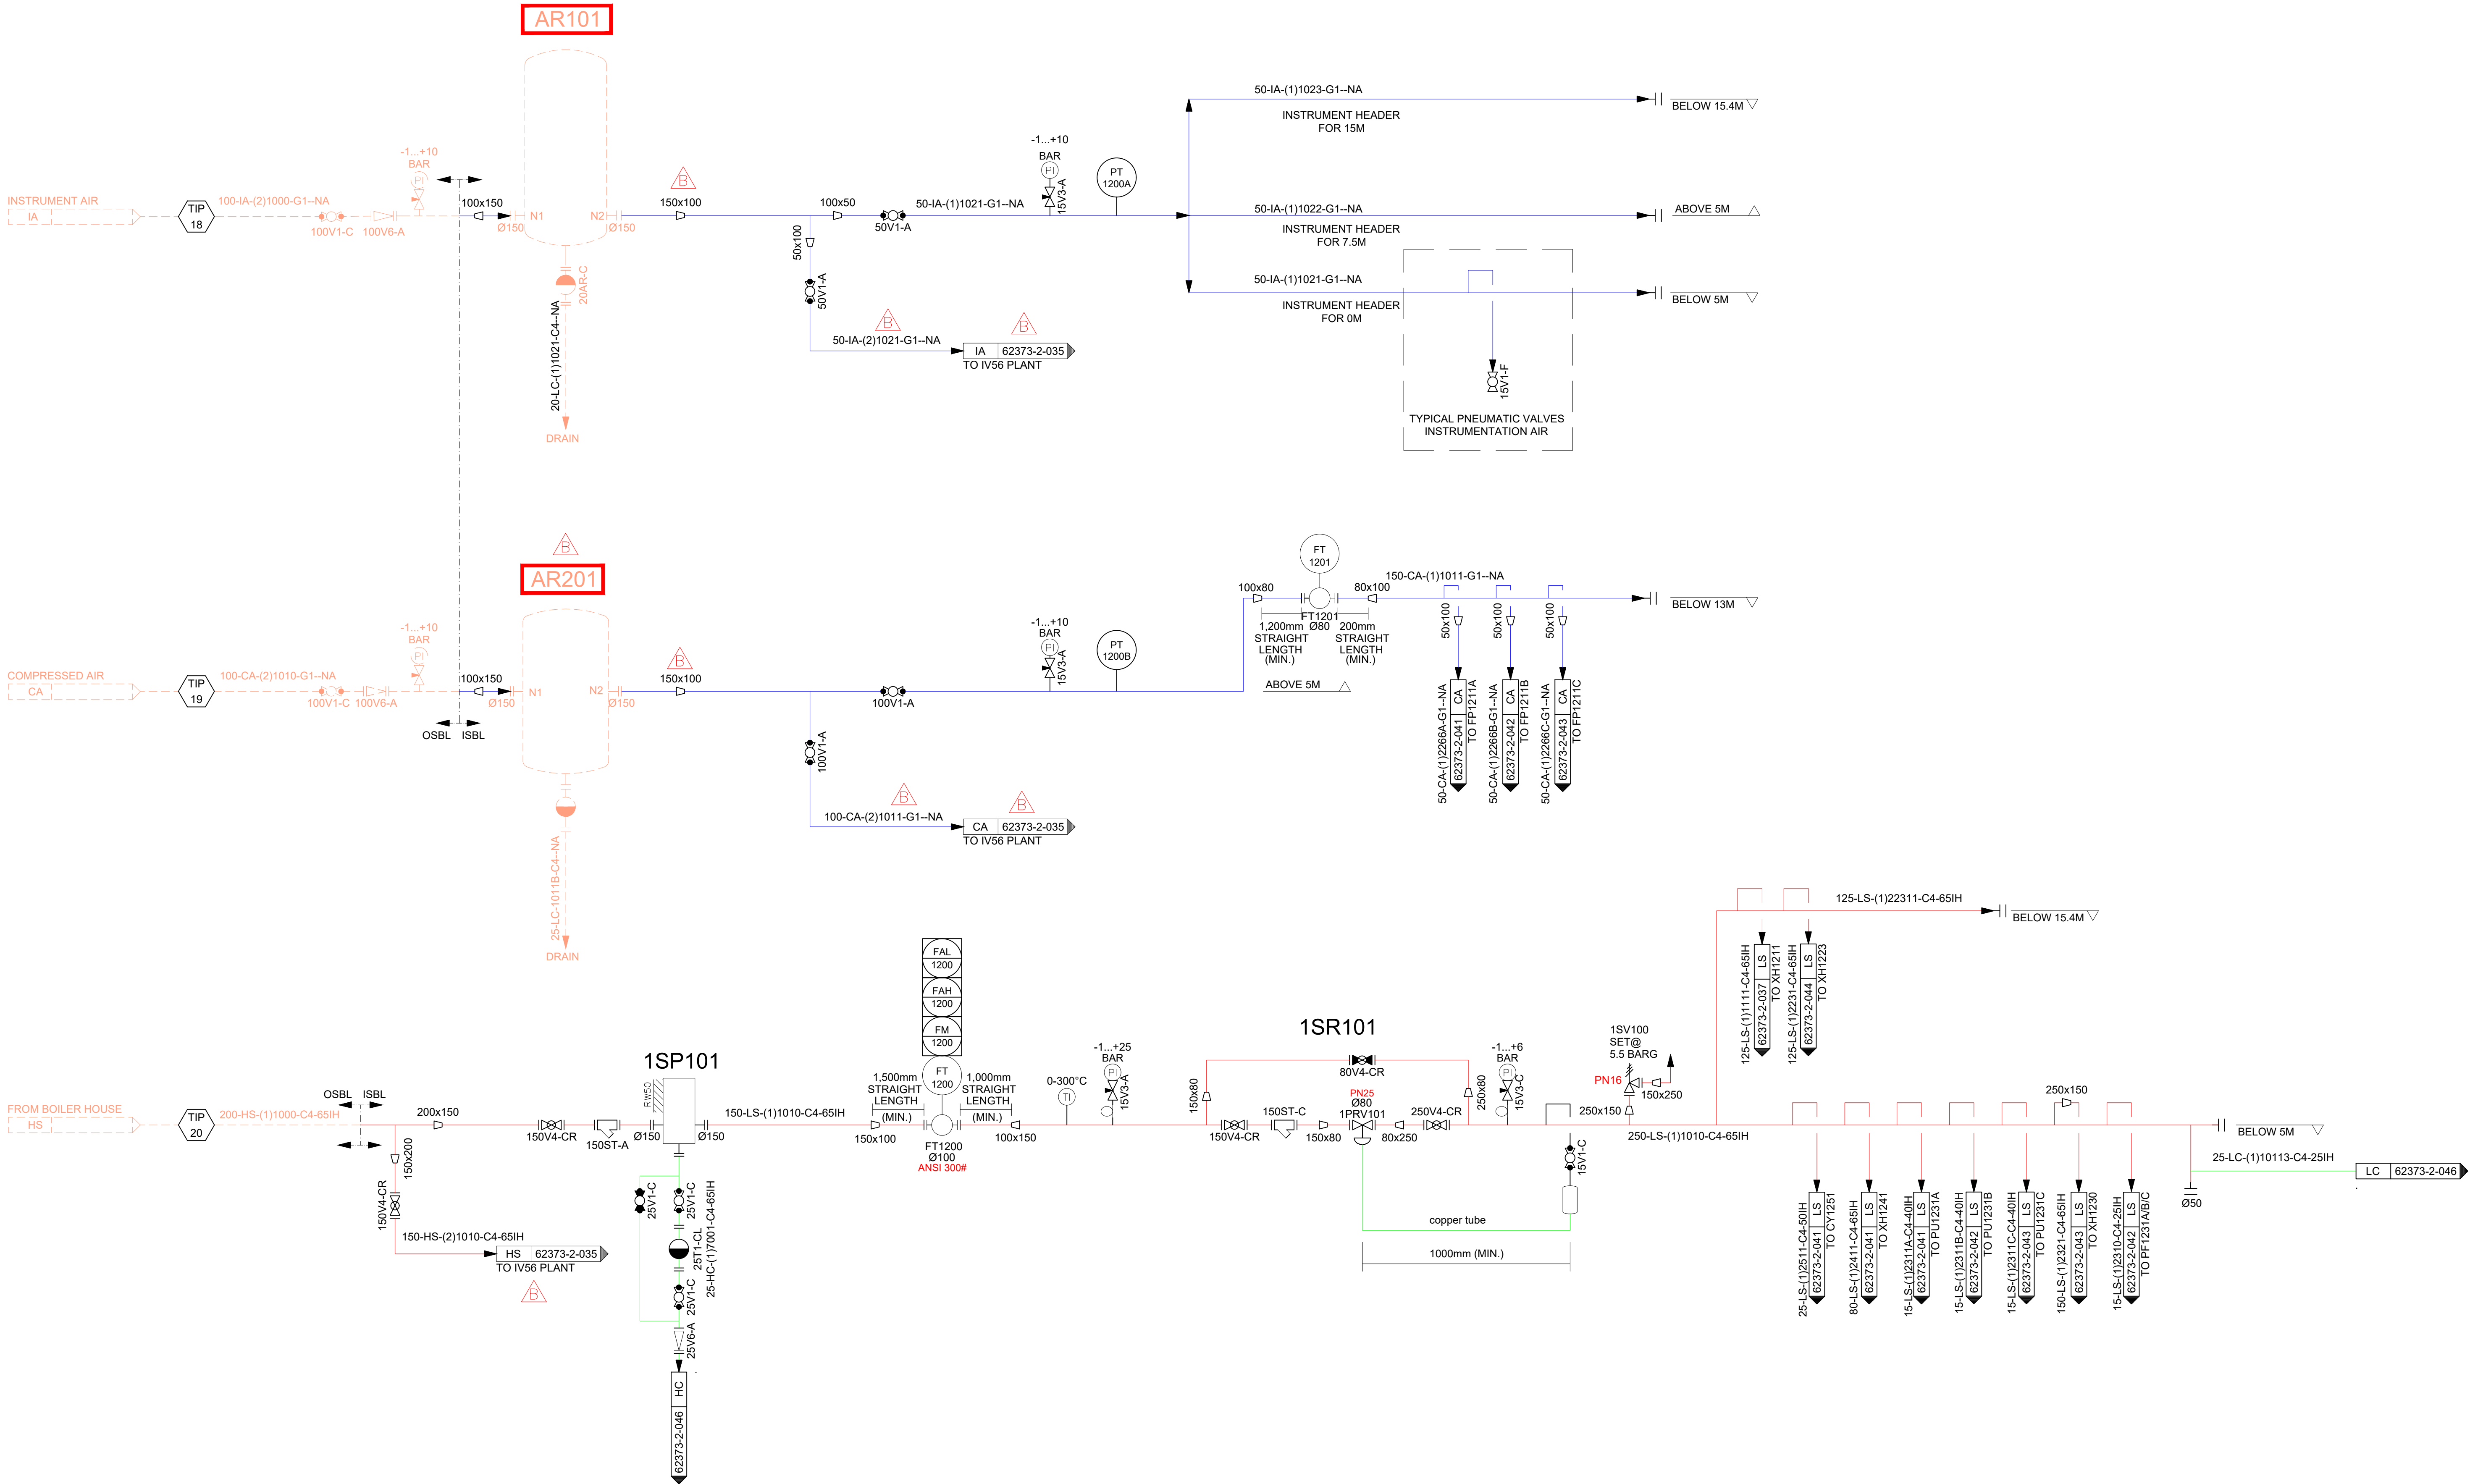




NOTE

1. - - - - : DENOTES ITEM NOT SUPPLIED BY LIPICO TECHNOLOGIES.
2. ALL FLANGES ARE ANSI 150# , UNLESS OTHERWISE STATED.
3. ALL THREADED CONNECTIONS ARE NPT STANDARD UNLESS OTHERWISE STATED.
4. PN10 , PN16 , PN25 , PN40 : DIN STANDARD.

NO.	DESCRIPTION	DATE	BY	CHK'D
2.	REVISED AS SHOWN	270918	DZF	
1.	REVISED AS SHOWN	120918	DZF	
REVISIONS				

This drawing is the property of LIPICO Technologies Pte Ltd. total or partial reproduction or utilization of this document is forbidden without prior written authorization of LIPICO Technologies Pte Ltd.

Customer			PT. MULTIMAS NABATI ASAHAN (SERANG)		
			Scale :	N.T.S.	
			Date :	020318	
			Drawn By :	DZHAFRI	
			Checked :		
Project Name 1,500MTD DRY FRACTIONATION PLANT (IV60)			Approved :		
			Sheet No. :	Of	
PIPING & INSTRUMENTATION DIAGRAM FOR UTILITIES SECTION (PART 1)			Drawing No.	62373-2-045	Rev.
					B

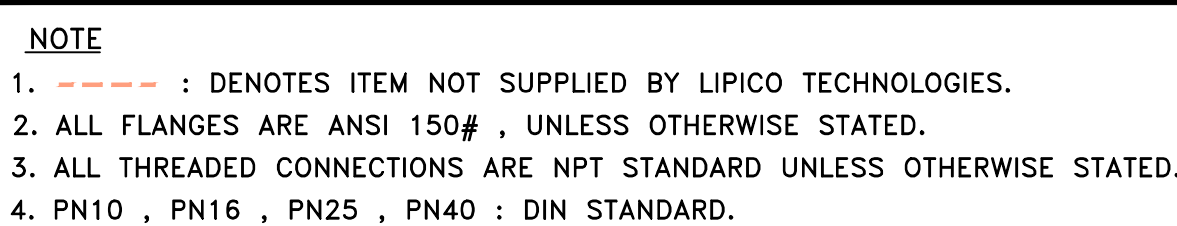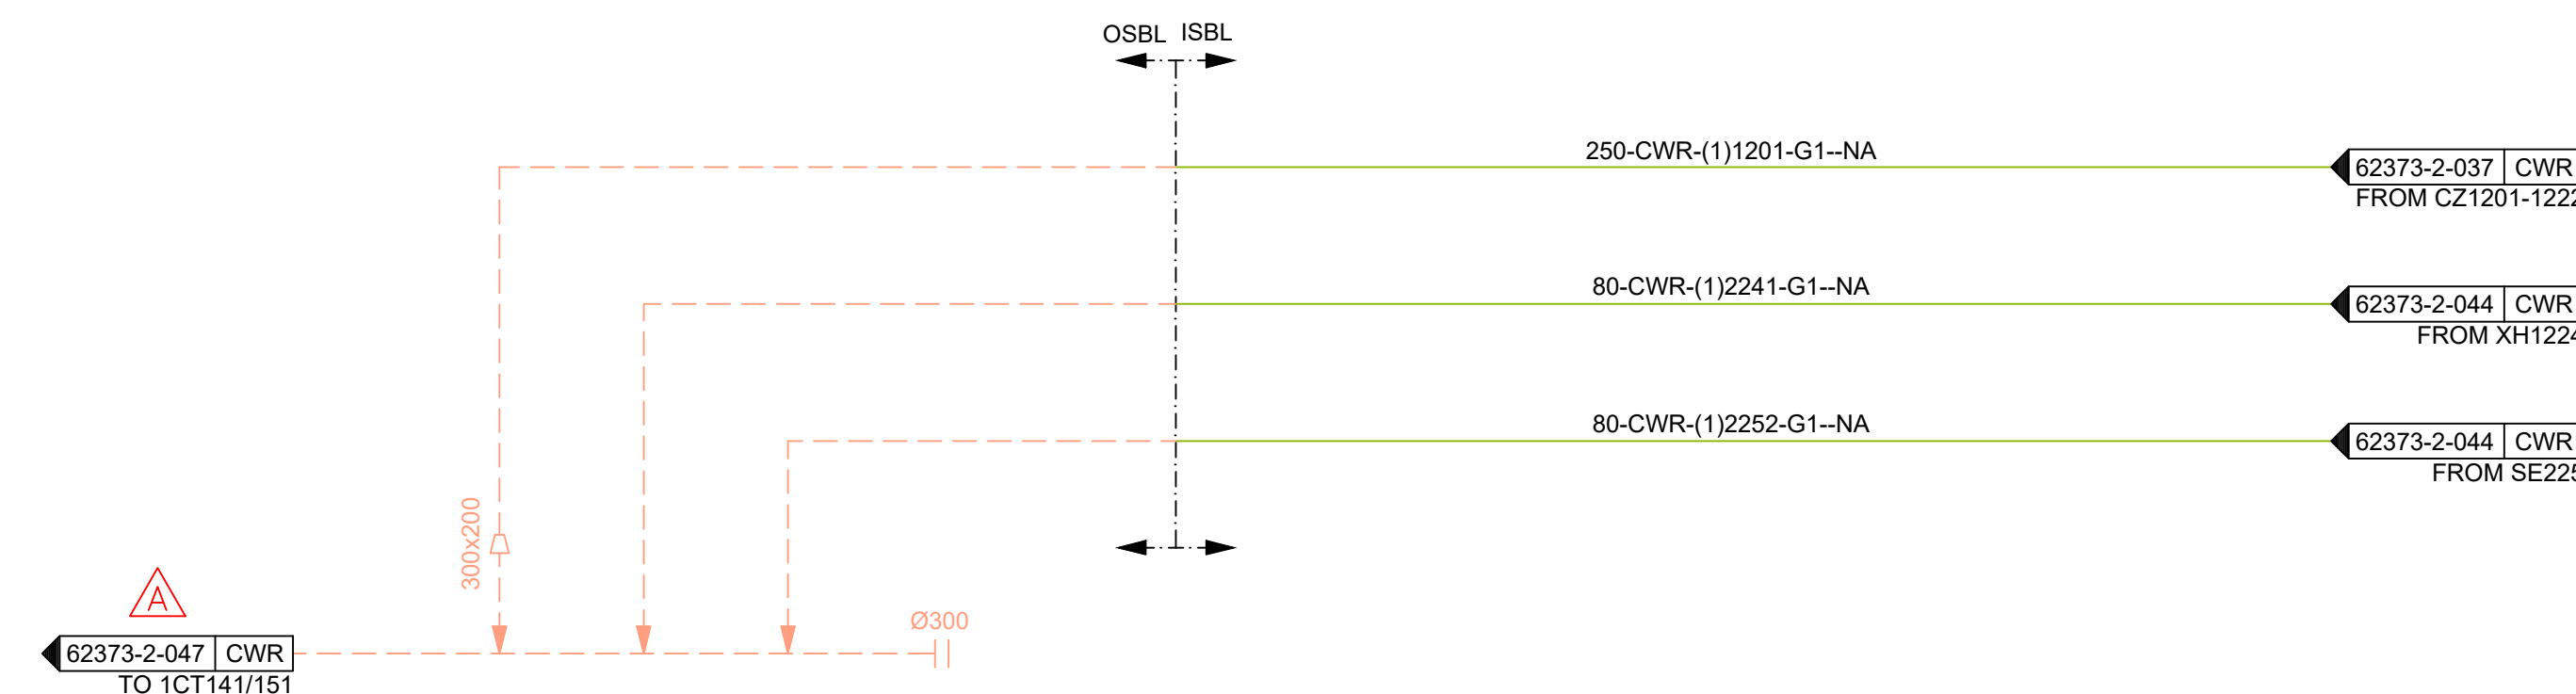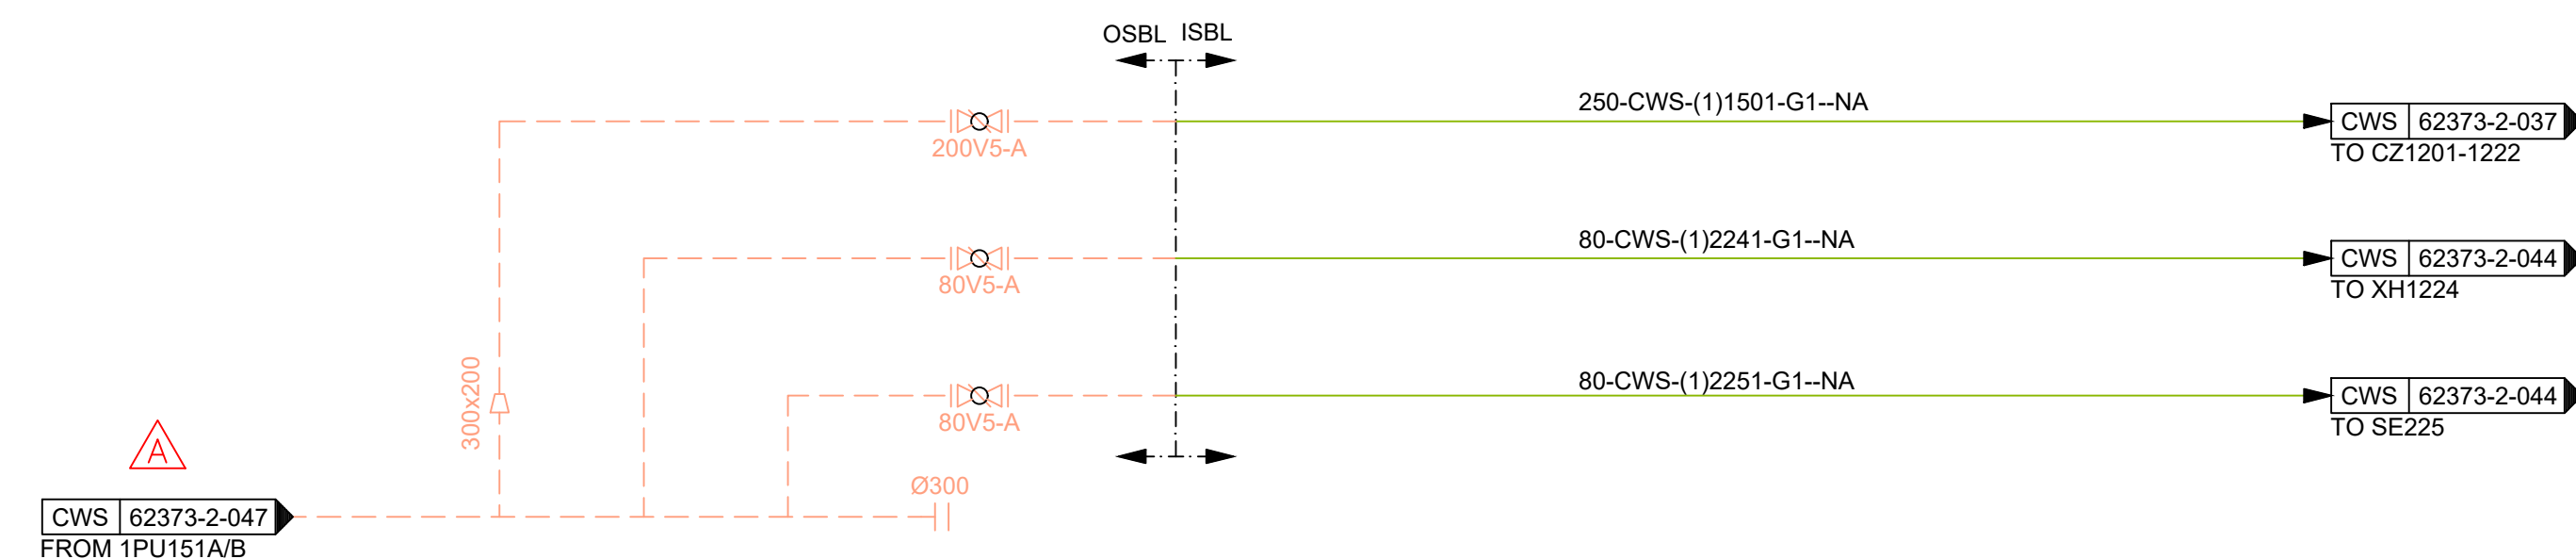

1.	REVISED AS SHOWN 	180718	DZF	
NO.	DESCRIPTION	DATE	BY	CHK'D
REVISIONS				

This drawing is the property of LUPICO Technologies Pte Ltd
total or partial reproduction or utilization of this document
is forbidden without prior written authorization of LUPICO
Technologies Pte Ltd.

Customer		
PT. MULTIMAS NABATI ASAHAN (SERANG)		
	Scale :	N.T.S.
	Date :	050318
	Drawn By :	DZHAFRI
	Checked :	
	Approved :	
Project Name		
1,500MTD DRY FRACTIONATION PLANT (IV60)		
PIPING & INSTRUMENTATION DIAGRAM FOR UTILITIES SECTION (PART 2)	Drawing No.	Rev.
	62373-2-046	