


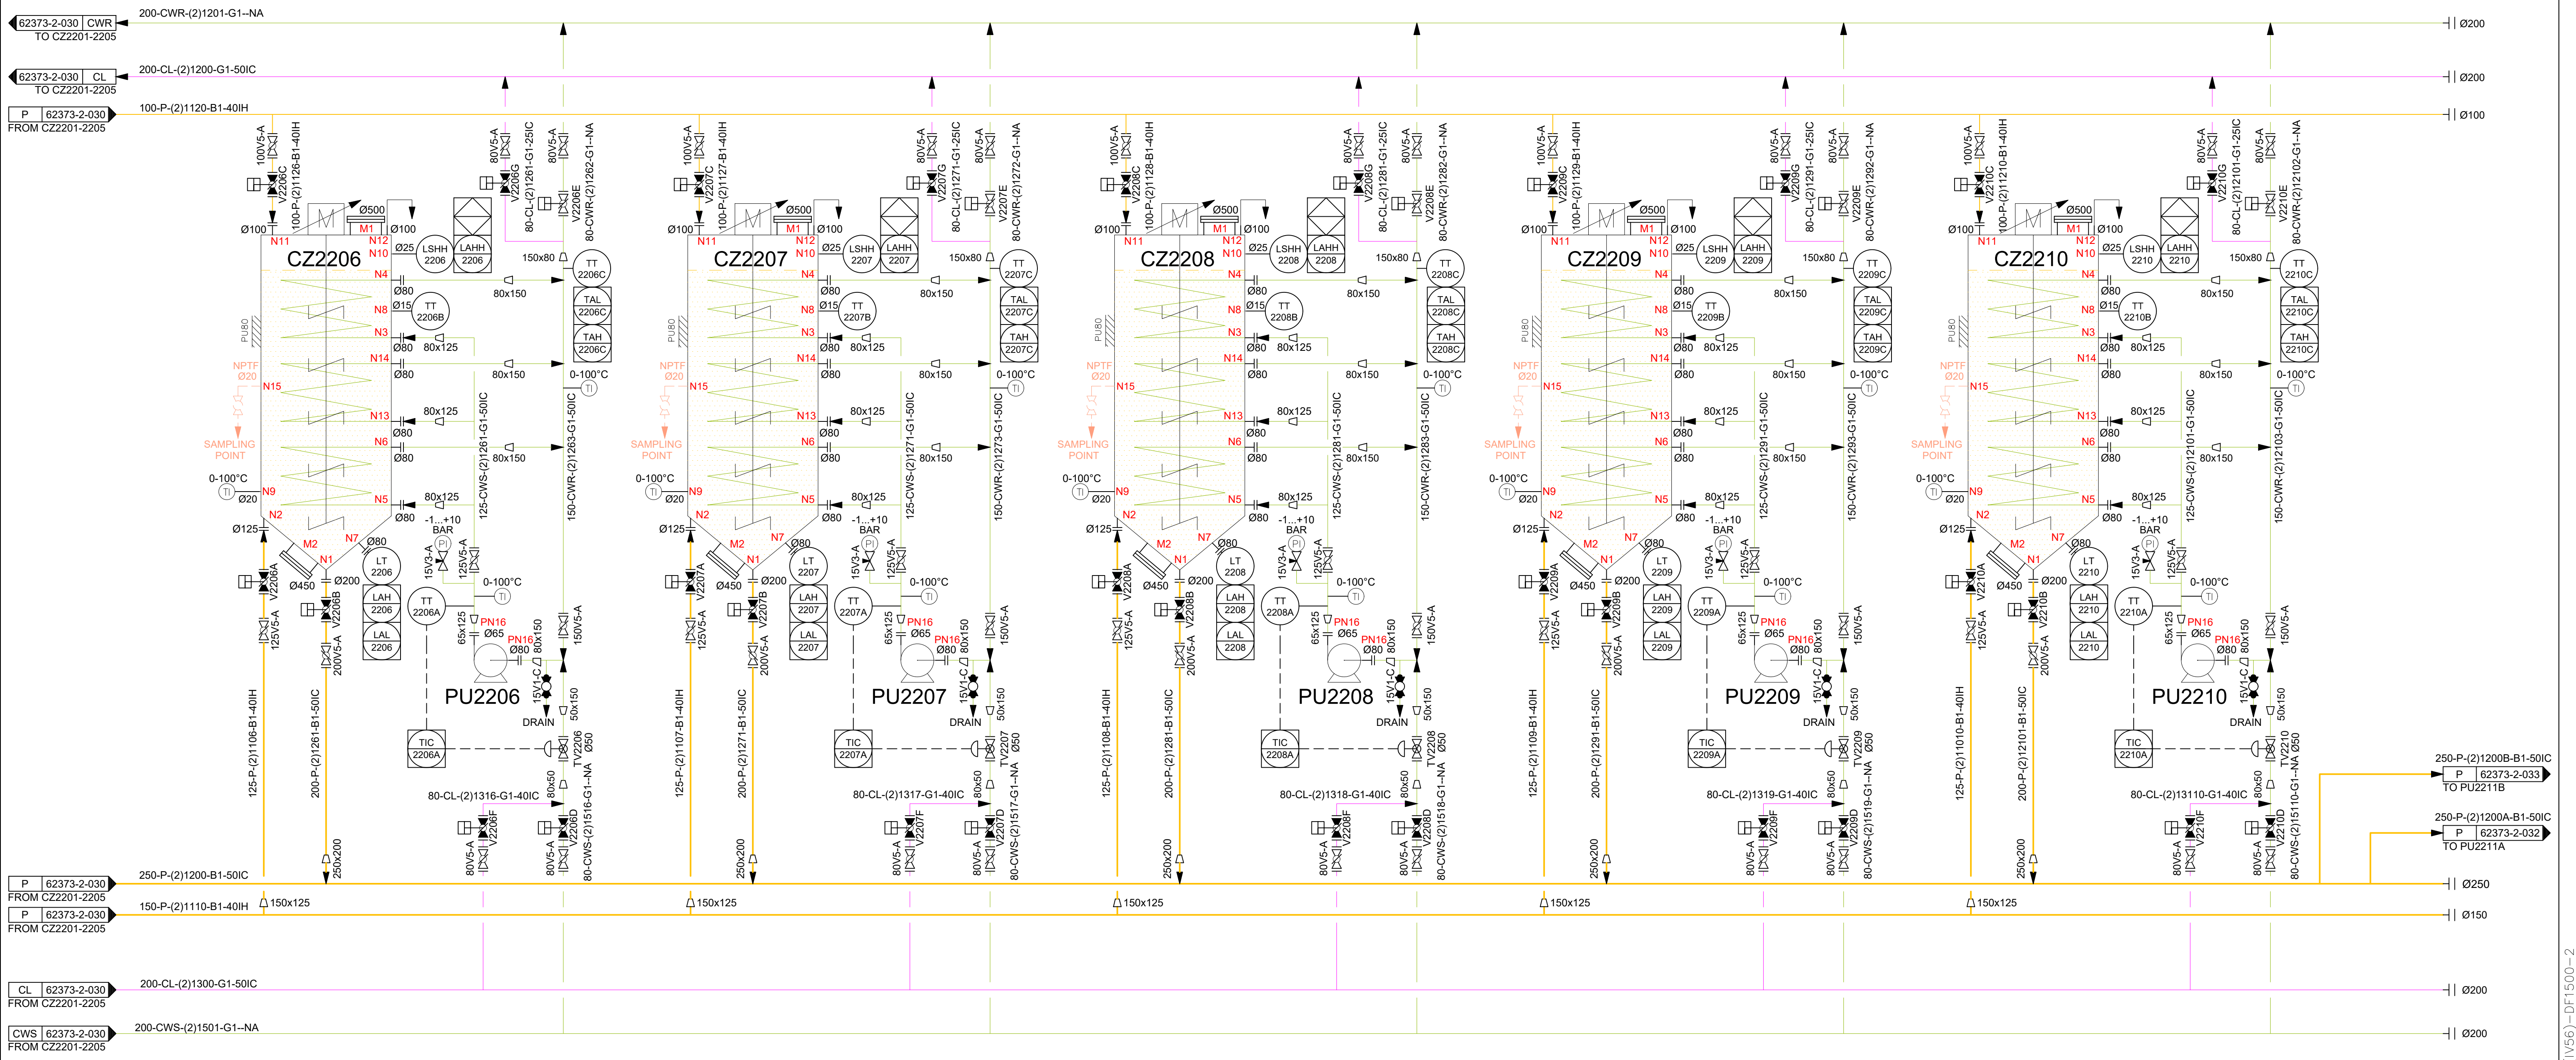

NOTES					This drawing is the property of LIPICO Technologies Pte Ltd total or partial reproduction or utilization of this document is forbidden without prior written authorization of LIPICO Technologies Pte Ltd.	Customer PT. MULTIMAS NABATI ASAHAN (SERANG)			
						 lipico		Scale : N.T.S.	
								Date : 130318	
								Drawn By : DZHAFRI	
								Checked :	
								Approved :	
						Project Name 1,500MTD DRY FRACTIONATION PLANT (IV56)			
						Sheet No. : Of			
						Drawing No. 62373-2-031		Rev.	



Scale : N.T.S.

Date : 130318


Drawn By : DZHAFRI

Checked :

Approved :

Sheet No. : Of

PIPING & INSTRUMENTATION DIAGRAM FOR
CRYSTALLIZATION (PART 2)

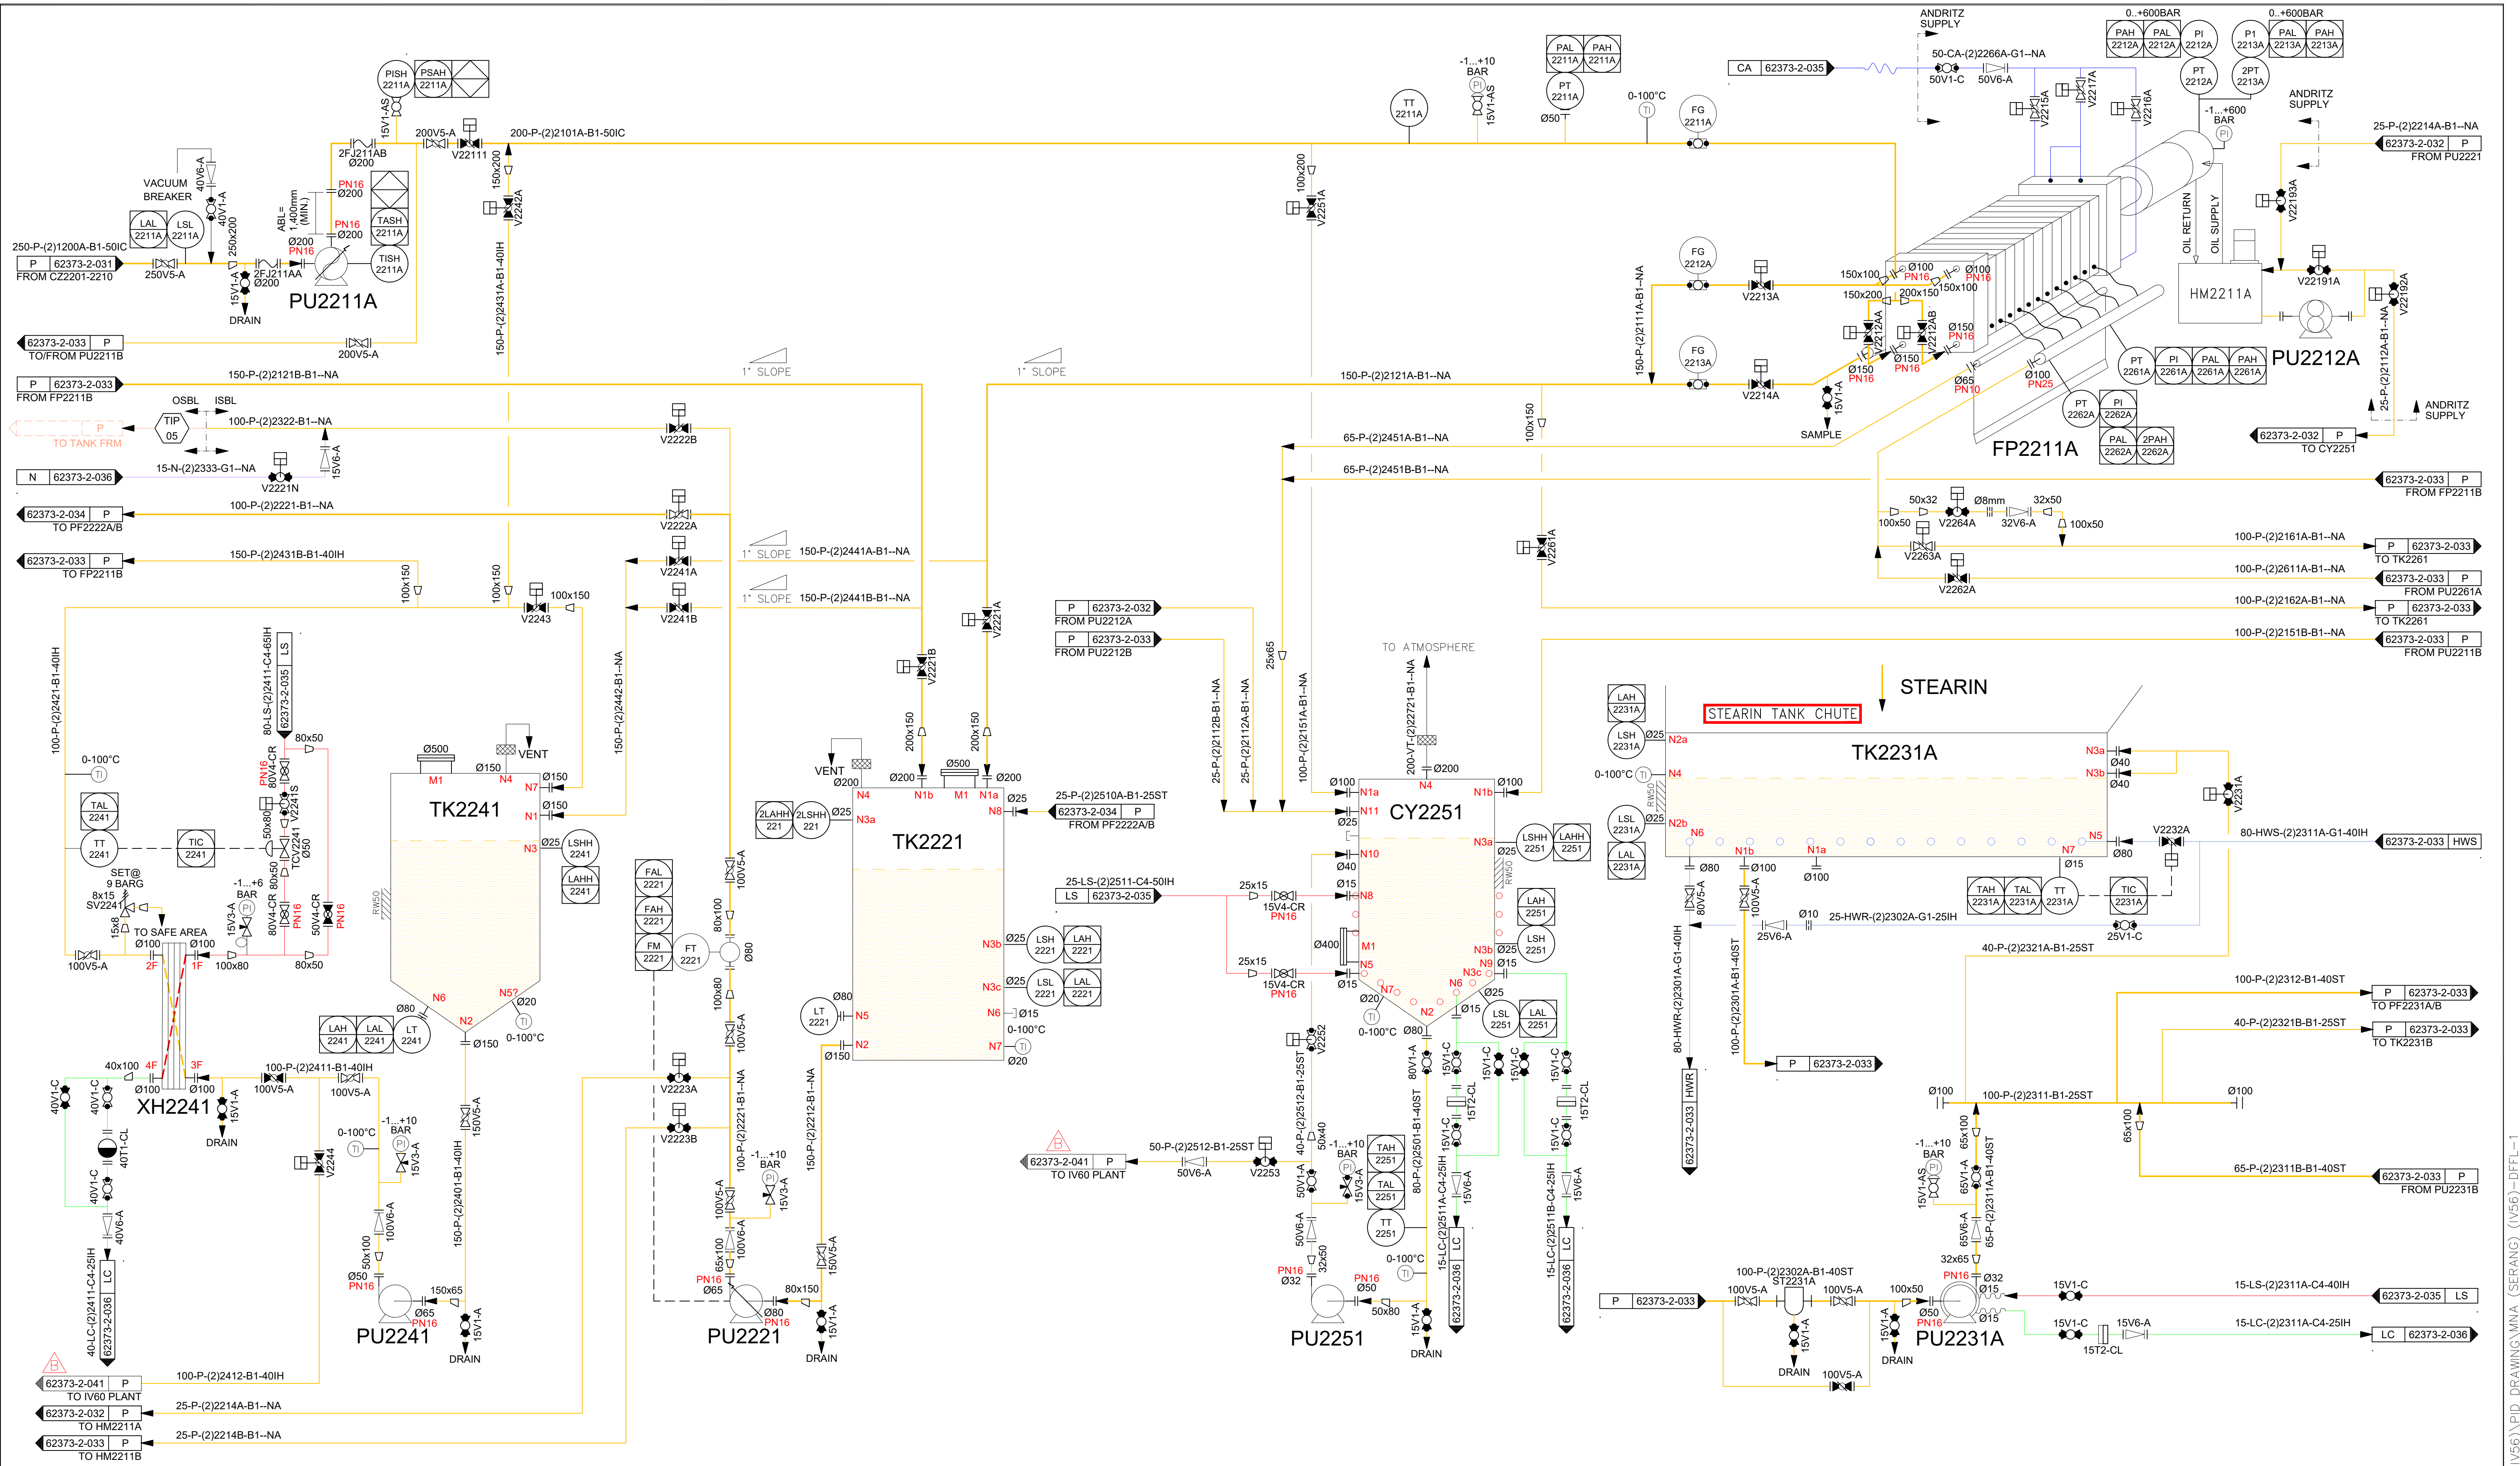


NOTES

NO.	DESCRIPTION	DATE	BY	CHK'D
2.	REVISED AS SHOWN 	270918	DZF	
1.	REVISED AS SHOWN 	040918	DZF	JONATHAN
NO.	DESCRIPTION	DATE	BY	CHK'D
REVISIONS				

This drawing is the property of UPMCO Technologies Pte Ltd. Total or partial reproduction or utilization of this document is forbidden without prior written authorization of UPMCO Technologies Pte Ltd.

Customer PT. MULTIMAS NABATI ASAHAN (SERANG)		Scale : N.T.S.
		Date : 140318
Project Name 1,500MTD DRY FRACTIONATION PLANT (IV56)		Drawn By : DZHAFRI
PIPING & INSTRUMENTATION DIAGRAM FOR FILTRATION SECTION (PART 1)		Checked :
		Approved :
		Sheet No. : Or
		Drawing No. 62373-2-032
		Rev. B

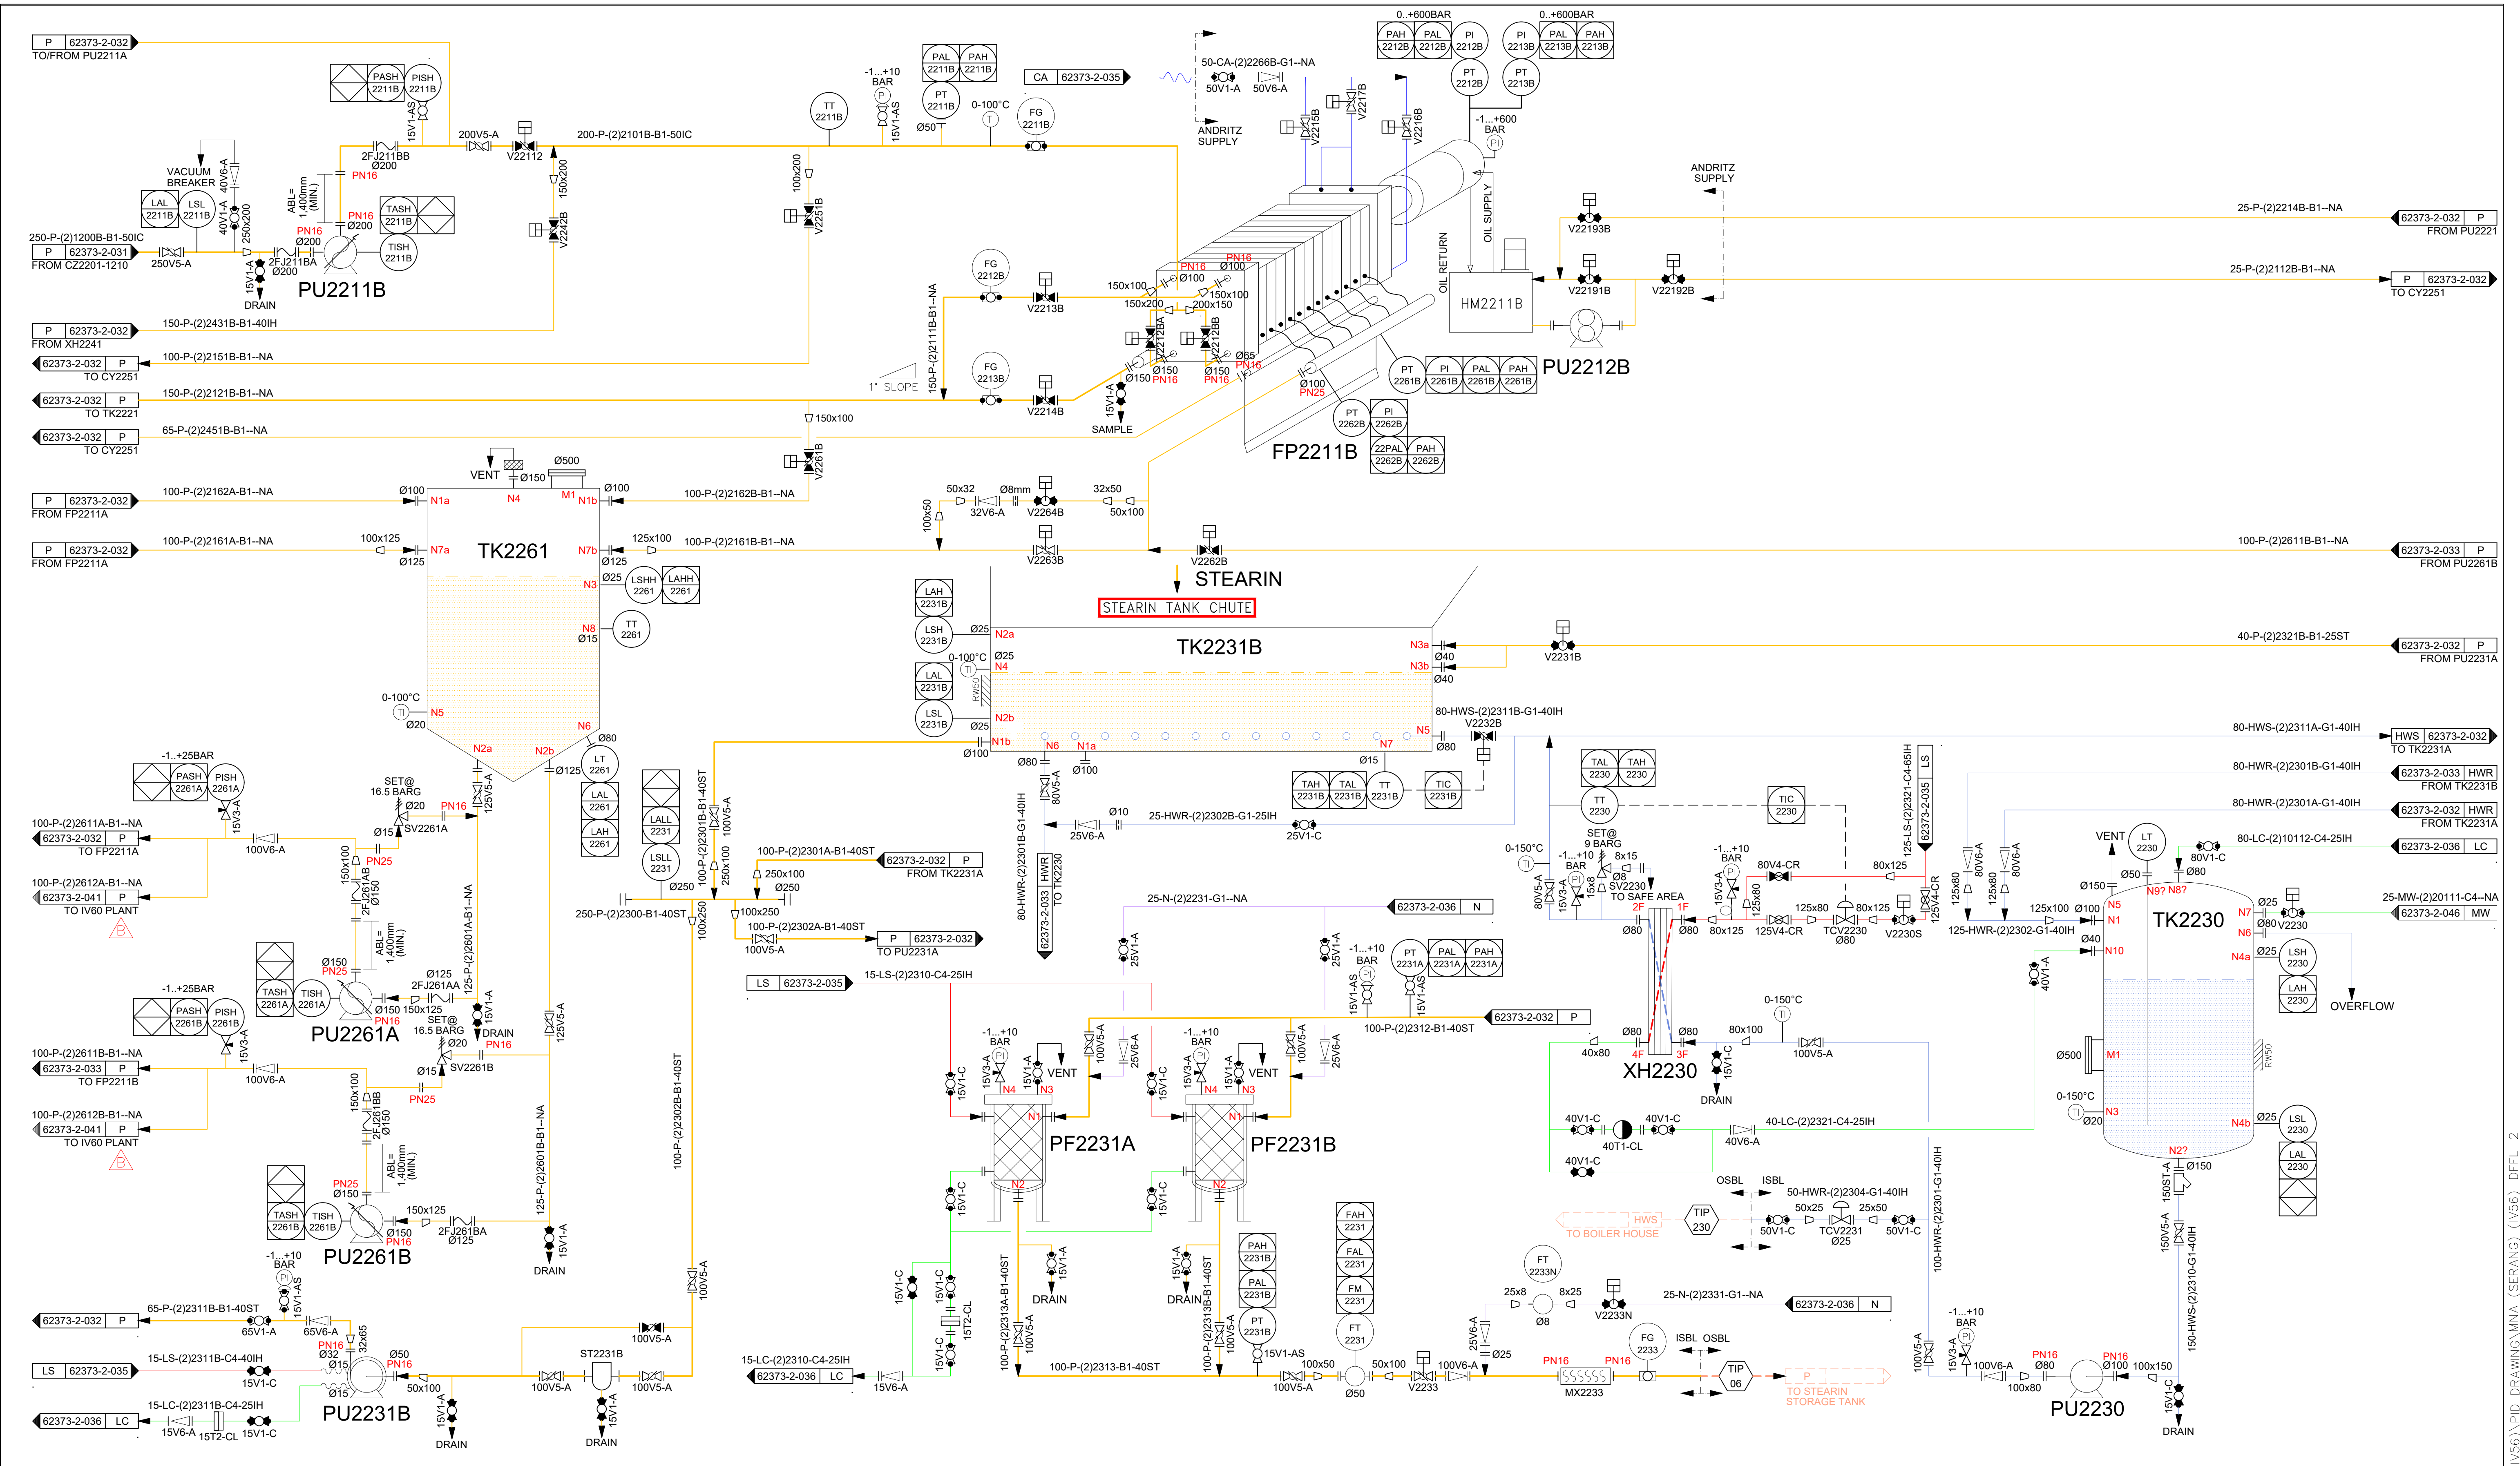


NOTES

NO.	DESCRIPTION	DATE	BY	CHK'D
2.	REVISED AS SHOWN 	270918	DZF	JONATHAN
1.	REVISED AS SHOWN 	040918	DZF	JONATHAN


REVISIONS

This drawing is the property of UPRCO Technologies Pte Ltd. Total or partial reproduction or utilization of this document is forbidden without prior written authorization of UPRCO Technologies Pte Ltd.

Customer PT. MULTIMAS NABATI ASAHAN (SERANG)	
	
Project Name 1,500MTD DRY FRACTIONATION PLANT (IV56)	Scale : N.T.S. Date : 140318 Drawn By : DZHAFRI Checked : Approved : Sheet No. : Of Drawing No. 62373-2-033 Rev. B
PIPING & INSTRUMENTATION DIAGRAM FOR FILTRATION SECTION (PART 2)	

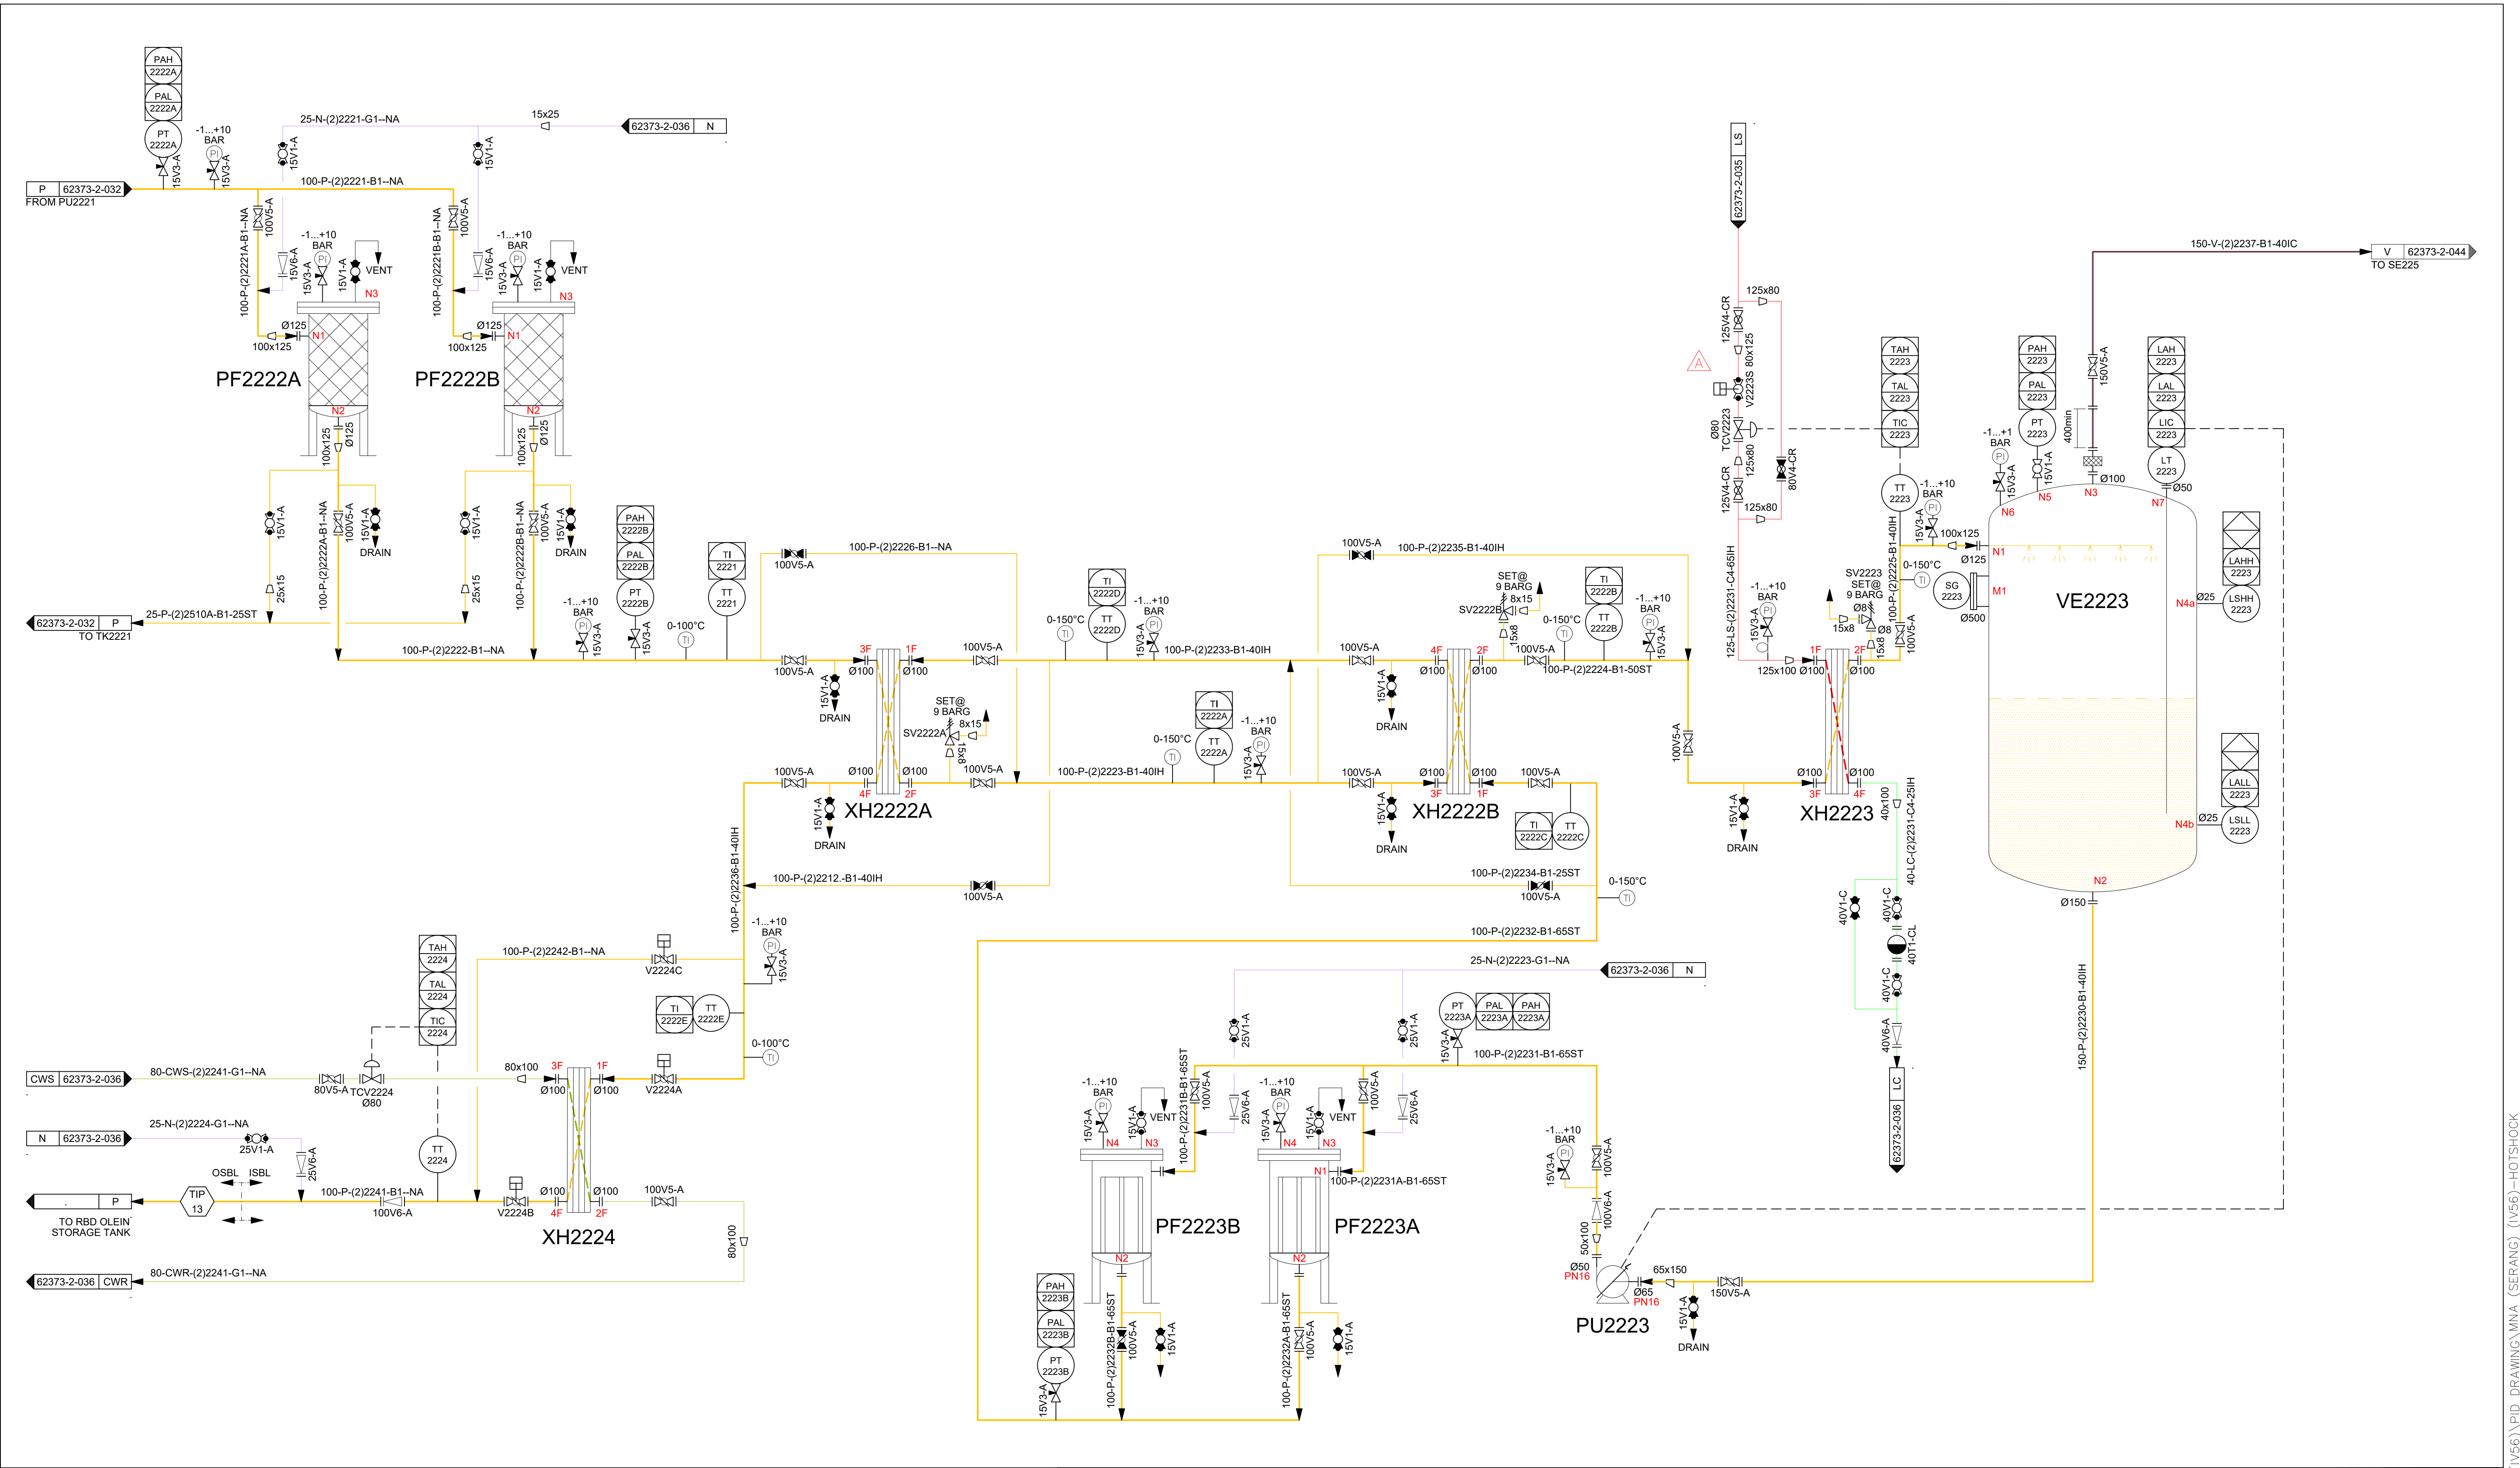

NOTES									This drawing is the property of LUPICO Technologies Pte Ltd total or partial reproduction or utilization of this document is forbidden without prior written authorization of LUPICO Technologies Pte Ltd.	Customer PT. MULTIMAS NABATI ASAHAN (SERANG)				
												Scale : N.T.S.		
												Date : 140318		
												Drawn By : DZHAFRI		
												Checked :		
												Approved :		
										Project Name		1,500MTD DRY FRACTIONATION PLANT (IV56)		
										PIPING & INSTRUMENTATION DIAGRAM FOR HOT SHOCK SYSTEM		Drawing No. 62373-2-034		Rev. A

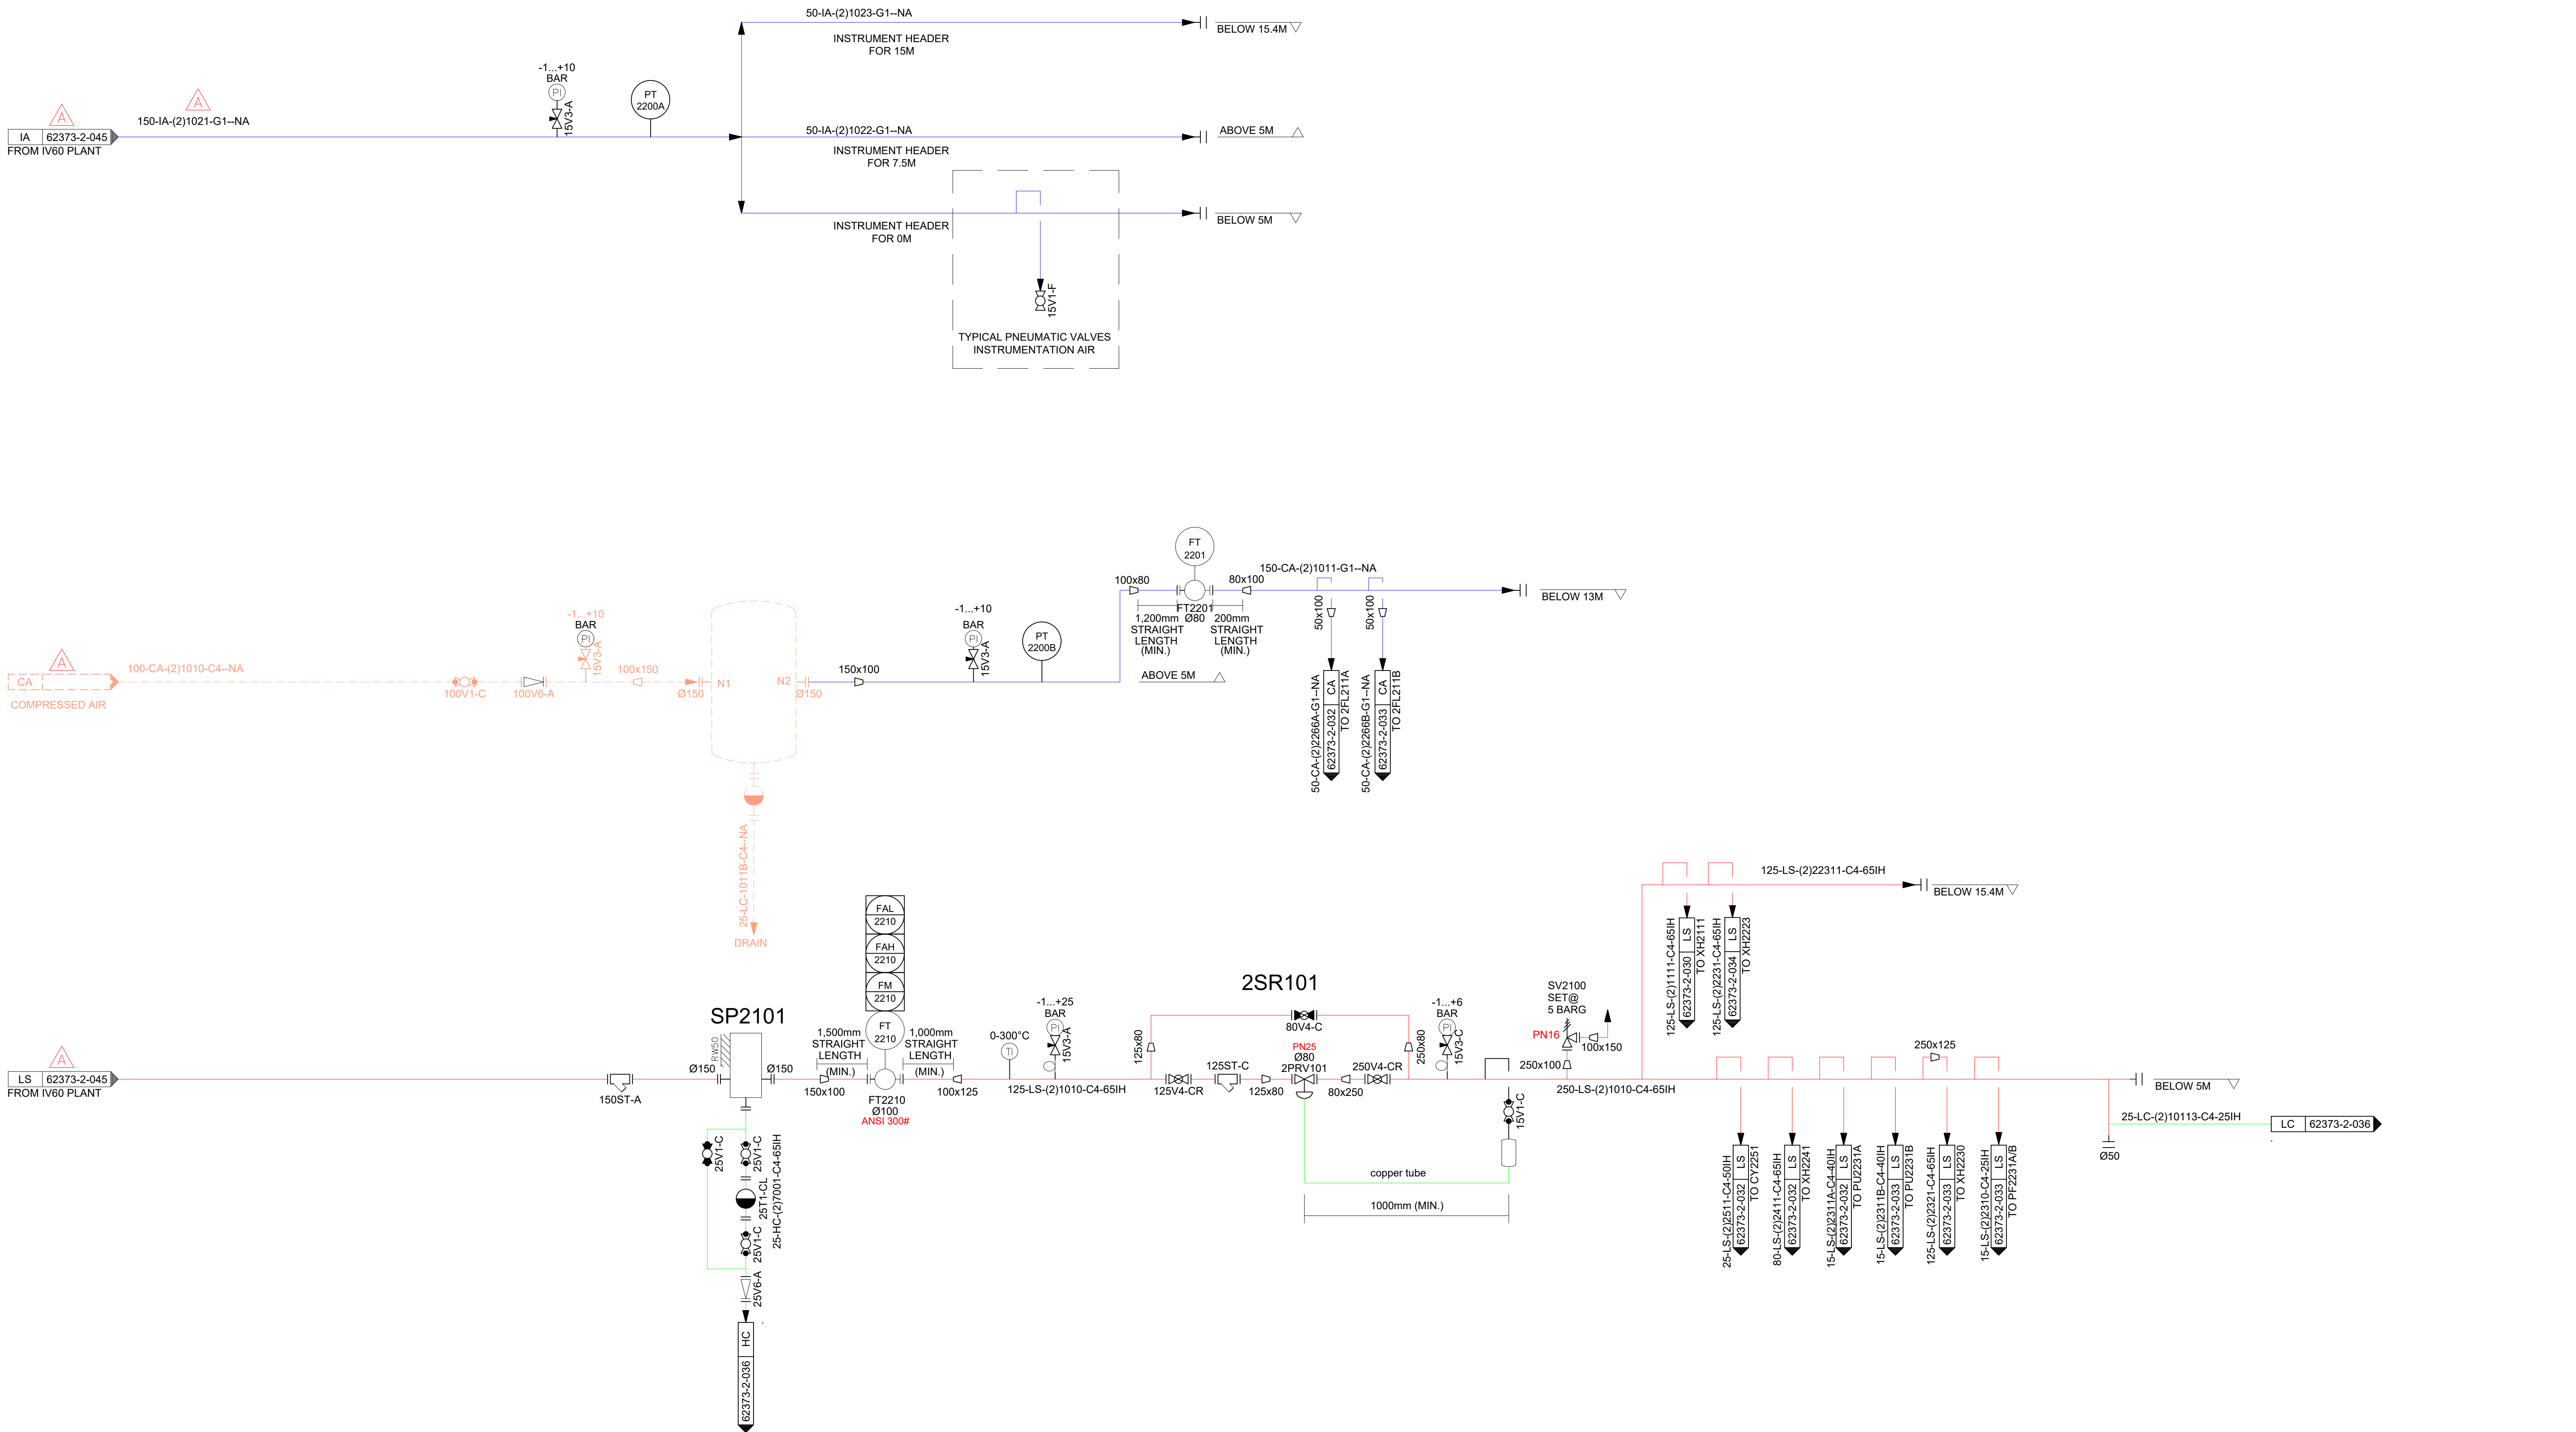

NOTE

1. - - - - : DENOTES ITEM NOT SUPPLIED BY LIPICO TECHNOLOGIES.





2. ALL FLANGES ARE ANSI 150# , UNLESS OTHERWISE STATED.

3. ALL THREADED CONNECTIONS ARE NPT STANDARD UNLESS OTHERWISE STATED.

4. PN10 , PN16 , PN25 , PN40 : DIN STANDARD.

1.	REVISED AS SHOWN	270918	DZF	CHK'D	
NO.	DESCRIPTION	DATE	BY	CHK'D	
REVISIONS					

Customer			PT. MULTIMAS NABATI ASAHAN (SERANG)		
			Scale :	N.T.S.	
			Date :	140318	
			Drawn By :	DZHAFFRI	
			Checked :		
Project Name			Approved :		
			Sheet No. :	Of	
PIPING & INSTRUMENTATION DIAGRAM FOR UTILITIES SECTION (PART 1)			Drawing No.	62373-2-035	Rev.

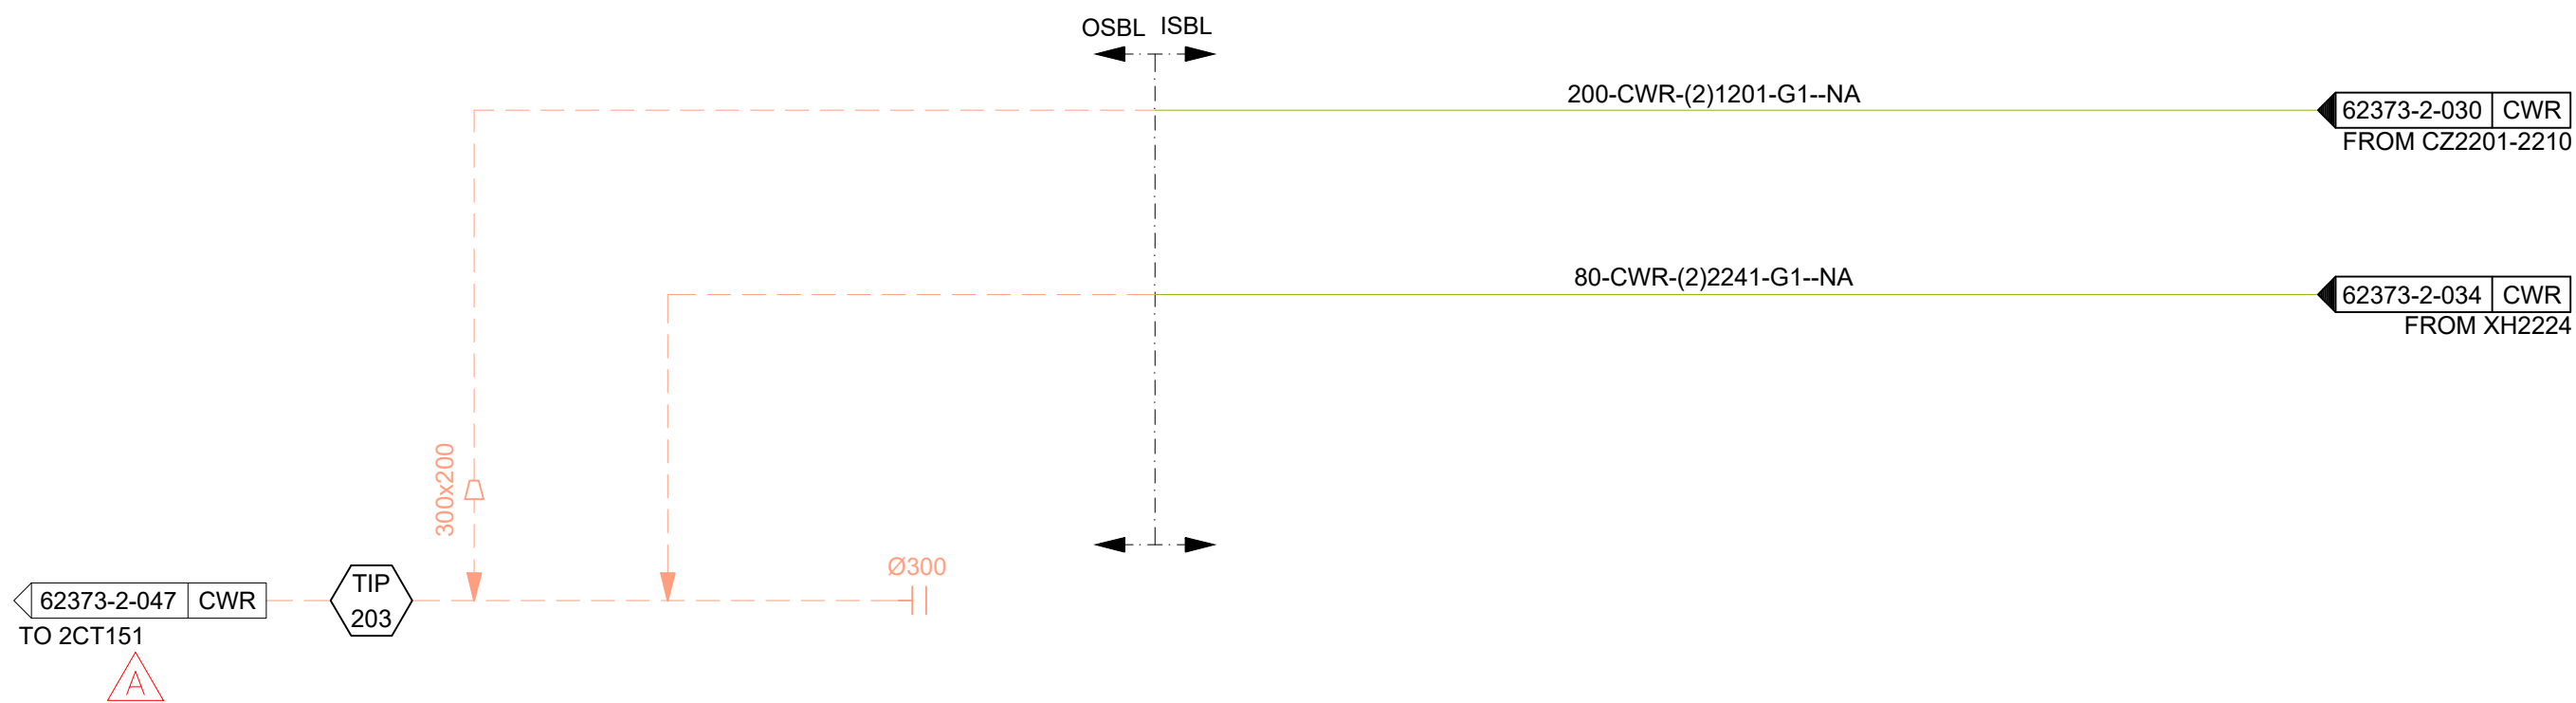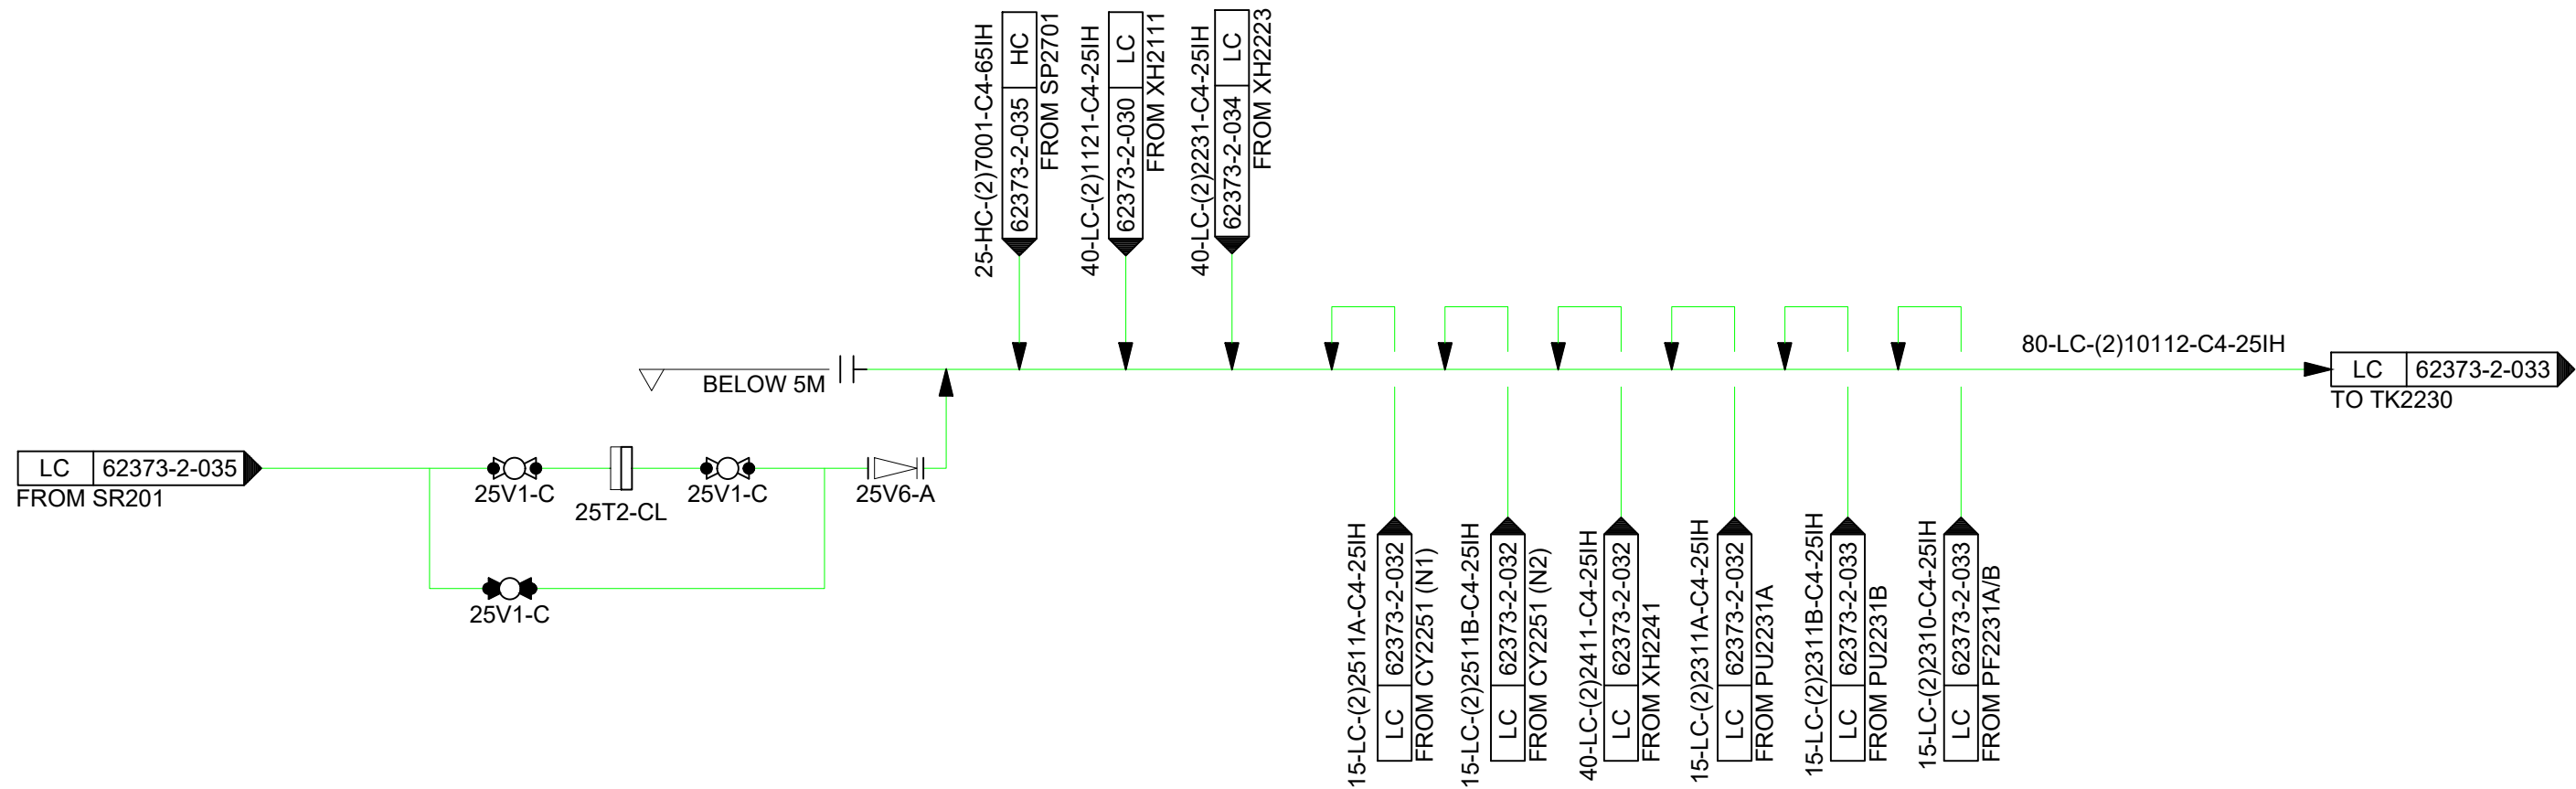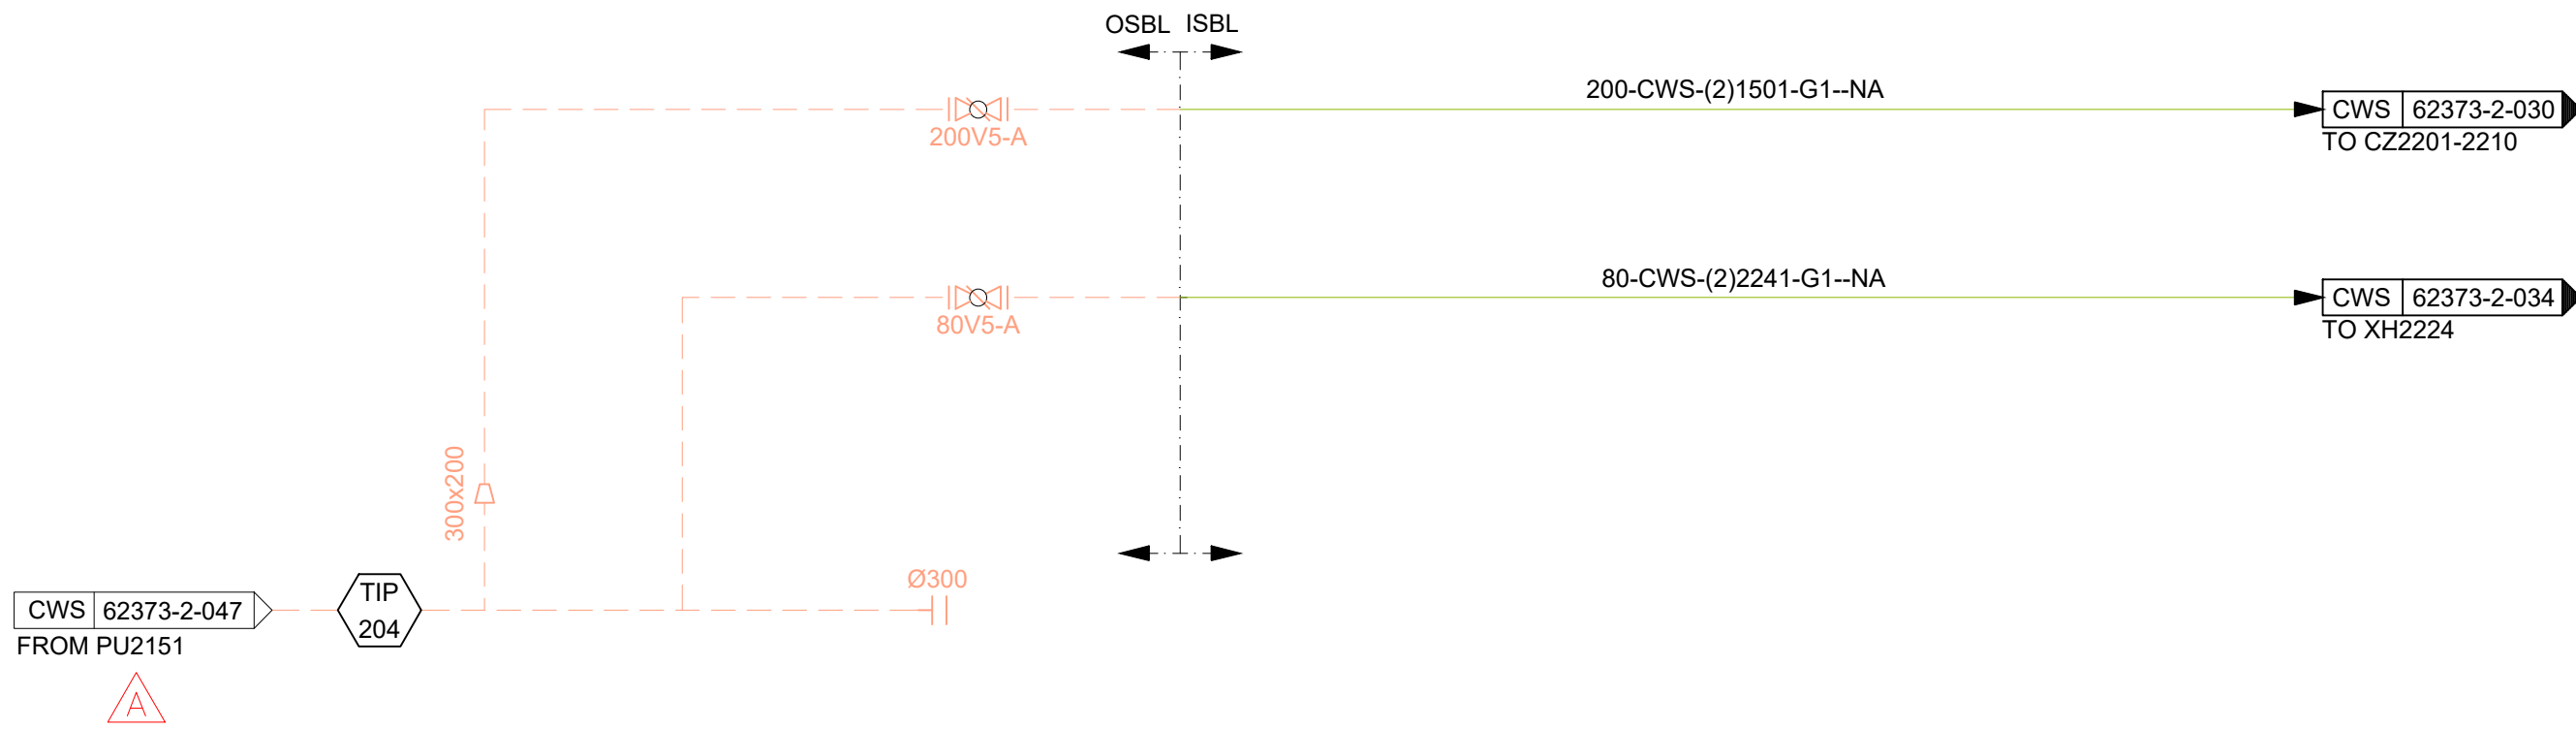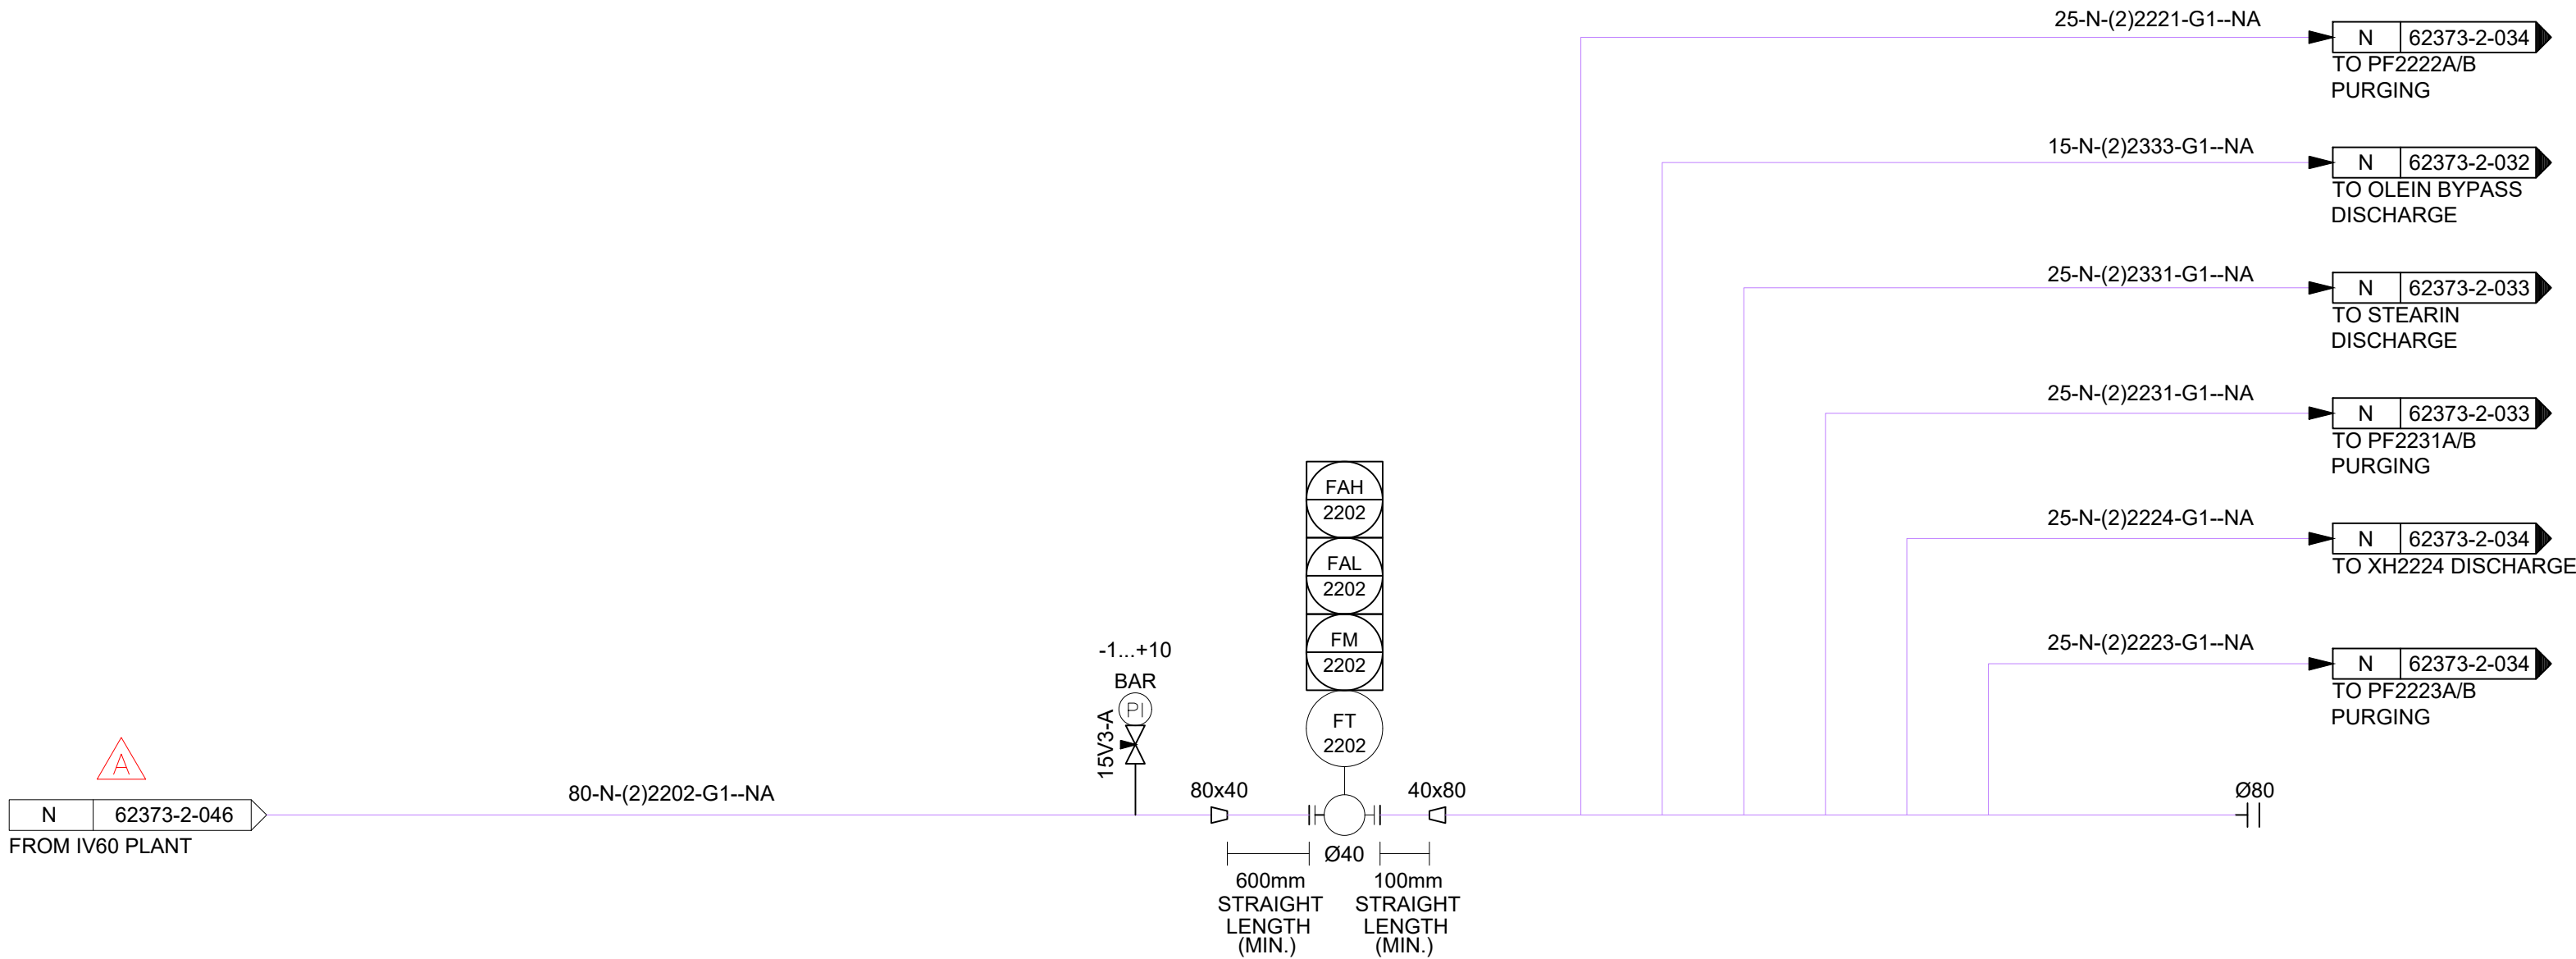

NOTE

1. - - - - : DENOTES ITEM NOT SUPPLIED BY LIPICO TECHNOLOGIES.
2. ALL FLANGES ARE ANSI 150# , UNLESS OTHERWISE STATED.
3. ALL THREADED CONNECTIONS ARE NPT STANDARD UNLESS OTHERWISE STATED.
4. PN10 , PN16 , PN25 , PN40 : DIN STANDARD.

NO.	DESCRIPTION	DATE	BY	CHK'D
1.	REVISED AS SHOWN	180718	DZF	
REVISIONS				

This drawing is the property of LIPICO Technologies Pte Ltd. total or partial reproduction or utilization of this document is forbidden without prior written authorization of LIPICO Technologies Pte Ltd.

Customer			PT. MULTIMAS NABATI ASAHAN (SERANG)		
			Scale :	N.T.S.	
			Date :	140318	
			Drawn By :	DZHAFFRI	
			Checked :		
Project Name			Approved :		
			Sheet No. :	Of	Rev.
PIPING & INSTRUMENTATION DIAGRAM FOR UTILITIES SECTION (PART 2)			Drawing No.	62373-2-036	