


BD#3 Central Control Room

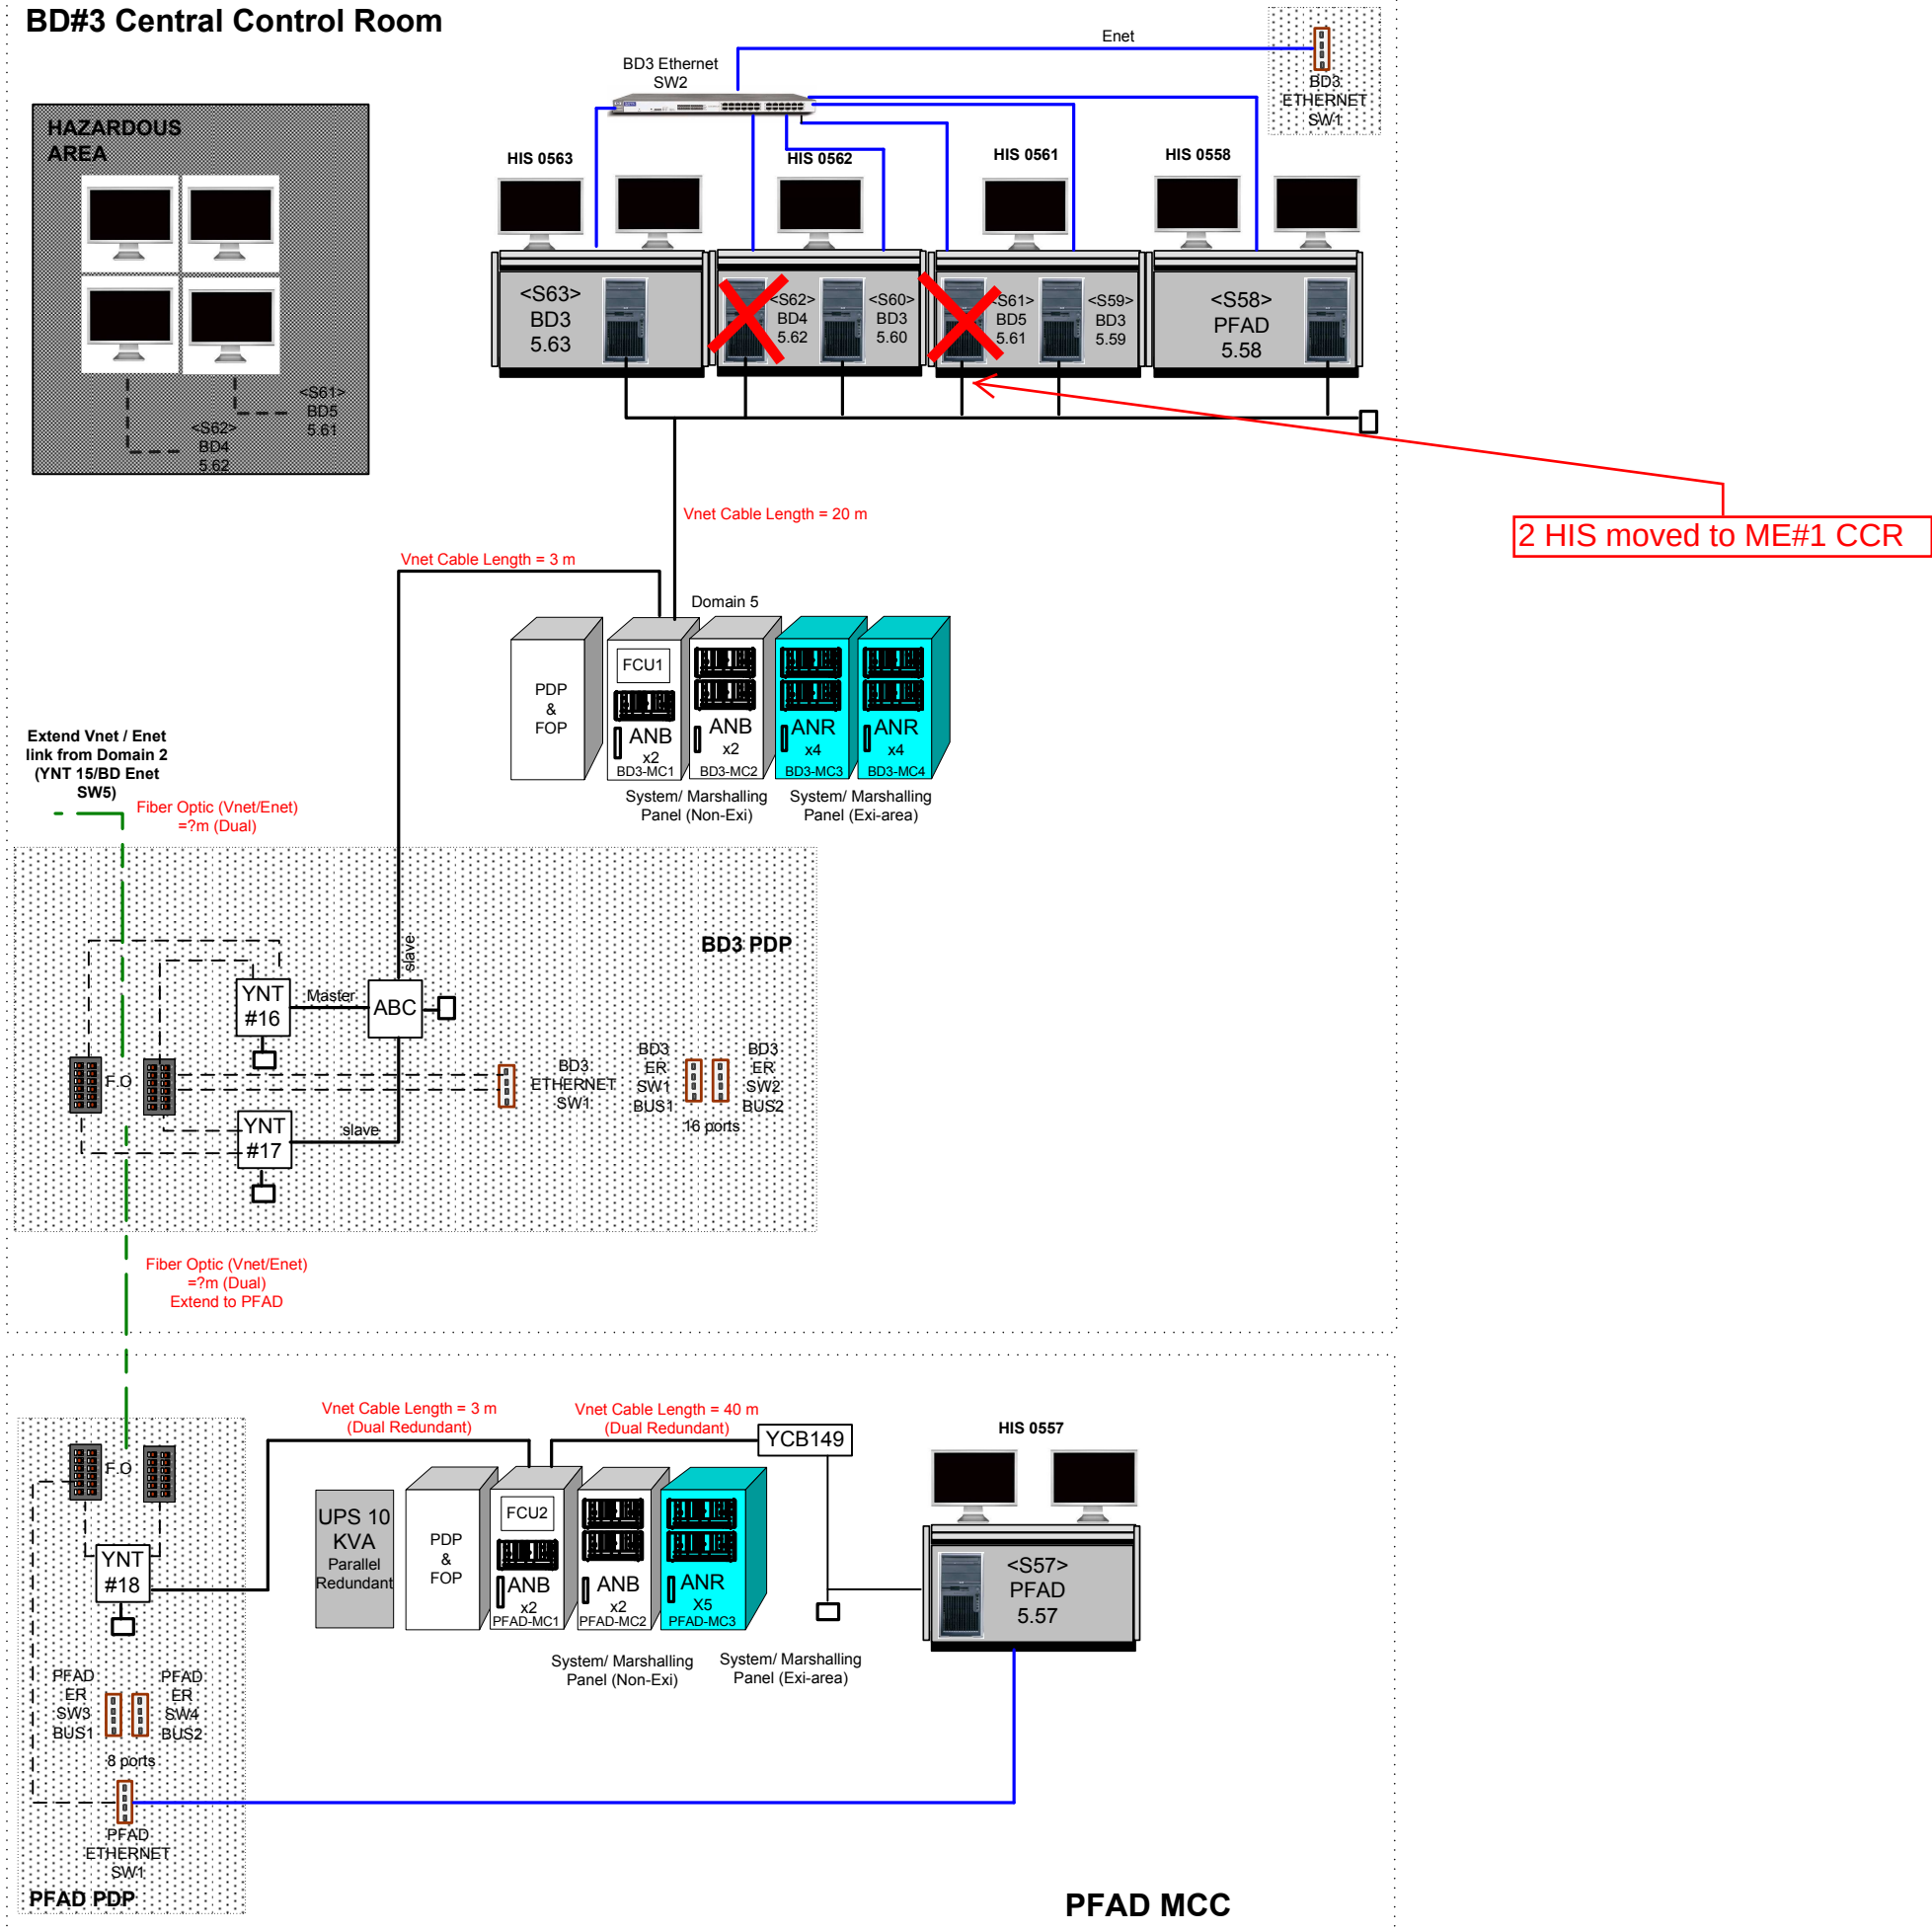

- Legend**
- HIS : Operator Workstation
 - FCU : Field Control Station
 - EWS : Engineering Workstation
 - FOP : Fiber Optic Panel
 - PDP : Power Distribution Panel
 - Enet Cat5 Cable
 - Vnet 10 Base 5/2 Cable
 - FO Patch Cord
 - Fiber Optic Cable