


BD/ME Plant  
(Domain 2)

MES Control Room  
(Domain 2)

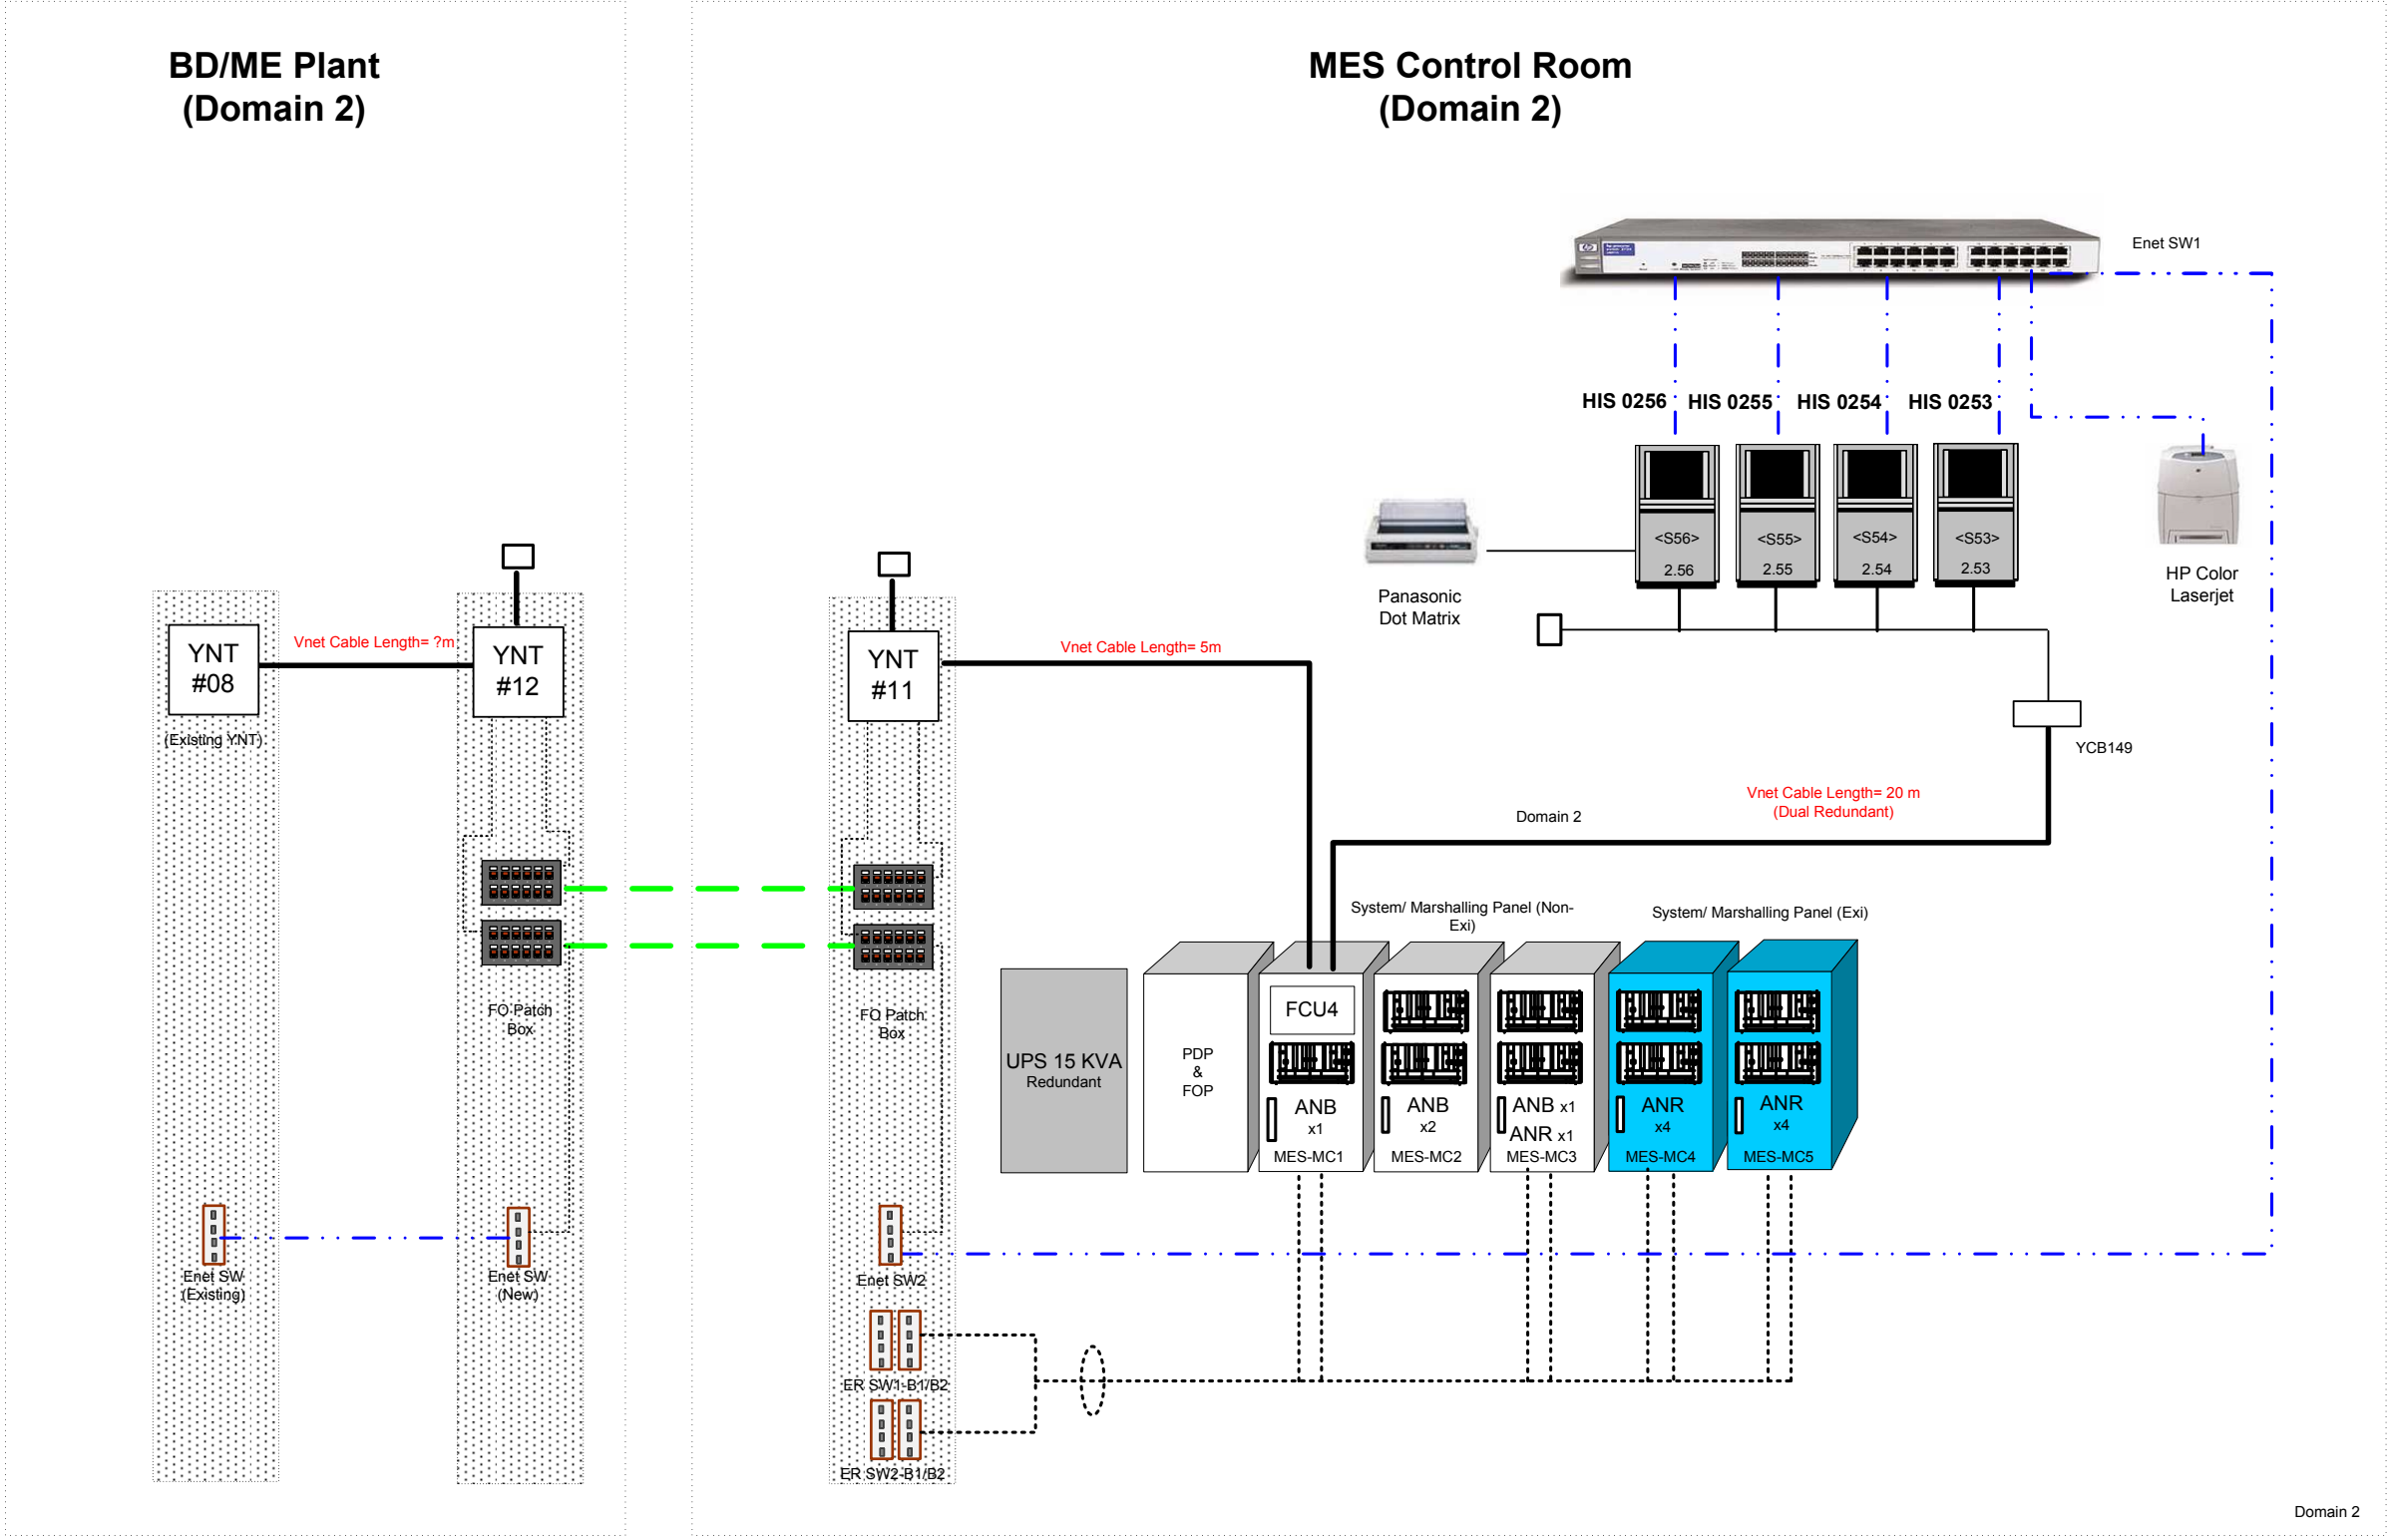

- Legend**
- HIS : Operator Workstation
  - FCS : Field Control Station
  - EWS : Engineering Workstation
  - FOP : Fiber Optic Panel
  - PDP : Power Distribution Panel
  - \*P : 800(W)x800(D)x2100(H)
  - : Enet Cat5 Cable
  - : Vnet 10 Base 5 Cable
  - : Vnet 10 Base 2 Cable
  - : Fiber Optic Cable

|      |             |            |             |      |             |             |               |                              |  |
|------|-------------|------------|-------------|------|-------------|-------------|---------------|------------------------------|--|
|      |             |            |             |      | First Issue |             | Rev 0         | Project Name :               |  |
|      |             |            |             |      |             | By          | Date          | WILMAR SURABAYA MES Project  |  |
|      |             |            |             |      | Drawn       | HAFIZ IDRUS | 18 April 2011 | Title : SYSTEM CONFIGURATION |  |
|      |             |            |             |      | Checked     | WP YONG     | 18 April 2011 | Doc no : WSMES-D01-001       |  |
| Rev. | Description | Revised By | Approved By | Date | Approved    | CN LEE      | 18 April 2011 | Page : 2 / 2                 |  |