


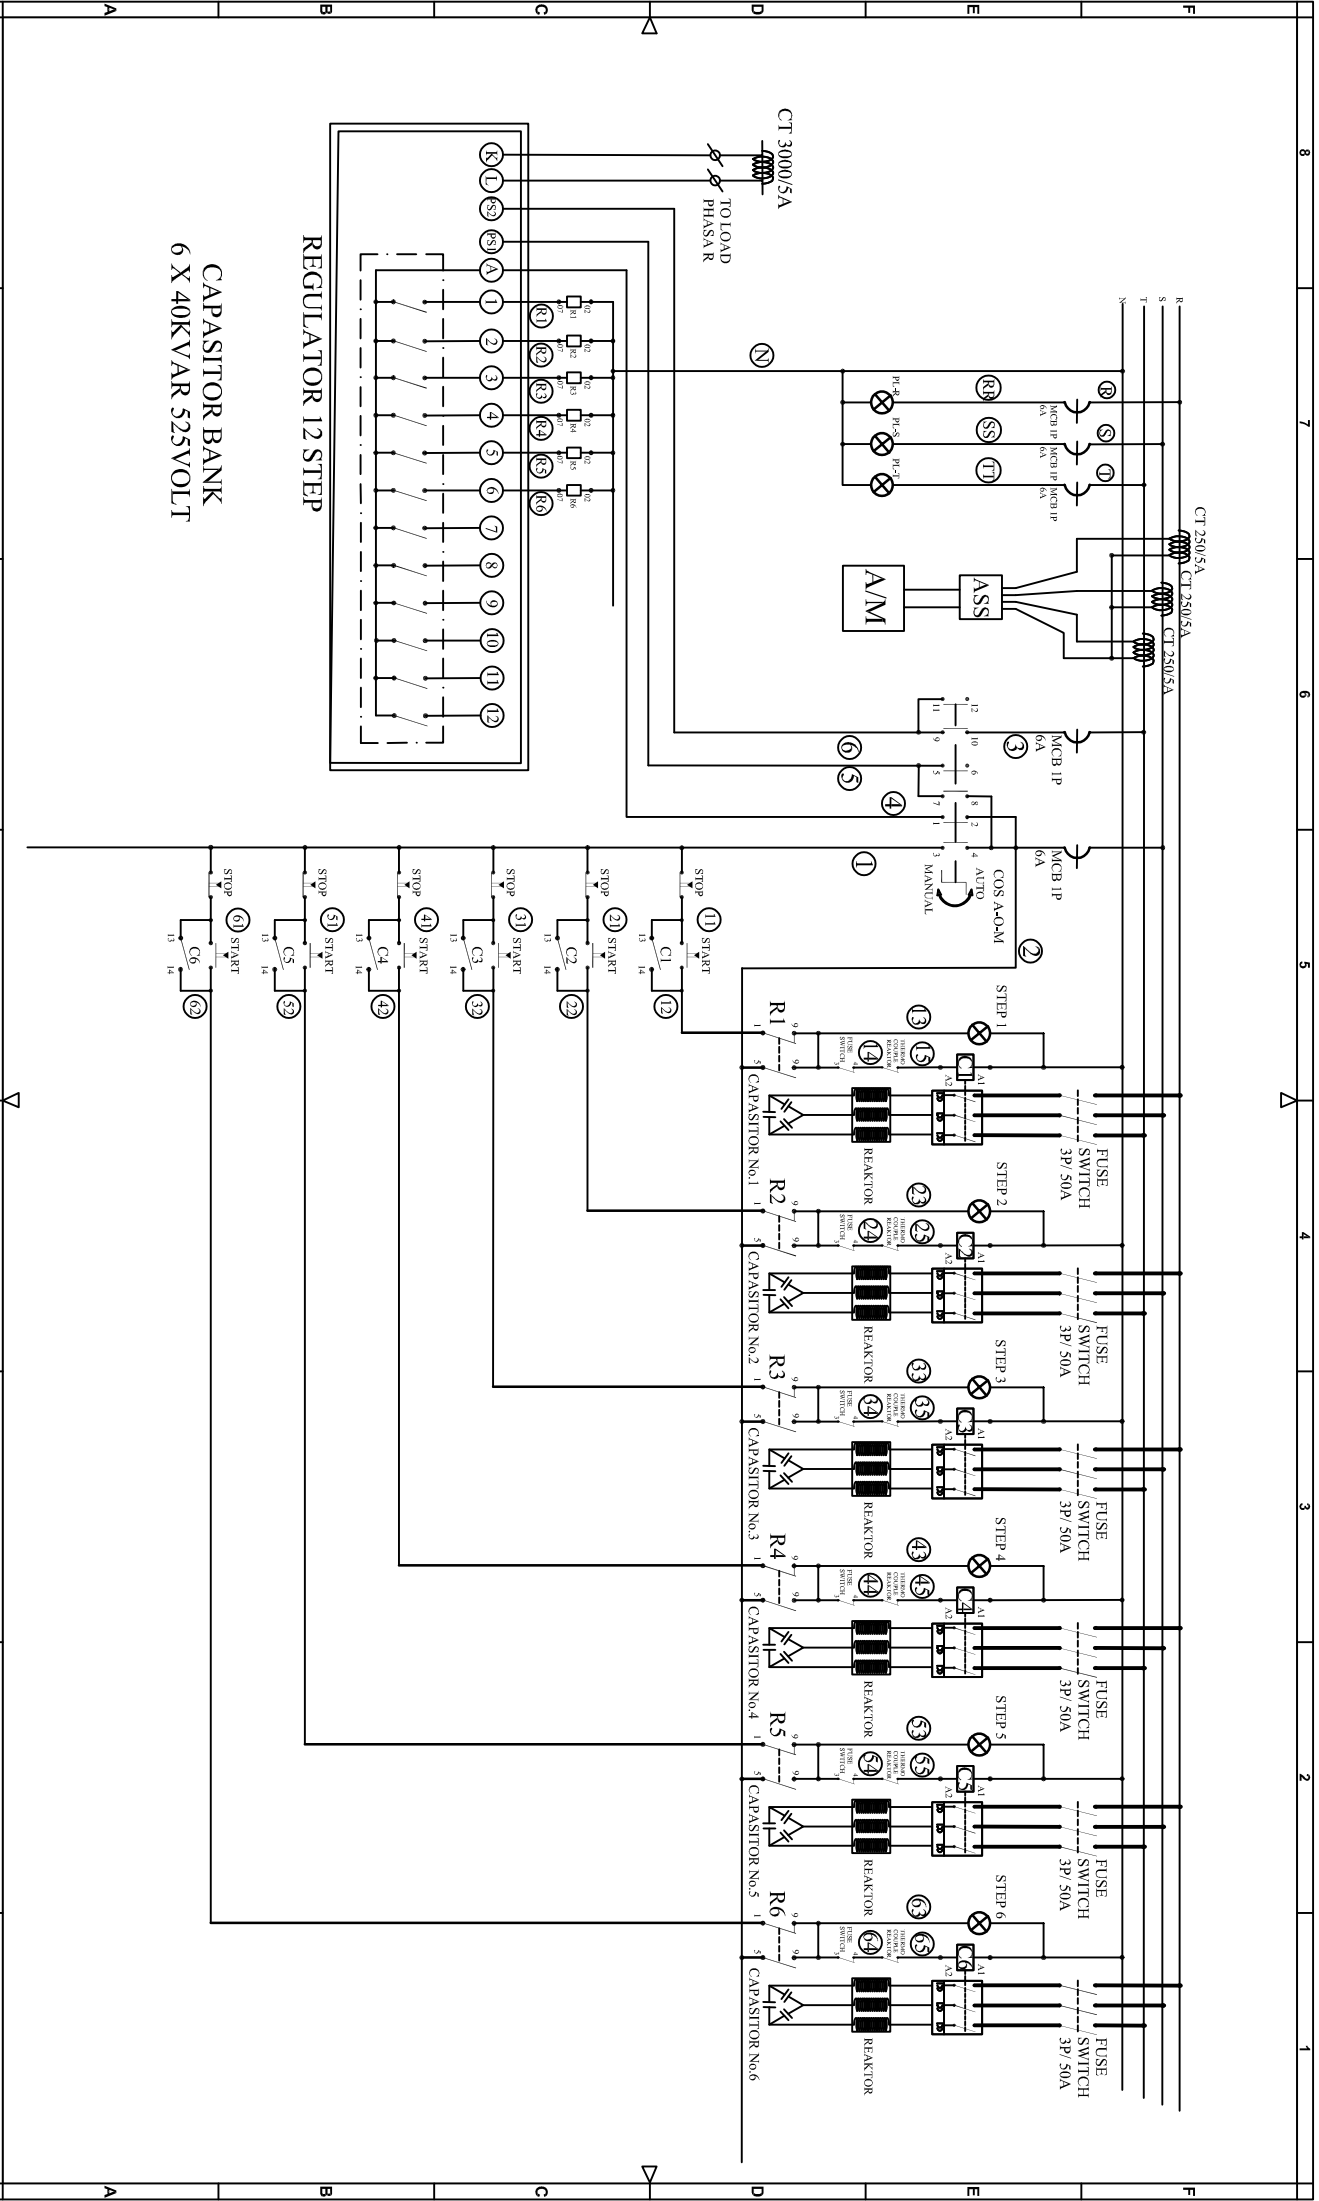

Customer :		7		6		5		4		3		2		1					
PT. MULTIMAS NABATI ASAHAN						Judul :													
Nama Proyek : MNA - 01 - 1814						PFC - 01 A (Switchyar Area) 6 STEP X 40KVAR 525V (CT 8000/5A)													
No. Dok. :		PRD 15-01-19 A		No. Dwg. :		DWG 15-01-19 A		Dimensi :		mm		Skala :		NTS					
PT. ANDALAS CITRA ELEKTRINDO								Toleransi Dimensi Panel Free Standing :		+/- 1%		-							
								Toleransi Dimensi Panel Wall Mounting :		+/- 2%		-							
								Revisi :		Tanggal :		Digambar Oleh :		Dipertiksa Oleh :		Disetujui Oleh :			
										9 Juli 19		DJS						-	