


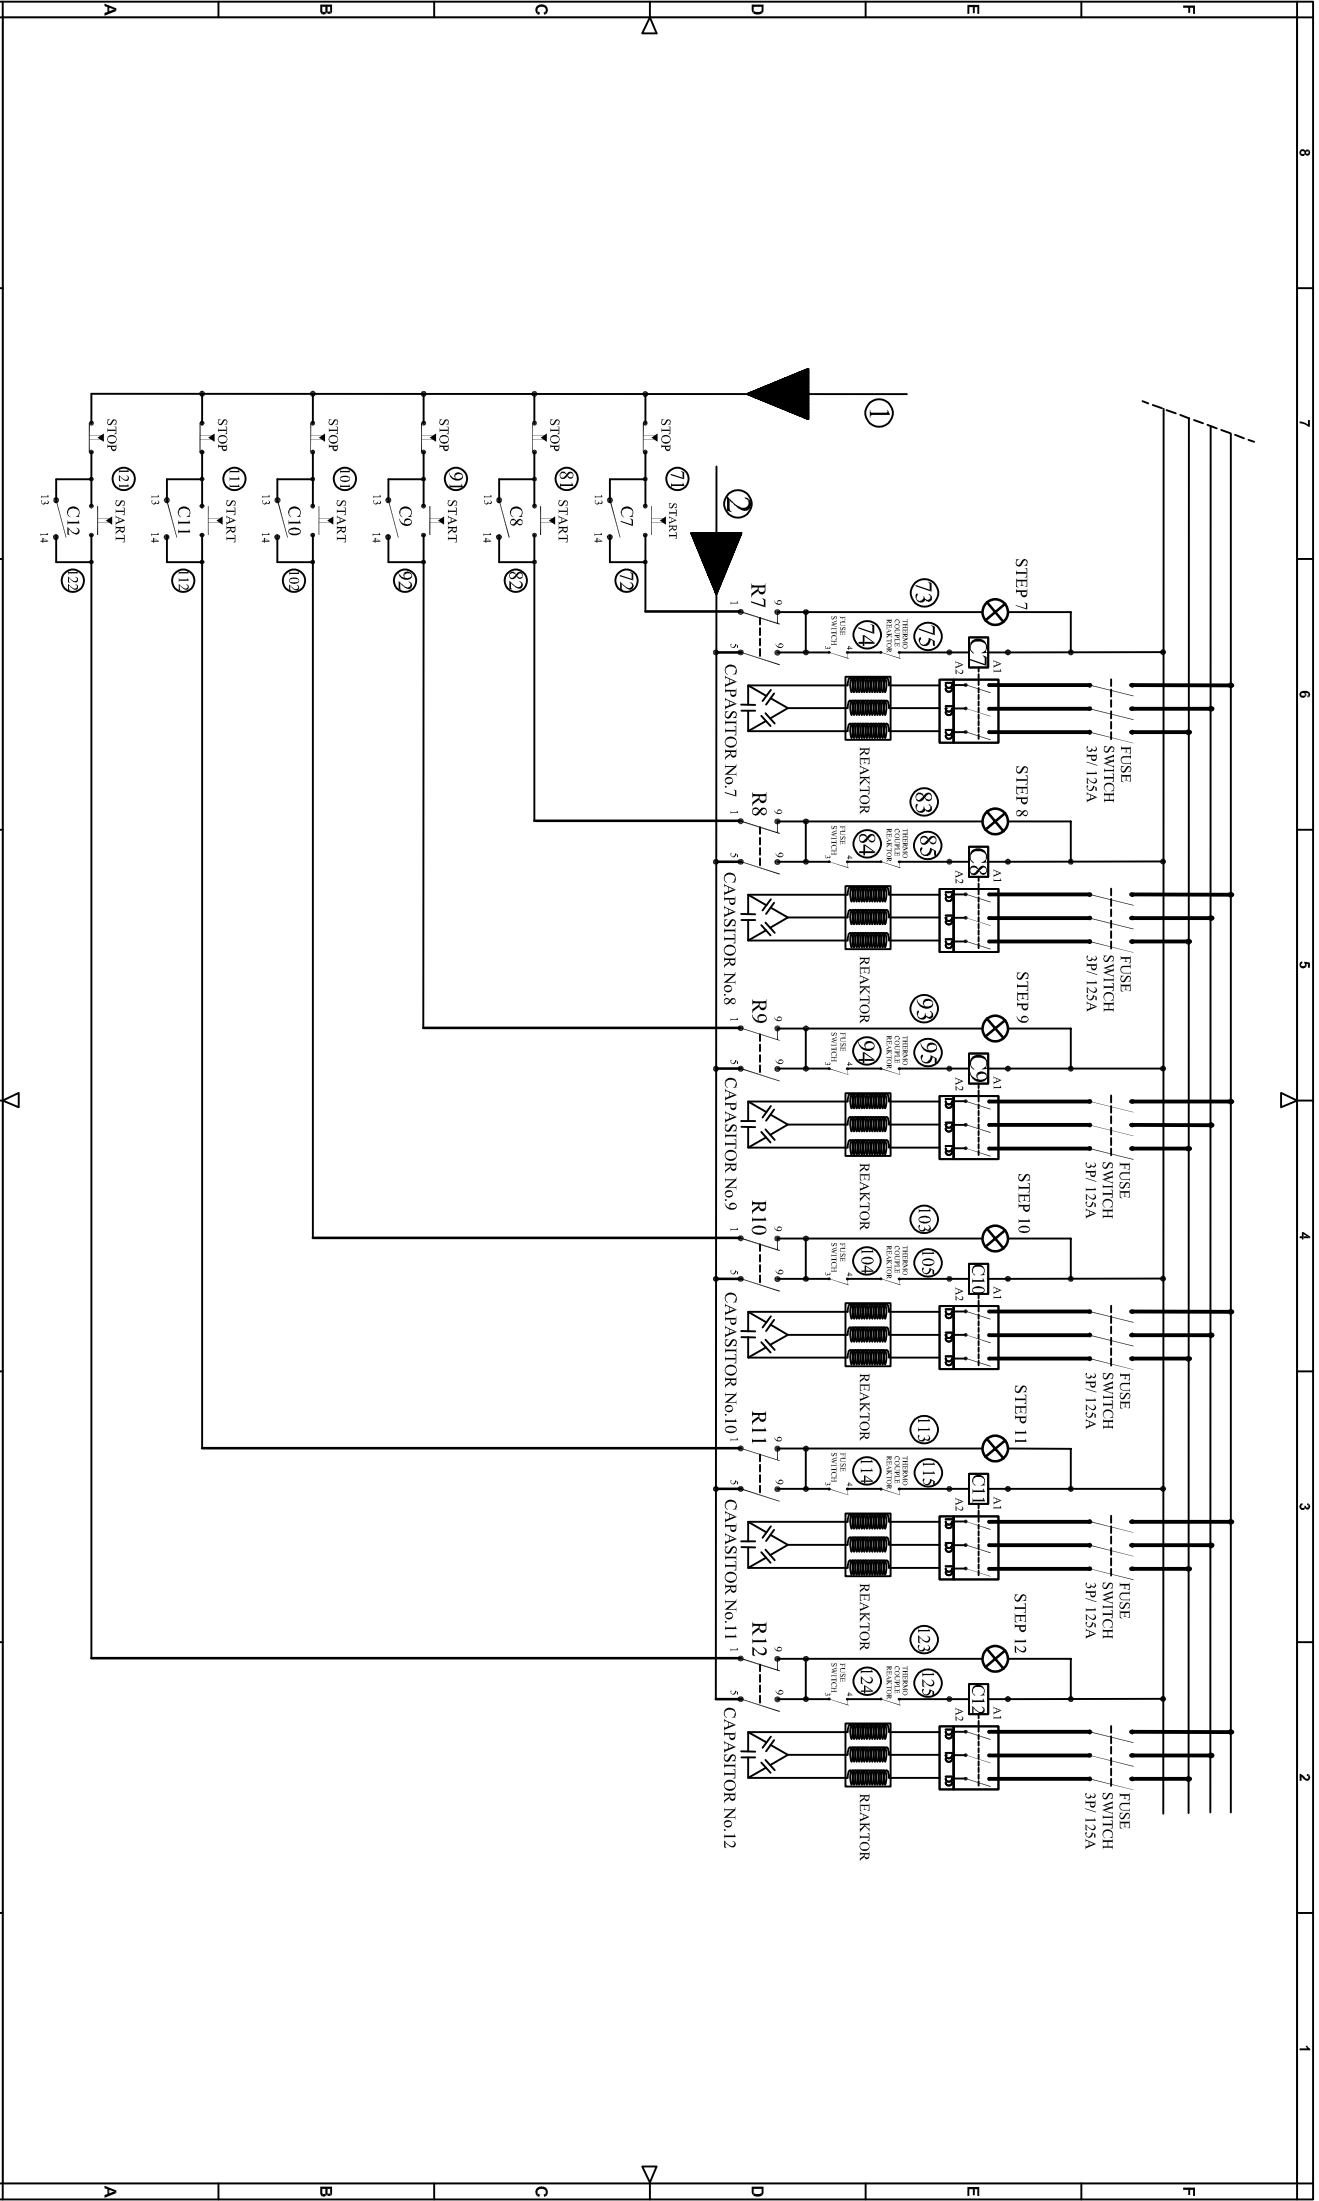

Customer : PT. MULTIMAS NABATI ASAHAN		Judd :		PFC-20A (Boiler #1)		Revisi :		Tanggal :		Digambar Oleh :		Diperiksa Oleh :		Disetujui Oleh :	
Nama Proyek : MNA - 01 - 1814		12 STEP X 80KVAR 525V (CT 4000/5A)		-		-		9 Juli 19		DJS		-		-	
No. Dwg. : PRD 15-01-19 B1		No. Dwg. : DWG 15-01-19 B1		Dimensi : mm		Skala :		NTS		-		-		-	
Toleransi Dimensi Panel Free Standing : +/- 1%		Toleransi Dimensi Panel Wall Mounting : +/- 2%		-		-		-		-		-		-	
PT. ANDALAS CITRA ELEKTRINDO		2/3		-		-		-		-		-		-	

