


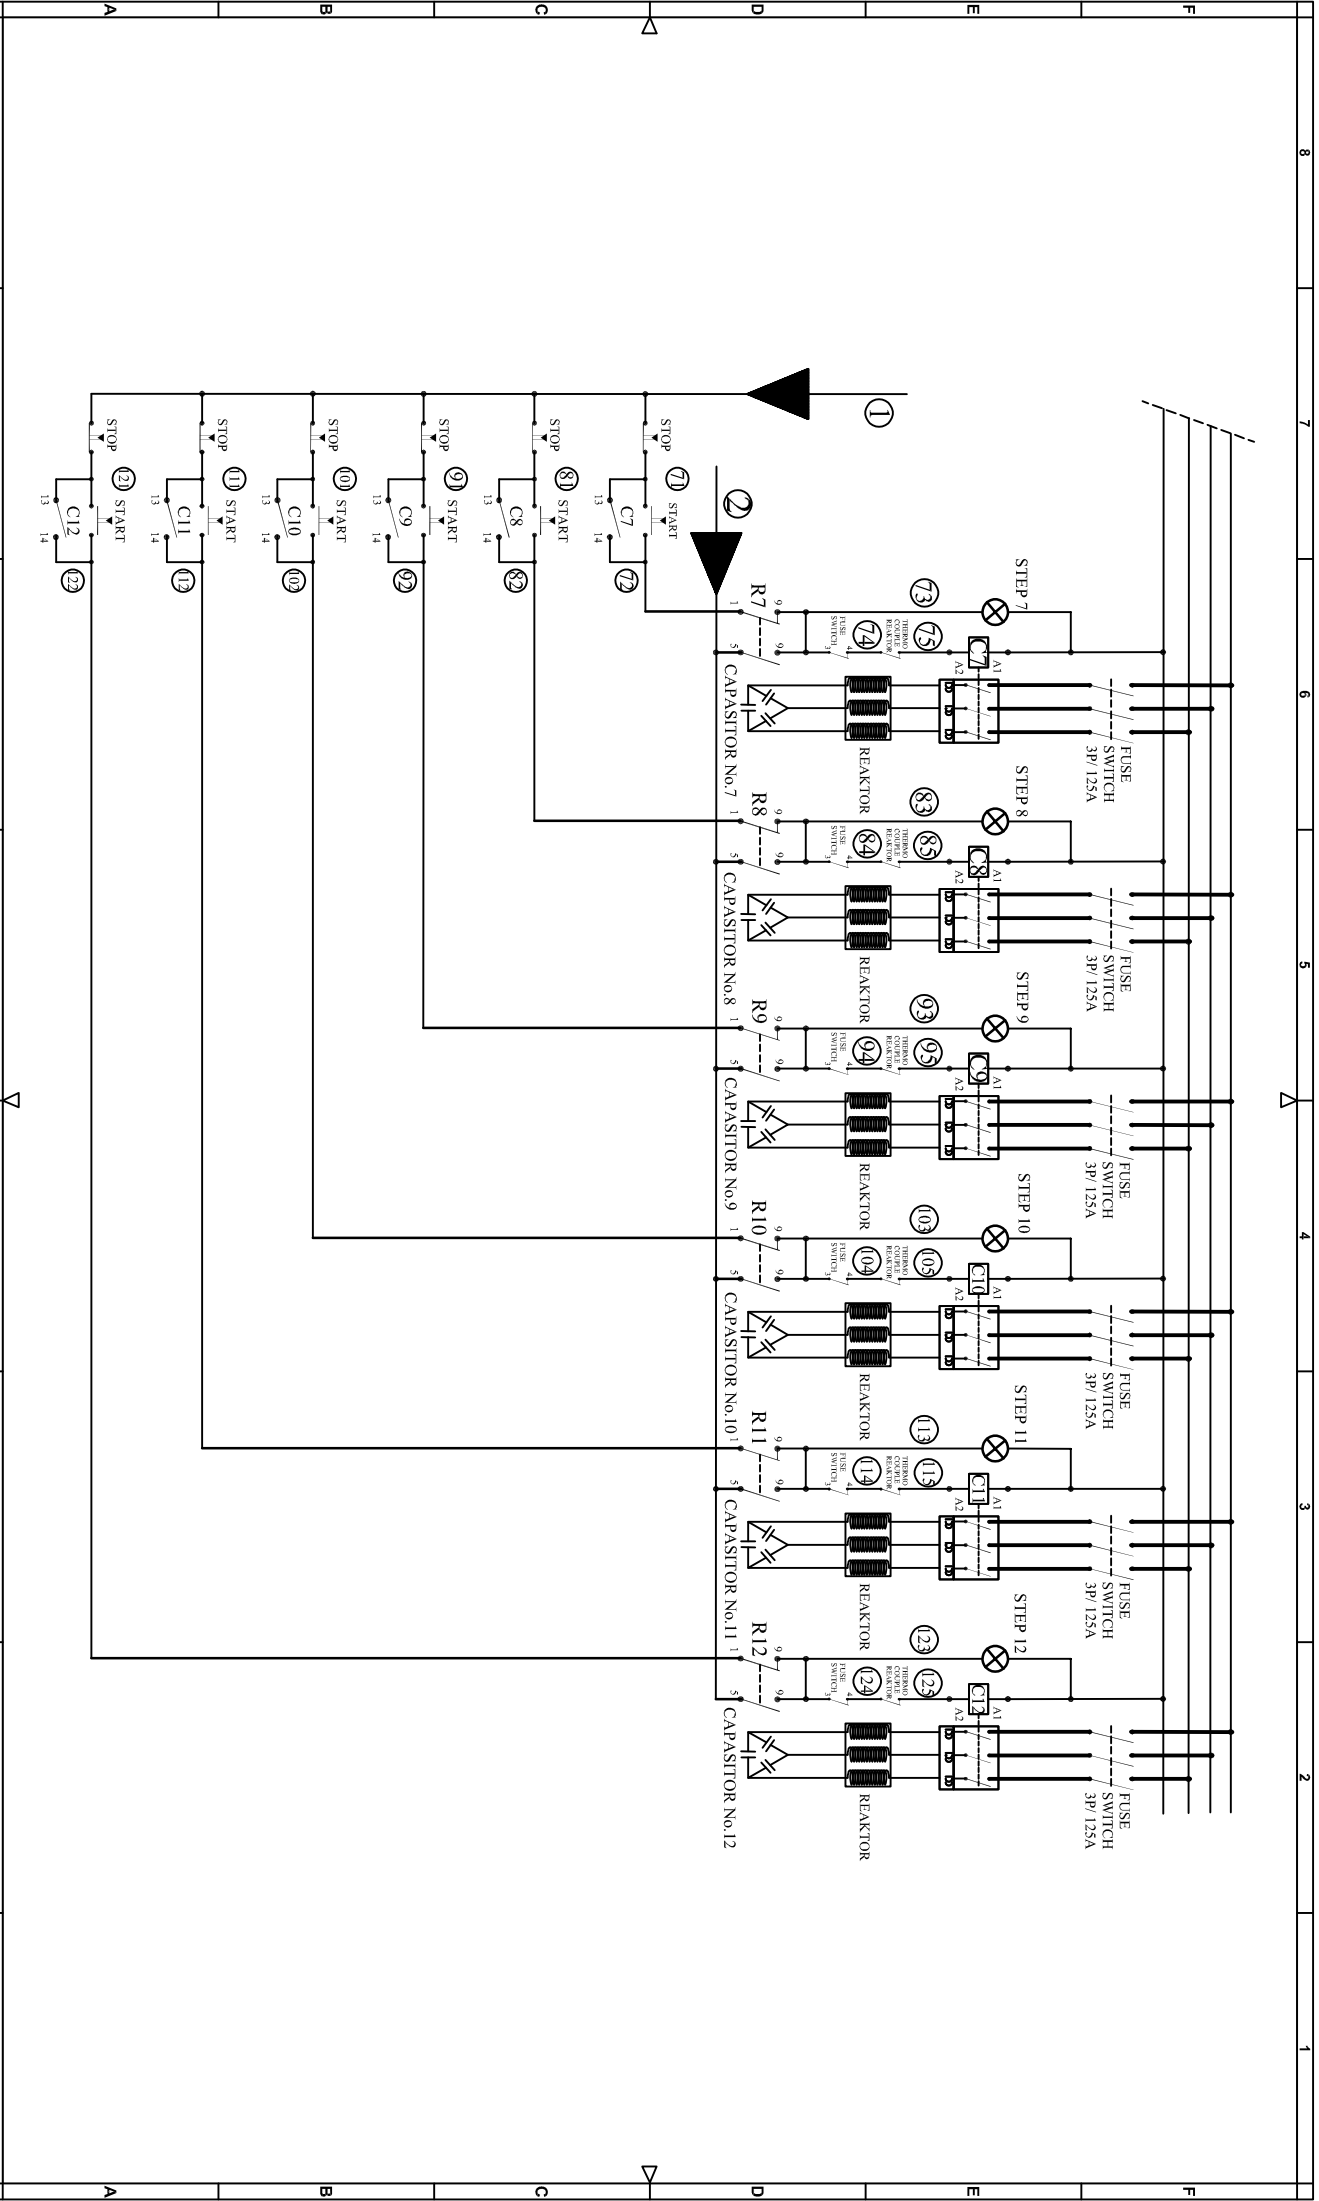

Customer : PT. MULTIMAS NABATI ASAHAN		Judd : PFC-21A (Boiler #2)		Revisi : -		Tanggal : 9 Juli 19		Digambar Oleh : DJS		Diperiksa Oleh : -		Disetujui Oleh : -	
Nama Proyek : MNA - 01 - 1814		12 STEP X 80KVAR 525V (CT 4000/5A)		-		-		-		-		-	
No. Dwg : PRD 15-01-19 B2		DWG 15-01-19 B2		Dimensi : mm		Skala : -		NTS		-		-	
PT. ANDALAS CITRA ELEKTRINDO		Toleransi Dimensi Panel Free Standing : +/- 1%		Toleransi Dimensi Panel Wall Mounting : +/- 2%		-		-		-		-	
												Halaman : 2/3	

