


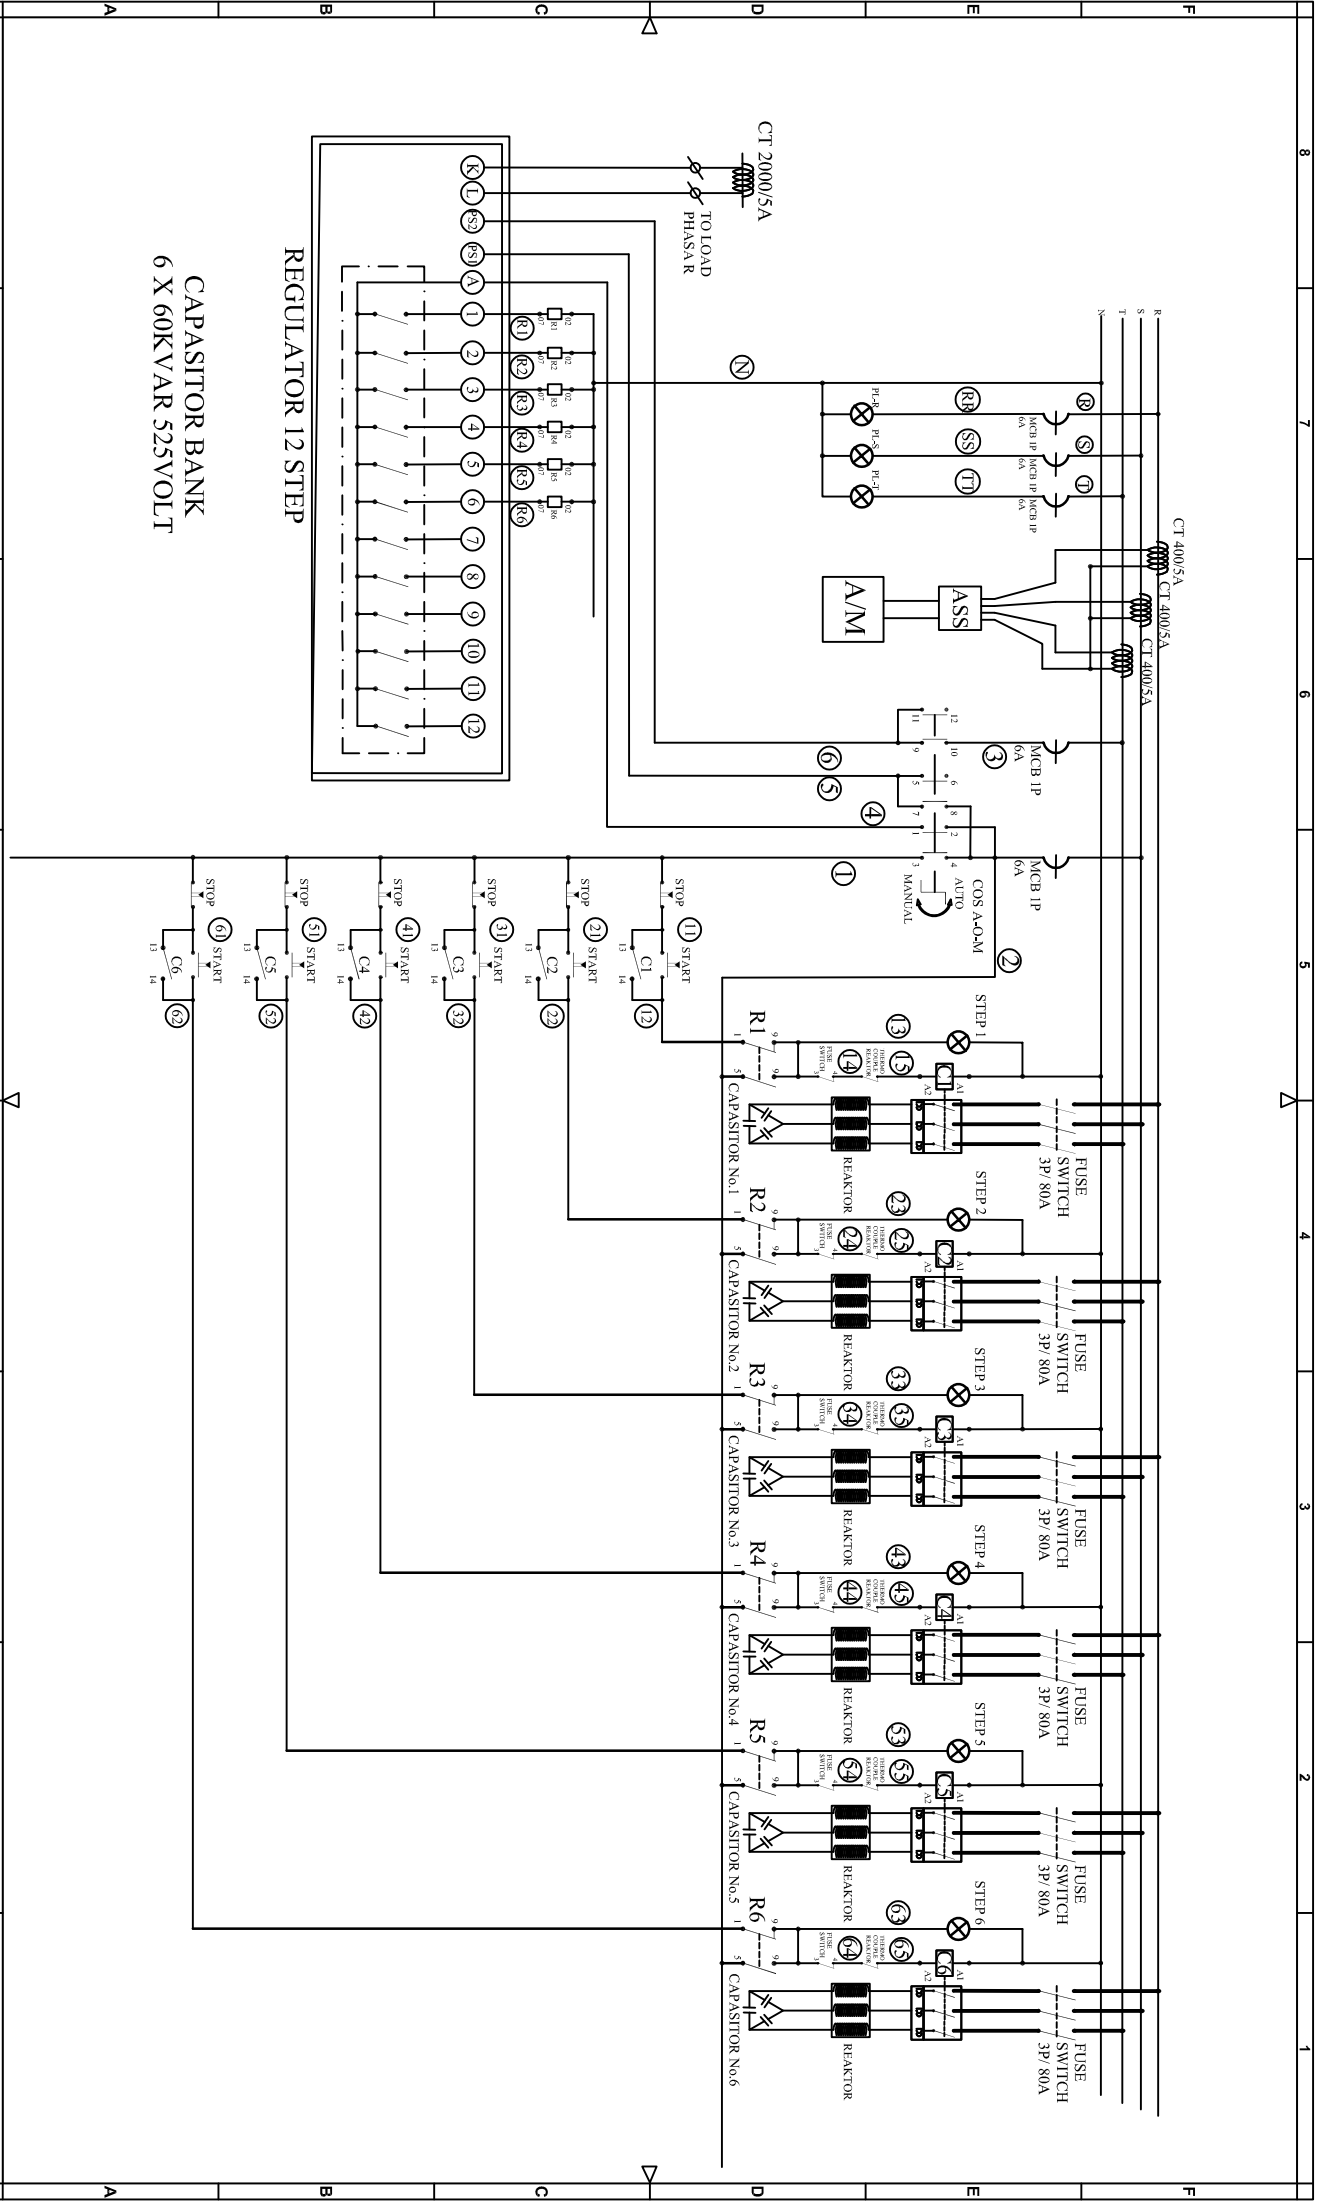

Customer : PT. MULTIMAS NABATI ASAHAN		Judo :		Revisi :		Tanggal :		Dipertiksa Oleh :		Disetujui Oleh :	
Nama Proyek : -		PFC-22B (WWTP/HYDRANT)		-		9 Juli 19		DJS		-	
No. Dok. : PRD 15-01-19 C(2)		No. Dwg. : DW 15-01-19C (2)		Dimensi : mm		Skala :		NTS		-	
		6 X 60KVAR 525V CT 2000/5A		Toleransi Dimensi Panel Free Standing : +/- 1%		-		-		-	
				Toleransi Dimensi Panel Wall Mounting : +/- 2%		-		-		-	
PT. ANDALAS CITRA ELEKTRINDO										Halaman : 1/2	

