



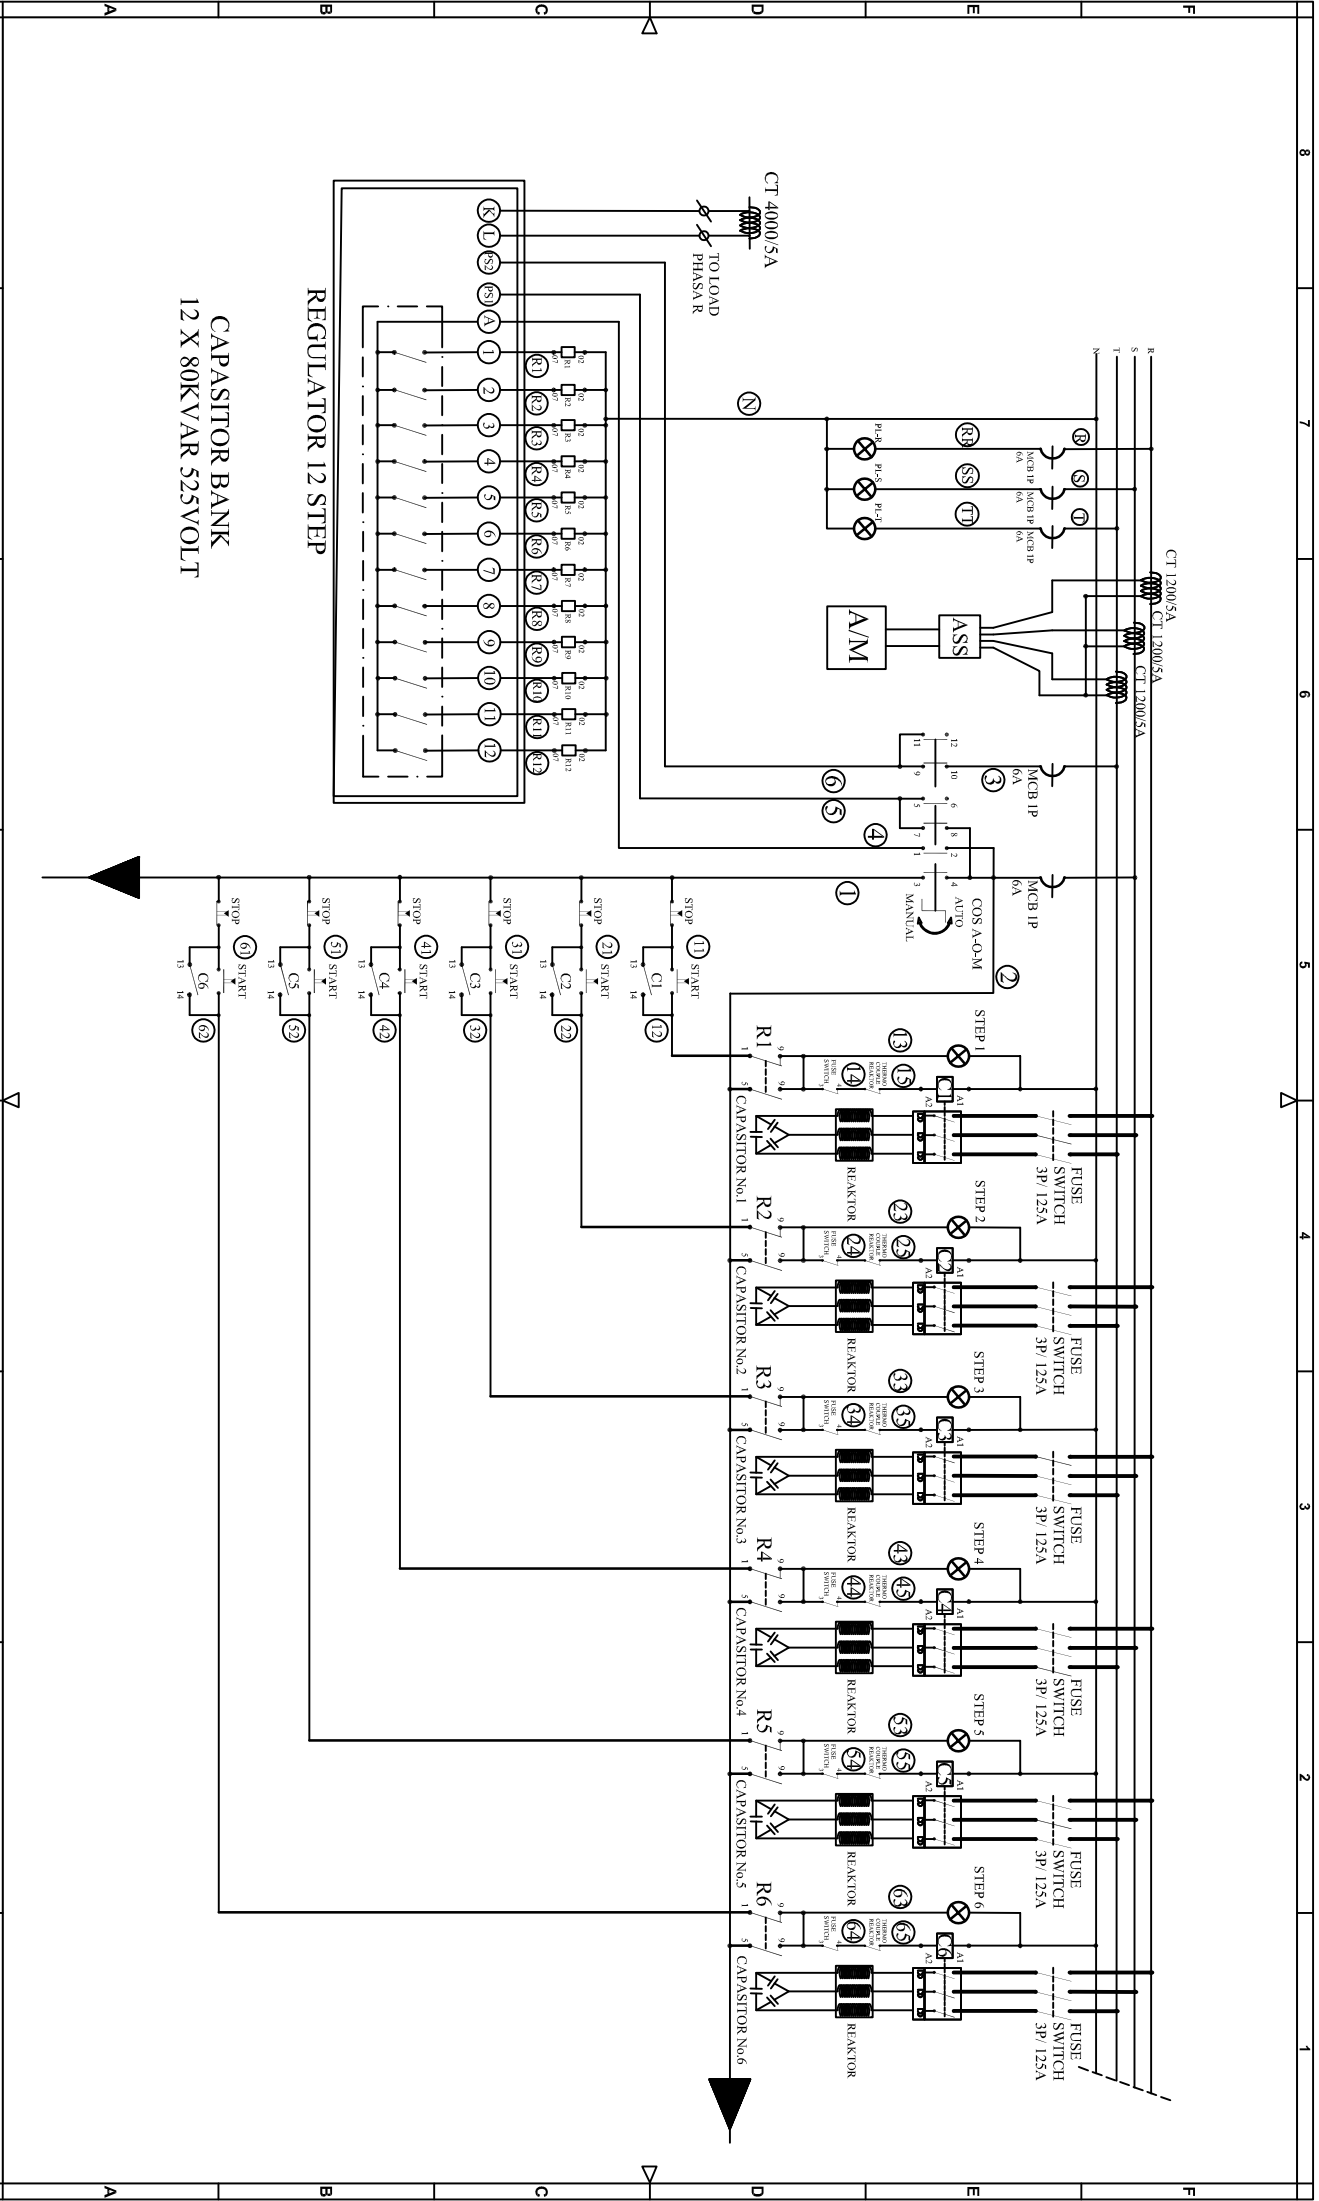

Customer : PT. MULTIMAS NABATI ASAHAN		Judd : 12 STEP X 80KVAR 525V (CT 4000/5A)		Revisi : 9 Juli 19		Tanggal : DJS		Dipertiksa Oleh : -		Disetujui Oleh : -	
Nama Proyek : MNA - 01 - 1814		DWG 16-01-19 (1)		Dimensi : mm		Skala : -		NTS		Toleransi Dimensi Panel Free Standing : +/- 1%	
No. Doc. : PRD 16-01-19 (1)		No. Dwg. : DWG 16-01-19 (1)		Toleransi Dimensi Panel Wall Mounting : +/- 2%		-		-		-	
PT. ANDALAS CITRA ELEKTRINDO		PFC-25B (Refinery #1)		12 STEP X 80KVAR 525V (CT 4000/5A)		-		-		-	
										Halaman : 1/3	



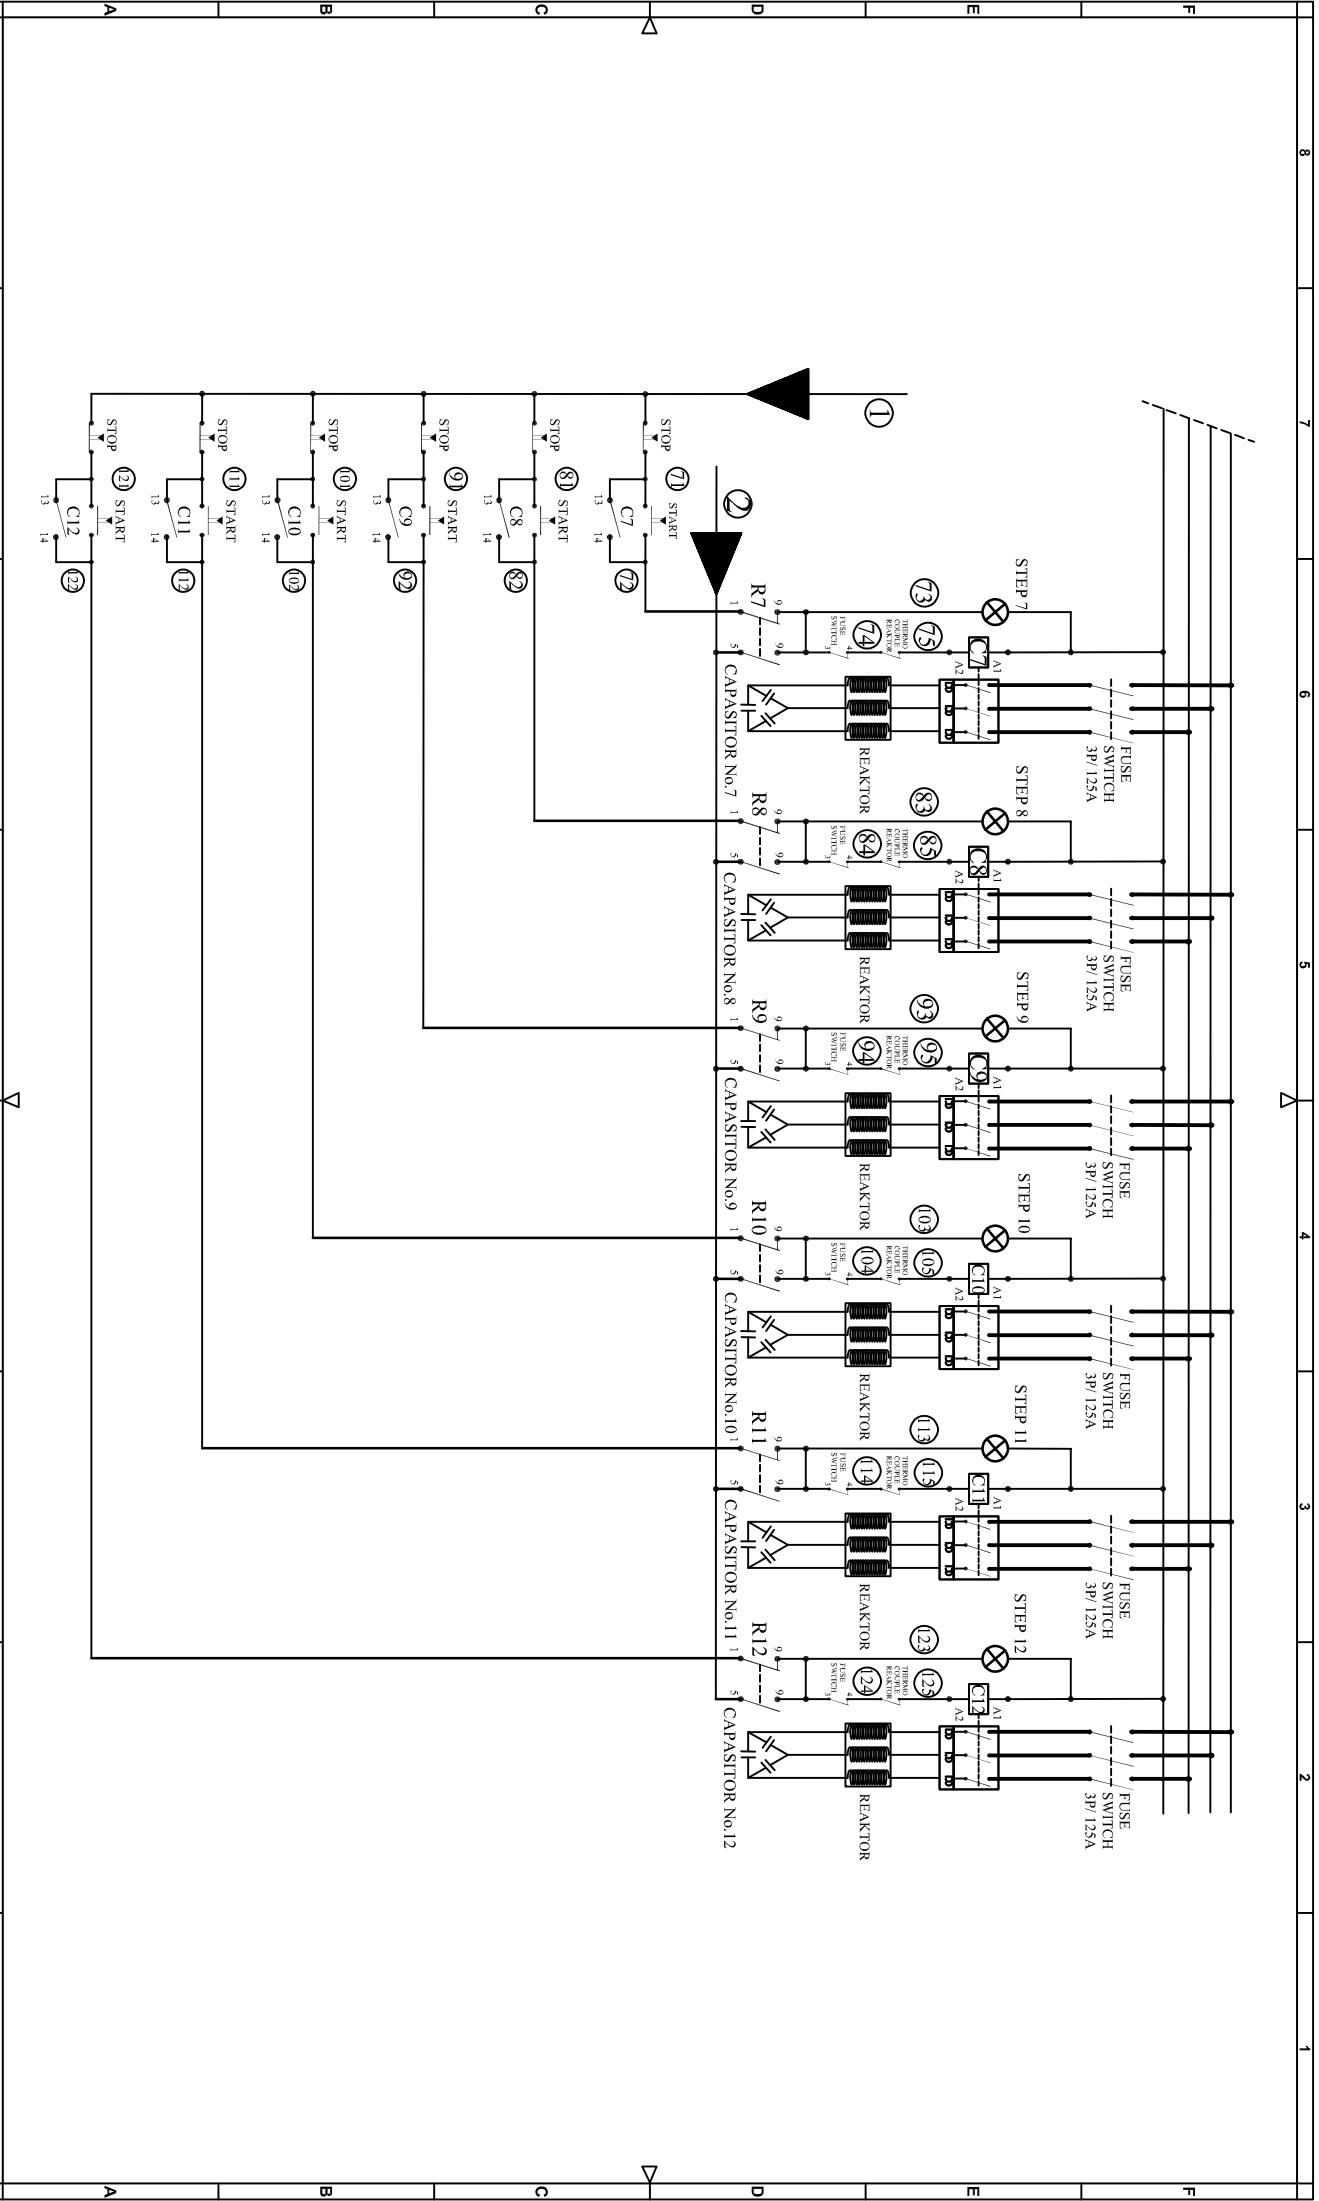

Customer : PT. MULTIMAS NABATI ASAHAN		Judd : PFC-25B (Refinery #1)		Revisi : 9 Juli 19		Tanggal : DJS		Dipertiksa Oleh : -		Disetujui Oleh : -	
Nama Proyek : MNA - 01 - 1814		12 STEP X 80K VAR 525V (CT 4000/5A)		-		-		-		-	
No. Dck : PRD 16-01-19 (1)		No. Dwg : DWG 16-01-19 (1)		Dimensi : mm		Skala : -		NTS		-	
PT. ANDALAS CITRA ELEKTRINDO		Toleransi Dimensi Panel Free Standing : +/- 1%		Toleransi Dimensi Panel Wall Mounting : +/- 2%		-		-		-	
										Halaman : 2/3	

