

WE RESERVE ALL RIGHTS IN THIS DOCUMENT AND IN THE INFORMATION CONTAINED THEREIN. REPRODUCTION, USE OR DISCLOSURE TO THIRD PARTIES WITHOUT EXPRESS AUTHORITY IS STRICTLY FORBIDDEN.

1		2		3		4		5		6		7		8		
A																
B																
C																
D																
E																
F																
				Date Prep.	26.03.2020	PROJECT TITLE				ABB EPMV		COVER SHEET		Scale	NTS	= H02
				Prepared	YR	BIODIESEL AND FLEXTech PLANT						BIODIESEL PLANT		Customer	PT Multimas Nabati Asahan	& 302
00	Issued for Approval	26.03.20	YR	Checked	AW									SCHEMATIC DIAGRAM		Drawing Nbr.
Ind.	Revision	Date	Name	Approved	AI	Based on: BE320003				PT. ABB Sakti Industri		SBC-W INCOMING 2		Customer Doc. Nbr.		Cont. 29
1		2		3		4		5		6		7		8		

UniSec

Medium Voltage Switchgear

PT MULTIMAS NABATI ASAHAN

BIODIESEL PLANT

SCHEMATIC DIAGRAM

SBC-W INCOMING 2

H02


WE RESERVE ALL RIGHTS IN THIS DOCUMENT AND IN THE INFORMATION CONTAINED THEREIN. REPRODUCTION, USE OR DISCLOSURE TO THIRD PARTIES WITHOUT EXPRESS AUTHORITY IS STRICTLY FORBIDDEN.


1		2		3		4		5		6		7		8		
A	-BG131	POSITION SWITCHES SIGNALLING DISCONNECTOR -QBD3 IN OPEN POSITION						-CA	CAPACITORS							A
	-BG132	POSITION SWITCHES SIGNALLING DISCONNECTOR -QBD3 IN CLOSED POSITION						-CA1	CAPACITOR FOR FRONT VENTILATOR							
	-BG133	POSITION SWITCHES SIGNALLING DISCONNECTOR -QBD3 IN OPEN POSITION AND NOT IN OPERATION (OPERATING LEVER NOT INSERTED)						-CA2	CAPACITOR FOR REAR VENTILATOR							
	-BG141...	POSITION SWITCHES SIGNALLING SWITCH-DISCONNECTOR -QBS CLOSED IN FEEDER POSITION						-EA1	LIGHTING LAMP LOCATED IN L.V. INSTRUMENT COMPARTMENT.							
	-BG142	POSITION SWITCHES SIGNALLING SWITCH-DISCONNECTOR -QBS IN OPEN POSITION						-EA2	LIGHTING LAMP LOCATED IN CABLE COMPARTMENT							
B	-BG143...	POSITION SWITCHES SIGNALLING SWITCH-DISCONNECTOR -QBS CLOSED IN EARTH POSITION						-EA3	LIGHTING LAMP LOCATED IN OPERATING MECHANISM ENCLOSURE							B
	-BG151	POSITION SWITCHES SIGNALLING DISCONNECTOR -QBD5 CLOSED IN FEEDER POSITION						-EA4	LIGHTING LAMP LOCATED IN CIRCUIT BREAKER COMPARTIMENT							
	-BG152	POSITION SWITCHES SIGNALLING DISCONNECTOR -QBD5 IN OPEN POSITION						-EB1	HEATER LOCATED IN CABLE COMPARTMENT							
	-BG153	POSITION SWITCHES SIGNALLING DISCONNECTOR -QBD5 CLOSED IN EARTH POSITION						-EB2	HEATER LOCATED IN CIRCUIT-BREAKER COMPARTMENT							
	-BGK	POSITION SWITCH OF KEY LOCK						-EB3	HEATER LOCATED IN MOTOR CABINET							
C	-BGL1	POSITION SWITCH OF ELECTROMECHANICAL LOCK -RLE1						-EB4	HEATER FOR VENTILATION TEST							C
	-BGS1...-BG54	POSITION SWITCHES OF CIRCUIT-BREAKER SPRINGS						-EB5	HEATER LOCATED IN L.V. INSTRUMET COMPARTMENT.							
	-BGS5	PROXIMITY SWITCH SIGNALLING SPRINGS IN CHARGED POSITION						-EB7	HEATERS LOCATED IN LEFT SIDE OF THE OPERATING MECHANISM ENCLOSURE							
	-BGT1	POSITION SWITCHES ON TRUCK SIGNALLING TRUCK IN SERVICE POSITION						-EB8	HEATERS LOCATED IN RIGHT SIDE OF THE OPERATING MECHANISM ENCLOSURE							
	-BGT2	POSITION SWITCHES ON TRUCK SIGNALLING TRUCK IN TEST POSITION						-FA1	SURGE ARRESTER LOCATED ON PHASE L1							
D	-BGT3	POSITION SWITCH ON TRUCK SIGNALLING TRUCK NOT IN ISOLATING TRAVEL POSITION						-FA2	SURGE ARRESTER LOCATED ON PHASE L2							D
	-BGT4	POSITION SWITCHES ON SWITCHGEAR SIGNALLING TRUCK IN SERVICE POSITION						-FA3	SURGE ARRESTER LOCATED ON PHASE L3							
	-BGT5	POSITION SWITCHES ON SWITCHGEAR SIGNALLING TRUCK IN TEST POSITION						-FCD	FUSE-DISCONNECTORS FOR PROTECTION OF AUXILIARY CIRCUITS							
	-BGT6	POSITION SWITCHES SIGNALLING V.T. TRUCK IN SERVICE POSITION						-FCF1	MEDIUM VOLTAGE FUSE LOCATED ON PHASE L1							
	-BGT7	POSITION SWITCHES SIGNALLING V.T. TRUCK IN TEST POSITION						-FCF2	MEDIUM VOLTAGE FUSE LOCATED ON PHASE L2							
E	-BGT8	POSITION SWITCHES SIGNALLING EARTHING TRUCK IN SERVICE POSITION						-FCF3	MEDIUM VOLTAGE FUSE LOCATED ON PHASE L3							E
	-BGT11	PROXIMITY SWITCH SIGNALLING TRUCK IN SERVICE POSITION						-FCM1	MINIATURE CIRCUIT-BREAKER FOR PROTECTION OF SPRINGS CHARGING MOTOR ON MAIN CIRCUIT-BREAKER							
	-BGT12	PROXIMITY SWITCH SIGNALLING TRUCK IN TEST POSITION						-FCM2...-FCM10	MINIATURE CIRCUIT-BREAKERS FOR PROTECTION OF AUXILIARY CIRCUITS							
	-BGV1	POSITION SWITCH OF FRONT VENTILATOR						-FCM11	MINIATURE CIRCUIT-BREAKER FOR PROTECTION OF VENTILATOR -MV1							
	-BGV2	POSITION SWITCH OF REAR VENTILATOR						-FCM12	MINIATURE CIRCUIT-BREAKER FOR PROTECTION OF VENTILATOR -MV2							
F	-BM	HYGROSTAT						-FCM13	MINIATURE CIRCUIT-BREAKER FOR PROTECTION OF VENTILATOR -MV3							F
	-BPA4	PRESSURE SWITCH LOCATED IN CABLE COMPARTMENT FOR DETECTION OF INTERNAL ARCING						-FCT	THERMAL OVERLOAD RELEASES							
	-BPA5	PRESSURE SWITCH LOCATED IN CIRCUIT-BREAKER OR IN UPPER VT COMPARTMENT FOR DETECTION OF INTERNAL ARCING						-GA	GENERATORS							
	-BPA6	PRESSURE SWITCH LOCATED IN BUSBAR OR IN BUSBAR AND CIRCUIT-BREAKER COMPARTMENT FOR DETECTION OF INTERNAL ARCING						-GQ1	FRONT VENTILATOR							
	-BPA7	PRESSURE SWITCH LOCATED IN VOLTAGE TRANSFORMER ISOLATING COMPARTMENT FOR DETECTION OF INTERNAL ARCING						-GQ2	REAR VENTILATOR							
G	-BPS1	PRESSURE SWITCH LOCATED ON CIRCUIT-BREAKER OR ON POLE OF PHASE L1 OF CIRCUIT-BREAKER						-GQ3	VENTILATOR LOCATED ON CIRCUIT-BREAKER TRUCK							G
	-BPS2	PRESSURE SWITCH LOCATED ON CIRCUIT-BREAKER POLE OF PHASE L2						-KFA1	AUXILIARY RELAY SIGNALLING LOW GAS PRESSURE							
	-BPS3	PRESSURE SWITCH LOCATED ON CIRCUIT-BREAKER POLE OF PHASE L3						-KFA2	AUXILIARY RELAY SIGNALLING INSUFFICIENT GAS PRESSURE							
	-BR	FLAME DETECTORS, SMOKE DETECTORS						-KFA3...-KFA9	AUXILIARY RELAYS OR CONTACTORS							
	-BT	THERMOSTAT						-KFC	CLOSING RELAYS OR CONTACTORS							
H	-BT1	THERMOSTAT FOR DE-ENERGIZATION OF VENTILATORS						-KFI	INTEGRATED CIRCUITS							H
	-BT2	THERMOSTAT FOR ENERGIZATION OF VENTILATORS						-KFL	LOCKOUT RELAY							
	-BT3	THERMOSTAT SIGNALLING HIGH TEMPERATURE ALARM						-KFM	MICROPROCESSORS							
	-BU	BUCHHOLZ RELAY						-KFN	ANTIPUMPING RELAYS							
	-BX1	UNIT WITH SENSORS FOR DETECTION OF INTERNAL ARCING						-KFO	OPENING RELAYS OR CONTACTORS							
I	-BX2	ADDITIONAL CURRENT SENSING UNIT FOR DETECTION OF INTERNAL ARCING						-KFP	PROGRAMMABLE LOGIC CONTROLLERS (PLC)							I
	-BZ,-BZ4	MULTIFUNCTION SENSORS						-KFR	RECLOSING RELAYS							
	-BZ1	COMBINED CURRENT AND VOLTAGE SENSOR, LOCATED ON PHASE L1						-KFS	SYNCHRONIZING DEVICES							
	-BZ2	COMBINED CURRENT AND VOLTAGE SENSOR, LOCATED ON PHASE L2						-KFT	AUXILIARY TIME RELAYS, DELAY ELEMENTS							
	-BZ3	COMBINED CURRENT AND VOLTAGE SENSOR, LOCATED ON PHASE L3						-KFZ	CONTROLLERS							
J								-MBC	CLOSING RELEASE OF CIRCUIT-BREAKER							J
								-MAD	MOTOR FOR ELECTRICAL OPERATION OF DISCONNECTOR -QBD							
								-MAD1	MOTOR FOR ELECTRICAL OPERATION OF DICONNECTOR -QBD1							
								-MAD2	MOTOR FOR ELECTRICAL OPERATION OF DICONNECTOR -QBD2							
								-MAD9	MOTOR FOR ELECTRICAL OPERATION OF SWITCH-DISCONNECTOR -QBS							
Ind.		Revision	Date	Name	Approved	Based on:		PT. ABB Sakti Industri		SBC-W INCOMING 2		Customer Doc. Nbr.		Cont.		
1		2		3		4		5		6		7		8		

WE RESERVE ALL RIGHTS IN THIS DOCUMENT AND IN THE INFORMATION CONTAINED THEREIN. REPRODUCTION, USE OR DISCLOSURE TO THIRD PARTIES WITHOUT EXPRESS AUTHORITY IS STRICTLY FORBIDDEN.

1		2		3		4		5		6		7		8						
A	-TFA	ACTIVE POWER TRANSDUCERS						-XD11	TERMINAL BLOCK FOR INTERCONNECTIONS OF CONTROL CIRCUITS							A				
	-TFC	CURRENT TRANSDUCERS						-XD12	TERMINAL BLOCK FOR INTERCONNECTIONS OF CIRCUITS OF MOTOR FOR CIRCUIT-BREAKER SPRINGS CHARGING											
	-TFF	FREQUENCY TRANSDUCERS						-XD13	TERMINAL BLOCK FOR INTERCONNECTIONS OF CIRCUITS OF MOTOR FOR SWITCH-DISCONNECTOR OPERATION											
	-TFJ	ACTIVE ENERGY TRANSDUCERS						-XD14	TERMINAL BLOCK FOR INTERCONNECTIONS OF A.C. AUXILIARY CIRCUITS											
	-TFK	REACTIVE ENERGY TRANSDUCERS						-XD16	TERMINAL BLOCK FOR INTERCONNECTION (CONNECTION BETWEEN PANELS) OF VOLTAGE CIRCUITS											
	-TFM	MULTIFUNCTION TRANSDUCERS						-XD17	TERMINAL BLOCK FOR INTERCONNECTION OF MOD-BUS											
	-TFP	POWER-FACTOR TRANSDUCERS						-XD18	TERMINAL BLOCK FOR INTERCONNECTIONS OF CURRENT CIRCUITS											
	-TFQ	REACTIVE POWER TRANSDUCERS						-XD19	TERMINAL BLOCK FOR SPECIAL USE											
	-TFS	SIGNAL CONVERTERS						-XDJ	TERMINAL BLOCK FOR AUXILIARY CIRCUITS OF DISCONNECTORS -QBD											
	-TFV	VOLTAGE TRANSDUCERS						-XDJ1	TERMINAL BLOCK FOR AUXILIARY CIRCUITS OF SWITCH-DISCONNECTOR -QBS											
B	-WA	BUSBARS						-XDM	SEALABLE TERMINAL BLOCK FOR MEASUREMENT							B				
	-WBC	POWER CABLES						-XDS	CURRENT SOCKETS											
	-WE	EARTHING CABLES FOR L.V. INSTRUMENT COMPARTMENT.						-XDT	TERMINAL BLOCK FOR POSITION CONTACTS OF TRUCK AND OF CONNECTOR -XDB											
	-WGC	CONTROL CABLES						-XDU	CONNECTOR FOR ISOLATION OF CIRCUITS OF LOWER VOLTAGE TRANSFORMER TRUCK											
	-WGS	COMMUNICATION CABLES (SHIELDED TWISTED PAIRS)						-XDU1	TERMINAL BLOCK FOR CIRCUITS OF LOWER VOLTAGE TRANSFORMER TRUCK											
	-WH	OPTICAL FIBRES						-XDV	TERMINAL BLOCK FOR CIRCUITS OF VOLTAGE TRANSFORMERS											
	-XDA	TERMINAL BLOCK FOR CIRCUITS OF CURRENT TRANSFORMERS						-XDV1	CONNECTOR FOR CIRCUITS OF VOLTAGE TRANSFORMERS LOCATED ON PHASE L1											
	-XDA1	CONNECTOR FOR CIRCUITS OF CURRENT TRANSFORMERS LOCATED ON PHASE L1						-XDV2	CONNECTOR FOR CIRCUITS OF VOLTAGE TRANSFORMERS LOCATED ON PHASE L2											
	-XDA2	CONNECTOR FOR CIRCUITS OF CURRENT TRANSFORMERS LOCATED ON PHASE L2						-XDV3	CONNECTOR FOR CIRCUITS OF VOLTAGE TRANSFORMERS LOCATED ON PHASE L3											
	-XDA3	CONNECTOR FOR CIRCUITS OF CURRENT TRANSFORMERS LOCATED ON PHASE L3						-XDV4	CONNECTOR FOR CIRCUITS OF ANTIFERRORESONANCE RESISTOR											
C	-XDA5	CONNECTOR FOR CIRCUITS OF NEUTRAL (RESIDUAL) CURRENT TRANSFORMER						-XDX	SUPPORT TERMINAL BLOCK							C				
	-XDB	CONNECTOR FOR ISOLATION OF CIRCUIT-BREAKER (OR UPPER VOLTAGE TRANSFORMER TRUCK) AUXILIARY CIRCUITS						-XE1	EARTHING TERMINAL BLOCKS FOR LV COMPARTMENT, LEFT SIDE											
	-XDB1	CONNECTOR FOR AUXILIARY CIRCUITS OF CIRCUIT-BREAKER (OR UPPER VOLTAGE TRANSFORMER TRUCK)						-XE2	EARTHING TERMINAL BLOCKS FOR LV COMPARTMENT, RIGHT SIDE											
	-XDB2	CONNECTOR FOR ADDITIONAL AUXILIARY CIRCUITS OF CIRCUIT-BREAKER						-XE5	EARTHING TERMINAL BLOCKS FOR MV COMPARTMENT, VOLTAGE INDICATOR SIDE											
	-XDB10...-XDB89	CONNECTOR FOR CIRCUIT-BREAKER INTERNAL CIRCUITS						-XE6	EARTHING TERMINAL BLOCKS FOR MV COMPARTMENT, REAR BOTTOM SIDE											
	-XDB7	CONNECTOR FOR TRUCK POSITION CONTACTS						-XE7	EARTHING TERMINAL BLOCKS FOR MV COMPARTMENT, LEFT SIDE											
	-XDB91	CONNECTOR FOR OPENING RELEASE CIRCUITS OF SWITCH-DISCONNECTOR						-XE8	EARTHING TERMINAL BLOCKS FOR MV COMPARTMENT, FRONT BOTTOM SIDE											
	-XDB92	CONNECTOR FOR CLOSING RELEASE CIRCUITS OF SWITCH-DISCONNECTOR						-XE9	EARTHING TERMINAL BLOCK FOR TRANSFORMERS IN BUSBAR COMPARTMENT											
	-XDB93	CONNECTOR FOR POSITION SWITCHES OF SWITCH-DISCONNECTOR																		
	-XDB95	CONNECTOR FOR CIRCUITS OF EARTHING SWITCH LOCKING MAGNET																		
D	-XDC	CUSTOMER TERMINAL BLOCK														D				
	-XDC1	CUSTOMER TERMINAL BLOCK FOR AUXILIARY CIRCUITS OF CIRCUIT BREAKER																		
	-XDC2	CUSTOMER TERMINAL BLOCK FOR AUXILIARY CIRCUITS OF SWITCH-DISCONNECTOR																		
	-XDC3	CUSTOMER TERMINAL BLOCK FOR AUXILIARY CIRCUITS OF PROTECTION RELAY AND MULTIFUNCTION UNIT																		
	-XDC4	CUSTOMER TERMINAL BLOCK FOR AUXILIARY CIRCUITS OF VOLTAGE TRANSFORMERS																		
	-XDC5	CUSTOMER TERMINAL BLOCK FOR AUXILIARY CIRCUITS OF MINIATURE CIRCUIT BREAKER																		
	-XDE	TERMINAL BLOCK FOR AUXILIARY CIRCUITS OF EARTHING SWITCH -QCE																		
	-XDE1	TERMINAL BLOCK FOR INTERNAL CIRCUITS OF EARTHING SWITCH -QCE																		
	-XDE2	TERMINAL BLOCK FOR AUXILIARY CIRCUITS OF EARTHING SWITCH -QCE1 OR -QCE2																		
	-XDE3	TERMINAL BLOCK FOR INTERNAL CIRCUITS OF EARTHING SWITCH -QCE1 OR -QCE2																		
E	-XDF	TERMINAL BLOCK FOR AUXILIARY CIRCUITS OF FORCED COOLING VENTILATORS														E				
	-XDF1	CONNECTOR FOR ISOLATION OF CIRCUITS OF FRONT VENTILATOR																		
	-XDF2	CONNECTOR FOR REAR VENTILATOR CIRCUITS																		
	-XDF3	CONNECTOR FOR FRONT VENTILATOR CIRCUITS																		
	-XDH	TERMINAL BLOCK FOR VARIOUS CIRCUITS (HEATERS, POSITION SWITCHES DETECTING INTERNAL ARCING, ETC.)																		
	-XDI	TERMINAL BLOCK FOR INTERCONNECTION (CONNECTION BETWEEN PANELS)																		
F					Date Prep.	26.03.2020	PROJECT TITLE		ABB	EPMV	REFERENCE DESIGNATIONS		Scale	NTS	= H02	F				
					Prepared	YR	BIODIESEL AND FLEXTech PLANT						Customer	PT Multimas Nabati Asahan	& 302					
	00	Issued for Approval	26.03.20	YR	Checked	AW	Drawing Nbr.	20.003-MNA-302					Sh.	6						
	Ind.	Revision	Date	Name	Approved	AI	Based on:	BE320003			PT. ABB Sakti Industri		SCHEMATIC DIAGRAM		SBC-W INCOMING 2					
													Customer Doc. Nbr.		Cont.		29			
1		2		3		4		5		6		7		8						

WE RESERVE ALL RIGHTS IN THIS DOCUMENT AND IN THE INFORMATION CONTAINED THEREIN. REPRODUCTION, USE OR DISCLOSURE TO THIRD PARTIES WITHOUT EXPRESS AUTHORITY IS STRICTLY FORBIDDEN.

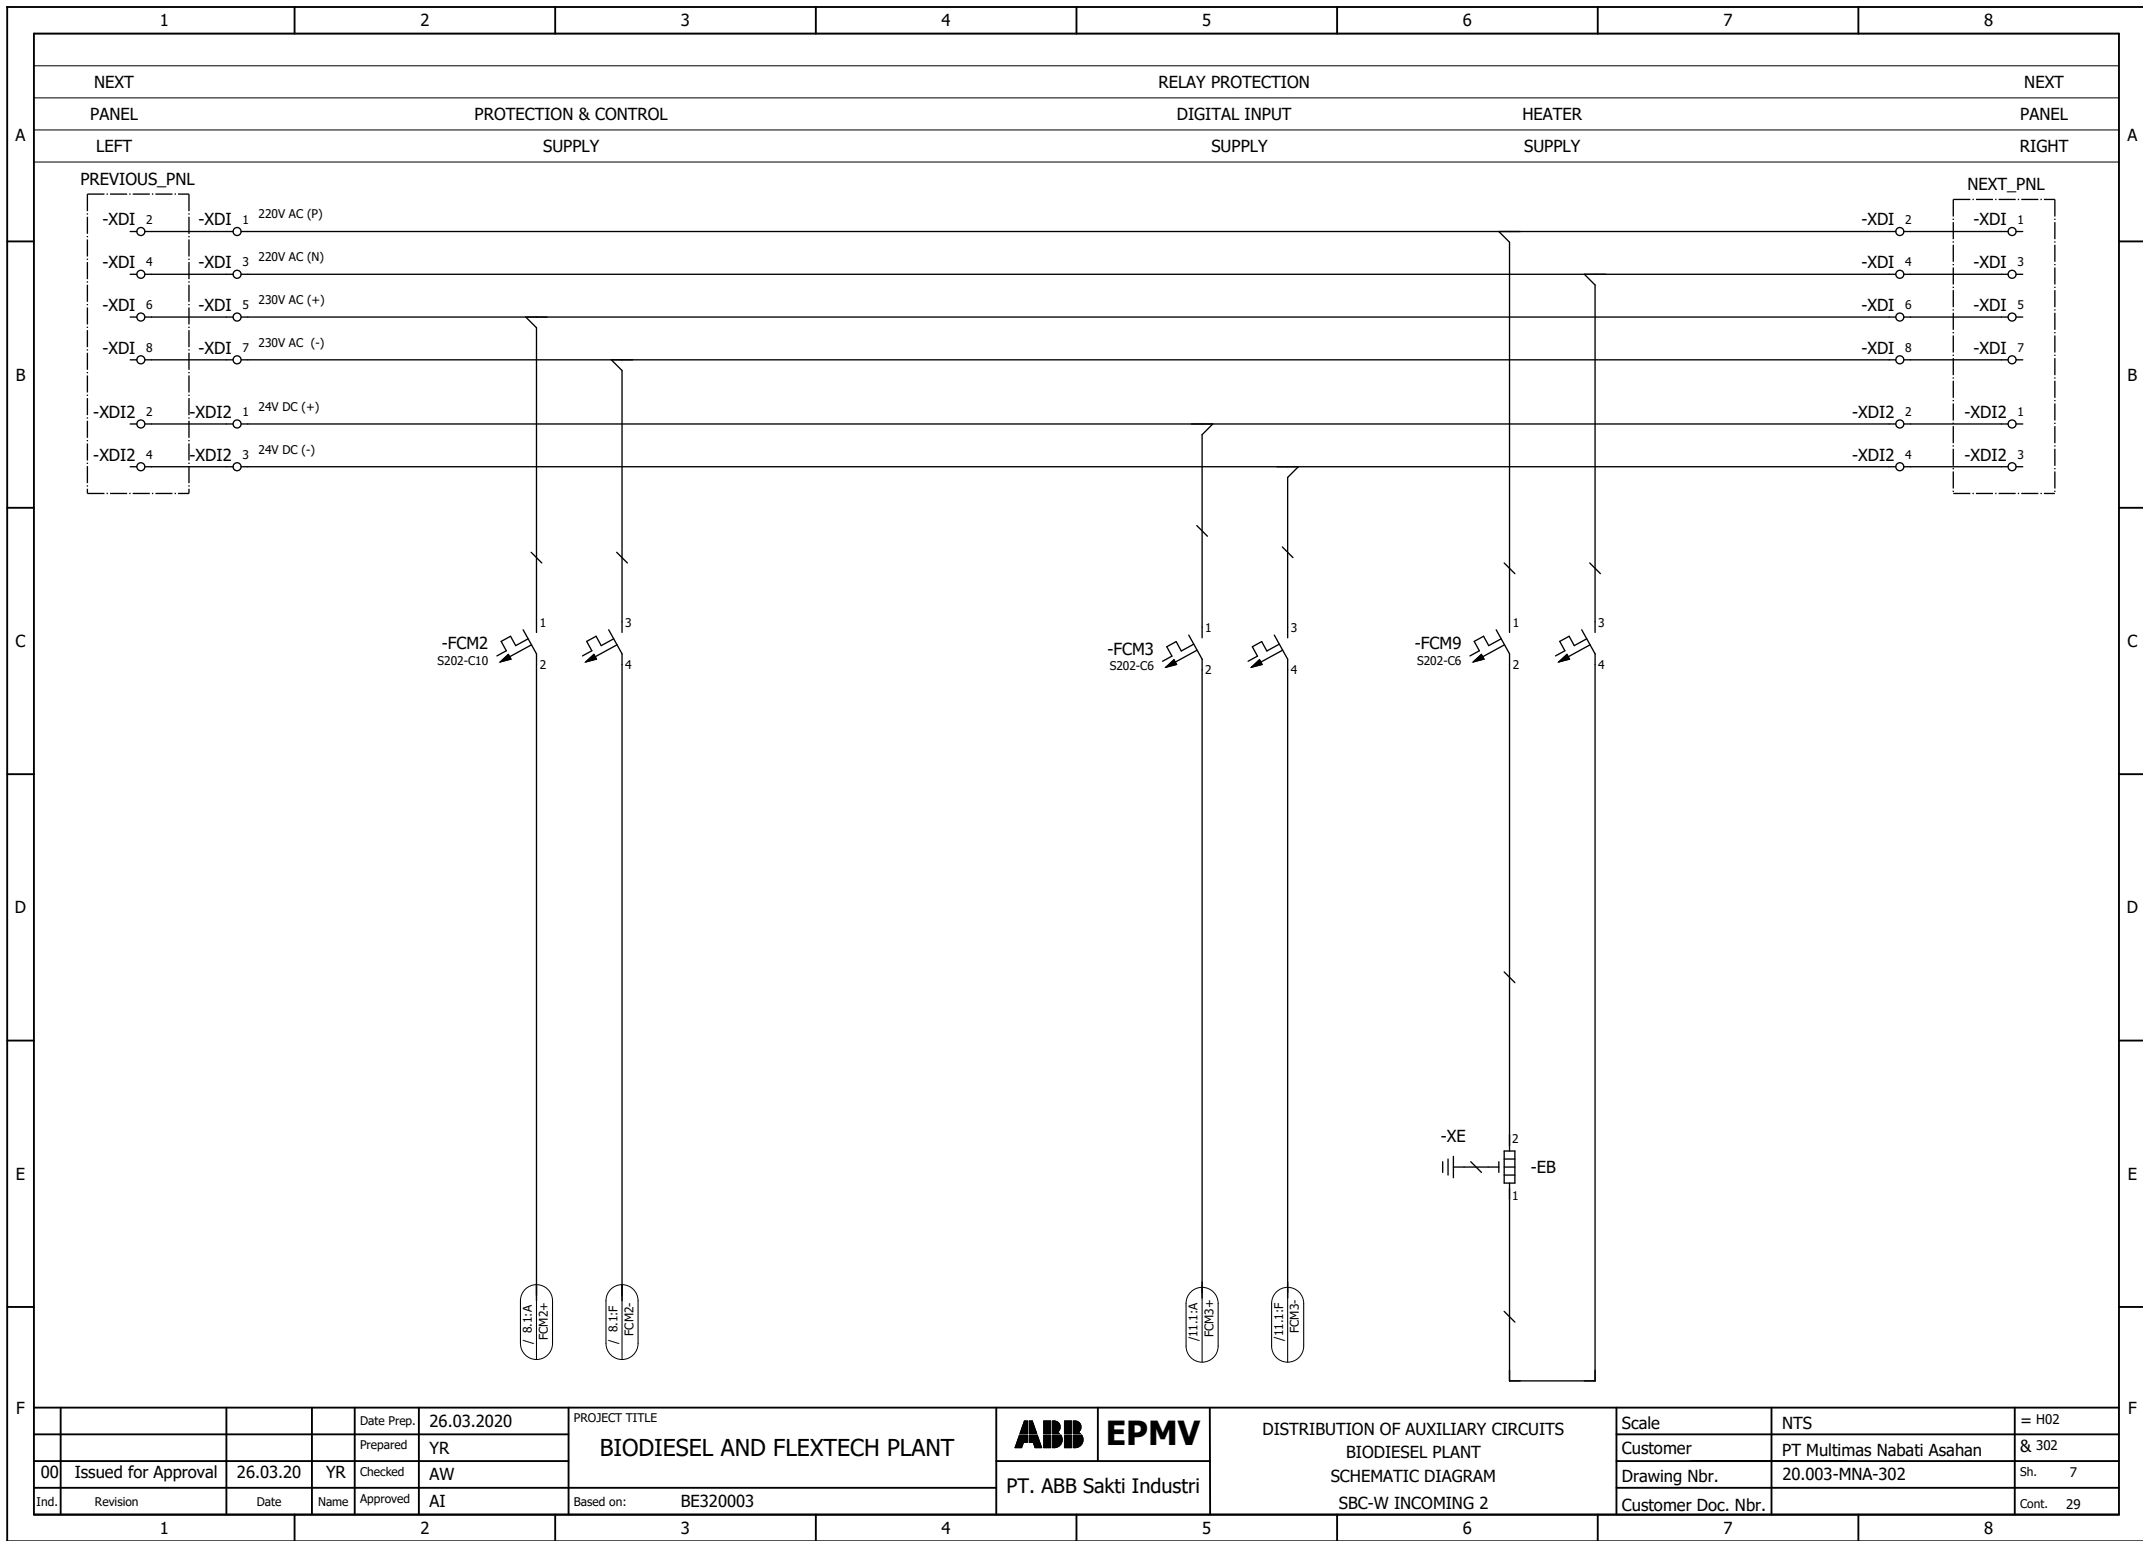


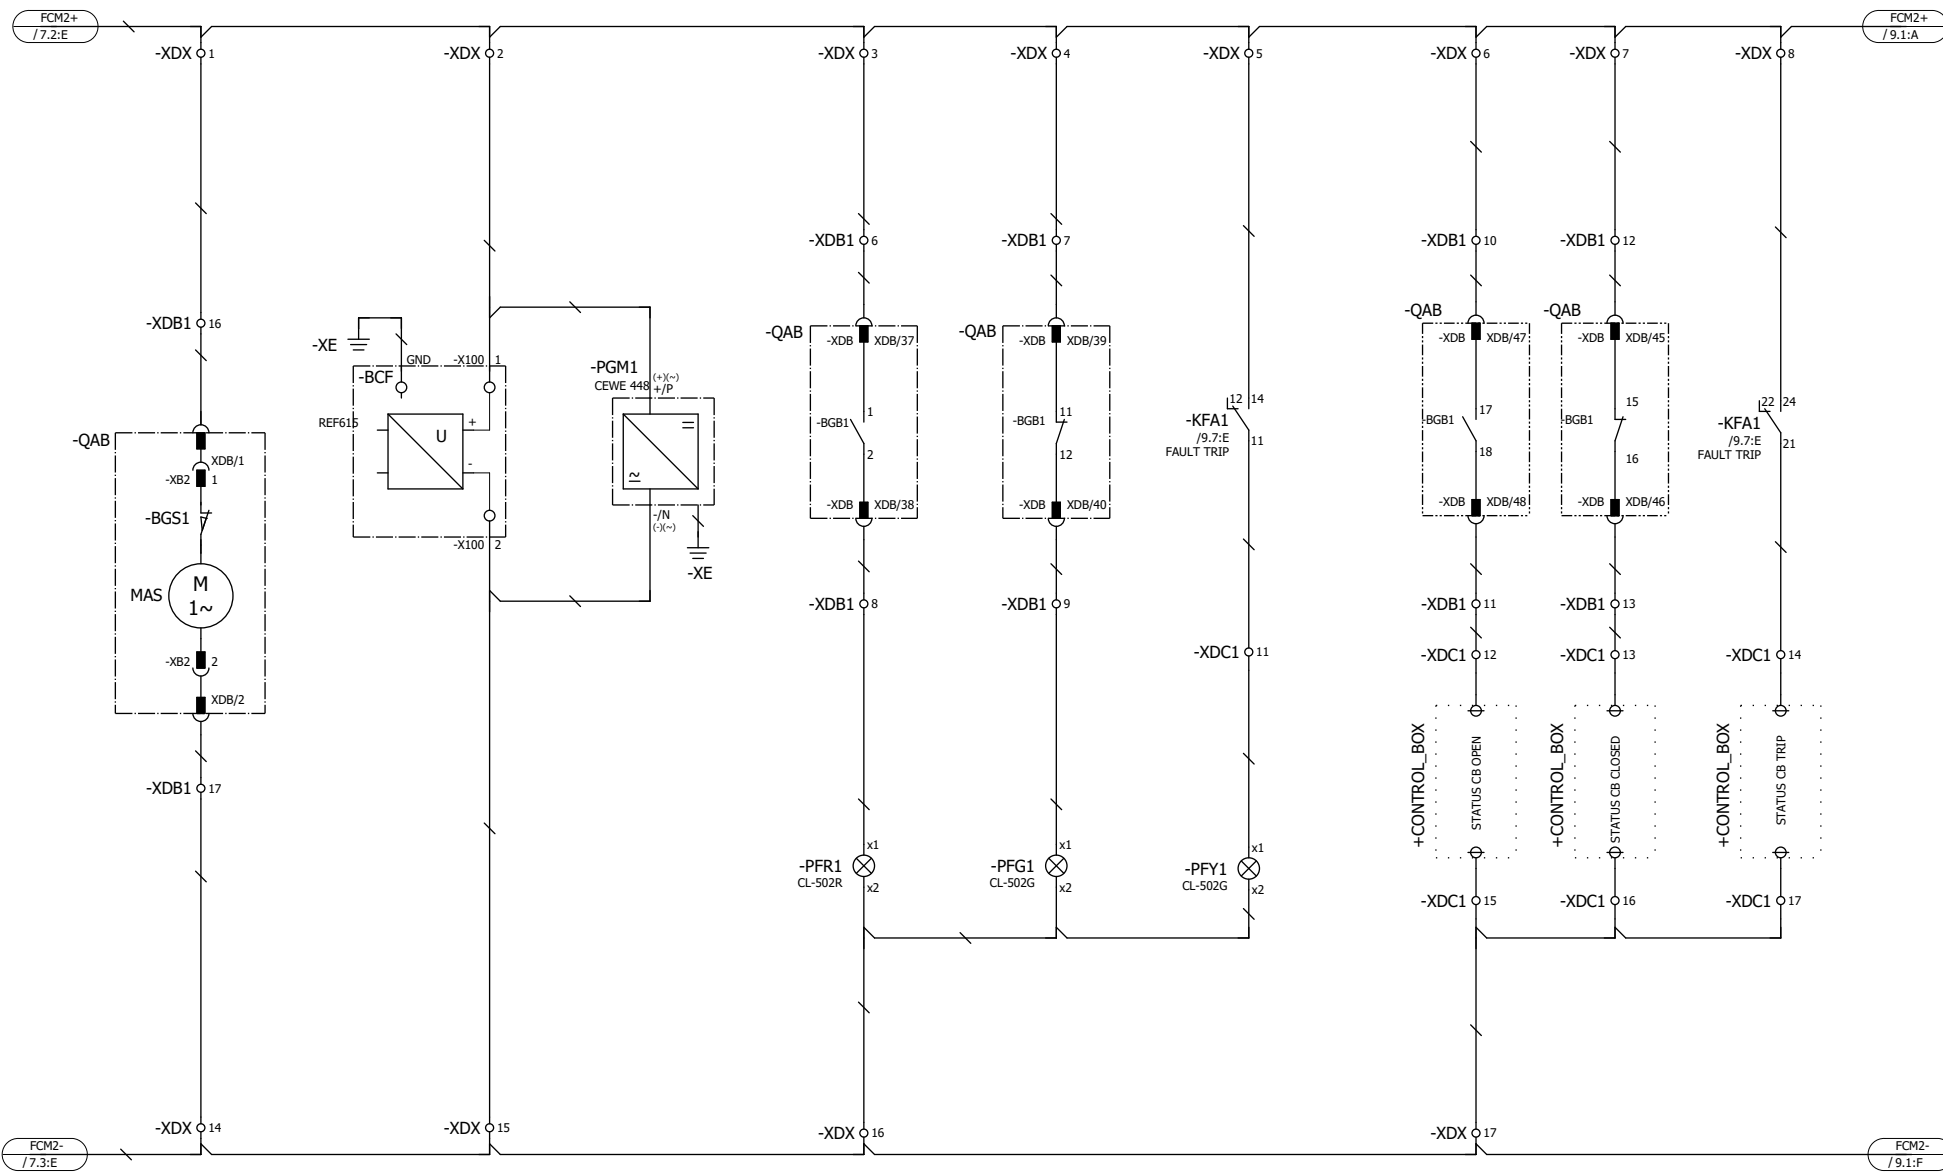

			Date Prep.	26.03.2020	PROJECT TITLE BIODIESEL AND FLEXTech PLANT	ABB	EPMV	AUXILIARY CIRCUIT BIODIESEL PLANT SCHEMATIC DIAGRAM SBC-W INCOMING 2	Scale	NTS	= H02		
			Prepared	YR					Customer	PT Multimas Nabati Asahan	& 302		
00	Issued for Approval	26.03.20	YR	Checked		AW	PT. ABB Sakti Industri		Drawing Nbr.	20.003-MNA-302	Sh.	8	
Ind.	Revision	Date	Name	Approved	AI	Based on:			BE320003	Customer Doc. Nbr.		Cont.	29

			Date Prep.	26.03.2020	PROJECT TITLE BIODIESEL AND FLEXTech PLANT	ABB	EPMV	DIGITAL INPUT/OUTPUT RELAY BIODIESEL PLANT SCHEMATIC DIAGRAM SBC-W INCOMING 2	Scale	NTS	= H02	
			Prepared	YR					Customer	PT Multimas Nabati Asahan	& 302	
00	Issued for Approval	26.03.20	YR	Checked		AW	PT. ABB Sakti Industri		Drawing Nbr.	20.003-MNA-302	Sh.	11
Ind.	Revision	Date	Name	Approved	AI	Based on: BE320003			Customer Doc. Nbr.		Cont.	29

WE RESERVE ALL RIGHTS IN THIS DOCUMENT AND IN THE INFORMATION CONTAINED THEREIN. REPRODUCTION, USE OR DISCLOSURE TO THIRD PARTIES WITHOUT EXPRESS AUTHORITY IS STRICTLY FORBIDDEN.

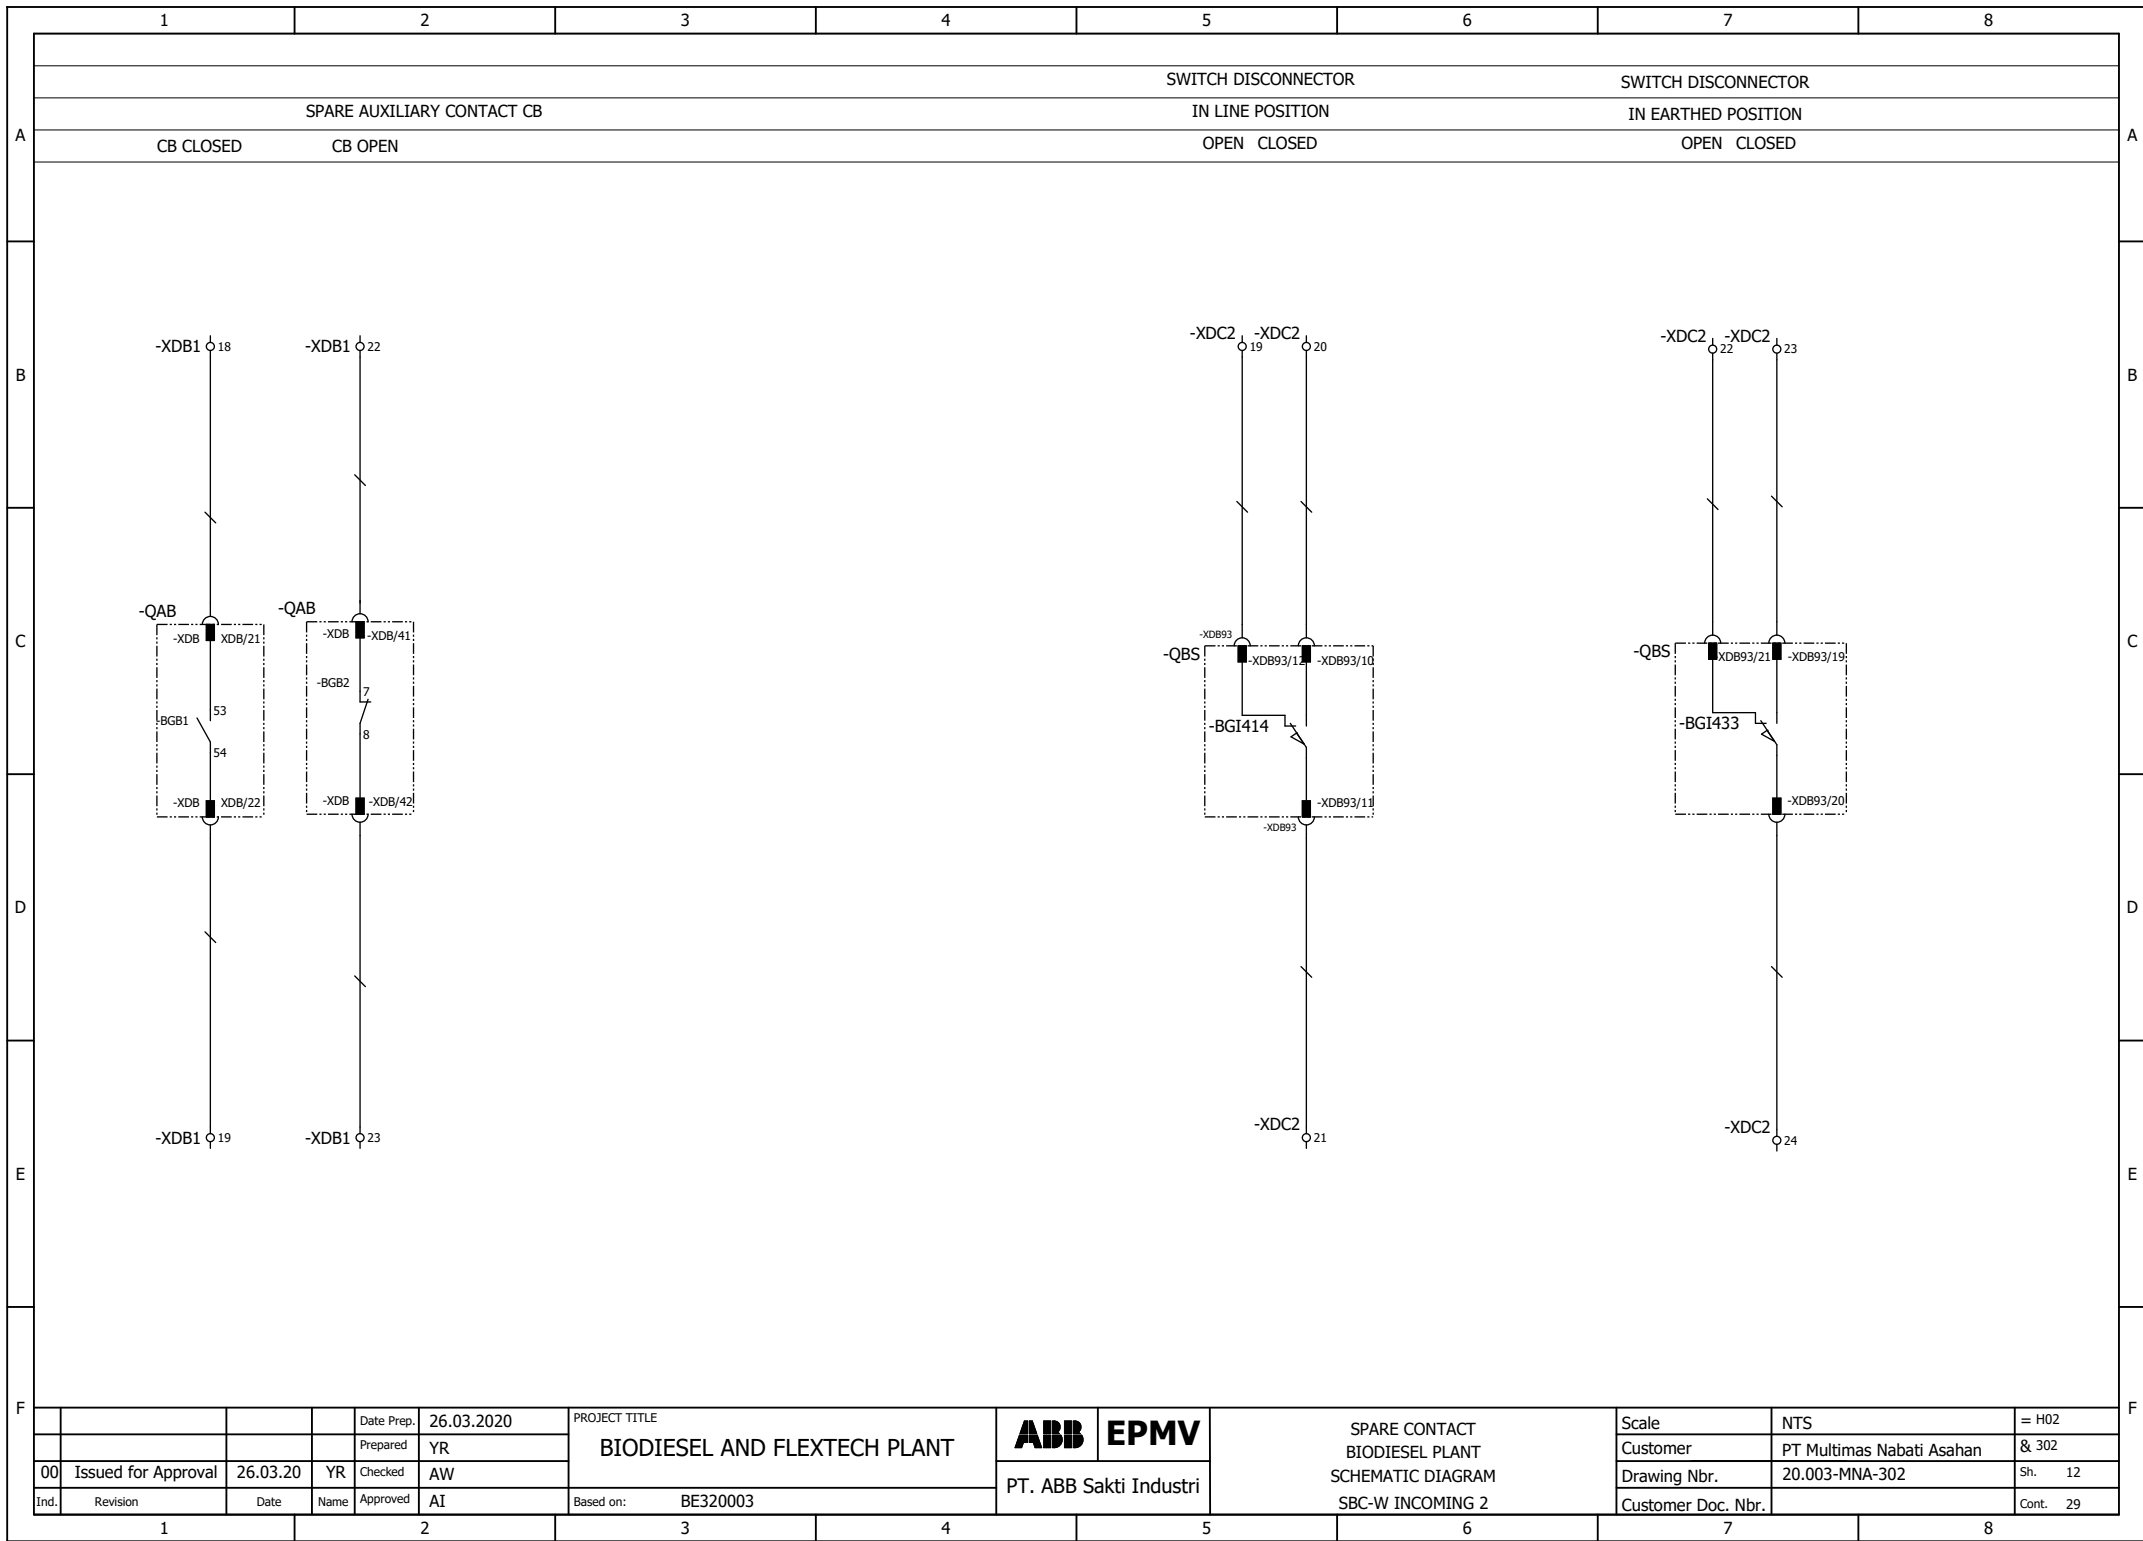


				Date Prep.	26.03.2020
				Prepared	YR
00	Issued for Approval	26.03.20	YR	Checked	AW
Ind.	Revision	Date	Name	Approved	AI

PROJECT TITLE	
BIODIESEL AND FLEXTech PLANT	
Based on:	BE320003

ABB	EPMV
PT. ABB Sakti Industri	

SPARE CONTACT
BIODIESEL PLANT
SCHEMATIC DIAGRAM
SBC-W INCOMING 2


Scale	NTS	= H02
Customer	PT Multimas Nabati Asahan	& 302
Drawing Nbr.	20.003-MNA-302	Sh. 12
Customer Doc. Nbr.		Cont. 29

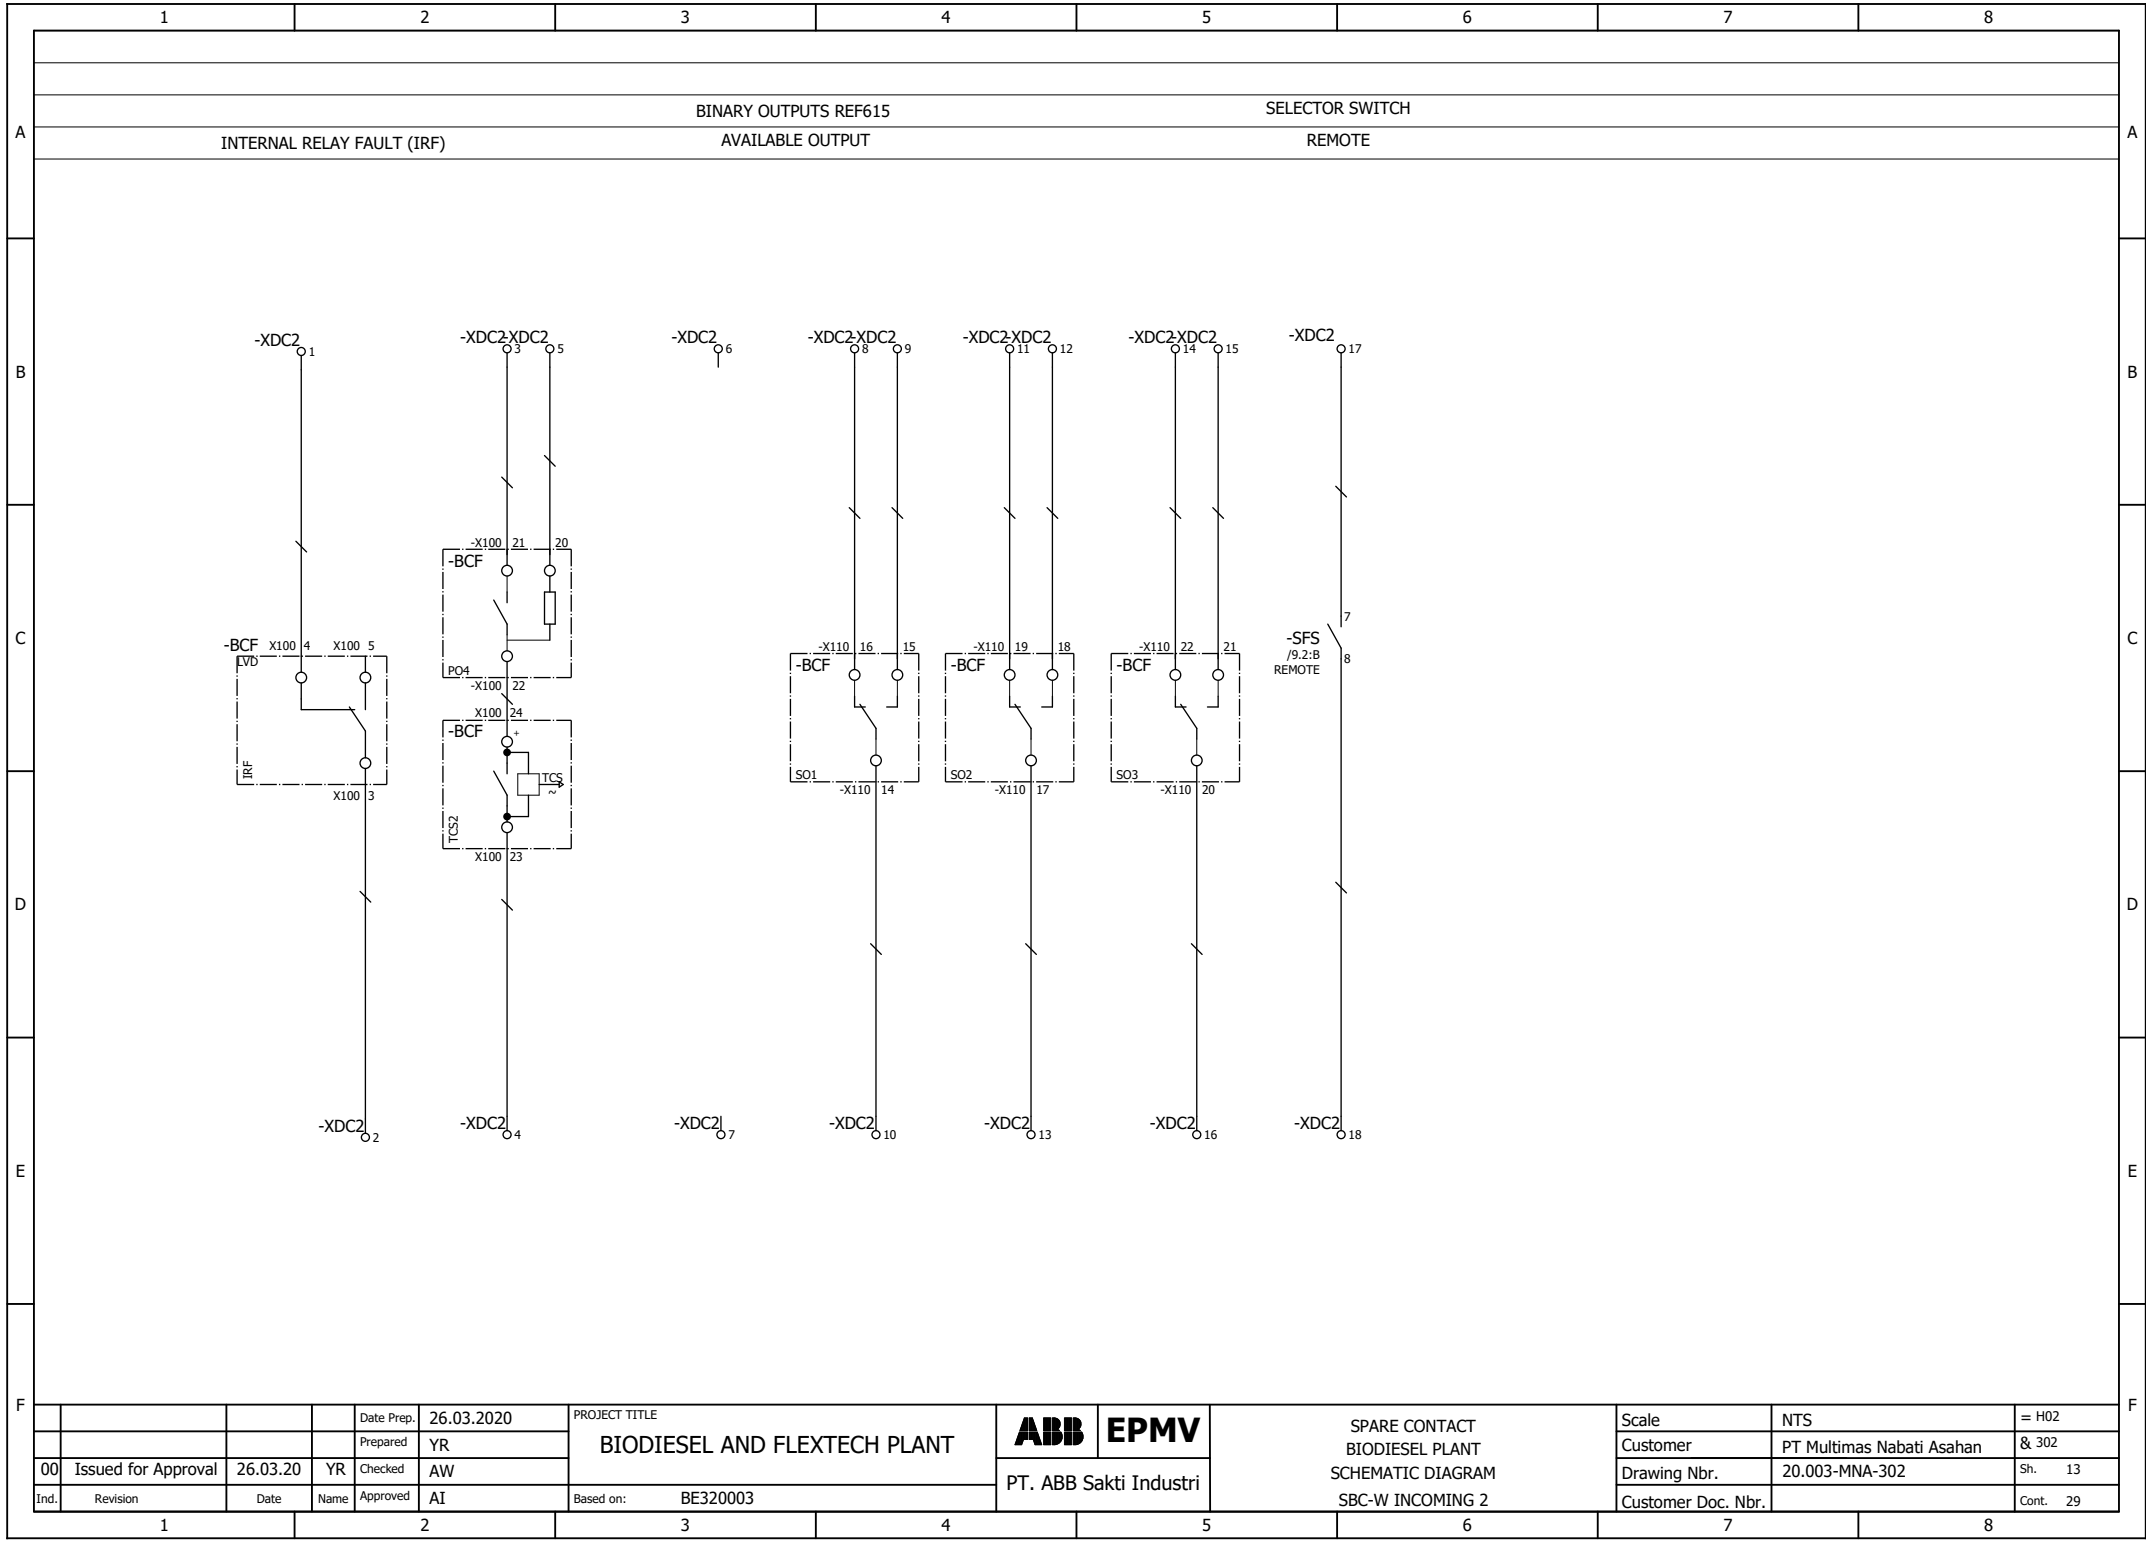[illegible]

	1	2	3	4	5	6	7	8	
A	BINARY OUTPUTS REF615				SELECTOR SWITCH	
	INTERNAL RELAY FAULT (IRF)		AVAILABLE OUTPUT		REMOTE	
B	
C	
D	
E	
F	<table border="1"> <tr> <td></td><td></td><td>Date Prep.</td><td>26.03.2020</td><td colspan="2">PROJECT TITLE</td><td rowspan="2">ABB EPMV</td><td rowspan="2">SPARE CONTACT BIODIESEL PLANT SCHEMATIC DIAGRAM SBC-W INCOMING 2</td><td>Scale</td><td>NTS</td><td>= H02</td></tr> <tr> <td>00</td><td>Issued for Approval</td><td>26.03.20</td><td>YR</td><td>Prepared</td><td>YR</td><td colspan="2">Customer</td><td>PT Multimas Nabati Asahan</td><td>& 302</td></tr> <tr> <td>Ind.</td><td>Revision</td><td>Date</td><td>Name</td><td>Approved</td><td>AI</td><td>Based on:</td><td>BE320003</td><td>Drawing Nbr.</td><td>20.003-MNA-302</td><td>Sh. 13</td></tr> <tr> <td colspan="7"></td><td>PT. ABB Sakti Industri</td><td>Customer Doc. Nbr.</td><td></td><td>Cont. 29</td></tr> </table>										Date Prep.	26.03.2020	PROJECT TITLE		ABB EPMV	SPARE CONTACT BIODIESEL PLANT SCHEMATIC DIAGRAM SBC-W INCOMING 2	Scale	NTS	= H02	00	Issued for Approval	26.03.20	YR	Prepared	YR	Customer		PT Multimas Nabati Asahan	& 302	Ind.	Revision	Date	Name	Approved	AI	Based on:	BE320003	Drawing Nbr.	20.003-MNA-302	Sh. 13								PT. ABB Sakti Industri	Customer Doc. Nbr.		Cont. 29
		Date Prep.	26.03.2020	PROJECT TITLE		ABB EPMV	SPARE CONTACT BIODIESEL PLANT SCHEMATIC DIAGRAM SBC-W INCOMING 2	Scale	NTS	= H02	
00	Issued for Approval	26.03.20	YR	Prepared	YR			Customer		PT Multimas Nabati Asahan	& 302	
Ind.	Revision	Date	Name	Approved	AI	Based on:	BE320003	Drawing Nbr.	20.003-MNA-302	Sh. 13	
							PT. ABB Sakti Industri	Customer Doc. Nbr.		Cont. 29	
	1	2	3	4	5	6	7	8	


			Date Prep.	26.03.2020	PROJECT TITLE BIODIESEL AND FLEXTech PLANT	ABB	EPMV	CURRENT TRANSFORMER BIODIESEL PLANT SCHEMATIC DIAGRAM SBC-W INCOMING 2	Scale	NTS	= H02	
			Prepared	YR					Customer	PT Multimas Nabati Asahan	& 302	
00	Issued for Approval	26.03.20	YR	Checked		AW	PT. ABB Sakti Industri		Drawing Nbr.	20.003-MNA-302	Sh.	14
Ind.	Revision	Date	Name	Approved	AI	Based on: BE320003			Customer Doc. Nbr.		Cont.	29

			Date Prep.	26.03.2020	PROJECT TITLE BIODIESEL AND FLEXTech PLANT	ABB	EPMV	VOLTAGE TRANSFORMER BIODIESEL PLANT SCHEMATIC DIAGRAM SBC-W INCOMING 2	Scale	NTS	= H02	
			Prepared	YR					Customer	PT Multimas Nabati Asahan	& 302	
00	Issued for Approval	26.03.20	YR	Checked		AW	PT. ABB Sakti Industri		Drawing Nbr.	20.003-MNA-302	Sh.	15
Ind.	Revision	Date	Name	Approved	AI	Based on: BE320003			Customer Doc. Nbr.		Cont.	29

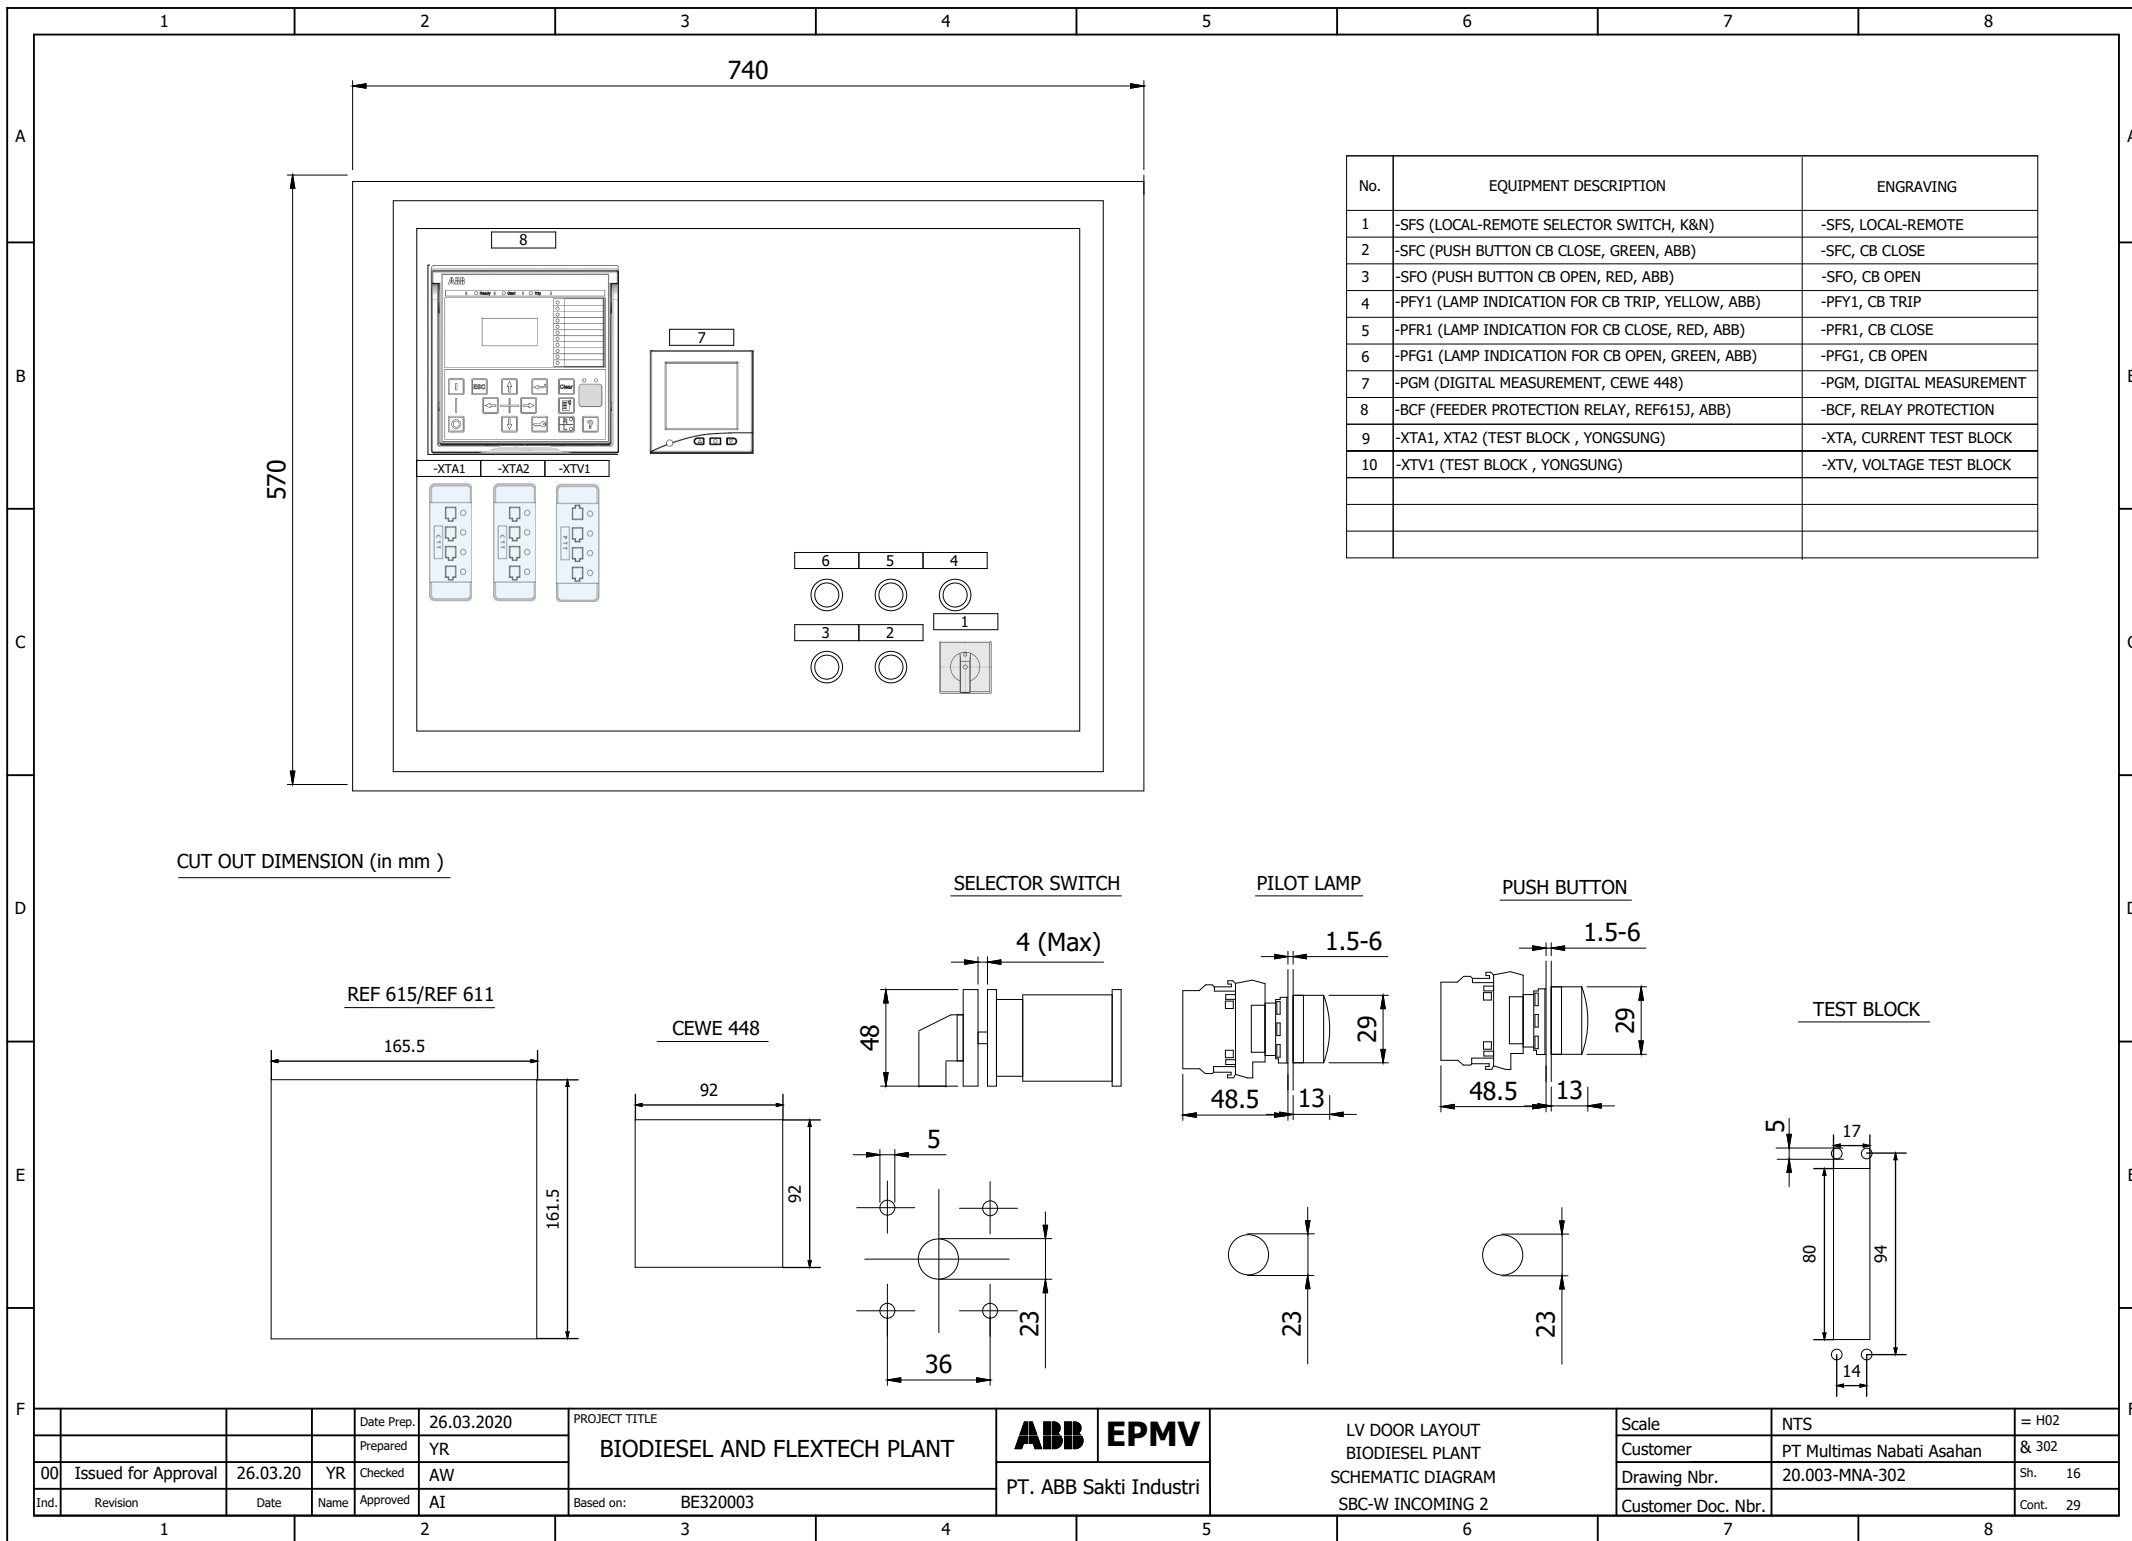

No.	EQUIPMENT DESCRIPTION	ENGRAVING
1	-SFS (LOCAL-REMOTE SELECTOR SWITCH, K&N)	-SFS, LOCAL-REMOTE
2	-SFC (PUSH BUTTON CB CLOSE, GREEN, ABB)	-SFC, CB CLOSE
3	-SFO (PUSH BUTTON CB OPEN, RED, ABB)	-SFO, CB OPEN
4	-PFY1 (LAMP INDICATION FOR CB TRIP, YELLOW, ABB)	-PFY1, CB TRIP
5	-PFR1 (LAMP INDICATION FOR CB CLOSE, RED, ABB)	-PFR1, CB CLOSE
6	-PFG1 (LAMP INDICATION FOR CB OPEN, GREEN, ABB)	-PFG1, CB OPEN
7	-PGM (DIGITAL MEASUREMENT, CEWE 448)	-PGM, DIGITAL MEASUREMENT
8	-BCF (FEEDER PROTECTION RELAY, REF615J, ABB)	-BCF, RELAY PROTECTION
9	-XTA1, XTA2 (TEST BLOCK, YONGSUNG)	-XTA, CURRENT TEST BLOCK
10	-XTV1 (TEST BLOCK, YONGSUNG)	-XTV, VOLTAGE TEST BLOCK


CUT OUT DIMENSION (in mm)

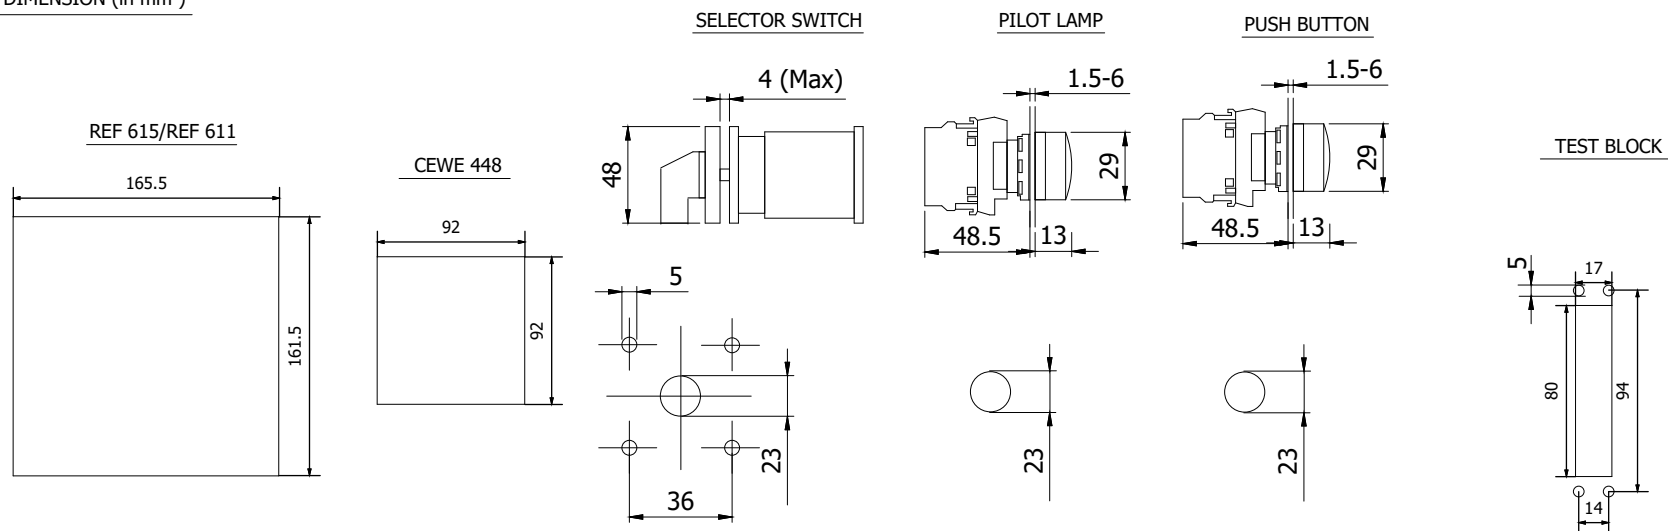

			Date Prep.	26.03.2020	PROJECT TITLE BIODIESEL AND FLEXTECH PLANT	ABB	EPMV	LV DOOR LAYOUT BIODIESEL PLANT SCHEMATIC DIAGRAM SBC-W INCOMING 2	Scale	NTS	= H02	
			Prepared	YR					Customer	PT Multimas Nabati Asahan	& 302	
00	Issued for Approval	26.03.20	YR	Checked		AW	Drawing Nbr.		20.003-MNA-302	Sh.	16	
Ind.	Revision	Date	Name	Approved	AI	Based on:	BE320003		Customer Doc. Nbr.		Cont.	29
						PT. ABB Sakti Industri						

ABB EPMV
PT. ABB Sakti Industri

LV DOOR LAYOUT
BIODIESEL PLANT
SCHEMATIC DIAGRAM
SBC-W INCOMING 2

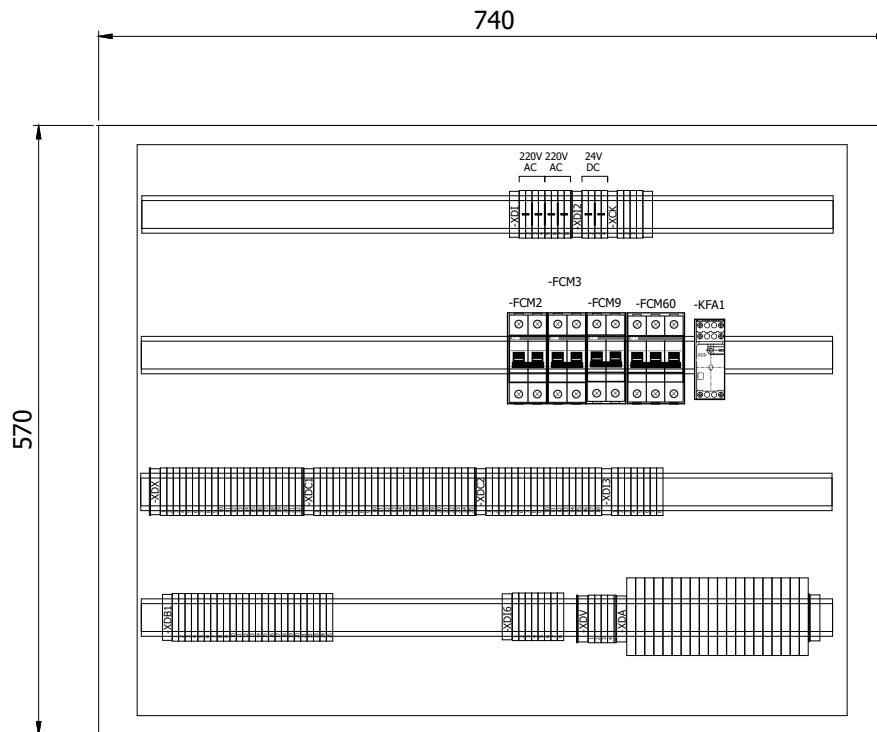[illegible]

			Date Prep.	26.03.2020	PROJECT TITLE BIODIESEL AND FLEXTech PLANT	ABB	EPMV	LV BOX LAYOUT BIODIESEL PLANT SCHEMATIC DIAGRAM SBC-W INCOMING 2	Scale	NTS	= H02	
			Prepared	YR					Customer	PT Multimas Nabati Asahan	& 302	
00	Issued for Approval	26.03.20	YR	Checked		AW	Drawing Nbr.		20.003-MNA-302	Sh.	17	
Ind.	Revision	Date	Name	Approved	AI	Based on:	BE320003		Customer Doc. Nbr.		Cont.	29
						PT. ABB Sakti Industri						

WE RESERVE ALL RIGHTS IN THIS DOCUMENT AND IN THE INFORMATION CONTAINED THEREIN. REPRODUCTION, USE OR DISCLOSURE TO THIRD PARTIES WITHOUT EXPRESS AUTHORITY IS STRICTLY FORBIDDEN.

1		2		3		4		5		6		7		8							
Summarized parts list																					
IDABB_F02_005-IDABB																					
Carry over: 0.00																					
A	TAG ID				DESCRIPTION				MANUFACTUR/BRAND		PART NUMBER		QUANTITY	REMARKS							
	-BCF				Feeder Management Relay HBFJAEAGABC1ANA11G				ABB		REF615J HBFJAEAGABC1ANA11G		2	/8.2:C;/15.7:B							
B	-EB				HEATER 230VAC, 50W				SANYANG		CDXN010033P0009		1	/7.6:E							
	-FCM2				MCB S202-C10 MCB. 2P, 10A				ABB		2CDS252001R0104		1	/7.2:C							
	-FCM3;-FCM9				MCB S202-C6 MCB. 2P, 6A				ABB		2CDS252001R0064		2	/7.5:C;/7.6:C							
	-FCM60				MCB S203-C6 MCB. 3P, 6A				ABB		2CDS253001R0064		1	/15.4:A							
	-FCM61;-FCM62				MCB S202-C2 MCB. 2P, 2A				ABB		2CDS252001R0024		2	/15.5:D;/15.7:E							
C	-KFA1				Auxiliary Relay 230AC 4COS				PHOENIX		1YRA3DL266230001		1	/9.7:E							
	-PFG1				PILOT LIGHT GREEN #CL-523G#230VAC CL-523G				ABB		1SFA619402R5232		1	/8.5:E							
	-PFR1				PILOT LIGHT RED #CL-523R#230VAC CL-523R				ABB		1SFA619402R5231		1	/8.4:E							
	-PFY1				PILOT LIGHT YELLOW #CL-523Y#230VAC CL-523Y				ABB		1SFA619402R5233		1	/8.6:E							
	-PGM1				POWER METER CEWE 448 Class : 0.5s; CT Input : 1A; VT Input : 57.7-240V (L-N); Aux. Voltage: 80-300VAC/DC				CEWE		1YRA4EA0350001		1	/8.3:C							
D	-SFC				PUSH BUTTON, CP1-10G-11,1NC+1NO GREEN COLOUR				ABB		1SFA619100R1072		1	/9.2:B							
	-SFO				PUSH BUTTON, CP1-10R-11,1NC+1NO RED COLOUR				ABB		1SFA619100R1071		1	/9.4:B							
	-SFS				LOCAL/REMOTE Selector Switch Type : S0-CA10-A721-600-FT2; Contact : 2NC & 2NO; Mounting Type : FT2				K&N		1YRA3DA17900201		1	/9.2:B							
	-XTA1;-XTA2				Current Test Block Rated Current : 10A, 250V; Mounting : Flush Mounting				YONGSUNG		YSCTT-04C		2	/14.4:B;/14.4:D							
	-XTV1				Voltage Test Block Rated Current : 10A, 250V; Mounting : Flush Mounting				YONGSUNG		YSPTT-04C		1	/15.5:A							
E																					
F																					
				Date Prep.		26.03.2020		PROJECT TITLE				Scale		NTS		= H02					
				Prepared		YR		BIODIESEL AND FLEXTECH PLANT				Customer		PT Multimas Nabati Asahan		& 302					
00		Issued for Approval		26.03.20		YR		Checked		AW		Drawing Nbr.				20.003-MNA-302		Sh. 18			
Ind.		Revision		Date		Name		Approved		AI		Based on:				BE320003		Customer Doc. Nbr.		Cont. 29	
1		2		3		4		5		6		7		8							

BIODIESEL AND FLEXTECH PLANT



PT. ABB Sakti Industri

PART LIST
BIODIESEL PLANT
SCHEMATIC DIAGRAM
SBC-W INCOMING 2

Scale	NTS	= H02
Customer	PT Multimas Nabati Asahan	& 302
Drawing Nbr.	20.003-MNA-302	Sh. 18
Customer Doc. Nbr.		Cont. 29

XCK

REMARK: ☆ INTERPANEL LIGHT BUS OFFERED TOGETHER WITH PANELS.
 ▲ OUTGOING CONTROL CABLE (Supply by Customer).
 ● BRIDGE BAR.
 ✕ PARTITION PLATE.
 (TEST JUMPER.

- ☆ INTERPANEL LIGHT BUS, OFFERED TOGETHER WITH PANELS.
- △ OUTGOING CONTROL CABLE (Supply by Customer).
- BRIDGE BAR.
- ✕ PARTITION PLATE.
- (TEST JUMPER.

XDI2

F		E		D		C		B		A									
REMARK		CABLE		EQUIPMENT		Wire No		Terminal number		TYPE		WIRE NO.		EQUIPMENT		CABLE		REMARK	
BLACK 1.5 mm²				-PREVIOUS_PNL-XDI6:2				1 ●		PT 2.5				-NEXT_PNL-XDI6:1					
BLACK 1.5 mm²				-PREVIOUS_PNL-XDI6:4				2 ●		PT 2.5				-NEXT_PNL-XDI6:2					
				-PREVIOUS_PNL-XDI6:3				3 ●		PT 2.5				-NEXT_PNL-XDI6:3					
				-PREVIOUS_PNL-XDI6:6				4 ●		PT 2.5				-NEXT_PNL-XDI6:4					
				-PREVIOUS_PNL-XDI6:8				5 ●		PT 2.5									
								6 ●		PT 2.5									
								7 ●		PT 2.5									
								8 ●		PT 2.5									

F				E				D				C				B				A																							
REMARK				CABLE				EQUIPMENT				Wire No				Terminal number				TYPE				WIRE NO.				EQUIPMENT				CABLE				REMARK							
BLACK 1,5 mm²				-FCM60:1												1				PT 2,5								-BAT1:a								BLACK 1,5 mm²							
BLACK 1,5 mm²								-FCM60:3								2				PT 2,5								-BAT2:a								BLACK 1,5 mm²							
BLACK 1,5 mm²								-FCM60:5								3				PT 2,5								-BAT3:a								BLACK 1,5 mm²							
BLACK 1,5 mm²								-XTV1:8								● 4				PT 2,5								-BAT1:n								BLACK 1,5 mm²							
Y/G 2,5 mm²								-XE2								● 5				PT 2,5								-BAT2:n								BLACK 1,5 mm²							
BLACK 1,5 mm²								-FCM61:1								● 6				PT 2,5								-BAT3:n								BLACK 1,5 mm²							
BLACK 1,5 mm²								-RAA1:x1								● 7				PT 2,5								-BAT1:da								BLACK 1,5 mm²							
																● 8				PT 2,5								-BAT1:dn								BLACK 1,5 mm²							
																● 9				PT 2,5								-BAT2:da								BLACK 1,5 mm²							
																● 10				PT 2,5								-BAT2:dn								BLACK 1,5 mm²							
																● 11				PT 2,5								-BAT3:da								BLACK 1,5 mm²							
																● 12				PT 2,5								-BAT3:dn								BLACK 1,5 mm²							
BLACK 1,5 mm²								-RAA1:x2								● 13				PT 2,5																BLACK 1,5 mm²							
BLACK 1,5 mm²								-FCM61:3								● 14				PT 2,5																BLACK 1,5 mm²							
Y/G 2,5 mm²								-XE2																																			
BLACK 1,5 mm²								-BCF:X130:9								15				PT 2,5								-FCM62:2															
BLACK 1,5 mm²								-BCF:X130:10								16				PT 2,5								-FCM62:4															

- ☆ INTERPANEL LIGHT BUS, OFFERED TOGETHER WITH PANELS.
- △ OUTGOING CONTROL CABLE (Supply by Customer).
- BRIDGE BAR.
- ✕ PARTITION PLATE.
- (TEST JUMPER.