

WE RESERVE ALL RIGHTS IN THIS DOCUMENT AND IN THE INFORMATION CONTAINED THEREIN. REPRODUCTION, USE OR DISCLOSURE TO THIRD PARTIES WITHOUT EXPRESS AUTHORITY IS STRICTLY FORBIDDEN.

1		2		3		4		5		6		7		8																	
UniSec Medium Voltage Switchgear PT MULTIMAS NABATI ASAHAN BIODIESEL PLANT SCHEMATIC DIAGRAM SBC-W OUTGOING H03,H04,H05																															
				Date Prep.		26.03.2020		PROJECT TITLE						Scale		NTS		= H03,H04,H05													
				Prepared		YR		BIODIESEL AND FLEXTech PLANT				ABB EPMV		Customer		PT Multimas Nabati Asahan		& 303													
00		Issued for Approval		26.03.20		YR		Checked		AW		PT. ABB Sakti Industri				Drawing Nbr.		20.003-MNA-303		Sh. 1											
Ind.		Revision		Date		Name		Approved		AI		Based on: BE320003				Customer Doc. Nbr.				Cont. 28											
1				2				3				4				5				6				7				8			

WE RESERVE ALL RIGHTS IN THIS DOCUMENT AND IN THE INFORMATION CONTAINED THEREIN. REPRODUCTION, USE OR DISCLOSURE TO THIRD PARTIES WITHOUT EXPRESS AUTHORITY IS STRICTLY FORBIDDEN.


SHEET INDEX

PAGE	PAGE NAME	REVISION		
==BIODIESEL_PLANT=H03,H04,H05&303/1	COVER SHEET	00		
==BIODIESEL_PLANT=H03,H04,H05&303/2	Index of Sheet	00		
==BIODIESEL_PLANT=H03,H04,H05&303/3	REFERENCE DESIGNATIONS	00		
==BIODIESEL_PLANT=H03,H04,H05&303/4	REFERENCE DESIGNATIONS	00		
==BIODIESEL_PLANT=H03,H04,H05&303/5	REFERENCE DESIGNATIONS	00		
==BIODIESEL_PLANT=H03,H04,H05&303/6	REFERENCE DESIGNATIONS	00		
==BIODIESEL_PLANT=H03,H04,H05&303/7	DISTRIBUTION OF AUXILIARY CIRCUITS	00		
==BIODIESEL_PLANT=H03,H04,H05&303/8	AUXILIARY SUPPLY CIRCUIT	00		
==BIODIESEL_PLANT=H03,H04,H05&303/9	CIRCUIT BREAKER CONTROL	00		
==BIODIESEL_PLANT=H03,H04,H05&303/10	AUXILIARY MOTOR & RELAY	00		
==BIODIESEL_PLANT=H03,H04,H05&303/11	DIGITAL INPUT/OUTPUT RELAY	00		
==BIODIESEL_PLANT=H03,H04,H05&303/12	SPARE CONTACT	00		
==BIODIESEL_PLANT=H03,H04,H05&303/13	CURRENT TRANSFORMER	00		
==BIODIESEL_PLANT=H03,H04,H05&303/14	VOLTAGE TRANSFORMER	00		
==BIODIESEL_PLANT=H03,H04,H05&303/15	LV DOOR LAYOUT	00		
==BIODIESEL_PLANT=H03,H04,H05&303/16	LV BOX LAYOUT	00		
==BIODIESEL_PLANT=H03,H04,H05&303/17	PART LIST	00		
==BIODIESEL_PLANT=H03,H04,H05&303/18	Terminal diagram ==BIODIESEL_PLANT=H03,H04,H05+-XCK	00		
==BIODIESEL_PLANT=H03,H04,H05&303/19	Terminal diagram ==BIODIESEL_PLANT=H03,H04,H05+-XDA	00		
==BIODIESEL_PLANT=H03,H04,H05&303/20	Terminal diagram ==BIODIESEL_PLANT=H03,H04,H05+-XDB1	00		
==BIODIESEL_PLANT=H03,H04,H05&303/21	Terminal diagram ==BIODIESEL_PLANT=H03,H04,H05+-XDC1	00		
==BIODIESEL_PLANT=H03,H04,H05&303/22	Terminal diagram ==BIODIESEL_PLANT=H03,H04,H05+-XDC2	00		
==BIODIESEL_PLANT=H03,H04,H05&303/23	Terminal diagram ==BIODIESEL_PLANT=H03,H04,H05+-XDI	00		
==BIODIESEL_PLANT=H03,H04,H05&303/24	Terminal diagram ==BIODIESEL_PLANT=H03,H04,H05+-XDI2	00		
==BIODIESEL_PLANT=H03,H04,H05&303/25	Terminal diagram ==BIODIESEL_PLANT=H03,H04,H05+-XDI3	00		
==BIODIESEL_PLANT=H03,H04,H05&303/26	Terminal diagram ==BIODIESEL_PLANT=H03,H04,H05+-XDI6	00		
==BIODIESEL_PLANT=H03,H04,H05&303/27	Terminal diagram ==BIODIESEL_PLANT=H03,H04,H05+-XDV	00		
==BIODIESEL_PLANT=H03,H04,H05&303/28	Terminal diagram ==BIODIESEL_PLANT=H03,H04,H05+-XDX	00		

--	--	--	--	--	--	--	--	--	--	--	--

				Date Prep.	26.03.2020	PROJECT TITLE BIODIESEL AND FLEXTech PLANT		ABB	EPMV	Index of Sheet BIODIESEL PLANT SCHEMATIC DIAGRAM SBC-W OUTGOING	Scale	NTS	= H03,H04,H05
				Prepared	YR						Customer	PT Multimas Nabati Asahan	& 303
00	Issued for Approval	26.03.20	YR	Checked	AW			Drawing Nbr.	20.003-MNA-303		Sh. 2		
nd.	Revision	Date	Name	Approved	AI	Based on: BE320003		PT. ABB Sakti Industri			Customer Doc. Nbr.		Cont. 28


WE RESERVE ALL RIGHTS IN THIS DOCUMENT AND IN THE INFORMATION CONTAINED THEREIN. REPRODUCTION, USE OR DISCLOSURE TO THIRD PARTIES WITHOUT EXPRESS AUTHORITY IS STRICTLY FORBIDDEN.

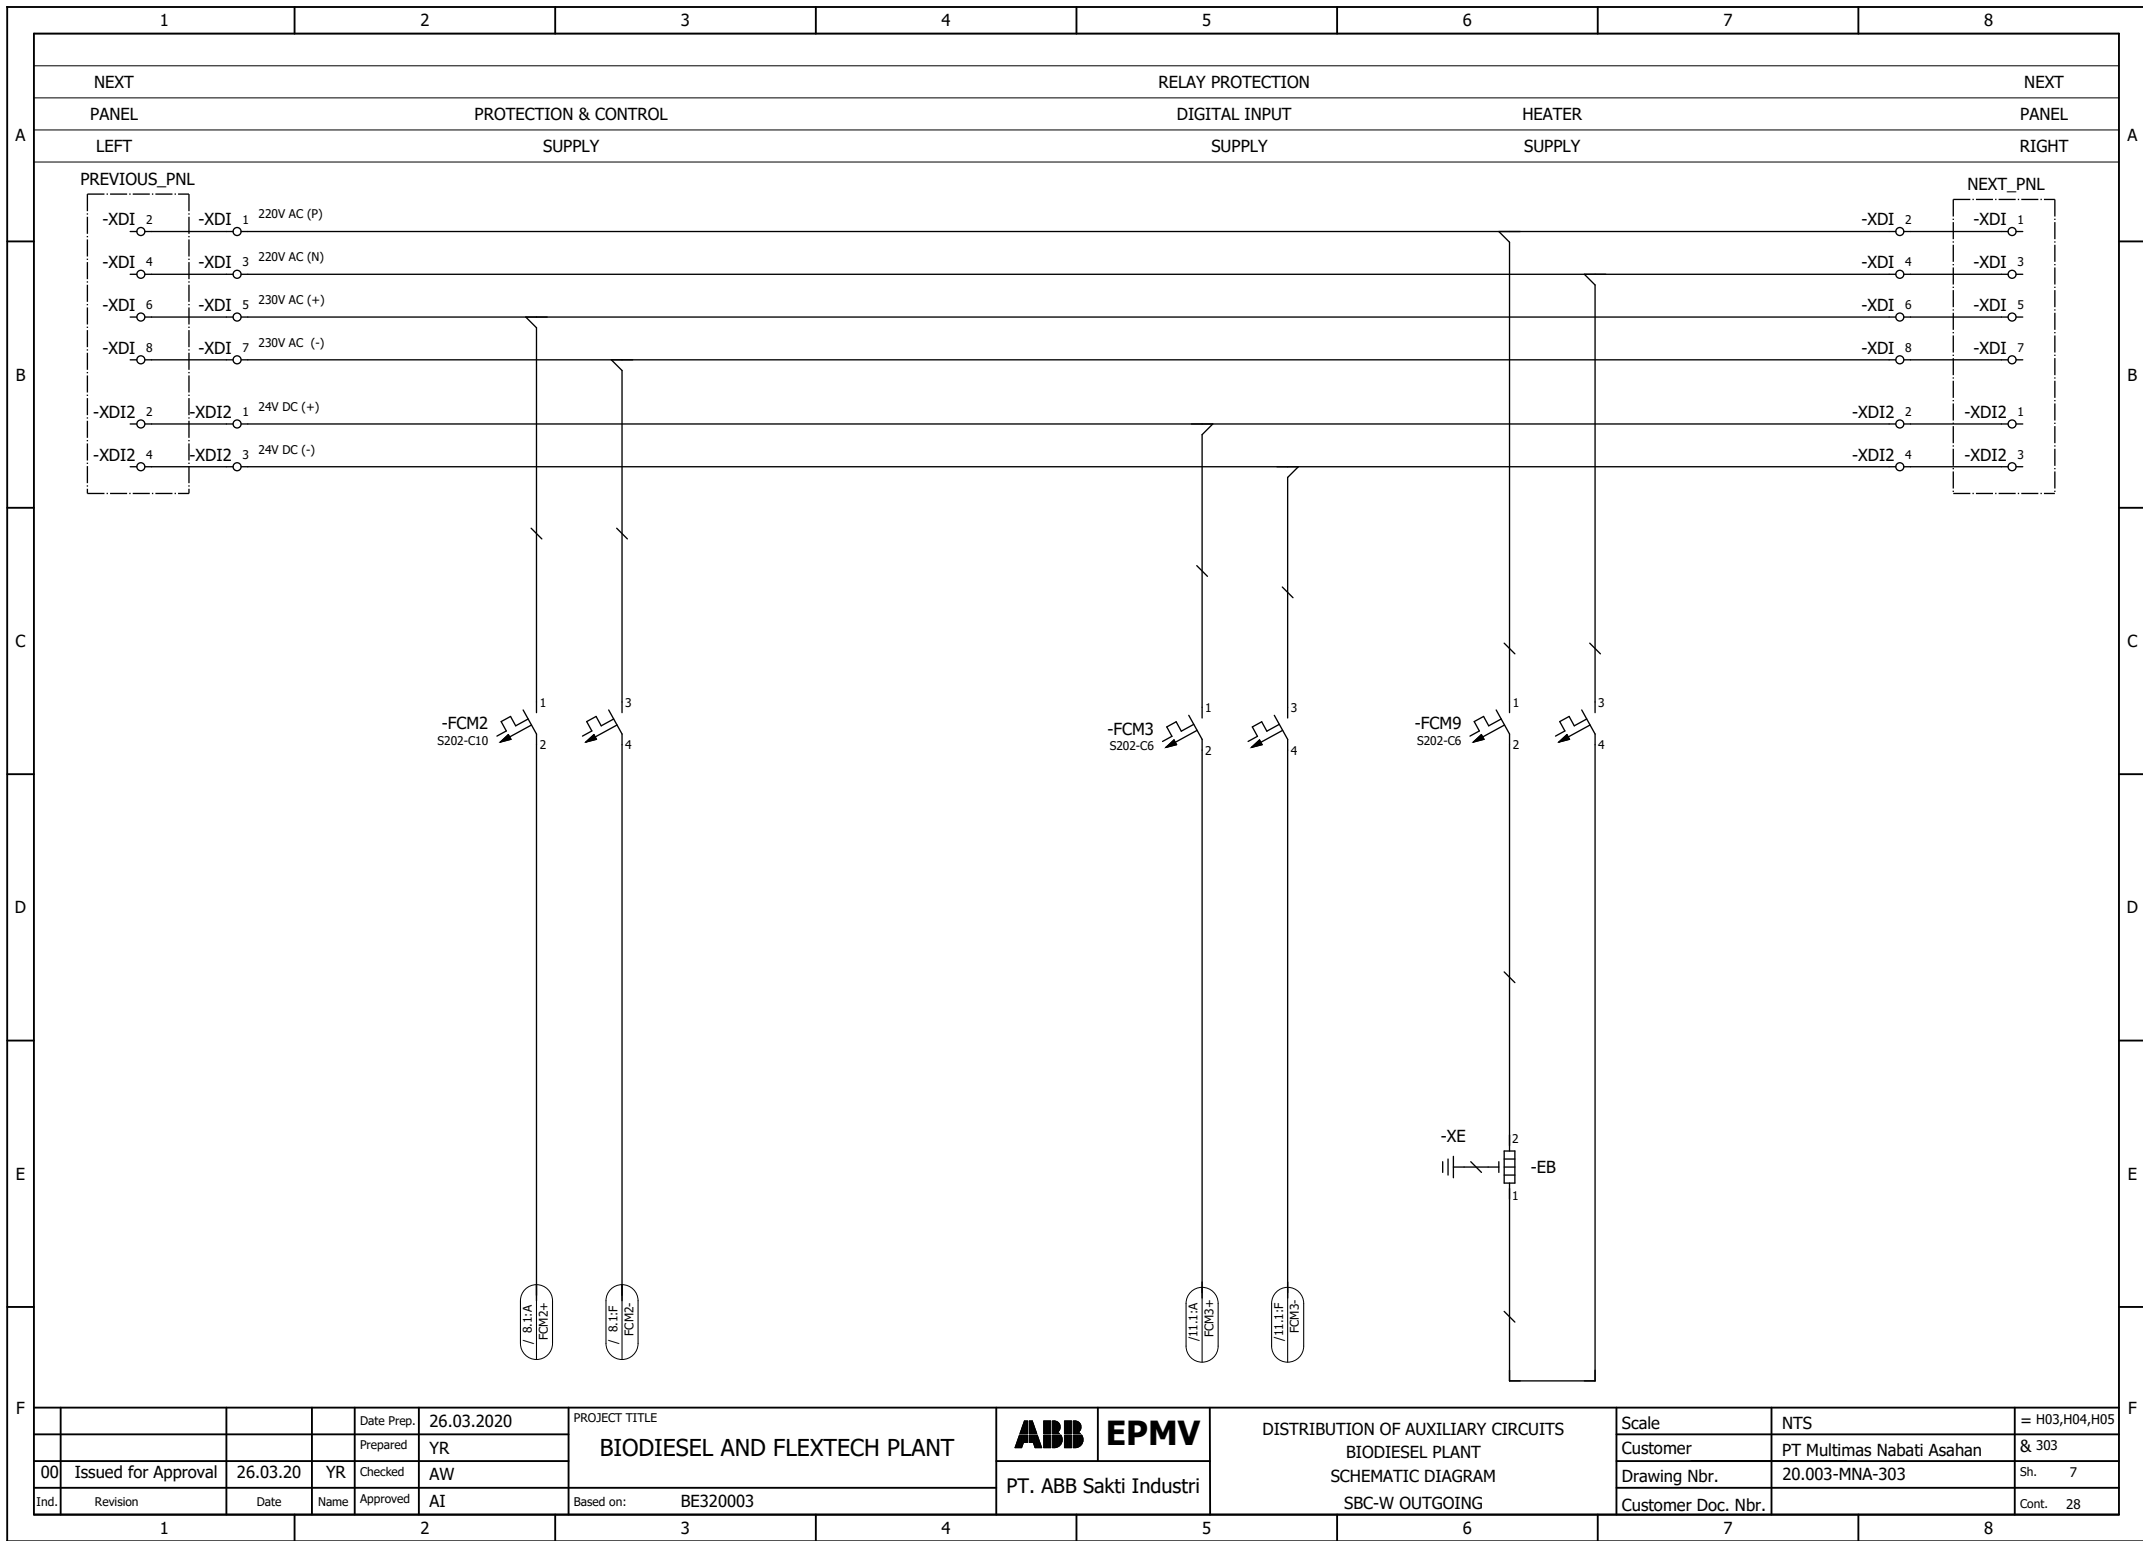


1		2		3		4		5		6		7		8	
CIRCUIT BREAKER		AUX. SUPPLY		INDICATION LAMP		INDICATION FOR REMOTE CONTROL BOX									
MOTOR SPRING CHARGE		PROT. RELAY		DIGITAL METER		CB CLOSED		CB OPEN		CB TRIP		CB CLOSED		CB OPEN	
FCM2+ / 7.2:E		FCM2- / 7.3:E		FCM2+ / 9.1:A		FCM2- / 9.1:F									

			Date Prep.	26.03.2020	PROJECT TITLE BIODIESEL AND FLEXTech PLANT	ABB	EPMV	AUXILIARY SUPPLY CIRCUIT BIODIESEL PLANT SCHEMATIC DIAGRAM SBC-W OUTGOING	Scale	NTS	= H03,H04,H05
			Prepared	YR					Customer	PT Multimas Nabati Asahan	& 303
00	Issued for Approval	26.03.20	YR	Checked		AW	PT. ABB Sakti Industri		Drawing Nbr.	20.003-MNA-303	Sh. 8
Ind.	Revision	Date	Name	Approved		AI			Based on: BE320003	Customer Doc. Nbr.	

WE RESERVE ALL RIGHTS IN THIS DOCUMENT AND IN THE INFORMATION CONTAINED THEREIN. REPRODUCTION, USE OR DISCLOSURE TO THIRD PARTIES WITHOUT EXPRESS AUTHORITY IS STRICTLY FORBIDDEN.

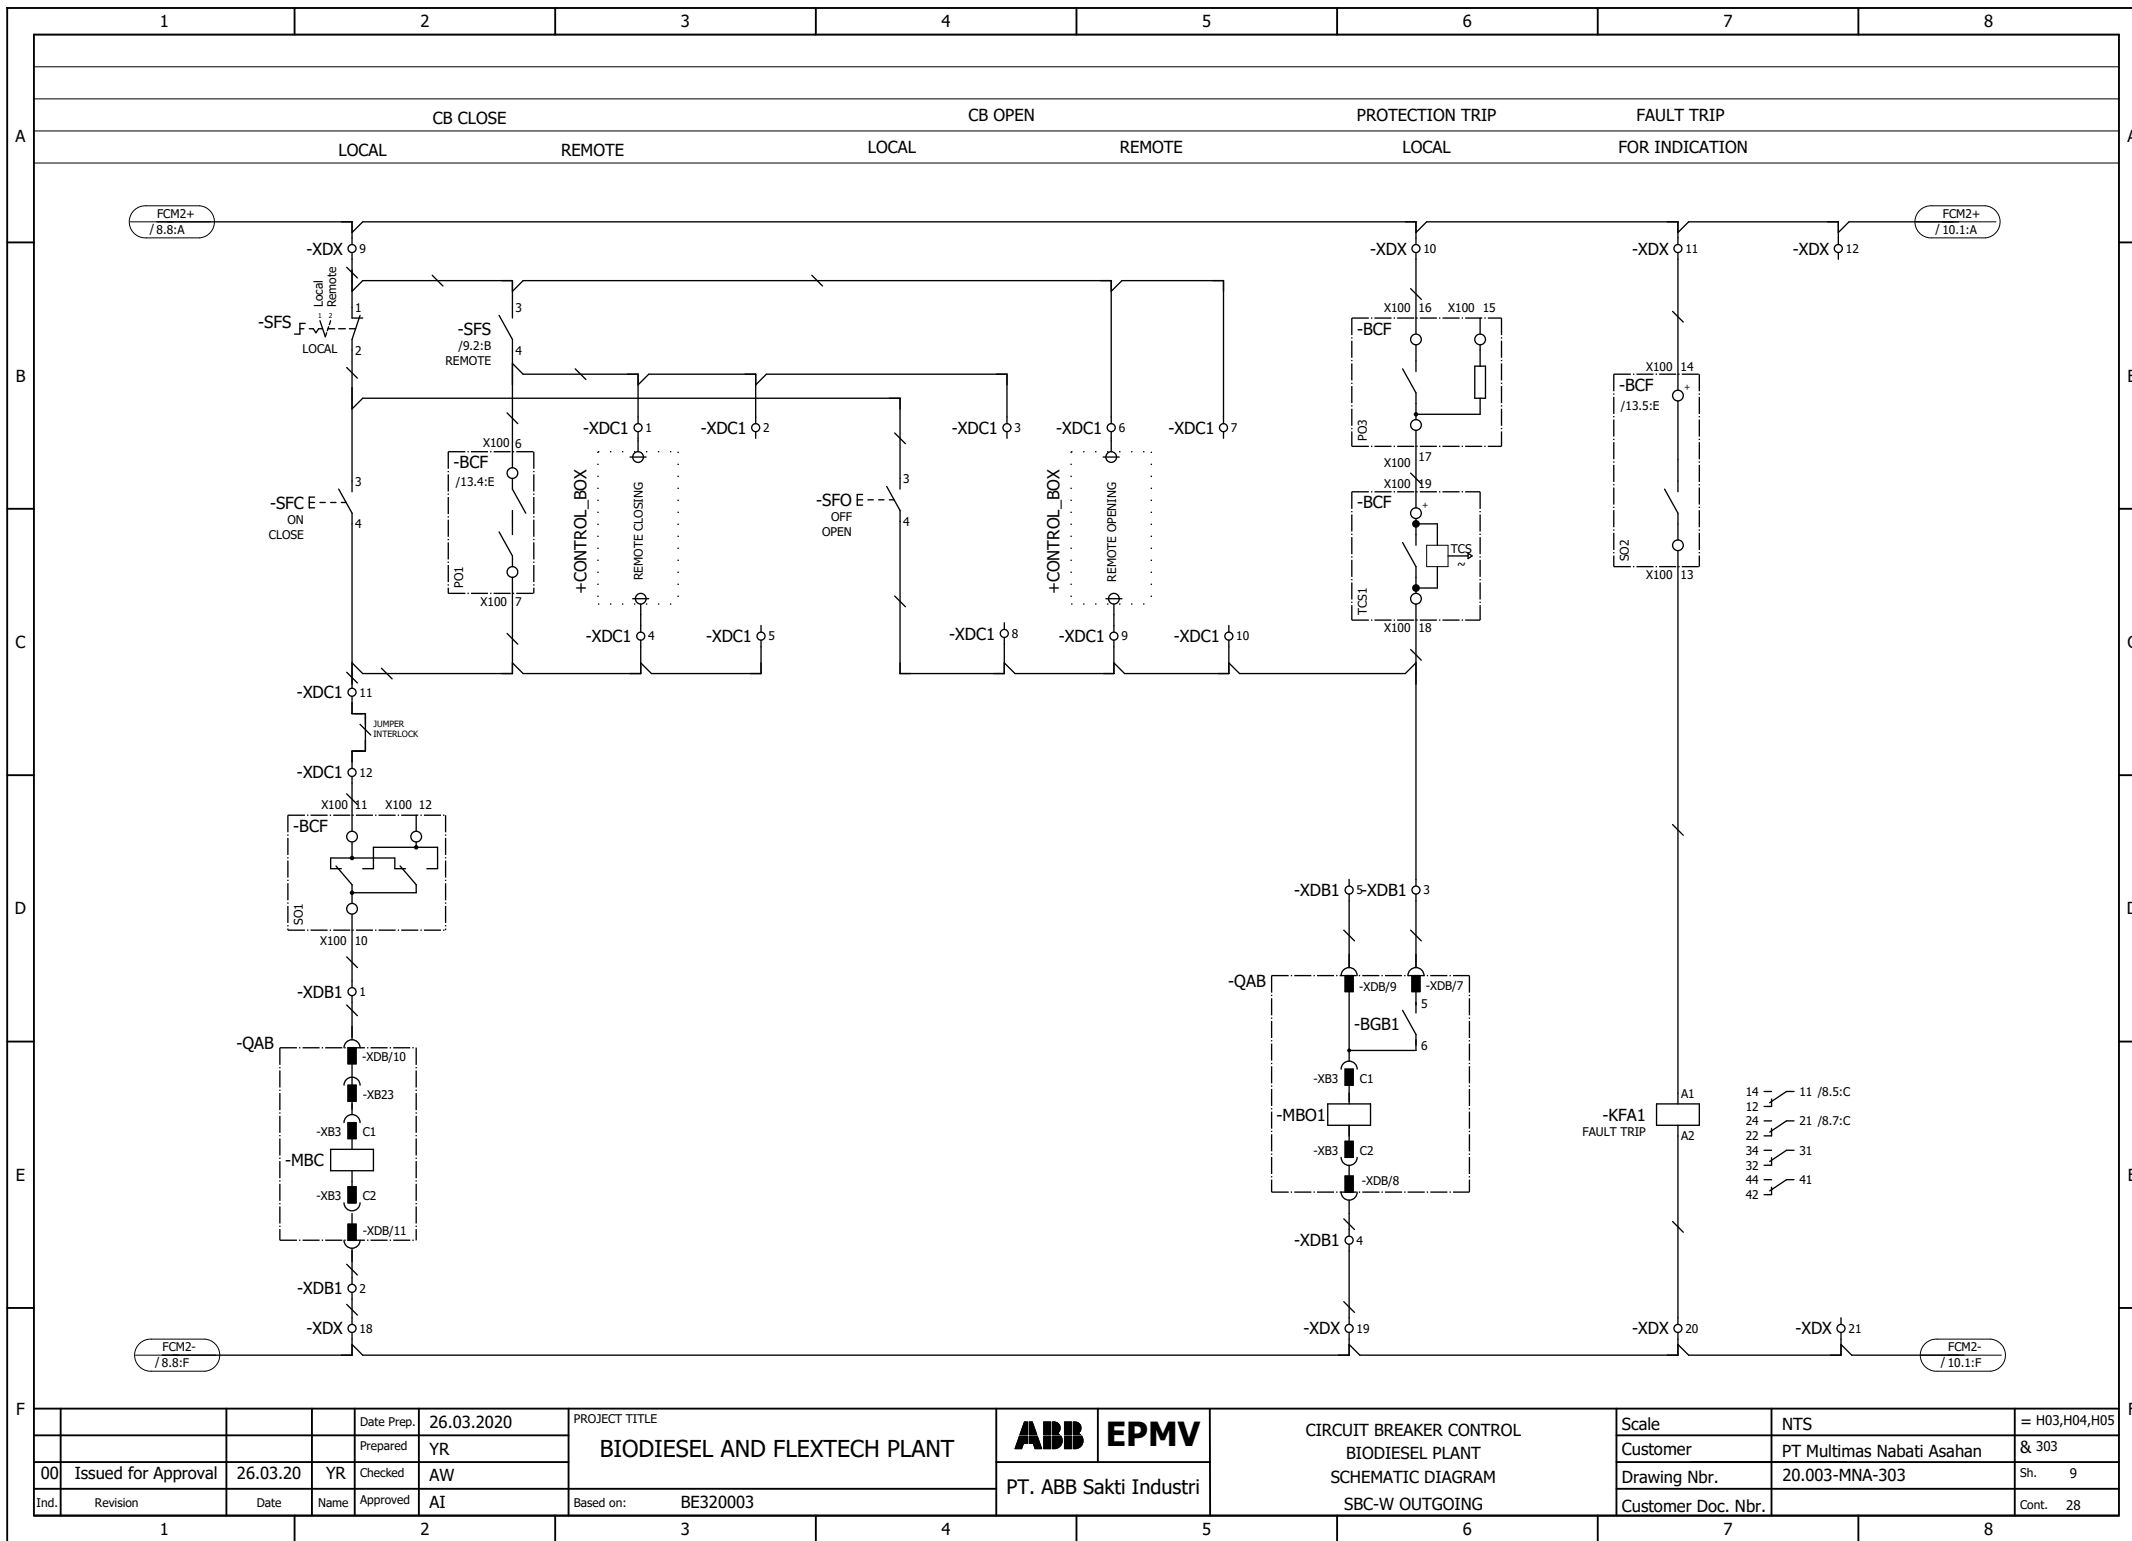

WE RESERVE ALL RIGHTS IN THIS DOCUMENT AND IN THE INFORMATION CONTAINED THEREIN. REPRODUCTION, USE OR DISCLOSURE TO THIRD PARTIES WITHOUT EXPRESS AUTHORITY IS STRICTLY FORBIDDEN.

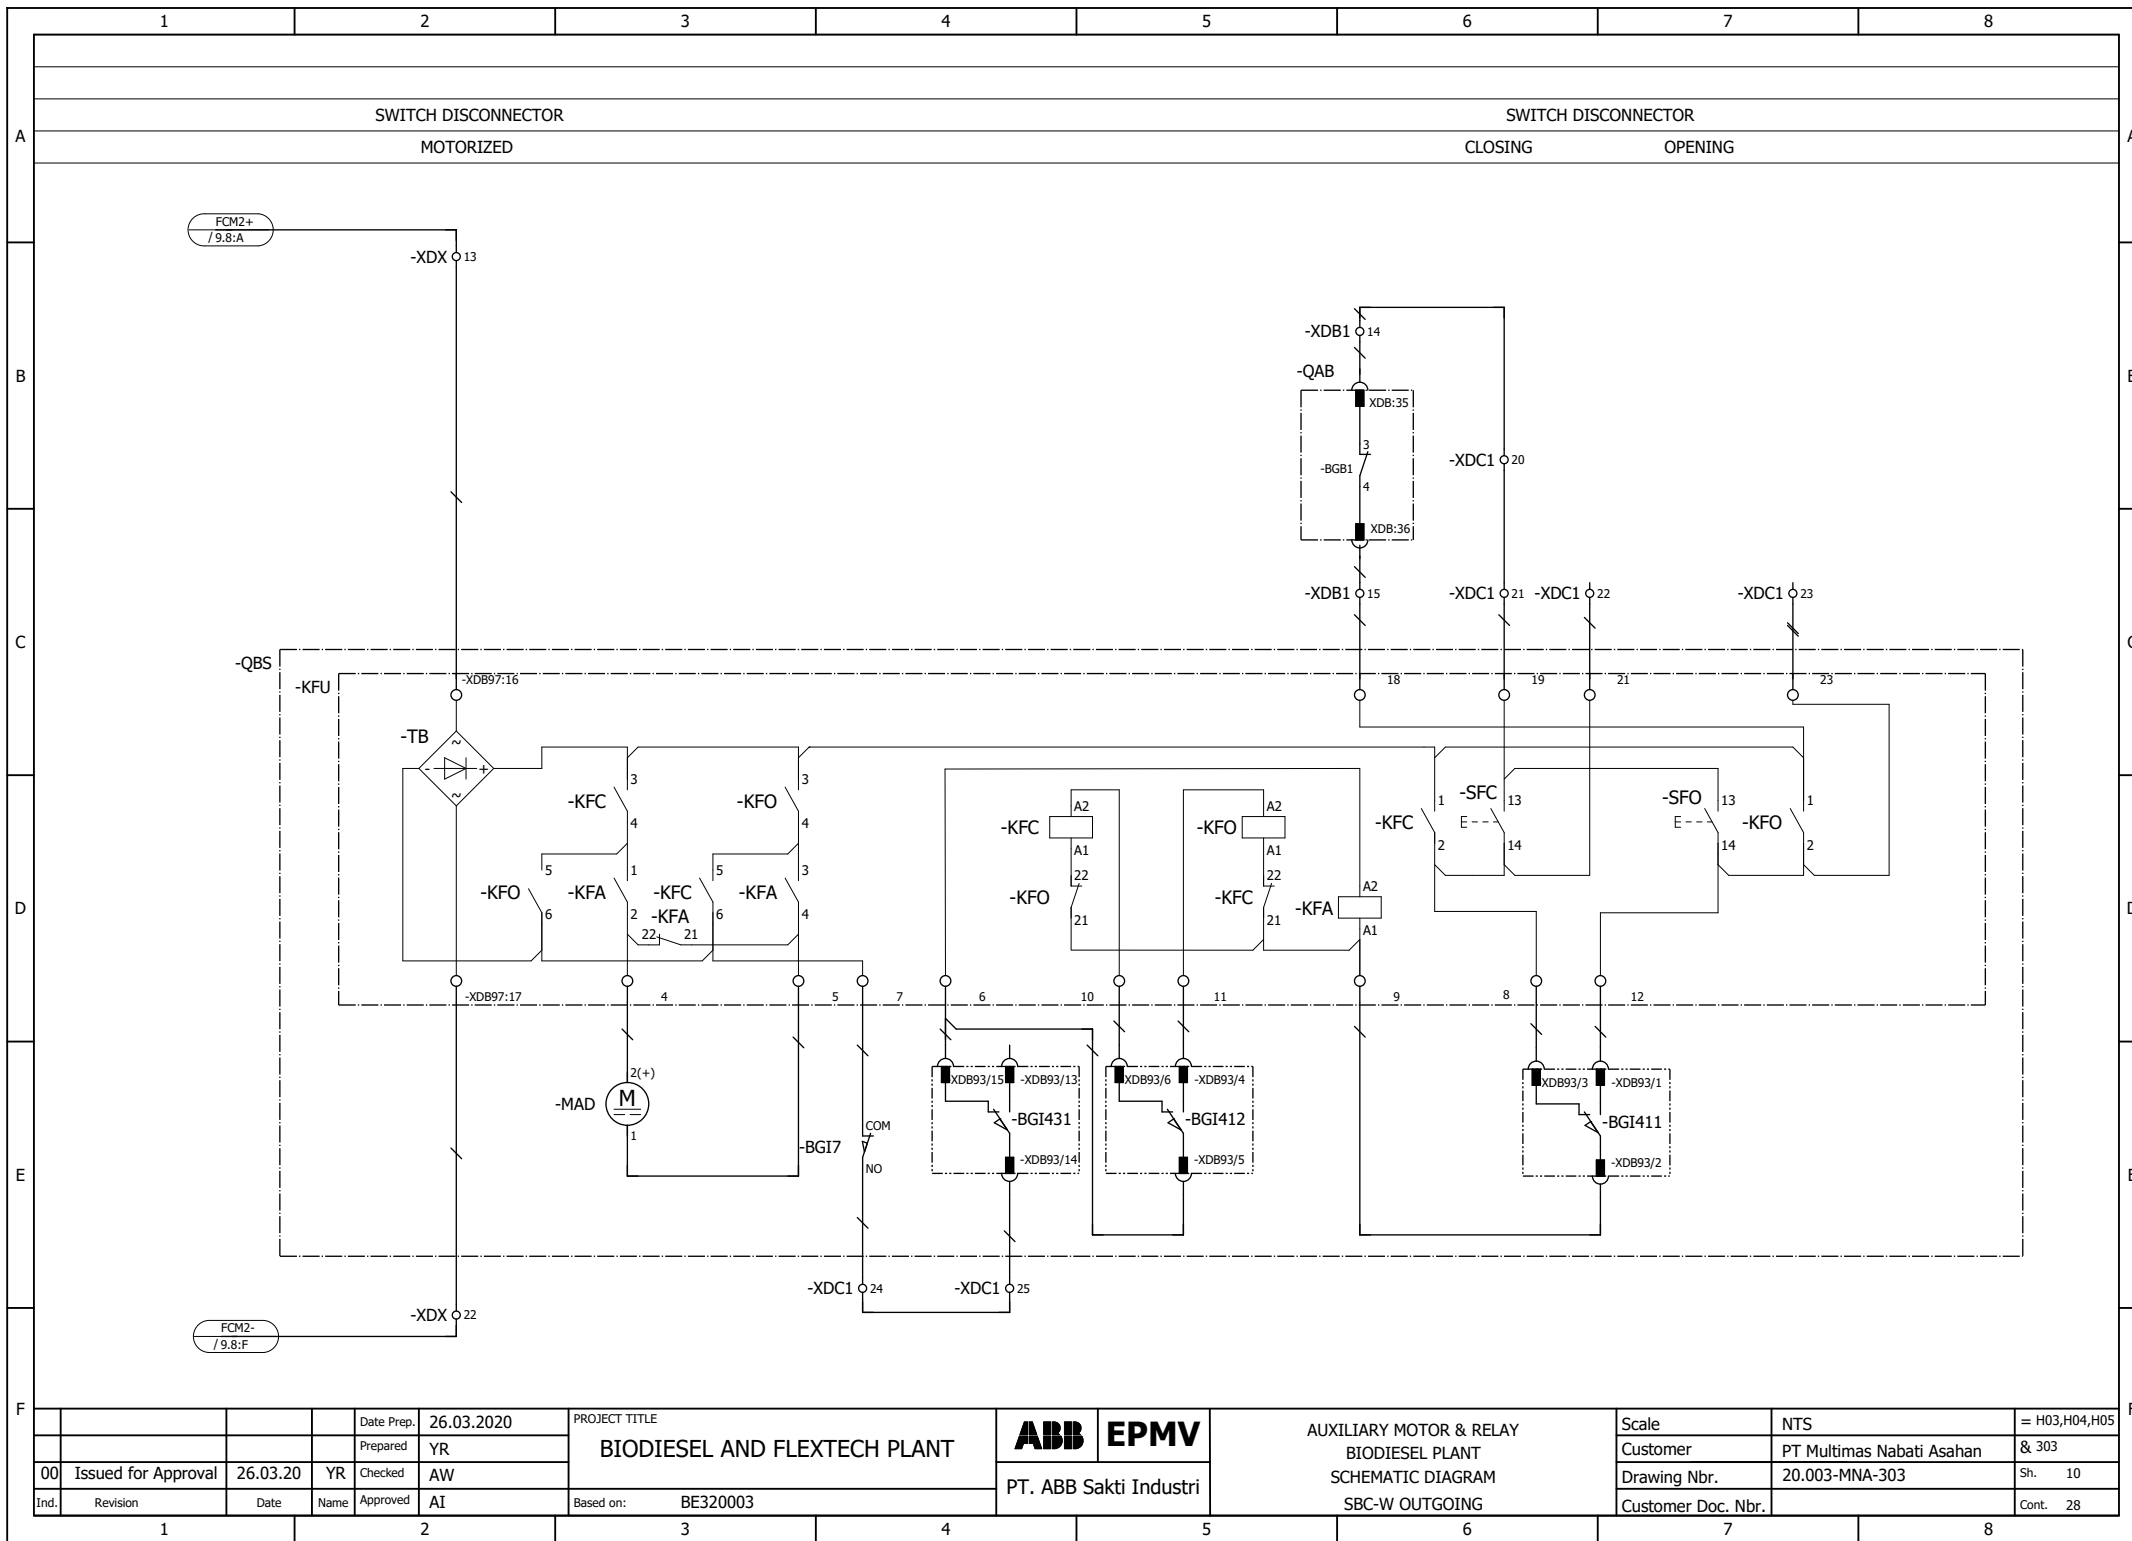


			Date Prep.	26.03.2020
			Prepared	YR
00	Issued for Approval	26.03.20	Checked	AW
Ind.	Revision	Date	Name	Approved
			AI	

PROJECT TITLE	
BIODIESEL AND FLEXTech PLANT	
Based on:	BE320003

ABB	EPMV
PT. ABB Sakti Industri	

AUXILIARY MOTOR & RELAY
BIODIESEL PLANT
SCHEMATIC DIAGRAM
SBC-W OUTGOING

Scale	NTS	= H03,H04,H05
Customer	PT Multimas Nabati Asahan	& 303
Drawing Nbr.	20.003-MNA-303	Sh. 10
Customer Doc. Nbr.		Cont. 28

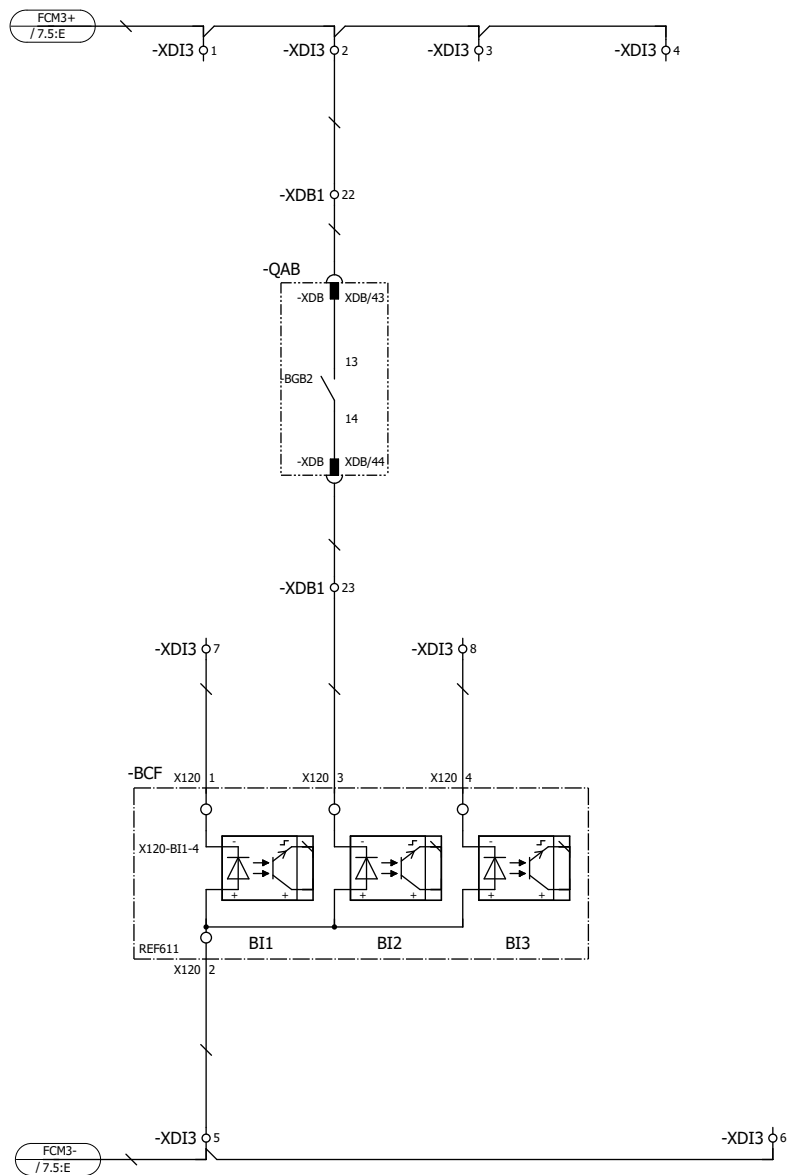


			Date Prep.	26.03.2020	PROJECT TITLE BIODIESEL AND FLEXTech PLANT	ABB	EPMV	DIGITAL INPUT/OUTPUT RELAY BIODIESEL PLANT SCHEMATIC DIAGRAM SBC-W OUTGOING	Scale	NTS	= H03,H04,H05	
			Prepared	YR					Customer	PT Multimas Nabati Asahan	& 303	
00	Issued for Approval	26.03.20	YR	Checked		AW	PT. ABB Sakti Industri		Drawing Nbr.	20.003-MNA-303	Sh.	11
Ind.	Revision	Date	Name	Approved	AI	Based on: BE320003			Customer Doc. Nbr.		Cont.	28

			Date Prep.	26.03.2020	PROJECT TITLE BIODIESEL AND FLEXTech PLANT	ABB	EPMV	SPARE CONTACT BIODIESEL PLANT SCHEMATIC DIAGRAM SBC-W OUTGOING	Scale	NTS	= H03,H04,H05
			Prepared	YR					Customer	PT Multimas Nabati Asahan	& 303
00	Issued for Approval	26.03.20	YR	Checked		AW	PT. ABB Sakti Industri		Drawing Nbr.	20.003-MNA-303	Sh.
Ind.	Revision	Date	Name	Approved	AI	Based on: BE320003			Customer Doc. Nbr.		Cont.

			Date Prep.	26.03.2020	PROJECT TITLE BIODIESEL AND FLEXTech PLANT	ABB	EPMV	CURRENT TRANSFORMER BIODIESEL PLANT SCHEMATIC DIAGRAM SBC-W OUTGOING	Scale	NTS	= H03,H04,H05	
			Prepared	YR					Customer	PT Multimas Nabati Asahan	& 303	
00	Issued for Approval	26.03.20	YR	Checked		AW	PT. ABB Sakti Industri		Drawing Nbr.	20.003-MNA-303	Sh.	13
Ind.	Revision	Date	Name	Approved	AI	Based on: BE320003			Customer Doc. Nbr.		Cont.	28

WE RESERVE ALL RIGHTS IN THIS DOCUMENT AND IN THE INFORMATION CONTAINED THEREIN. REPRODUCTION, USE OR DISCLOSURE TO THIRD PARTIES WITHOUT EXPRESS AUTHORITY IS STRICTLY FORBIDDEN.

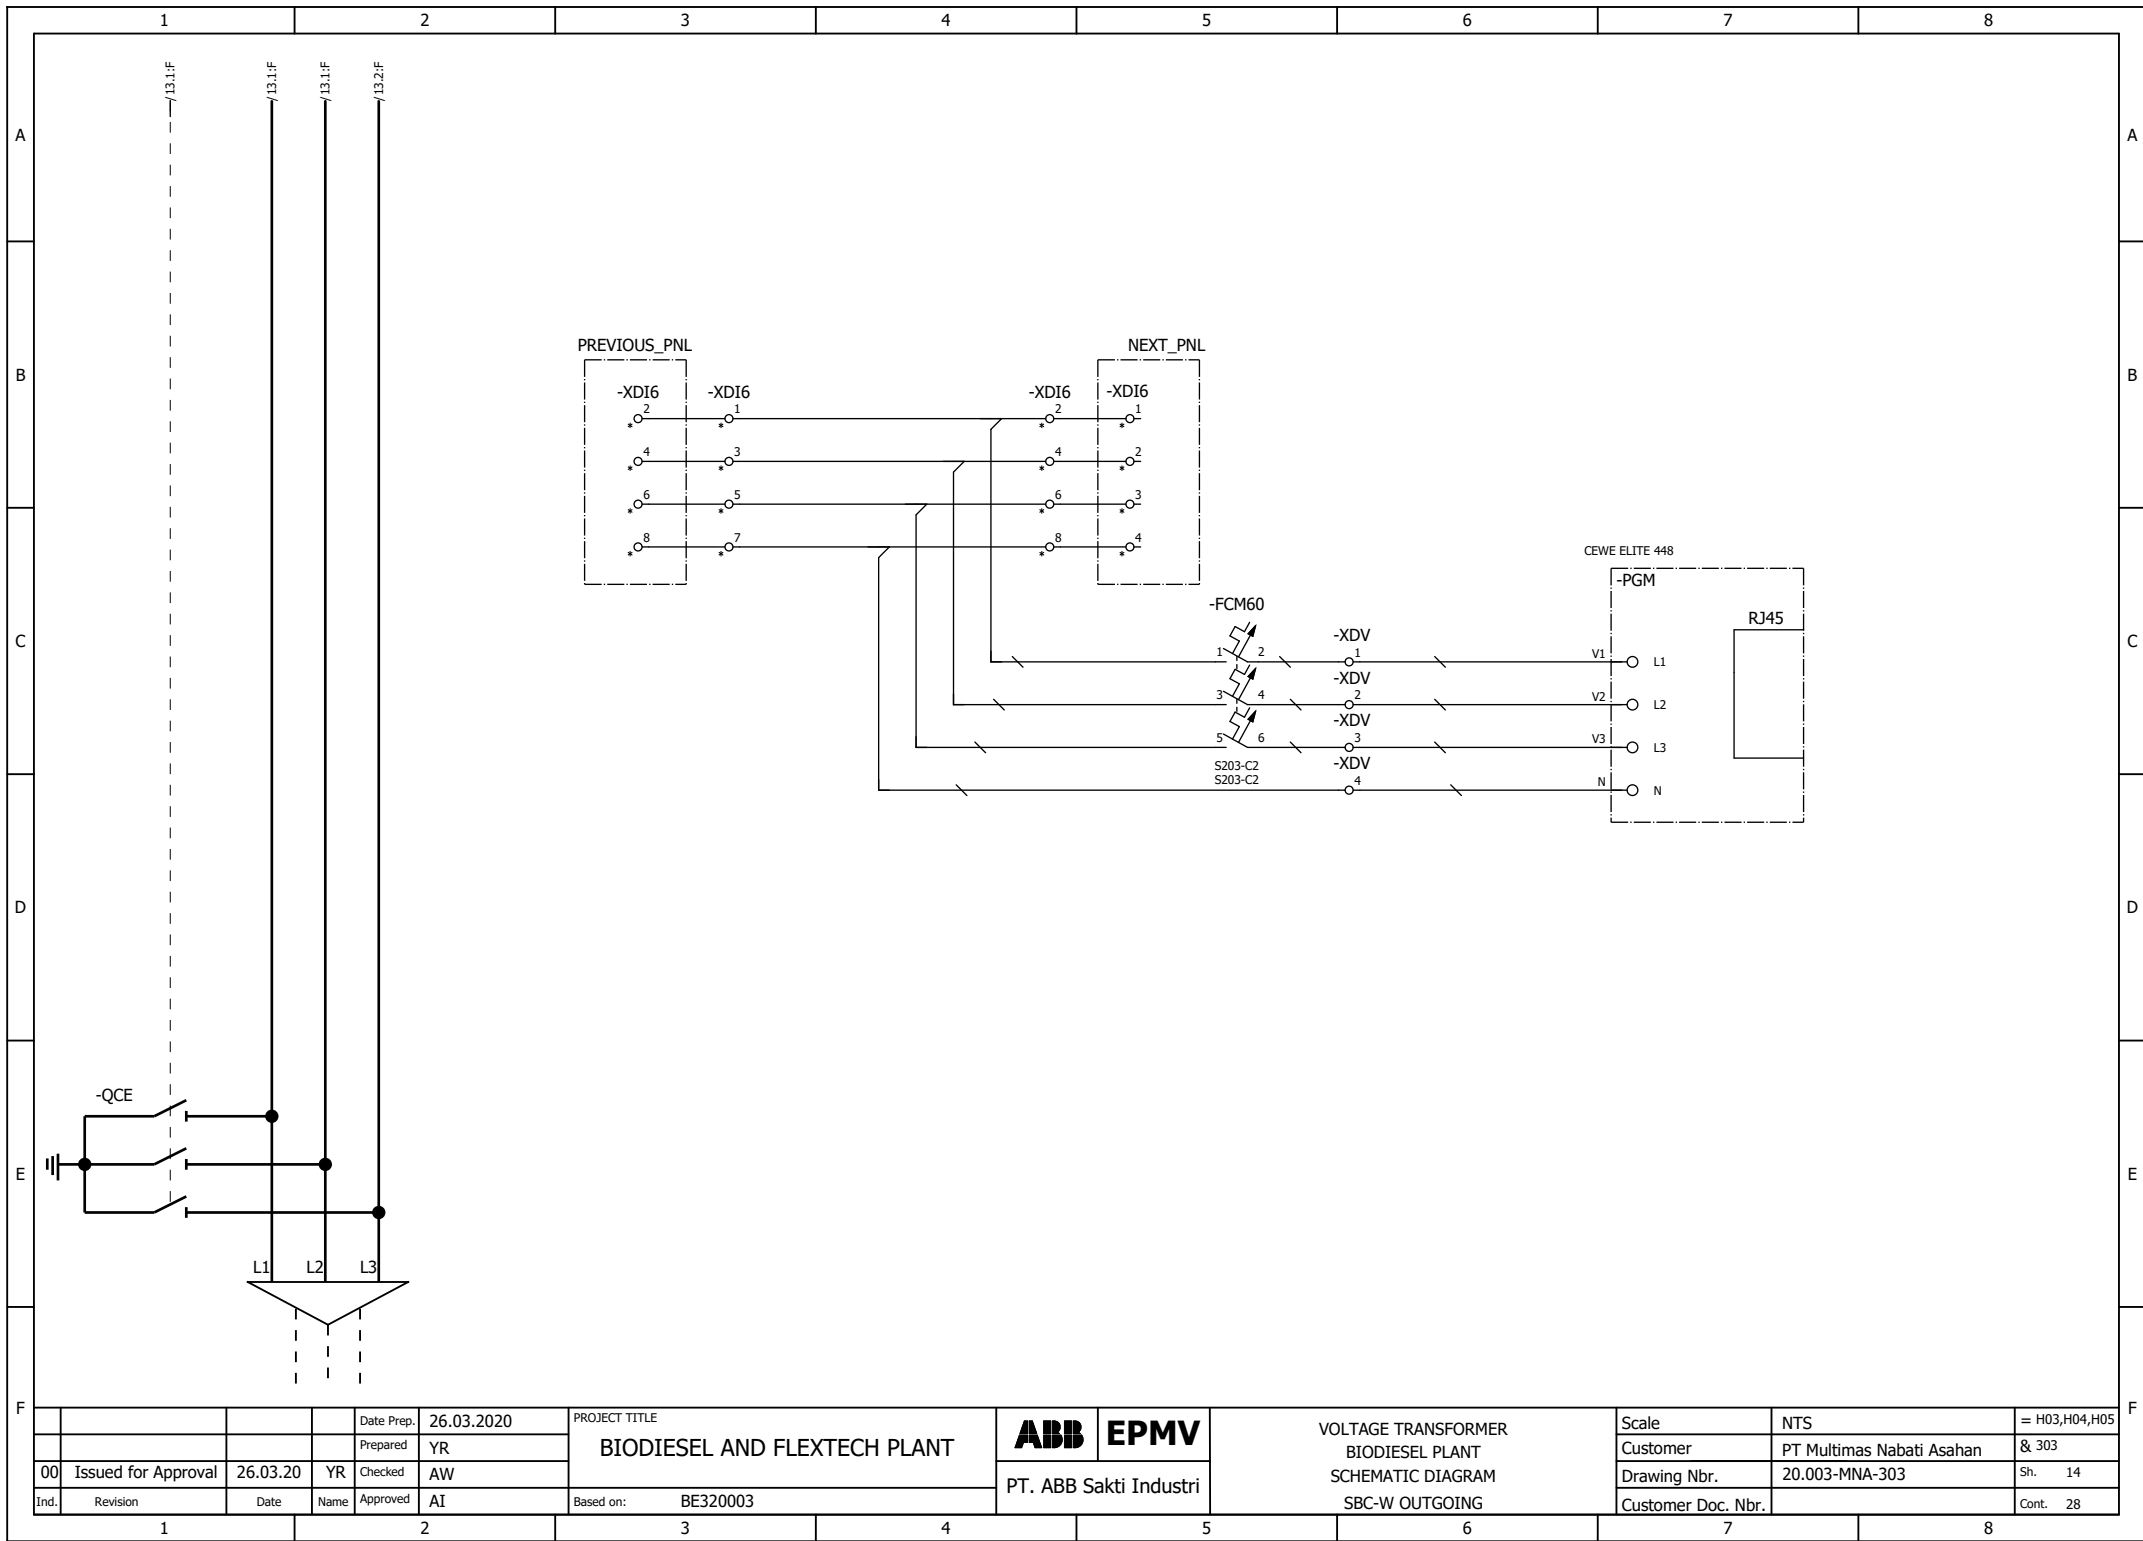


				Date Prep.	26.03.2020
				Prepared	YR
00	Issued for Approval	26.03.20	YR	Checked	AW
Ind.	Revision	Date	Name	Approved	AI

PROJECT TITLE	
BIODIESEL AND FLEXTech PLANT	
Based on:	BE320003

ABB	EPMV
PT. ABB Sakti Industri	


VOLTAGE TRANSFORMER
BIODIESEL PLANT
SCHEMATIC DIAGRAM
SBC-W OUTGOING

Scale	NTS	= H03,H04,H05
Customer	PT Multimas Nabati Asahan	& 303
Drawing Nbr.	20.003-MNA-303	Sh. 14
Customer Doc. Nbr.		Cont. 28

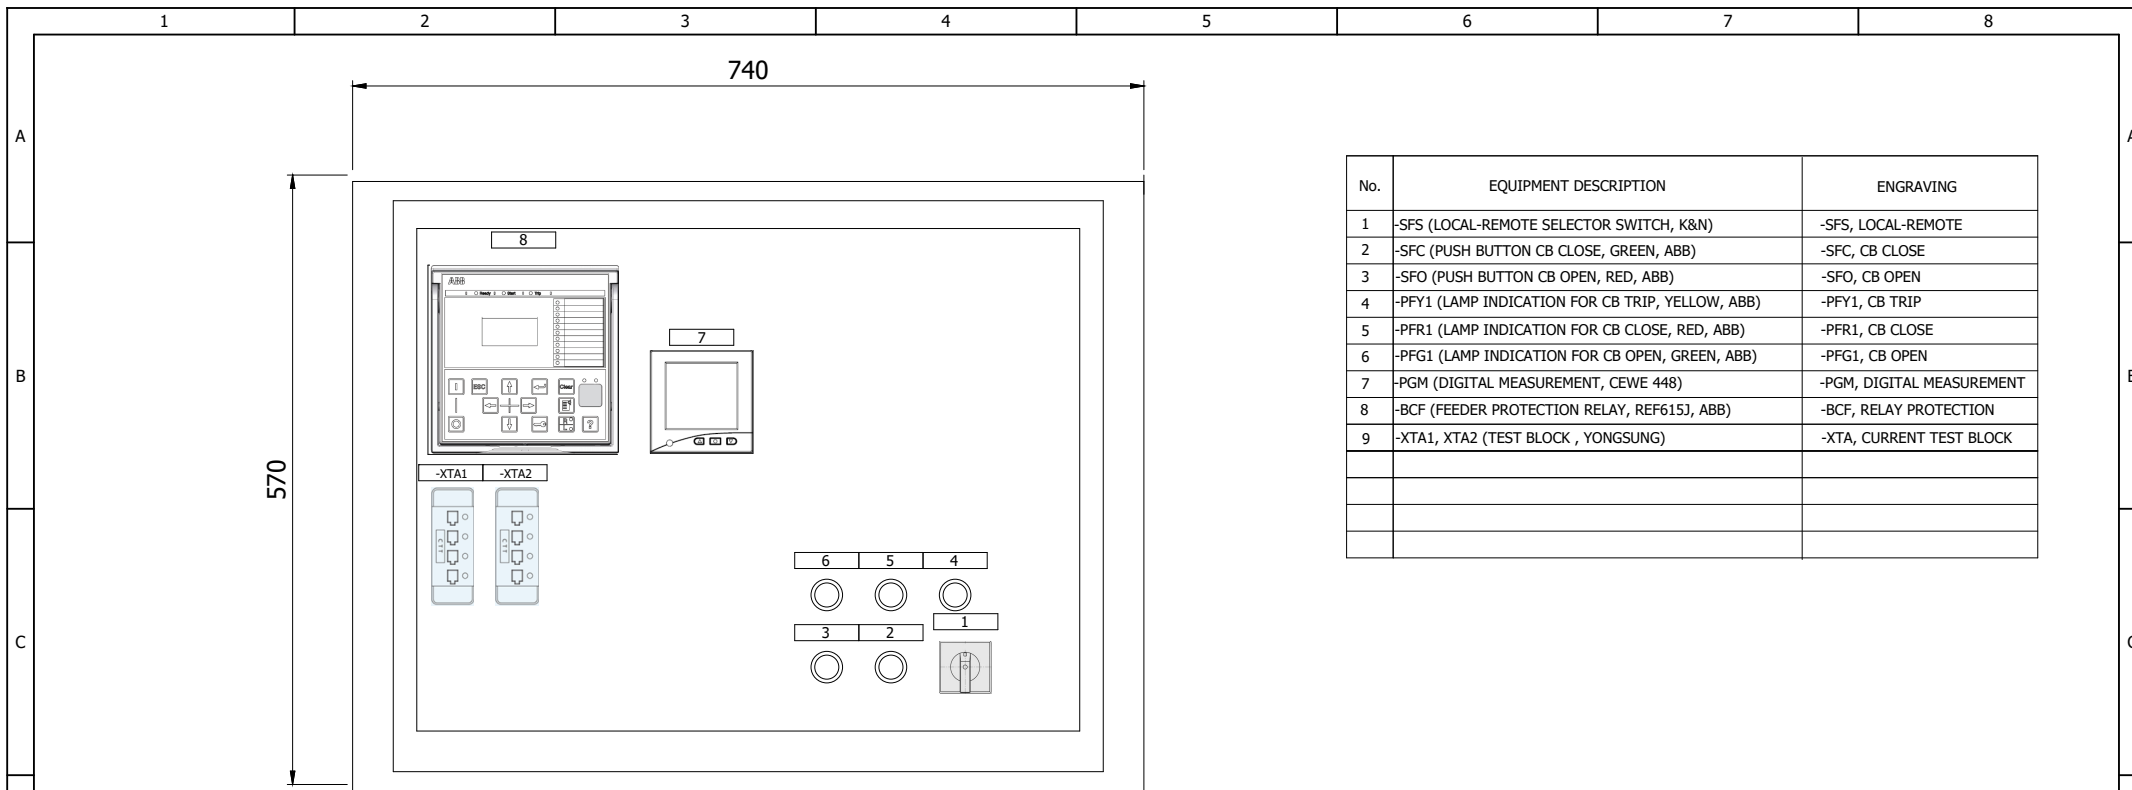


No.	EQUIPMENT DESCRIPTION	ENGRAVING
1	-SFS (LOCAL-REMOTE SELECTOR SWITCH, K&N)	-SFS, LOCAL-REMOTE
2	-SFC (PUSH BUTTON CB CLOSE, GREEN, ABB)	-SFC, CB CLOSE
3	-SFO (PUSH BUTTON CB OPEN, RED, ABB)	-SFO, CB OPEN
4	-PFY1 (LAMP INDICATION FOR CB TRIP, YELLOW, ABB)	-PFY1, CB TRIP
5	-PFR1 (LAMP INDICATION FOR CB CLOSE, RED, ABB)	-PFR1, CB CLOSE
6	-PFG1 (LAMP INDICATION FOR CB OPEN, GREEN, ABB)	-PFG1, CB OPEN
7	-PGM (DIGITAL MEASUREMENT, CEWE 448)	-PGM, DIGITAL MEASUREMENT
8	-BCF (FEEDER PROTECTION RELAY, REF615J, ABB)	-BCF, RELAY PROTECTION
9	-XTA1, XTA2 (TEST BLOCK , YONGSUNG)	-XTA, CURRENT TEST BLOCK

CUT OUT DIMENSION (in mm)

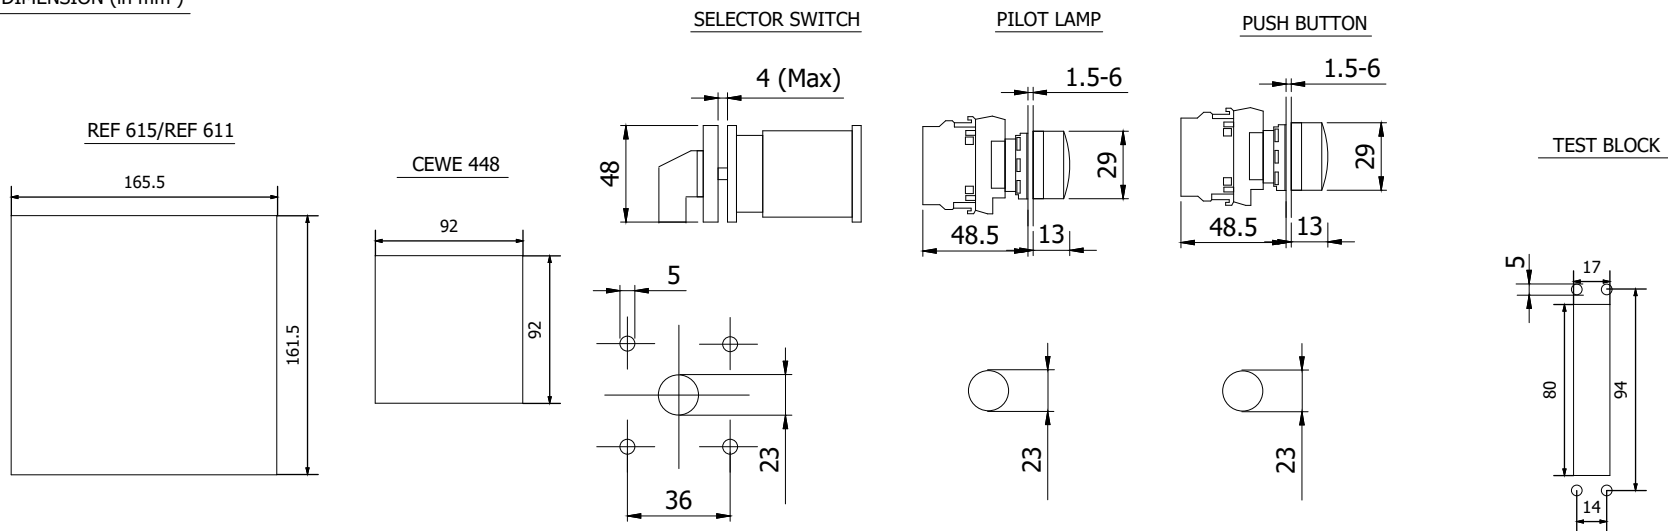

			Date Prep.	26.03.2020	PROJECT TITLE BIODIESEL AND FLEXTECH PLANT	ABB	EPMV	LV DOOR LAYOUT BIODIESEL PLANT SCHEMATIC DIAGRAM SBC-W OUTGOING	Scale	NTS	= H03,H04,H05	
			Prepared	YR					Customer	PT Multimas Nabati Asahan	& 303	
00	Issued for Approval	26.03.20	YR	Checked		AW	Drawing Nbr.		20.003-MNA-303	Sh.	15	
Ind.	Revision	Date	Name	Approved	AI	PT. ABB Sakti Industri			Customer Doc. Nbr.		Cont.	28
					Based on:	BE320003						

WE RESERVE ALL RIGHTS IN THIS DOCUMENT AND IN THE INFORMATION CONTAINED THEREIN. REPRODUCTION, USE OR DISCLOSURE TO THIRD PARTIES WITHOUT EXPRESS AUTHORITY IS STRICTLY FORBIDDEN.

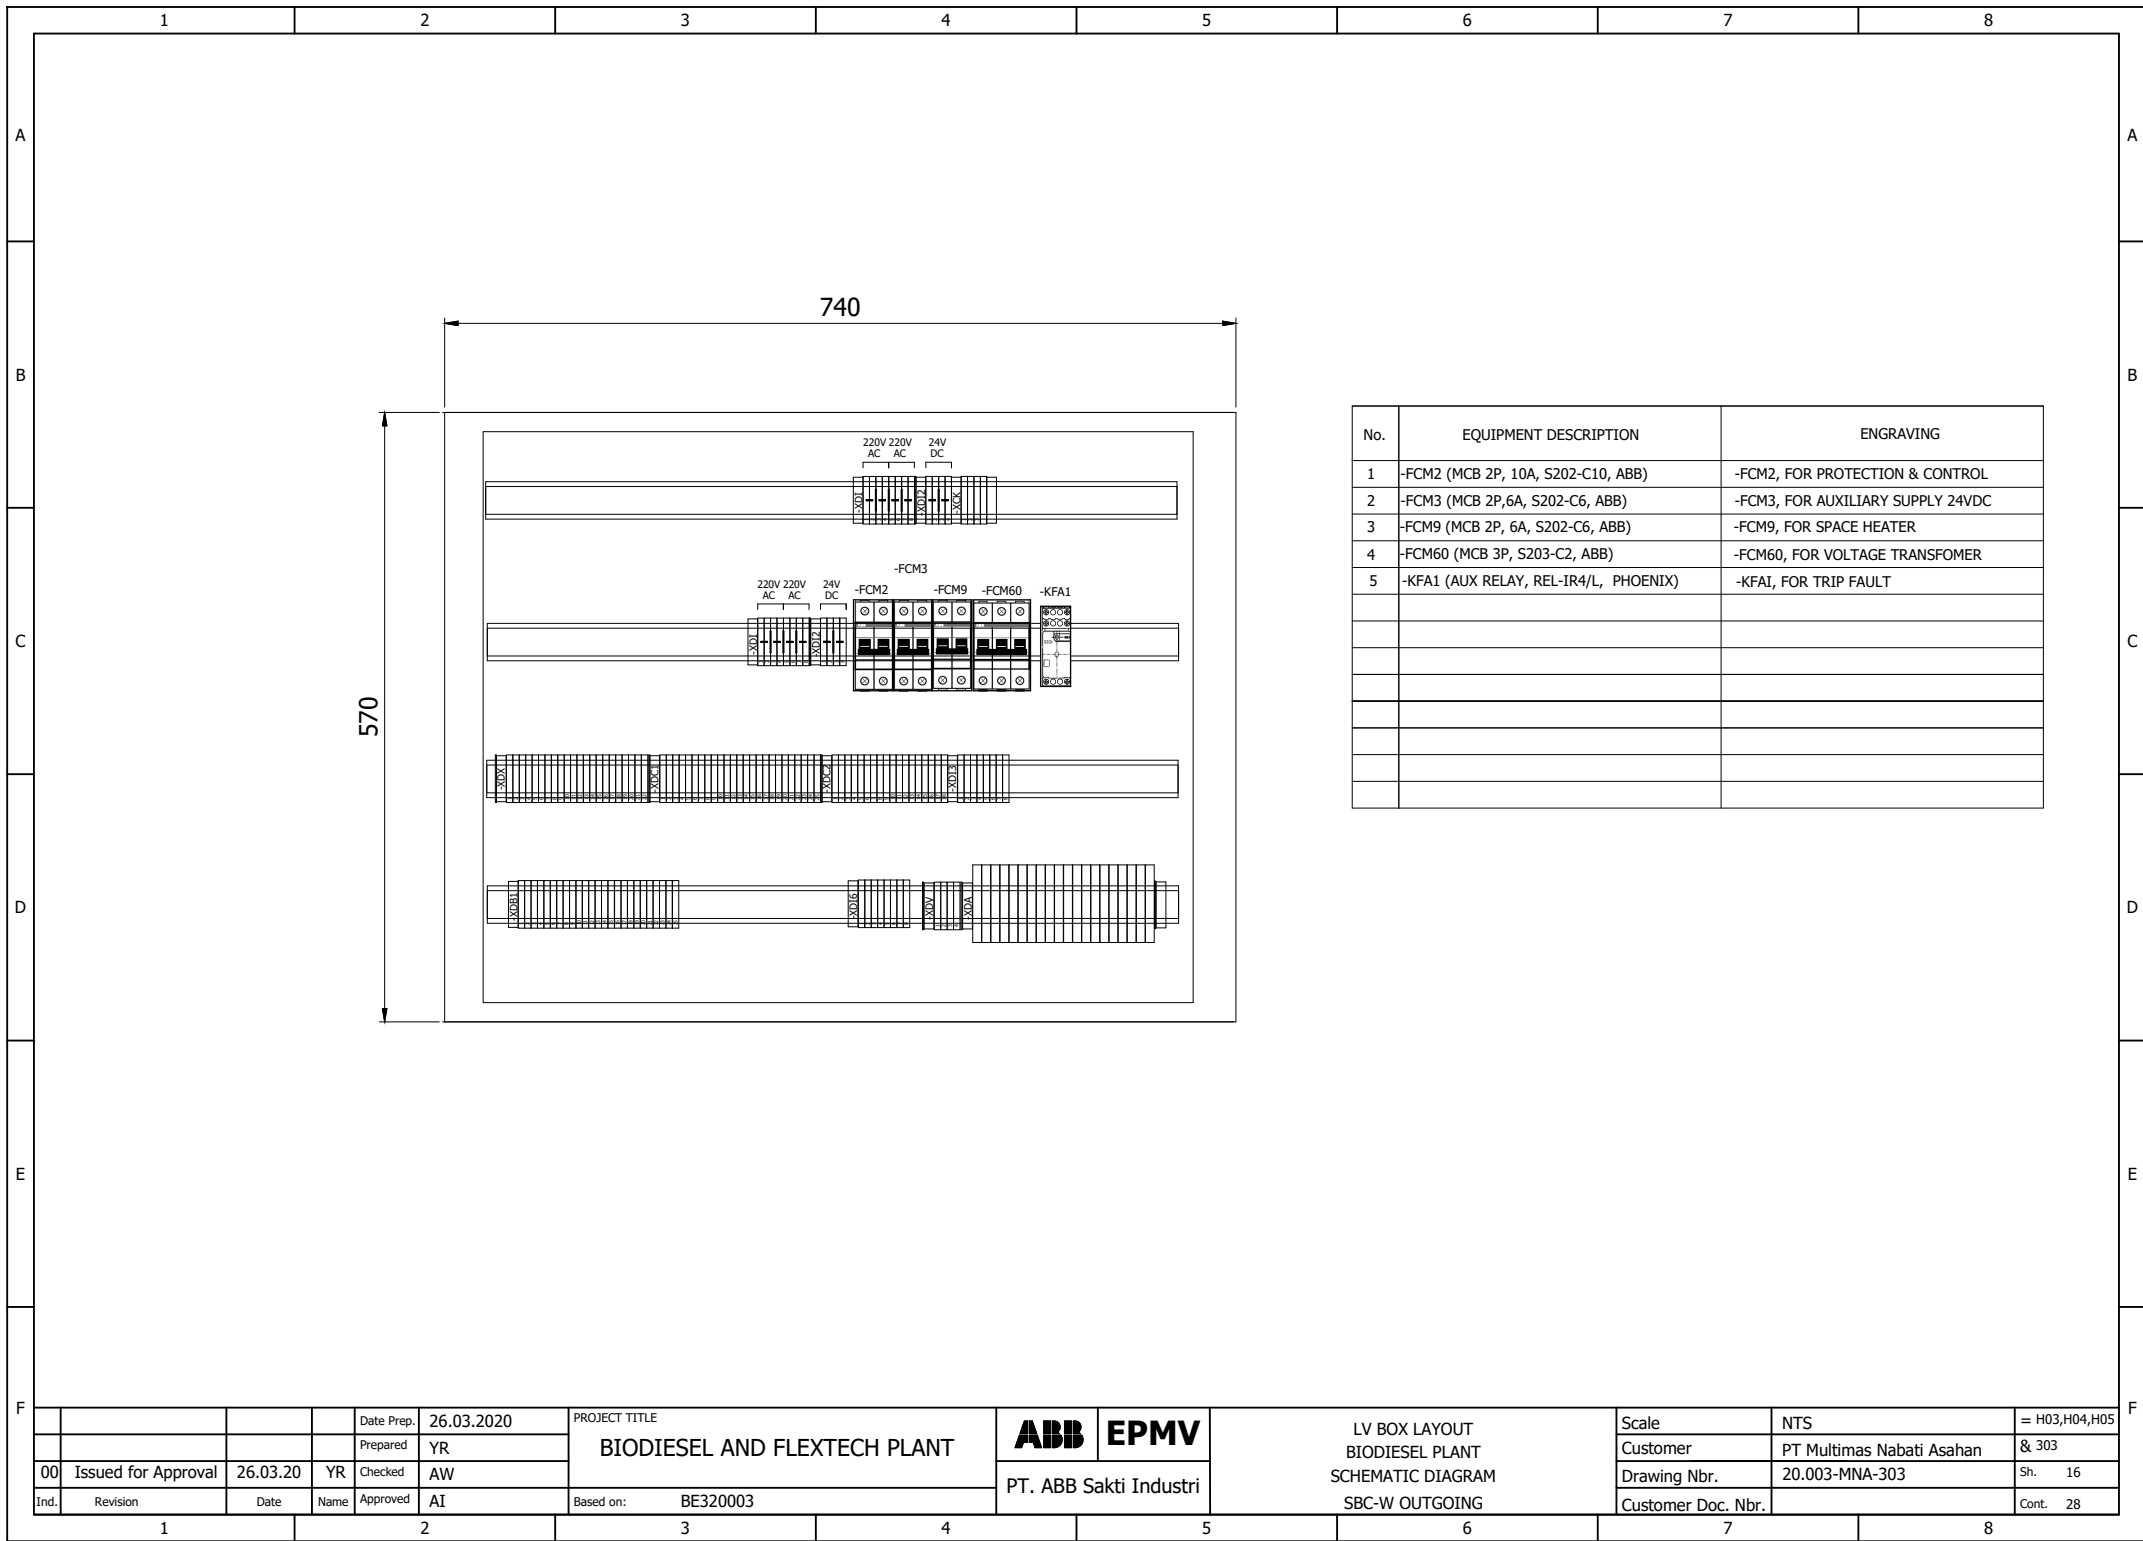

				Date Prep.	26.03.2020	PROJECT TITLE		ABB EPMV	LV BOX LAYOUT BIODIESEL PLANT SCHEMATIC DIAGRAM SBC-W OUTGOING	Scale	NTS	= H03,H04,H05
				Prepared	YR	BIODIESEL AND FLEXTech PLANT				Customer	PT Multimas Nabati Asahan	& 303
00	Issued for Approval	26.03.20	YR	Checked	AW					Drawing Nbr.	20.003-MNA-303	Sh. 16
Ind.	Revision	Date	Name	Approved	AI	Based on: BE320003		PT. ABB Sakti Industri	Customer Doc. Nbr.		Cont. 28	

WE RESERVE ALL RIGHTS IN THIS DOCUMENT AND IN THE INFORMATION CONTAINED THEREIN. REPRODUCTION, USE OR DISCLOSURE TO THIRD PARTIES WITHOUT EXPRESS AUTHORITY IS STRICTLY FORBIDDEN.

1		2		3		4		5		6		7		8			
Summarized parts list																	
IDABB_F02_005-IDABB																	
Carry over: 0.00																	
A	TAG ID			DESCRIPTION				MANUFACTUR/BRAND		PART NUMBER		QUANTITY		REMARKS			
	-BCF			Feeder Management Relay REF611HBAABC1NN11G				ABB		REF611HBAABC1NN11G		1		/8.2:C			
B	-EB			HEATER 230VAC, 50W				SANYANG		CDXN010033P0009		1		/7.6:E			
	-FCM2			MCB S202-C10 MCB. 2P, 10A				ABB		2CDS252001R0104		1		/7.2:C			
	-FCM3;-FCM9			MCB S202-C6 MCB. 2P, 6A				ABB		2CDS252001R0064		2		/7.5:C;/7.6:C			
	-FCM60			MCB S203-C2 MCB. 3P, 2A				ABB		2CDS253001R0024		1		/14.5:C			
C	-KFA1			Auxiliary Relay 230AC 4COS				PHOENIX		1YRA3DL266230001		1		/9.7:E			
	-PFG1			PILOT LIGHT GREEN #CL-523G#230VAC CL-523G				ABB		1SFA619402R5232		1		/8.5:E			
	-PFR1			PILOT LIGHT RED #CL-523R#230VAC CL-523R				ABB		1SFA619402R5231		1		/8.4:E			
	-PFY1			PILOT LIGHT YELLOW #CL-523Y#230VAC CL-523Y				ABB		1SFA619402R5233		1		/8.6:E			
D	-PGM1			POWER METER CEWE 448 Class : 0.5s; CT Input : 1A; VT Input : 57.7-240V (L-N); Aux. Voltage: 80-300VAC/DC				CEWE		1YRA4EA0350001		1		/8.3:C			
	-SFC			PUSH BUTTON, CP1-10G-11,1NC+1NO GREEN COLOUR				ABB		1SFA619100R1072		1		/9.2:B			
	-SFO			PUSH BUTTON, CP1-10R-11,1NC+1NO RED COLOUR				ABB		1SFA619100R1071		1		/9.4:B			
	-SFS			LOCAL/REMOTE Selector Switch Type : S0-CA10-A721-600-FT2; Contact : 2NC & 2NO; Mounting Type : FT2				K&N		1YRA3DA17900201		1		/9.2:B			
E	-XTA1;-XTA2			Current Test Block Rated Current : 10A, 250V; Mounting : Flush Mounting				YONGSUNG		YSCTT-04C		2		/13.4:C;/13.4:D			
F																	
				Date Prep.	26.03.2020		PROJECT TITLE					Scale		NTS		= H03,H04,H05	
				Prepared	YR		BIODIESEL AND FLEXTech PLANT			ABB EPMV		Customer		PT Multimas Nabati Asahan		& 303	
00		Issued for Approval		26.03.20	YR	Checked	AW		PT. ABB Sakti Industri			Drawing Nbr.		20.003-MNA-303		Sh. 17	
Ind.		Revision		Date	Name	Approved	AI		Based on: BE320003			Customer Doc. Nbr.				Cont. 28	
1				2		3		4		5		6		7		8	

--	--

REMARK: ☆ INTERPANEL LIGHT BUS, OFFERED TOGETHER WITH PANELS.
 △ OUTGOING CONTROL CABLE (Supply by Customer).
 ● BRIDGE BAR.
 ✕ PARTITION PLATE.
 (TEST JUMPER.

F				E		D		C		B		A						
XDC1																		
REMARK				CABLE	EQUIPMENT	Wire No	Terminal number	TYPE	WIRE NO.	EQUIPMENT	CABLE	REMARK						
BLACK 1,5 mm²					+CONTROL_BOX		1 ●	PT 2.5		-SFS:4		BLACK 1,5 mm²						
							2 ●	PT 2.5										
							3 ●	PT 2.5		+CONTROL_BOX								
							4 ●	PT 2.5										
							5 ●	PT 2.5										
BLACK 1,5 mm²					+CONTROL_BOX		6 ●	PT 2.5		-SFS:3		BLACK 1,5 mm²						
							7 ●	PT 2.5										
							8 ●	PT 2.5										
							9 ●	PT 2.5		+CONTROL_BOX								
							10 ●	PT 2.5										
BLACK 1,5 mm²					-BCF:X100:18		11 ●	PT 2.5		-SFC:4		BLACK 1,5 mm²						
							12 ●	PT 2.5										
							13	PT 2.5		-PFY1:x1								
							14	PT 2.5		+CONTROL_BOX								
							15	PT 2.5		+CONTROL_BOX								
BLACK 1,5 mm²					-KFA1:21		16	PT 2.5		+CONTROL_BOX		BLACK 1,5 mm²						
					+CONTROL_BOX		17 ●	PT 2.5		-XDx:17								
					+CONTROL_BOX		18 ●	PT 2.5										
					+CONTROL_BOX		19 ●	PT 2.5										
							20 ●	PT 2.5		-XDB1:14								
BLACK 1,5 mm²					-QBS-KFU-XDB97:19		21 ●	PT 2.5				BLACK 1,5 mm²						
					-QBS-KFU-XDB97:21		22	PT 2.5										
					-QBS-KFU-XDB97:23		23	PT 2.5										
							24 ●	PT 2.5		-QBS-BG17:NO								
							25 ●	PT 2.5		-QBS:-XDB93/14								
					REMARK: ☆ INTERPANEL LIGHT BUS OFFERED TOGETHER WITH PANELS.													
					△ OUTGOING CONTROL CABLE (Supply by Customer).													
● BRIDGE BAR.																		
✕ PARTITION PLATE.																		
(TEST JUMPER.																		

1		2		3		4		5		6		7		8	
Date Prep. 26.03.2020		PROJECT TITLE		BIODIESEL AND FLEXTECH PLANT		ABB EPMV		Terminal diagram BIODIESEL PLANT SCHEMATIC DIAGRAM SBC-W OUTGOING		Scale				= H03,H04,H05	
00 Issued for Approval 26.03.20		YR		Checked AW		PT. ABB Sakti Industri				Customer		PT Multimas Nabati Asahan		& 303	
Ind. Revision		Date		Name Approved AI		Based on: BE320003				Drawing Nbr.		20.003-MNA-303		Sh. 21	
										Customer Doc. Nbr.				Cont. 28	

XDI

- ☆ INTERPANEL LIGHT BUS OFFERED TOGETHER WITH PANELS.
- △ OUTGOING CONTROL CABLE (Supply by Customer).
- BRIDGE BAR.
- ✕ PARTITION PLATE.
- (TEST JUMPER.

XDI2

WE RESERVE ALL RIGHTS IN THIS DOCUMENT AND IN THE INFORMATION CONTAINED THEREIN. REPRODUCTION, USE OR DISCLOSURE TO THIRD PARTIES WITHOUT EXPRESS AUTHORITY IS STRICTLY FORBIDDEN.

1		2		3		4		5		6		7		8									
A		B		C		D		E		F		A		B		C		D		E		F	
XDI3		REMARK	CABLE	EQUIPMENT	WIRE NO.	TYPE	Terminal number	Wire No	EQUIPMENT	CABLE	REMARK	REMARK: ☆ INTERPANEL LIGHT BUS, OFFERED TOGETHER WITH PANELS. △ OUTGOING CONTROL CABLE (Supply by Customer). ● BRIDGE BAR. ✕ PARTITION PLATE. (TEST JUMPER.											
		BLACK 1,5 mm²				PT 2.5	1				BLACK 1,5 mm²												
				-XDB1:22		PT 2.5	2																
						PT 2.5	3																
						PT 2.5	4																
				-FCM3:4		PT 2.5	5															BLACK 1,5 mm²	
						PT 2.5	6																
				-BCF:X120:1		PT 2.5	7															BLACK 1,5 mm²	
				-BCF:X120:4		PT 2.5	8															BLACK 1,5 mm²	
														</									

F		E		D		C		B		A									
REMARK		CABLE		EQUIPMENT		Wire No		Terminal number		TYPE		WIRE NO.		EQUIPMENT		CABLE		REMARK	
BLACK 1,5 mm²				-PREVIOUS_PNL-XDI6:2				1 ●		PT 2.5				-NEXT_PNL-XDI6:1					
BLACK 1,5 mm²				-PREVIOUS_PNL-XDI6:4				2 ●		PT 2.5									
BLACK 1,5 mm²				-PREVIOUS_PNL-XDI6:6				3 ●		PT 2.5						-NEXT_PNL-XDI6:2			
BLACK 1,5 mm²				-PREVIOUS_PNL-XDI6:8				4 ●		PT 2.5									
BLACK 1,5 mm²				-XDV:4				5 ●		PT 2.5									
								6 ●		PT 2.5									
								7 ●		PT 2.5									
								8 ●		PT 2.5						-NEXT_PNL-XDI6:4			

1		2		3		4		5		6		7		8									
A		B		C		D		E		F		A		B		C		D		E		F	
XDV																							
REMARK		CABLE		EQUIPMENT		WIRE NO.		TYPE		Terminal number		Wire No		EQUIPMENT		CABLE		REMARK					
BLACK 1,5 mm²				-FCM60.2				PT 2.5		1				-PGM:V1				BLACK 1,5 mm²					
BLACK 1,5 mm²				-FCM60.4				PT 2.5		2				-PGM:V2				BLACK 1,5 mm²					
BLACK 1,5 mm²				-FCM60.6				PT 2.5		3				-PGM:V3				BLACK 1,5 mm²					
BLACK 1,5 mm²				-XD16:8				PT 2.5		4				-PGM:N				BLACK 1,5 mm²					

XDX									
REMARK	CABLE	EQUIPMENT	Wire No	Terminal number	TYPE	WIRE NO.	EQUIPMENT	CABLE	REMARK
BLACK 1,5 mm²		-XDB1:16		● 1	PT 2.5				BLACK 1,5 mm²
BLACK 1,5 mm²		-BCF:-X100:1		● 2	PT 2.5				
BLACK 1,5 mm²		-XDB1:6		● 3	PT 2.5				
BLACK 1,5 mm²		-XDB1:7		● 4	PT 2.5				
BLACK 1,5 mm²		-KFA1:14		● 5	PT 2.5				
BLACK 1,5 mm²		-XDB1:10		● 6	PT 2.5				
BLACK 1,5 mm²		-XDB1:12		● 7	PT 2.5				
BLACK 1,5 mm²		-KFA1:24		● 8	PT 2.5				
BLACK 1,5 mm²		-SFS:1		● 9	PT 2.5				
BLACK 1,5 mm²		-BCF:X100:16		● 10	PT 2.5				
BLACK 1,5 mm²		-BCF:X100:14		● 11	PT 2.5				
				● 12	PT 2.5				
BLACK 1,5 mm²		-QBS-KFU-XDB97:16		● 13	PT 2.5				BLACK 1,5 mm²
BLACK 1,5 mm²		-FCM2:4		● 14	PT 2.5				BLACK 1,5 mm²
				● 15	PT 2.5				BLACK 1,5 mm²
				● 16	PT 2.5				BLACK 1,5 mm²
				● 17	PT 2.5				BLACK 1,5 mm²
				● 18	PT 2.5				BLACK 1,5 mm²
				● 19	PT 2.5				BLACK 1,5 mm²
				● 20	PT 2.5				BLACK 1,5 mm²
				● 21	PT 2.5				BLACK 1,5 mm²
				● 22	PT 2.5				BLACK 1,5 mm²