

WE RESERVE ALL RIGHTS IN THIS DOCUMENT AND IN THE INFORMATION CONTAINED THEREIN. REPRODUCTION, USE OR DISCLOSURE TO THIRD PARTIES WITHOUT EXPRESS AUTHORITY IS STRICTLY FORBIDDEN.

1	2	3	4	5	6	7	8	
A								A
B								B
C								C
D								D
E								E
F								F
<								

LOCAL CONTROL PANEL

PT MULTIMAS NABATI ASAHAN

BIODIESEL PLANT

			Date Prep.	26.03.2020	PROJECT TITLE				Scale	NTS	= LCP
			Prepared	YR	BIODIESEL AND FLEXTECH PLANT				Customer	PT Multimas Nabati Asahan	& 300
00	Issued for approval	15.01.19	YR	Checked	AW			Drawing Nbr.	20.003-LCP-300	Sh.	1
Ind.	Revision	Date	Name	Approved	AI	Based on: BE320003		Customer Doc. Nbr.		Cont.	11



COVER SHEET

BIODIESEL PLANT


LOCAL CONTROL PANEL

PAGE	PAGE NAME	REVISION		
==BIODIESEL_PLANT=LCP&300/1	COVER SHEET	00		
==BIODIESEL_PLANT=LCP&300/2	Index of Sheet	00		
==BIODIESEL_PLANT=LCP&300/3	CIRCUIT CONTROL	00		
==BIODIESEL_PLANT=LCP&300/4	CIRCUIT CONTROL	00		
==BIODIESEL_PLANT=LCP&300/5	LCP LAYOUT	00		
==BIODIESEL_PLANT=LCP&300/6	PART LIST	00		
==BIODIESEL_PLANT=LCP&300/7	Terminal diagram ==BIODIESEL_PLANT=LCP+-X1	00		
==BIODIESEL_PLANT=LCP&300/8	Terminal diagram ==BIODIESEL_PLANT=LCP+-X2	00		
==BIODIESEL_PLANT=LCP&300/9	Terminal diagram ==BIODIESEL_PLANT=LCP+-X3	00		
==BIODIESEL_PLANT=LCP&300/10	Terminal diagram ==BIODIESEL_PLANT=LCP+-X4	00		
==BIODIESEL_PLANT=LCP&300/11	Terminal diagram ==BIODIESEL_PLANT=LCP+-X5	00		


F

F

WE RESERVE ALL RIGHTS IN THIS DOCUMENT AND IN THE INFORMATION CONTAINED THEREIN. REPRODUCTION, USE OR DISCLOSURE TO THIRD PARTIES WITHOUT EXPRESS AUTHORITY IS STRICTLY FORBIDDEN.

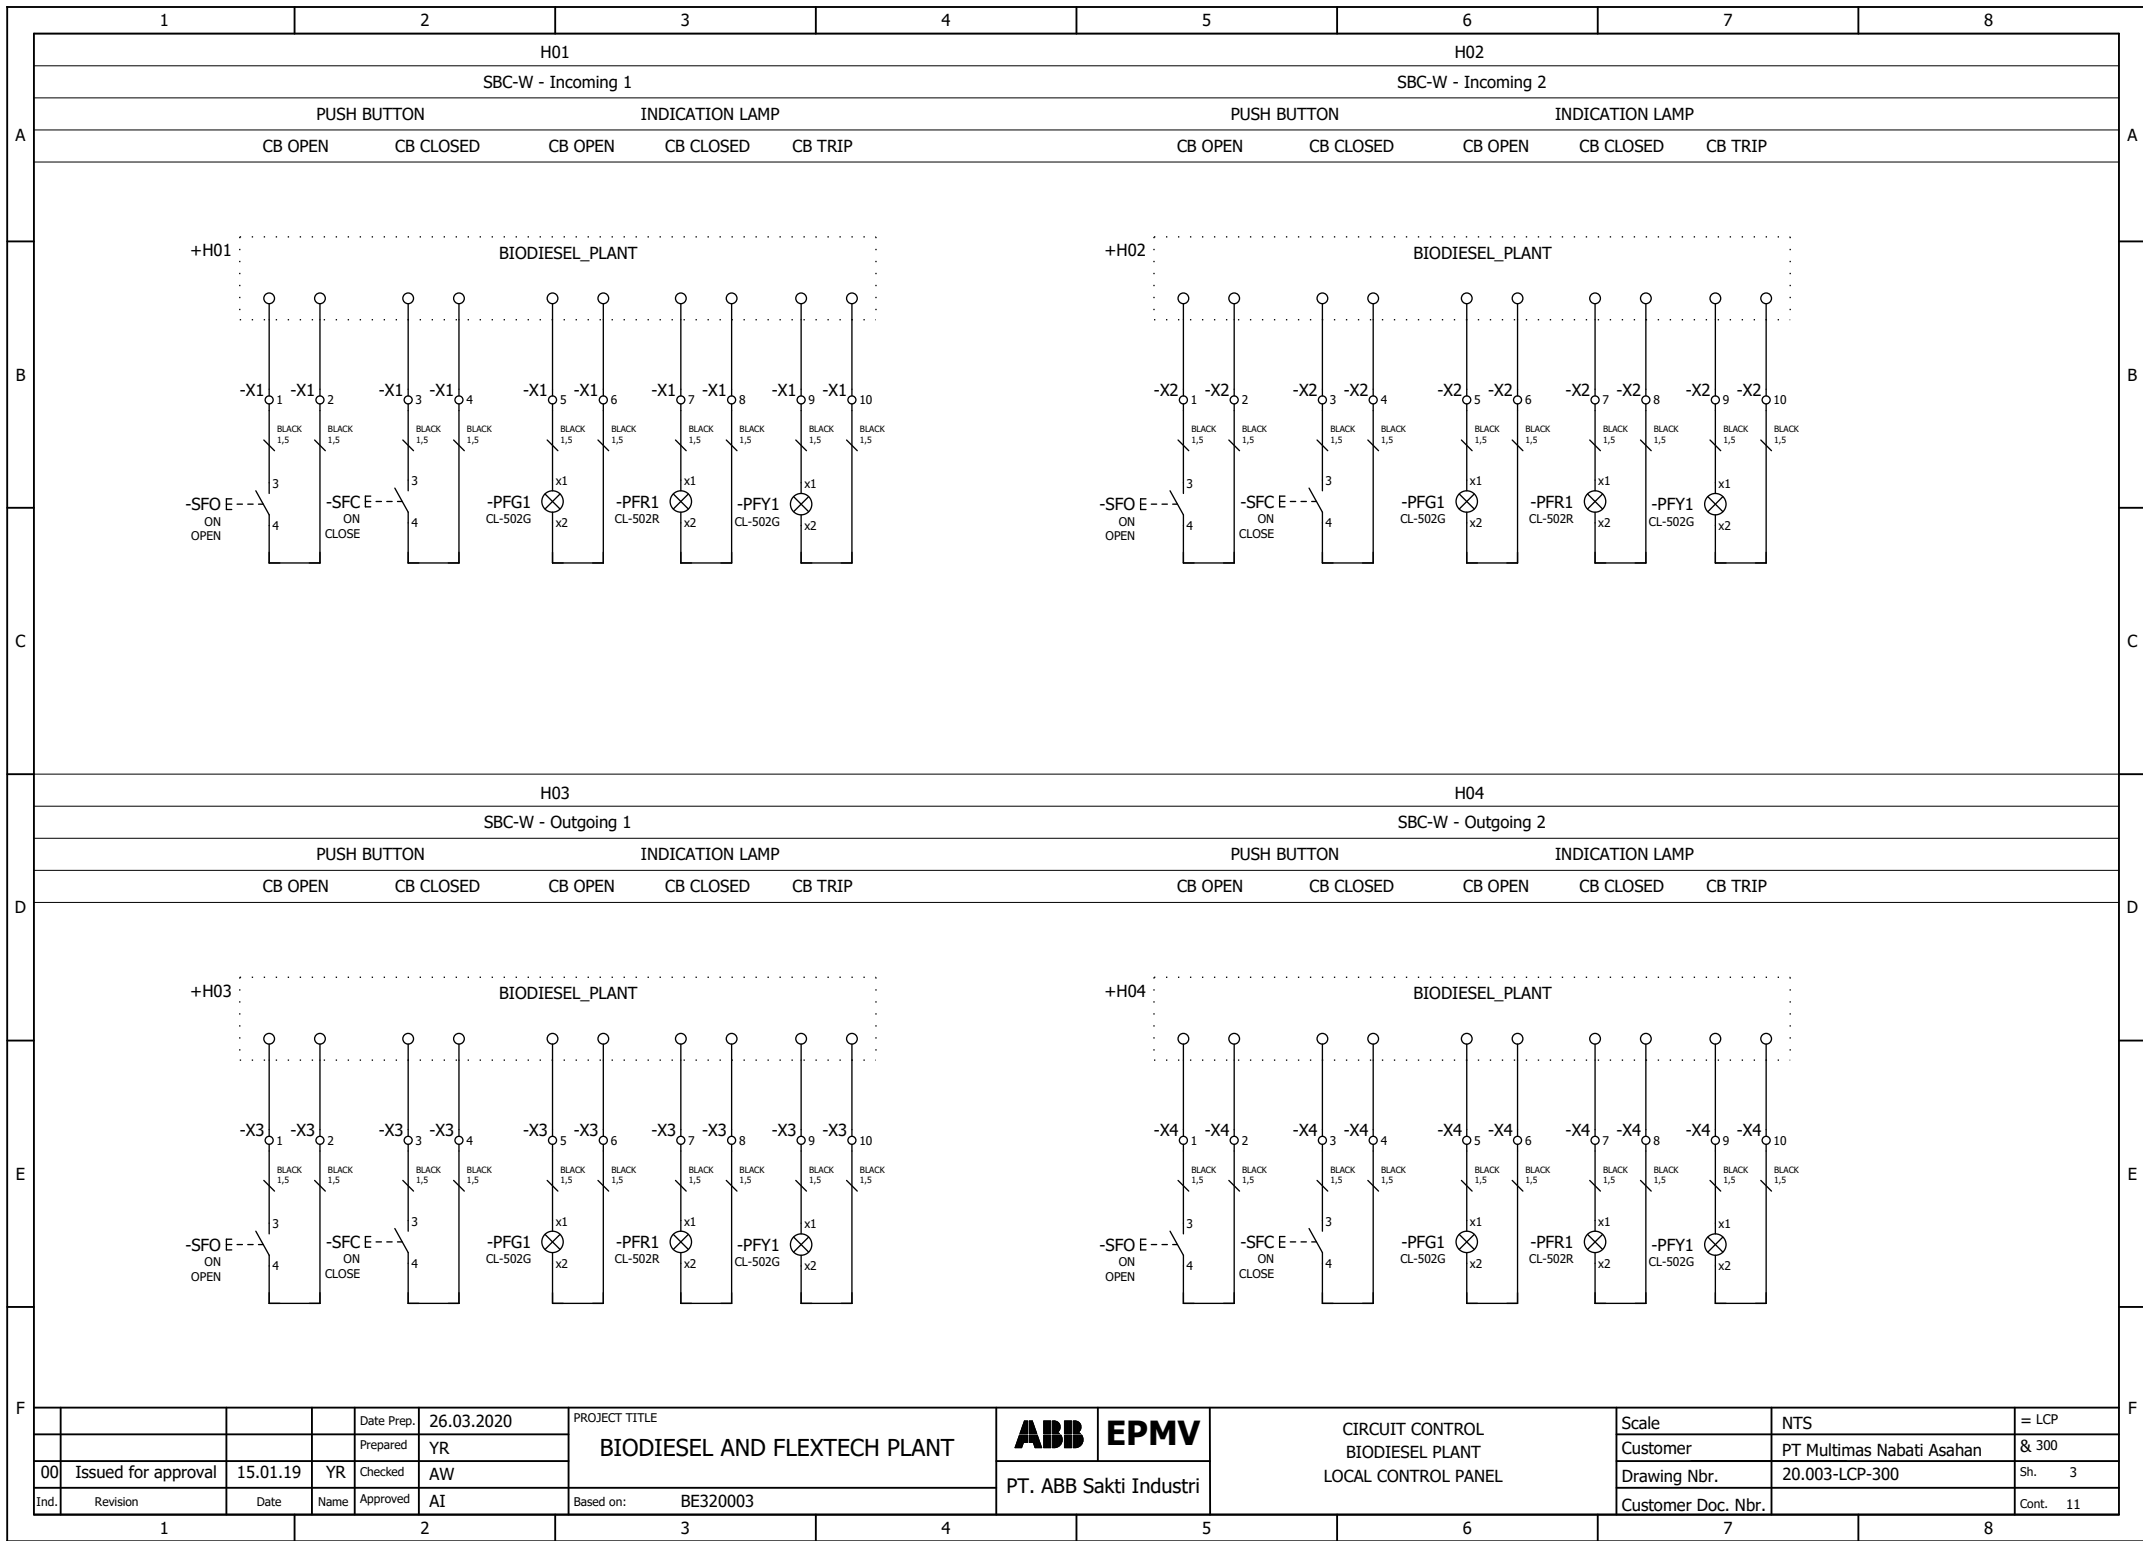

WE RESERVE ALL RIGHTS IN THIS DOCUMENT AND IN THE INFORMATION CONTAINED THEREIN. REPRODUCTION, USE OR DISCLOSURE TO THIRD PARTIES WITHOUT EXPRESS AUTHORITY IS STRICTLY FORBIDDEN.

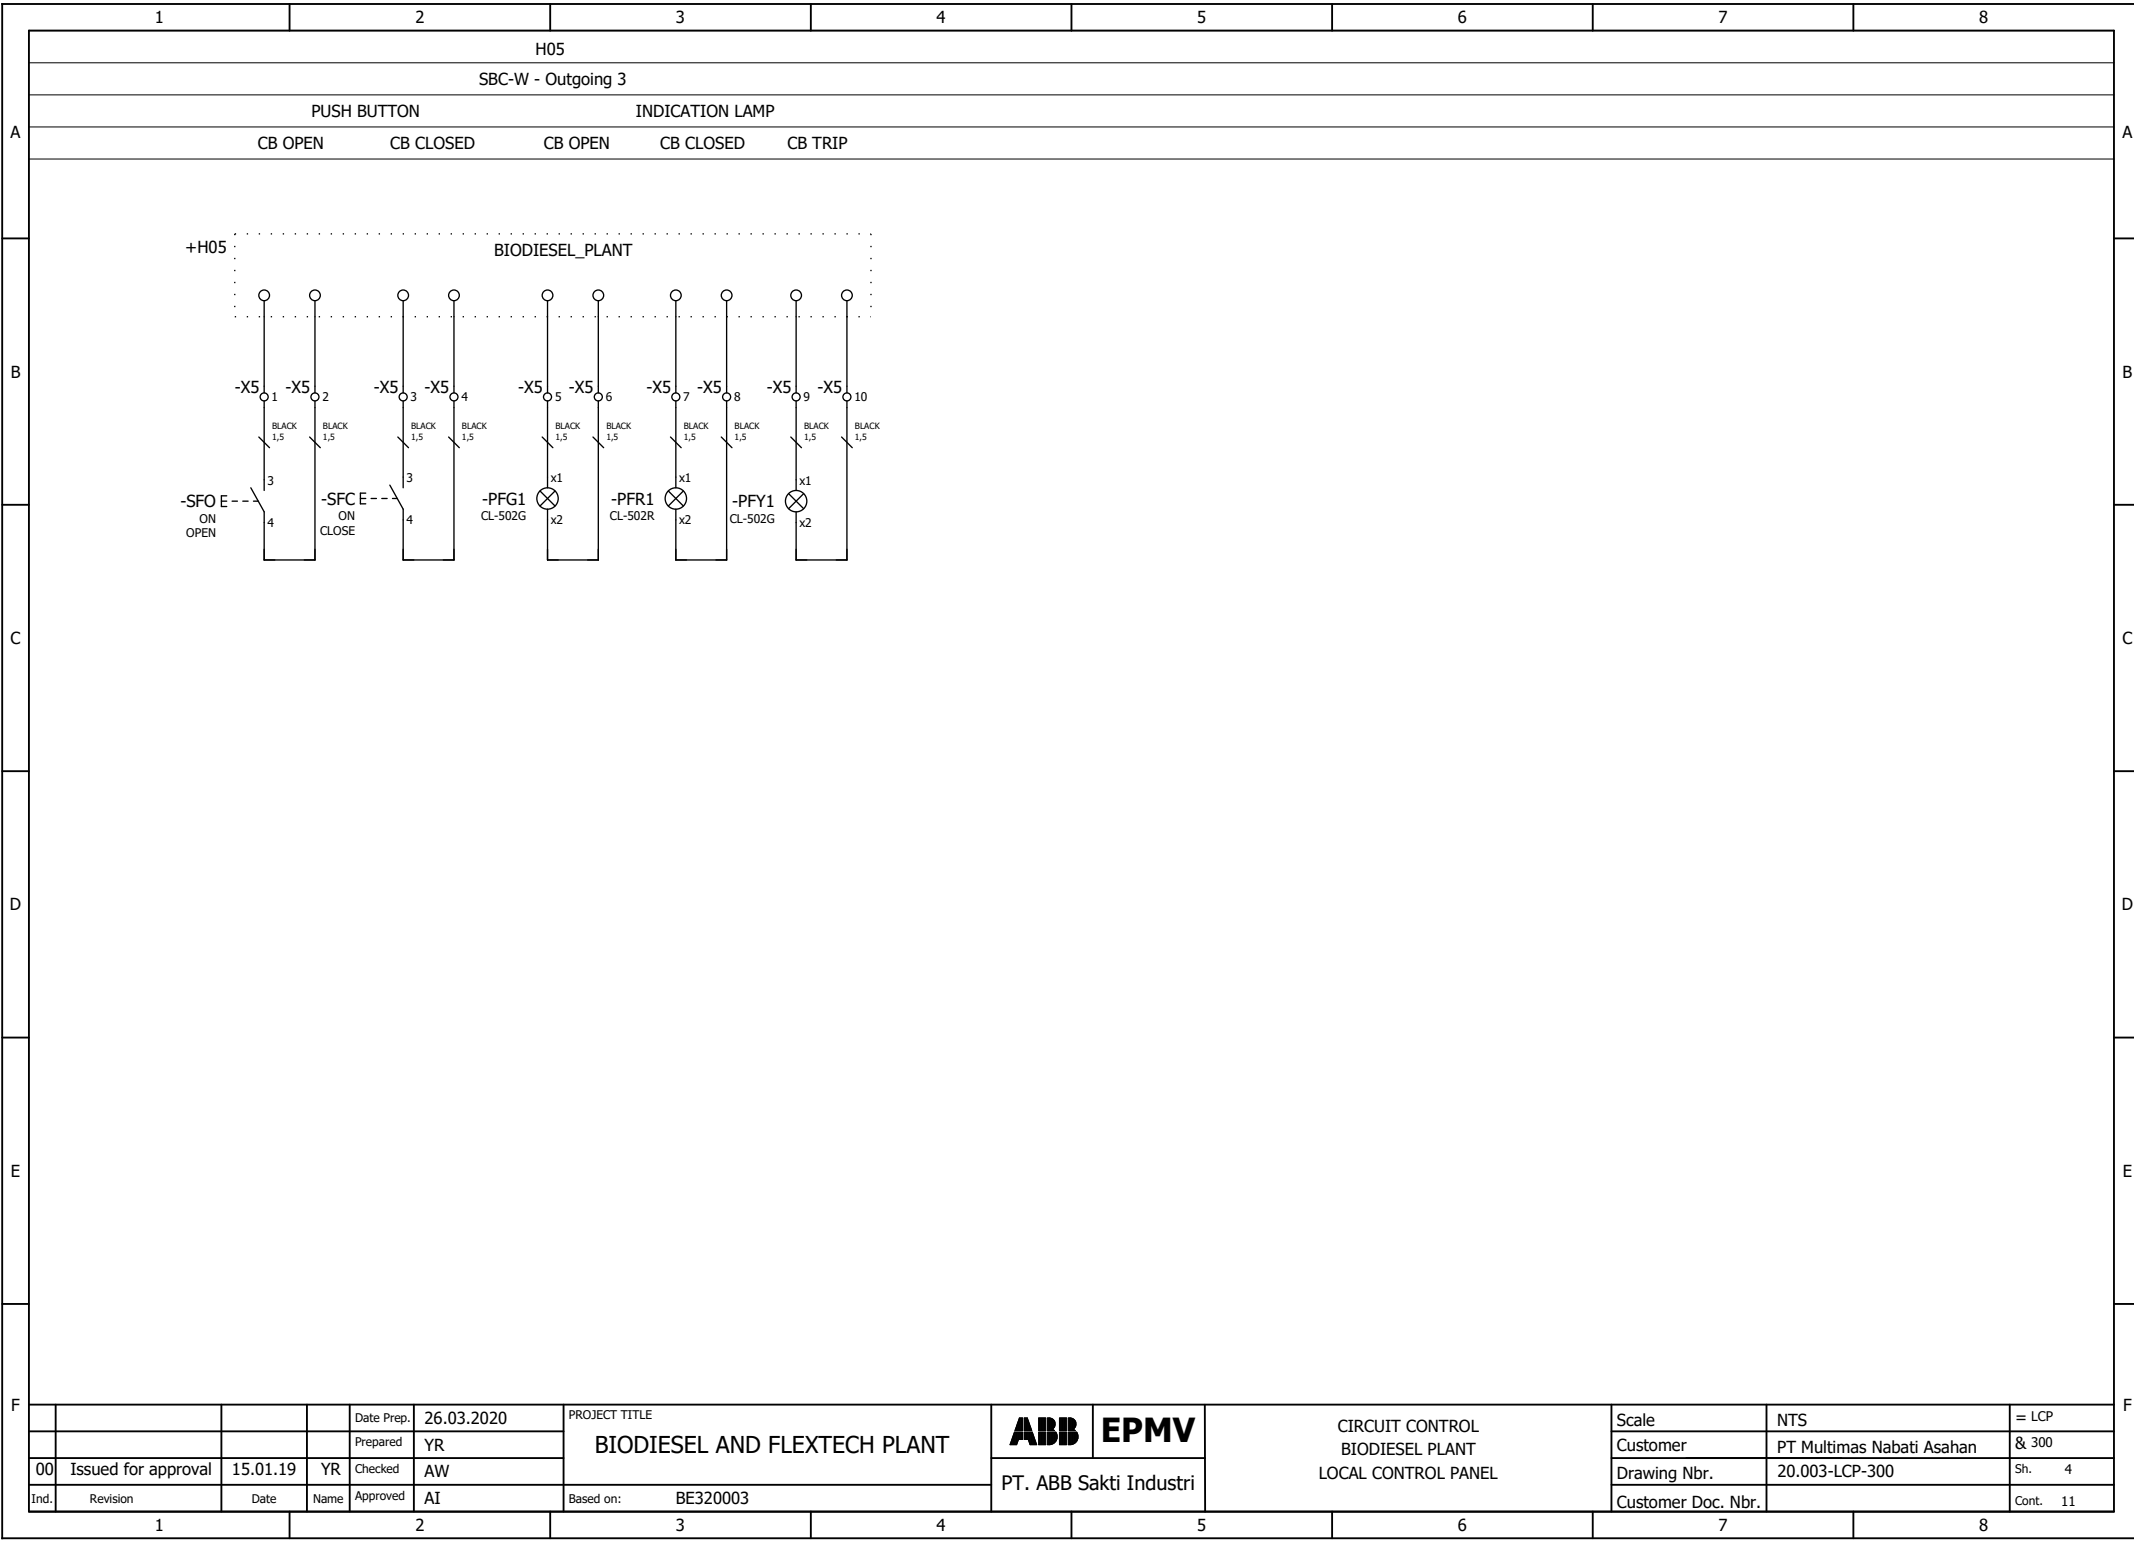

1

2

3

4

5


6

7



8

WE RESERVE ALL RIGHTS IN THIS DOCUMENT AND IN THE INFORMATION CONTAINED THEREIN. REPRODUCTION, USE OR DISCLOSURE TO THIRD PARTIES WITHOUT EXPRESS AUTHORITY IS STRICTLY FORBIDDEN.

PANEL LAYOUT

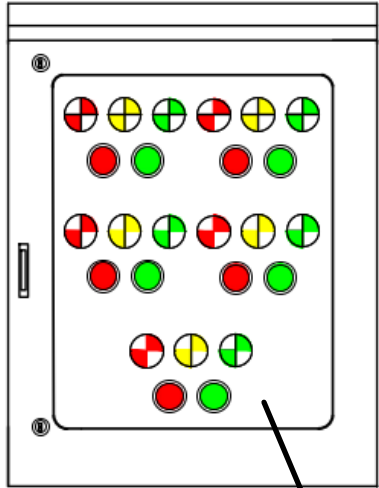

GLASS DOOR

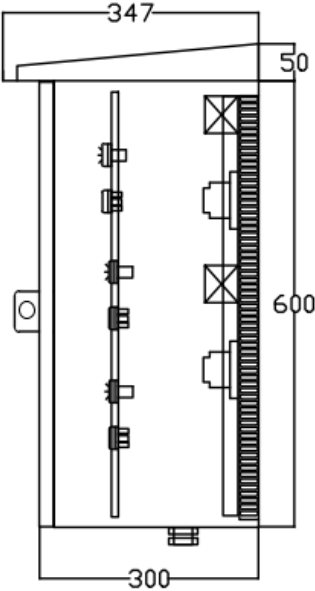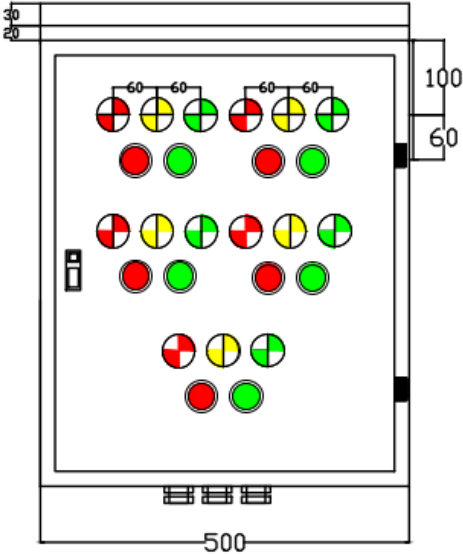

				Date Prep.	26.03.2020	PROJECT TITLE BIODIESEL AND FLEXTech PLANT	ABB	EPMV	LCP LAYOUT BIODIESEL PLANT LOCAL CONTROL PANEL	Scale	NTS	= LCP
				Prepared	YR					Customer	PT Multimas Nabati Asahan	& 300
00	Issued for approval	15.01.19	YR	Checked	AW		Drawing Nbr.	20.003-LCP-300		Sh. 5		
Ind.	Revision	Date	Name	Approved	AI	Based on:	BE320003			Customer Doc. Nbr.		Cont. 11
						PT. ABB Sakti Industri						

WE RESERVE ALL RIGHTS IN THIS DOCUMENT AND IN THE INFORMATION CONTAINED THEREIN. REPRODUCTION, USE OR DISCLOSURE TO THIRD PARTIES WITHOUT EXPRESS AUTHORITY IS STRICTLY FORBIDDEN.

1		2		3		4		5		6		7		8	
Summarized parts list															
IDABB_F02_005-IDABB															
Carry over: 0.00															
TAG ID		DESCRIPTION				MANUFACTUR/BRAND		PART NUMBER		QUANTITY		REMARKS			
-PFG1		PILOT LAMP GREEN Voltage: 230VAC				FORT		PL FORT GREEN		5		/3.2:B;/3.2:E;/3.6:B;/3.6:E;/4.2:B			
-PFR1		PILOT LAMP RED Voltage: 230VAC				FORT		PL FORT RED		5		/3.3:B;/3.3:E;/3.6:B;/3.6:E;/4.3:B			
-PFY1		PILOT LAMP YELLOW Voltage: 230VAC				FORT		PL FORT YELLOW		5		/3.3:B;/3.3:E;/3.7:B;/3.7:E;/4.3:B			
-SFC		PUSH BUTTON GREEN COLOUR				FORT		PB FORT GREEN		5		/3.2:B;/3.2:E;/3.5:B;/3.5:E;/4.2:B			
-SFO		PUSH BUTTON RED COLOUR				FORT		PB FORT RED		5		/3.1:B;/3.1:E;/3.5:B;/3.5:E;/4.1:B			

- ☆ INTERPANEL LIGHT BUS, OFFERED TOGETHER WITH PANELS.
- △ OUTGOING CONTROL CABLE (Supply by Customer).
- BRIDGE BAR.
- ✕ PARTITION PLATE.
- (TEST JUMPER.

1		2		3		4		5		6		7		8									
A		B		C		D		E		F		A		B		C		D		E		F	
X2										REMARK	CABLE	EQUIPMENT	Wire No	Terminal number	TYPE	WIRE NO.	EQUIPMENT	CABLE	REMARK				
										BLACK 1,5 mm²	-SFO:3	-SFO:3		1	PT 2.5		+H02						
										BLACK 1,5 mm²	-SFO:4	-SFO:4		2	PT 2.5		+H02						
										BLACK 1,5 mm²	-SFC:3	-SFC:3		3	PT 2.5		+H02						
										BLACK 1,5 mm²	-SFC:4	-SFC:4		4	PT 2.5		+H02						
										BLACK 1,5 mm²	-PFG1:X1	-PFG1:X1		5	PT 2.5		+H02						
										BLACK 1,5 mm²	-PFG1:X2	-PFG1:X2		6	PT 2.5		+H02						
										BLACK 1,5 mm²	-PFR1:X1	-PFR1:X1		7	PT 2.5		+H02						
										BLACK 1,5 mm²	-PFR1:X2	-PFR1:X2		8	PT 2.5		+H02						
										BLACK 1,5 mm²	-PFY1:X1	-PFY1:X1		9	PT 2.5		+H02						
										BLACK 1,5 mm²	-PFY1:X2	-PFY1:X2		10	PT 2.5		+H02						
														</									

- ☆ INTERPANEL LIGHT BUS, OFFERED TOGETHER WITH PANELS.
- △ OUTGOING CONTROL CABLE (Supply by Customer).
- BRIDGE BAR.
- ✕ PARTITION PLATE.
- (TEST JUMPER.

