

WE RESERVE ALL RIGHTS IN THIS DOCUMENT AND IN THE INFORMATION CONTAINED THEREIN. REPRODUCTION, USE OR DISCLOSURE TO THIRD PARTIES WITHOUT EXPRESS AUTHORITY IS STRICTLY FORBIDDEN.

1		2		3		4		5		6		7		8	
A															A
B															B
C															C
D															D
E															E
F															F
				Date Prep.	15.11.2018	PROJECT TITLE		ABB	EPMV	COVER SHEET MVD-01 20kV MAIN SUBSTATION SCHEMATIC DIAGRAM WBC INCOMING		Scale		= H01	
				Prepared	YR	MV Switchgear for MNA Serang Plant						Customer	PT Multimas Nabati Asahan	& 301	
00	Issued for Approval	28.12.18	YR	Checked	AW			PT. ABB Sakti Industri				Drawing Nbr.	IDUNISEC-BE318042-301	Sh.	1
Ind.	Revision	Date	Name	Approved	AI	Based on: BE318042						Customer Doc. Nbr.		Cont.	31
1		2		3		4		5		6		7		8	

WE RESERVE ALL RIGHTS IN THIS DOCUMENT AND IN THE INFORMATION CONTAINED THEREIN. REPRODUCTION, USE OR DISCLOSURE TO THIRD PARTIES WITHOUT EXPRESS AUTHORITY IS STRICTLY FORBIDDEN.

	1	2	3	4	5	6	7	8								
A	SHEET INDEX								A							
B	PAGE		PAGE NAME			REVISION			B							
	==MVD-01=H01&301/1		COVER SHEET			00										
	==MVD-01=H01&301/2		Index of Sheet			00										
	==MVD-01=H01&301/3		REFERENCE DESIGNATIONS			00										
	==MVD-01=H01&301/4		REFERENCE DESIGNATIONS			00										
	==MVD-01=H01&301/5		REFERENCE DESIGNATIONS			00										
	==MVD-01=H01&301/6		REFERENCE DESIGNATIONS			00										
	==MVD-01=H01&301/7		DISTRIBUTION OF AUXILIARY CIRCUITS			00										
	==MVD-01=H01&301/8		CONTROL CIRCUITS			00										
	==MVD-01=H01&301/9		CONTROL CIRCUITS			00										
	==MVD-01=H01&301/10		CONTROL CIRCUITS			00										
	==MVD-01=H01&301/11		BINARY INPUTS			00										
	==MVD-01=H01&301/12		AVAILABLE CONTACTS			00										
	==MVD-01=H01&301/13		AVAILABLE CONTACTS			00										
	==MVD-01=H01&301/14		AVAILABLE CONTACTS			00										
	==MVD-01=H01&301/15		MAIN CIRCUITS			00										
	==MVD-01=H01&301/16		MAIN CIRCUITS			00										
	==MVD-01=H01&301/17		LV DOOR LAYOUT			00										
	==MVD-01=H01&301/18		LV BOX LAYOUT			00										
	==MVD-01=H01&301/19		PART LIST			00										
	==MVD-01=H01&301/20		Terminal diagram =H01+-XDA			00										
	==MVD-01=H01&301/21		Terminal diagram =H01+-XDB1			00										
	==MVD-01=H01&301/22		Terminal diagram =H01+-XDC1			00										
	==MVD-01=H01&301/23		Terminal diagram =H01+-XDC2			00										
	==MVD-01=H01&301/24		Terminal diagram =H01+-XDE			00										
	==MVD-01=H01&301/25		Terminal diagram =H01+-XDI			00										
	==MVD-01=H01&301/26		Terminal diagram =H01+-XDI2			00										
	==MVD-01=H01&301/27		Terminal diagram =H01+-XDI3			00										
	==MVD-01=H01&301/28		Terminal diagram =H01+-XDI6			00										
	==MVD-01=H01&301/29		Terminal diagram =H01+-XDT			00										
	==MVD-01=H01&301/30		Terminal diagram =H01+-XDX			00										
E									E							
F					Date Prep.	15.11.2018	PROJECT TITLE		ABB	EPMV	Index of Sheet		Scale		= H01	F
					Prepared	YR	MV Switchgear for MNA Serang Plant				MVD-01 20kV MAIN SUBSTATION		Customer	PT Multimas Nabati Asahan	& 301	
	00	Issued for Approval	28.12.18	YR	Checked	AW			PT. ABB Sakti Industri		SCHEMATIC DIAGRAM		Drawing Nbr.	IDUNISEC-BE318042-301	Sh. 2	
	Ind.	Revision	Date	Name	Approved	AI	Based on: BE318042		WBC INCOMING		Customer Doc. Nbr.			Cont. 31		
	1		2		3		4		5		6		7		8	

WE RESERVE ALL RIGHTS IN THIS DOCUMENT AND IN THE INFORMATION CONTAINED THEREIN. REPRODUCTION, USE OR DISCLOSURE TO THIRD PARTIES WITHOUT EXPRESS AUTHORITY IS STRICTLY FORBIDDEN.

A	REFERENCE DESIGNATION OF OBJECTS IN ELECTRICAL DOCUMENTS														A
	(IN COMPLIANCE WITH STANDARD IEC 81346-2 AND ABB TECHNICAL STANDARD 2NBA000001)														
B	DESIGNATION	DESCRIPTION													B
	-AA	MULTIFUNCTION UNIT (CENTRAL UNIT)													
	-BAD1,-BAD4	CAPACITIVE VOLTAGE DIVIDER LOCATED ON PHASE L1													
	-BAD2,-BAD5	CAPACITIVE VOLTAGE DIVIDER LOCATED ON PHASE L2													
	-BAD3,-BAD6	CAPACITIVE VOLTAGE DIVIDER LOCATED ON PHASE L3													
	-BAR	VOLTAGE PROTECTION RELAY													
	-BAS1	VOLTAGE SENSOR LOCATED ON PHASE L1													
	-BAS2	VOLTAGE SENSOR LOCATED ON PHASE L2													
	-BAS3	VOLTAGE SENSOR LOCATED ON PHASE L3													
	-BAT1	VOLTAGE TRANSFORMER LOCATED ON PHASE L1													
C	-BAT2	VOLTAGE TRANSFORMER LOCATED ON PHASE L2													C
	-BAT3	VOLTAGE TRANSFORMER LOCATED ON PHASE L3													
	-BAT4	VOLTAGE TRANSFORMER IN BUSBAR COMPARTMENT LOCATED ON PHASE L1													
	-BAT5	VOLTAGE TRANSFORMER IN BUSBAR COMPARTMENT LOCATED ON PHASE L2													
	-BAT6	VOLTAGE TRANSFORMER IN BUSBAR COMPARTMENT LOCATED ON PHASE L3													
	-BCD	DIFFERENTIAL PROTECTIVE RELAY													
	-BCF	FEEDER PROTECTION RELAY													
	-BCG	GENERATOR PROTECTION RELAY													
	-BCM	MOTOR PROTECTION RELAY													
	-BCN	NEUTRAL (RESIDUAL) CURRENT TRANSFORMER													
D	-BCP	TRANSFORMER PROTECTION RELAY													D
	-BCR	CURRENT PROTECTION RELAY													
	-BCS1	CURRENT SENSOR LOCATED ON PHASE L1													
	-BCS2	CURRENT SENSOR LOCATED ON PHASE L2													
	-BCS3	CURRENT SENSOR LOCATED ON PHASE L3													
	-BCT1	CURRENT TRANSFORMER LOCATED ON PHASE L1													
	-BCT2	CURRENT TRANSFORMER LOCATED ON PHASE L2													
	-BCT3	CURRENT TRANSFORMER LOCATED ON PHASE L3													
	-BCT4,-BCT7	CURRENT TRANSFORMER LOCATED ON PHASE L1													
	-BCT5,-BCT8	CURRENT TRANSFORMER LOCATED ON PHASE L2													
E	-BCT6,-BCT9	CURRENT TRANSFORMER LOCATED ON PHASE L3													E
	-BCZ	DISTANCE PROTECTION RELAY													
	-BEF	FREQUENCY PROTECTION RELAY													
	-BER	SUPERVISION RELAYS													
	-BES	SYNCHRONIZING RELAY													
	-BET	THERMAL PROTECTION RELAY													
	-BGA1	POSITION SWITCH FOR DETECTION OF INTERNAL ARCING IN CIRCUIT-BREAKER COMPARTMENT													
	-BGA2	POSITION SWITCH FOR DETECTION OF INTERNAL ARCING IN BUSBAR COMPARTMENT (SINGLE BUSBAR SYSTEM) OR IN FRONT BUSBAR COMPARTMENT (DOUBLE BUSBAR SYSTEM)													
	-BGA3	POSITION SWITCH FOR DETECTION OF INTERNAL ARCING IN CABLE COMPARTMENT													
	-BGA4	POSITION SWITCH FOR DETECTION OF INTERNAL ARCING IN REAR BUSBAR COMPARTMENT (DOUBLE BUSBAR SYSTEM)													
F	-BGB1...-BGB3	POSITION SWITCHES OF CIRCUIT-BREAKER													F
	-BGB4	POSITION SWITCH OF CIRCUIT-BREAKER: PASSING CONTACT CLOSING MOMENTARILY WHEN THE BREAKER OPENS													

WE RESERVE ALL RIGHTS IN THIS DOCUMENT AND IN THE INFORMATION CONTAINED THEREIN. REPRODUCTION, USE OR DISCLOSURE TO THIRD PARTIES WITHOUT EXPRESS AUTHORITY IS STRICTLY FORBIDDEN.

A	-MAE	MOTOR FOR ELECTRICAL OPERATION OF EARTHING SWITCH -QCE	-QBH	MANUAL CIRCUIT-BREAKERS
	-MAE1	MOTOR FOR ELECTRICAL OPERATION OF EARTHING SWITCH -QCE1 OR -QCE2	-QBL	LINKS
B	-MAE8	MOTOR FOR ELECTRICAL OPERATION OF EARTHING SWITCH -QCE SUPPLIED TOGETHER WITH SWITCH-DISCONNECTOR -QBS	-QBM	MINIATURE SWITCH-DISCONNECTORS
	-MAS	MOTOR FOR CIRCUIT-BREAKER SPRINGS CHARGING	-QBS	SWITCH-DISCONNECTORS
C	-MAT	MOTOR FOR ELECTRICAL OPERATION OF TRUCK RACKING-IN/OUT	-QBT	TRUCK
	-MBC	CLOSING RELEASE OF CIRCUIT-BREAKER	-QCA	EARTHING SWITCH FOR ELIMINATION OF INTERNAL ARCING
D	-MBC4	CLOSING RELEASE OF SWITCH-DISCONNECTOR -QBS	-QCE	EARTHING SWITCH
	-MBO1	FIRST OPENING RELEASE OF CIRCUIT-BREAKER	-QCE1	EARTHING SWITCH OF BUSBARS (SINGLE BUSBAR SYSTEM) OR OF FRONT BUSBARS (DOUBLE BUSBAR SYSTEM)
E	-MBO2	SECOND OPENING RELEASE OF CIRCUIT-BREAKER	-QCE2	EARTHING SWITCH OF REAR BUSBARS (DOUBLE BUSBAR SYSTEM)
	-MBO3	OPENING SOLENOID FOR OVERCURRENT RELEASE OF CIRCUIT-BREAKER OR INDIRECT OVERCURRENT RELEASE ON CIRCUIT-BREAKER	-QQ	CLUTCHES
F	-MBO4	OPENING RELEASE OF SWITCH-DISCONNECTOR -QBS	-RAA	ANTIFERRORESONANCE RESISTOR
	-MBU	UNDERVOLTAGE RELEASE OF CIRCUIT-BREAKER	-RAD	DIODES
G	-PFB	BLUE SIGNAL LAMPS	-RAI	INDUCTORS
	-PFF	FLAG RELAYS	-RAR	RESISTORS
H	-PFG	GREEN SIGNAL LAMPS	-RF	FILTERS
	-PFR	RED SIGNAL LAMPS	-RLE1	ELECTROMECHANICAL LOCK PREVENTING CIRCUIT-BREAKER CLOSING
I	-PFS	SHORT CIRCUIT INDICATORS	-RLE2	ELECTROMECHANICAL LOCK PREVENTING TRUCK RACKING-IN/OUT
	-PFV	VOLTAGE INDICATORS	-RLE3	ELECTROMECHANICAL LOCK PREVENTING INSERTION OF LEVER FOR CLOSING OPERATION OF EARTHING SWITCH -QCE
J	-PFV1	VOLTAGE INDICATORS ON FEEDER SIDE	-RLE4	ELECTROMECHANICAL LOCK PREVENTING THE DOOR OPENING OPERATION
	-PFV2	VOLTAGE INDICATORS ON BUSBAR SIDE	-RLE5	ELECTROMECHANICAL LOCK PREVENTING OPERATION OF DISCONNECTOR -QBD
K	-PFW	WHITE SIGNAL LAMPS	-RLE6	ELECTROMECHANICAL LOCK PREVENTING INSERTION OF LEVER FOR CLOSING OPERATION OF DISCONNECTOR -QBD1
	-PFX	CROSS INDICATORS, ELECTROMECHANICAL INDICATORS	-RLE7	ELECTROMECHANICAL LOCK PREVENTING INSERTION OF LEVER FOR CLOSING OPERATION OF DISCONNECTOR -QBD2
L	-PFY	YELLOW SIGNAL LAMPS	-RLE8	ELECTROMECHANICAL LOCK PREVENTING INSERTION OF LEVER FOR CLOSING OPERATION OF EARTHING SWITCH -QCE1 OR -QCE2
	-PGA	AMMETERS	-RLE9	ELECTROMECHANICAL LOCK PREVENTING OPERATION OF SWITCH-DISCONNECTOR -QBS
M	-PGC	COUNTERS	-RLE11	ELECTROMECHANICAL LOCK PREVENTING INSERTION OF LEVER FOR OPERATION OF DISCONNECTOR -QBD4
	-PGF	FREQUENCYMETERS	-RLE12	ELECTROMECHANICAL LOCK PREVENTING INSERTION OF LEVER FOR OPERATION OF DISCONNECTOR -QBD5
N	-PGH	HOURMETERS	-SFA	AMMETRIC SWITCHES
	-PGI	PROTECTION AND CONTROL UNIT: HUMAN MACHINE INTERFACE	-SFC	CONTROL SWITCHES, CLOSING PUSH-BUTTONS
O	-PGI1	HUMAN MACHINE INTERFACE OF ELECTRONIC CONTROLLED CIRCUIT-BREAKER (ON CIRCUIT-BREAKER)	-SFL	LOCKING CONTACTS
	-PGI2	HUMAN MACHINE INTERFACE FOR ELECTRONIC CONTROLLED CIRCUIT-BREAKER (ON SWITCHGEAR)	-SFO	OPENING PUSH-BUTTONS
P	-PGJ	ACTIVE ENERGY METERS	-SFR	RESET PUSH-BUTTONS
	-PGK	REACTIVE ENERGY METERS	-SFS	SELECTOR SWITCHES
Q	-PGM	MULTIFUNCTION INDICATORS	-SFT	TEST PUSH-BUTTONS
	-PGP	POWER-FACTOR METERS	-SFU	UNLOCKING PUSH-BUTTONS
R	-PGQ	VARMETERS	-SFV	VOLTMETRIC SWITCHES
	-PGS	SYNCHRONOSCOPES	-TA	POWER TRANSFORMERS
S	-PGV	VOLTMETERS	-TB	CONVERTER
	-PGW	WATTMETERS	-TB1	RECTIFIER FOR FIRST OPENING RELEASE
T	-PJ	ACOUSTICAL SIGNAL DEVICES (BELLS, SIRENS)	-TB2	RECTIFIER FOR SECOND OPENING RELEASE
	-QAB	CIRCUIT-BREAKERS	-TB3	RECTIFIER FOR CLOSING RELEASE
U	-QAC	CONTACTORS (FOR POWER)	-TB4	RECTIFIER FOR ELECTROMECHANICAL LOCK PREVENTING CIRCUIT-BREAKER CLOSING
	-QBD	DISCONNECTORS	-TB5	RECTIFIER FOR ELECTROMECHANICAL LOCK PREVENTING TRUCK RACKING-IN/OUT
V	-QBD1	FRONT BUSBAR DISCONNECTORS (DOUBLE BUSBAR SYSTEM)	-TB6	RECTIFIER FOR UNDERVOLTAGE RELEASE
	-QBD2	REAR BUSBAR DISCONNECTORS (DOUBLE BUSBAR SYSTEM)	-TB7	ERECTIFIER FOR INDIRECT OVERCURRENT RELEASE ON CIRCUIT-BREAKER
W	-QBD3	FEEDER DISCONNECTORS (DOUBLE BUSBAR SYSTEM)		
	-QBD4	TWO-WAY DISCONNECTOR		
X	-QBD5	TWO-WAY DISCONNECTOR ON BUSBAR RISER		


				Date Prep.	15.11.2018	PROJECT TITLE		ABB	EPMV	REFERENCE DESIGNATIONS MVD-01 20kV MAIN SUBSTATION	Scale		= H01
				Prepared	YR	MV Switchgear for MNA Serang Plant					Customer	PT Multimas Nabati Asahan	& 301
00	Issued for Approval	28.12.18	YR	Checked	AW			PT. ABB Sakti Industri		SCHEMATIC DIAGRAM	Drawing Nbr.	IDUNISEC-BE318042-301	Sh. 5
Ind.	Revision	Date	Name	Approved	AI	Based on: BE318042				WBC INCOMING	Customer Doc. Nbr.		Cont. 31

1	2	3	4	5	6	7	8
---	---	---	---	---	---	---	---


WE RESERVE ALL RIGHTS IN THIS DOCUMENT AND IN THE INFORMATION CONTAINED THEREIN. REPRODUCTION, USE OR DISCLOSURE TO THIRD PARTIES WITHOUT EXPRESS AUTHORITY IS STRICTLY FORBIDDEN.

A	-TFA	ACTIVE POWER TRANSDUCERS	A
	-TFC	CURRENT TRANSDUCERS	
	-TFF	FREQUENCY TRANSDUCERS	
	-TFJ	ACTIVE ENERGY TRANSDUCERS	
	-TFK	REACTIVE ENERGY TRANSDUCERS	
	-TFM	MULTIFUNCTION TRANSDUCERS	
	-TFP	POWER-FACTOR TRANSDUCERS	
	-TFQ	REACTIVE POWER TRANSDUCERS	
	-TFS	SIGNAL CONVERTERS	
	-TFV	VOLTAGE TRANSDUCERS	
B	-WA	BUSBARS	B
	-WBC	POWER CABLES	
	-WE	EARTHING CABLES FOR L.V. INSTRUMENT COMPARTMENT.	
	-WGC	CONTROL CABLES	
	-WGS	COMMUNICATION CABLES (SHIELDED TWISTED PAIRS)	
	-WH	OPTICAL FIBRES	
	-XDA	TERMINAL BLOCK FOR CIRCUITS OF CURRENT TRANSFORMERS	
	-XDA1	CONNECTOR FOR CIRCUITS OF CURRENT TRANSFORMERS LOCATED ON PHASE L1	
	-XDA2	CONNECTOR FOR CIRCUITS OF CURRENT TRANSFORMERS LOCATED ON PHASE L2	
	-XDA3	CONNECTOR FOR CIRCUITS OF CURRENT TRANSFORMERS LOCATED ON PHASE L3	
C	-XDA5	CONNECTOR FOR CIRCUITS OF NEUTRAL (RESIDUAL) CURRENT TRANSFORMER	C
	-XDB	CONNECTOR FOR ISOLATION OF CIRCUIT-BREAKER (OR UPPER VOLTAGE TRANSFORMER TRUCK) AUXILIARY CIRCUITS	
	-XDB1	CONNECTOR FOR AUXILIARY CIRCUITS OF CIRCUIT-BREAKER (OR UPPER VOLTAGE TRANSFORMER TRUCK)	
	-XDB2	CONNECTOR FOR ADDITIONAL AUXILIARY CIRCUITS OF CIRCUIT-BREAKER	
	-XDB10...-XDB89	CONNECTOR FOR CIRCUIT-BREAKER INTERNAL CIRCUITS	
	-XDB7	CONNECTOR FOR TRUCK POSITION CONTACTS	
	-XDB91	CONNECTOR FOR OPENING RELEASE CIRCUITS OF SWITCH-DISCONNECTOR	
	-XDB92	CONNECTOR FOR CLOSING RELEASE CIRCUITS OF SWITCH-DISCONNECTOR	
	-XDB93	CONNECTOR FOR POSITION SWITCHES OF SWITCH-DISCONNECTOR	
	-XDB95	CONNECTOR FOR CIRCUITS OF EARTHING SWITCH LOCKING MAGNET	
D	-XDC	CUSTOMER TERMINAL BLOCK	D
	-XDC1	CUSTOMER TERMINAL BLOCK FOR AUXILIARY CIRCUITS OF CIRCUIT BREAKER	
	-XDC2	CUSTOMER TERMINAL BLOCK FOR AUXILIARY CIRCUITS OF SWITCH-DISCONNECTOR	
	-XDC3	CUSTOMER TERMINAL BLOCK FOR AUXILIARY CIRCUITS OF PROTECTION RELAY AND MULTIFUNCTION UNIT	
	-XDC4	CUSTOMER TERMINAL BLOCK FOR AUXILIARY CIRCUITS OF VOLTAGE TRANSFORMERS	
	-XDC5	CUSTOMER TERMINAL BLOCK FOR AUXILIARY CIRCUITS OF MINIATURE CIRCUIT BREAKER	
	-XDE	TERMINAL BLOCK FOR AUXILIARY CIRCUITS OF EARTHING SWITCH -QCE	
	-XDE1	TERMINAL BLOCK FOR INTERNAL CIRCUITS OF EARTHING SWITCH -QCE	
	-XDE2	TERMINAL BLOCK FOR AUXILIARY CIRCUITS OF EARTHING SWITCH -QCE1 OR -QCE2	
	-XDE3	TERMINAL BLOCK FOR INTERNAL CIRCUITS OF EARTHING SWITCH -QCE1 OR -QCE2	
E	-XDF	TERMINAL BLOCK FOR AUXILIARY CIRCUITS OF FORCED COOLING VENTILATORS	E
	-XDF1	CONNECTOR FOR ISOLATION OF CIRCUITS OF FRONT VENTILATOR	
	-XDF2	CONNECTOR FOR REAR VENTILATOR CIRCUITS	
	-XDF3	CONNECTOR FOR FRONT VENTILATOR CIRCUITS	
	-XDH	TERMINAL BLOCK FOR VARIOUS CIRCUITS (HEATERS, POSITION SWITCHES DETECTING INTERNAL ARCING, ETC.)	
	-XDI	TERMINAL BLOCK FOR INTERCONNECTION (CONNECTION BETWEEN PANELS)	

				Date Prep.	15.11.2018	PROJECT TITLE MV Switchgear for MNA Serang Plant	ABB	EPMV	DISTRIBUTION OF AUXILIARY CIRCUITS MVD-01 20kV MAIN SUBSTATION SCHEMATIC DIAGRAM WBC INCOMING	Scale		= H01
				Prepared	YR					Customer	PT Multimas Nabati Asahan	& 301
00	Issued for Approval	28.12.18	YR	Checked	AW		Drawing Nbr.	IDUNISEC-BE318042-301		Sh. 7		
Ind.	Revision	Date	Name	Approved	AI	Based on:	BE318042	Customer Doc. Nbr.			Cont. 31	
						PT. ABB Sakti Industri						

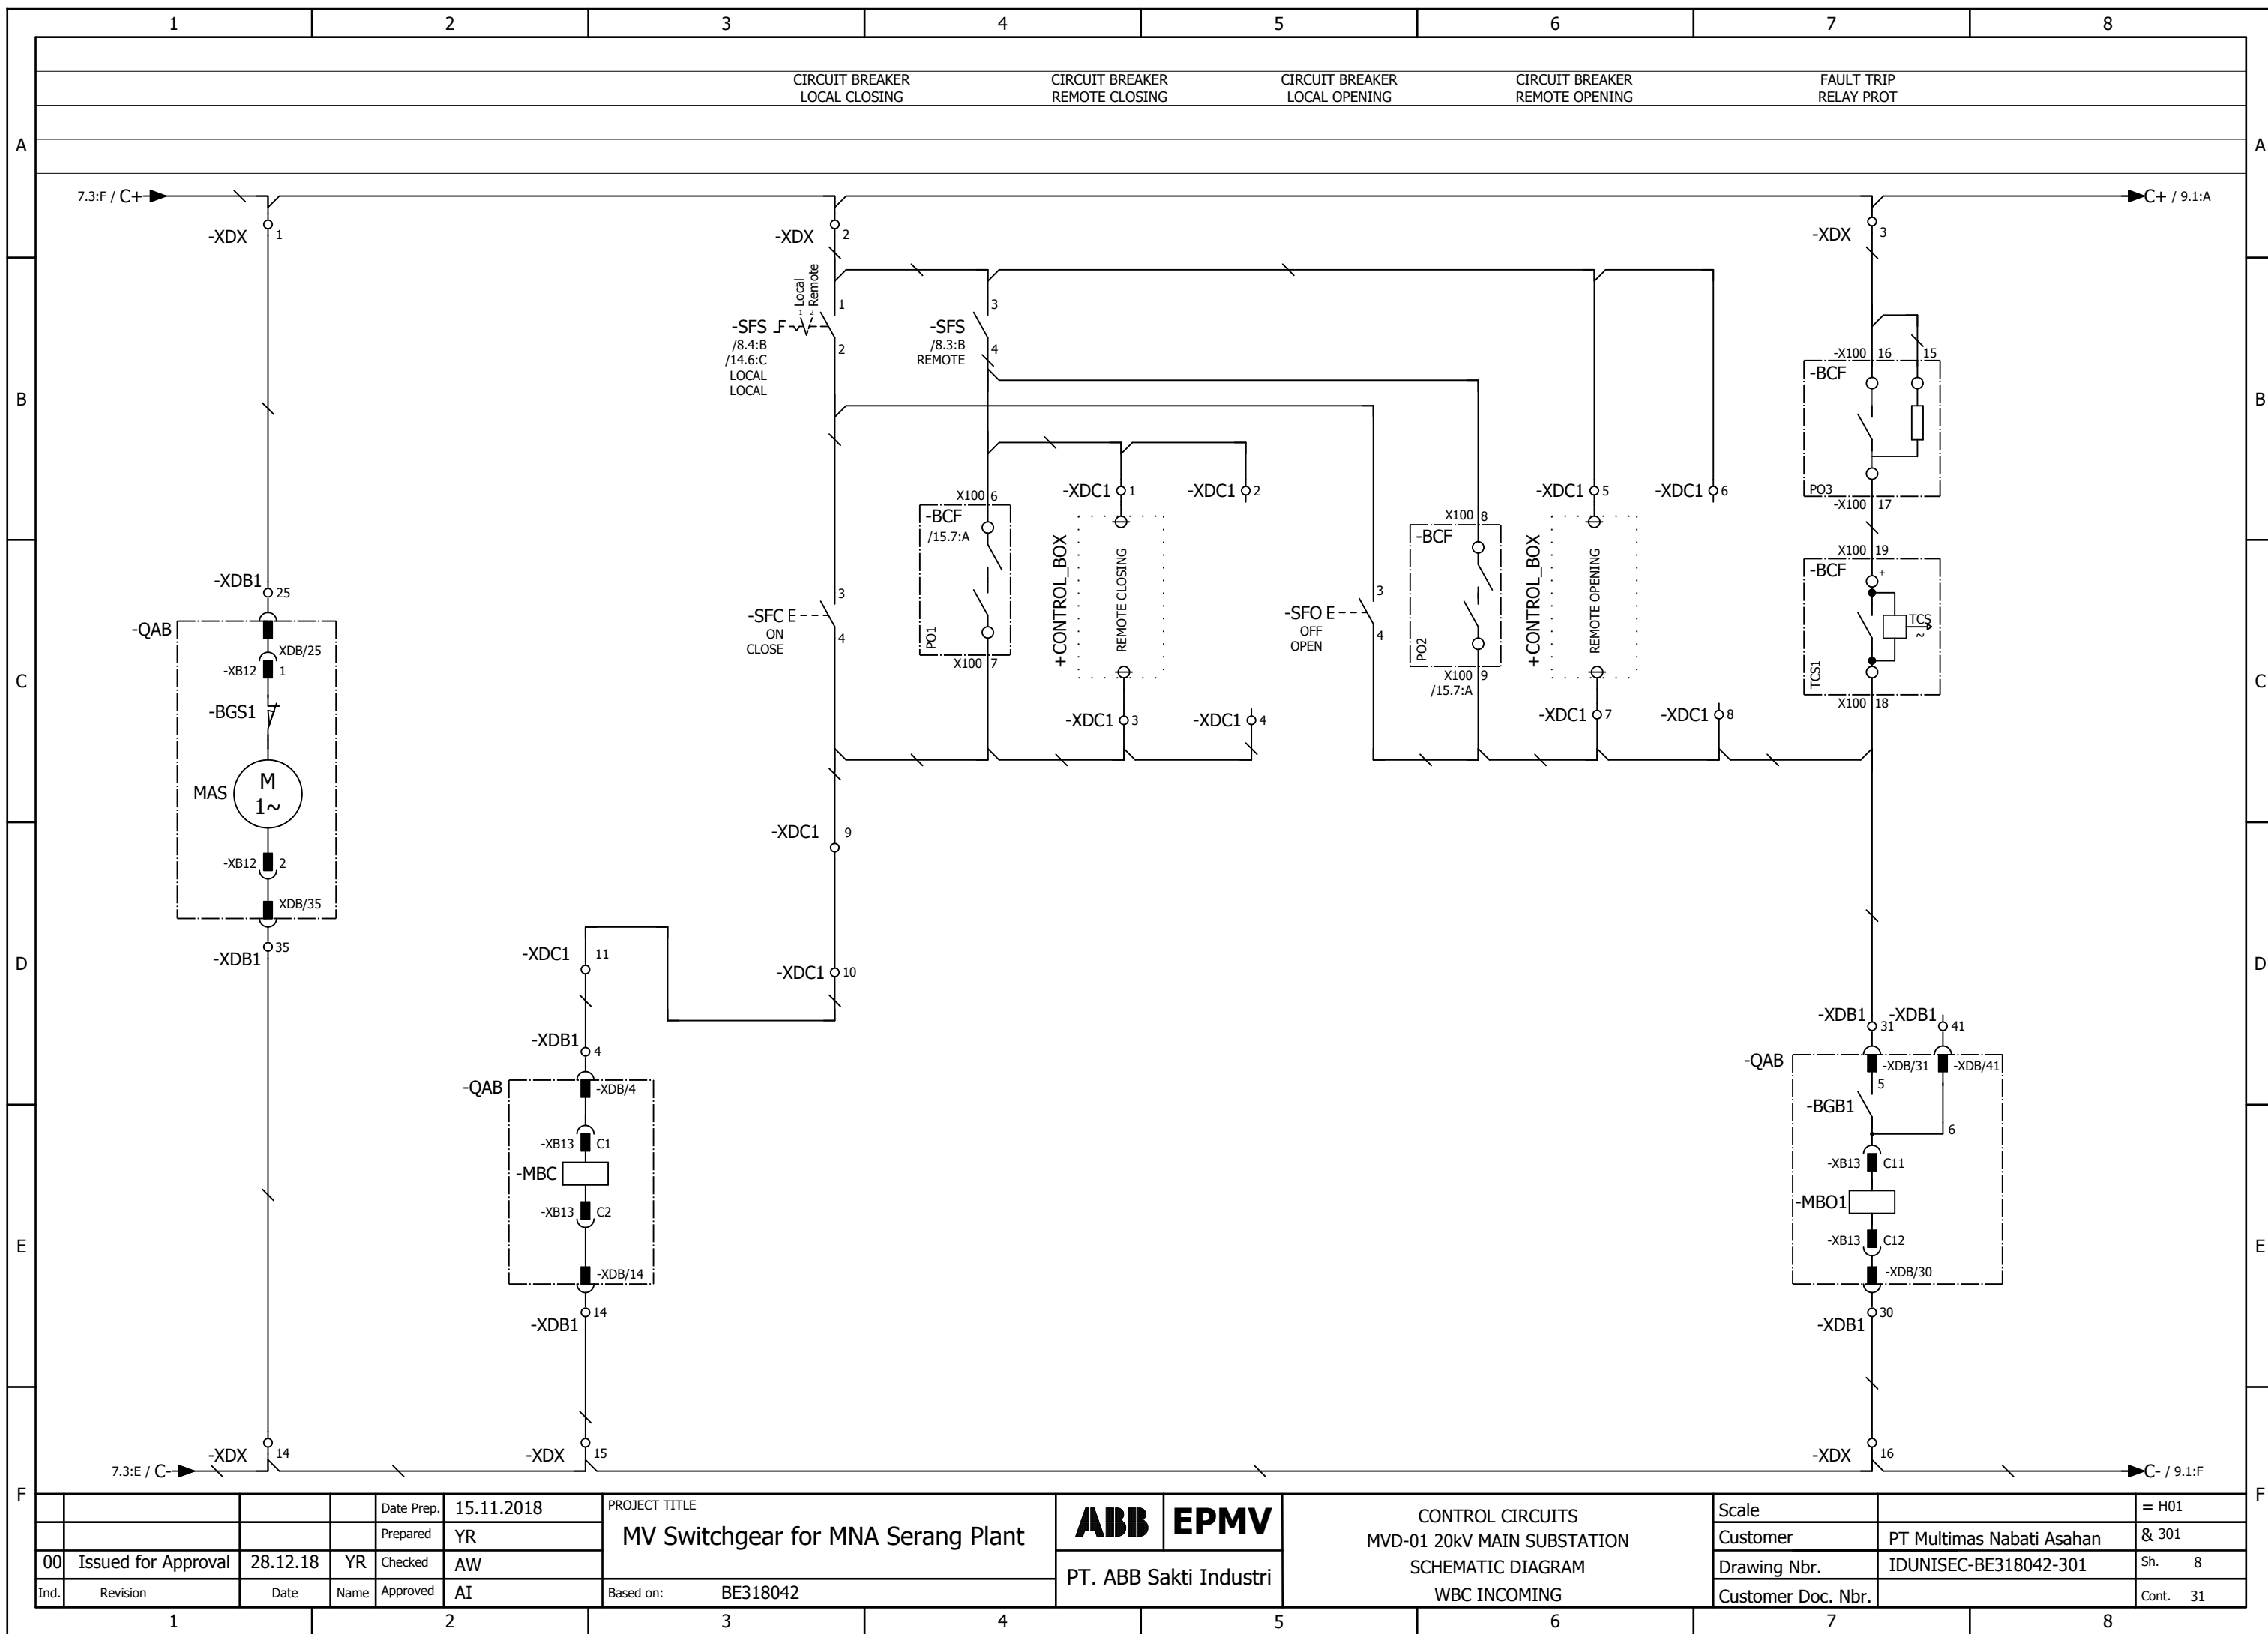


WE RESERVE ALL RIGHTS IN THIS DOCUMENT AND IN THE INFORMATION CONTAINED THEREIN. REPRODUCTION, USE OR DISCLOSURE TO THIRD PARTIES WITHOUT EXPRESS AUTHORITY IS STRICTLY FORBIDDEN.

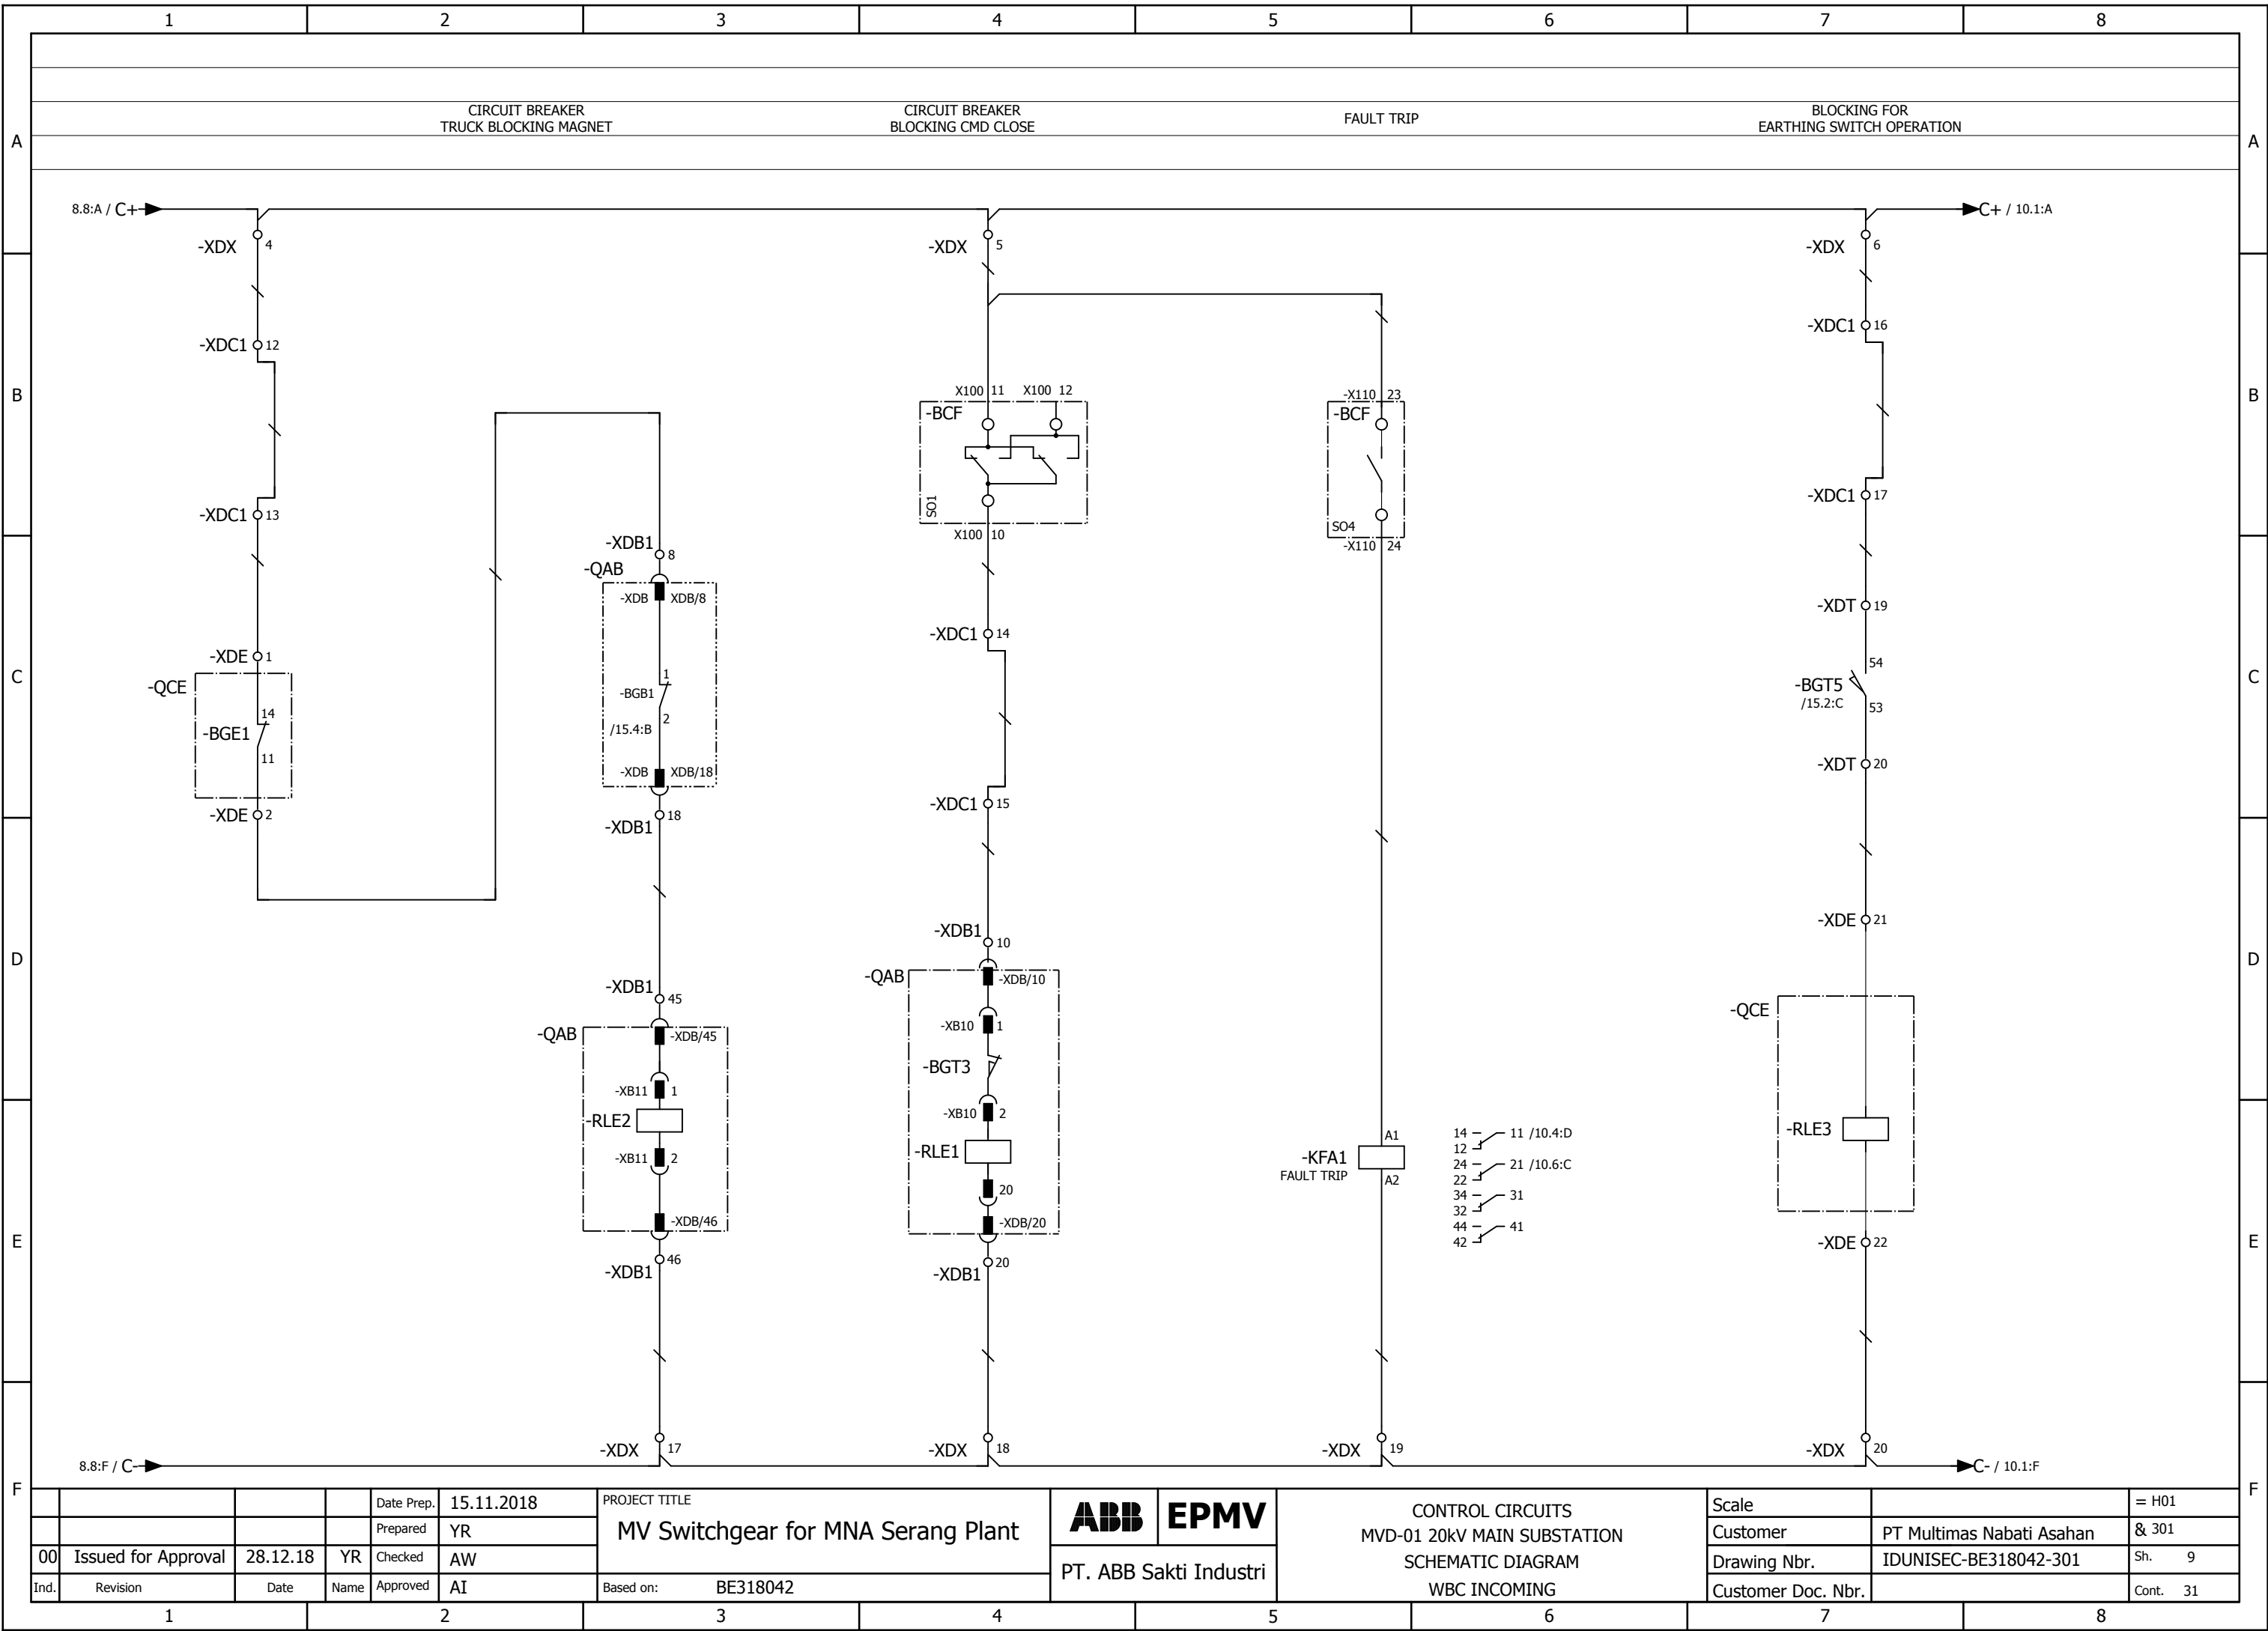


				Date Prep.	15.11.2018	PROJECT TITLE MV Switchgear for MNA Serang Plant	ABB	EPMV	CONTROL CIRCUITS MVD-01 20kV MAIN SUBSTATION SCHEMATIC DIAGRAM WBC INCOMING	Scale		= H01
				Prepared	YR					Customer	PT Multimas Nabati Asahan	& 301
00	Issued for Approval	28.12.18	YR	Checked	AW		Drawing Nbr.	IDUNISEC-BE318042-301		Sh. 9		
Ind.	Revision	Date	Name	Approved	AI	Based on:	BE318042	PT. ABB Sakti Industri		Customer Doc. Nbr.		Cont. 31

WE RESERVE ALL RIGHTS IN THIS DOCUMENT AND IN THE INFORMATION CONTAINED THEREIN. REPRODUCTION, USE OR DISCLOSURE TO THIRD PARTIES WITHOUT EXPRESS AUTHORITY IS STRICTLY FORBIDDEN.

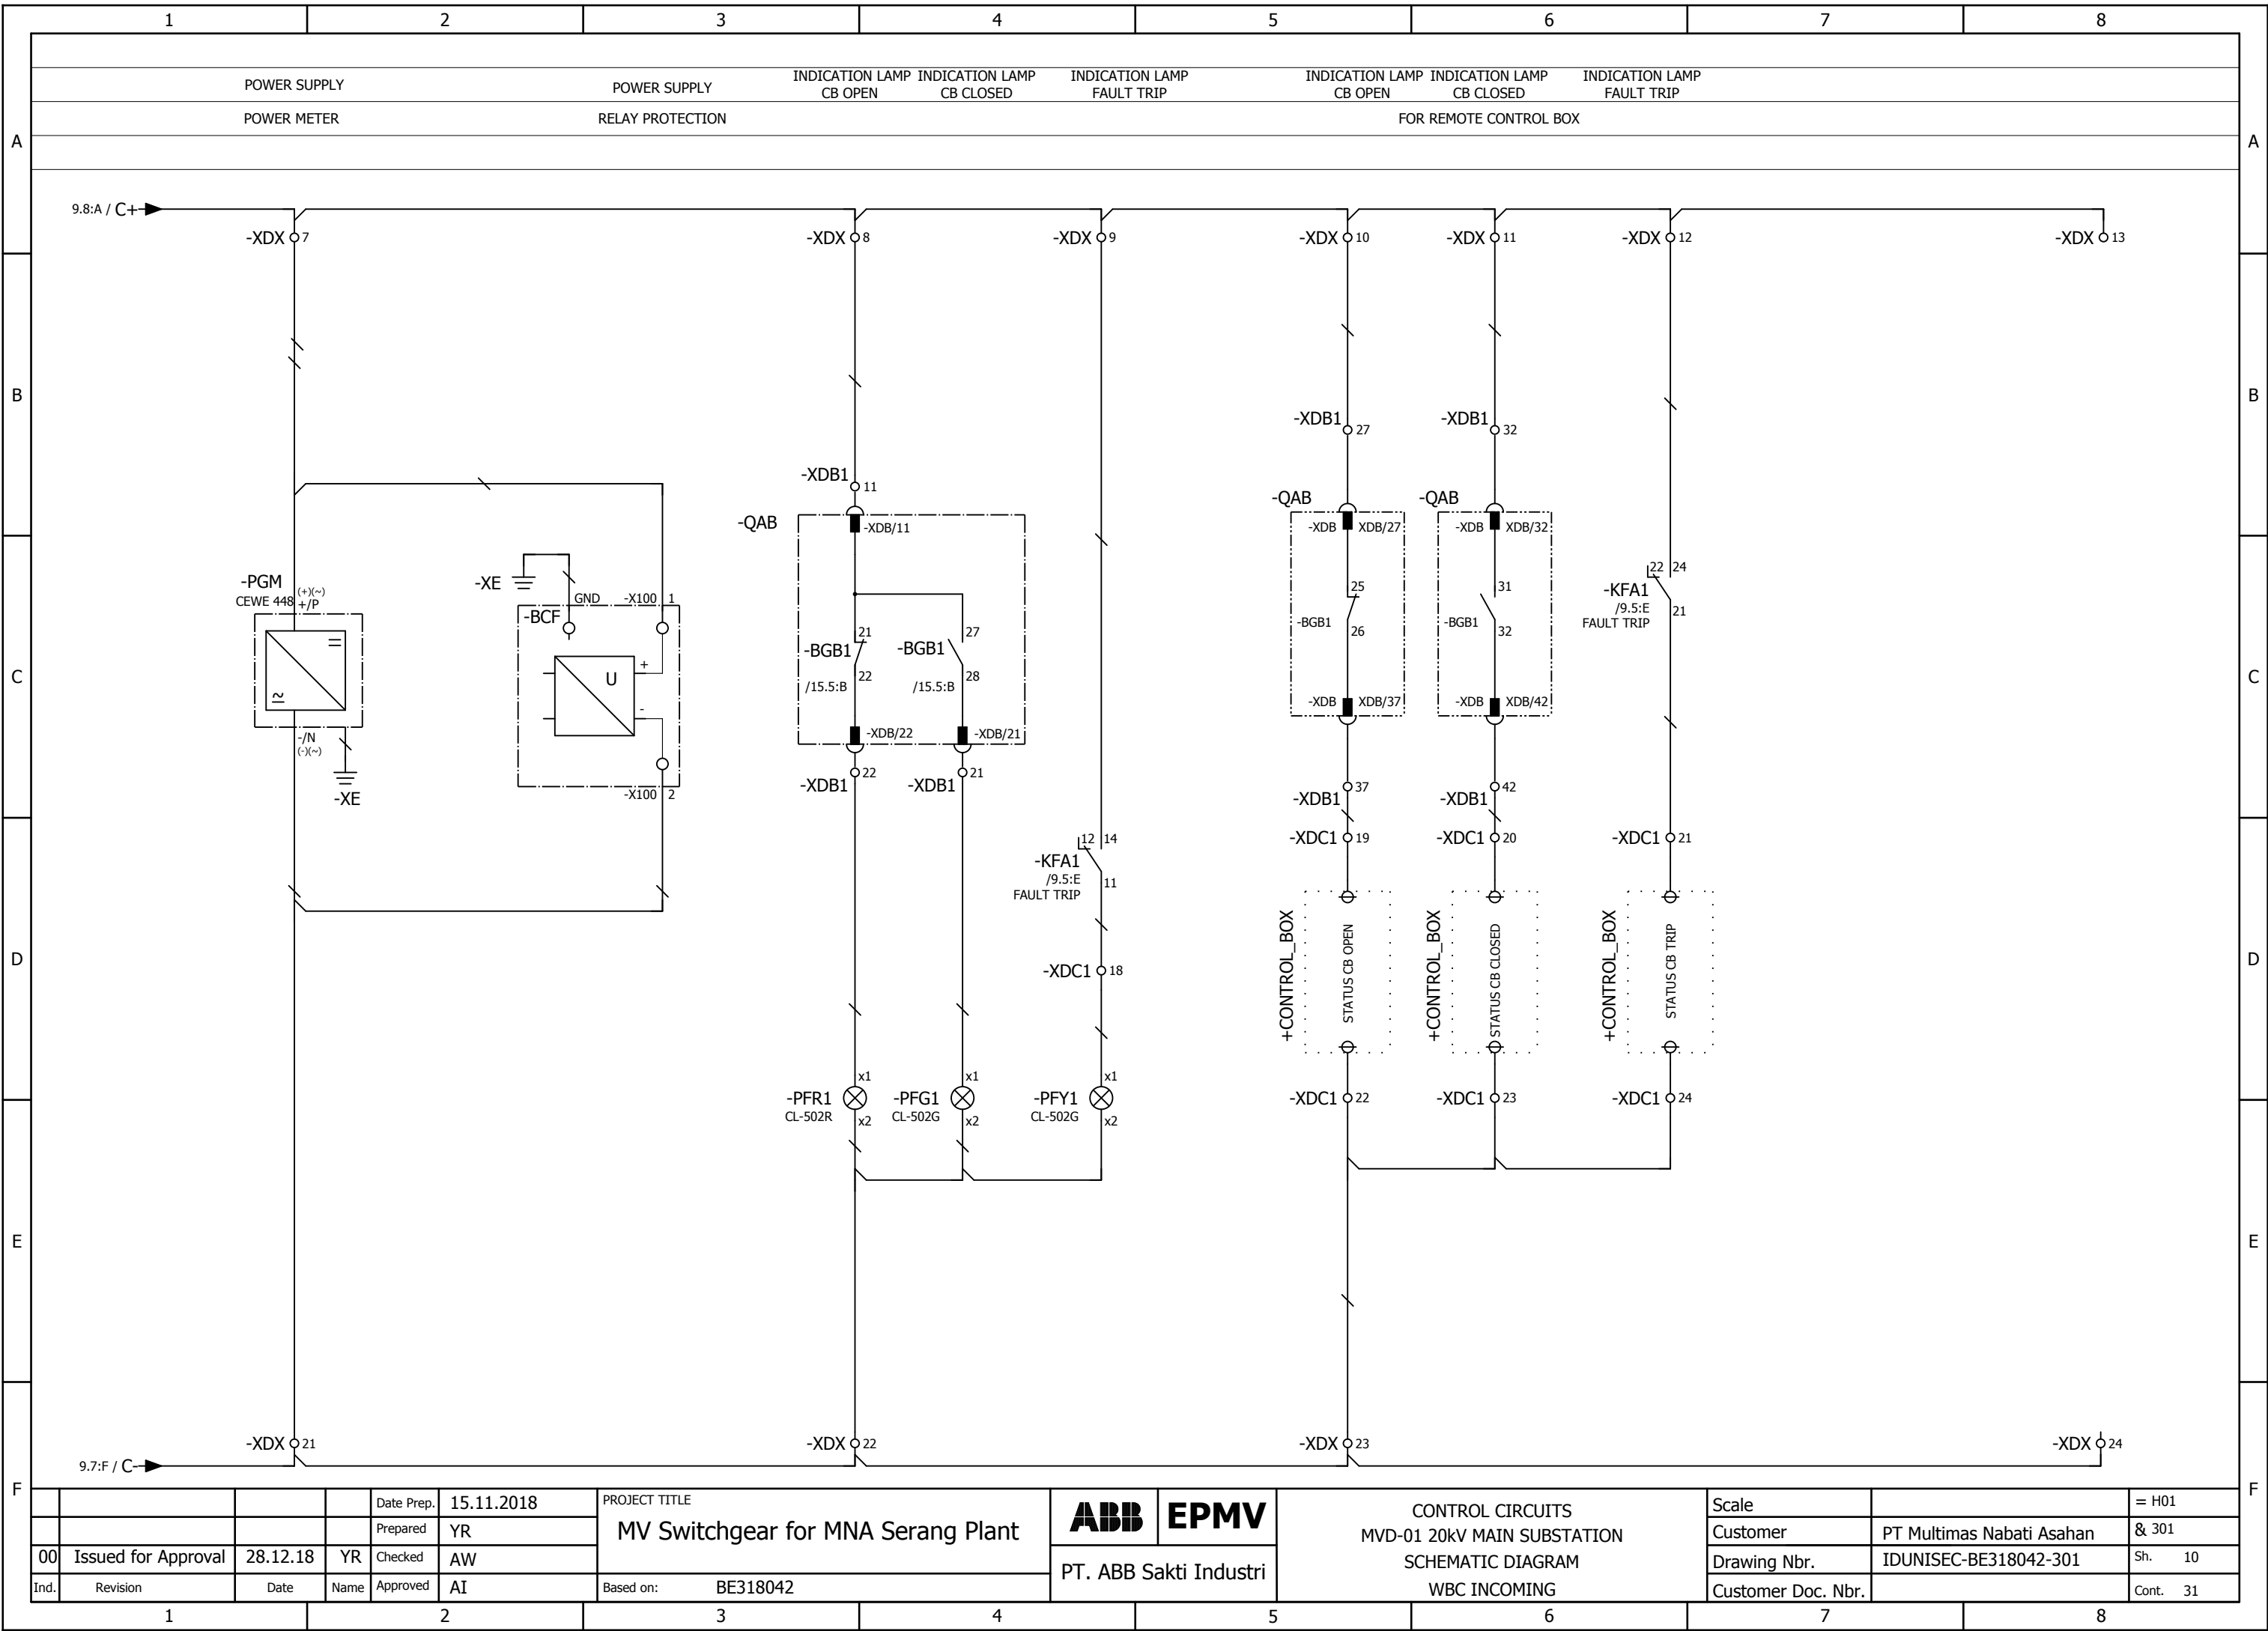

WE RESERVE ALL RIGHTS IN THIS DOCUMENT AND IN THE INFORMATION CONTAINED THEREIN. REPRODUCTION, USE OR DISCLOSURE TO THIRD PARTIES WITHOUT EXPRESS AUTHORITY IS STRICTLY FORBIDDEN.

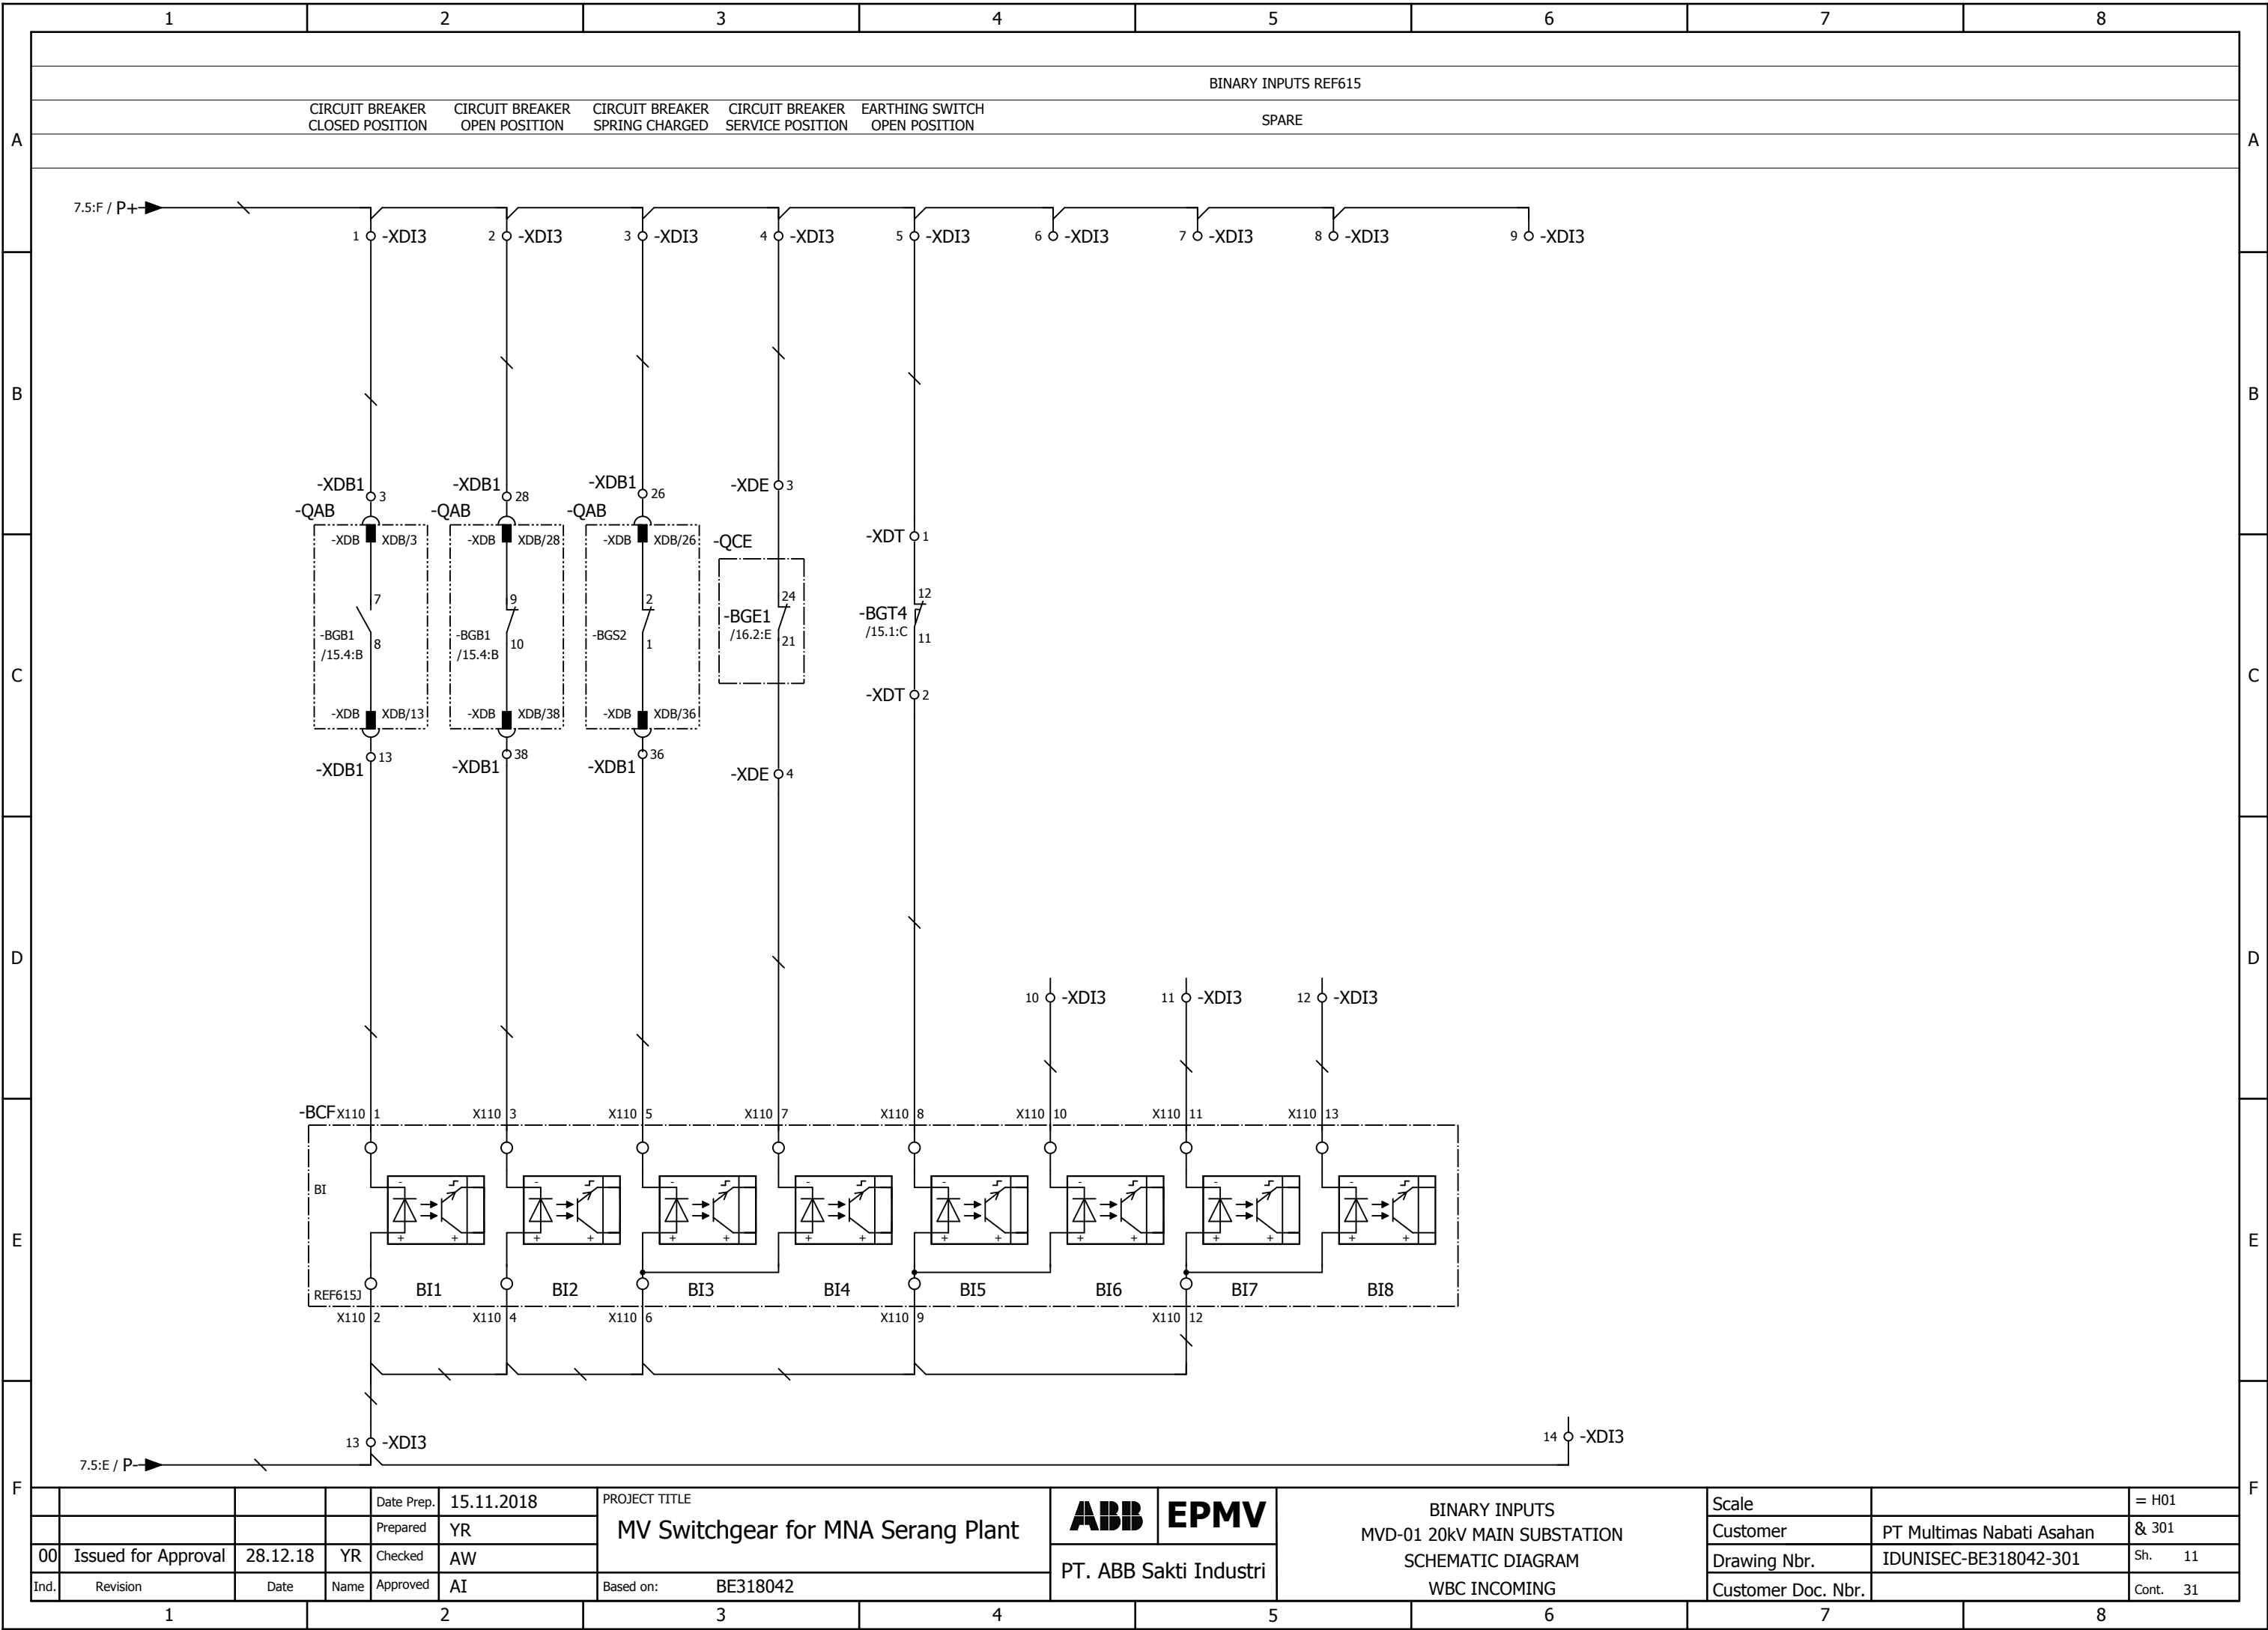


				Date Prep.	15.11.2018
				Prepared	YR
00	Issued for Approval	28.12.18	YR	Checked	AW
Ind.	Revision	Date	Name	Approved	AI

PROJECT TITLE	
MV Switchgear for MNA Serang Plant	
Based on:	BE318042


ABB	EPMV
PT. ABB Sakti Industri	

BINARY INPUTS	
MVD-01 20kV MAIN SUBSTATION	
SCHEMATIC DIAGRAM	
WBC INCOMING	

Scale		= H01
Customer	PT Multimas Nabati Asahan	& 301
Drawing Nbr.	IDUNISEC-BE318042-301	Sh. 11
Customer Doc. Nbr.		Cont. 31

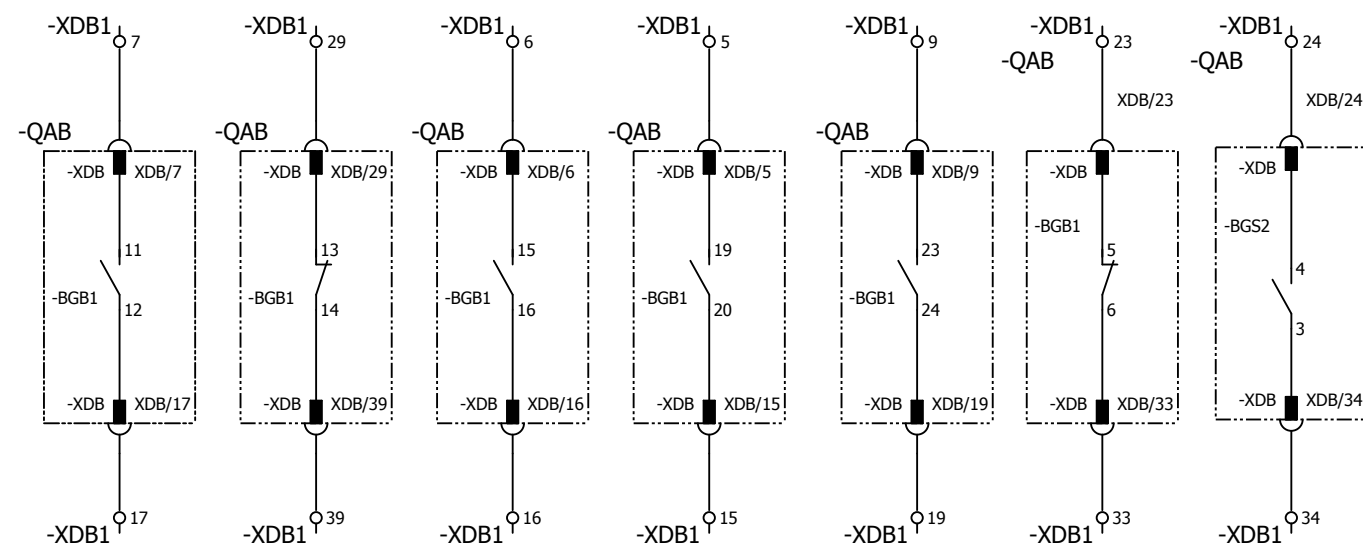


				Date Prep.	15.11.2018	PROJECT TITLE MV Switchgear for MNA Serang Plant	ABB	EPMV	AVAILABLE CONTACTS MVD-01 20kV MAIN SUBSTATION SCHEMATIC DIAGRAM WBC INCOMING	Scale		= H01
				Prepared	YR					Customer	PT Multimas Nabati Asahan	& 301
00	Issued for Approval	28.12.18	YR	Checked	AW					Drawing Nbr.	IDUNISEC-BE318042-301	Sh. 12
Ind.	Revision	Date	Name	Approved	AI	Based on: BE318042	PT. ABB Sakti Industri		Customer Doc. Nbr.		Cont. 31	

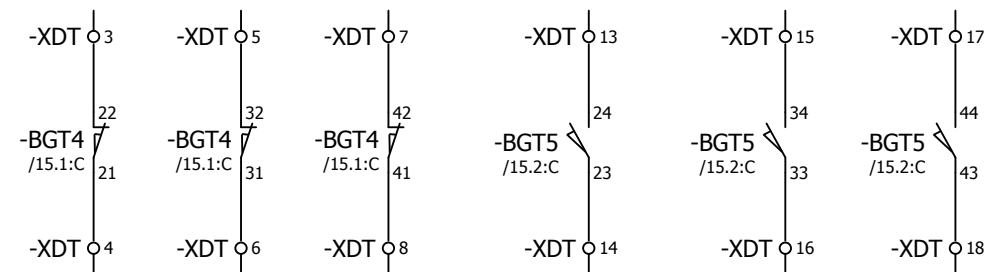



				Date Prep.	15.11.2018	PROJECT TITLE MV Switchgear for MNA Serang Plant	ABB	EPMV	AVAILABLE CONTACTS MVD-01 20kV MAIN SUBSTATION SCHEMATIC DIAGRAM WBC INCOMING	Scale		= H01	
				Prepared	YR					PT. ABB Sakti Industri	Customer	PT Multimas Nabati Asahan	& 301
00	Issued for Approval	28.12.18	YR	Checked	AW						Drawing Nbr.	IDUNISEC-BE318042-301	Sh. 13
Ind.	Revision	Date	Name	Approved	AI	Based on:	BE318042	Customer Doc. Nbr.			Cont. 31		

WE RESERVE ALL RIGHTS IN THIS DOCUMENT AND IN THE INFORMATION CONTAINED THEREIN. REPRODUCTION, USE OR DISCLOSURE TO THIRD PARTIES WITHOUT EXPRESS AUTHORITY IS STRICTLY FORBIDDEN.

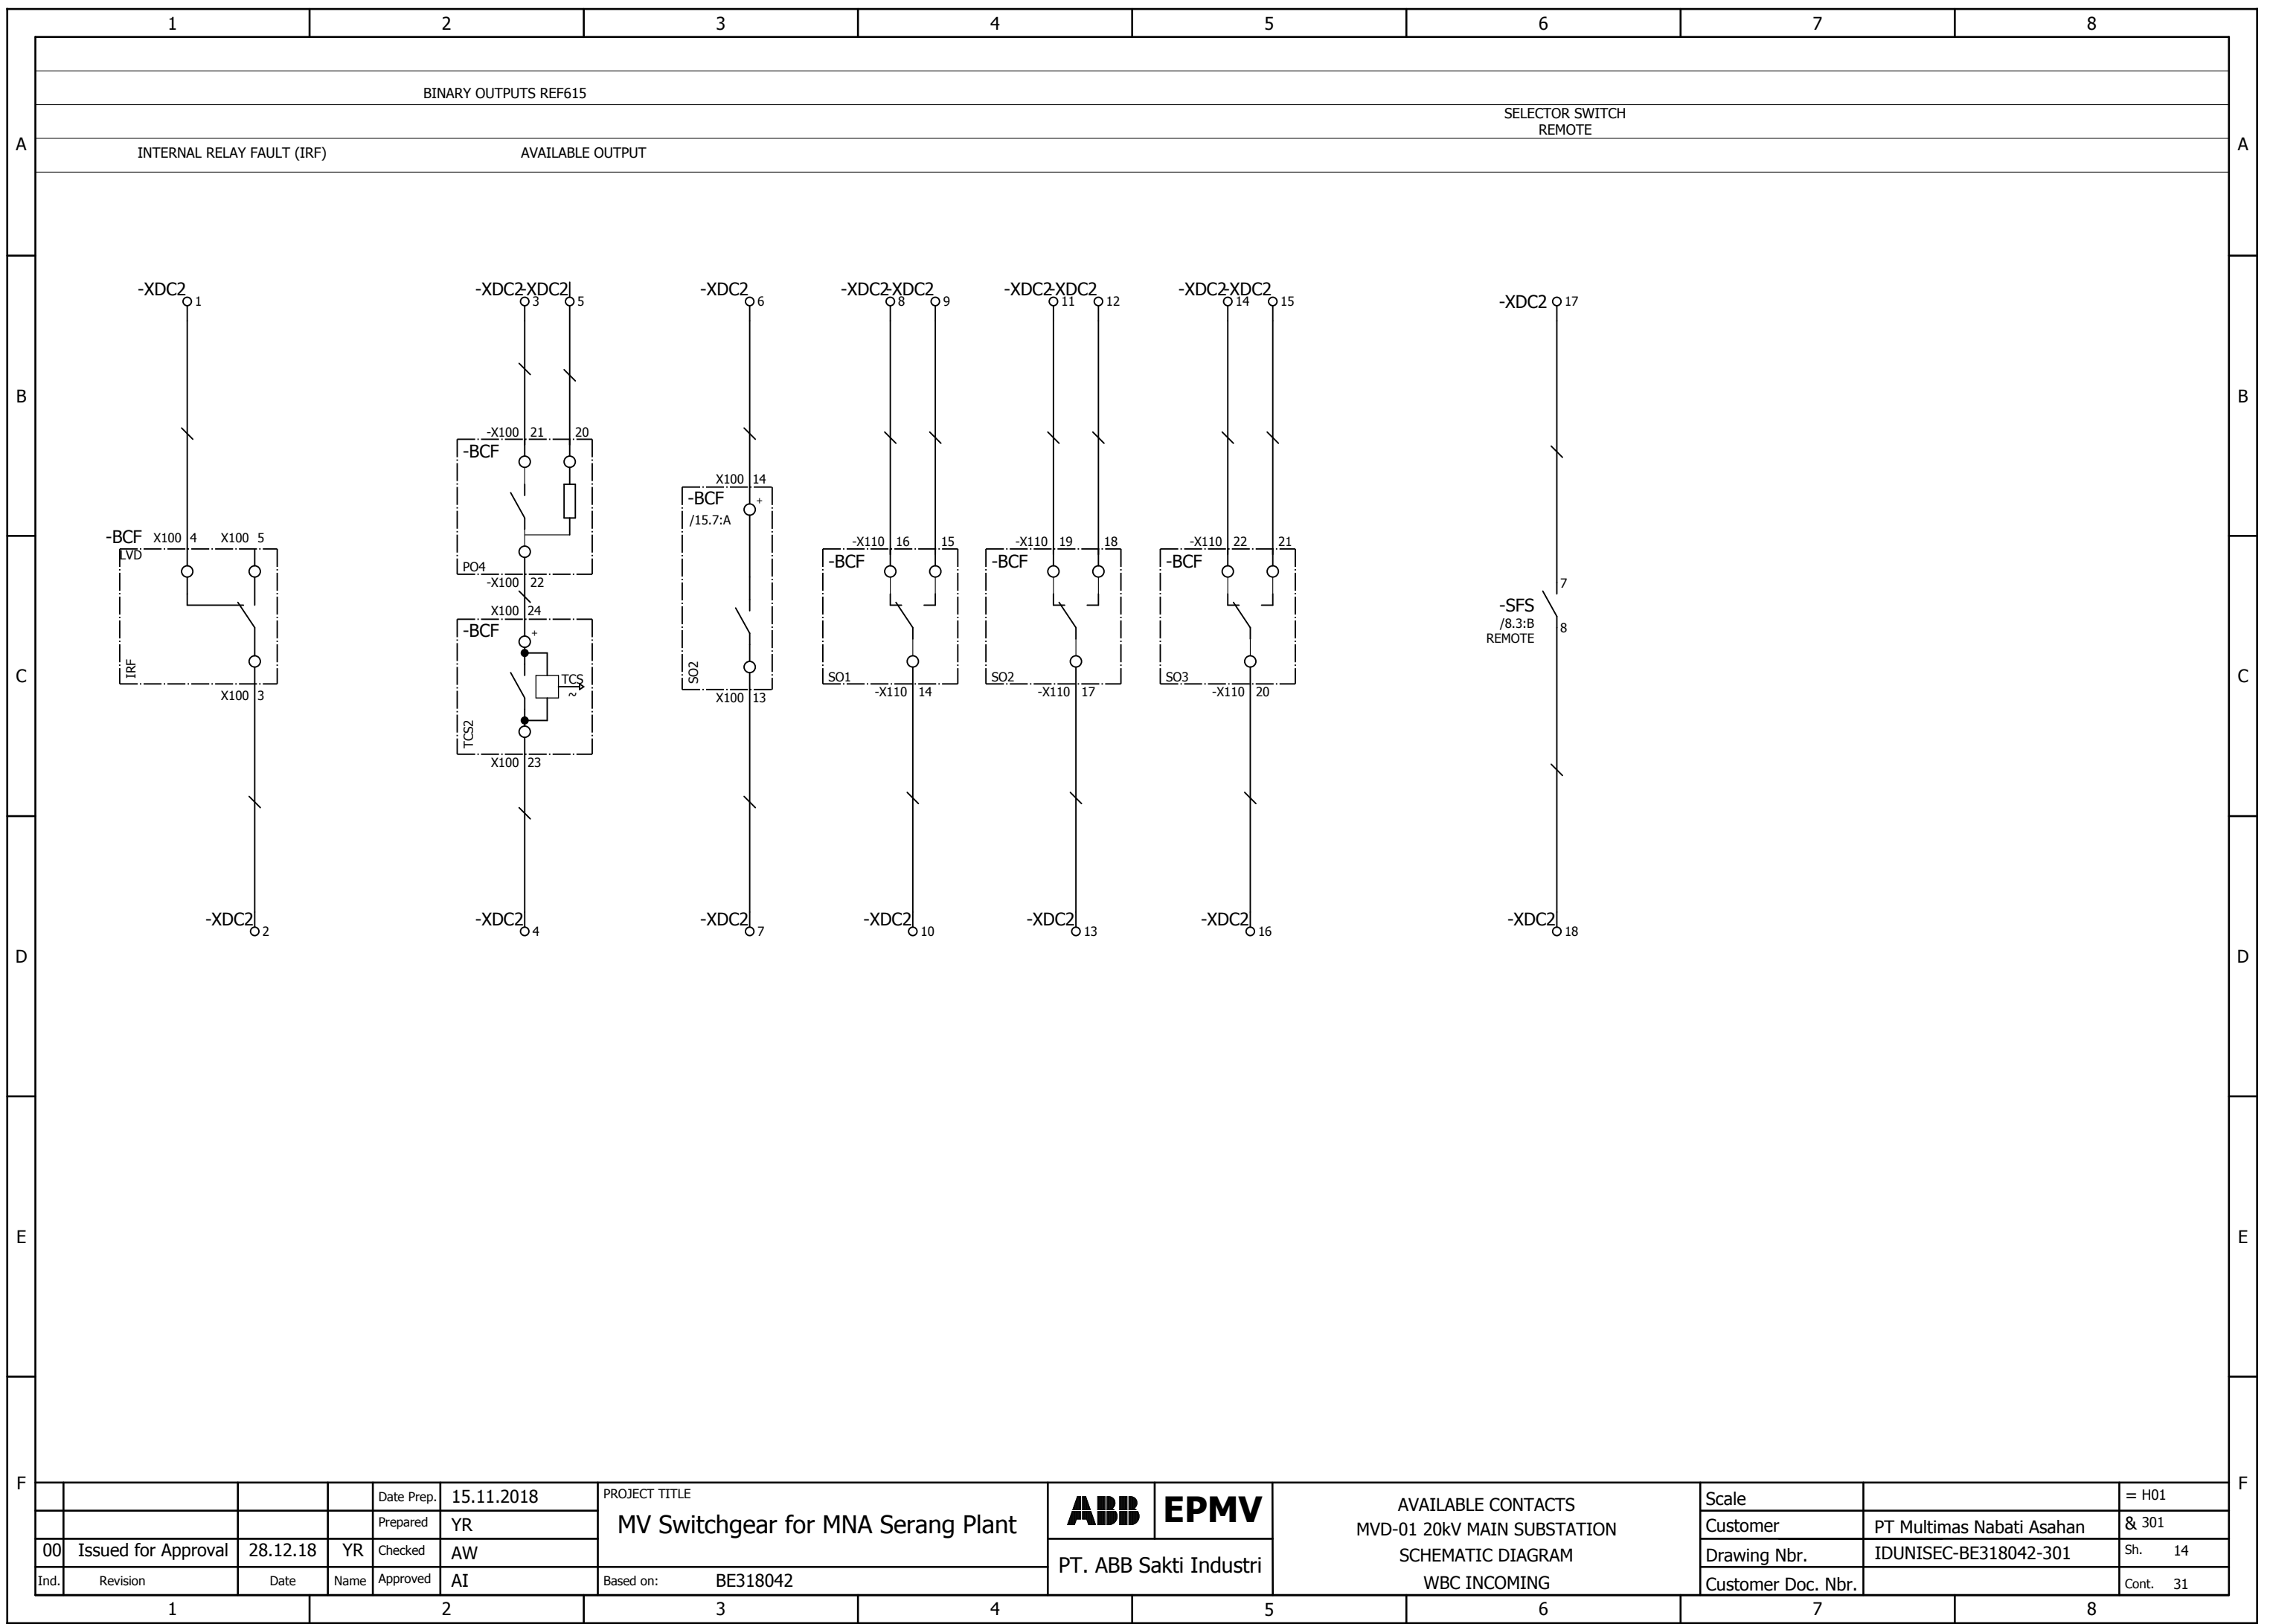


WE RESERVE ALL RIGHTS IN THIS DOCUMENT AND IN THE INFORMATION CONTAINED THEREIN. REPRODUCTION, USE OR DISCLOSURE TO THIRD PARTIES WITHOUT EXPRESS AUTHORITY IS STRICTLY FORBIDDEN.

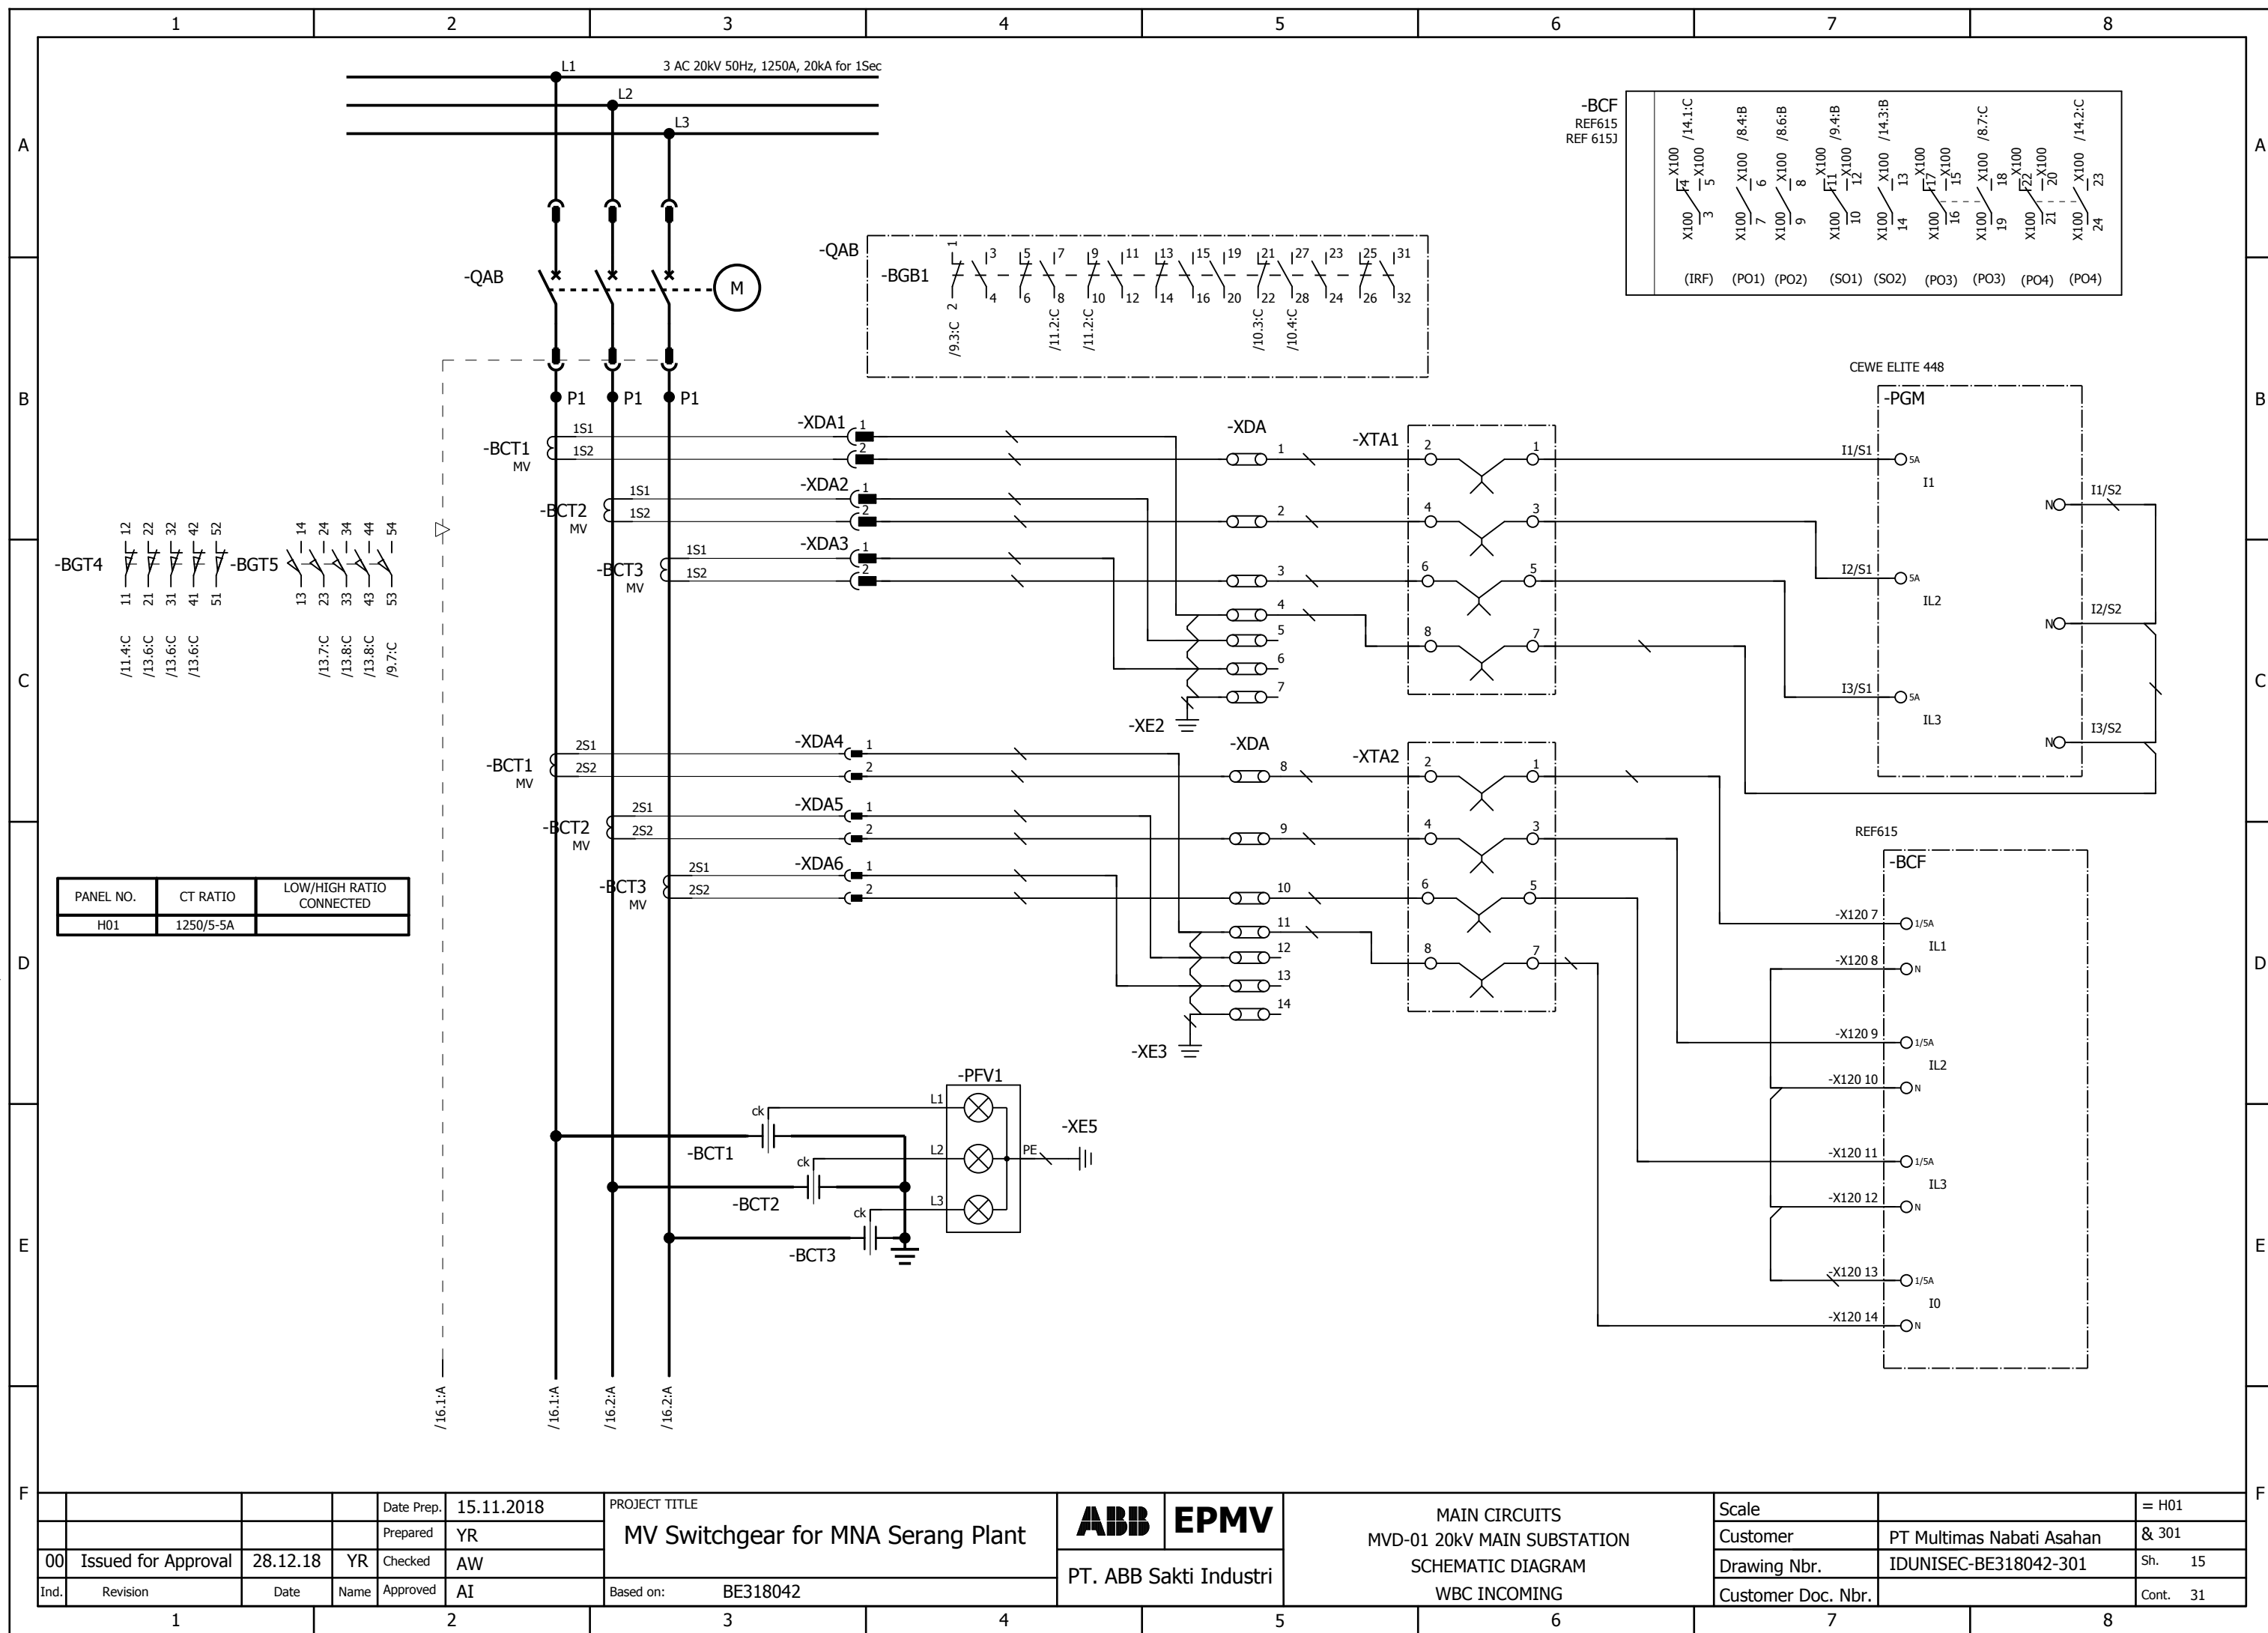

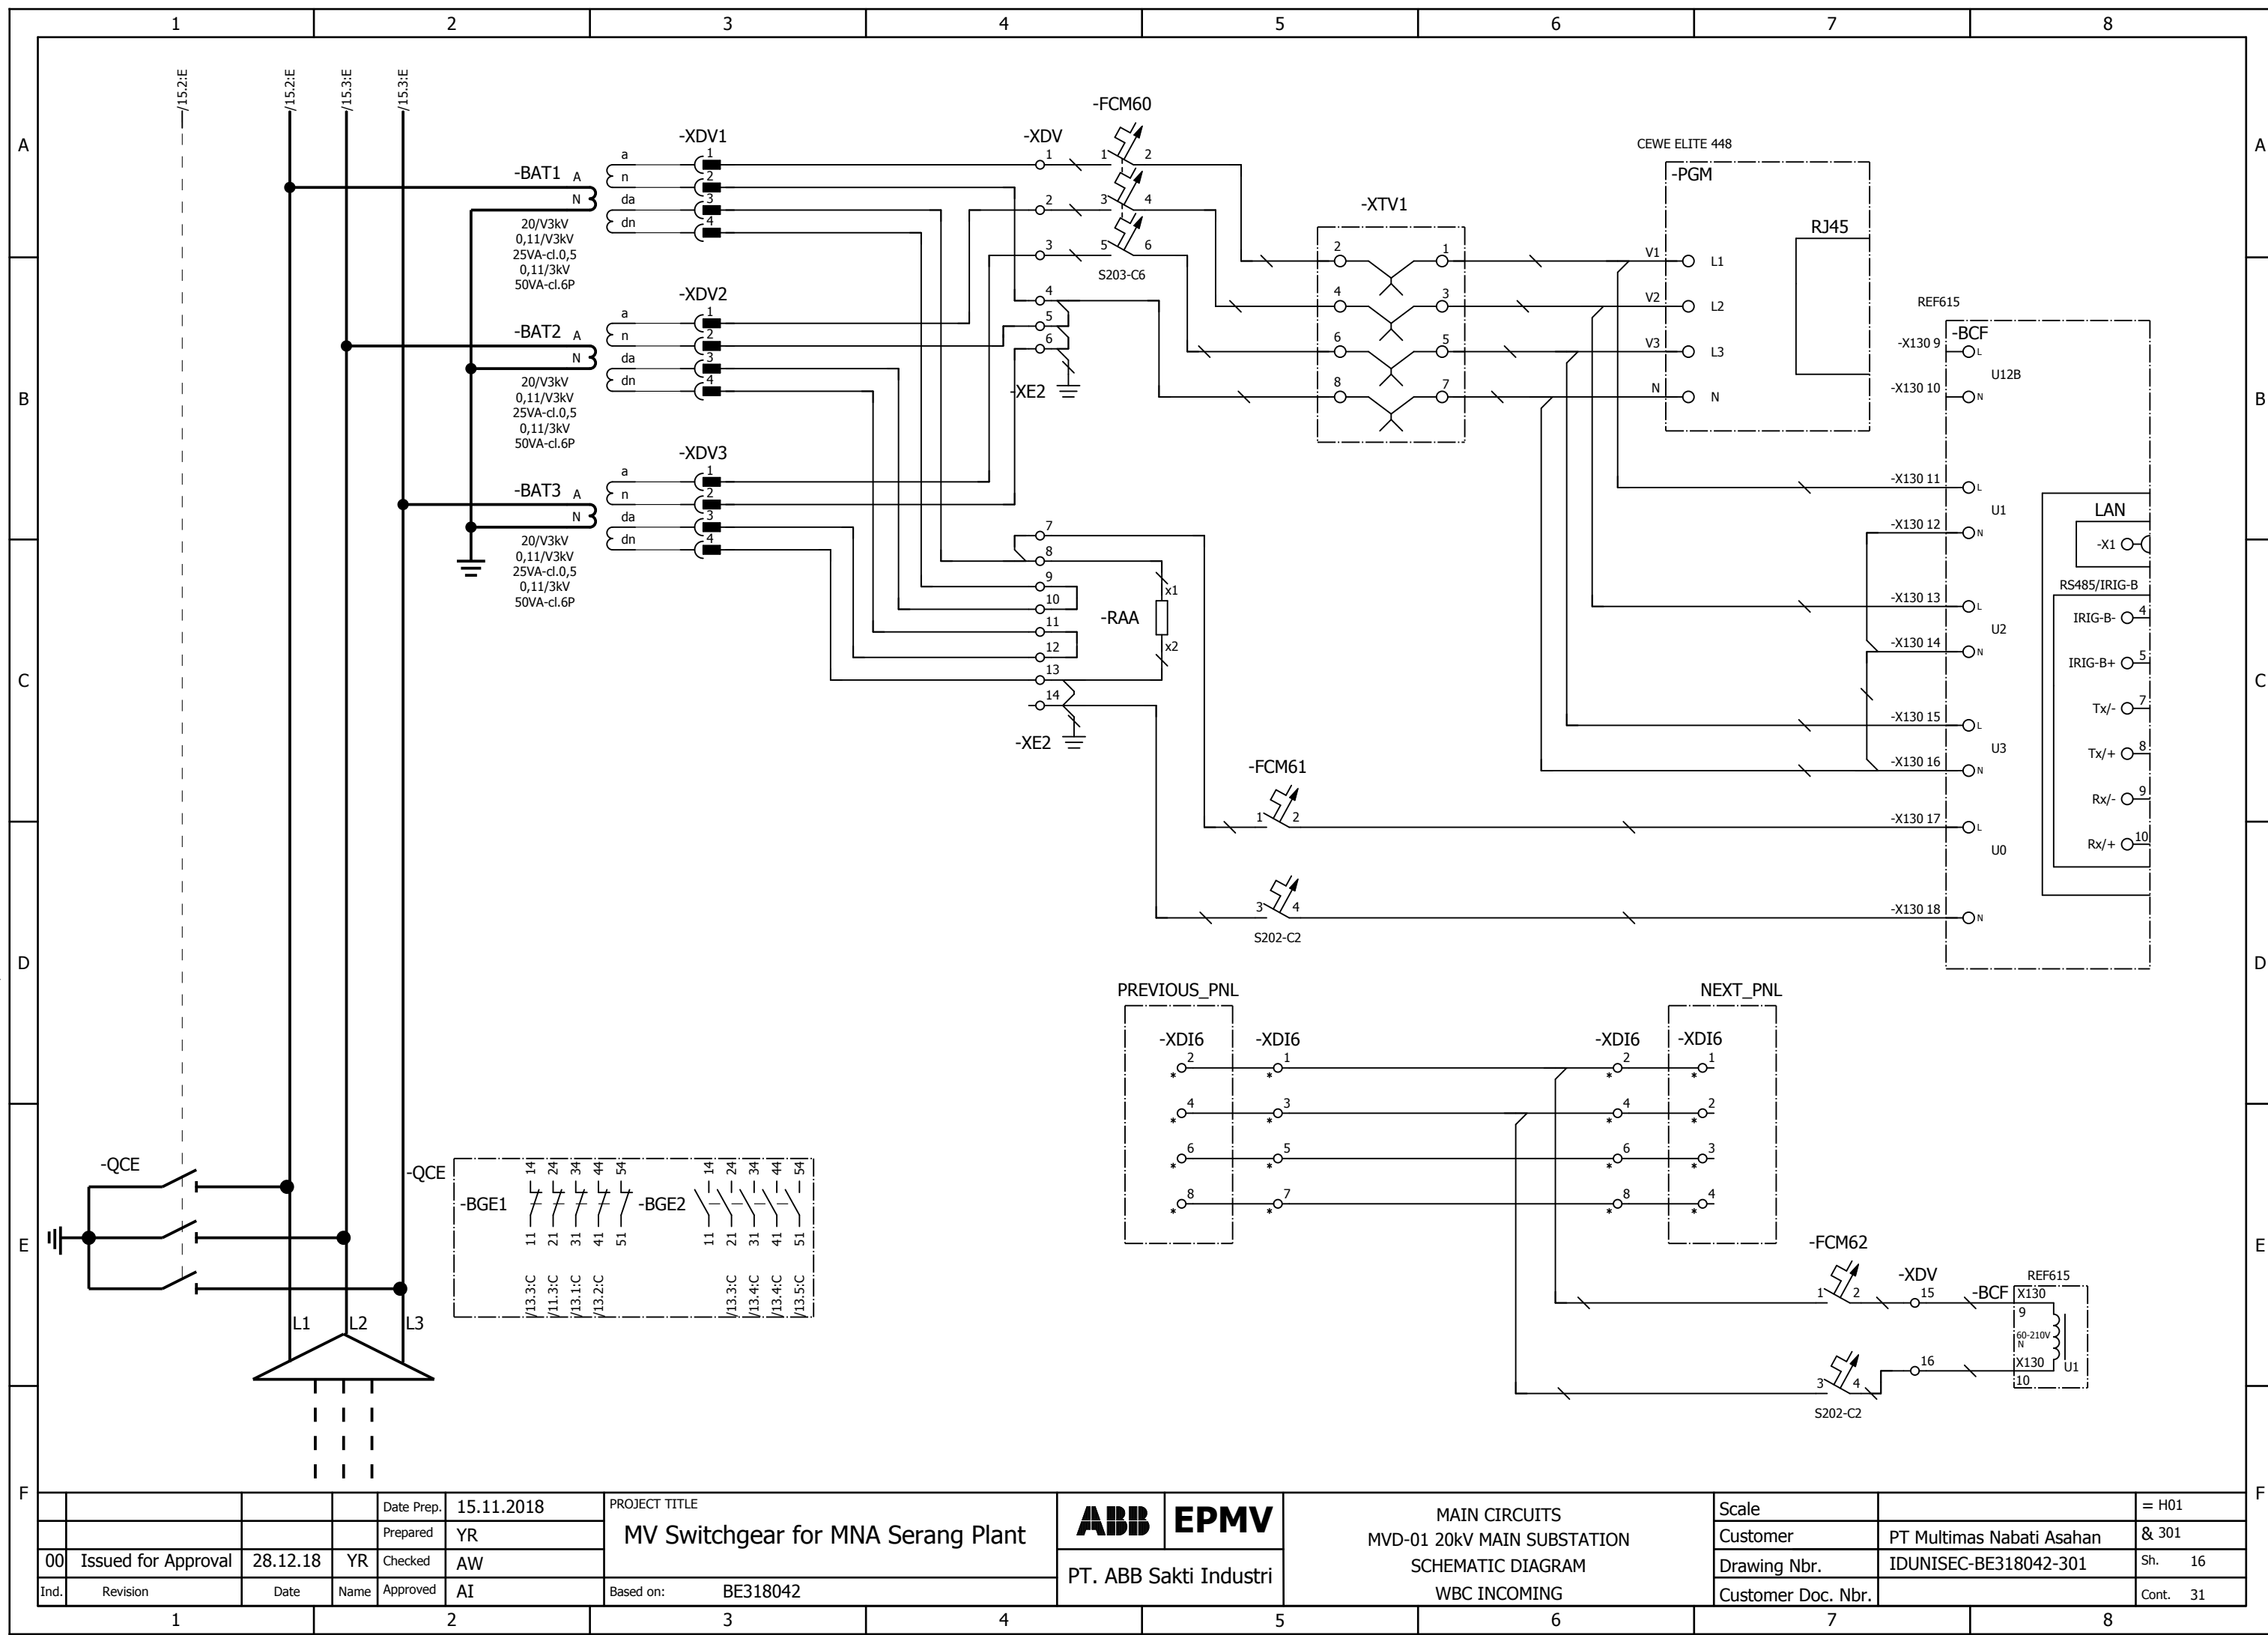

No.	EQUIPMENT DESCRIPTION	ENGRAVING
1	-SFS (LOCAL-OFF-REMOTE SELECTOR SWITCH, K&N)	-SFS, LOCAL-OFF-REMOTE
2	-SFC (PUSH BUTTON CB CLOSE, GREEN, ABB)	-SFC, CB CLOSE
3	-SFO (PUSH BUTTON CB OPEN, RED, ABB)	-SFO, CB OPEN
4	-PFY1 (LAMP INDICATION FOR CB TRIP, YELLOW, ABB)	-PFY1, CB TRIP
5	-PFR1 (LAMP INDICATION FOR CB CLOSE, RED, ABB)	-PFR1, CB CLOSE
6	-PFG1 (LAMP INDICATION FOR CB OPEN, GREEN, ABB)	-PFG1, CB OPEN
7	-PGJ (DIGITAL MEASUREMENT, CEWE 448)	-PGJ, DIGITAL MEASUREMENT
8	-BCF (FEEDER PROTECTION RELAY, REF615J, ABB)	-BCF, RELAY PROTECTION
9	-XTA1, XTA2 (TEST BLOCK , YONGSUNG)	-XTA, CURRENT TEST BLOCK
10	-XTV1 (TEST BLOCK , YONGSUNG)	-XTV, VOLTAGE TEST BLOCK

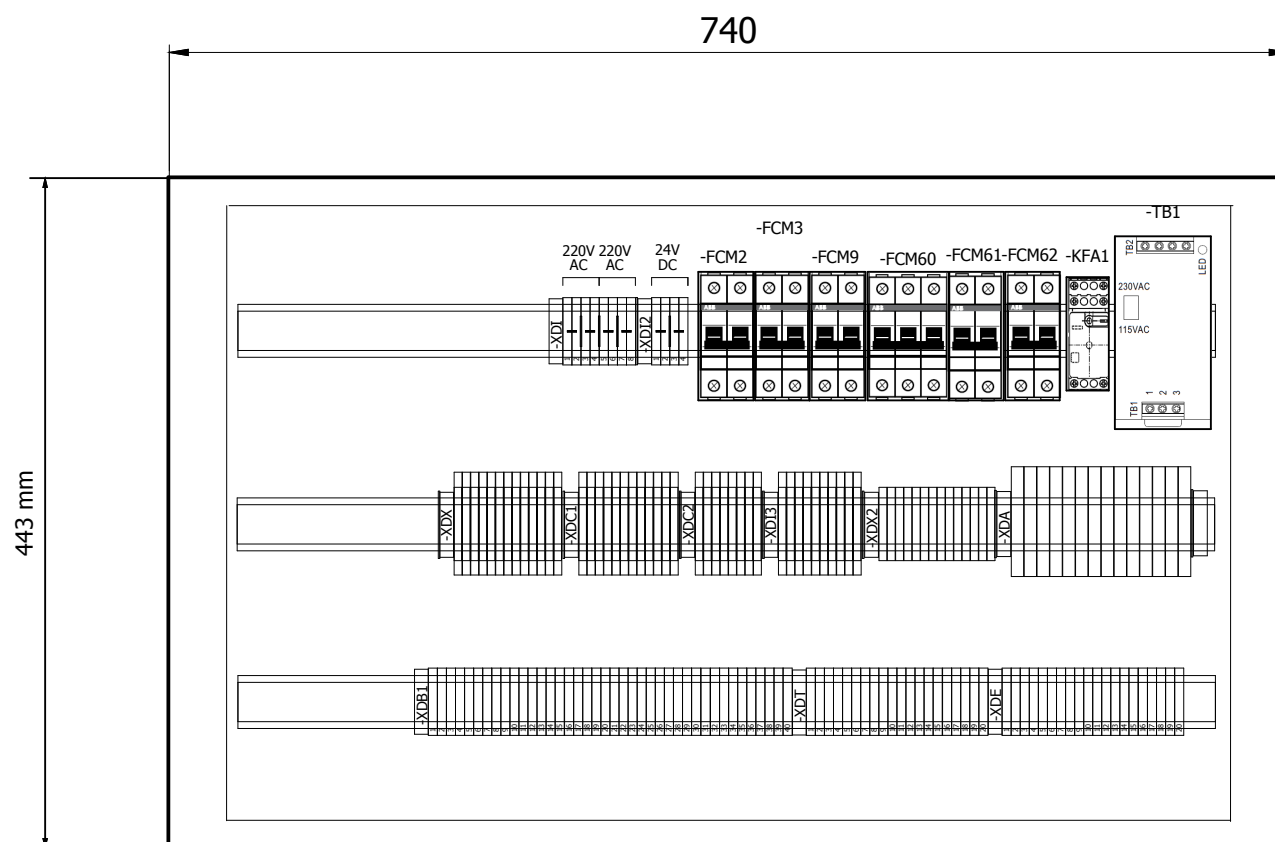[illegible]

				Date Prep.	15.11.2018	PROJECT TITLE MV Switchgear for MNA Serang Plant			LV BOX LAYOUT MVD-01 20kV MAIN SUBSTATION SCHEMATIC DIAGRAM WBC INCOMING	Scale		= H01
				Prepared	YR					PT. ABB Sakti Industri	Customer	PT Multimas Nabati Asahan
00	Issued for Approval	28.12.18	YR	Checked	AW		Drawing Nbr.	IDUNISEC-BE318042-301			Sh. 18	
Ind.	Revision	Date	Name	Approved	AI	Based on:	BE318042	Customer Doc. Nbr.				Cont. 31

WE RESERVE ALL RIGHTS IN THIS DOCUMENT AND IN THE INFORMATION CONTAINED THEREIN. REPRODUCTION, USE OR DISCLOSURE TO THIRD PARTIES WITHOUT EXPRESS AUTHORITY IS STRICTLY FORBIDDEN.

Summarized parts list														IDABB_F02_005-IDABB	
														Carry over: 0.00	
TAG ID		DESCRIPTION				MANUFACTUR/BRAND		PART NUMBER		QUANTITY		REMARKS			
-BCF		Feeder Management Relay HBFJAEAGABC1ANA11G				ABB		REF615J HBFJAEAGABC1ANA11G		1		/16.7:B			
-EB		HEATER 230VAC, 50W				SANYANG		CDXN010033P0009		1		/7.7:E			
-FCM2		MCB S202-C10 MCB. 2P, 10A				ABB		2CDS252001R0104		1		/7.2:C			
-FCM3;-FCM9		MCB S202-C6 MCB. 2P, 6A				ABB		2CDS252001R0064		2		/7.5:C;/7.6:C			
-FCM60		MCB S203-C6 MCB. 3P, 6A				ABB		2CDS253001R0064		1		/16.4:A			
-FCM61;-FCM62		MCB S202-C2 MCB. 2P, 2A				ABB		2CDS252001R0024		2		/16.5:D;/16.7:E			
-KFA1		Auxiliary Relay 230AC 4COS				PHOENIX		1YRA3DL266230001		1		/9.5:E			
-PFG1		PILOT LIGHT GREEN #CL-523G#230VAC CL-523G				ABB		1SFA619402R5232		1		/10.4:D			
-PFR1		PILOT LIGHT RED #CL-523R#230VAC CL-523R				ABB		1SFA619402R5231		1		/10.3:D			
-PFY1		PILOT LIGHT YELLOW #CL-523Y#230VAC CL-523Y				ABB		1SFA619402R5233		1		/10.4:D			
-PGM		POWER METER CEWE 448 Class : 0.5s; CT Input : 1A; VT Input : 57.7-240V (L-N); Aux. Voltage: 80-300VAC/DC				CEWE		1YRA4EA0350001		1		/10.1:C			
-SFC		PUSH BUTTON, YW1B-M1E10-G GREEN COLOUR				IDEC		1YRA3DA14700001		1		/8.3:C			
-SFO		PUSH BUTTON, YW1B-M1E10-R RED COLOUR				IDEC		1YRA3DA14700002		1		/8.5:C			
-SFS		LOCAL/REMOTE Selector Switch Type : S0-CA10-A723-600-E; 4NC (for LOCAL Position) & 4NO (for REMOTE Position)				K&N		1YRA3DA17940011		1		/8.3:B			
-TB1		Voltage Input : 85-264 VAC/120-370V DC Voltage Output : 24 VDC, 5A				MEANWELL		DR-120-24		1		/7.3:D			
-XTA1;-XTA2		Current Test Block Rated Current : 10A, 250V; Mounting : Flush Mounting				YONGSUNG		YSCTT-04C		2		/15.5:B;/15.5:C			
-XTV1		Voltage Test Block Rated Current : 10A, 250V; Mounting : Flush Mounting				YONGSUNG		YSPTT-04C		1		/16.5:A			
										</					

[illegible]

[illegible]

[illegible]

F										E										D										C										B										A	
										REMARK										CABLE										EQUIPMENT										Wire No										Terminal number										TYPE										WIRE NO.										EQUIPMENT										CABLE										REMARK	

[illegible]

[illegible]

[illegible]

[illegible]

F															E															D															C															B															A	
															REMARK															CABLE															EQUIPMENT															WIRE NO.															TYPE															Terminal number															REMARK	
															1,5 mm²																														-PREVIOUS_PNL-XDI6:2	PT 2.5															1 1	

[illegible]

[illegible]

F										D	C	B	A			
REMARK										CABLE	EQUIPMENT	WIRE NO.	EQUIPMENT	CABLE	REMARK	
1,5 mm²											-XDB1:25		PTTB 2,5		-FCM2:2	1,5 mm²
1,5 mm²											-SFS:1		PTTB 2,5			
1,5 mm²											-BCF:-X100:16		PTTB 2,5			
1,5 mm²											-XDC1:12		PTTB 2,5			
1,5 mm²											-BCF:X100:11		PTTB 2,5			
1,5 mm²											-XDC1:16		PTTB 2,5			
1,5 mm²											-PGM:+/P		PTTB 2,5			
1,5 mm²											-XDB1:11		PTTB 2,5			
1,5 mm²											-KFA1:14		PTTB 2,5			
1,5 mm²											-XDB1:27		PTTB 2,5			
1,5 mm²											-XDB1:32		PTTB 2,5			
1,5 mm²											-KFA1:24		PTTB 2,5			
2,5 mm²											-FCM2:4		PTTB 2,5		-XDB1:35	1,5 mm²
2,5 mm²													PTTB 2,5		-XDB1:14	1,5 mm²
2,5 mm²													PTTB 2,5		-XDB1:30	1,5 mm²
2,5 mm²													PTTB 2,5		-XDB1:46	1,5 mm²
2,5 mm²													PTTB 2,5		-XDB1:20	1,5 mm²
2,5 mm²													PTTB 2,5		-KFA1:A2	1,5 mm²
2,5 mm²													PTTB 2,5		-XDE:22	1,5 mm²
2,5 mm²													PTTB 2,5		-PGM:-/N	1,5 mm²
2,5 mm²													PTTB 2,5		-PFR1:x2	1,5 mm²
2,5 mm²													PTTB 2,5		-XDC1:22	1,5 mm²
2,5 mm²													PTTB 2,5			1,5 mm²
2,5 mm²													PTTB 2,5		-FCM9:2	1,5 mm²
2,5 mm²													PTTB 2,5		-FCM9:4	1,5 mm²
2,5 mm²																
2,5 mm²																
