



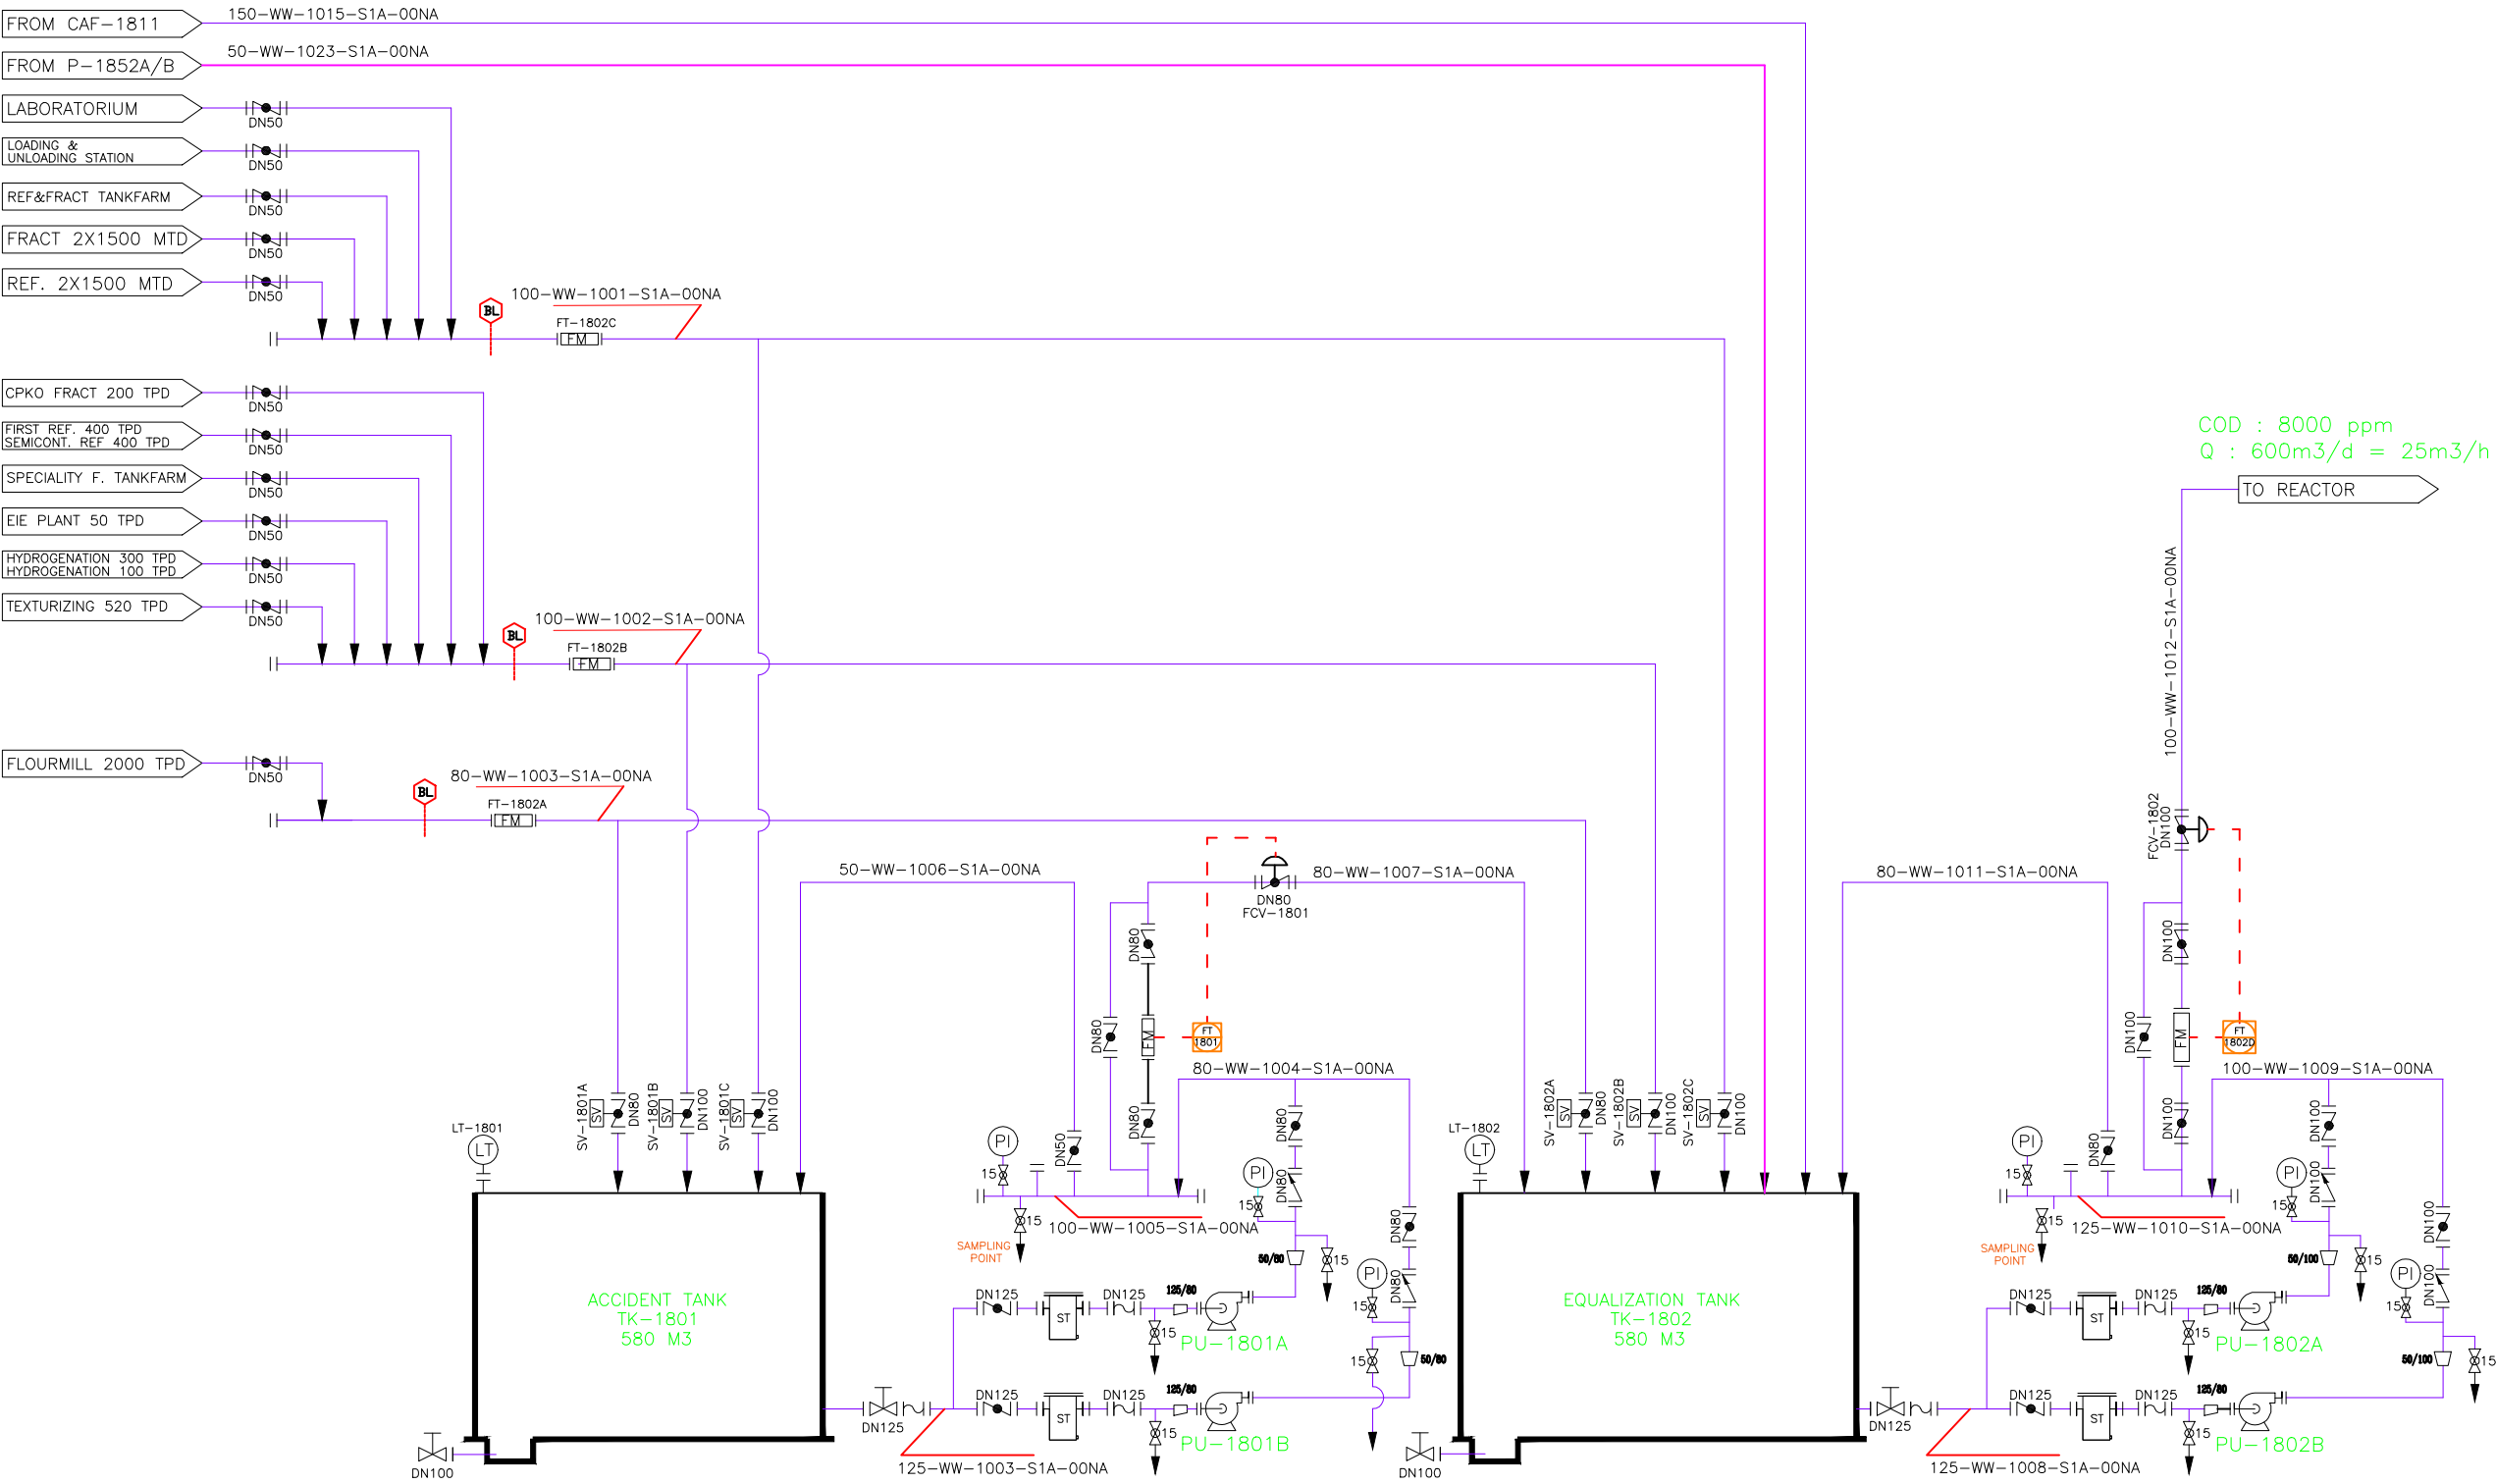

LEGEND/LEGENDA			
	WAFER CHECK VALVE		
	EXPANTIONT JOINT		
	GATE VALVE		
	BUTTERFLY VALVE		
	BASKET STRAINER		
	CONTROL VALVE		
	FLOW METER		
	CENTRIFUGAL PUMP		
	RADAR		
	LEVEL SWITCH HIGH		
	LEVEL SWITCH LOW		
	PH METER		
	PRESSURE GAUGE		
LINE NUMBER LEGEND			
XXX-XXX-XXXX-XXX-XXXX			
Thickness Insulation Insulation Type Corrosion Allowance Presure Rating Material Line Number Service Diameter Nominal (DN)			
STATUS			
REVISI/REVISION			
NO	KETERANGAN DESCRIPTION	PARAF SIGN	TANGGAL DATE
PEKERJAAN PROJECT			
EFFLUENT TREATMENT PLANT			
LOKASI LOCATION			
BLOCK PT. MNA SERANG			
SKALA SCALE	SEE TO DRAW	PARAF SIGN	TANGGAL DATE
DIGAMBAR DRAWN	FEIZY / ANDRY		22-11-17
DIPERIKSA CHECKED	WANAN A. WIBOWO		
DIPERIKSA CHECKED	NAN LIM		
DISETUJUI APPROVED BY	ERIK TJA		
GAMBAR TITLE			
ACCIDENT & EQUALIZATION TANK			
DRAWING NO. MNS-UTY-ETP-PID-001		REVISI REVISION	PAGE SHEET 1/3
MNA wilmar		PT.MULTIMAS NABATI ASAHAN MAILING ADDRESS : KAWASAN INDUSTRI MNA SERANG JL. RAYA BOJONEGARAH KM.5 KAL.162 Desa Terele Kec.KRAMATWATU SERANG, BANTEN, INDONESIA PHONE. (0254) -- 8495283	

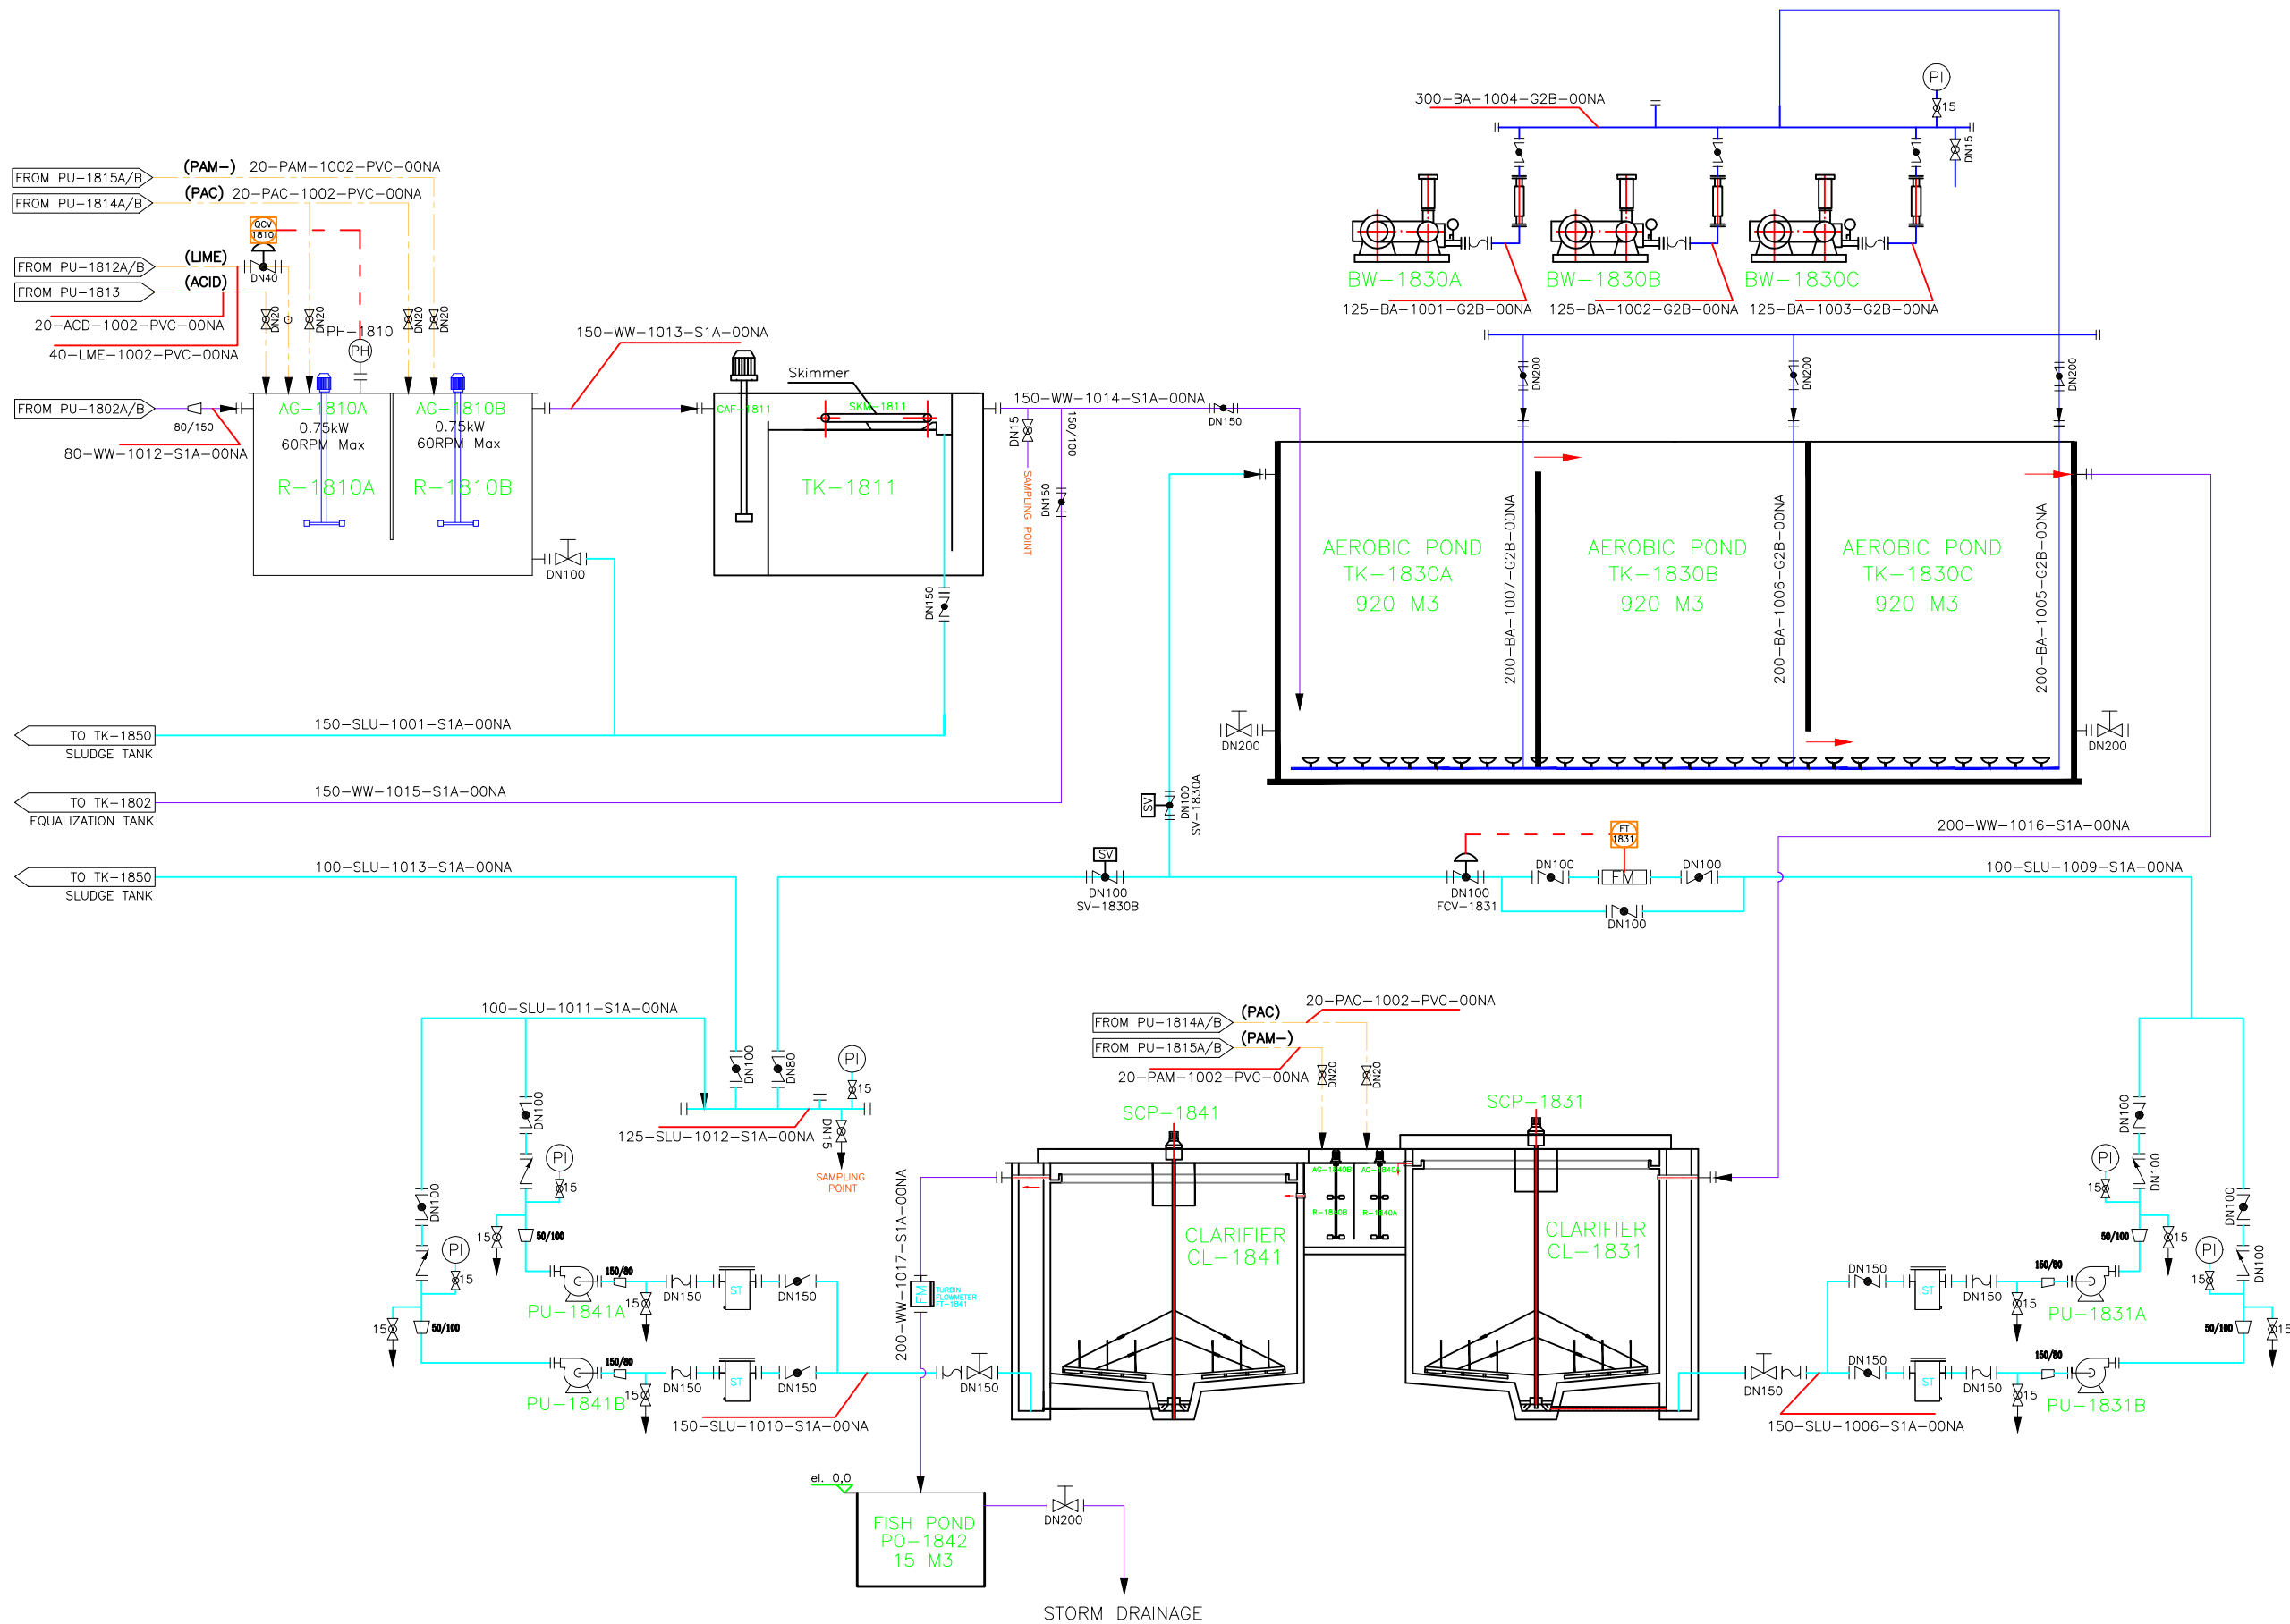

LEGEND/LEGENDA

	WAFER CHECK VALVE
	EXPANTIONT JOINT
	GATE VALVE
	BALL VALVE
	BUTTERFLY VALVE
	BASKET STRAINER
	CONTROL VALVE
	SELENOID VALVE
	CENTRIFUGAL PUMP
	FLOW METER
	PH METER
	BLOWER

LINE NUMBER LEGEND

XXX-XXX-XXXX-XXX-XXXX	Thickness Insulation
---	Insulation Type
---	Corrosion Allowance
---	Pressure Rating
---	Material
---	Line Number
---	Service
---	Diameter Nominal (DN)

STATUS

REVISI/REVISION

NO	KETERANGAN Description	PARAF SIGN	TANGGAL DATE

PEKERJAAN
PROJECT

EFFLUENT TREATMENT PLANT

LOKASI
LOCATION

BLOCK PT. MNA SERANG

SKALA SCALE	SEE TO DRAW	PARAF SIGN	TANGGAL DATE
DIGAMBAR DRAWN	FEIZY / ANDRY		22-11-17
DIPERIKSA CHECKED	WANAH A. WIBOWO		
DIPERIKSA CHECKED	IVAN LIM		
DISETUJUI APPROVED BY	ERIK TJA		


GAMBAR
TITLE

REACTOR, CAF, AEROBIC TANK
CLARIFIER I, CLARIFIER II AND FISH POND

DRAWING NO. MNAS-UTY-ETP-PID-001	REVISI REVISION	PAGE SHEET	2/3
-------------------------------------	--------------------	---------------	-----

 MNA	 PT.MULTIMAS NABATI ASAHAAN
---------	--------------------------------

MAILING ADDRESS : KAWASAN INDUSTRI MNA SERANG
Jl. Raya Bojonegara Km.5 KAL.162 Desa Tirta
KEC.KORAMATUTU SERANG, BANTEN, INDONESIA
PHONE. (0254) -- 8495283

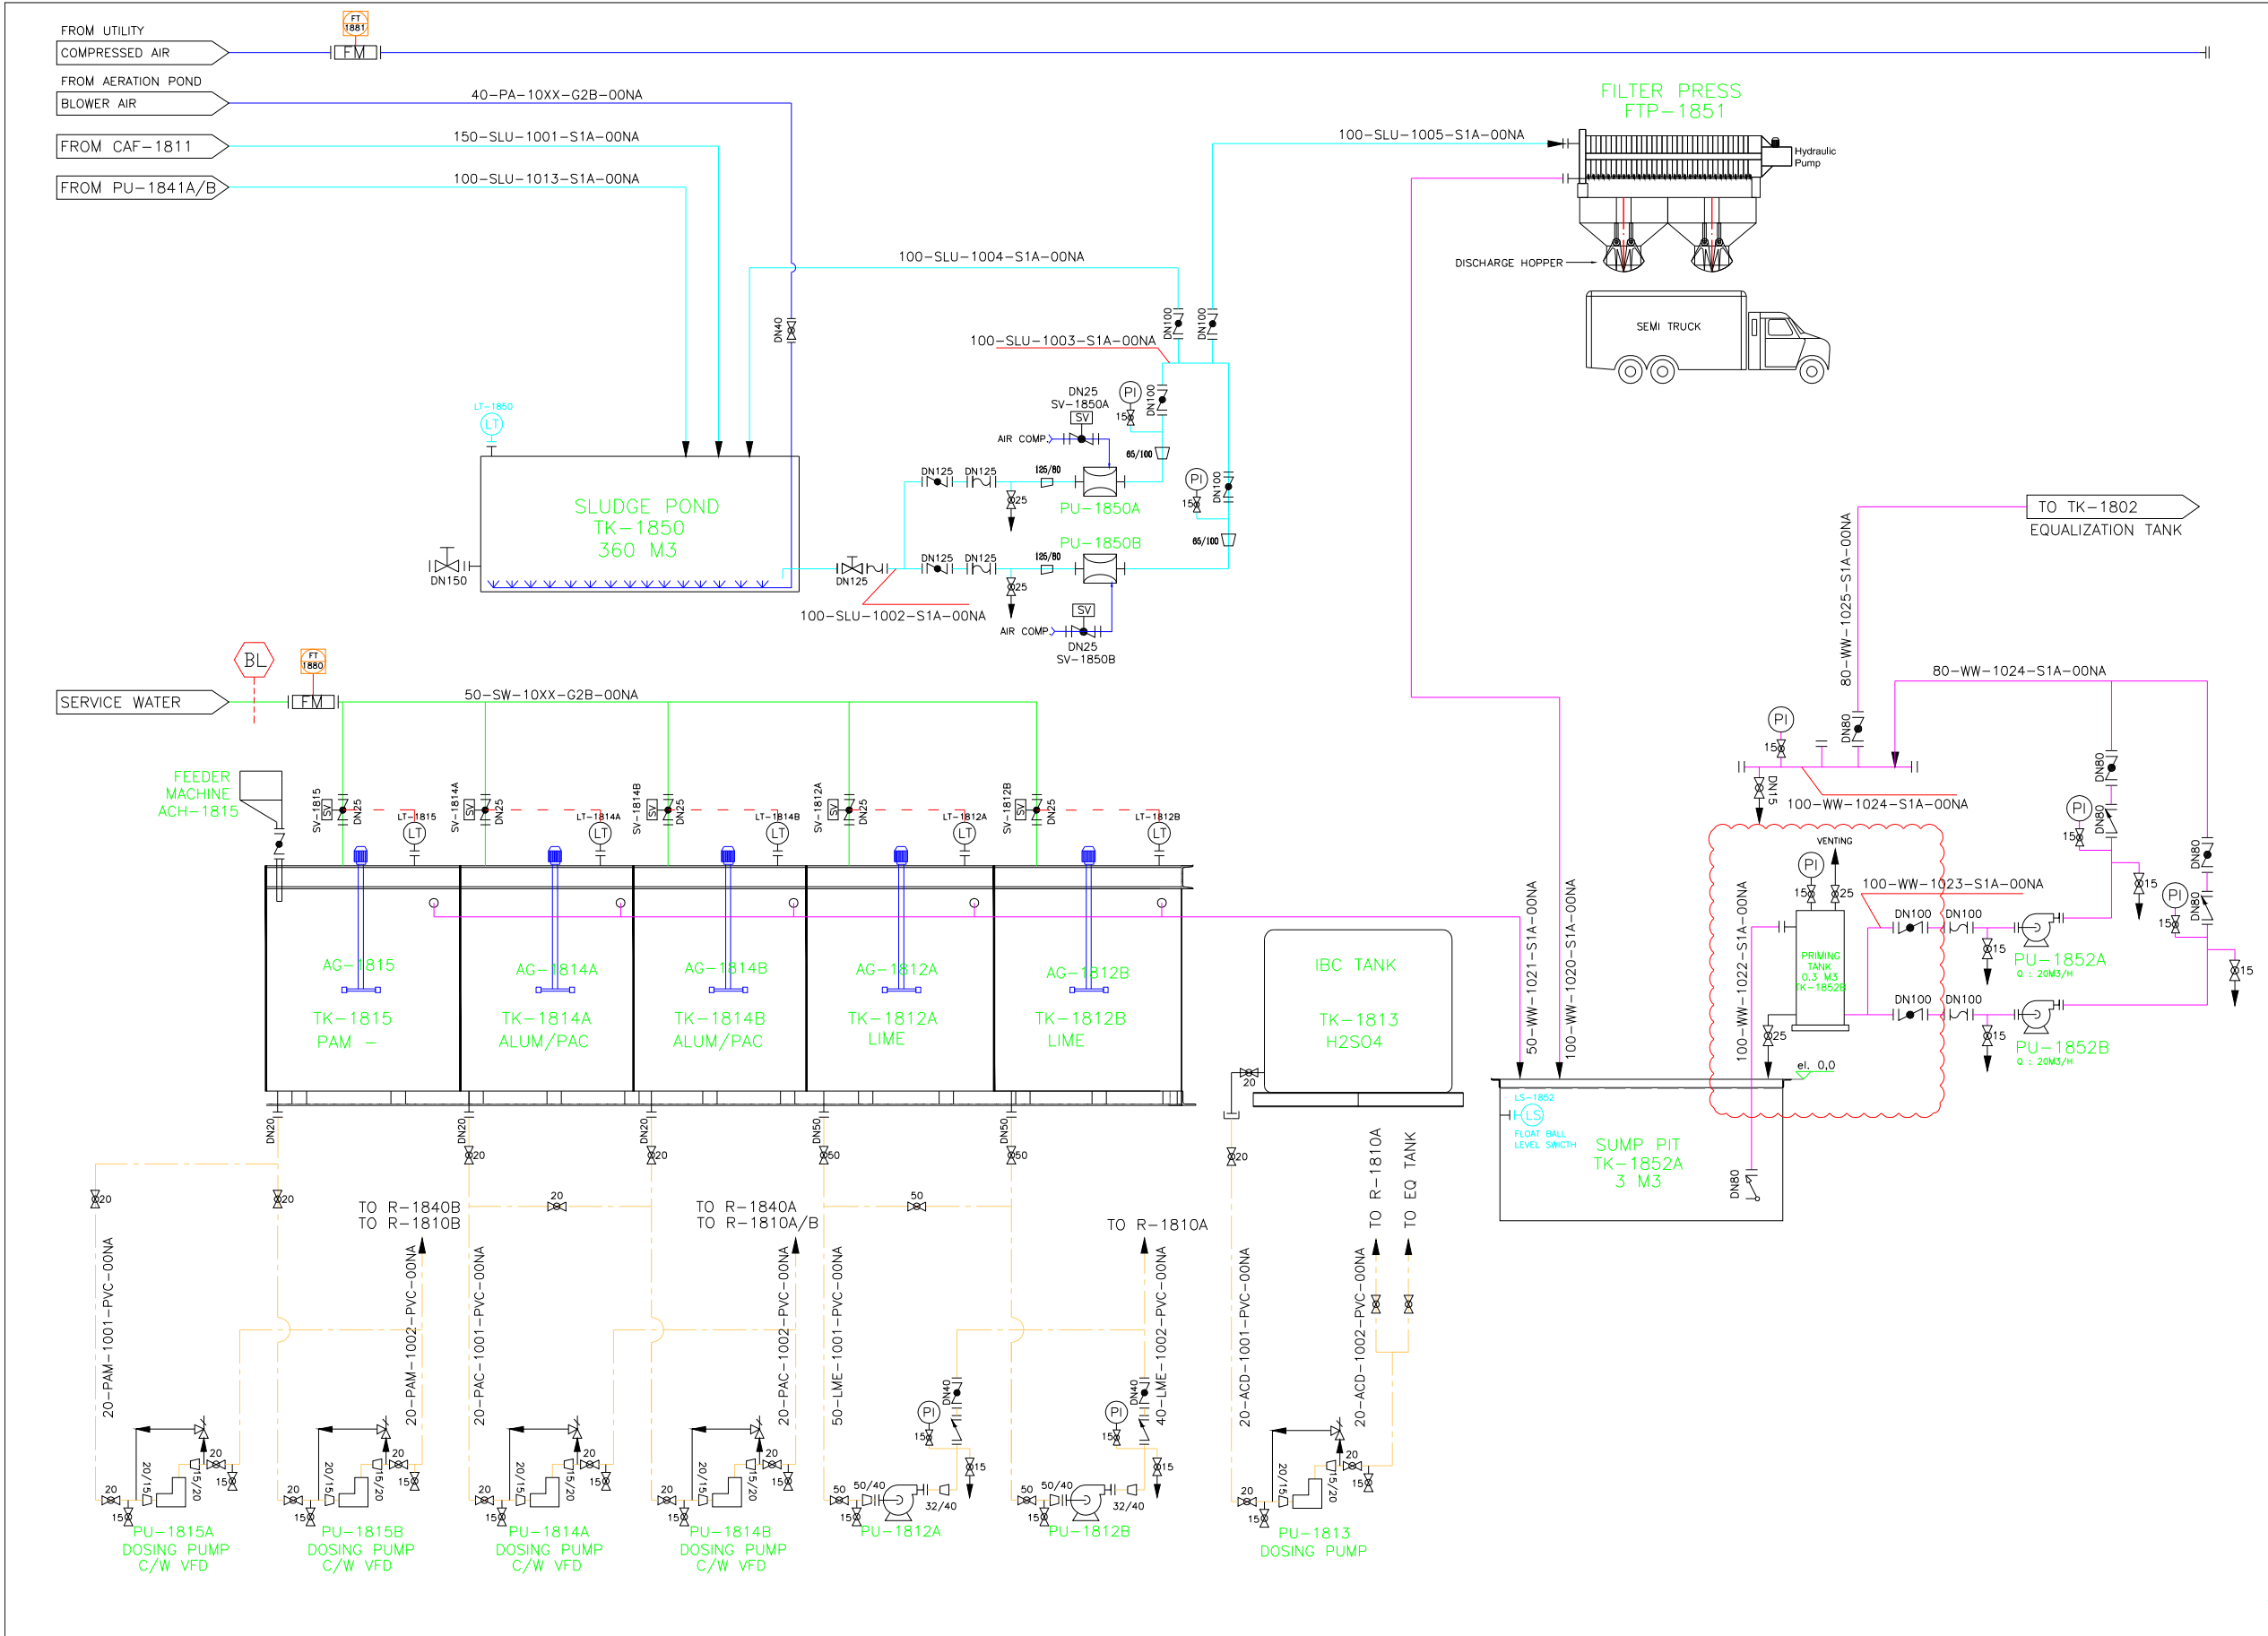

LEGEND/LEGENDA			
	WAFER CHECK VALVE		
	EXPANTIONT JOINT		
	GATE VALVE		
	BALL VALVE		
	BUTTERFLY VALVE		
	CENTRIFUGAL PUMP		
	DIAPHRAGM PUMP		
	RADAR		
	PH METER		
	LEVEL SWITCH HIGH		
	LEVEL SWITCH LOW		
	PRESSURE GAUGE		
LINE NUMBER LEGEND			
XXX-XXX-XXXX-XXX-XXXX			
Thickness Insulation Insulation Type Corrosion Allowance Presure Rating Material Line Number Service Diameter Nominal (DN)			
STATUS REVISI/REVISION			
NO	KETERANGAN DESCRIPTION	PARAF SIGN	TANGGAL DATE
PEKERJAAN PROJECT			
EFFLUENT TREATMENT PLANT			
LOKASI LOCATION			
BLOCK PT. MNA SERANG			
SKALA SCALE	SEE TO DRAW	PARAF SIGN	TANGGAL DATE
DIGAMBAR DRAWN	FEIZY / ANDRY		22-11-17
DIPERIKSA CHECKED	WAMAN A. WIBOWO		
DIPERIKSA CHECKED	IVAN LIM		
DISETUJUI APPROVED BY	ERIK TJIA		
GAMBAR TITLE			
SLUDGE TANK, FILTER PRESS, DEWATER TANK DAILY CHEMICAL TANK			
DRAWING NO. MNAS-UTY-ETP-PID-001		REVISI REVISION	PAGE SHEET 3/3
		PT.MULTIMAS NABATI ASAHAN	
MAILING ADDRESS : KAWASAN INDUSTRI MNA SERANG Jl. RAYA BONGKONGGARA KM.5 KAW.162 Desa Terate KEC.KRAMATJATI SERANG, BANTEN, INDONESIA PHONE. (0254) - 8495283			