

Section 100: Pre-Blending

Outside Battery Limit
(Wilmar scope on pipe & fitting)

FEED PUMP (PRIMARY)

Pump Type	Centrifugal pump
Flowrate	30.0m3/hr at 4.0 bar
Motor	7.5 kW at 2,900 RPM 400V/ 50 Hz
Connection size & type	Inlet: 2.5" / Outlet: 2.0" (SMS Union)
Hot water jacket	Included
Model	FPE 3532/175Ah

FEED PUMP (STANDBY)


Pump Type	Centrifugal pump
Flowrate	30.0m3/hr at 4.0 bar
Motor	7.5 kW at 2,900 RPM 400V/ 50 Hz
Connection size & type	Inlet: 2.5" / Outlet: 2.0" (SMS Union)
Hot water jacket	Included
Model	FPE 3532/175Ah

SECTION 200 : EMULSIFIER

Rev	Date of Rev	Rev. by	Project No	Customer Name
04	02.11.2018	EW	AUTT-C010-18	PT Wilmar Cahaya Indonesia, TBK
05	28.12.2018	EW		
06	01.02.2019	EW	FC-C010-18	Piping & Instrument Diagram
07	31.05.2019	EW		
08	30.07.2019	EW	Mike Teo	Polaron Long (CO2) Texturing Plant
Prepared by			Mike Teo	26 December 2017
Checked by				NTS
Scale				4 of 10




THIS DRAWING IS THE PROPERTY OF AUTTECH ENGINEERING. IT IS TO BE USED ONLY FOR THE PROJECT AND SITE SPECIFIC. ALL INFORMATION IS CONFIDENTIAL AND NOT TO BE RELEASED OR REPRODUCED IN ANY FORM WITHOUT PERMISSION.

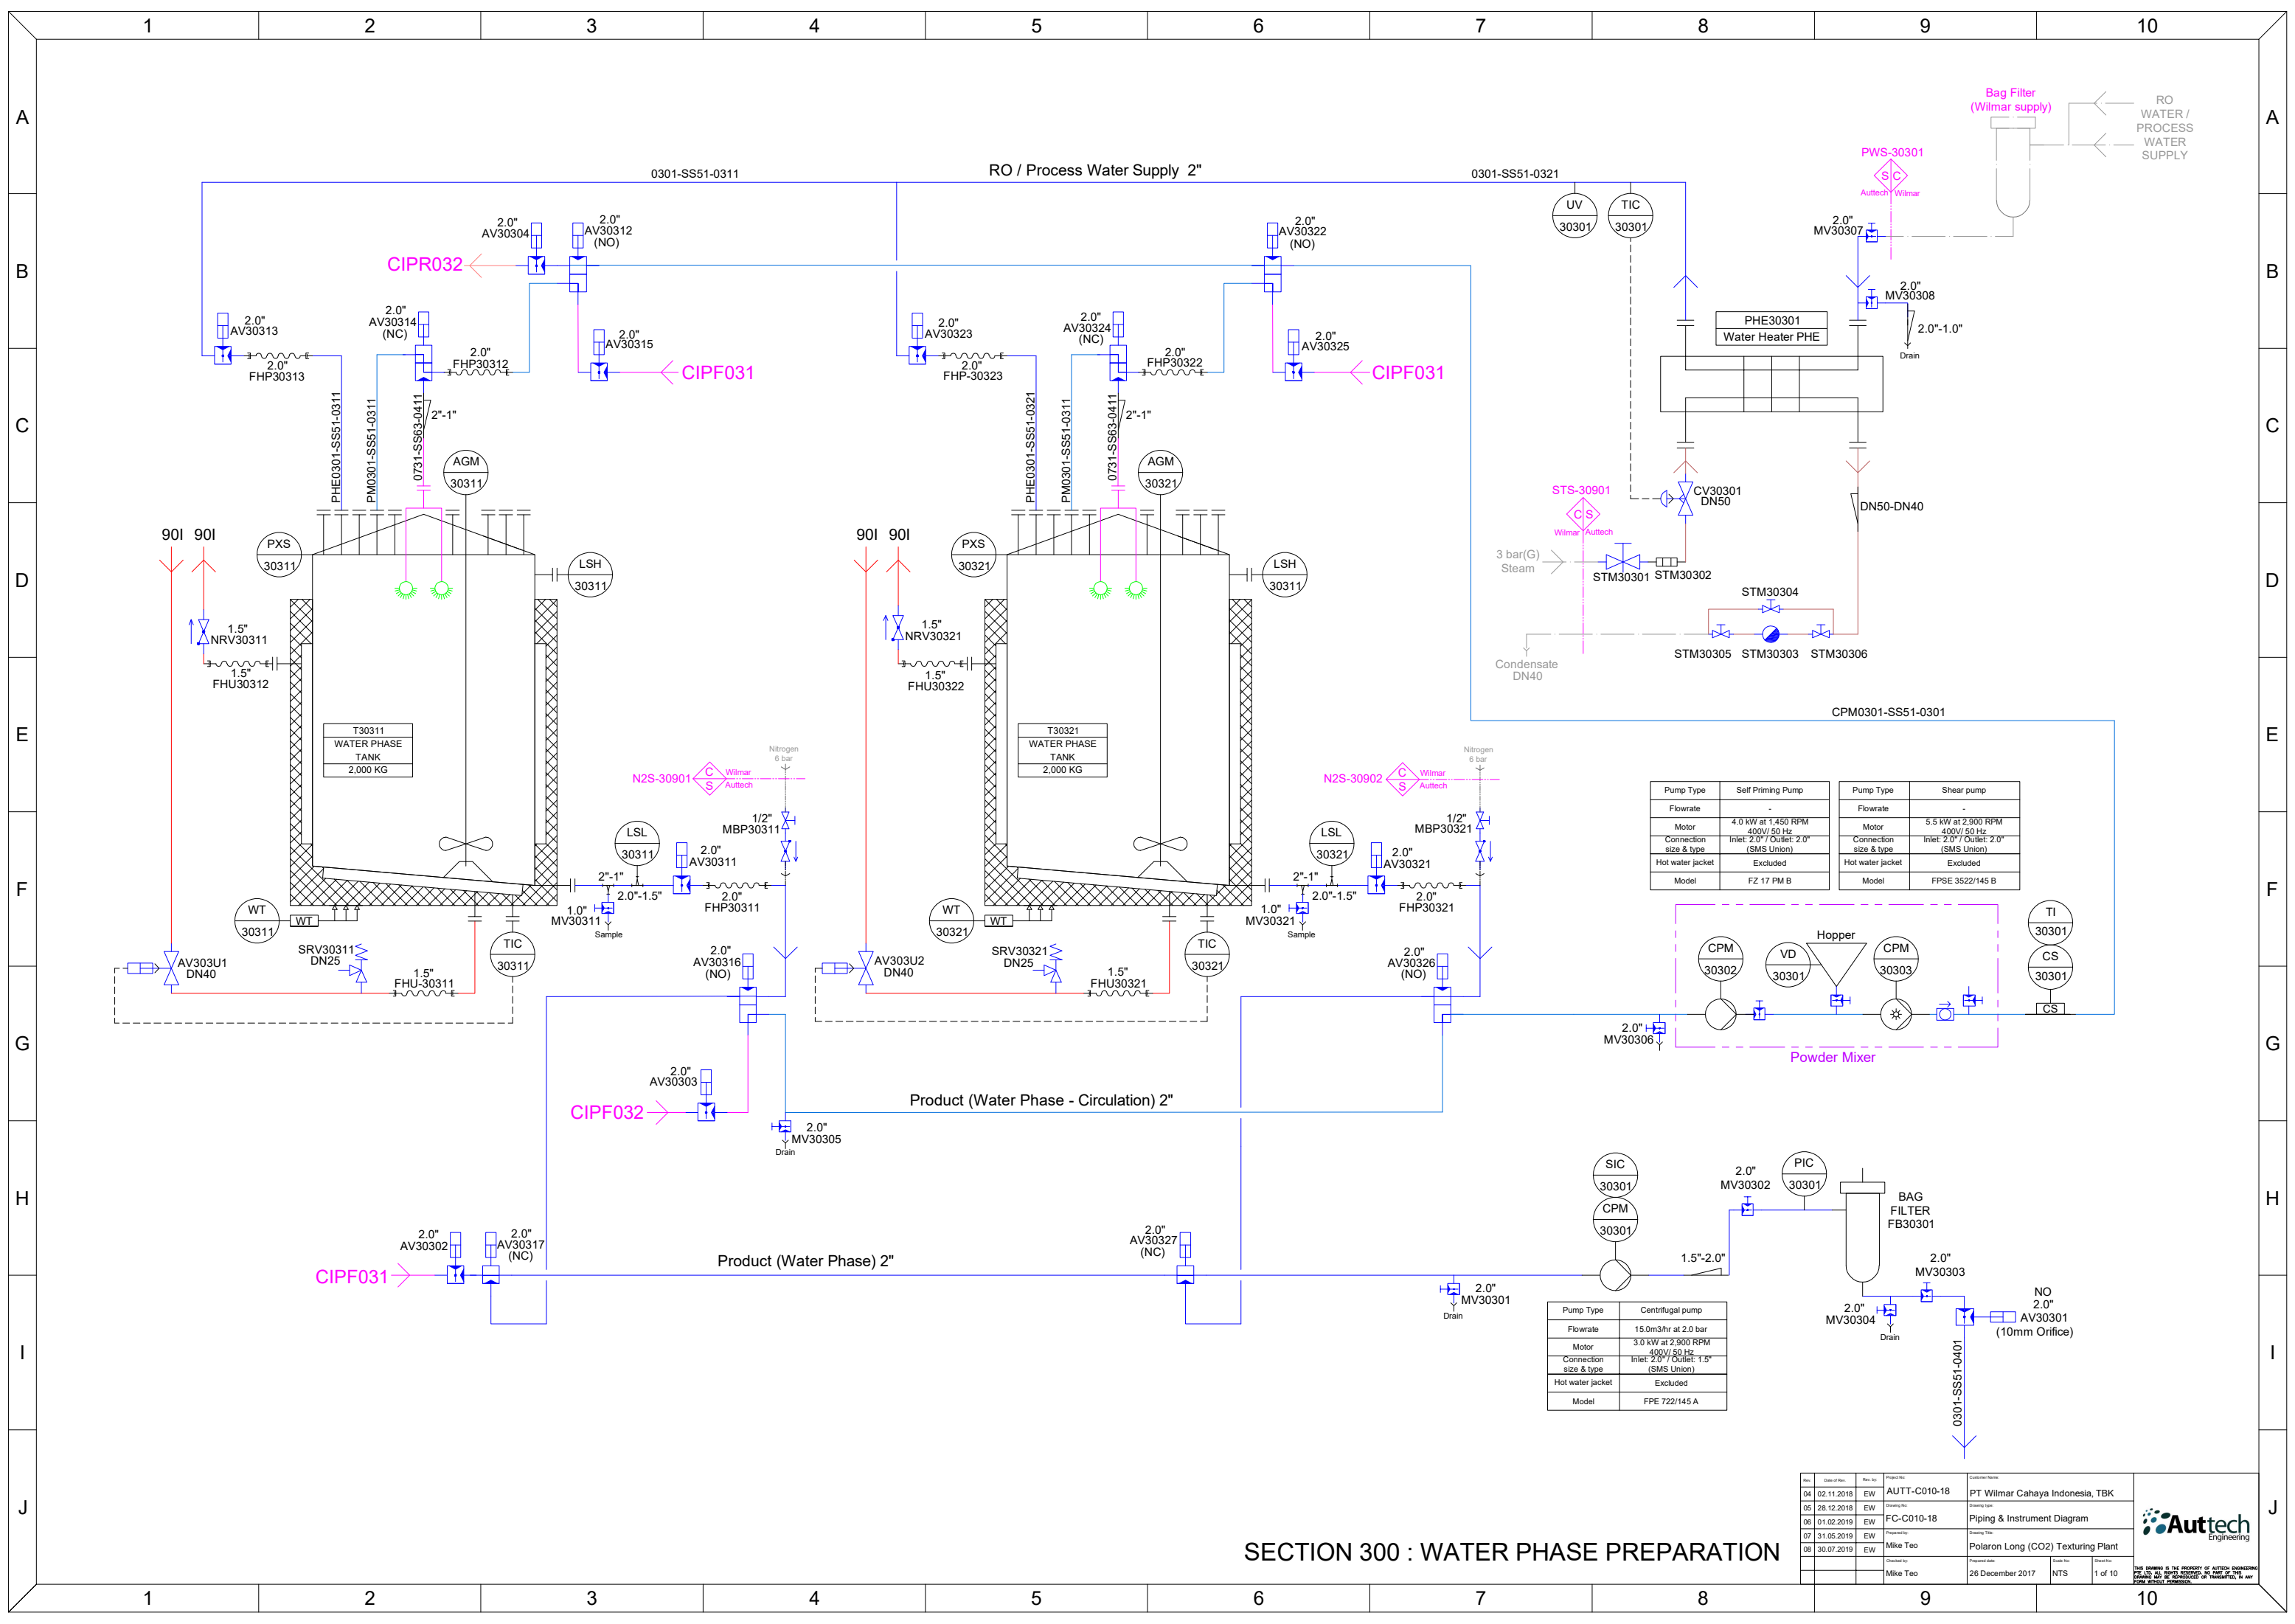

SECTION 300 : WATER PHASE PREPARATION

Rev.	Date of Rev.	Rev. by	Project No.	Customer Name
04	02.11.2018	EW	AUTT-C010-18	PT Wilmar Cahaya Indonesia, TBK
05	28.12.2018	EW		
06	01.02.2019	EW	FC-C010-18	Piping & Instrument Diagram
07	31.05.2019	EW		
08	30.07.2019	EW	Mike Teo	Polaron Long (CO2) Texturing Plant
		Checked by	Mike Teo	26 December 2017
		Prepared date		NTS
		Scale		1 of 10

THIS DRAWING IS THE PROPERTY OF AUTTECH ENGINEERING. IT IS TO BE USED ONLY FOR THE PROJECT SPECIFICALLY IDENTIFIED IN THE TITLE BLOCK. ALL RIGHTS ARE RESERVED BY AUTTECH ENGINEERING. NO PART OF THIS DRAWING IS TO BE REPRODUCED OR TRANSMITTED IN ANY FORM WITHOUT PERMISSION.

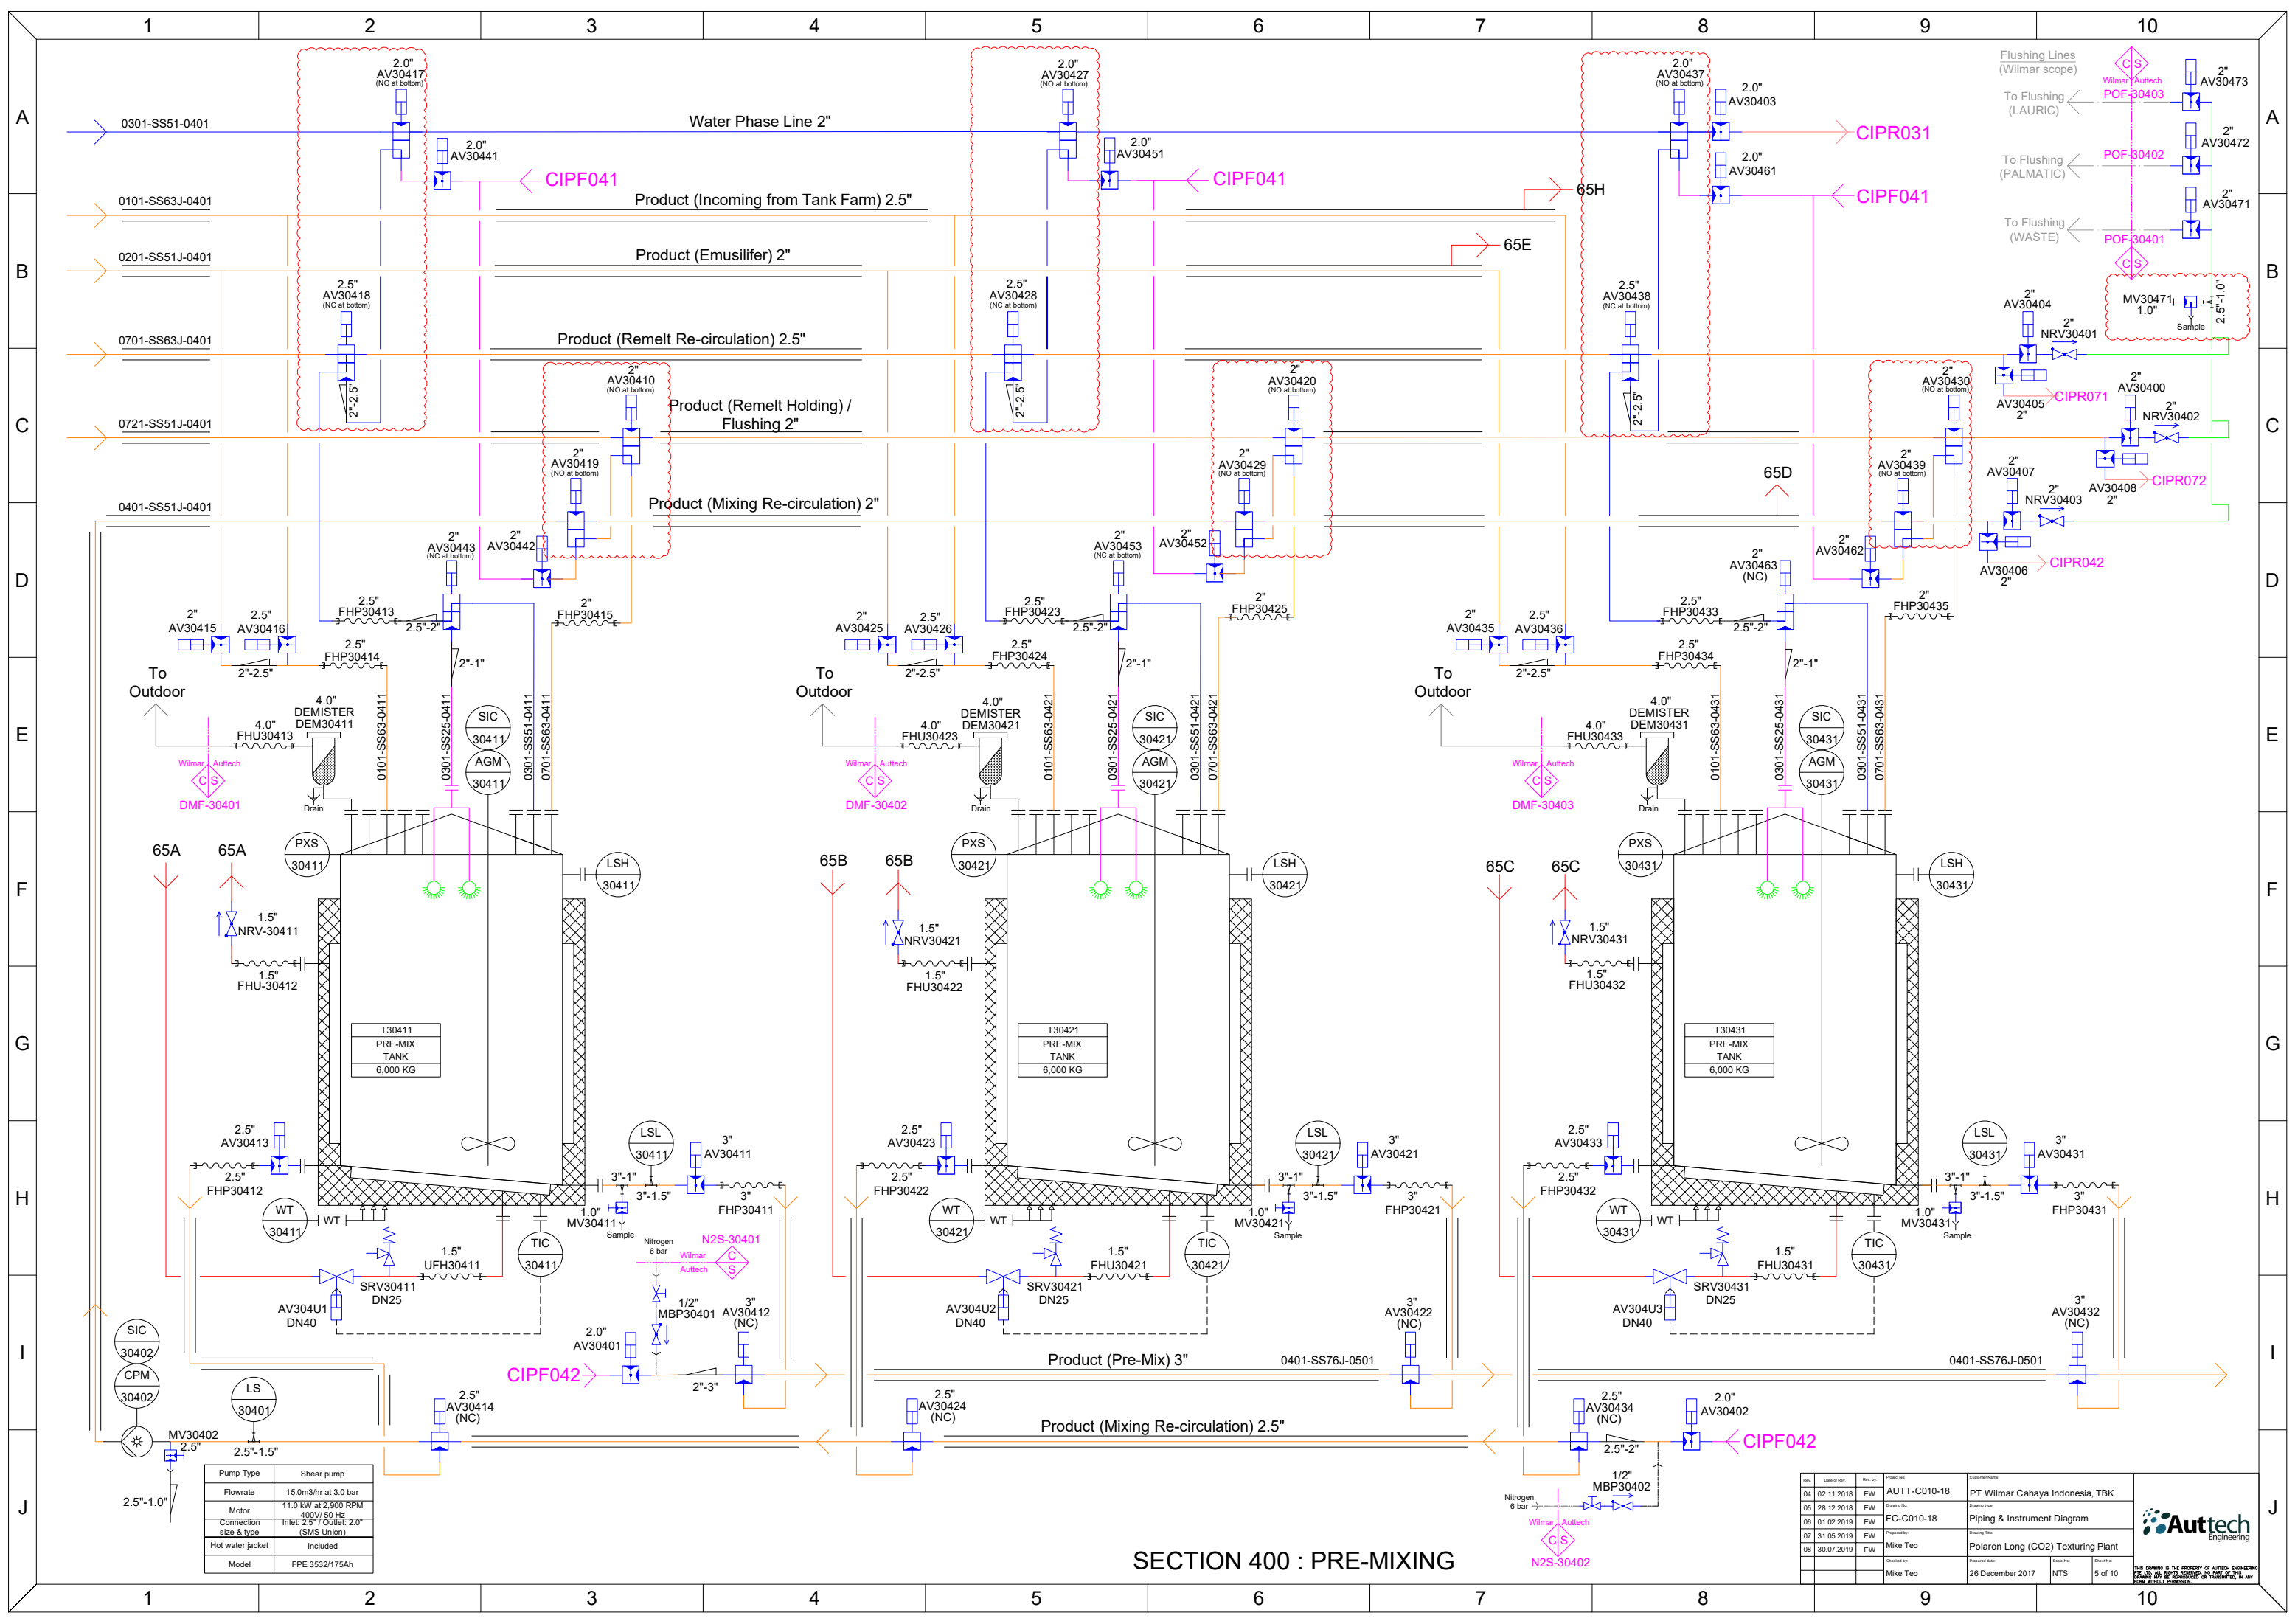


SECTION 400 : PRE-MIXING

Rev.	Date of Rev.	Rev. by	Project No.	Customer Name
04	02.11.2018	EW	AUTT-C010-18	PT Wilmar Cahaya Indonesia, TBK
05	28.12.2018	EW	FC-C010-18	Piping & Instrument Diagram
06	01.02.2019	EW		
07	31.05.2019	EW		
08	30.07.2019	EW		

Prepared by	Mike Teo	Project Title	Polaron Long (CO2) Texturing Plant
Checked by	Mike Teo	Scale No.	NTS
Drawn by		Sheet No.	5 of 10




THIS DRAWING IS THE PROPERTY OF AUTTECH ENGINEERING. IT IS TO BE USED ONLY FOR THE PROJECT AND SITE SPECIFICALLY MENTIONED. ALL RIGHTS RESERVED. NO REPRODUCTION OR TRANSMISSION IN ANY FORM WITHOUT PERMISSION.

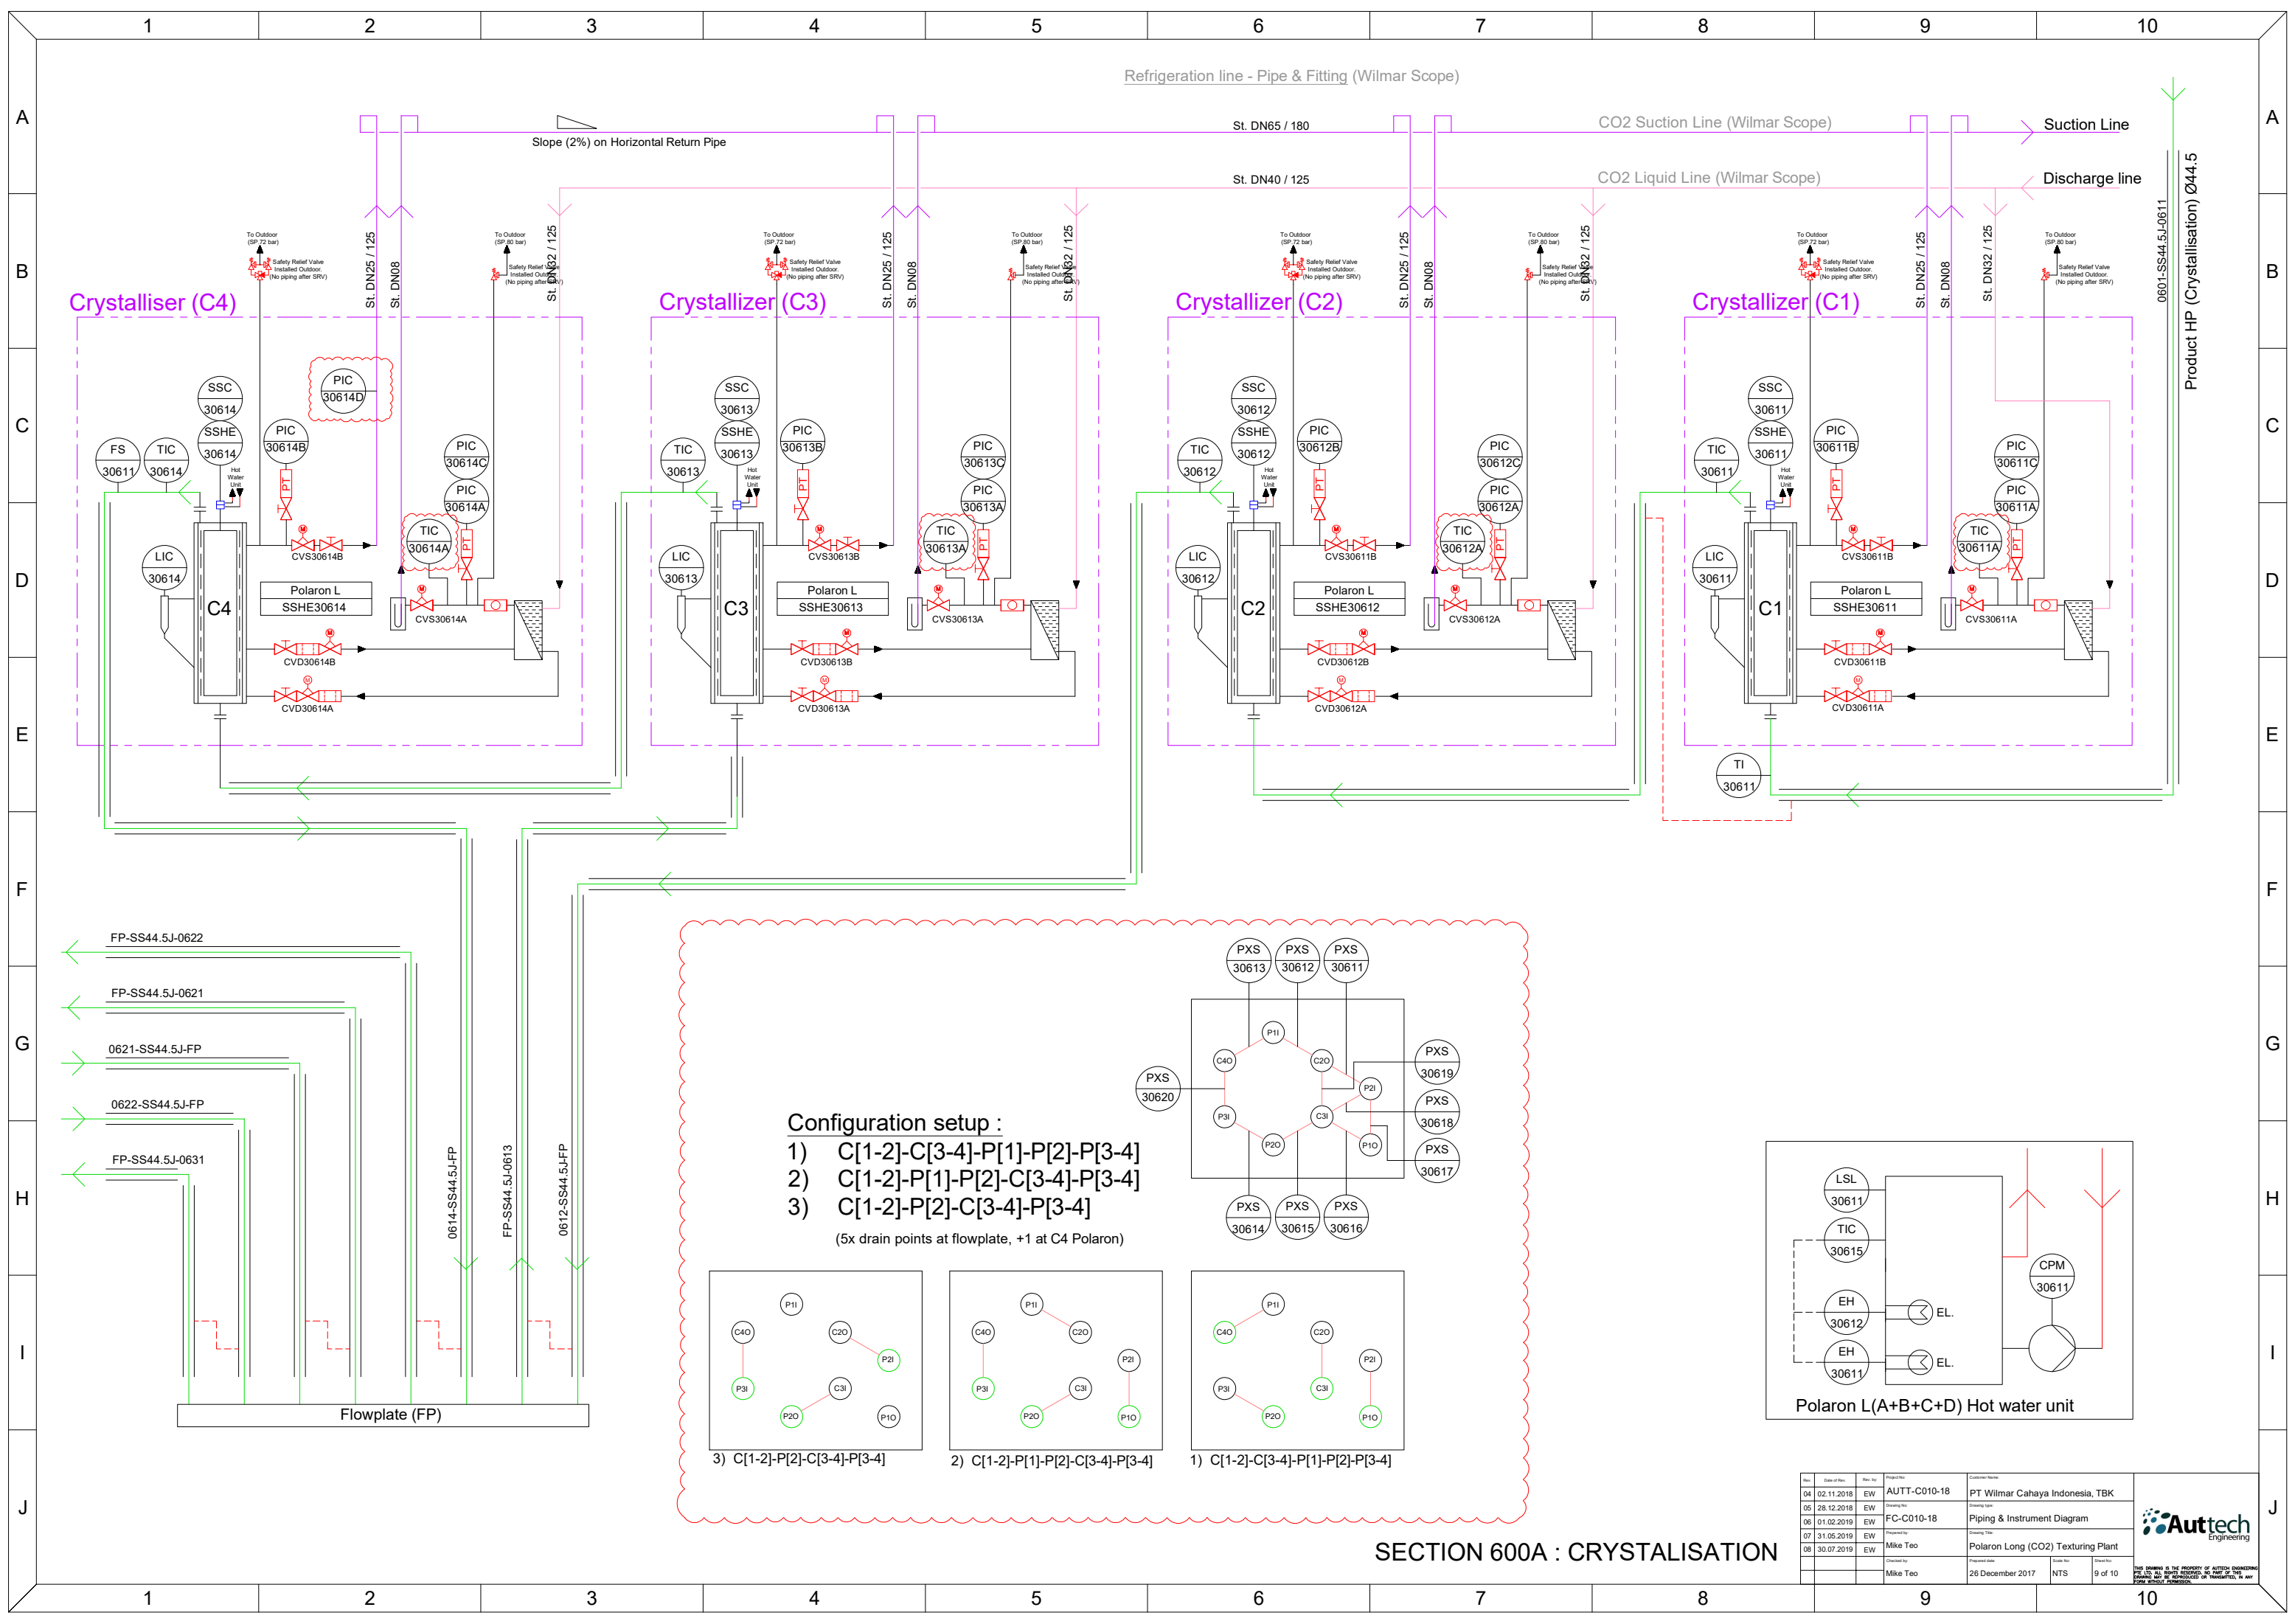

Configuration setup :

- 1) C[1-2]-C[3-4]-P[1]-P[2]-P[3-4]
- 2) C[1-2]-P[1]-P[2]-C[3-4]-P[3-4]
- 3) C[1-2]-P[2]-C[3-4]-P[3-4]

(5x drain points at flowplate, +1 at C4 Polaron)

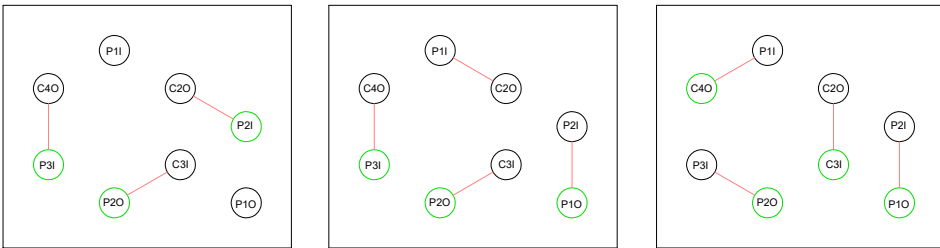


- 3) C[1-2]-P[2]-C[3-4]-P[3-4]
- 2) C[1-2]-P[1]-P[2]-C[3-4]-P[3-4]
- 1) C[1-2]-C[3-4]-P[1]-P[2]-P[3-4]

SECTION 600A : CRYSTALLISATION

Rev.	Date of Rev.	Rev. by	Project No.	Customer Name
04	02.11.2018	EW	AUTT-C010-18	PT Wilmar Cahaya Indonesia, TBK
05	28.12.2018	EW		
06	01.02.2019	EW	FC-C010-18	Piping & Instrument Diagram
07	31.05.2019	EW		
08	30.07.2019	EW	Mike Teo	Polaron Long (CO2) Texturing Plant
			Mike Teo	26 December 2017
				Scale: NTS
				Drawn: 9 of 10




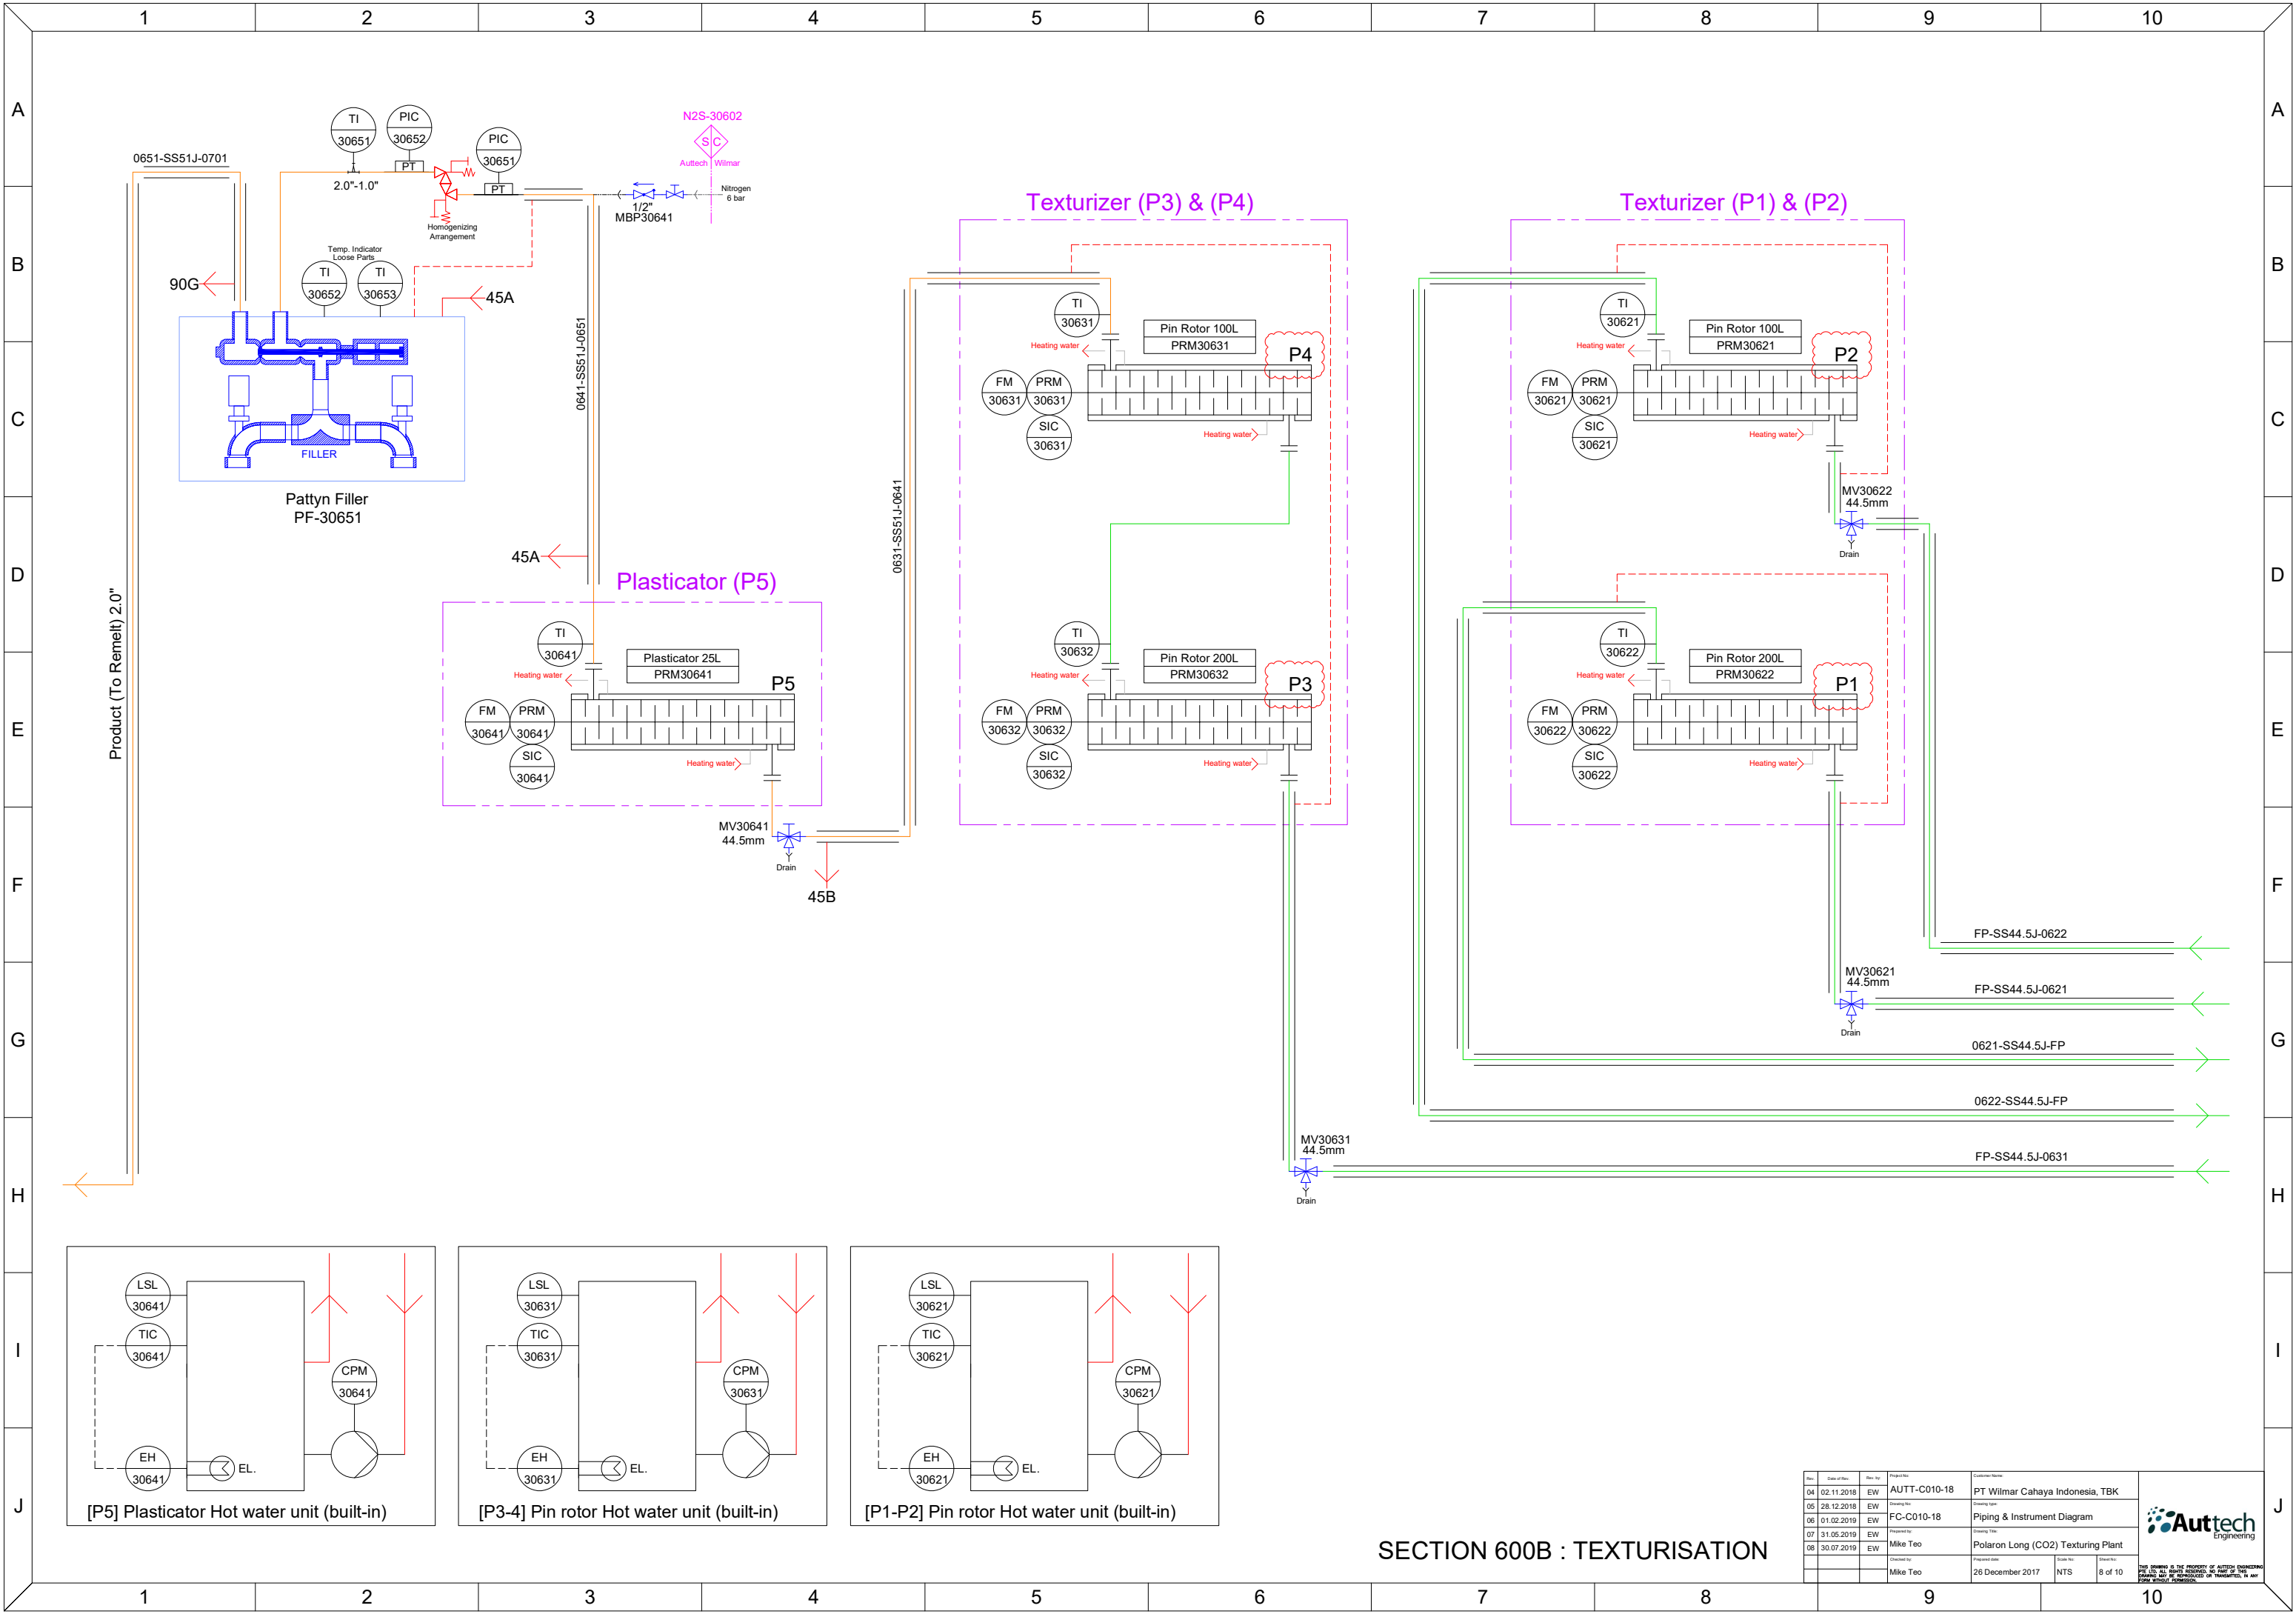


Rev.	Date of Rev.	Rev. by	Project No.	Customer Name
04	02.11.2018	EW	AUTT-C010-18	PT Wilmar Cahaya Indonesia, TBK
05	28.12.2018	EW		
06	01.02.2019	EW	FC-C010-18	Piping & Instrument Diagram
07	31.05.2019	EW		
08	30.07.2019	EW	Mike Teo	Polaron Long (CO2) Texturing Plant
			Mike Teo	26 December 2017
				Scale: NTS
				Drawn by: 8 of 10

Auttech Engineering

THIS DRAWING IS THE PROPERTY OF AUTTECH ENGINEERING. IT IS TO BE USED ONLY FOR THE PROJECT SPECIFICALLY IDENTIFIED HEREIN. ALL RIGHTS RESERVED. NO REPRODUCTION OR TRANSMISSION IN ANY FORM WITHOUT PERMISSION.

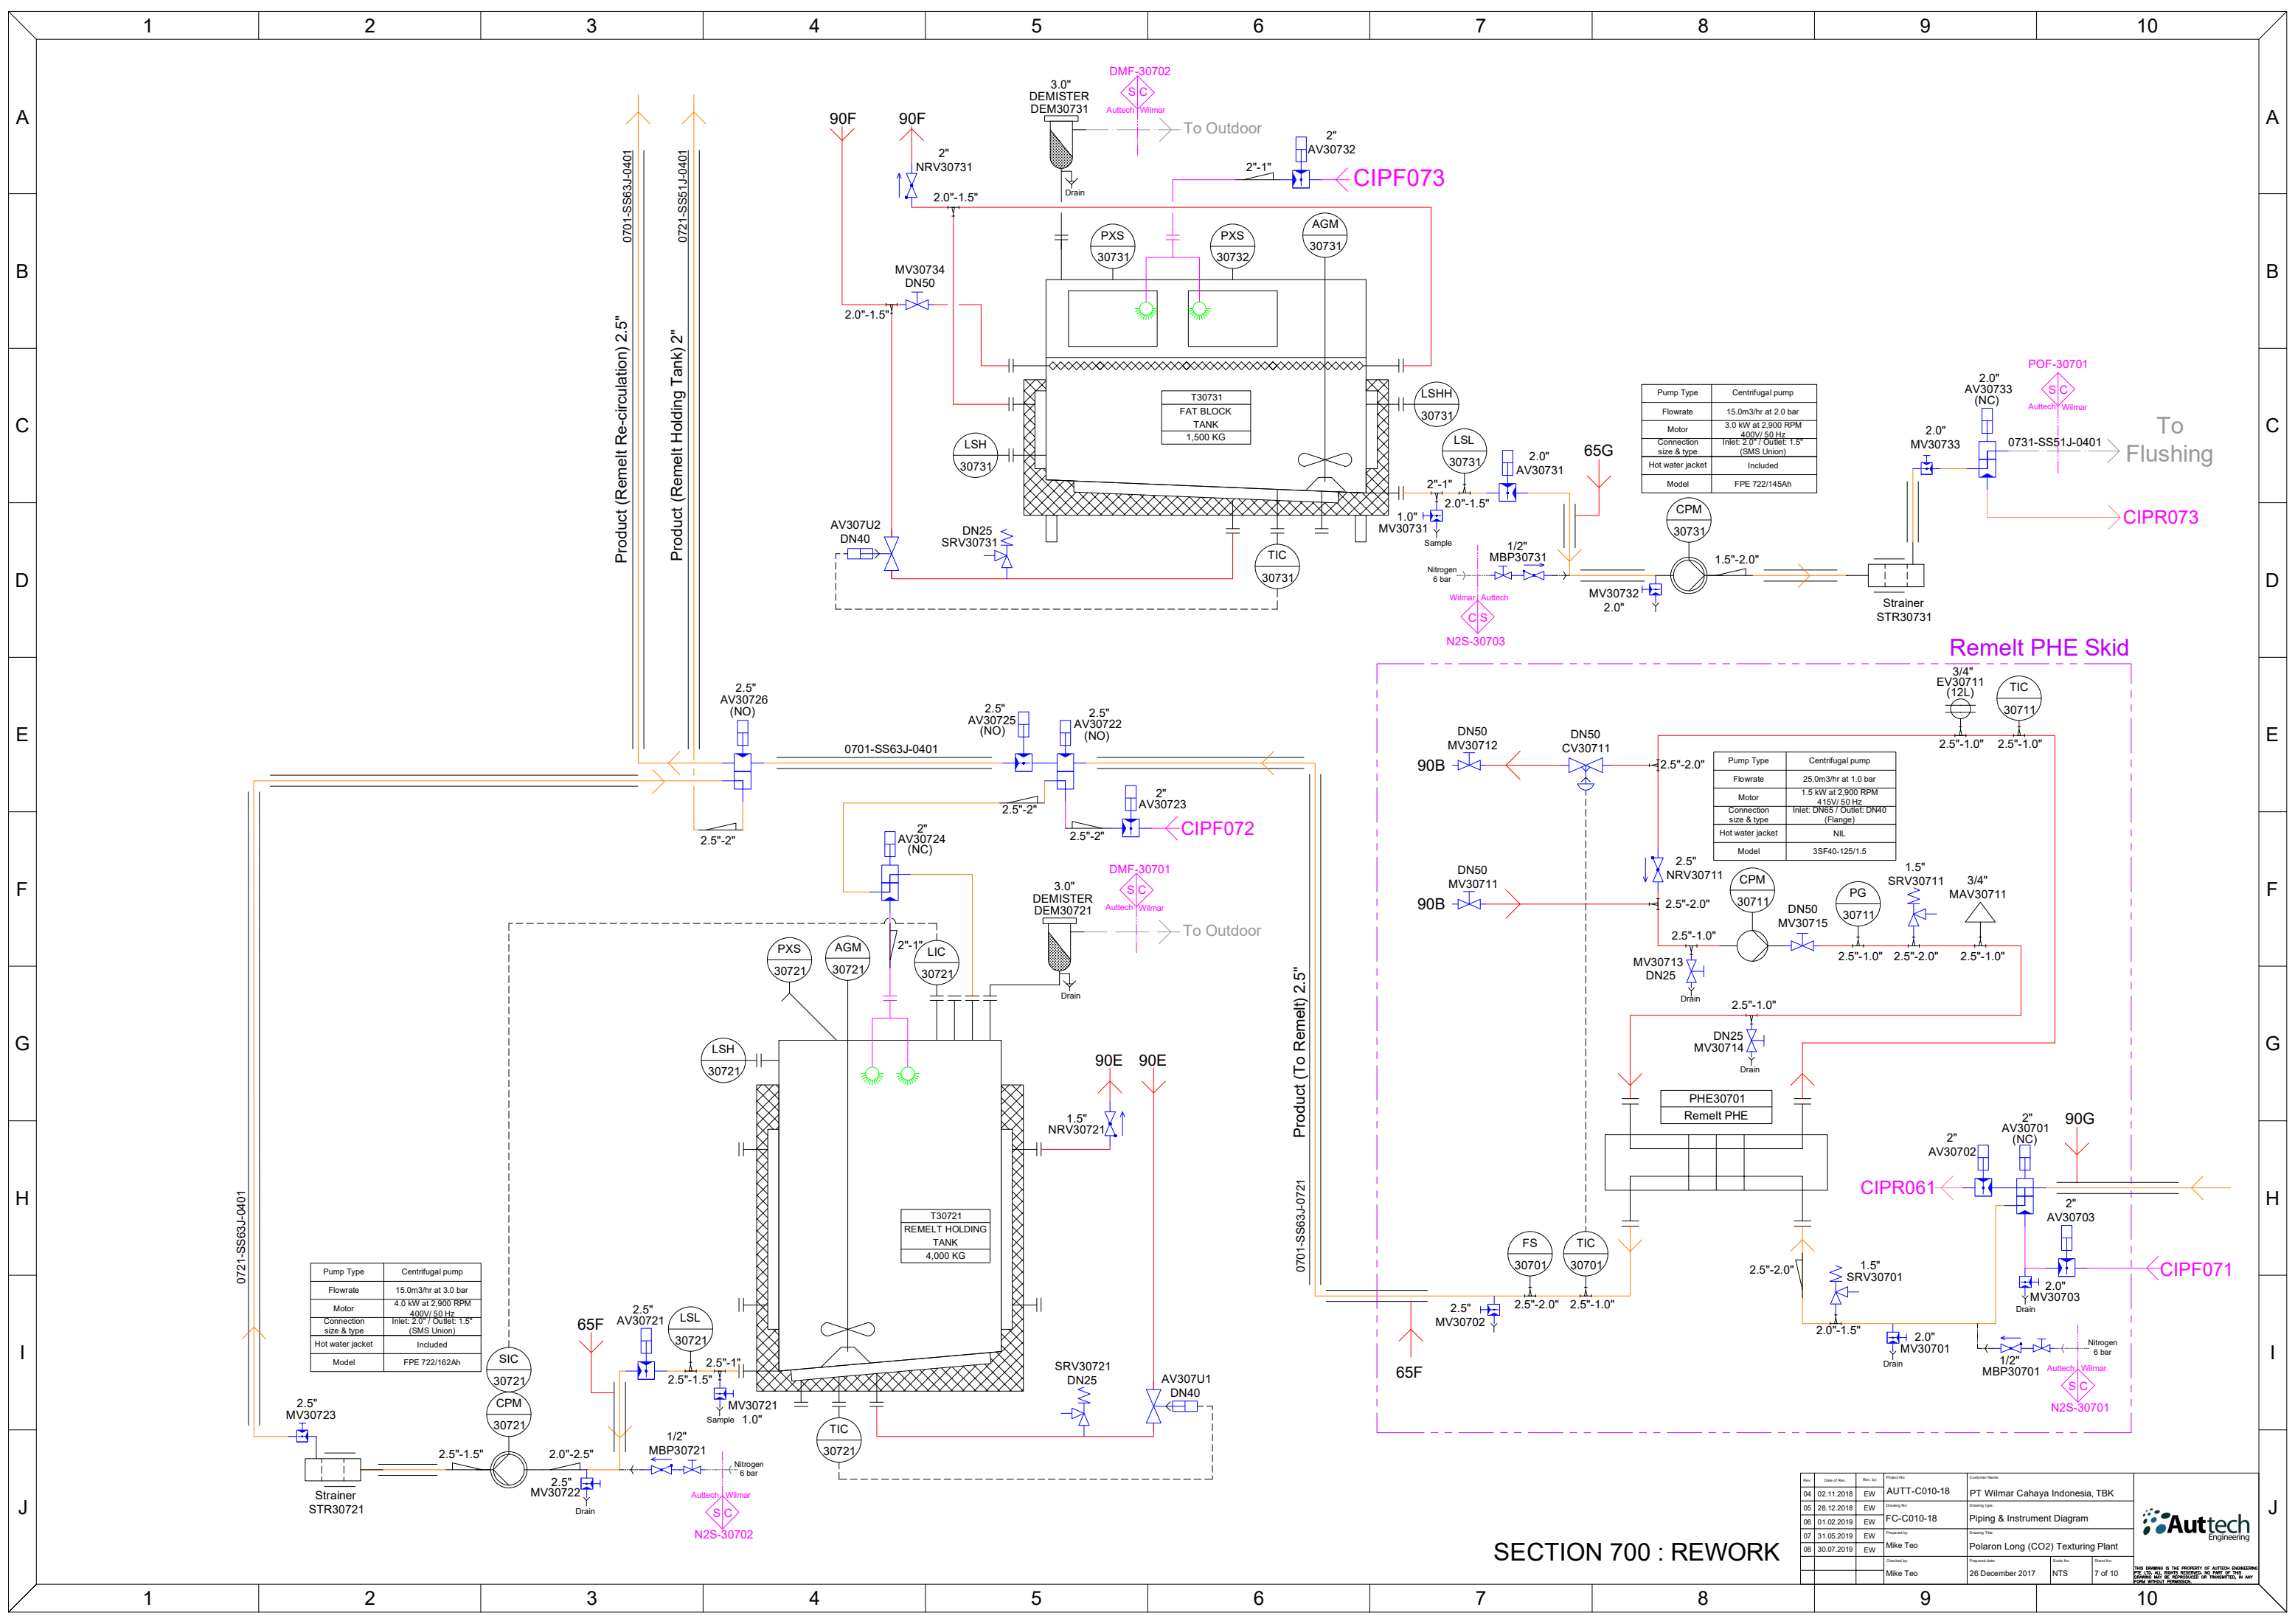

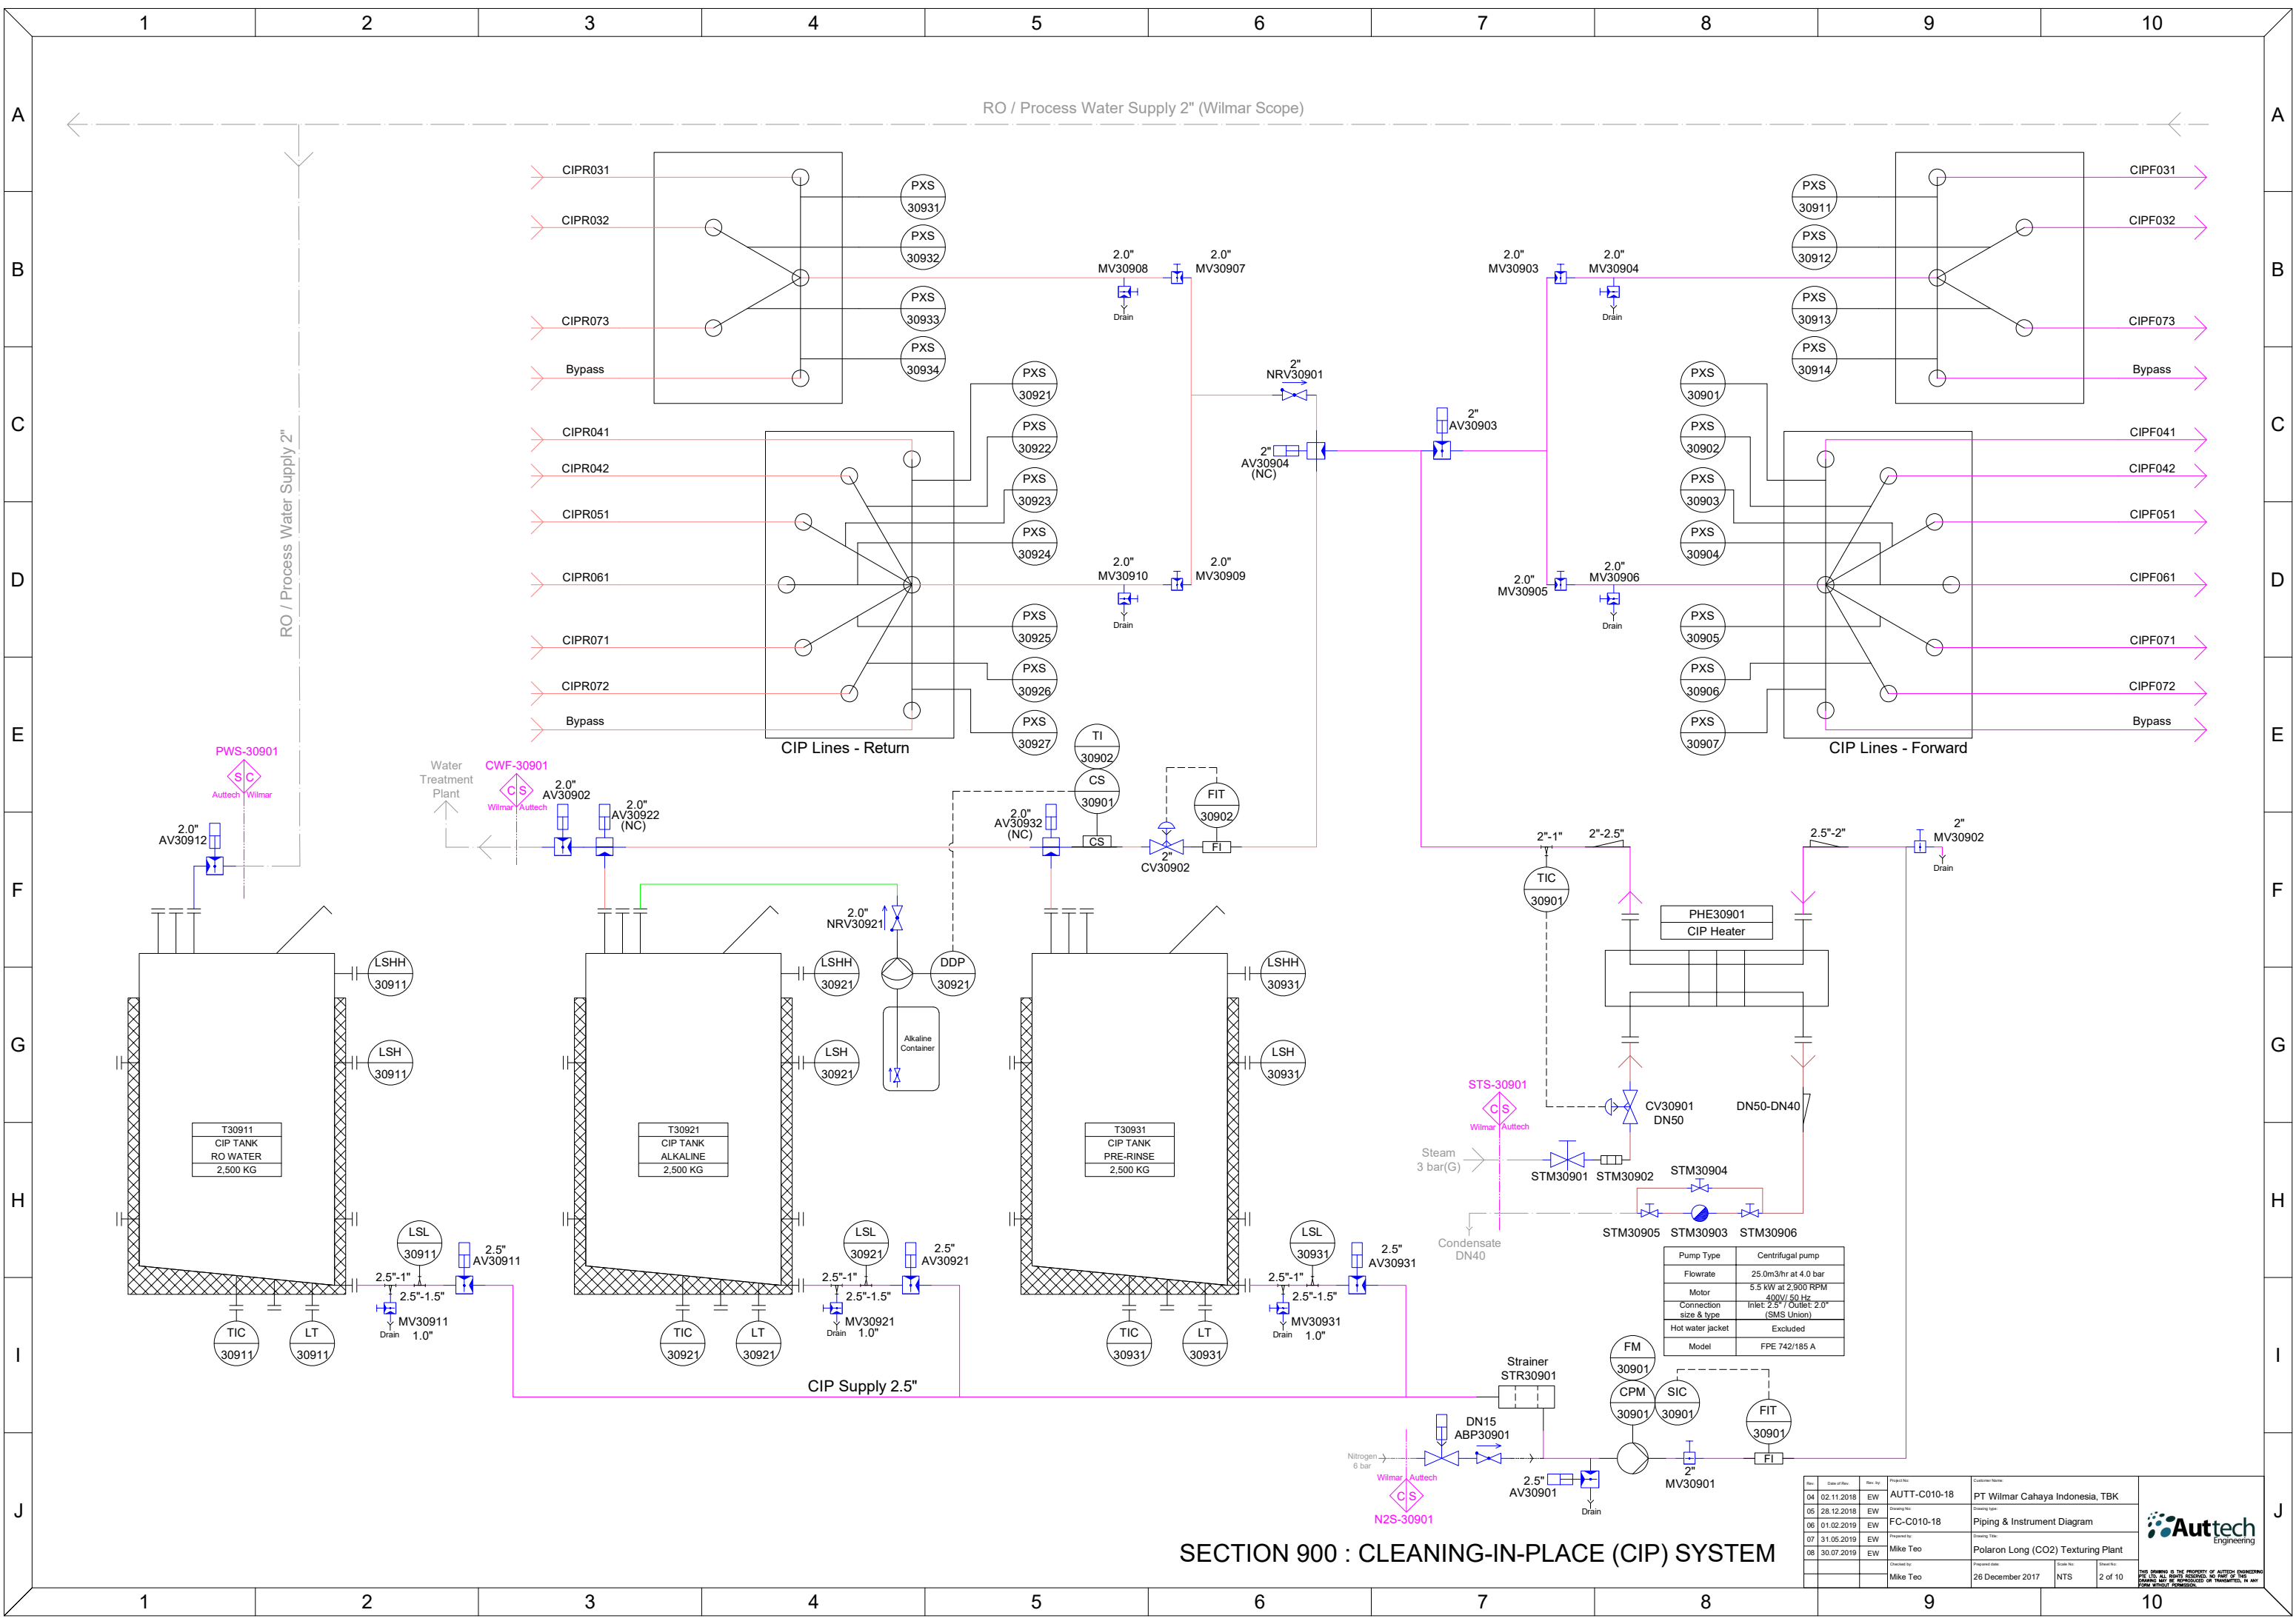

SECTION 900 : CLEANING-IN-PLACE (CIP) SYSTEM

Rev.	Date of Rev.	Rev. by	Project No.	Customer Name
04	02.11.2018	EW	AUTT-C010-18	PT Wilmar Cahaya Indonesia, TBK
05	28.12.2018	EW		
06	01.02.2019	EW	FC-C010-18	Piping & Instrument Diagram
07	31.05.2019	EW		
08	30.07.2019	EW	Mike Teo	Polaron Long (CO2) Texturing Plant
			Mike Teo	26 December 2017
				NTS
				2 of 10

Auttech
Engineering

THIS DRAWING IS THE PROPERTY OF AUTTECH ENGINEERING. IT IS TO BE USED ONLY FOR THE PROJECT AND SITE SPECIFICALLY IDENTIFIED. ALL RIGHTS RESERVED. NO REPRODUCTION OR TRANSMISSION IN ANY FORM WITHOUT PERMISSION.

