

WE RESERVE ALL RIGHTS IN THIS DOCUMENT AND IN THE INFORMATION CONTAINED THEREIN. REPRODUCTION, USE OR DISCLOSURE TO THIRD PARTIES WITHOUT EXPRESS AUTHORITY IS STRICTLY FORBIDDEN.

1		2		3		4		5		6		7		8	
A															
B															
C															
D															
E															
F															
UniSec Medium Voltage Switchgear PT MULTIMAS NABATI ASAHAN MVD-20 & MVD-21 20kV Boiler Plant SCHEMATIC DIAGRAM SBC-W OUTGOING H02,H08															
				Date Prep. 15.11.2018		PROJECT TITLE				COVER SHEET		Scale		NTS	
				Prepared YR		MV Switchgear for MNA Serang Plant				MVD-20 & MVD-21 20kV Boiler Plant		Customer		PT Multimas Nabati Asahan	
00		Issued for Approval		11.01.19 YR		Checked AW		PT. ABB Sakti Industri				Drawing Nbr.		18.042-MNA-306.03	
Ind.		Revision		Date		Name		Approved AI		Based on: BE318042				Customer Doc. Nbr.	
1		2		3		4		5		6		7		8	
= H02,H08															
& 306															
Sh. 1															
Cont. 27															

WE RESERVE ALL RIGHTS IN THIS DOCUMENT AND IN THE INFORMATION CONTAINED THEREIN. REPRODUCTION, USE OR DISCLOSURE TO THIRD PARTIES WITHOUT EXPRESS AUTHORITY IS STRICTLY FORBIDDEN.

1		2		3		4		5		6		7		8		
A	-BGI31	POSITION SWITCHES SIGNALLING DISCONNECTOR -QBD3 IN OPEN POSITION						-CA	CAPACITORS							A
	-BGI32	POSITION SWITCHES SIGNALLING DISCONNECTOR -QBD3 IN CLOSED POSITION						-CA1	CAPACITOR FOR FRONT VENTILATOR							
	-BGI33	POSITION SWITCHES SIGNALLING DISCONNECTOR -QBD3 IN OPEN POSITION AND NOT IN OPERATION (OPERATING LEVER NOT INSERTED)						-CA2	CAPACITOR FOR REAR VENTILATOR							
	-BGI41...	POSITION SWITCHES SIGNALLING SWITCH-DISCONNECTOR -QBS CLOSED IN FEEDER POSITION						-EA1	LIGHTING LAMP LOCATED IN L.V. INSTRUMENT COMPARTMENT.							
	-BGI42	POSITION SWITCHES SIGNALLING SWITCH-DISCONNECTOR -QBS IN OPEN POSITION						-EA2	LIGHTING LAMP LOCATED IN CABLE COMPARTMENT							
	-BGI43...	POSITION SWITCHES SIGNALLING SWITCH-DISCONNECTOR -QBS CLOSED IN EARTH POSITION						-EA3	LIGHTING LAMP LOCATED IN OPERATING MECHANISM ENCLOSURE							
B	-BGI42	POSITION SWITCHES SIGNALLING SWITCH-DISCONNECTOR -QBS IN OPEN POSITION						-EA4	LIGHTING LAMP LOCATED IN CIRCUIT BREAKER COMPARTIMENT							B
	-BGI51	POSITION SWITCHES SIGNALLING DISCONNECTOR -QBD5 CLOSED IN FEEDER POSITION						-EB1	HEATER LOCATED IN CABLE COMPARTMENT							
	-BGI52	POSITION SWITCHES SIGNALLING DISCONNECTOR -QBD5 IN OPEN POSITION						-EB2	HEATER LOCATED IN CIRCUIT-BREAKER COMPARTMENT							
	-BGI53	POSITION SWITCHES SIGNALLING DISCONNECTOR -QBD5 CLOSED IN EARTH POSITION						-EB3	HEATER LOCATED IN MOTOR CABINET							
	-BGK	POSITION SWITCH OF KEY LOCK						-EB4	HEATER FOR VENTILATION TEST							
	-BGL1	POSITION SWITCH OF ELECTROMECHANICAL LOCK -RLE1						-EB5	HEATER LOCATED IN L.V. INSTRUMET COMPARTMENT.							
	-BGS1...-BGS4	POSITION SWITCHES OF CIRCUIT-BREAKER SPRINGS						-EB7	HEATERS LOCATED IN LEFT SIDE OF THE OPERATING MECHANISM ENCLOSURE							
	-BGS5	PROXIMITY SWITCH SIGNALLING SPRINGS IN CHARGED POSITION						-EB8	HEATERS LOCATED IN RIGHT SIDE OF THE OPERATING MECHANISM ENCLOSURE							
C	-BGT1	POSITION SWITCHES ON TRUCK SIGNALLING TRUCK IN SERVICE POSITION						-FA1	SURGE ARRESTER LOCATED ON PHASE L1							C
	-BGT2	POSITION SWITCHES ON TRUCK SIGNALLING TRUCK IN TEST POSITION						-FA2	SURGE ARRESTER LOCATED ON PHASE L2							
	-BGT3	POSITION SWITCH ON TRUCK SIGNALLING TRUCK NOT IN ISOLATING TRAVEL POSITION						-FA3	SURGE ARRESTER LOCATED ON PHASE L3							
	-BGT4	POSITION SWITCHES ON SWITCHGEAR SIGNALLING TRUCK IN SERVICE POSITION						-FCD	FUSE-DISCONNECTORS FOR PROTECTION OF AUXILIARY CIRCUITS							
	-BGT5	POSITION SWITCHES ON SWITCHGEAR SIGNALLING TRUCK IN TEST POSITION						-FCF1	MEDIUM VOLTAGE FUSE LOCATED ON PHASE L1							
	-BGT6	POSITION SWITCHES SIGNALLING V.T. TRUCK IN SERVICE POSITION						-FCF2	MEDIUM VOLTAGE FUSE LOCATED ON PHASE L2							
	-BGT7	POSITION SWITCHES SIGNALLING V.T. TRUCK IN TEST POSITION						-FCF3	MEDIUM VOLTAGE FUSE LOCATED ON PHASE L3							
	-BGT8	POSITION SWITCHES SIGNALLING EARTHING TRUCK IN SERVICE POSITION						-FCM1	MINIATURE CIRCUIT-BREAKER FOR PROTECTION OF SPRINGS CHARGING MOTOR ON MAIN CIRCUIT-BREAKER							
	-BGT11	PROXIMITY SWITCH SIGNALLING TRUCK IN SERVICE POSITION						-FCM2...-FCM10	MINIATURE CIRCUIT-BREAKERS FOR PROTECTION OF AUXILIARY CIRCUITS							
	-BGT12	PROXIMITY SWITCH SIGNALLING TRUCK IN TEST POSITION						-FCM11	MINIATURE CIRCUIT-BREAKER FOR PROTECTION OF VENTILATOR -MV1							
	-BGV1	POSITION SWITCH OF FRONT VENTILATOR						-FCM12	MINIATURE CIRCUIT-BREAKER FOR PROTECTION OF VENTILATOR -MV2							
	-BGV2	POSITION SWITCH OF REAR VENTILATOR						-FCM13	MINIATURE CIRCUIT-BREAKER FOR PROTECTION OF VENTILATOR -MV3							
D	-BM	HYGROSTAT						-FCT	THERMAL OVERLOAD RELEASES							D
	-BPA4	PRESSURE SWITCH LOCATED IN CABLE COMPARTMENT FOR DETECTION OF INTERNAL ARCING						-GA	GENERATORS							
	-BPA5	PRESSURE SWITCH LOCATED IN CIRCUIT-BREAKER OR IN UPPER VT COMPARTMENT FOR DETECTION OF INTERNAL ARCING						-GQ1	FRONT VENTILATOR							
	-BPA6	PRESSURE SWITCH LOCATED IN BUSBAR OR IN BUSBAR AND CIRCUIT-BREAKER COMPARTMENT FOR DETECTION OF INTERNAL ARCING						-GQ2	REAR VENTILATOR							
	-BPA7	PRESSURE SWITCH LOCATED IN VOLTAGE TRANSFORMER ISOLATING COMPARTMENT FOR DETECTION OF INTERNAL ARCING						-GQ3	VENTILATOR LOCATED ON CIRCUIT-BREAKER TRUCK							
	-BPS1	PRESSURE SWITCH LOCATED ON CIRCUIT-BREAKER OR ON POLE OF PHASE L1 OF CIRCUIT-BREAKER						-KFA1	AUXILIARY RELAY SIGNALLING LOW GAS PRESSURE							
	-BPS2	PRESSURE SWITCH LOCATED ON CIRCUIT-BREAKER POLE OF PHASE L2						-KFA2	AUXILIARY RELAY SIGNALLING INSUFFICIENT GAS PRESSURE							
	-BPS3	PRESSURE SWITCH LOCATED ON CIRCUIT-BREAKER POLE OF PHASE L3						-KFA3...-KFA9	AUXILIARY RELAYS OR CONTACTORS							
	-BR	FLAME DETECTORS, SMOKE DETECTORS						-KFC	CLOSING RELAYS OR CONTACTORS							
E	-BT	THERMOSTAT						-KFI	INTEGRATED CIRCUITS							E
	-BT1	THERMOSTAT FOR DE-ENERGIZATION OF VENTILATORS						-KFL	LOCKOUT RELAY							
	-BT2	THERMOSTAT FOR ENERGIZATION OF VENTILATORS						-KFM	MICROPROCESSORS							
	-BT3	THERMOSTAT SIGNALLING HIGH TEMPERATURE ALARM						-KFN	ANTIPUMPING RELAYS							
	-BU	BUCHHOLZ RELAY						-KFO	OPENING RELAYS OR CONTACTORS							
	-BX1	UNIT WITH SENSORS FOR DETECTION OF INTERNAL ARCING						-KFP	PROGRAMMABLE LOGIC CONTROLLERS (PLC)							
	-BX2	ADDITIONAL CURRENT SENSING UNIT FOR DETECTION OF INTERNAL ARCING						-KFR	RECLOSING RELAYS							
	-BZ,-BZ4	MULTIFUNCTION SENSORS						-KFS	SYNCHRONIZING DEVICES							
	-BZ1	COMBINED CURRENT AND VOLTAGE SENSOR, LOCATED ON PHASE L1						-KFT	AUXILIARY TIME RELAYS, DELAY ELEMENTS							
	-BZ2	COMBINED CURRENT AND VOLTAGE SENSOR, LOCATED ON PHASE L2						-KFZ	CONTROLLERS							
	-BZ3	COMBINED CURRENT AND VOLTAGE SENSOR, LOCATED ON PHASE L3						-MBC	CLOSING RELEASE OF CIRCUIT-BREAKER							
F								-MAD	MOTOR FOR ELECTRICAL OPERATION OF DISCONNECTOR -QBD							F
								-MAD1	MOTOR FOR ELECTRICAL OPERATION OF DICONNECTOR -QBD1							
								-MAD2	MOTOR FOR ELECTRICAL OPERATION OF DICONNECTOR -QBD2							
								-MAD9	MOTOR FOR ELECTRICAL OPERATION OF SWITCH-DISCONNECTOR -QBS							
				Date Prep.	15.11.2018	PROJECT TITLE		ABB	EPMV	REFERENCE DESIGNATIONS		Scale	NTS		= H02,H08	
				Prepared	YR	MV Switchgear for MNA Serang Plant				MVD-20 & MVD-21 20kV Boiler Plant		Customer	PT Multimas Nabati Asahan		& 306	
00	Issued for Approval	11.01.19	YR	Checked	AW			PT. ABB Sakti Industri		SCHEMATIC DIAGRAM		Drawing Nbr.	18.042-MNA-306.03		Sh. 4	
Ind.	Revision	Date	Name	Approved	AI	Based on: BE318042				SBC-W OUTGOING		Customer Doc. Nbr.			Cont. 27	
1		2		3		4		5		6		7		8		

WE RESERVE ALL RIGHTS IN THIS DOCUMENT AND IN THE INFORMATION CONTAINED THEREIN. REPRODUCTION, USE OR DISCLOSURE TO THIRD PARTIES WITHOUT EXPRESS AUTHORITY IS STRICTLY FORBIDDEN.


A	-MAE	MOTOR FOR ELECTRICAL OPERATION OF EARTHING SWITCH -QCE						-QBH	MANUAL CIRCUIT-BREAKERS						
	-MAE1	MOTOR FOR ELECTRICAL OPERATION OF EARTHING SWITCH -QCE1 OR -QCE2						-QBL	LINKS						
	-MAE8	MOTOR FOR ELECTRICAL OPERATION OF EARTHING SWITCH -QCE SUPPLIED TOGETHER WITH SWITCH-DISCONNECTOR -QBS						-QBM	MINIATURE SWITCH-DISCONNECTORS						
	-MAS	MOTOR FOR CIRCUIT-BREAKER SPRINGS CHARGING						-QBS	SWITCH-DISCONNECTORS						
	-MAT	MOTOR FOR ELECTRICAL OPERATION OF TRUCK RACKING-IN/OUT						-QBT	TRUCK						
	-MBC	CLOSING RELEASE OF CIRCUIT-BREAKER						-QCA	EARTHING SWITCH FOR ELIMINATION OF INTERNAL ARCING						
	-MBC4	CLOSING RELEASE OF SWITCH-DISCONNECTOR -QBS						-QCE	EARTHING SWITCH						
	-MBO1	FIRST OPENING RELEASE OF CIRCUIT-BREAKER						-QCE1	EARTHING SWITCH OF BUSBARS (SINGLE BUSBAR SYSTEM) OR OF FRONT BUSBARS (DOUBLE BUSBAR SYSTEM)						
	-MBO2	SECOND OPENING RELEASE OF CIRCUIT-BREAKER						-QCE2	EARTHING SWITCH OF REAR BUSBARS (DOUBLE BUSBAR SYSTEM)						
	-MBO3	OPENING SOLENOID FOR OVERCURRENT RELEASE OF CIRCUIT-BREAKER OR INDIRECT OVERCURRENT RELEASE ON CIRCUIT-BREAKER						-QQ	CLUTCHES						
B	-MBO4	OPENING RELEASE OF SWITCH-DISCONNECTOR -QBS						-RAA	ANTIFERRORESONANCE RESISTOR						
	-MBU	UNDERVOLTAGE RELEASE OF CIRCUIT-BREAKER						-RAD	DIODES						
	-PFB	BLUE SIGNAL LAMPS						-RAI	INDUCTORS						
	-PFF	FLAG RELAYS						-RAR	RESISTORS						
	-PFG	GREEN SIGNAL LAMPS						-RF	FILTERS						
	-PFR	RED SIGNAL LAMPS						-RLE1	ELECTROMECHANICAL LOCK PREVENTING CIRCUIT-BREAKER CLOSING						
	-PFS	SHORT CIRCUIT INDICATORS						-RLE2	ELECTROMECHANICAL LOCK PREVENTING TRUCK RACKING-IN/OUT						
	-PFV	VOLTAGE INDICATORS						-RLE3	ELECTROMECHANICAL LOCK PREVENTING INSERTION OF LEVER FOR CLOSING OPERATION OF EARTHING SWITCH -QCE						
	-PFV1	VOLTAGE INDICATORS ON FEEDER SIDE						-RLE4	ELECTROMECHANICAL LOCK PREVENTING THE DOOR OPENING OPERATION						
	-PFV2	VOLTAGE INDICATORS ON BUSBAR SIDE						-RLE5	ELECTROMECHANICAL LOCK PREVENTING OPERATION OF DISCONNECTOR -QBD						
C	-PFW	WHITE SIGNAL LAMPS						-RLE6	ELECTROMECHANICAL LOCK PREVENTING INSERTION OF LEVER FOR CLOSING OPERATION OF DISCONNECTOR -QBD1						
	-PFX	CROSS INDICATORS, ELECTROMECHANICAL INDICATORS						-RLE7	ELECTROMECHANICAL LOCK PREVENTING INSERTION OF LEVER FOR CLOSING OPERATION OF DISCONNECTOR -QBD2						
	-PFY	YELLOW SIGNAL LAMPS						-RLE8	ELECTROMECHANICAL LOCK PREVENTING INSERTION OF LEVER FOR CLOSING OPERATION OF EARTHING SWITCH -QCE1 OR -QCE2						
	-PGA	AMMETERS						-RLE9	ELECTROMECHANICAL LOCK PREVENTING OPERATION OF SWITCH-DISCONNECTOR -QBS						
	-PGC	COUNTERS						-RLE11	ELECTROMECHANICAL LOCK PREVENTING INSERTION OF LEVER FOR OPERATION OF DISCONNECTOR -QBD4						
	-PGF	FREQUENCYMETERS						-RLE12	ELECTROMECHANICAL LOCK PREVENTING INSERTION OF LEVER FOR OPERATION OF DISCONNECTOR -QBD5						
	-PGH	HOURMETERS						-SFA	AMMETRIC SWITCHES						
	-PGI	PROTECTION AND CONTROL UNIT: HUMAN MACHINE INTERFACE						-SFC	CONTROL SWITCHES, CLOSING PUSH-BUTTONS						
	-PGI1	HUMAN MACHINE INTERFACE OF ELECTRONIC CONTROLLED CIRCUIT-BREAKER (ON CIRCUIT-BREAKER)						-SFL	LOCKING CONTACTS						
	-PGI2	HUMAN MACHINE INTERFACE FOR ELECTRONIC CONTROLLED CIRCUIT-BREAKER (ON SWITCHGEAR)						-SFO	OPENING PUSH-BUTTONS						
D	-PGJ	ACTIVE ENERGY METERS						-SFR	RESET PUSH-BUTTONS						
	-PGK	REACTIVE ENERGY METERS						-SFS	SELECTOR SWITCHES						
	-PGM	MULTIFUNCTION INDICATORS						-SFT	TEST PUSH-BUTTONS						
	-PGP	POWER-FACTOR METERS						-SFU	UNLOCKING PUSH-BUTTONS						
	-PGQ	VARMETERS						-SFV	VOLTMETRIC SWITCHES						
	-PGS	SYNCHRONOSCOPES						-TA	POWER TRANSFORMERS						
	-PGV	VOLTMETERS						-TB	CONVERTER						
	-PGW	WATTMETERS						-TB1	RECTIFIER FOR FIRST OPENING RELEASE						
	-PJ	ACOUSTICAL SIGNAL DEVICES (BELLS, SIRENS)						-TB2	RECTIFIER FOR SECOND OPENING RELEASE						
	-QAB	CIRCUIT-BREAKERS						-TB3	RECTIFIER FOR CLOSING RELEASE						
E	-QAC	CONTACTORS (FOR POWER)						-TB4	RECTIFIER FOR ELECTROMECHANICAL LOCK PREVENTING CIRCUIT-BREAKER CLOSING						
	-QBD	DISCONNECTORS						-TB5	RECTIFIER FOR ELECTROMECHANICAL LOCK PREVENTING TRUCK RACKING-IN/OUT						
	-QBD1	FRONT BUSBAR DISCONNECTORS (DOUBLE BUSBAR SYSTEM)						-TB6	RECTIFIER FOR UNDERVOLTAGE RELEASE						
	-QBD2	REAR BUSBAR DISCONNECTORS (DOUBLE BUSBAR SYSTEM)						-TB7	ERECTIFIER FOR INDIRECT OVERCURRENT RELEASE ON CIRCUIT-BREAKER						
	-QBD3	FEEDER DISCONNECTORS (DOUBLE BUSBAR SYSTEM)													
	-QBD4	TWO-WAY DISCONNECTOR													
	-QBD5	TWO-WAY DISCONNECTOR ON BUSBAR RISER													
1		2		3		4		5		6		7		8	
				Date Prep.	15.11.2018	PROJECT TITLE MV Switchgear for MNA Serang Plant		ABB	EPMV	REFERENCE DESIGNATIONS MVD-20 & MVD-21 20kV Boiler Plant		Scale	NTS		= H02,H08
				Prepared	YR							Customer	PT Multimas Nabati Asahan		& 306
00	Issued for Approval	11.01.19	YR	Checked	AW			PT. ABB Sakti Industri		SCHEMATIC DIAGRAM SBC-W OUTGOING		Drawing Nbr.	18.042-MNA-306.03		Sh. 5
Ind.	Revision	Date	Name	Approved	AI	Based on:	BE318042					Customer Doc. Nbr.			Cont. 27

WE RESERVE ALL RIGHTS IN THIS DOCUMENT AND IN THE INFORMATION CONTAINED THEREIN. REPRODUCTION, USE OR DISCLOSURE TO THIRD PARTIES WITHOUT EXPRESS AUTHORITY IS STRICTLY FORBIDDEN.


1		2		3		4		5		6		7		8		
A	-TFA	ACTIVE POWER TRANSDUCERS						-XDI1	TERMINAL BLOCK FOR INTERCONNECTIONS OF CONTROL CIRCUITS							A
	-TFC	CURRENT TRANSDUCERS						-XDI2	TERMINAL BLOCK FOR INTERCONNECTIONS OF CIRCUITS OF MOTOR FOR CIRCUIT-BREAKER SPRINGS CHARGING							
	-TFF	FREQUENCY TRANSDUCERS						-XDI3	TERMINAL BLOCK FOR INTERCONNECTIONS OF CIRCUITS OF MOTOR FOR SWITCH-DISCONNECTOR OPERATION							
	-TFJ	ACTIVE ENERGY TRANSDUCERS						-XDI4	TERMINAL BLOCK FOR INTERCONNECTIONS OF A.C. AUXILIARY CIRCUITS							
	-TFK	REACTIVE ENERGY TRANSDUCERS						-XDI6	TERMINAL BLOCK FOR INTERCONNECTION (CONNECTION BETWEEN PANELS) OF VOLTAGE CIRCUITS							
B	-TFM	MULTIFUNCTION TRANSDUCERS						-XDI7	TERMINAL BLOCK FOR INTERCONNECTION OF MOD-BUS							B
	-TFP	POWER-FACTOR TRANSDUCERS						-XDI8	TERMINAL BLOCK FOR INTERCONNECTIONS OF CURRENT CIRCUITS							
	-TFQ	REACTIVE POWER TRANSDUCERS						-XDI9	TERMINAL BLOCK FOR SPECIAL USE							
	-TFS	SIGNAL CONVERTERS						-XDJ	TERMINAL BLOCK FOR AUXILIARY CIRCUITS OF DISCONNECTORS -QBD							
	-TFV	VOLTAGE TRANSDUCERS						-XDJ1	TERMINAL BLOCK FOR AUXILIARY CIRCUITS OF SWITCH-DISCONNECTOR -QBS							
C	-WA	BUSBARS						-XDM	SEALABLE TERMINAL BLOCK FOR MEASUREMENT							C
	-WBC	POWER CABLES						-XDS	CURRENT SOCKETS							
	-WE	EARTHING CABLES FOR L.V. INSTRUMENT COMPARTMENT.						-XDT	TERMINAL BLOCK FOR POSITION CONTACTS OF TRUCK AND OF CONNECTOR -XDB							
	-WGC	CONTROL CABLES						-XDU	CONNECTOR FOR ISOLATION OF CIRCUITS OF LOWER VOLTAGE TRANSFORMER TRUCK							
	-WGS	COMMUNICATION CABLES (SHIELDED TWISTED PAIRS)						-XDU1	TERMINAL BLOCK FOR CIRCUITS OF LOWER VOLTAGE TRANSFORMER TRUCK							
D	-WH	OPTICAL FIBRES						-XDV	TERMINAL BLOCK FOR CIRCUITS OF VOLTAGE TRANSFORMERS							D
	-XDA	TERMINAL BLOCK FOR CIRCUITS OF CURRENT TRANSFORMERS						-XDV1	CONNECTOR FOR CIRCUITS OF VOLTAGE TRANSFORMERS LOCATED ON PHASE L1							
	-XDA1	CONNECTOR FOR CIRCUITS OF CURRENT TRANSFORMERS LOCATED ON PHASE L1						-XDV2	CONNECTOR FOR CIRCUITS OF VOLTAGE TRANSFORMERS LOCATED ON PHASE L2							
	-XDA2	CONNECTOR FOR CIRCUITS OF CURRENT TRANSFORMERS LOCATED ON PHASE L2						-XDV3	CONNECTOR FOR CIRCUITS OF VOLTAGE TRANSFORMERS LOCATED ON PHASE L3							
	-XDA3	CONNECTOR FOR CIRCUITS OF CURRENT TRANSFORMERS LOCATED ON PHASE L3						-XDV4	CONNECTOR FOR CIRCUITS OF ANTIFERRORESONANCE RESISTOR							
E	-XDA5	CONNECTOR FOR CIRCUITS OF NEUTRAL (RESIDUAL) CURRENT TRANSFORMER						-XDX	SUPPORT TERMINAL BLOCK							E
	-XDA8	CONNECTOR FOR ISOLATION OF CIRCUIT-BREAKER (OR UPPER VOLTAGE TRANSFORMER TRUCK) AUXILIARY CIRCUITS						-XE1	EARTHING TERMINAL BLOCKS FOR LV COMPARTMENT, LEFT SIDE							
	-XDB1	CONNECTOR FOR AUXILIARY CIRCUITS OF CIRCUIT-BREAKER (OR UPPER VOLTAGE TRANSFORMER TRUCK)						-XE2	EARTHING TERMINAL BLOCKS FOR LV COMPARTMENT, RIGHT SIDE							
	-XDB2	CONNECTOR FOR ADDITIONAL AUXILIARY CIRCUITS OF CIRCUIT-BREAKER						-XE5	EARTHING TERMINAL BLOCKS FOR MV COMPARTMENT, VOLTAGE INDICATOR SIDE							
	-XDB10...-XDB89	CONNECTOR FOR CIRCUIT-BREAKER INTERNAL CIRCUITS						-XE6	EARTHING TERMINAL BLOCKS FOR MV COMPARTMENT, REAR BOTTOM SIDE							
F	-XDB7	CONNECTOR FOR TRUCK POSITION CONTACTS						-XE7	EARTHING TERMINAL BLOCKS FOR MV COMPARTMENT, LEFT SIDE							F
	-XDB91	CONNECTOR FOR OPENING RELEASE CIRCUITS OF SWITCH-DISCONNECTOR						-XE8	EARTHING TERMINAL BLOCKS FOR MV COMPARTMENT, FRONT BOTTOM SIDE							
	-XDB92	CONNECTOR FOR CLOSING RELEASE CIRCUITS OF SWITCH-DISCONNECTOR						-XE9	EARTHING TERMINAL BLOCK FOR TRANSFORMERS IN BUSBAR COMPARTMENT							
	-XDB93	CONNECTOR FOR POSITION SWITCHES OF SWITCH-DISCONNECTOR														
	-XDB95	CONNECTOR FOR CIRCUITS OF EARTHING SWITCH LOCKING MAGNET														
G	-XDC	CUSTOMER TERMINAL BLOCK														G
	-XDC1	CUSTOMER TERMINAL BLOCK FOR AUXILIARY CIRCUITS OF CIRCUIT BREAKER														
	-XDC2	CUSTOMER TERMINAL BLOCK FOR AUXILIARY CIRCUITS OF SWITCH-DISCONNECTOR														
	-XDC3	CUSTOMER TERMINAL BLOCK FOR AUXILIARY CIRCUITS OF PROTECTION RELAY AND MULTIFUNCTION UNIT														
	-XDC4	CUSTOMER TERMINAL BLOCK FOR AUXILIARY CIRCUITS OF VOLTAGE TRANSFORMERS														
H	-XDC5	CUSTOMER TERMINAL BLOCK FOR AUXILIARY CIRCUITS OF MINIATURE CIRCUIT BREAKER														H
	-XDE	TERMINAL BLOCK FOR AUXILIARY CIRCUITS OF EARTHING SWITCH -QCE														
	-XDE1	TERMINAL BLOCK FOR INTERNAL CIRCUITS OF EARTHING SWITCH -QCE														
	-XDE2	TERMINAL BLOCK FOR AUXILIARY CIRCUITS OF EARTHING SWITCH -QCE1 OR -QCE2														
	-XDE3	TERMINAL BLOCK FOR INTERNAL CIRCUITS OF EARTHING SWITCH -QCE1 OR -QCE2														
I	-XDF	TERMINAL BLOCK FOR AUXILIARY CIRCUITS OF FORCED COOLING VENTILATORS														I
	-XDF1	CONNECTOR FOR ISOLATION OF CIRCUITS OF FRONT VENTILATOR														
	-XDF2	CONNECTOR FOR REAR VENTILATOR CIRCUITS														
	-XDF3	CONNECTOR FOR FRONT VENTILATOR CIRCUITS														
	-XDH	TERMINAL BLOCK FOR VARIOUS CIRCUITS (HEATERS, POSITION SWITCHES DETECTING INTERNAL ARCING, ETC.)														
J	-XDI	TERMINAL BLOCK FOR INTERCONNECTION (CONNECTION BETWEEN PANELS)														J

				Date Prep.	15.11.2018	PROJECT TITLE MV Switchgear for MNA Serang Plant				REFERENCE DESIGNATIONS MVD-20 & MVD-21 20kV Boiler Plant		Scale	NTS		= H02,H08
				Prepared	YR							Customer	PT Multimas Nabati Asahan		& 306
00	Issued for Approval	11.01.19	YR	Checked	AW							Drawing Nbr.	18.042-MNA-306.03		Sh. 6
Ind.	Revision	Date	Name	Approved	AI	Based on: BE318042		PT. ABB Sakti Industri		SCHEMATIC DIAGRAM SBC-W OUTGOING		Customer Doc. Nbr.			Cont. 27


1		2		3		4		5		6		7		8	
---	--	---	--	---	--	---	--	---	--	---	--	---	--	---	--

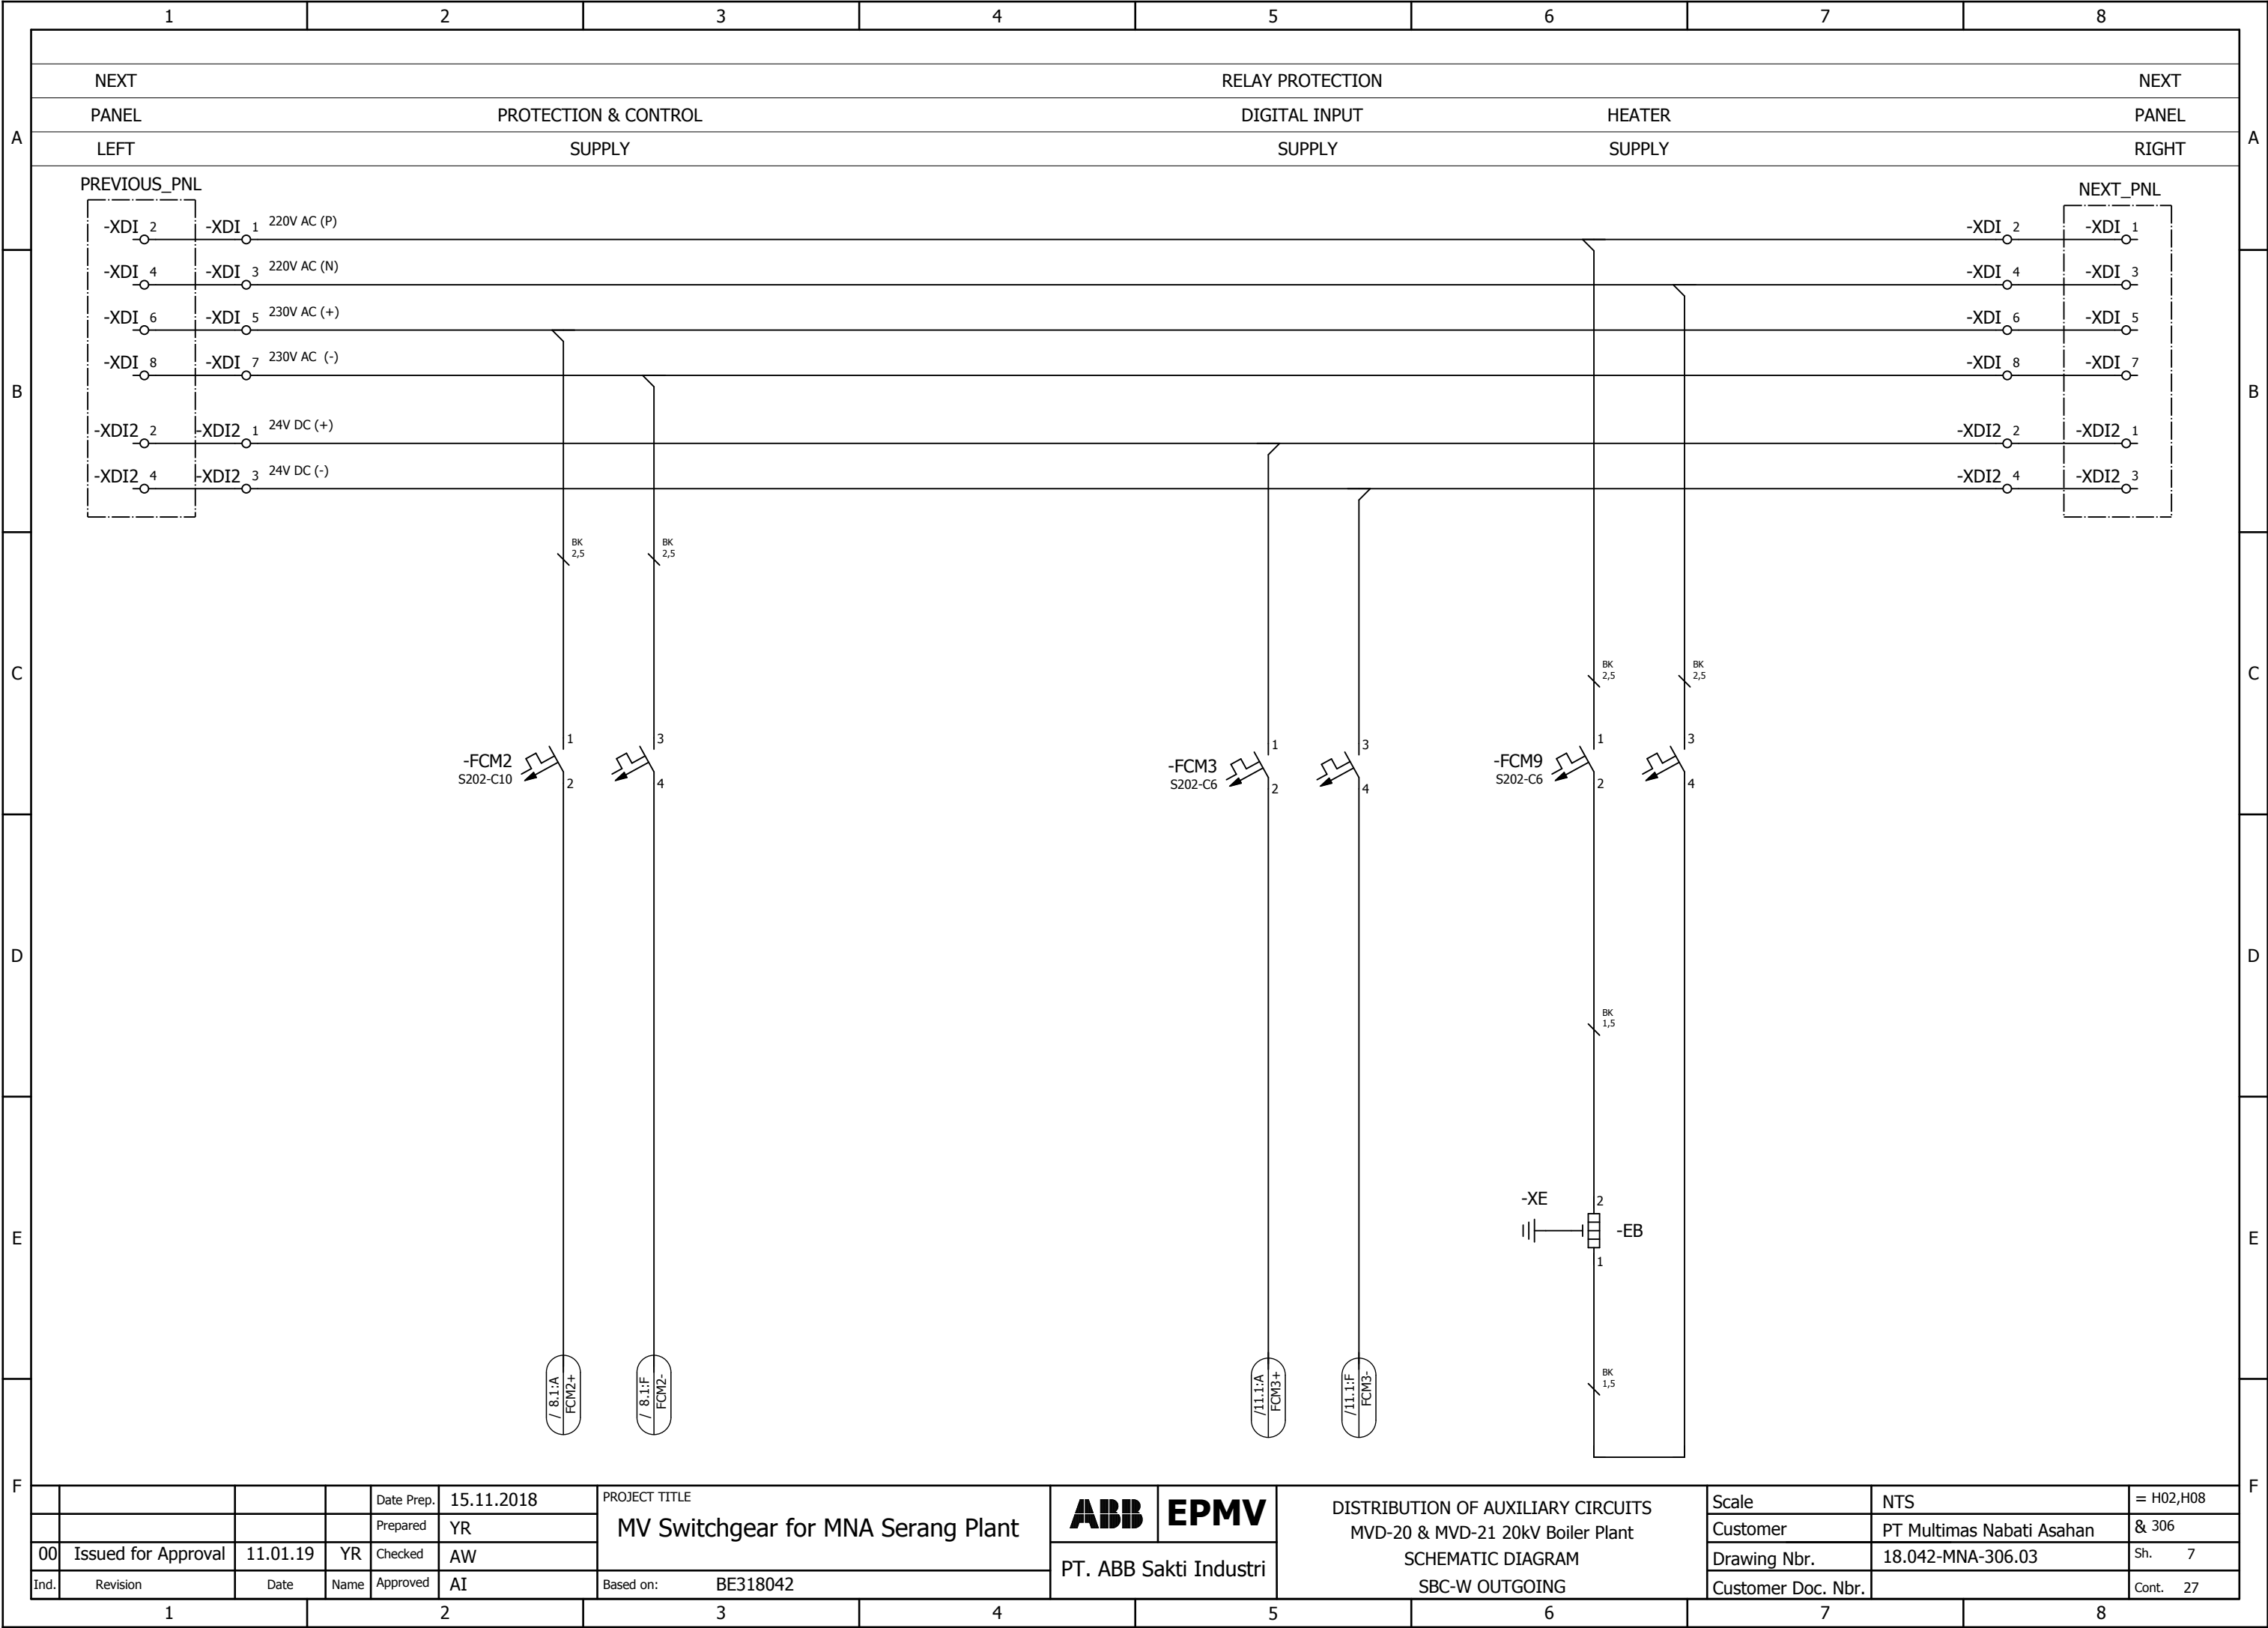

WE RESERVE ALL RIGHTS IN THIS DOCUMENT AND IN THE INFORMATION CONTAINED THEREIN. REPRODUCTION, USE OR DISCLOSURE TO THIRD PARTIES WITHOUT EXPRESS AUTHORITY IS STRICTLY FORBIDDEN.

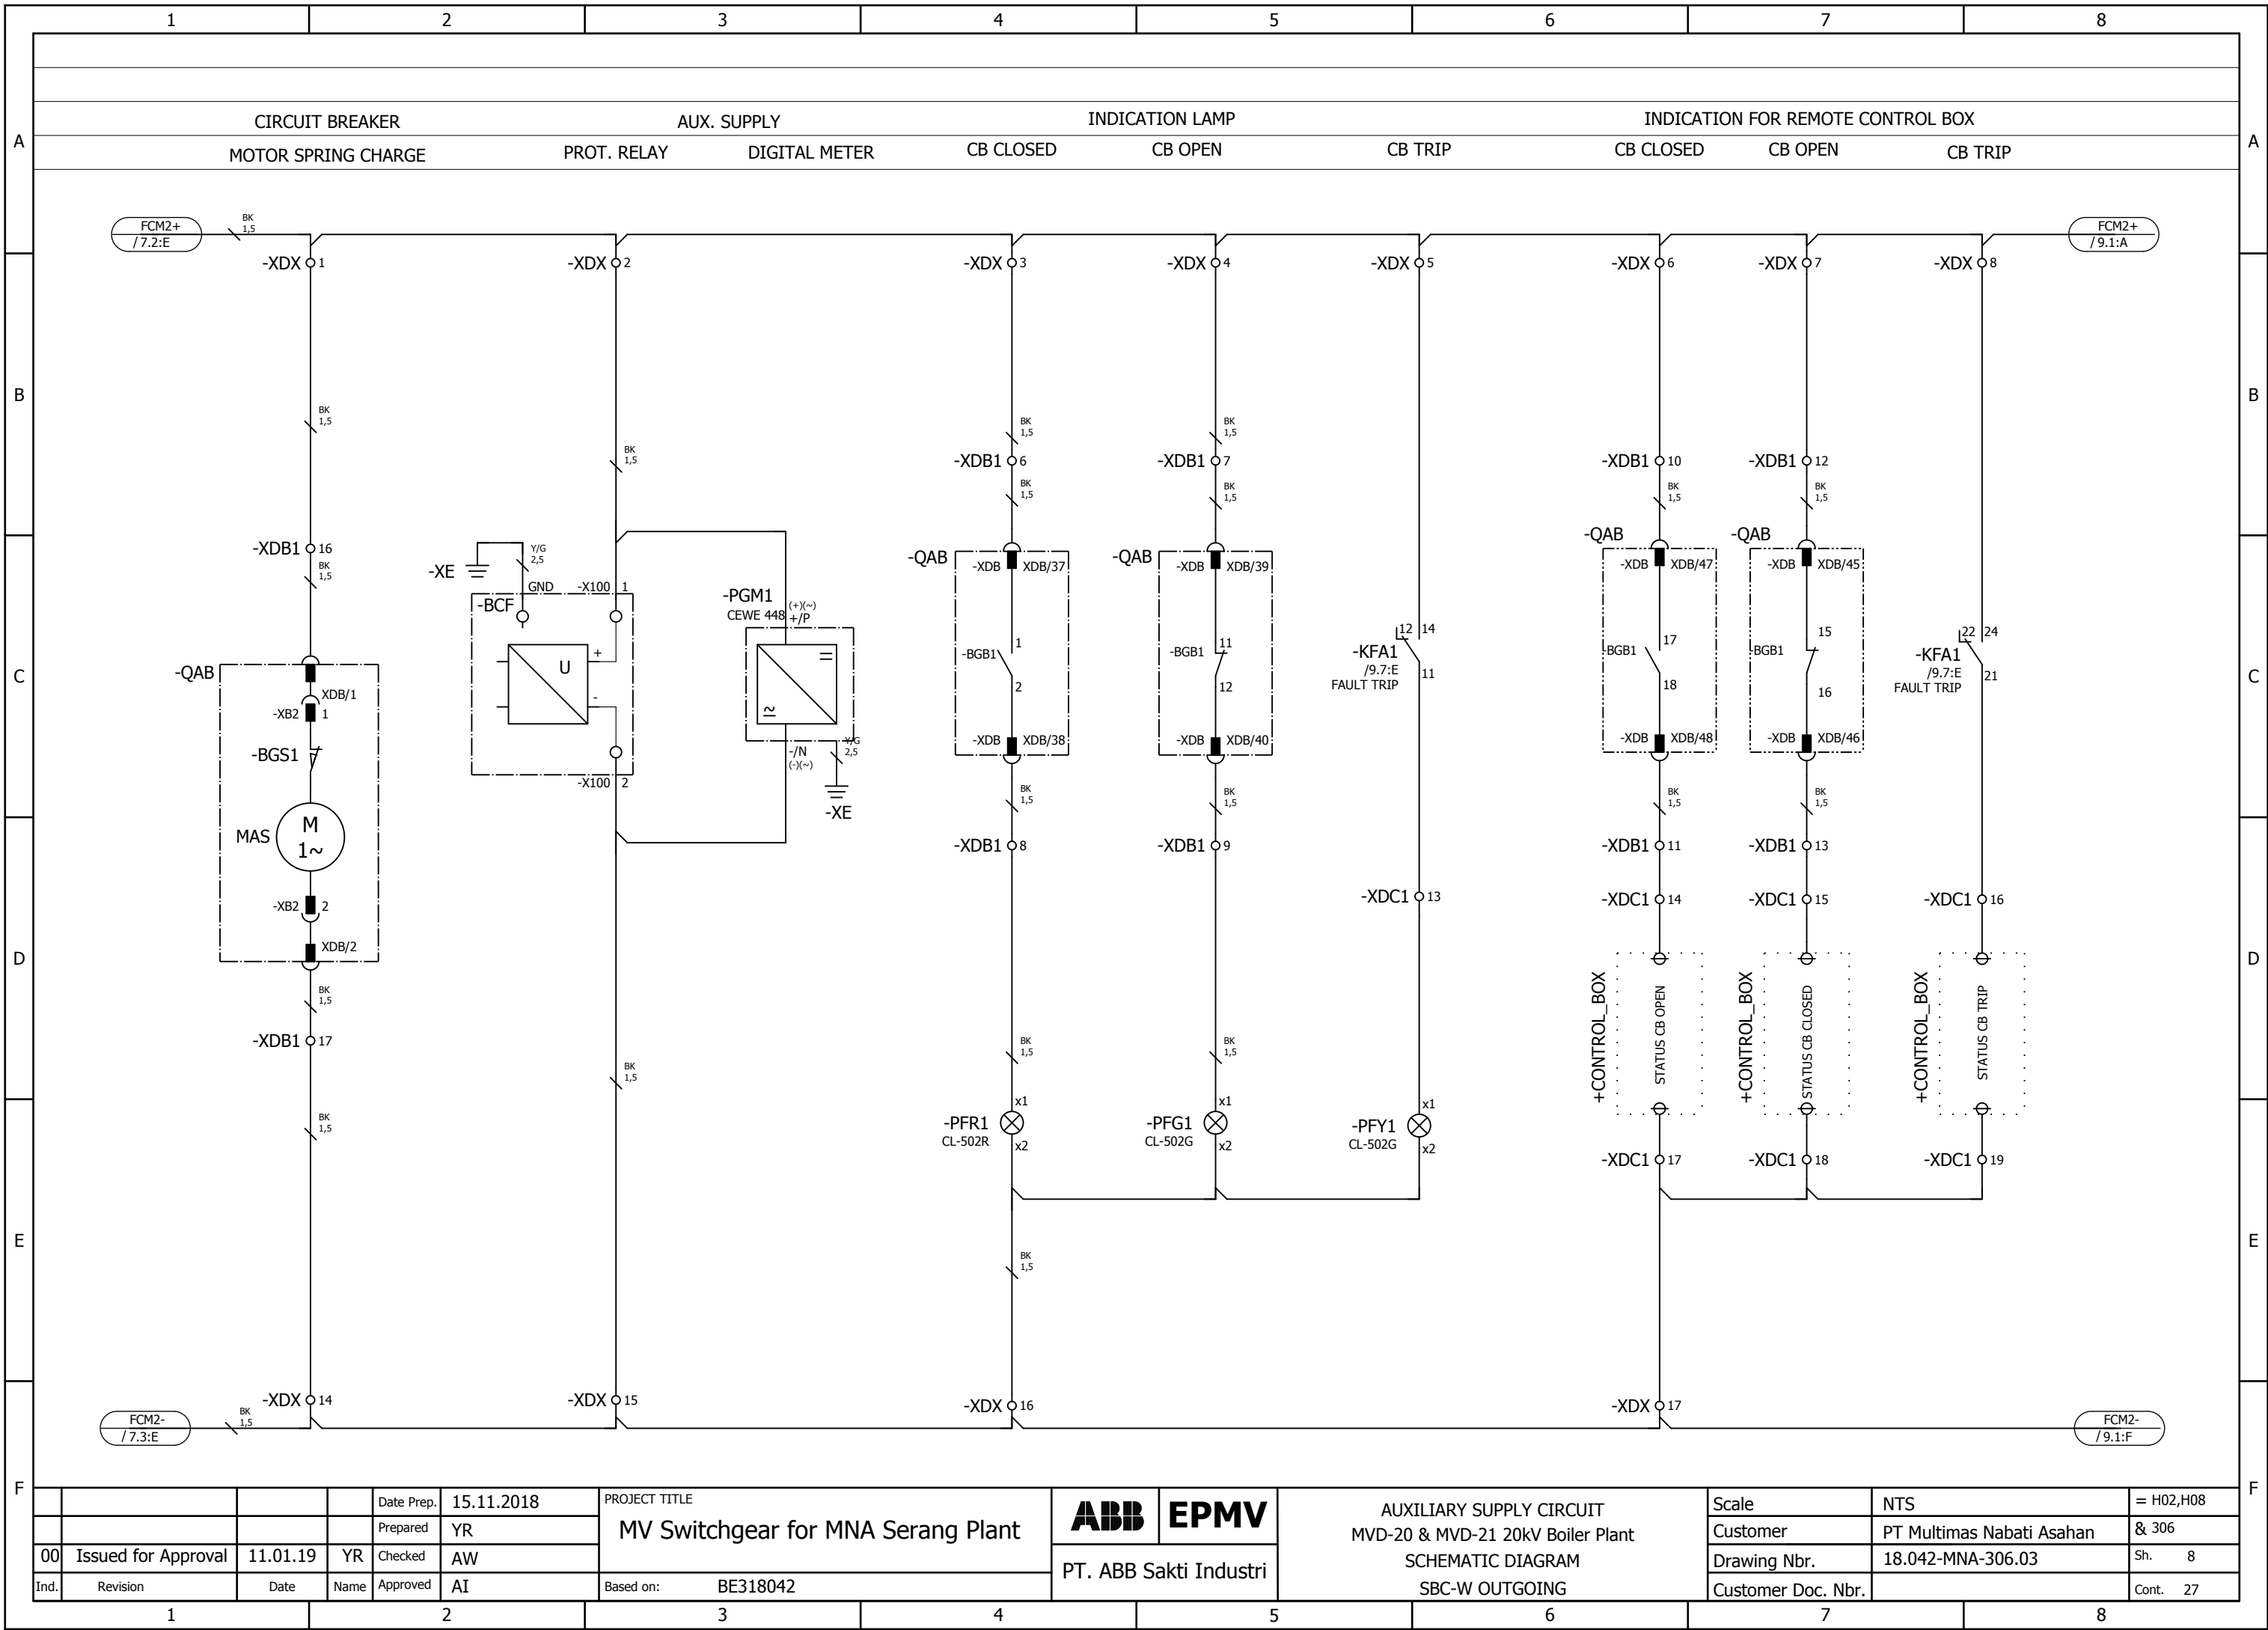


WE RESERVE ALL RIGHTS IN THIS DOCUMENT AND IN THE INFORMATION CONTAINED THEREIN. REPRODUCTION, USE OR DISCLOSURE TO THIRD PARTIES WITHOUT EXPRESS AUTHORITY IS STRICTLY FORBIDDEN.

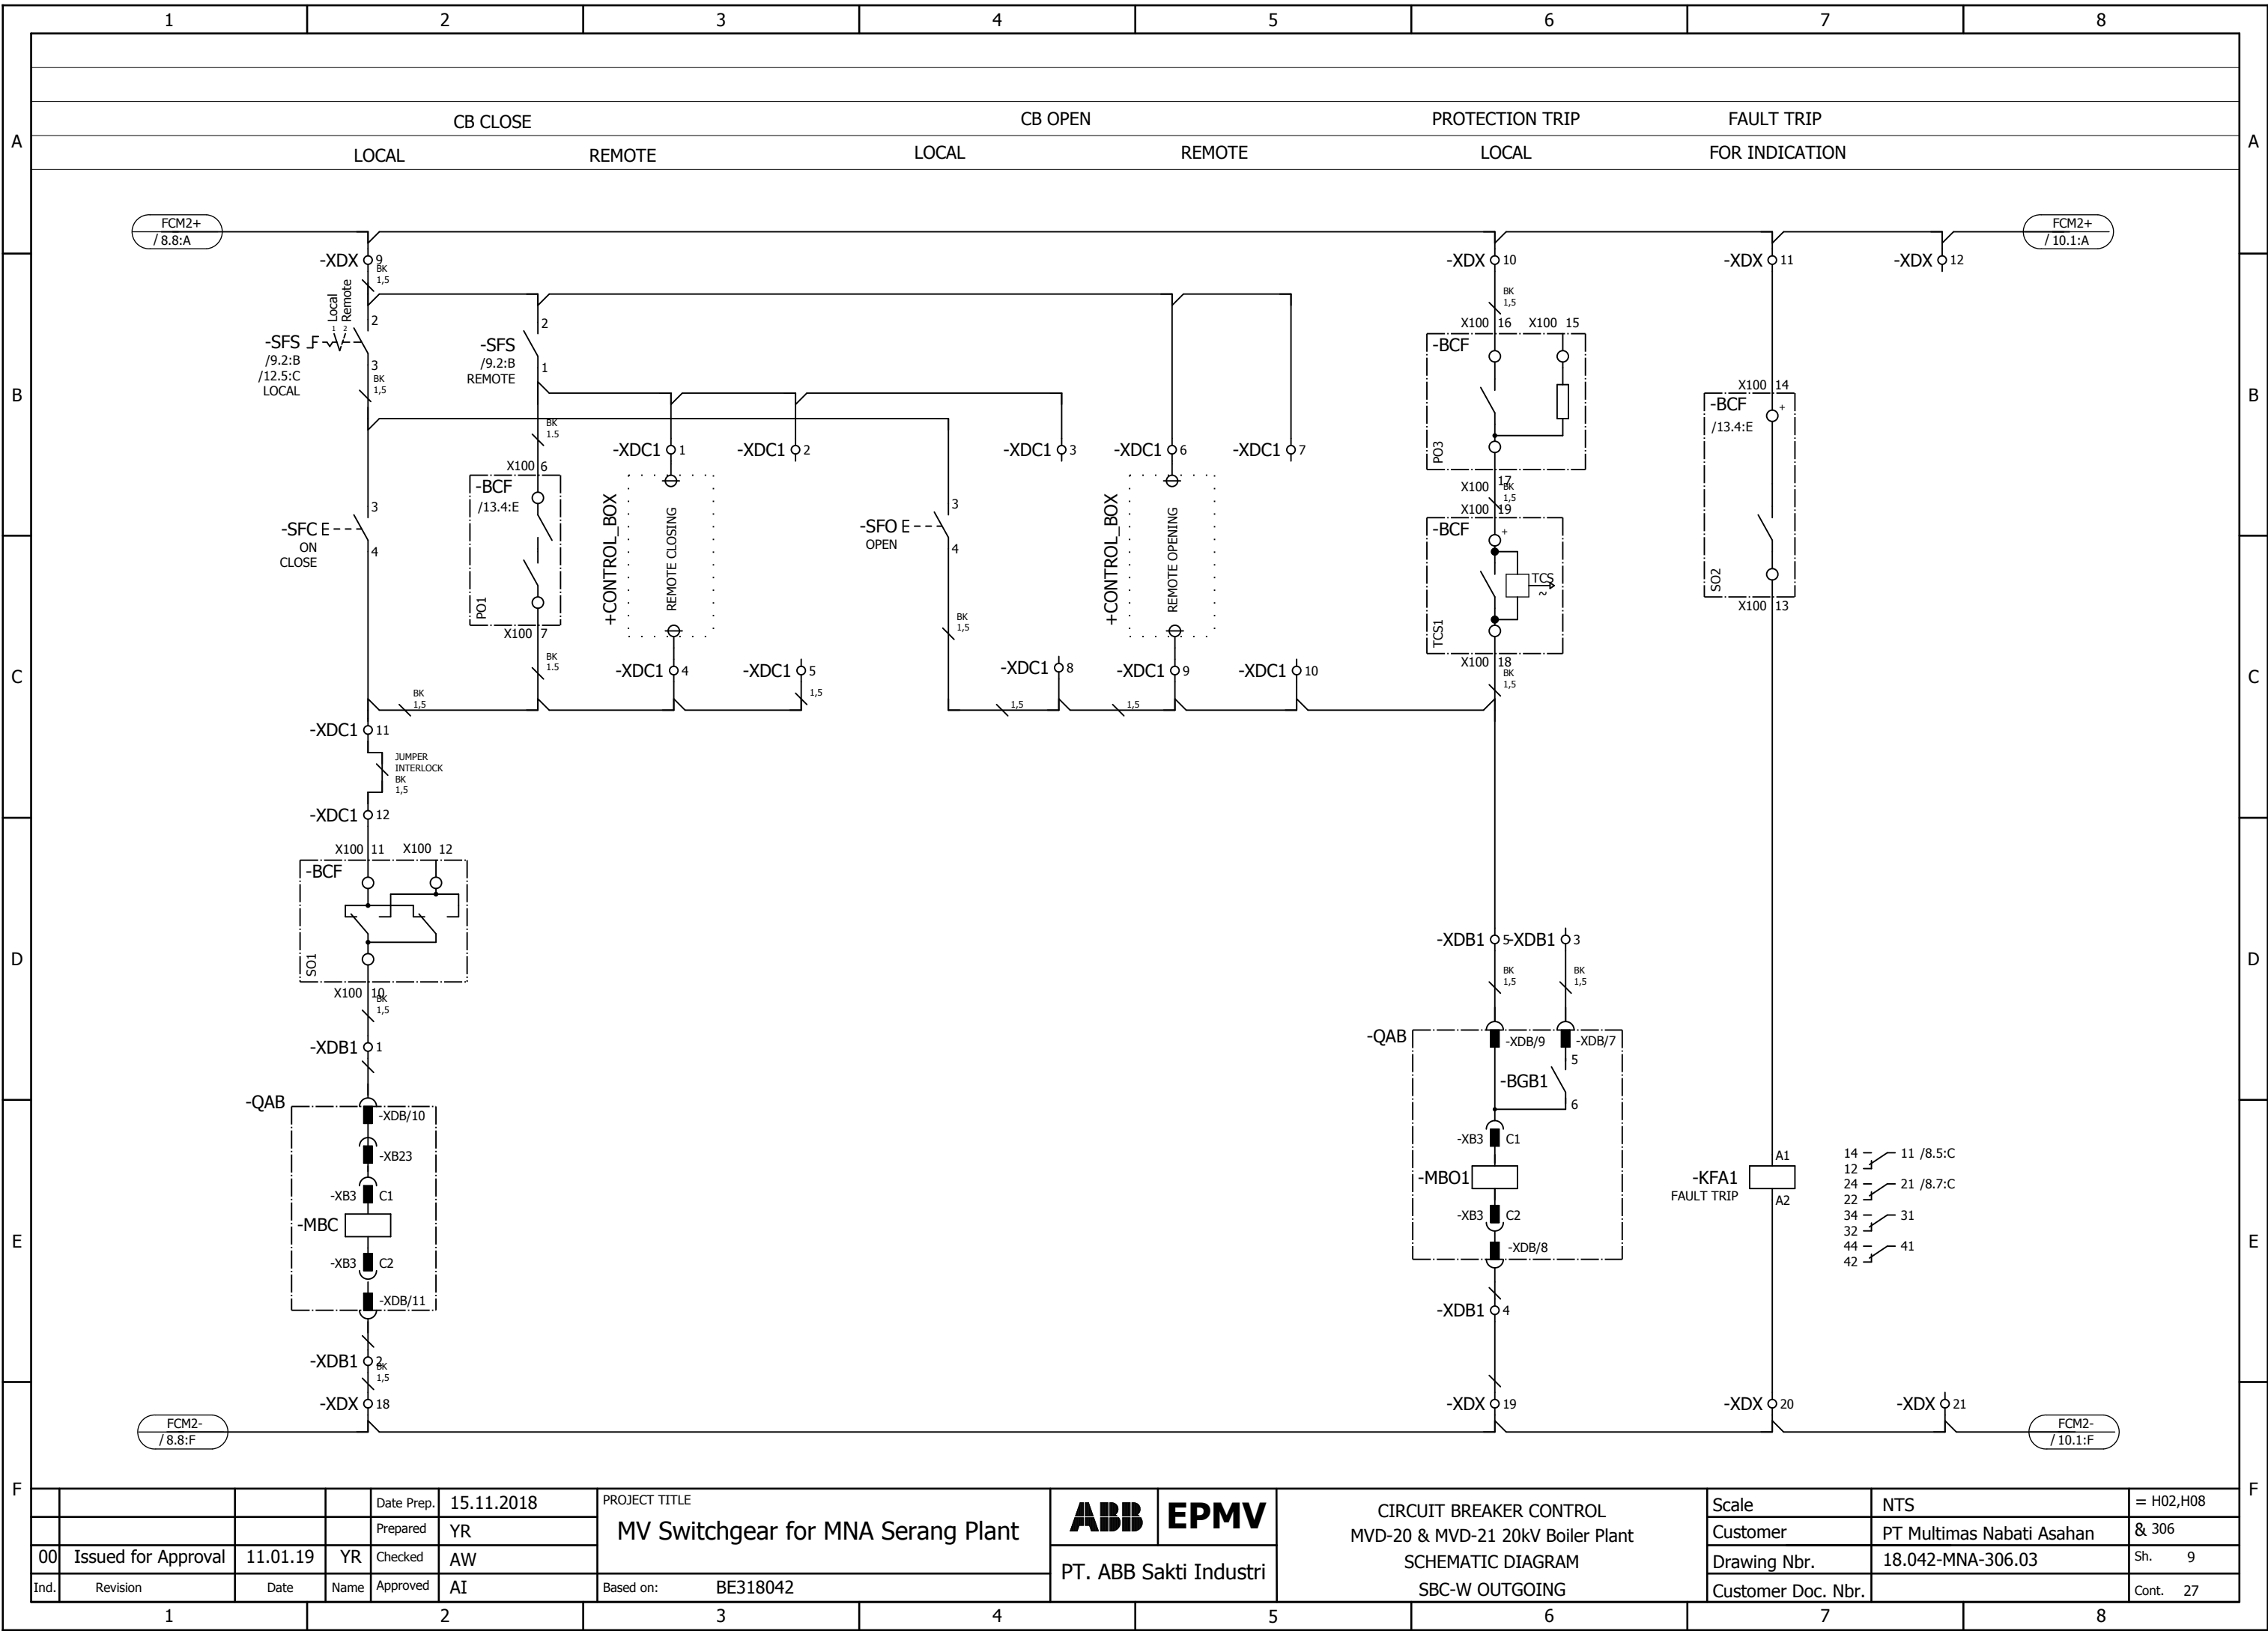


				Date Prep.	15.11.2018	PROJECT TITLE MV Switchgear for MNA Serang Plant			AUXILIARY MOTOR & RELAY MVD-20 & MVD-21 20kV Boiler Plant SCHEMATIC DIAGRAM SBC-W OUTGOING	Scale	NTS	= H02,H08
				Prepared	YR					Customer	PT Multimas Nabati Asahan	& 306
00	Issued for Approval	11.01.19	YR	Checked	AW		Drawing Nbr.	18.042-MNA-306.03		Sh. 10		
Ind.	Revision	Date	Name	Approved	AI	Based on:	BE318042	Customer Doc. Nbr.			Cont. 27	
							PT. ABB Sakti Industri					


WE RESERVE ALL RIGHTS IN THIS DOCUMENT AND IN THE INFORMATION CONTAINED THEREIN. REPRODUCTION, USE OR DISCLOSURE TO THIRD PARTIES WITHOUT EXPRESS AUTHORITY IS STRICTLY FORBIDDEN.

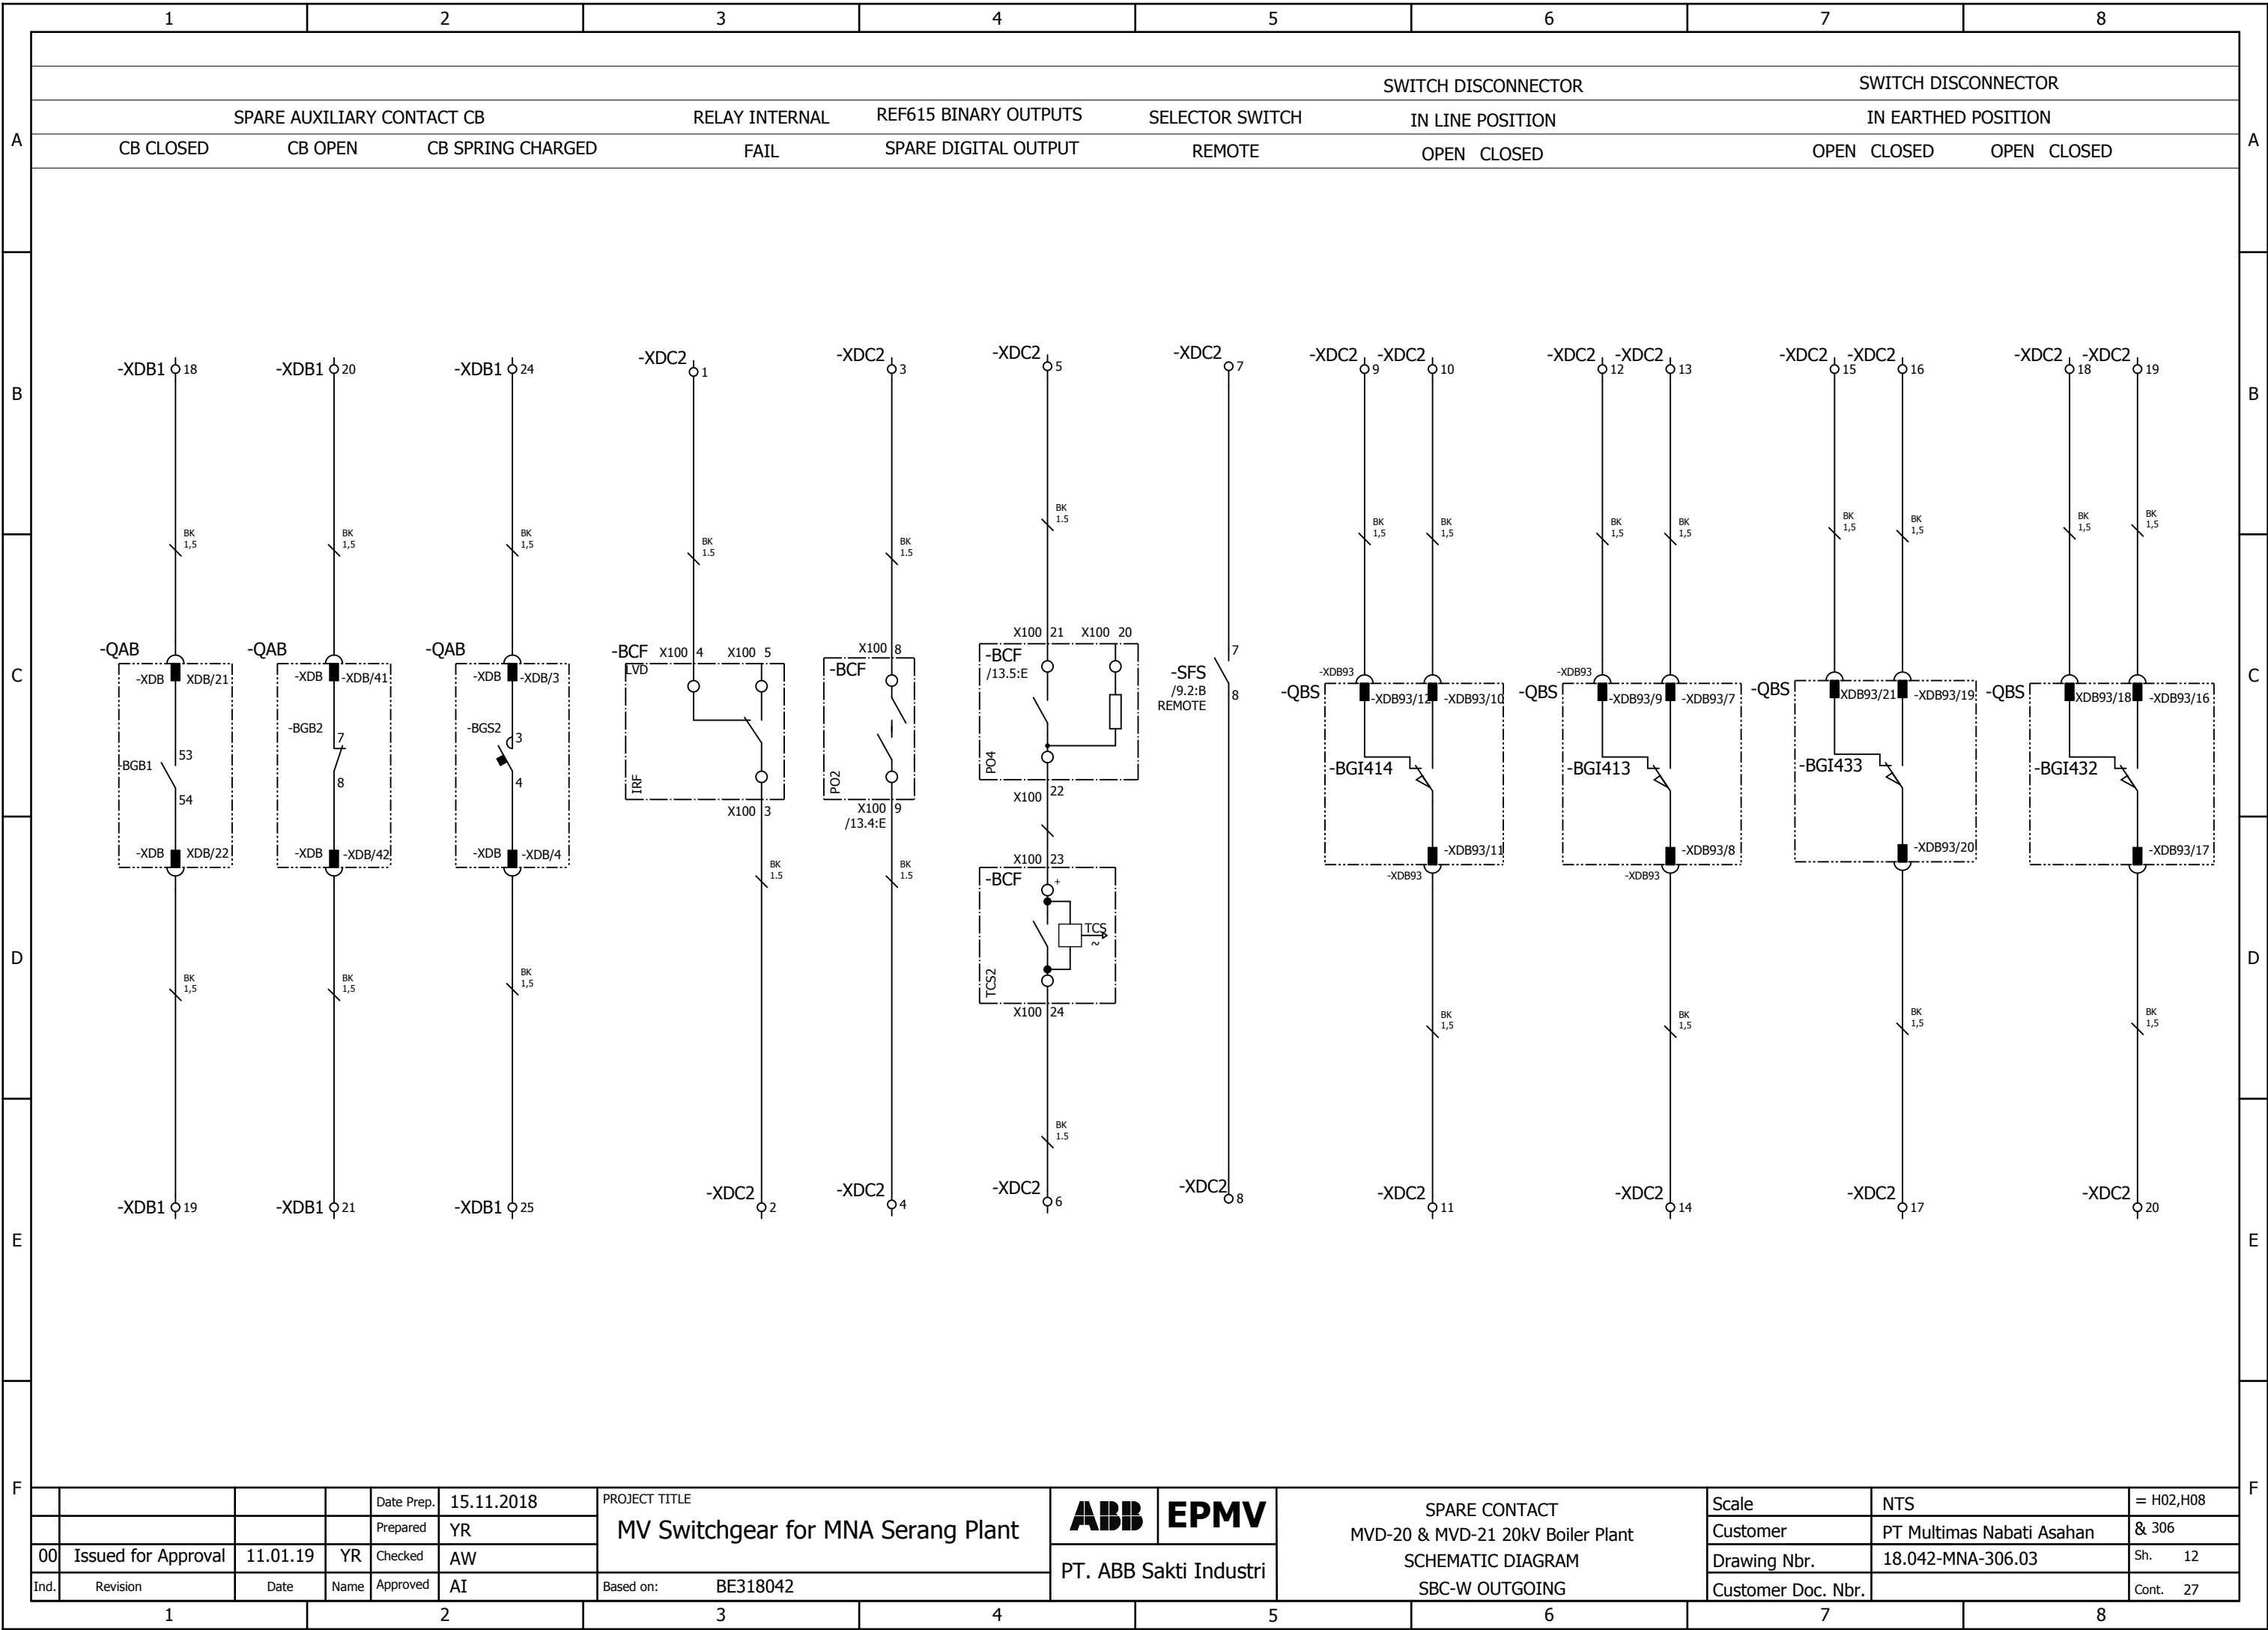

WE RESERVE ALL RIGHTS IN THIS DOCUMENT AND IN THE INFORMATION CONTAINED THEREIN. REPRODUCTION, USE OR DISCLOSURE TO THIRD PARTIES WITHOUT EXPRESS AUTHORITY IS STRICTLY FORBIDDEN.

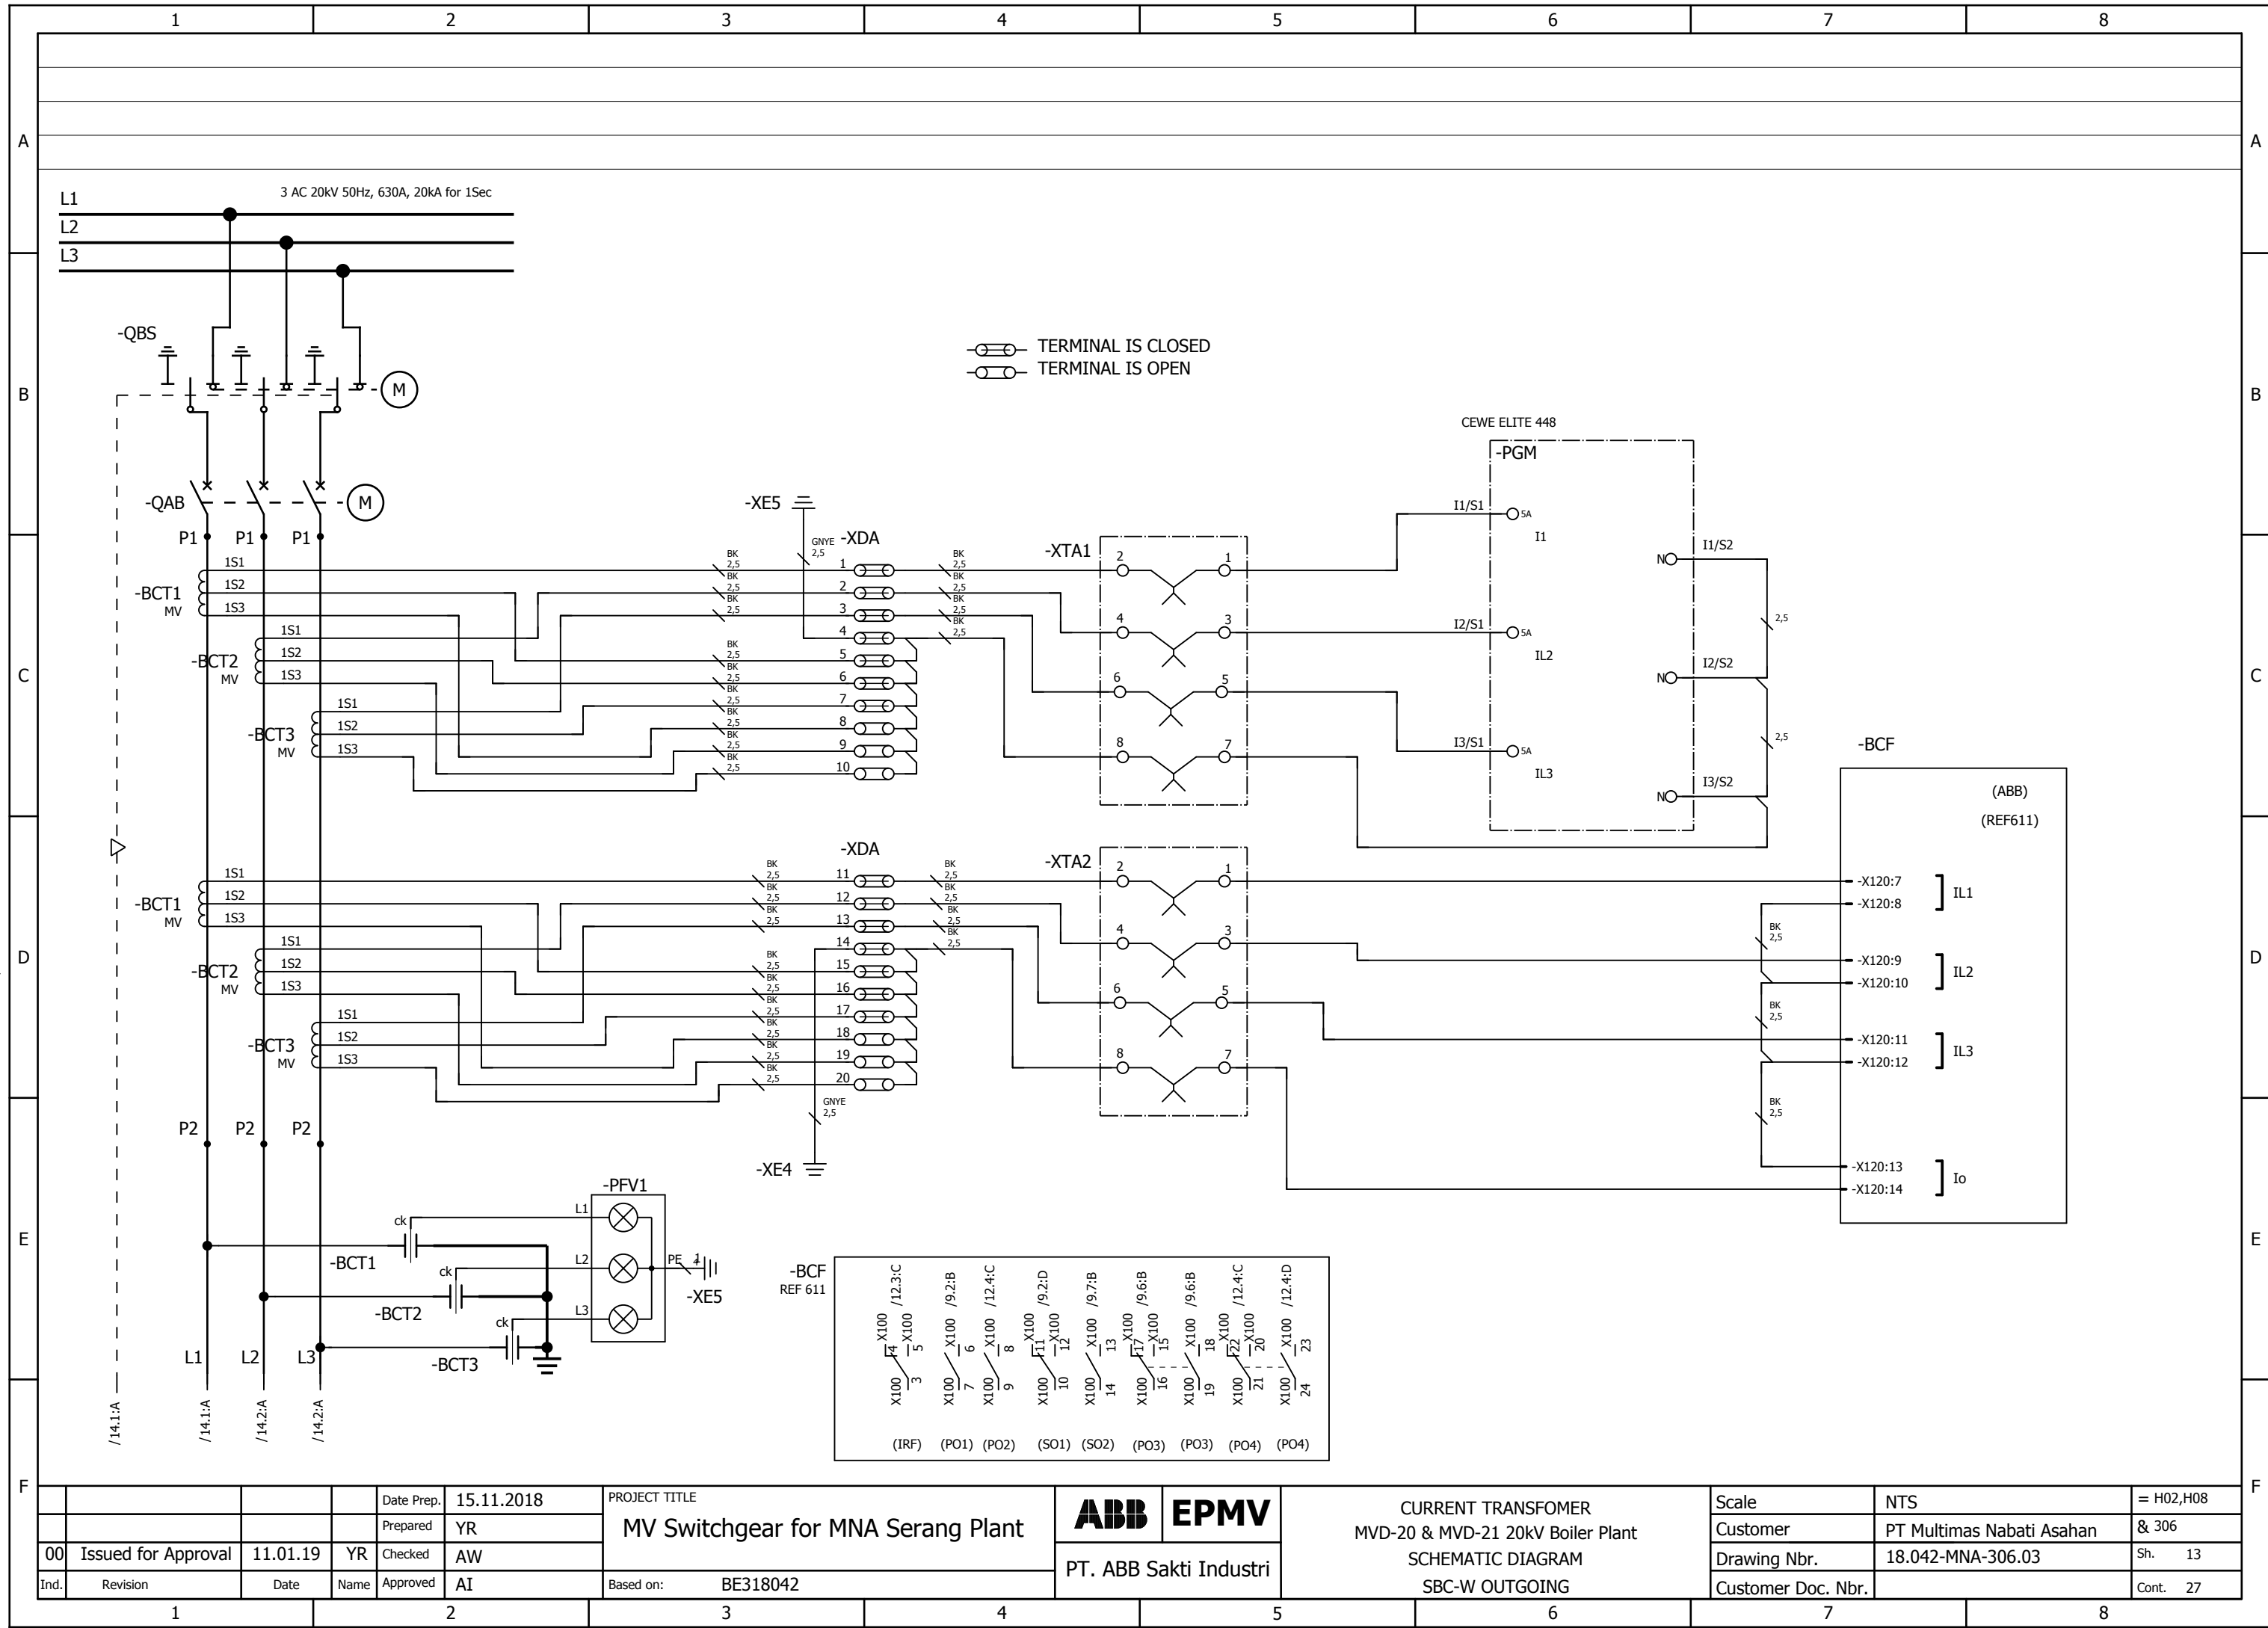


WE RESERVE ALL RIGHTS IN THIS DOCUMENT AND IN THE INFORMATION CONTAINED THEREIN. REPRODUCTION, USE OR DISCLOSURE TO THIRD PARTIES WITHOUT EXPRESS AUTHORITY IS STRICTLY FORBIDDEN.

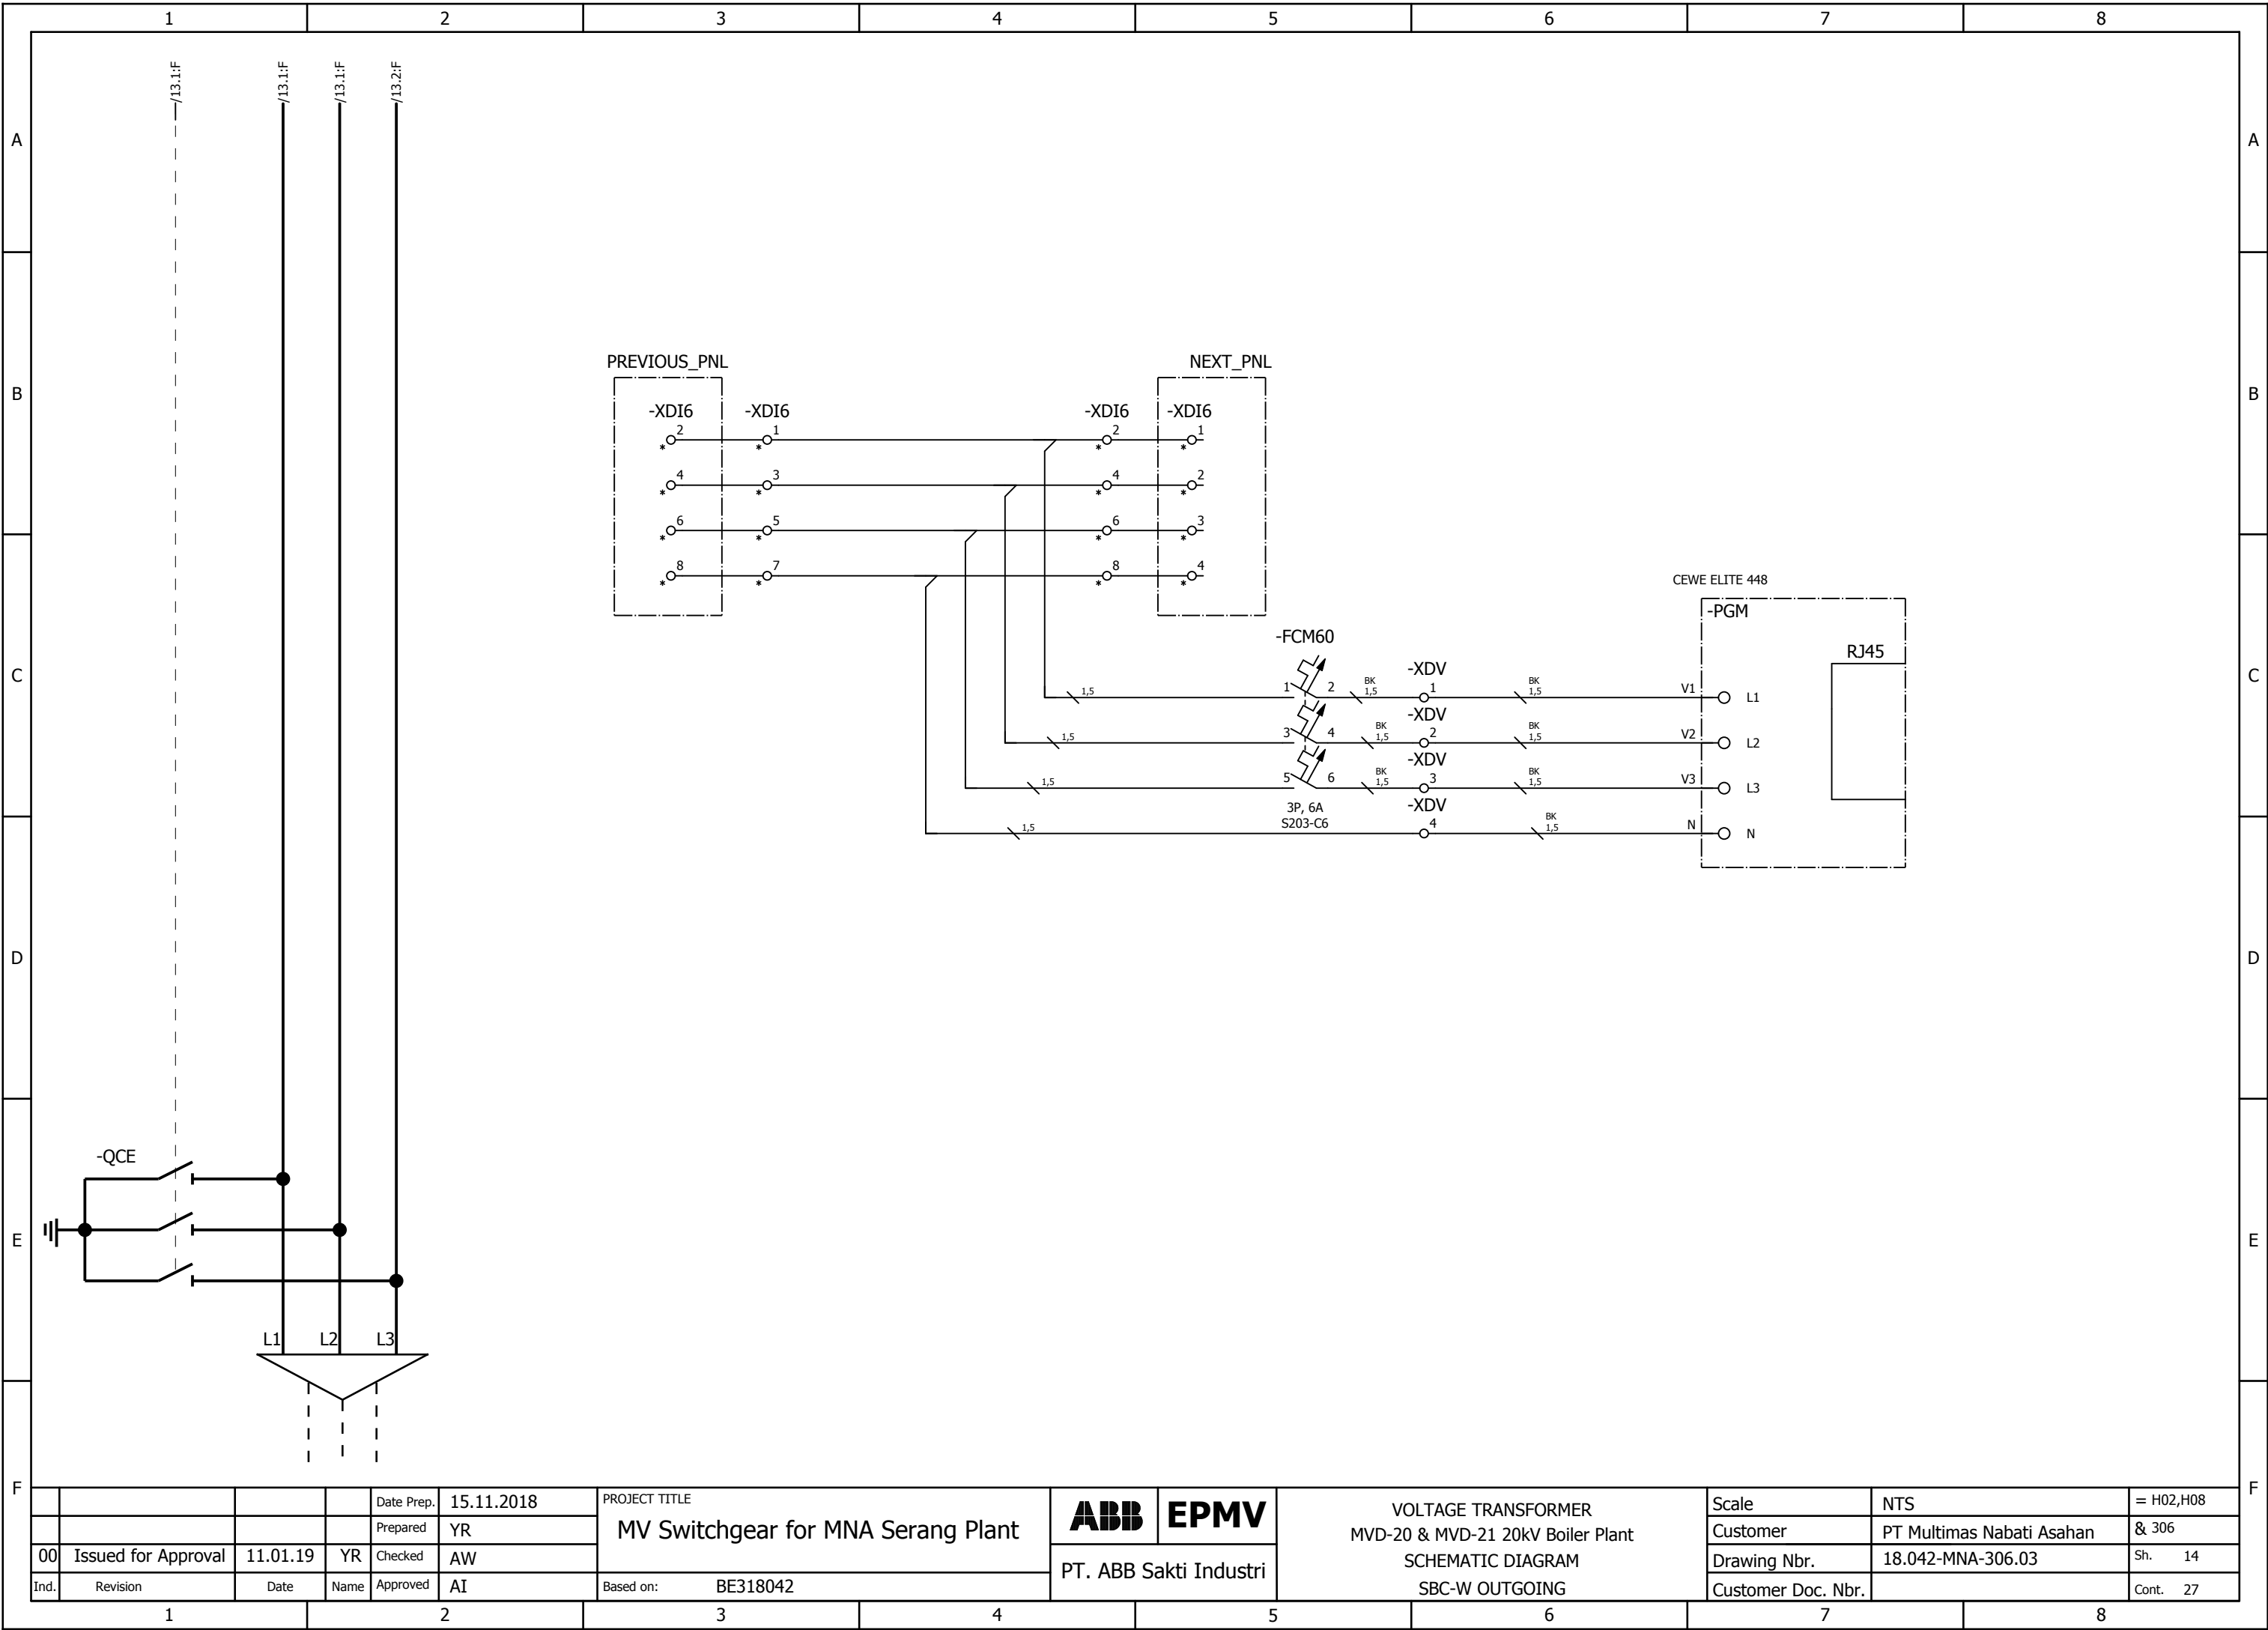

				Date Prep.	15.11.2018	PROJECT TITLE MV Switchgear for MNA Serang Plant		ABB EPMV	VOLTAGE TRANSFORMER MVD-20 & MVD-21 20kV Boiler Plant SCHEMATIC DIAGRAM SBC-W OUTGOING		Scale	NTS	= H02,H08
				Prepared	YR						Customer	PT Multimas Nabati Asahan	& 306
00		Issued for Approval		11.01.19	YR						Drawing Nbr.	18.042-MNA-306.03	Sh. 14
Ind.	Revision	Date	Name	Approved	AI	Based on:	BE318042	PT. ABB Sakti Industri			Customer Doc. Nbr.		Cont. 27

No.	EQUIPMENT DESCRIPTION	ENGRAVING
1	-SFS (LOCAL-OFF-REMOTE SELECTOR SWITCH, K&N)	-SFS, LOCAL-OFF-REMOTE
2	-SFC (PUSH BUTTON CB CLOSE, GREEN, ABB)	-SFC, CB CLOSE
3	-SFO (PUSH BUTTON CB OPEN, RED, ABB)	-SFO, CB OPEN
4	-PFY1 (LAMP INDICATION FOR CB TRIP, YELLOW, ABB)	-PFY1, CB TRIP
5	-PFR1 (LAMP INDICATION FOR CB CLOSE, RED, ABB)	-PFR1, CB CLOSE
6	-PFG1 (LAMP INDICATION FOR CB OPEN, GREEN, ABB)	-PFG1, CB OPEN
7	-PGJ (DIGITAL MEASUREMENT, CEWE 448)	-PGJ, DIGITAL MEASUREMENT
8	-BCF (FEEDER PROTECTION RELAY, REF615J, ABB)	-BCF, RELAY PROTECTION
9	-XTA1, XTA2 (TEST BLOCK , YONGSUNG)	-XTA, CURRENT TEST BLOCK

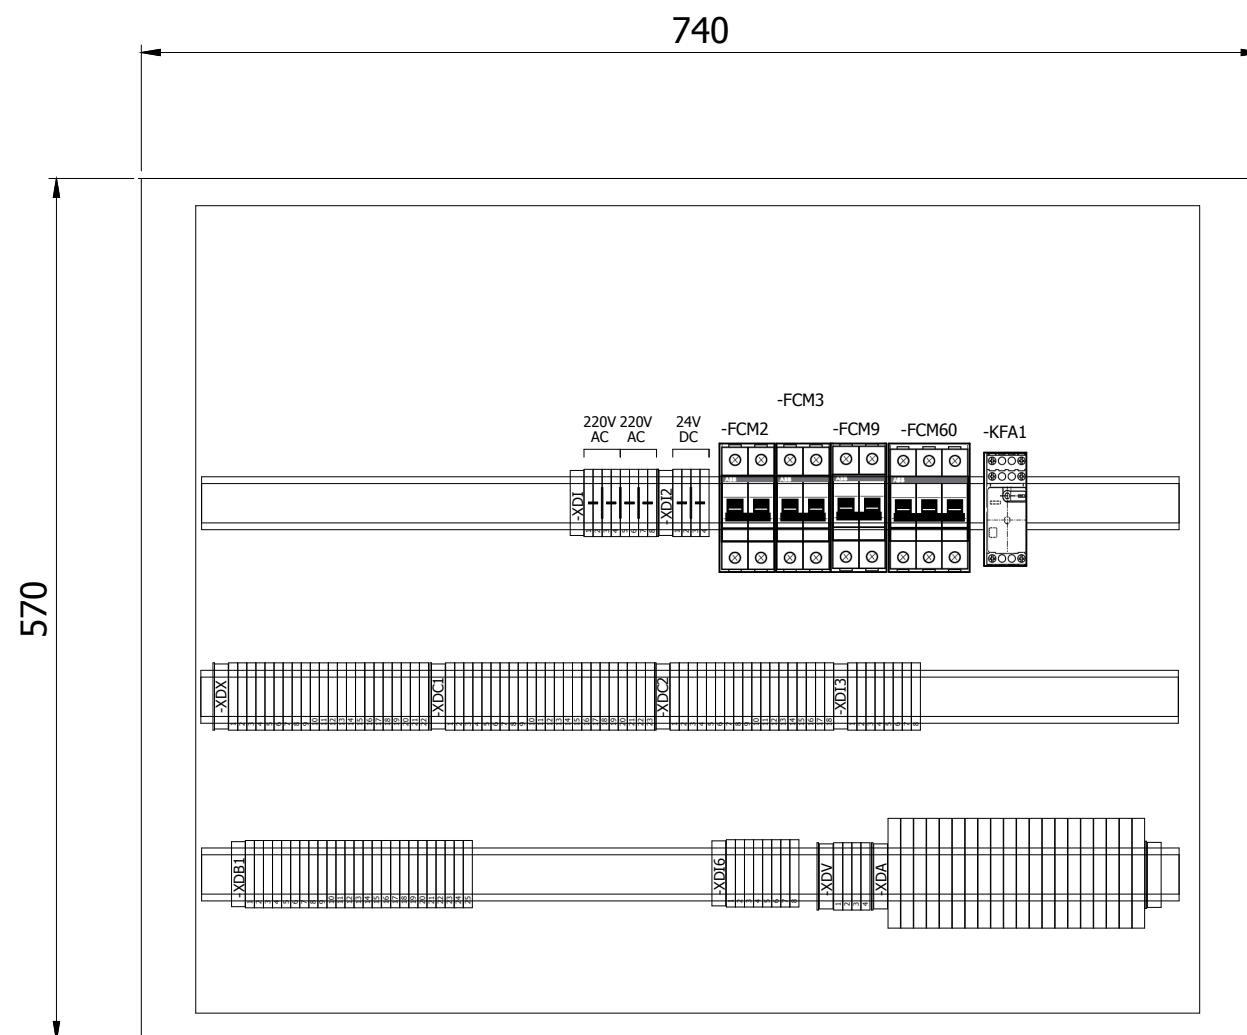[illegible]

				Date Prep.	15.11.2018	PROJECT TITLE MV Switchgear for MNA Serang Plant	 	LV BOX LAYOUT MVD-20 & MVD-21 20kV Boiler Plant SCHEMATIC DIAGRAM SBC-W OUTGOING	Scale	NTS	= H02,H08
				Prepared	YR				Customer	PT Multimas Nabati Asahan	& 306
00	Issued for Approval	11.01.19	YR	Checked	AW				Drawing Nbr.	18.042-MNA-306.03	Sh. 16
Ind.	Revision	Date	Name	Approved	AI	Based on: BE318042	PT. ABB Sakti Industri		Customer Doc. Nbr.		Cont. 27

WE RESERVE ALL RIGHTS IN THIS DOCUMENT AND IN THE INFORMATION CONTAINED THEREIN. REPRODUCTION, USE OR DISCLOSURE TO THIRD PARTIES WITHOUT EXPRESS AUTHORITY IS STRICTLY FORBIDDEN.

1		2		3		4		5		6		7		8	
Summarized parts list															
IDABB_F02_005-IDABB															
Carry over: 0.00															
TAG ID		DESCRIPTION				MANUFACTUR/BRAND		PART NUMBER		QUANTITY		REMARKS			
-BCF		Feeder Management Relay REF611HBAABC1NN11G				ABB		REF611HBAABC1NN11G		1		/8.2:C			
-EB		HEATER 230VAC, 50W				SANYANG		CDXN010033P0009		1		/7.6:E			
-FCM2		MCB S202-C10 MCB. 2P, 10A				ABB		2CDS252001R0104		1		/7.2:C			
-FCM3;-FCM9		MCB S202-C6 MCB. 2P, 6A				ABB		2CDS252001R0064		2		/7.5:C;/7.6:C			
-FCM60		MCB S203-C6 MCB. 3P, 6A				ABB		2CDS253001R0064		1		/14.5:C			
-KFA1		Auxiliary Relay 230AC 4COS				PHOENIX		1YRA3DL266230001		1		/9.7:E			
-PFG1		PILOT LIGHT GREEN #CL-523G#230VAC CL-523G				ABB		1SFA619402R5232		1		/8.5:E			
-PFR1		PILOT LIGHT RED #CL-523R#230VAC CL-523R				ABB		1SFA619402R5231		1		/8.4:E			
-PFY1		PILOT LIGHT YELLOW #CL-523Y#230VAC CL-523Y				ABB		1SFA619402R5233		1		/8.6:E			
-PGM1		POWER METER CEWE 448 Class : 0.5s; CT Input : 1A; VT Input : 57.7-240V (L-N); Aux. Voltage: 80-300VAC/DC				CEWE		1YRA4EA0350001		1		/8.3:C			
-SFC		PUSH BUTTON, YW1B-M1E10-G GREEN COLOUR				IDEC		1YRA3DA14700001		1		/9.2:B			
-SFO		PUSH BUTTON, YW1B-M1E10-R RED COLOUR				IDEC		1YRA3DA14700002		1		/9.4:B			
-SFS		LOCAL/REMOTE Selector Switch Type : S0-CA10-A723-600-E; 4NC (for LOCAL Position) & 4NO (for REMOTE Position)				K&N		1YRA3DA17940011		1		/9.2:B			
-XTA1;-XTA2		Current Test Block Rated Current : 10A, 250V; Mounting : Flush Mounting				YONGSUNG		YSCTT-04C		2		/13.4:C;/13.4:D			

[illegible]

[illegible]

[illegible]

[illegible]

[illegible]

[illegible]

[illegible]