



WE RESERVE ALL RIGHTS IN THIS DOCUMENT AND IN THE INFORMATION CONTAINED THEREIN. REPRODUCTION, USE OR DISCLOSURE TO THIRD PARTIES WITHOUT EXPRESS AUTHORITY IS STRICTLY FORBIDDEN.

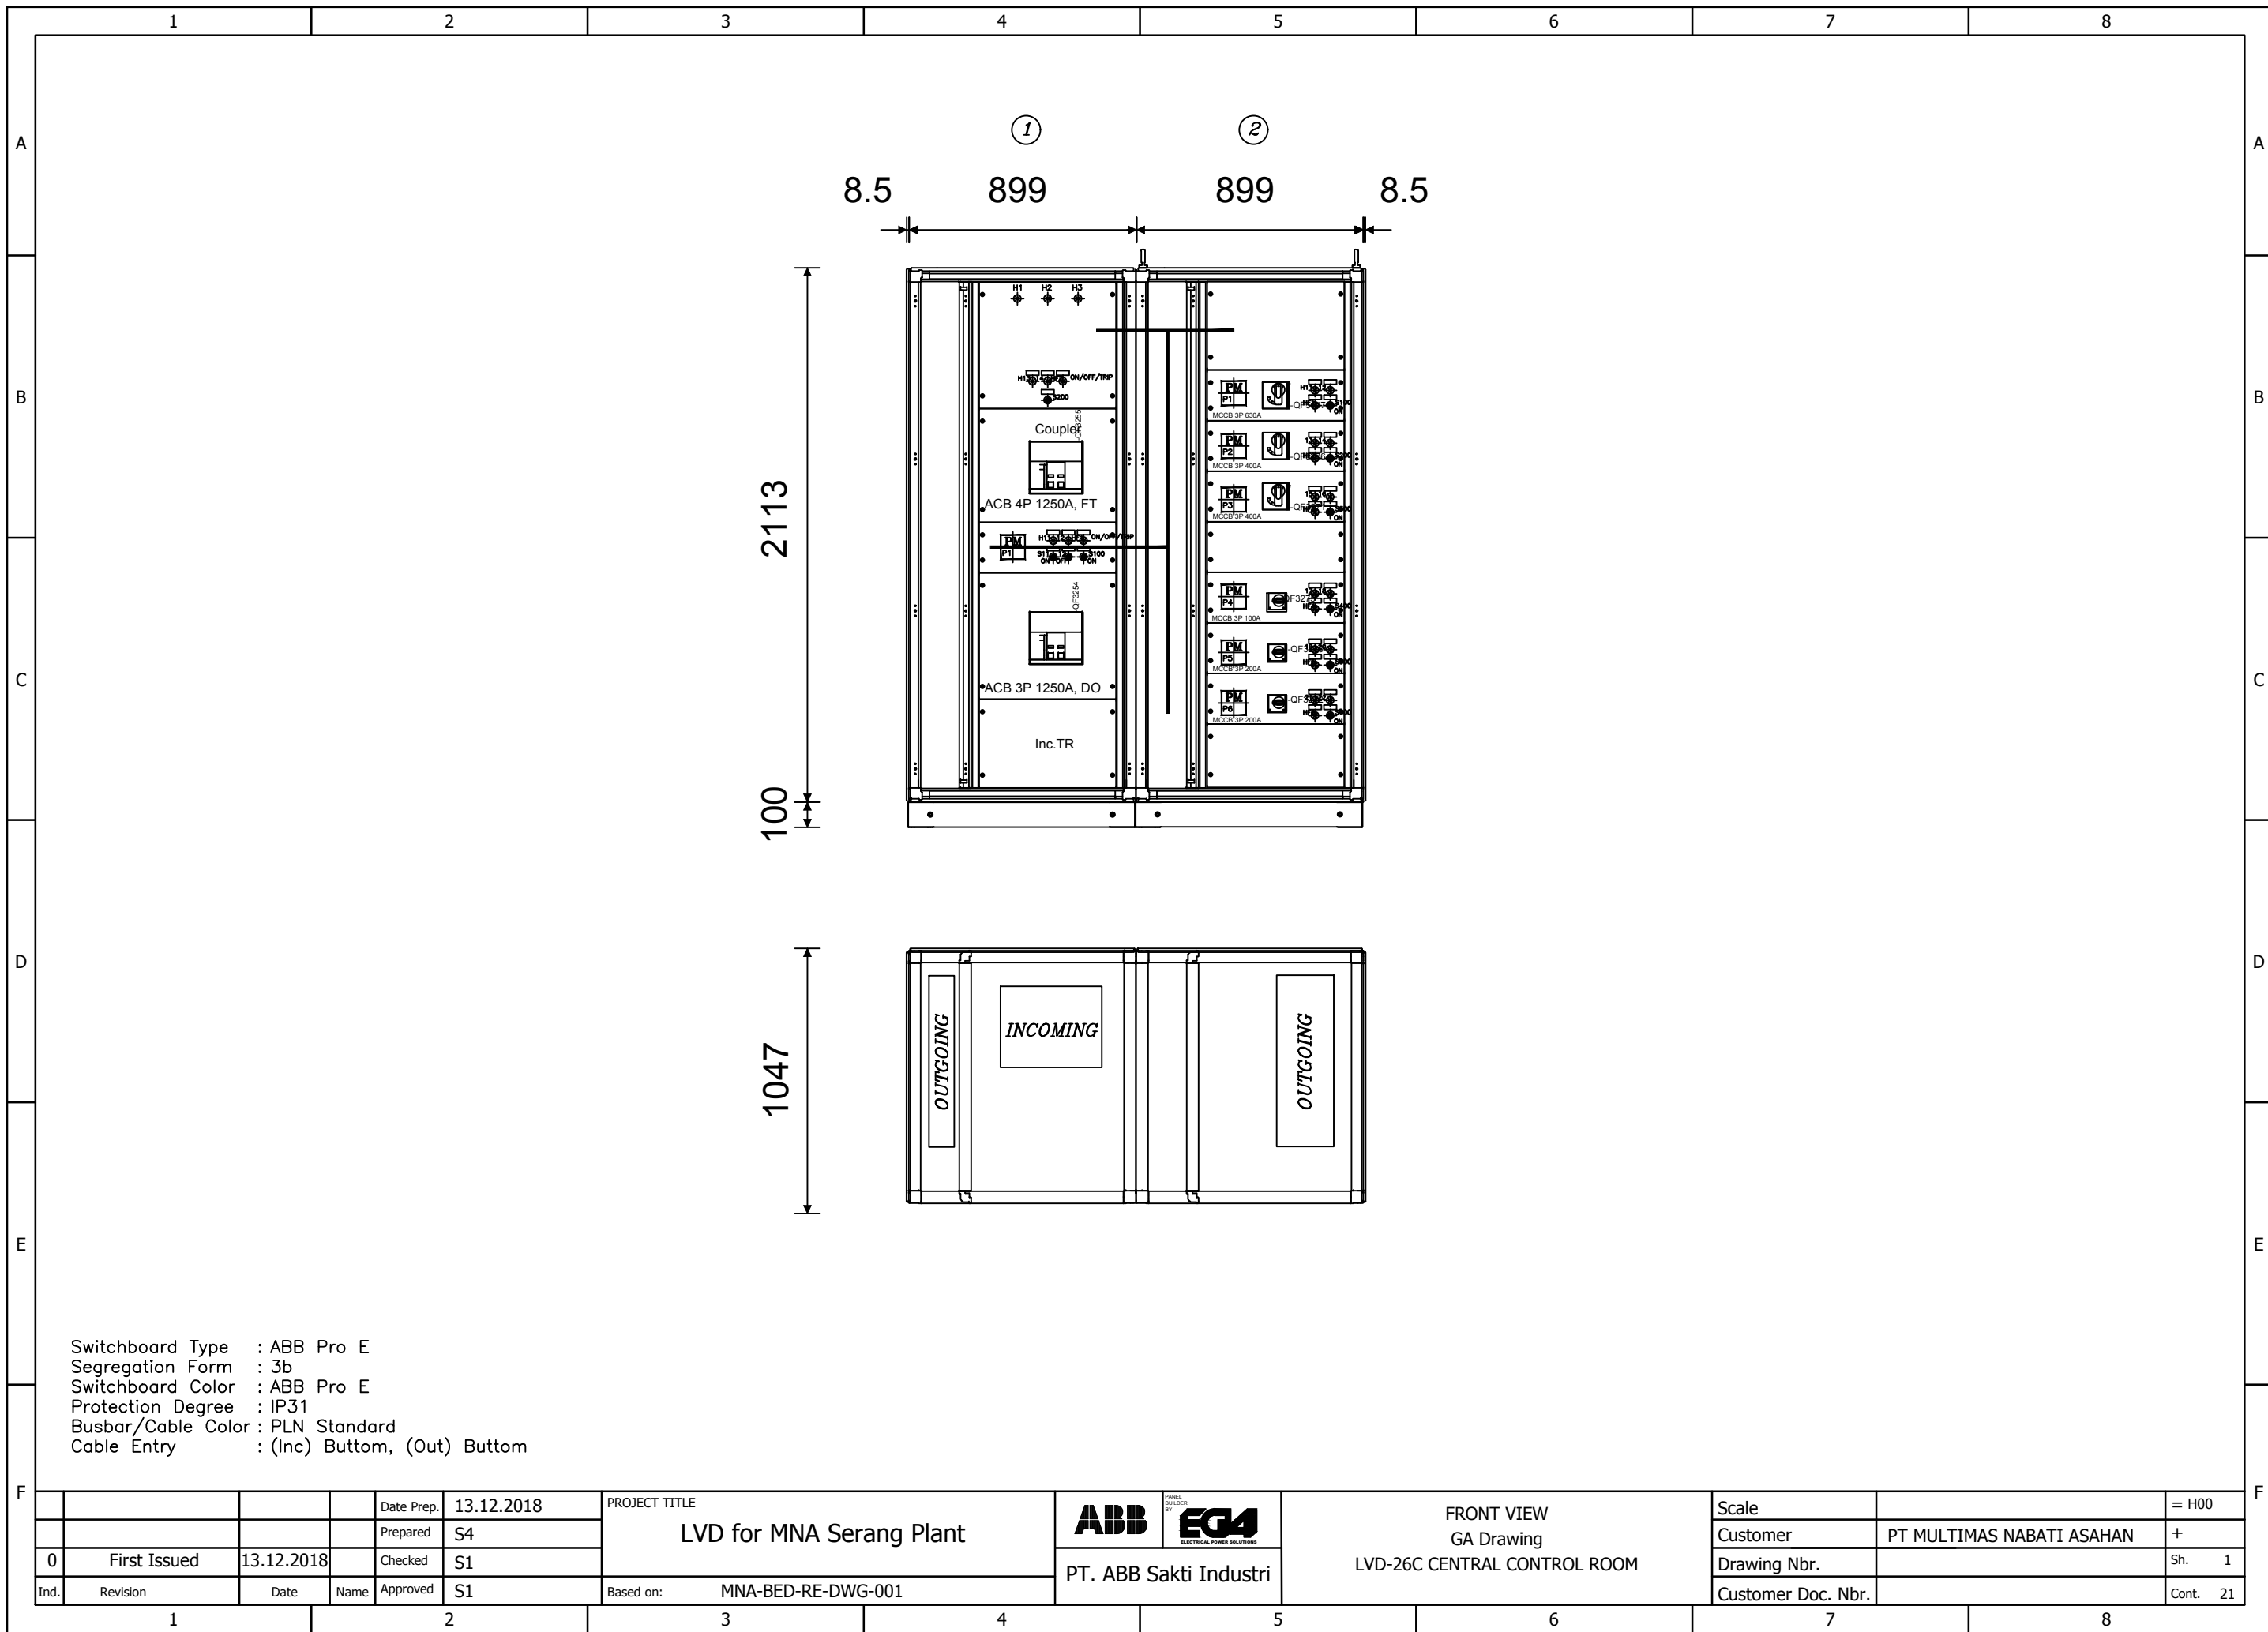


WE RESERVE ALL RIGHTS IN THIS DOCUMENT AND IN THE INFORMATION CONTAINED THEREIN. REPRODUCTION, USE OR DISCLOSURE TO THIRD PARTIES WITHOUT EXPRESS AUTHORITY IS STRICTLY FORBIDDEN.

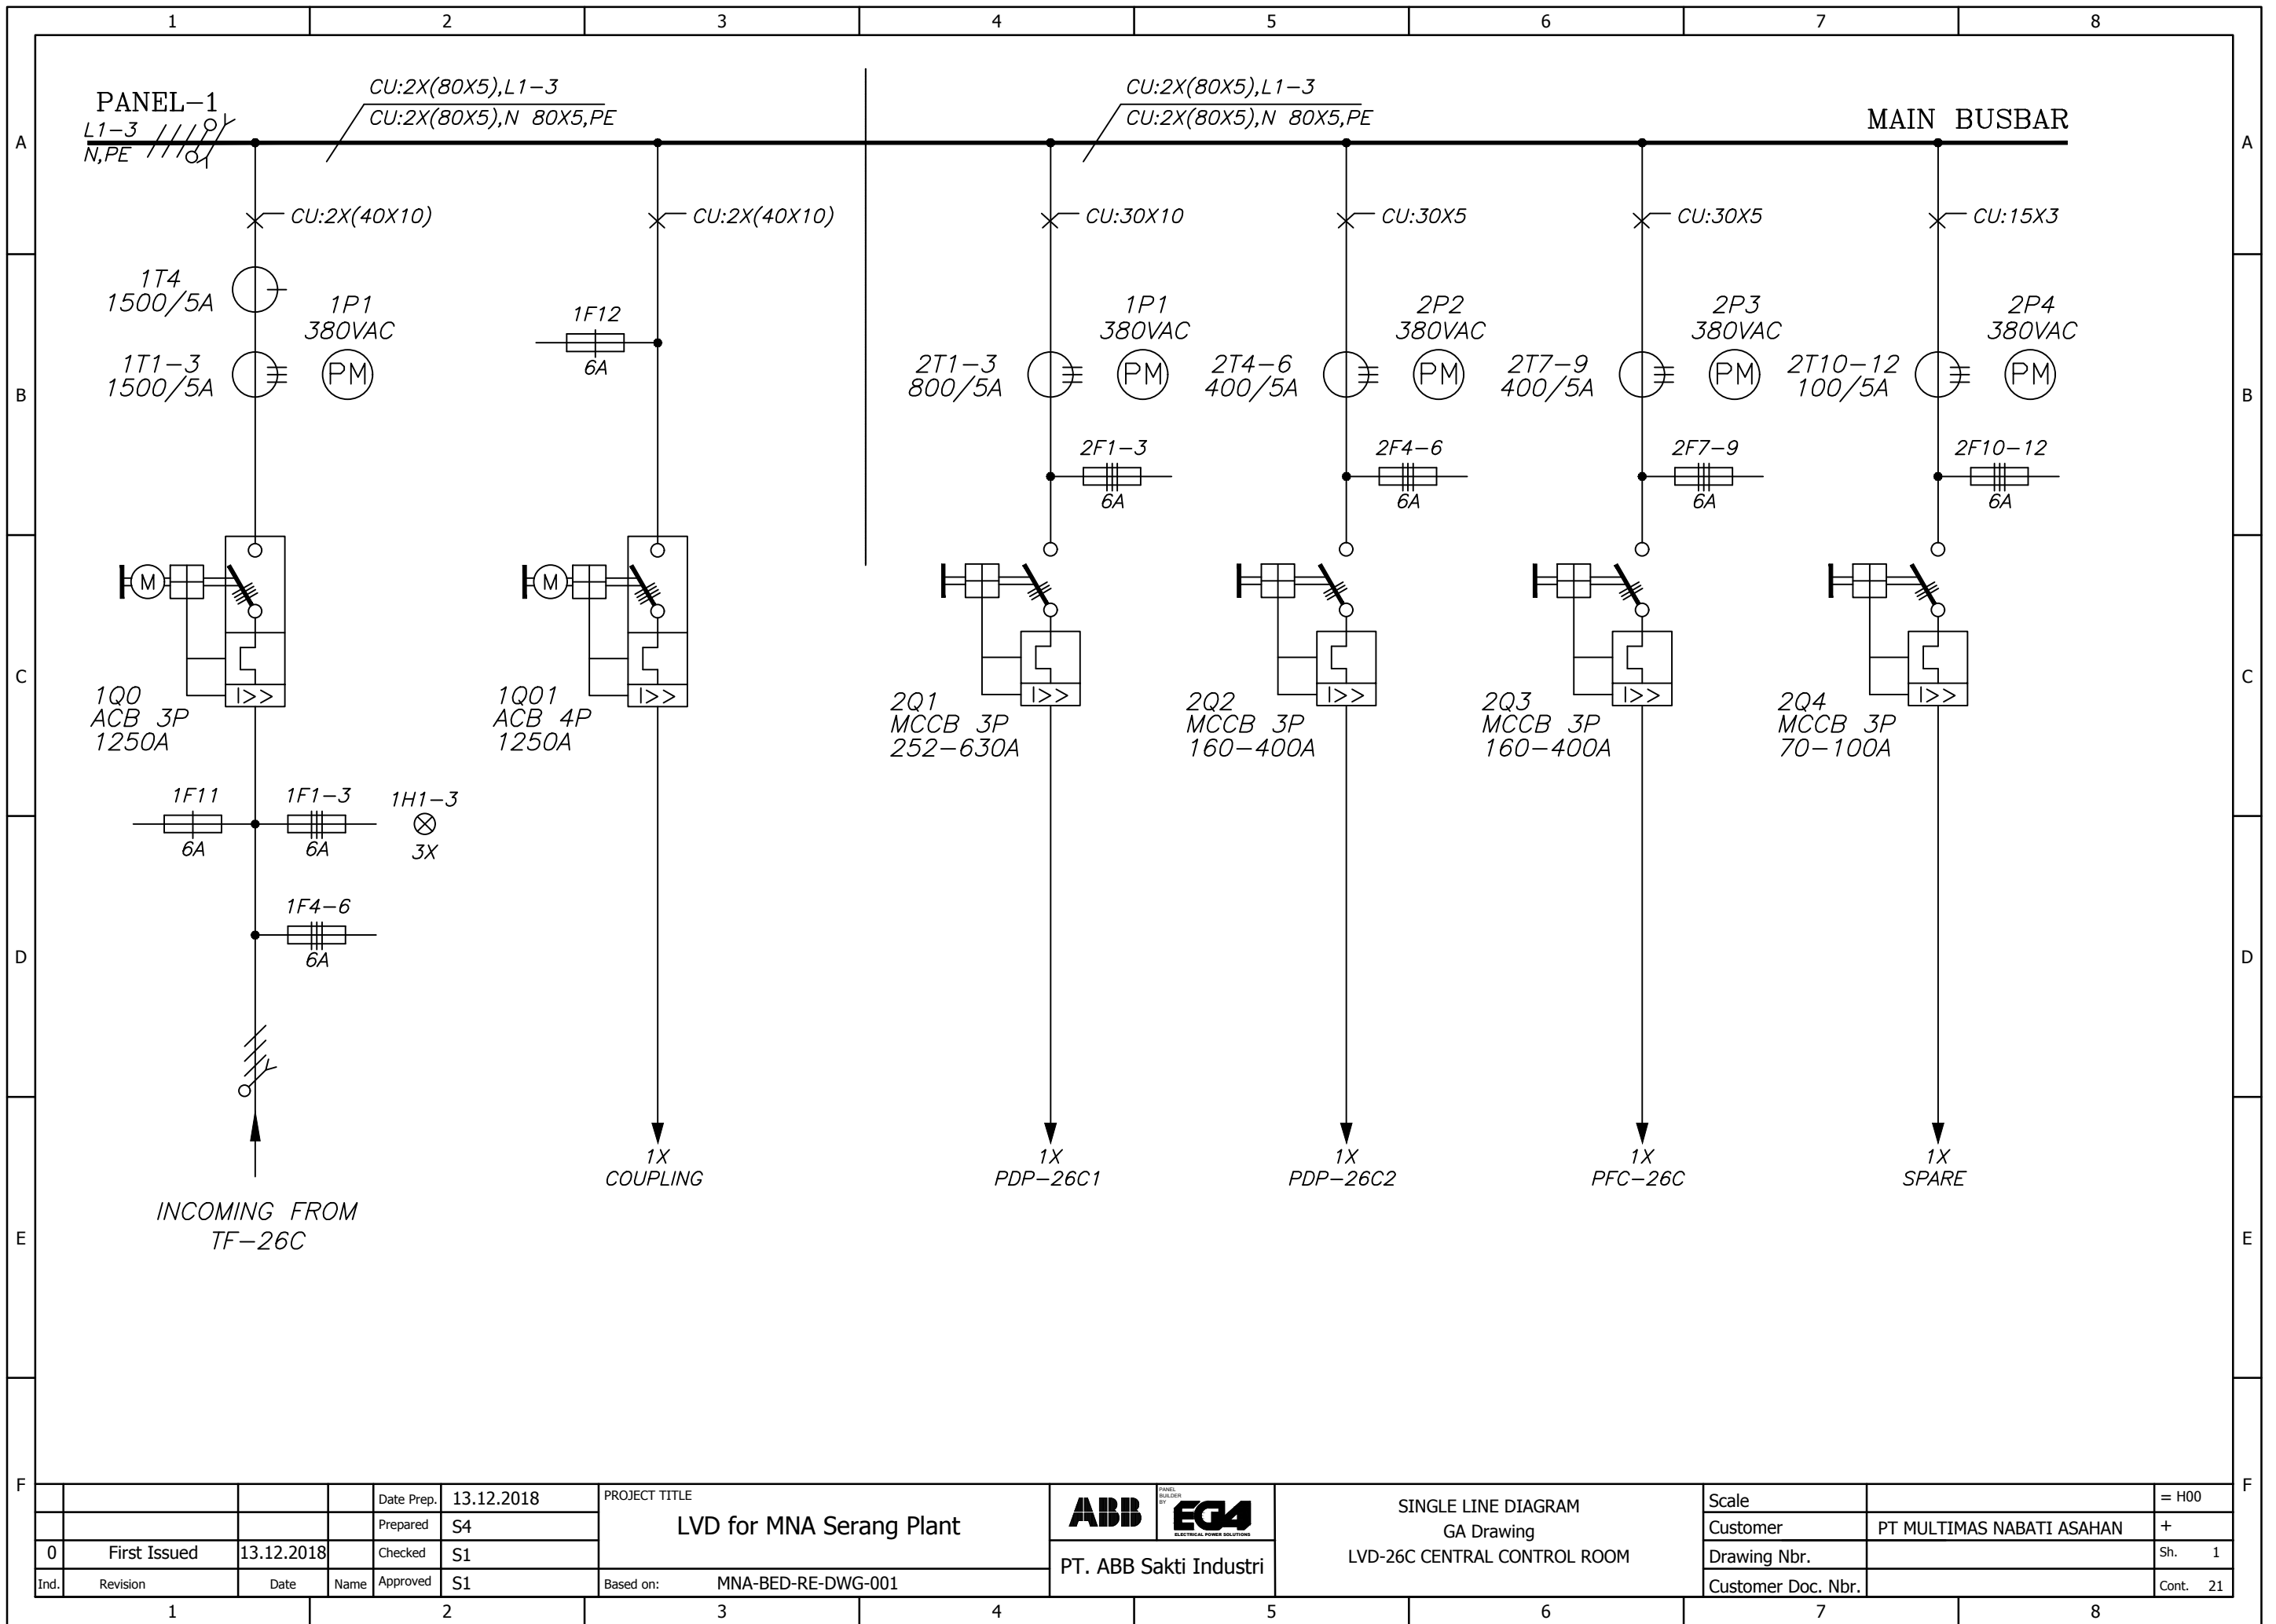


		Date Prep.	13.12.2018	PROJECT TITLE LVD for MNA Serang Plant		ABB PANEL BUILDING BY EG4 ELECTRICAL POWER SOLUTIONS		SINGLE LINE DIAGRAM GA Drawing LVD-26C CENTRAL CONTROL ROOM		Scale		= H00
		Prepared	S4							Customer	PT MULTIMAS NABATI ASAHAN	+
0		First Issued	13.12.2018	Checked	S1					Drawing Nbr.		Sh. 1
Ind.	Revision	Date	Name	Approved	S1	Based on:	MNA-BED-RE-DWG-001	PT. ABB Sakti Industri		Customer Doc. Nbr.		Cont. 21


WE RESERVE ALL RIGHTS IN THIS DOCUMENT AND IN THE INFORMATION CONTAINED THEREIN. REPRODUCTION, USE OR DISCLOSURE TO THIRD PARTIES WITHOUT EXPRESS AUTHORITY IS STRICTLY FORBIDDEN.

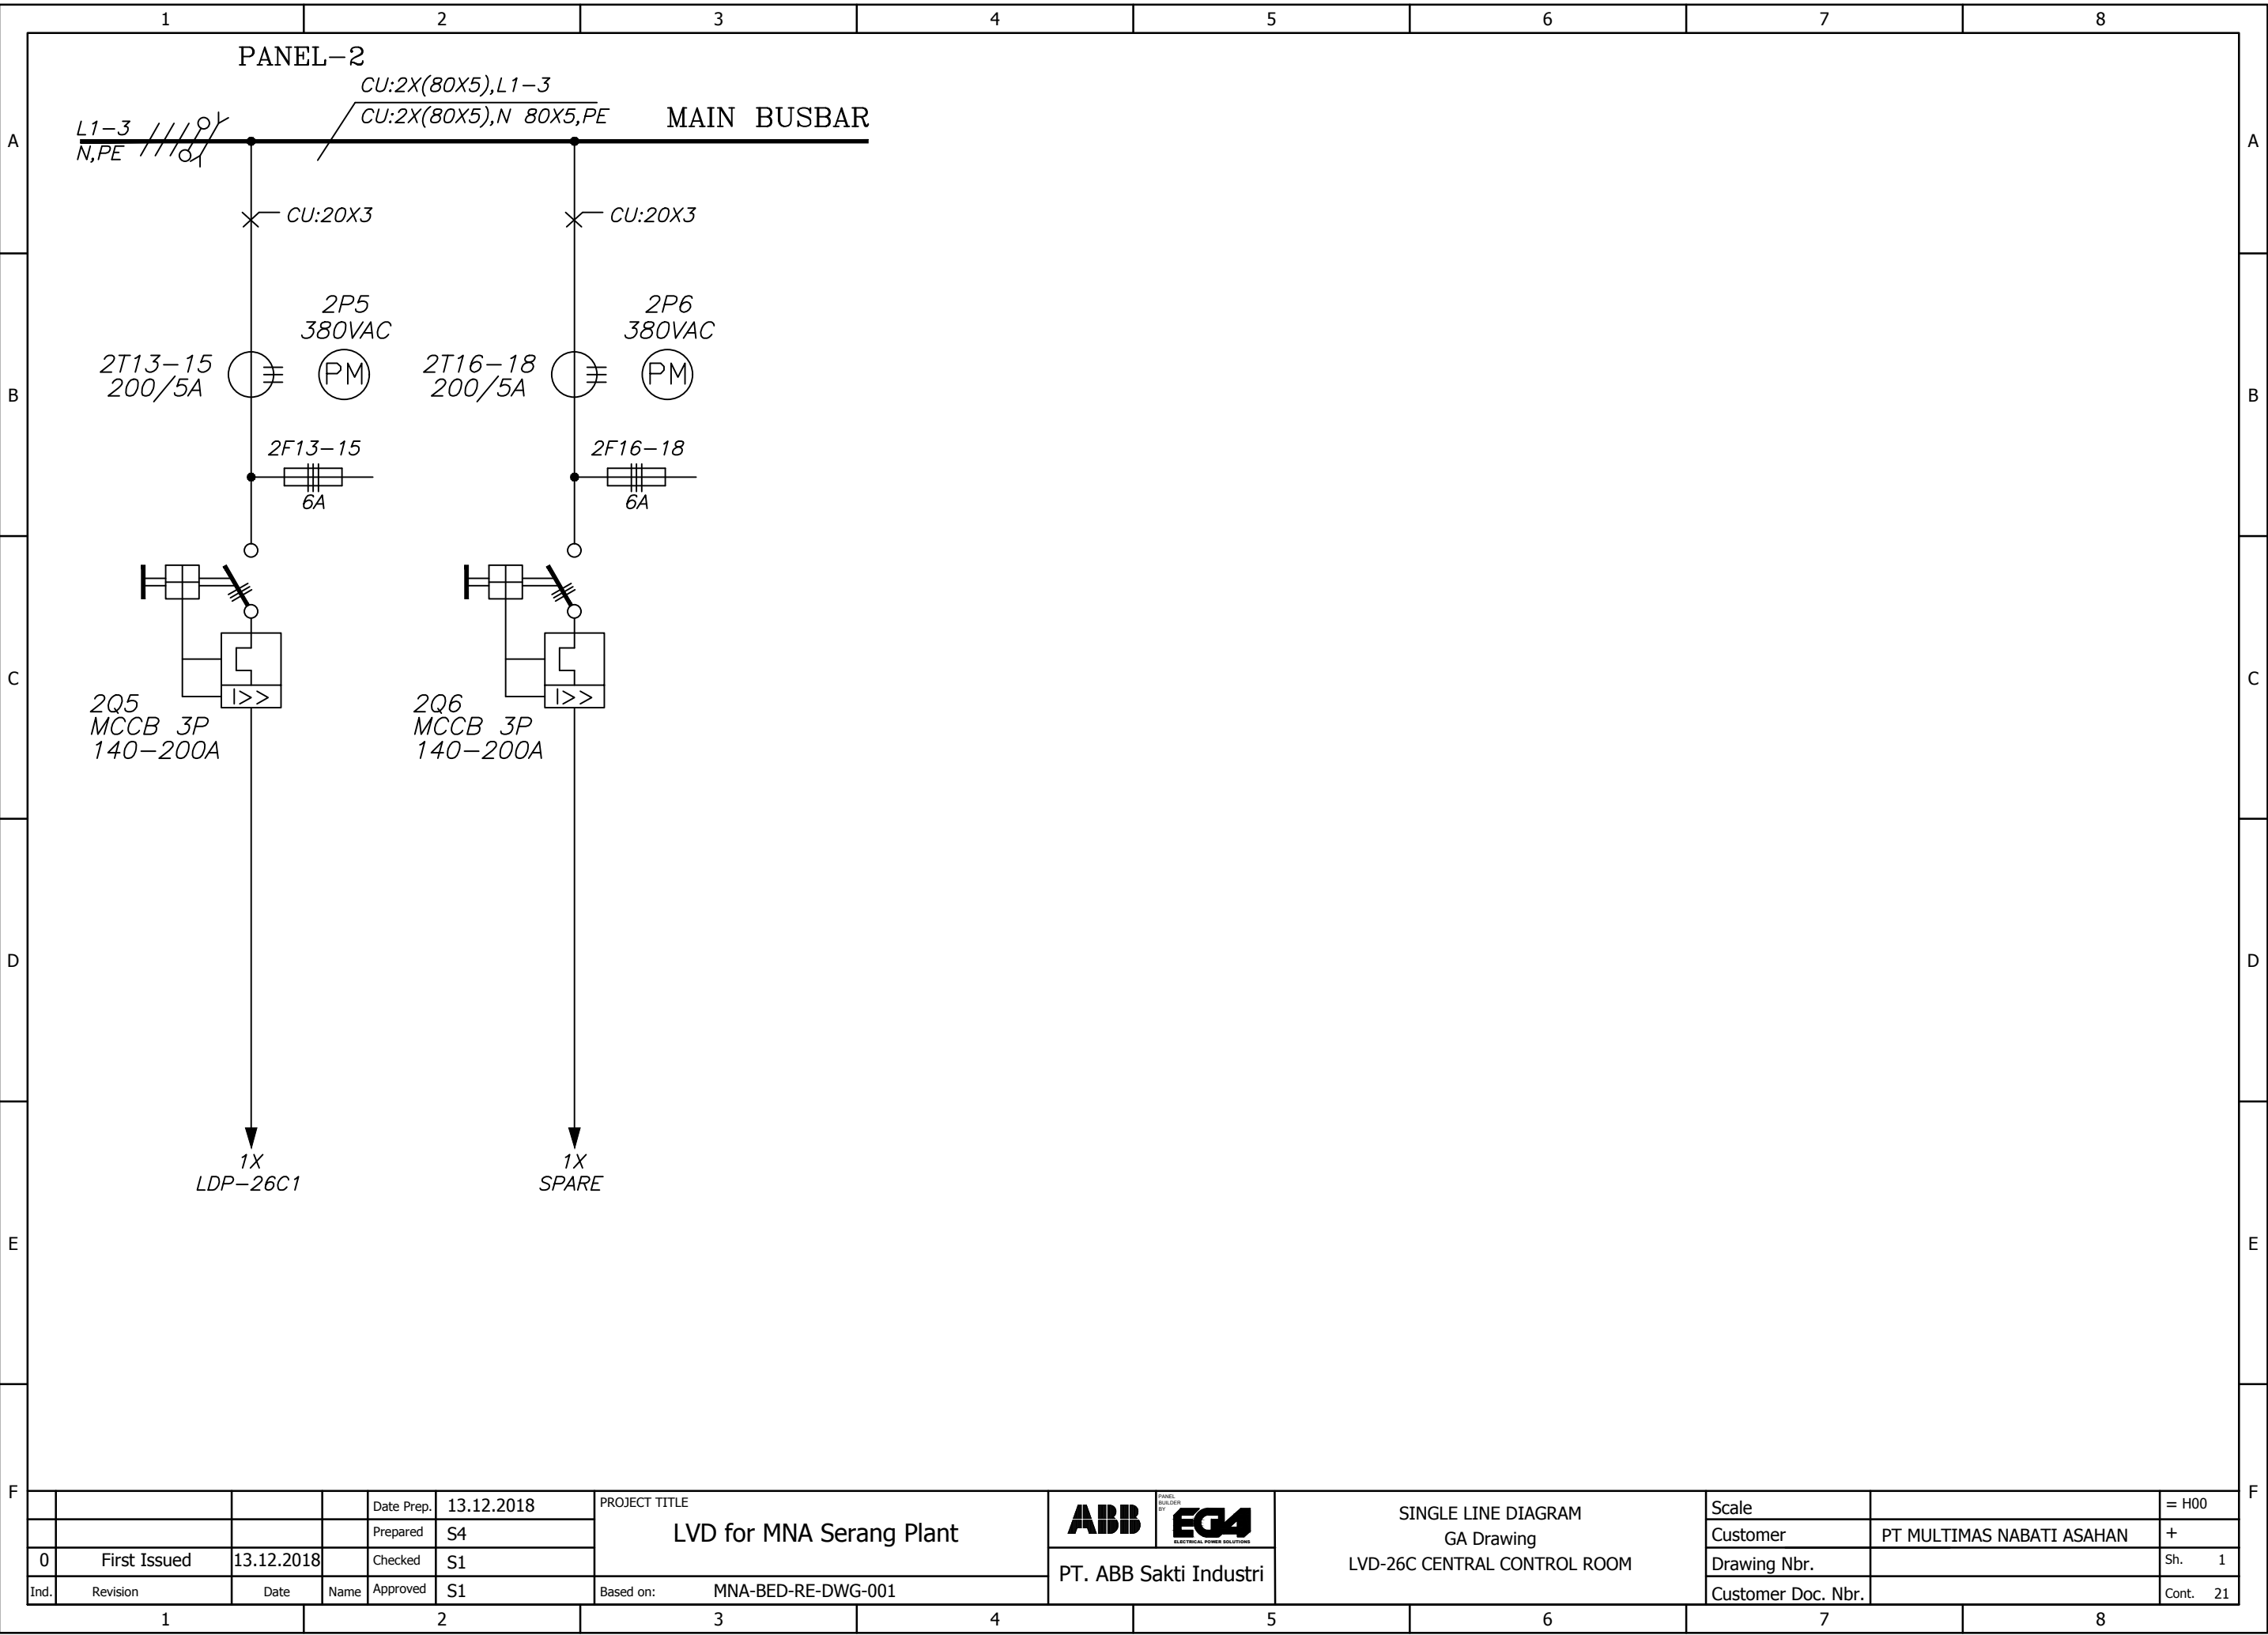


WE RESERVE ALL RIGHTS IN THIS DOCUMENT AND IN THE INFORMATION CONTAINED THEREIN. REPRODUCTION, USE OR DISCLOSURE TO THIRD PARTIES WITHOUT EXPRESS AUTHORITY IS STRICTLY FORBIDDEN.

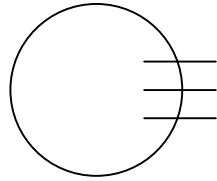


CT

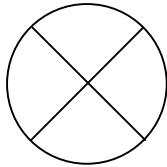


PILOT LAMP

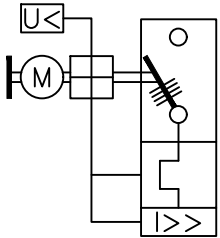

ACB

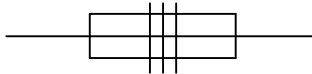

FUSE

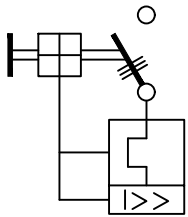


MCCB



DIGITAL POWER METER

				Date Prep.	13.12.2018	PROJECT TITLE LVD for MNA Serang Plant		  PT. ABB Sakti Industri	LEGEND GA Drawing LVD-26C CENTRAL CONTROL ROOM	Scale		= H00
				Prepared	S4					Customer	PT MULTIMAS NABATI ASAHAN	+
0	First Issued	13.12.2018		Checked	S1					Drawing Nbr.		Sh. 1
Ind.	Revision	Date	Name	Approved	S1	Based on:	MNA-BED-RE-DWG-001			Customer Doc. Nbr.		Cont. 21


WE RESERVE ALL RIGHTS IN THIS DOCUMENT AND IN THE INFORMATION CONTAINED THEREIN. REPRODUCTION, USE OR DISCLOSURE TO THIRD PARTIES WITHOUT EXPRESS AUTHORITY IS STRICTLY FORBIDDEN.

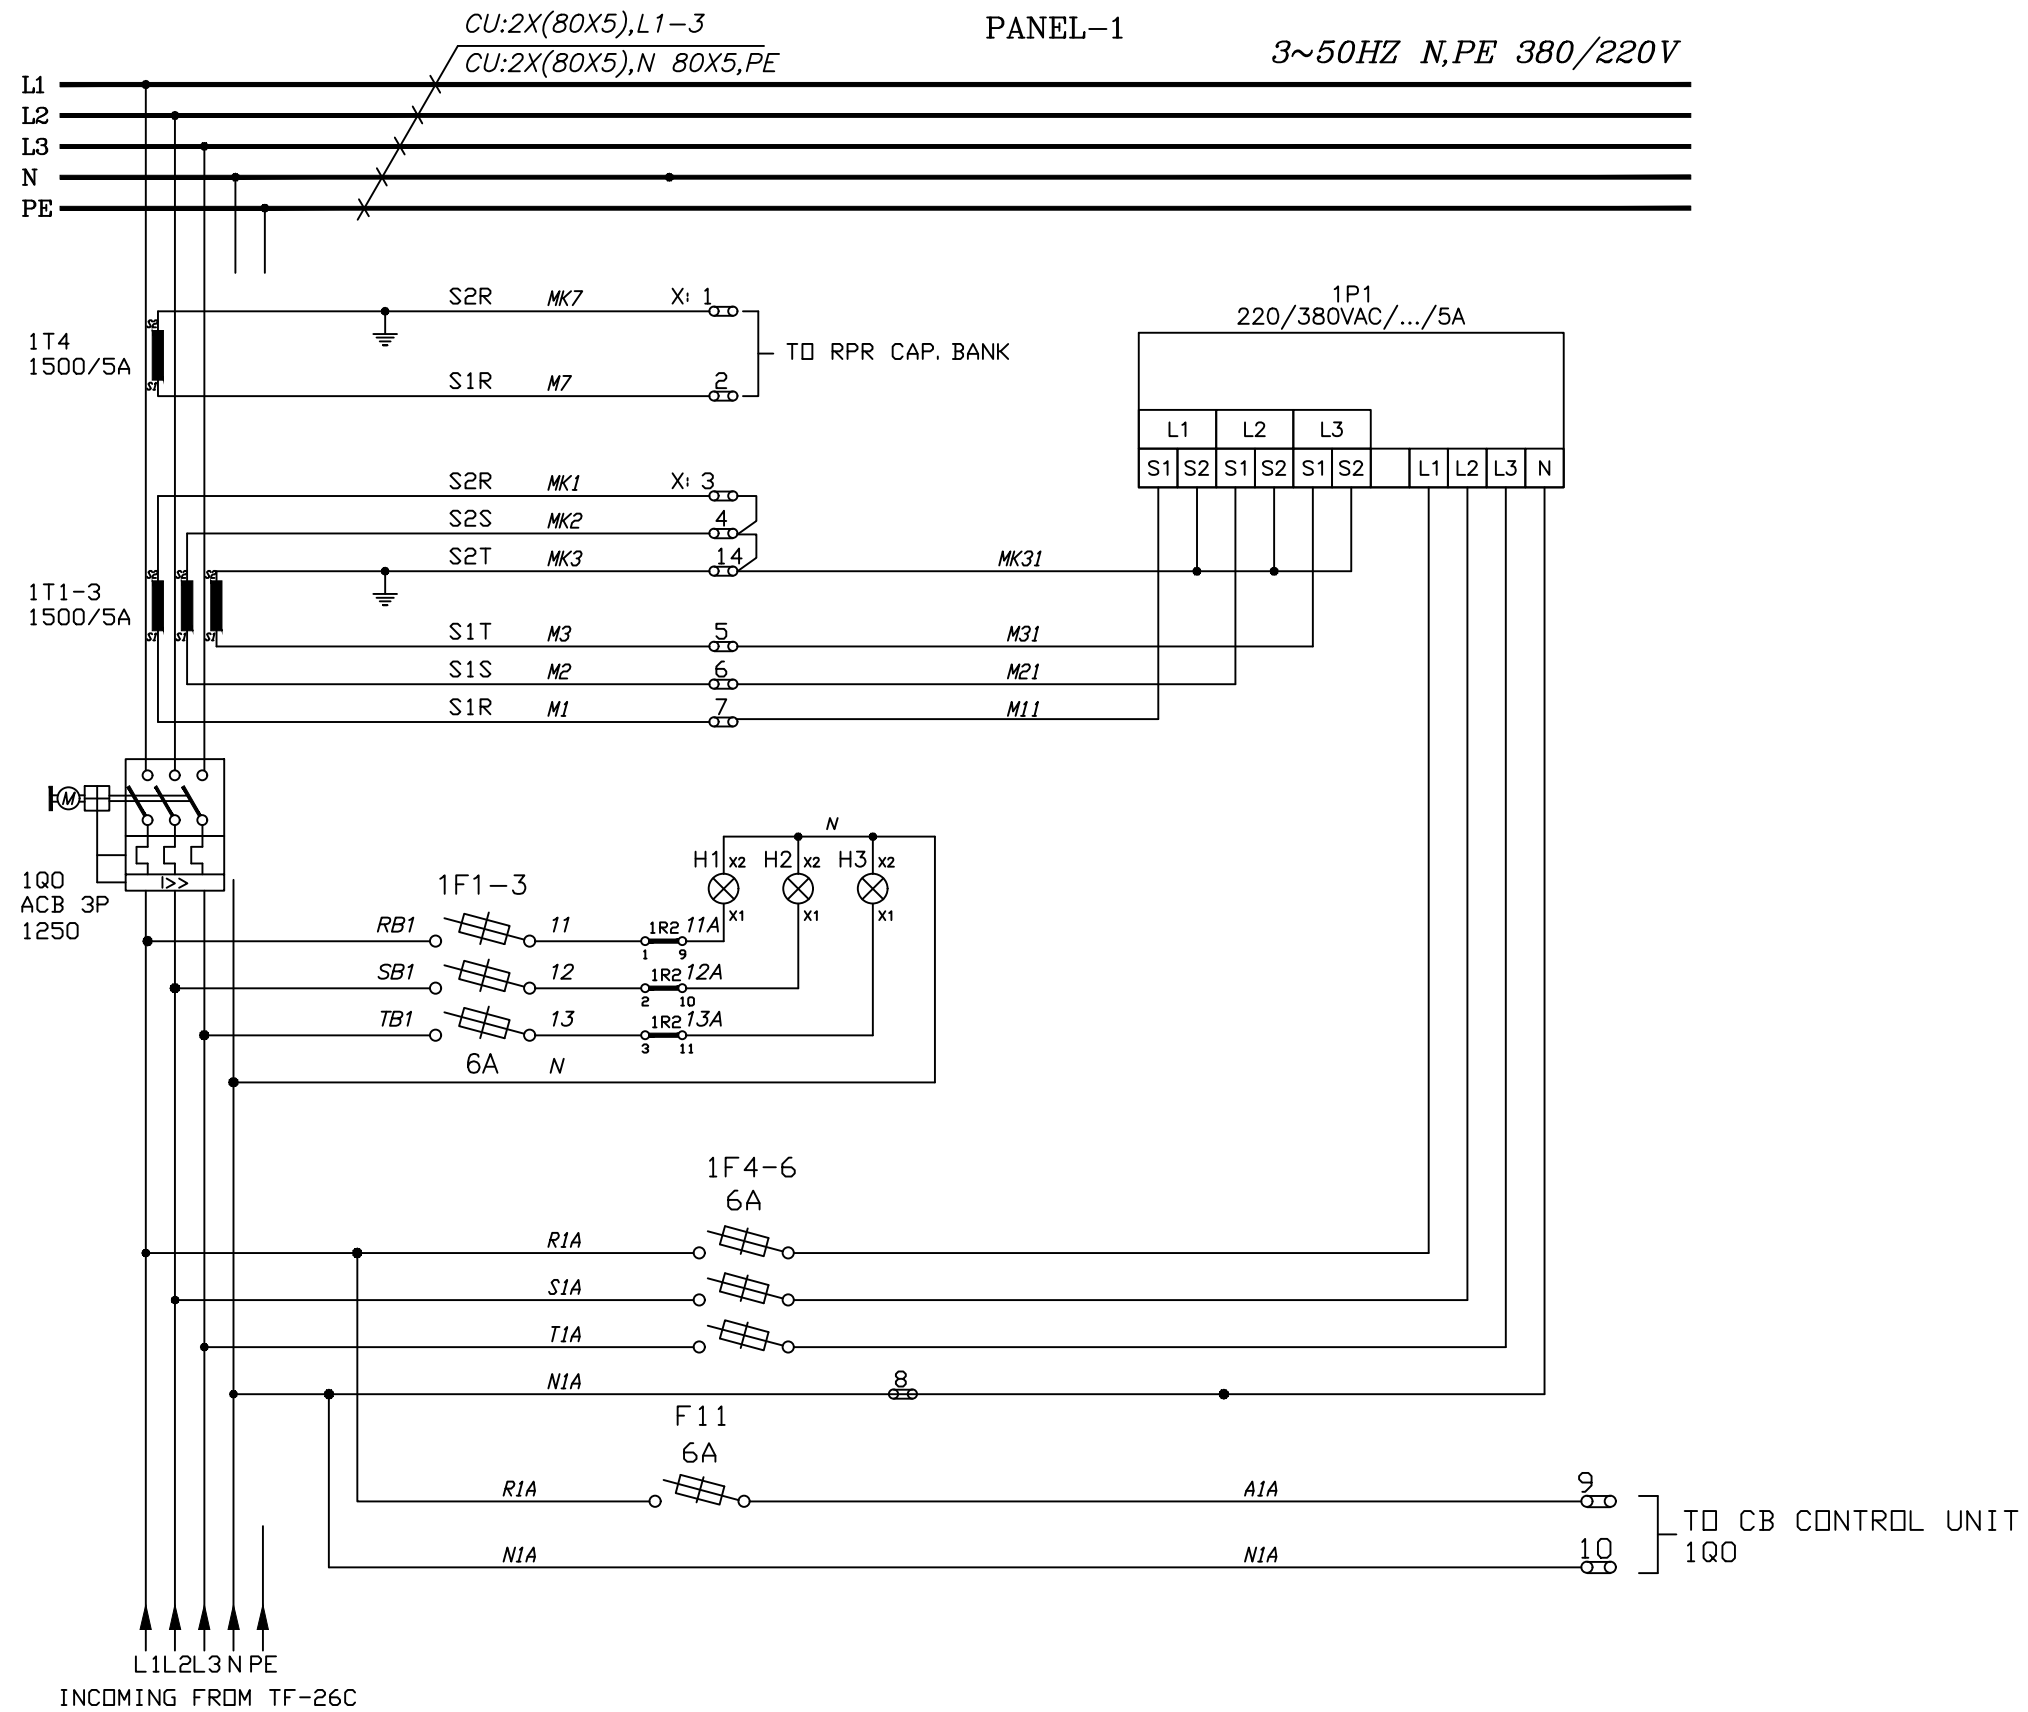

				Date Prep.	13.12.2018	PROJECT TITLE LVD for MNA Serang Plant	ABB PANEL BUILDER BY EG4 ELECTRICAL POWER SOLUTIONS	WIRING CONTROL DIAGRAM GA Drawing LVD-26C CENTRAL CONTROL ROOM	Scale		= H00
				Prepared	S4				Customer	PT MULTIMAS NABATI ASAHAN	+
0	First Issued	13.12.2018		Checked	S1				Drawing Nbr.		Sh. 1
Ind.	Revision	Date	Name	Approved	S1	Based on:	MNA-BED-RE-DWG-001	PT. ABB Sakti Industri	Customer Doc. Nbr.		Cont. 21


1 2 3 4 5 6 7 8

CB CONTROL UNIT (1Q0)
PANEL-1

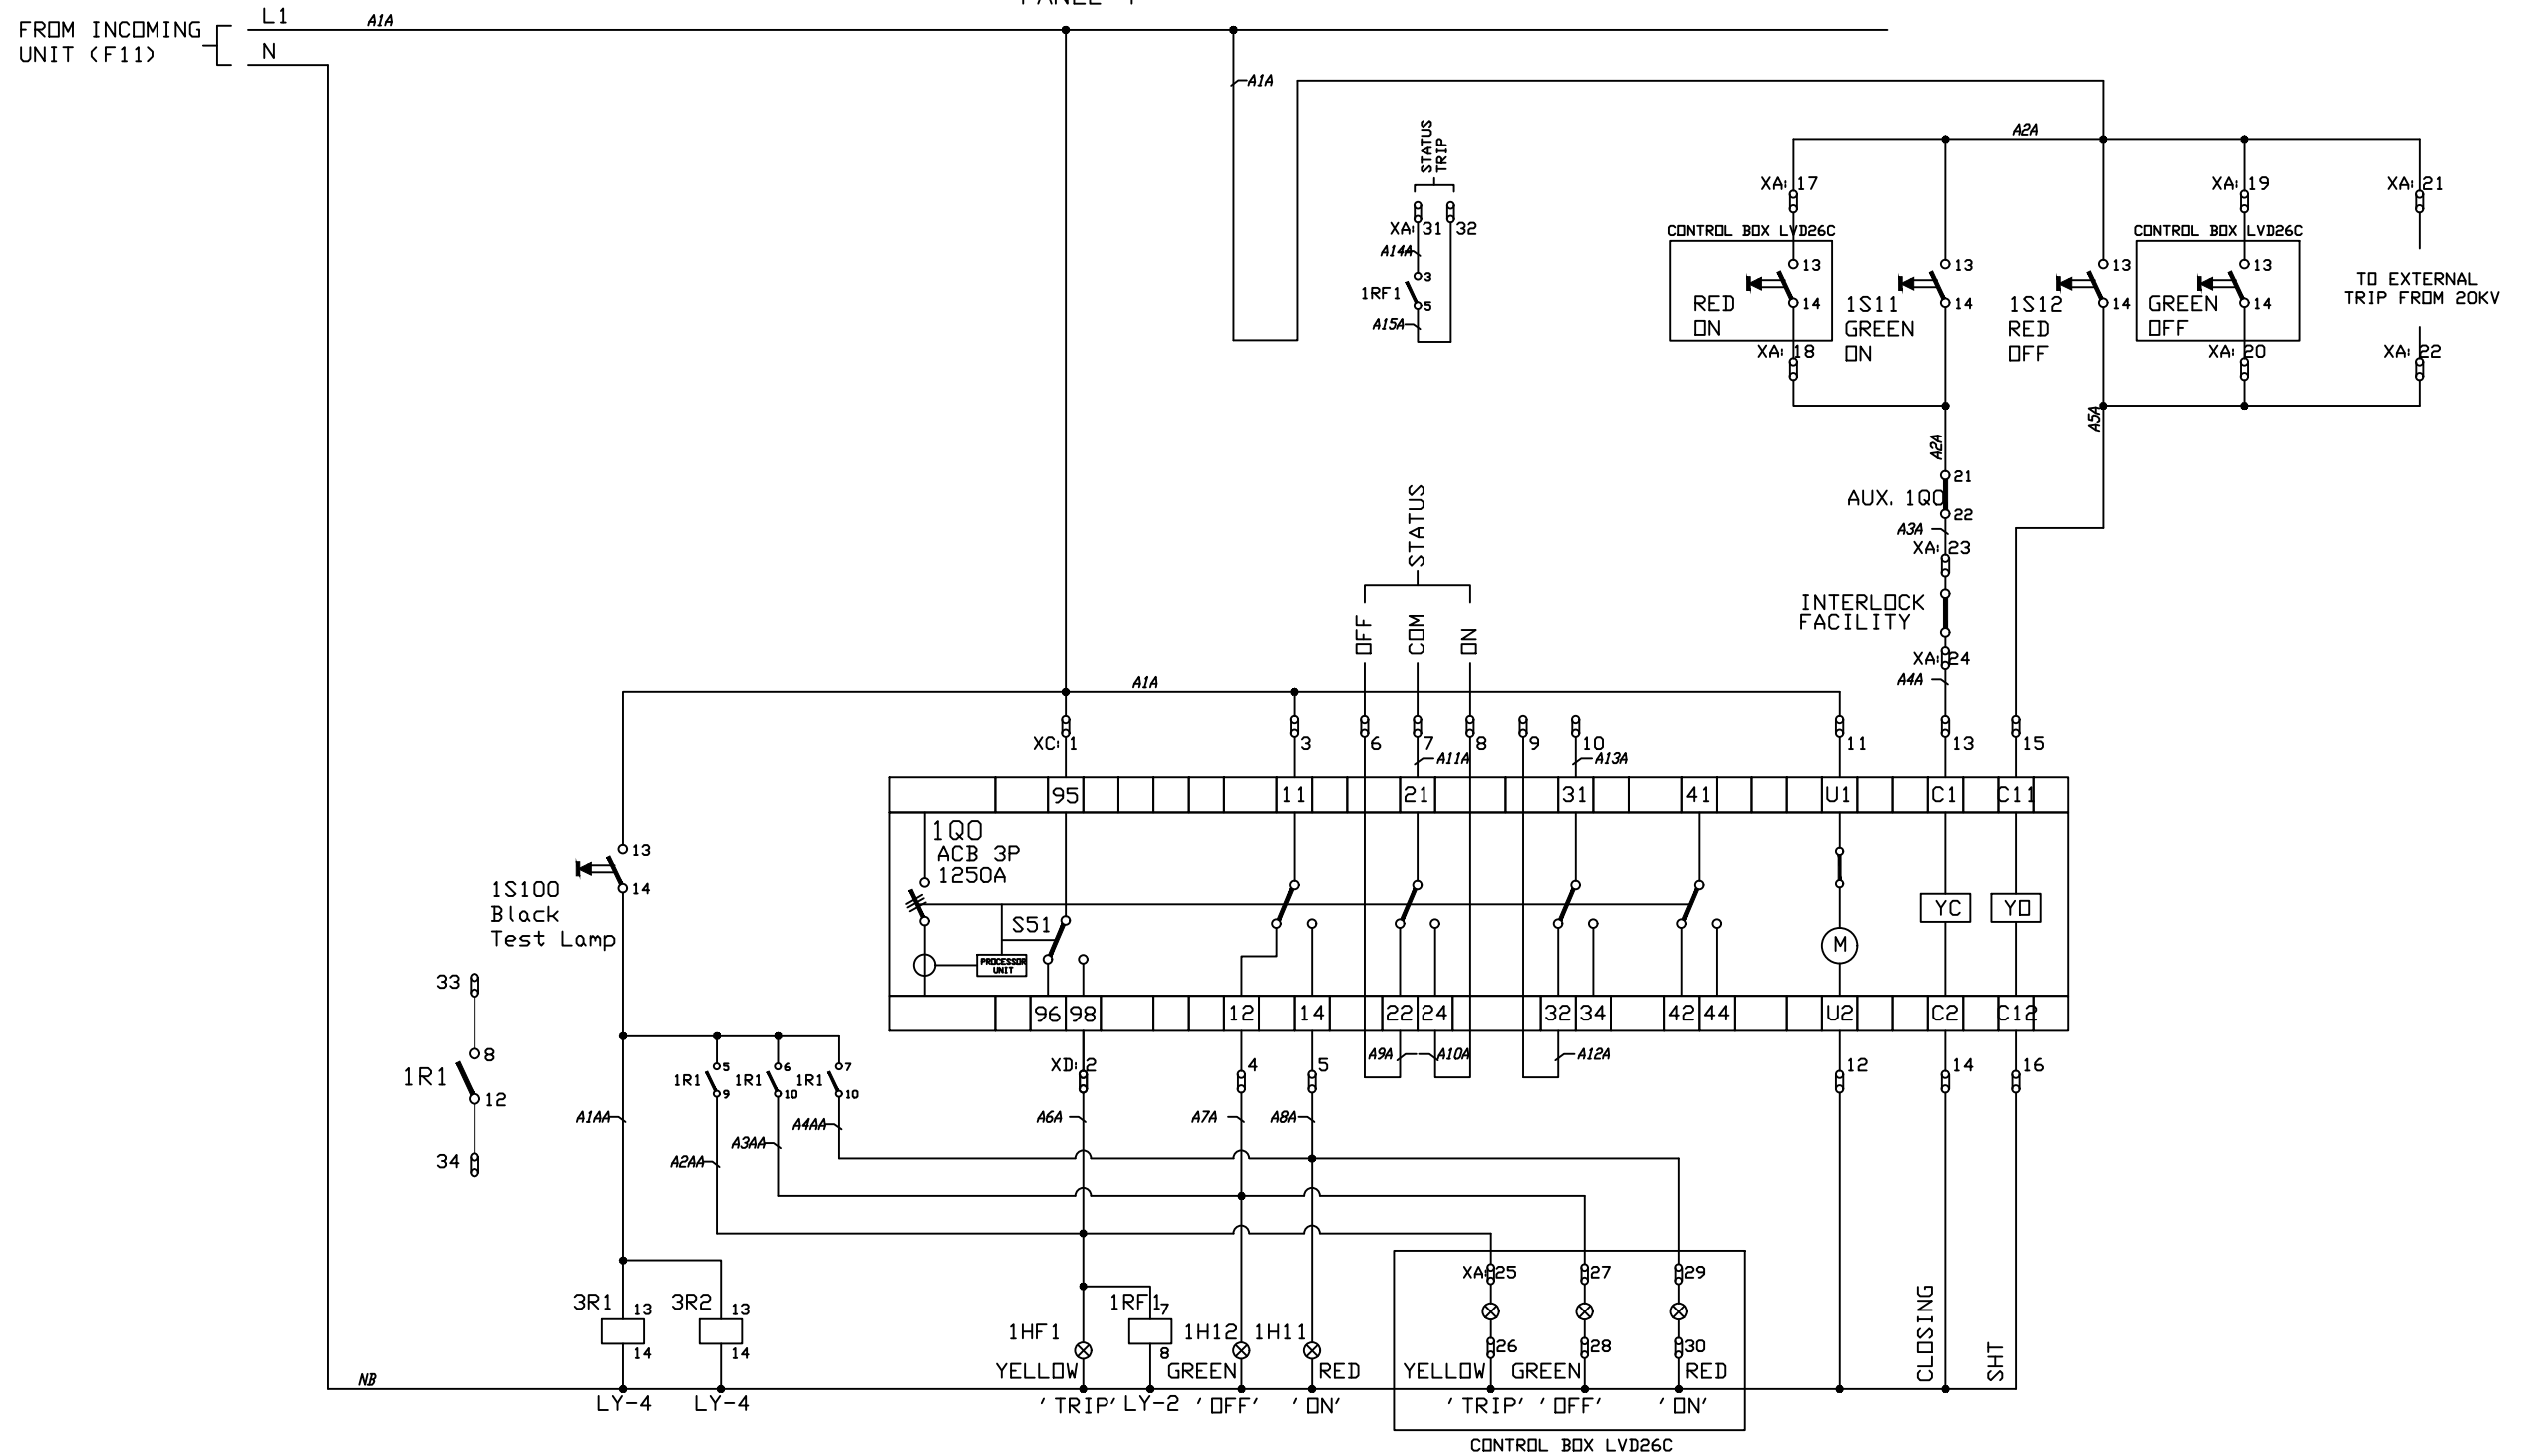


		Date Prep.	13.12.2018	PROJECT TITLE LVD for MNA Serang Plant		  PT. ABB Sakti Industri		WIRING CONTROL DIAGRAM GA Drawing LVD-26C CENTRAL CONTROL ROOM		Scale	= H00	
		Prepared	S4							Customer	PT MULTIMAS NABATI ASAHAN	+
0		First Issued	13.12.2018	Checked	S1					Drawing Nbr.		Sh. 1
Ind.	Revision	Date	Name	Approved	S1	Based on:	MNA-BED-RE-DWG-001			Customer Doc. Nbr.		Cont. 21

WE RESERVE ALL RIGHTS IN THIS DOCUMENT AND IN THE INFORMATION CONTAINED THEREIN. REPRODUCTION, USE OR DISCLOSURE TO THIRD PARTIES WITHOUT EXPRESS AUTHORITY IS STRICTLY FORBIDDEN.

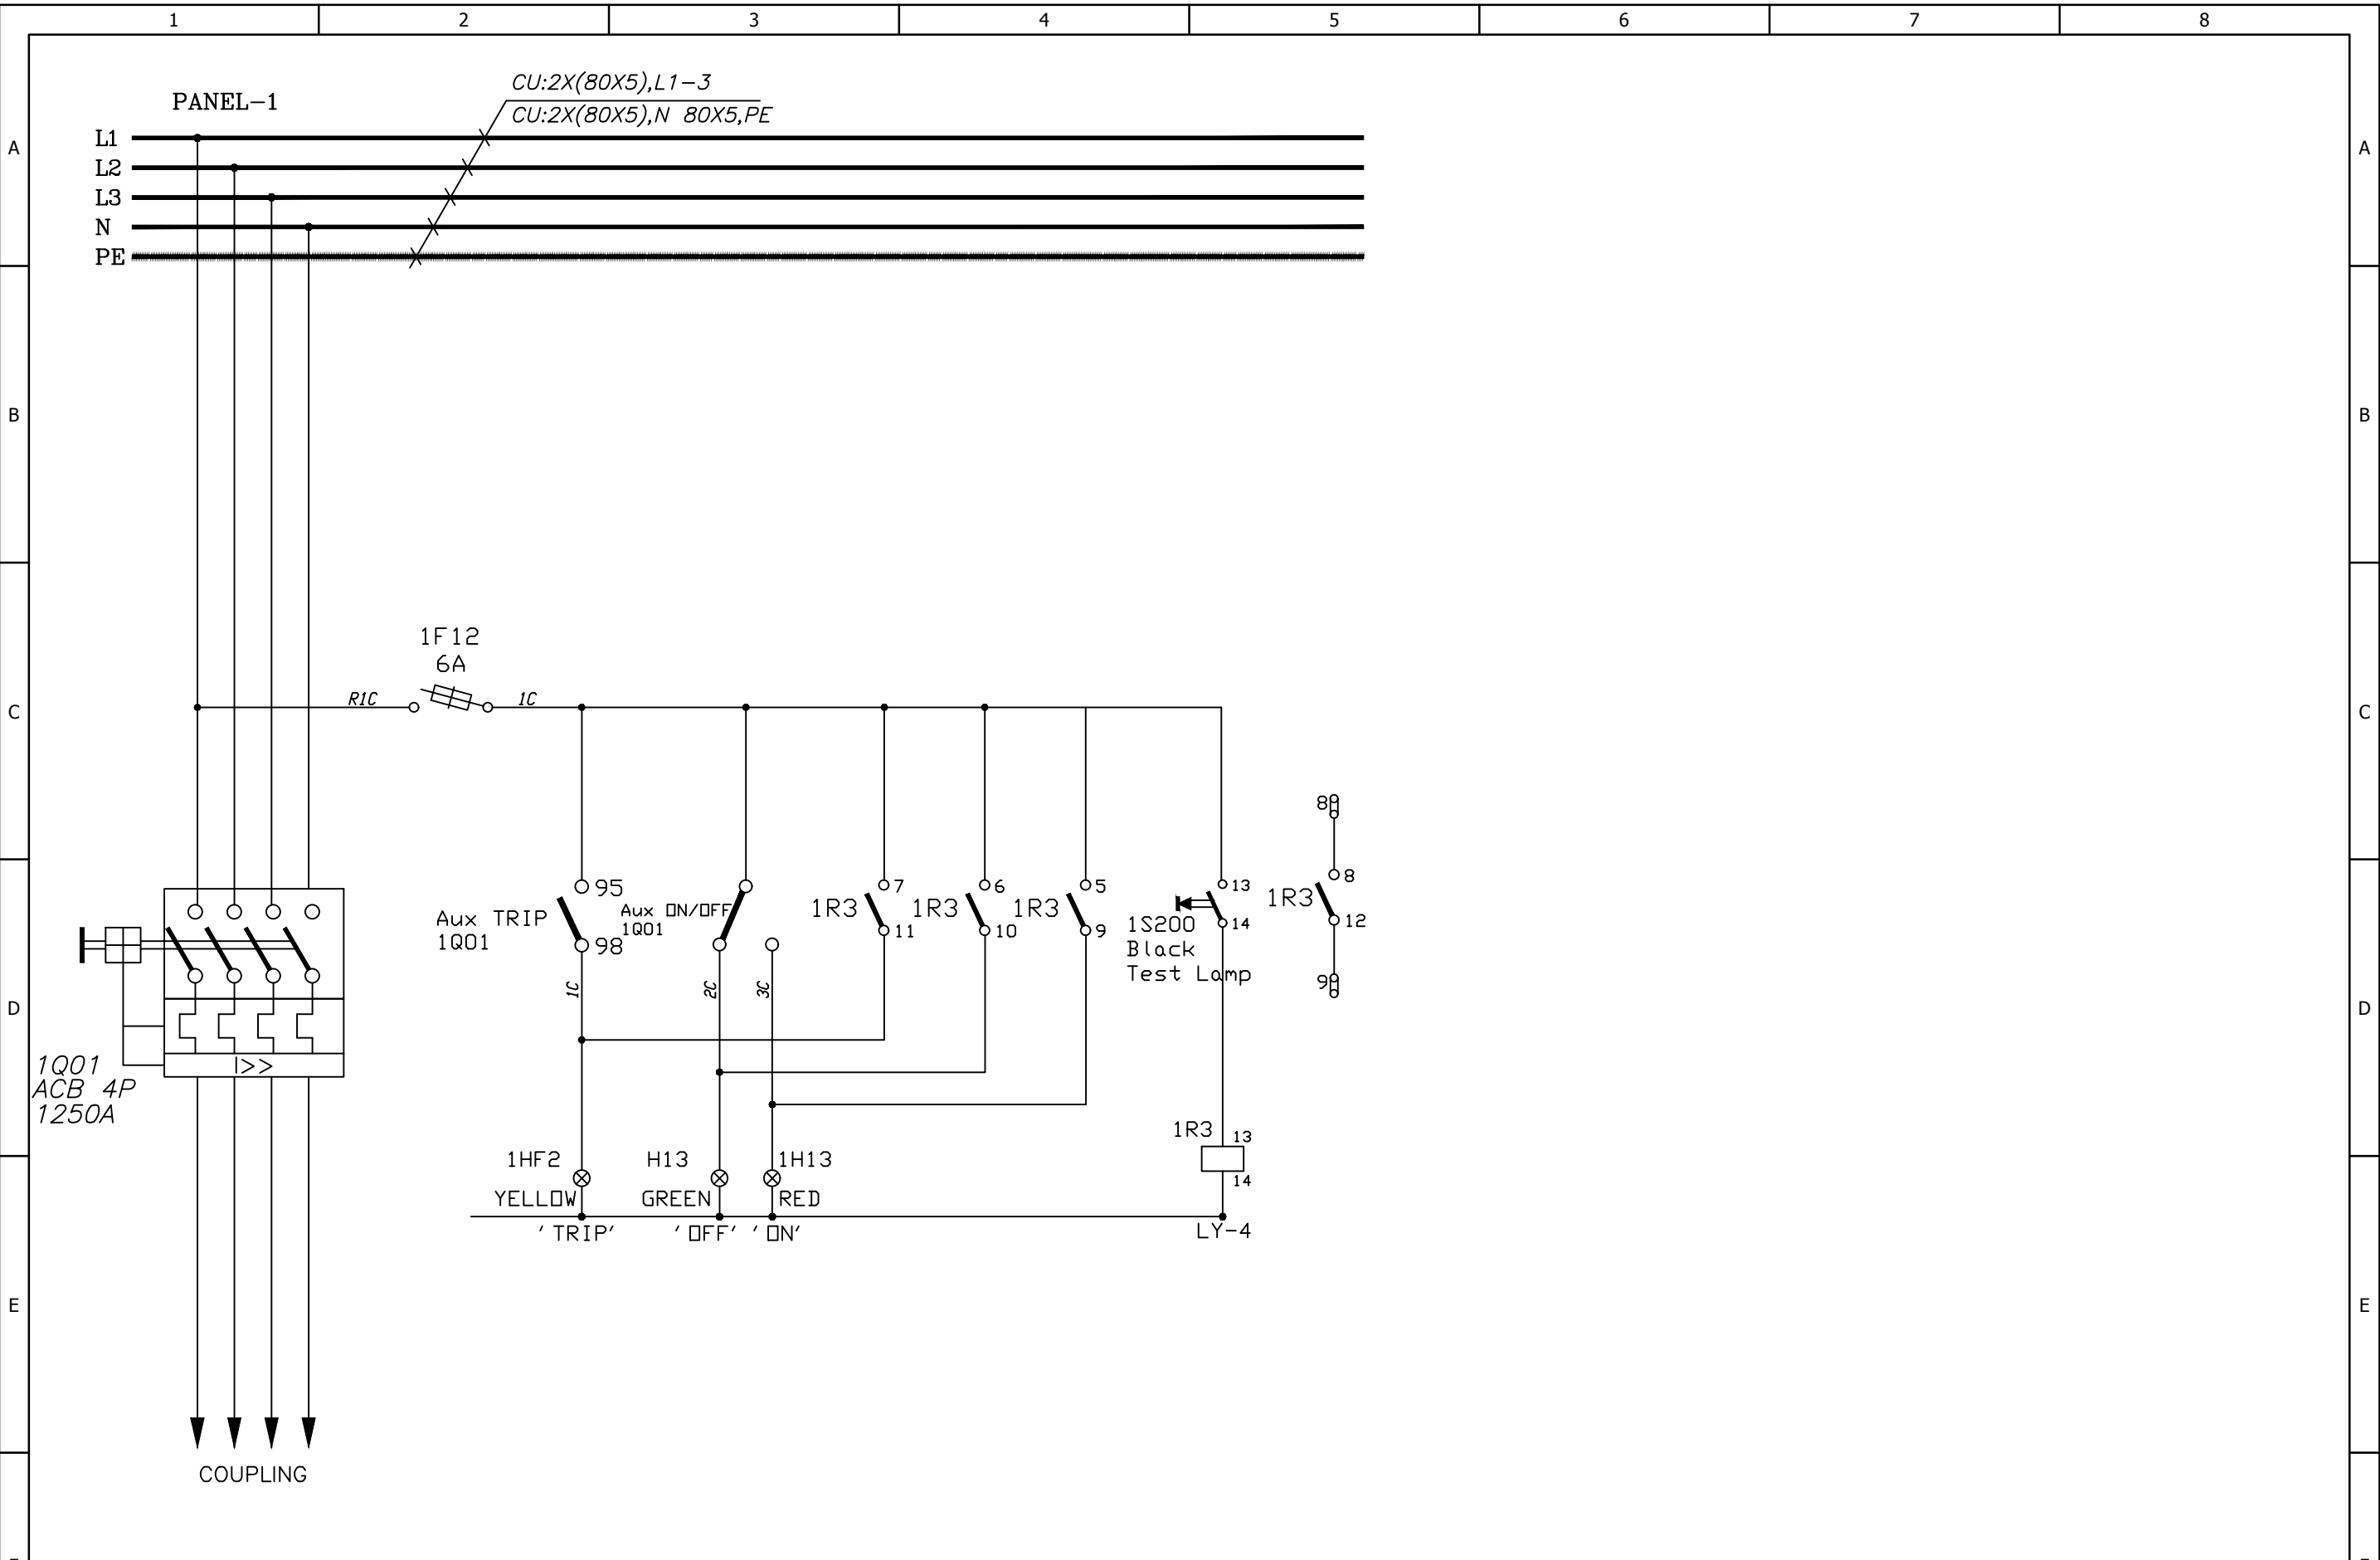


		Date Prep.		13.12.2018	PROJECT TITLE	ABB PANEL BUILDING BY EG4 ELECTRICAL POWER SOLUTIONS	WIRING CONTROL DIAGRAM GA Drawing LVD-26C CENTRAL CONTROL ROOM	Scale		= H00
		Prepared		S4				Customer	PT MULTIMAS NABATI ASAHAN	+
0		First Issued	13.12.2018	Checked	S1			Drawing Nbr.		Sh. 1
Ind.	Revision	Date	Name	Approved	S1	Based on:	MNA-BED-RE-DWG-001	Customer Doc. Nbr.		Cont. 21


WE RESERVE ALL RIGHTS IN THIS DOCUMENT AND IN THE INFORMATION CONTAINED THEREIN. REPRODUCTION, USE OR DISCLOSURE TO THIRD PARTIES WITHOUT EXPRESS AUTHORITY IS STRICTLY FORBIDDEN.

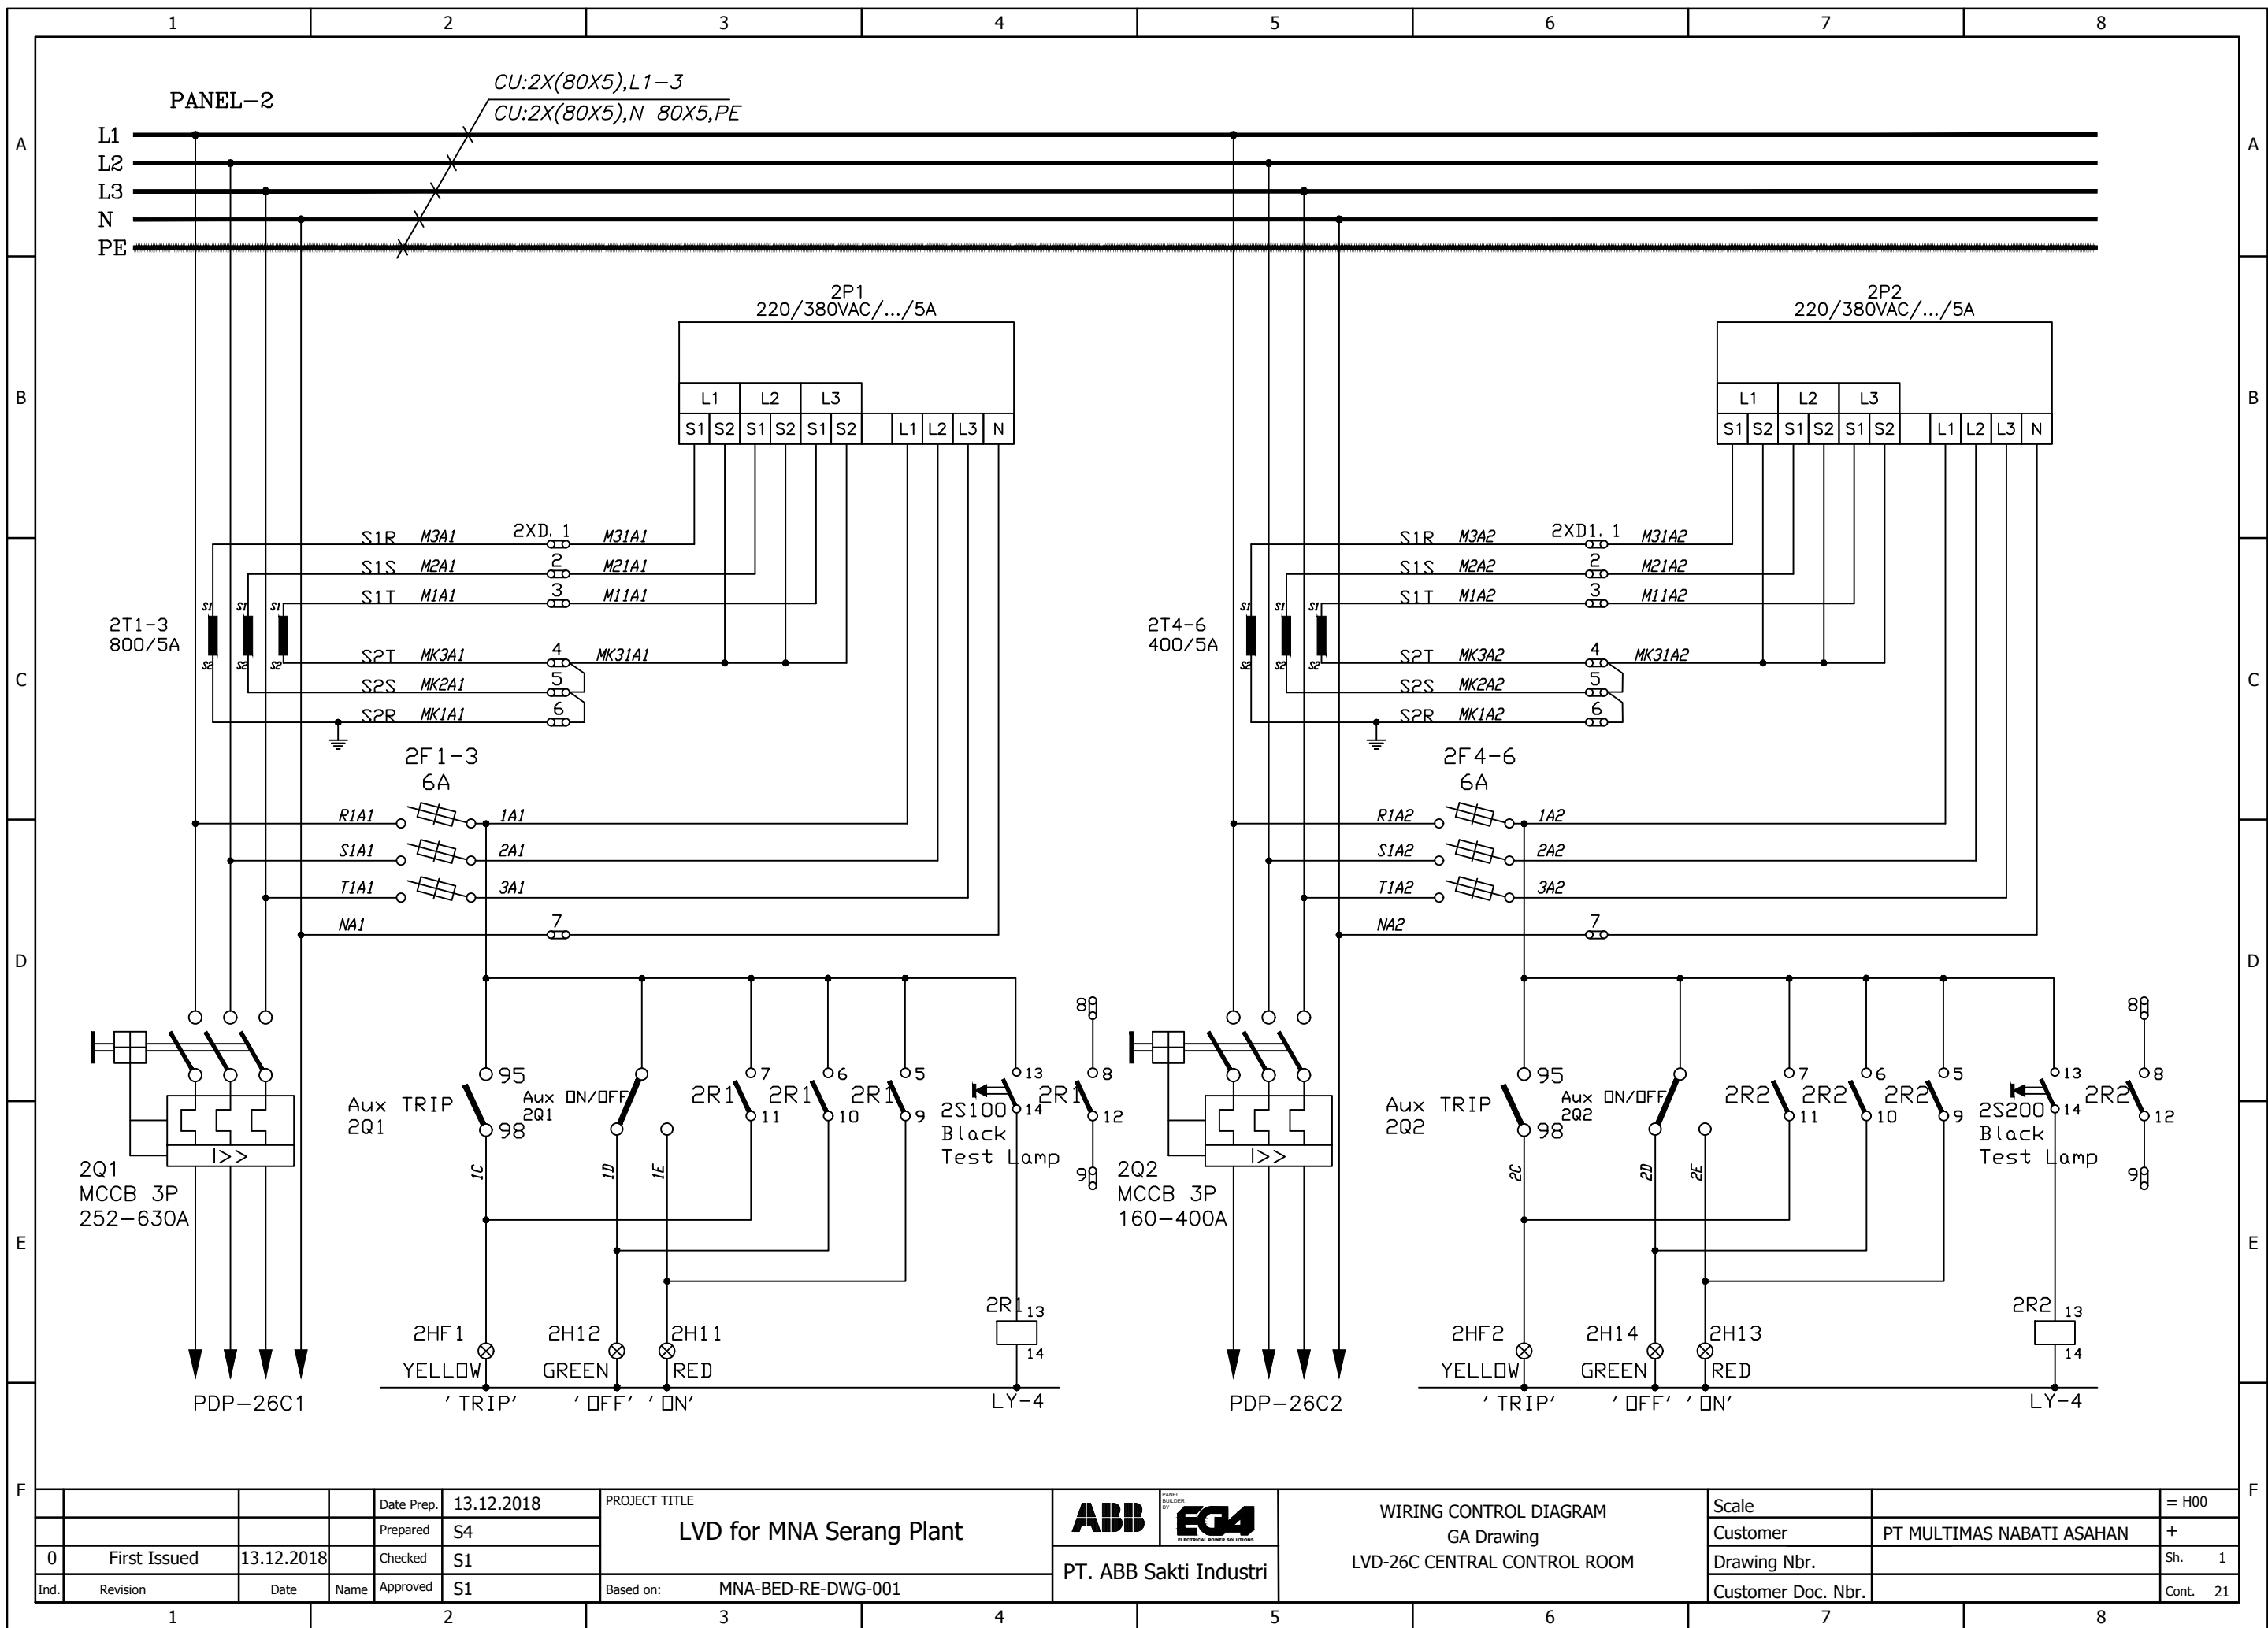

WE RESERVE ALL RIGHTS IN THIS DOCUMENT AND IN THE INFORMATION CONTAINED THEREIN. REPRODUCTION, USE OR DISCLOSURE TO THIRD PARTIES WITHOUT EXPRESS AUTHORITY IS STRICTLY FORBIDDEN.

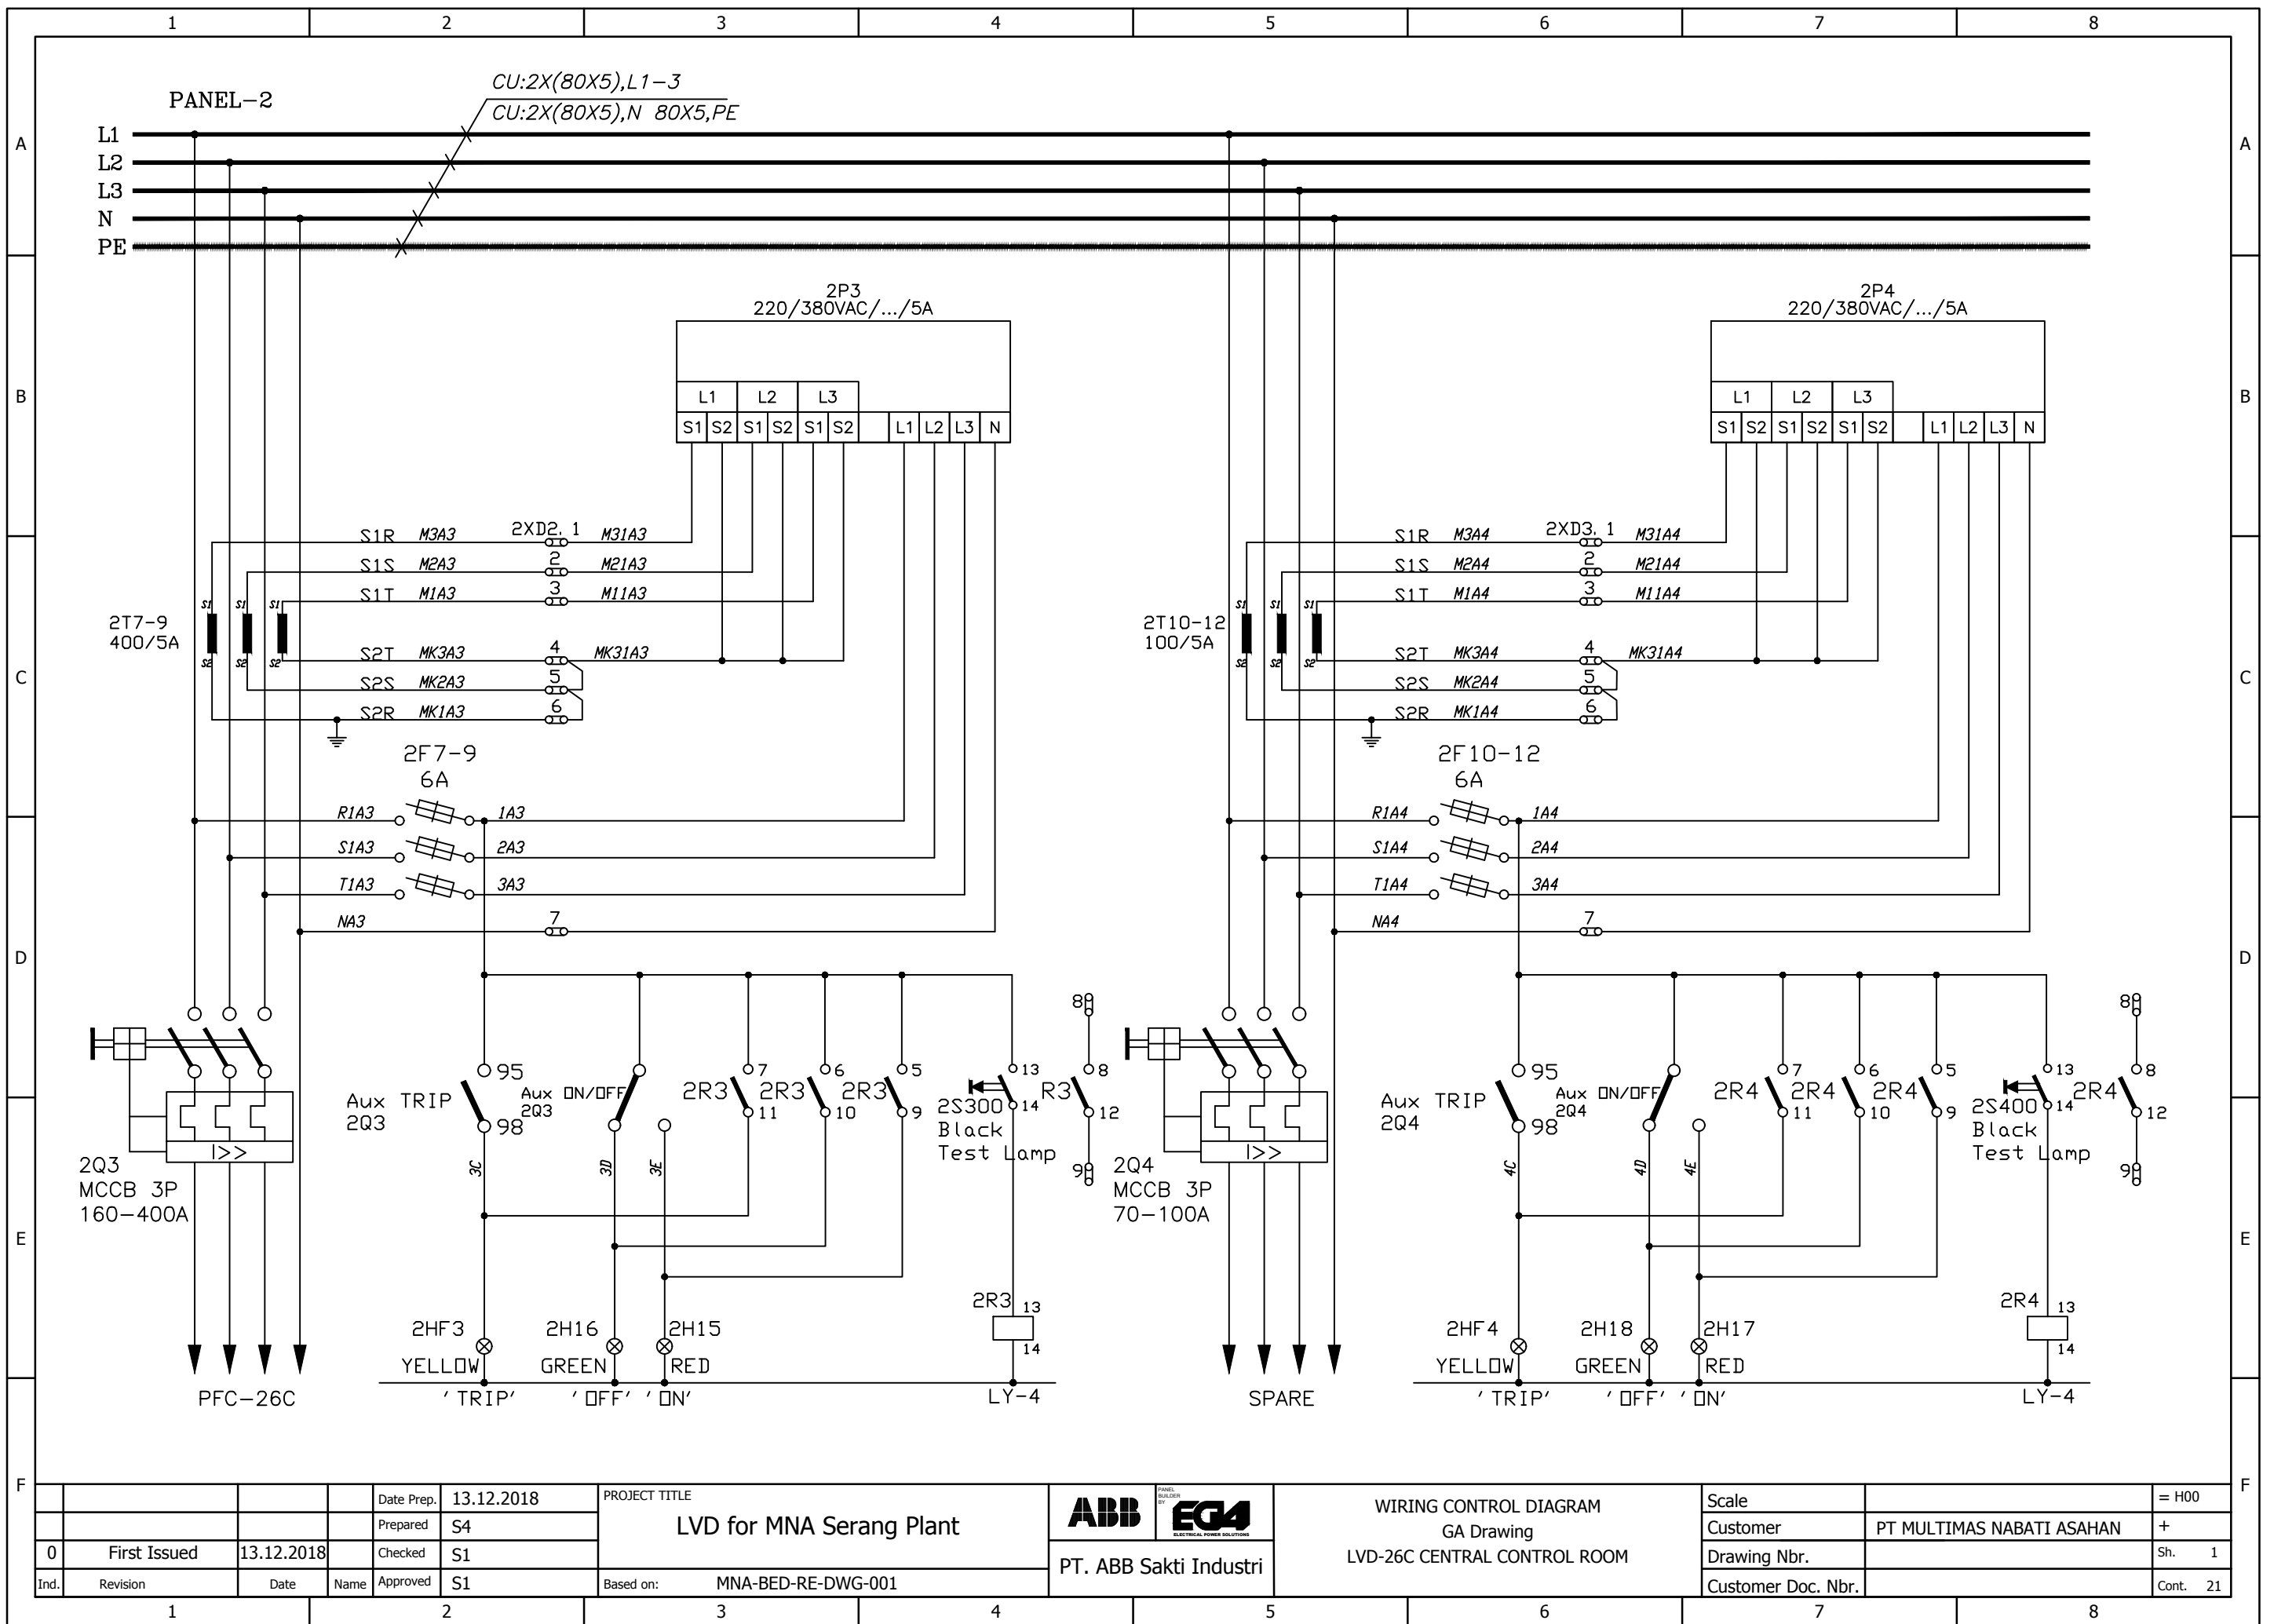

WE RESERVE ALL RIGHTS IN THIS DOCUMENT AND IN THE INFORMATION CONTAINED THEREIN. REPRODUCTION, USE OR DISCLOSURE TO THIRD PARTIES WITHOUT EXPRESS AUTHORITY IS STRICTLY FORBIDDEN.

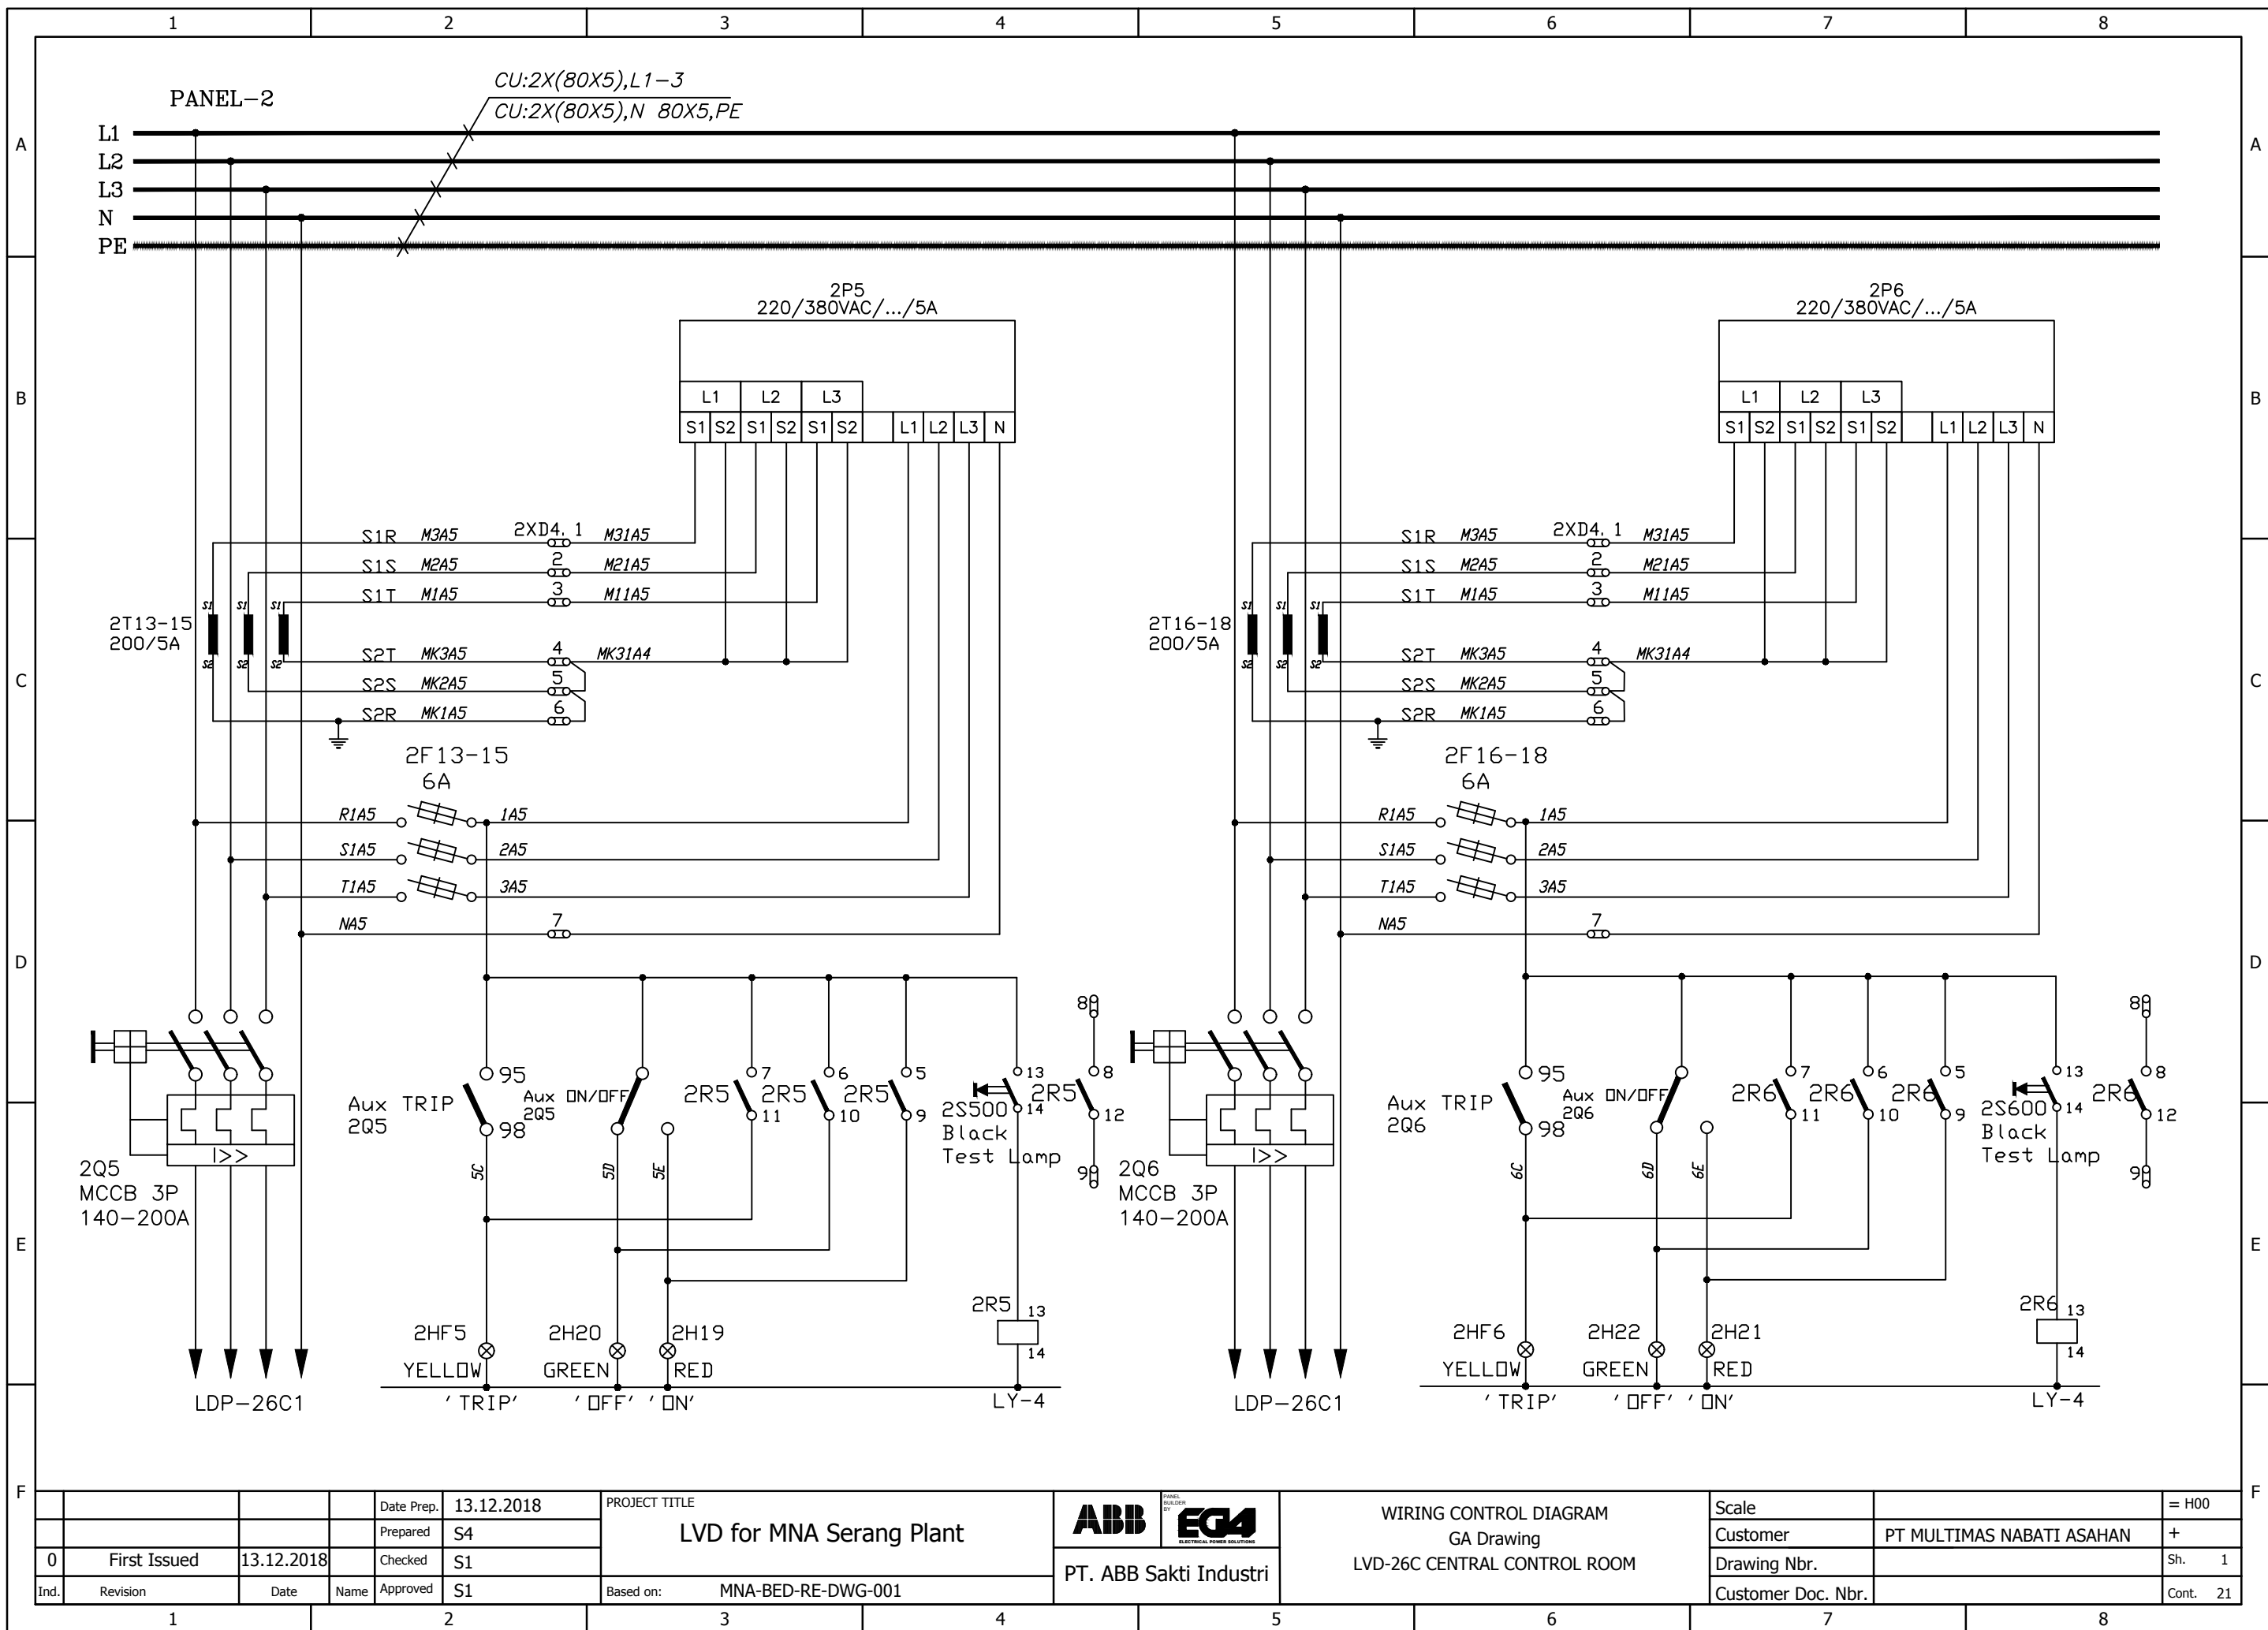

WE RESERVE ALL RIGHTS IN THIS DOCUMENT AND IN THE INFORMATION CONTAINED THEREIN. REPRODUCTION, USE OR DISCLOSURE TO THIRD PARTIES WITHOUT EXPRESS AUTHORITY IS STRICTLY FORBIDDEN.

1		2		3		4		5		6		7		8			
A	N O	DESCRIPTION			TECHNICAL DATA			QTY	DESIGNATION								
		INCOMING															
B	1	Fuse Carrier 6A			AXLE/Setara			7	1F11,1F1-6								
	2	Pilot Lamp (LED) 220Vac/50Hz, Red			AXLE/Setara			2	1H1,11								
	3	Pilot Lamp (LED) 220Vac/50Hz, Yellow			AXLE/Setara			2	1H2,HF1								
	4	Pilot Lamp (LED) 220Vac/50Hz, Green			AXLE/Setara			2	1H3,H12								
	5	DIGITAL POWER METER (*)			ABB, M2M ETHERNET			1	1P1								
	6	CT 1500/5A CL.0.5 20VA			Howig, HG 82-1500			4	1T1-4								
C	7	ACB 3P 1250A, 50KA, DO, Ekip Touch LSIG (*)			ABB, E1.2C12 D/O			1	1Q0								
	8	+ Shunt Trip Release (Y0) (*)			ABB, Y0			1	-								
	9	+ Motor (M) + Closing Release (YC) For E1.2 (*)			ABB, M+YC			1	-								
	10	+ Padlocks For E1.2 (*)			ABB,			1	-								
	11	+ Ekip Com Protocol IEC 61850 (*)			ABB,			1	-								
	12	Push Button On, 1NO, Green			Ega			1	S11								
	13	Push Button Off, 1NO, Red			Ega			1	S12								
	14	Control Relay 220Vac			Omron, LY-2			1	1RF1								
	15	Control Relay 220Vac			Omron, LY-4			2	1R1-2								
	16	Push Button Test Lamp, 1NO, Green			Ega			1	1S100								
D	17																
	18	COUPLER															
E	19	Fuse Carrier 6A			AXLE/Setara			1	2F12								
	20	Pilot Lamp (LED) 220Vac/50Hz, Red			AXLE/Setara			1	1H13								
	21	Pilot Lamp (LED) 220Vac/50Hz, Yellow			AXLE/Setara			1	1HF2								
	22	Pilot Lamp (LED) 220Vac/50Hz, Green			AXLE/Setara			1	1H14								
	23	ACB 4P 1250A, 50KA, FT, Ekip Dip LI (*)			ABB, E1.2C12 F/T			1	1Q01								
	24	Push Button Test Lamp , 1NO, Black			Ega			1	1S200								
	25	Control Relay 220Vac			Omron, LY-4			1	1R3								
	26																
F					Date Prep.	13.12.2018	PROJECT TITLE LVD for MNA Serang Plant		 	COMPONENT LIST GA Drawing LVD-26C CENTRAL CONTROL ROOM		Scale			= H00		
					Prepared	S4						Customer		PT MULTIMAS NABATI ASAHAN		+	
	0	First Issued	13.12.2018		Checked	S1						Drawing Nbr.				Sh.	1
	Ind.	Revision		Date	Name	Approved	S1	Based on: MNA-BED-RE-DWG-001				Customer Doc. Nbr.				Cont.	21
	1		2		3		4		5		6		7		8		

