

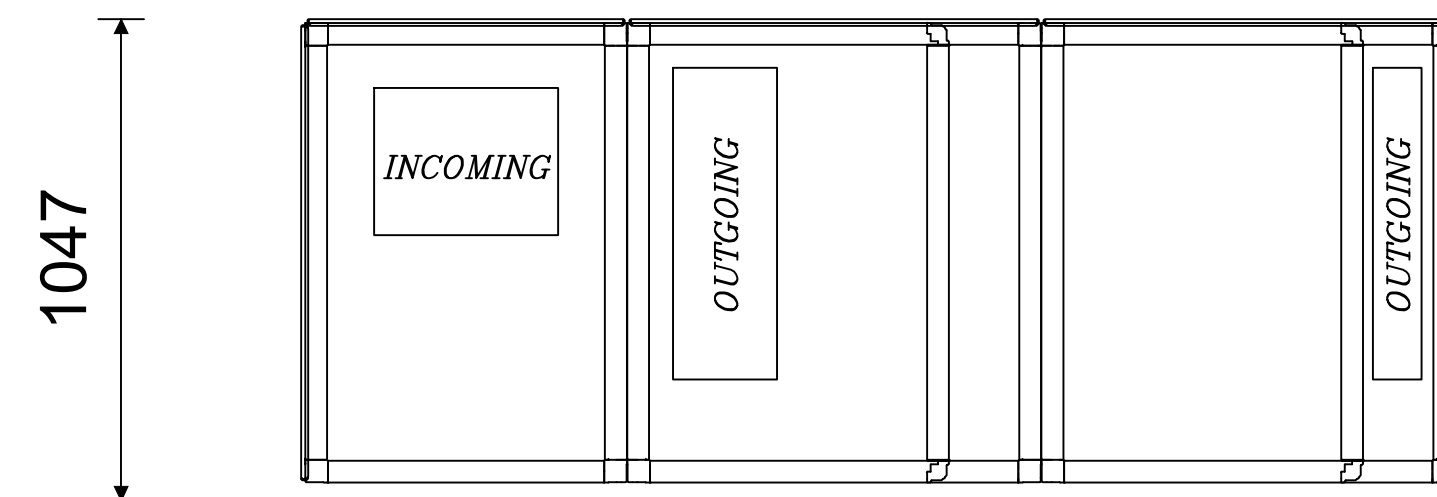


①
②
③

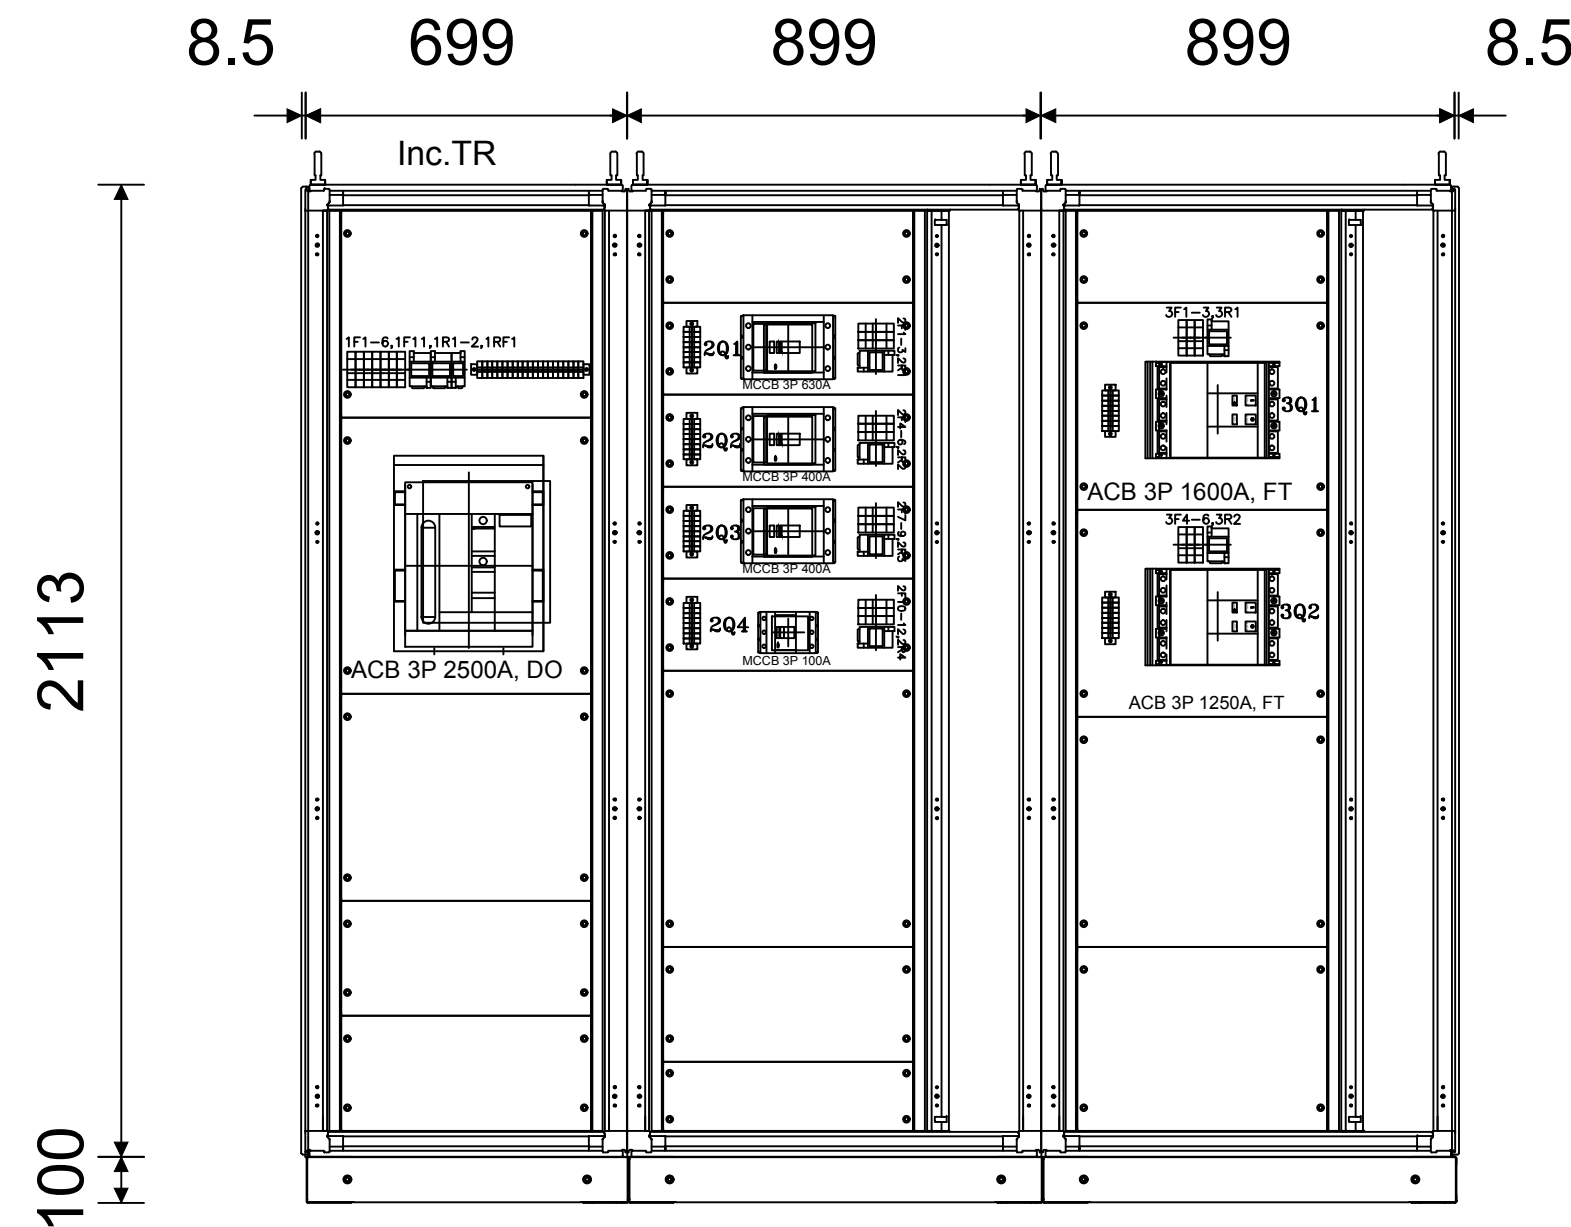

				Date Prep.	13.12.2018	PROJECT TITLE LVD for MNA Serang Plant	 	FRONT VIEW GA Drawing LVD-27A TANKFARM & UNLOADING	Scale		= H00
			Prepared	S4	Customer				PT MULTIMAS NABATI ASAHAN	+	
R1	First Issued	02.05.2019	Checked	S1	Drawing Nbr.					Sh. 1	
Ind.	Revision	Date	Name	Approved	S1	Based on: MNA-BED-RE-DWG-001	PT. ABB Sakti Industri		Customer Doc. Nbr.		Cont. 21

WE RESERVE ALL RIGHTS IN THIS DOCUMENT AND IN THE INFORMATION CONTAINED THEREIN. REPRODUCTION, USE OR DISCLOSURE TO THIRD PARTIES WITHOUT EXPRESS AUTHORITY IS STRICTLY FORBIDDEN.

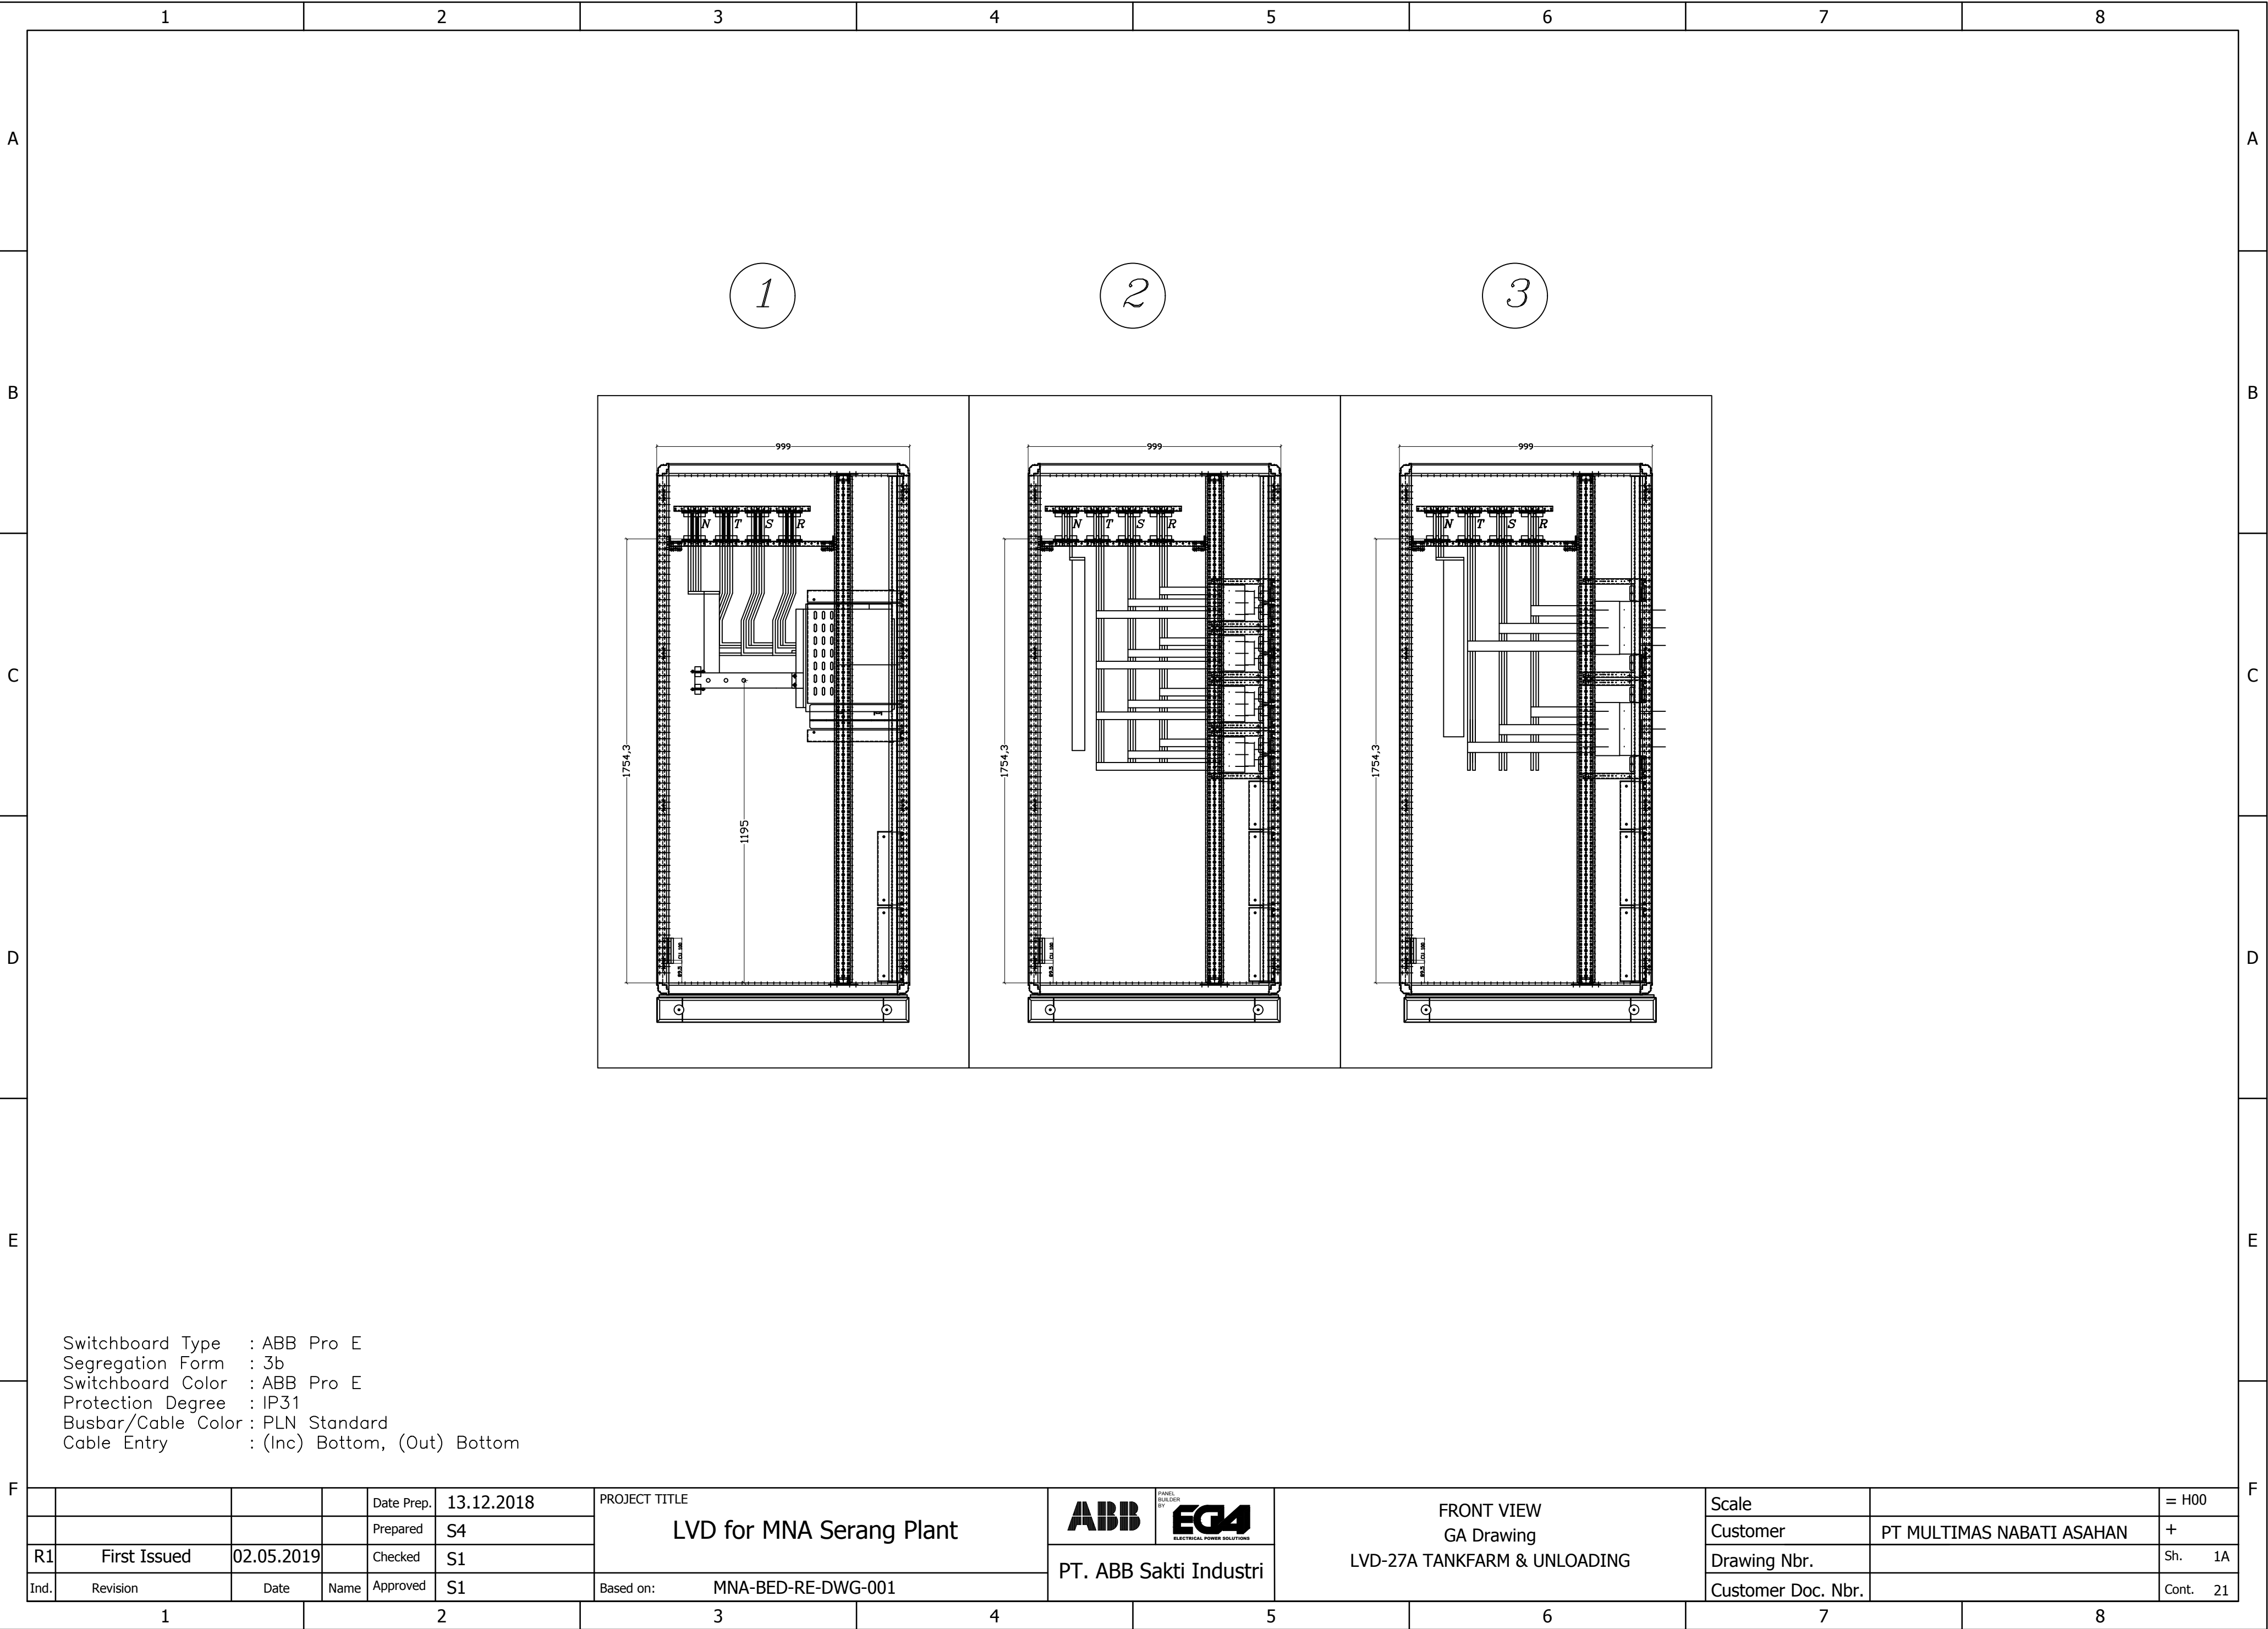

1

2

3

4


5

6


7


8

WE RESERVE ALL RIGHTS IN THIS DOCUMENT AND IN THE INFORMATION CONTAINED THEREIN. REPRODUCTION, USE OR DISCLOSURE TO THIRD PARTIES WITHOUT EXPRESS AUTHORITY IS STRICTLY FORBIDDEN.






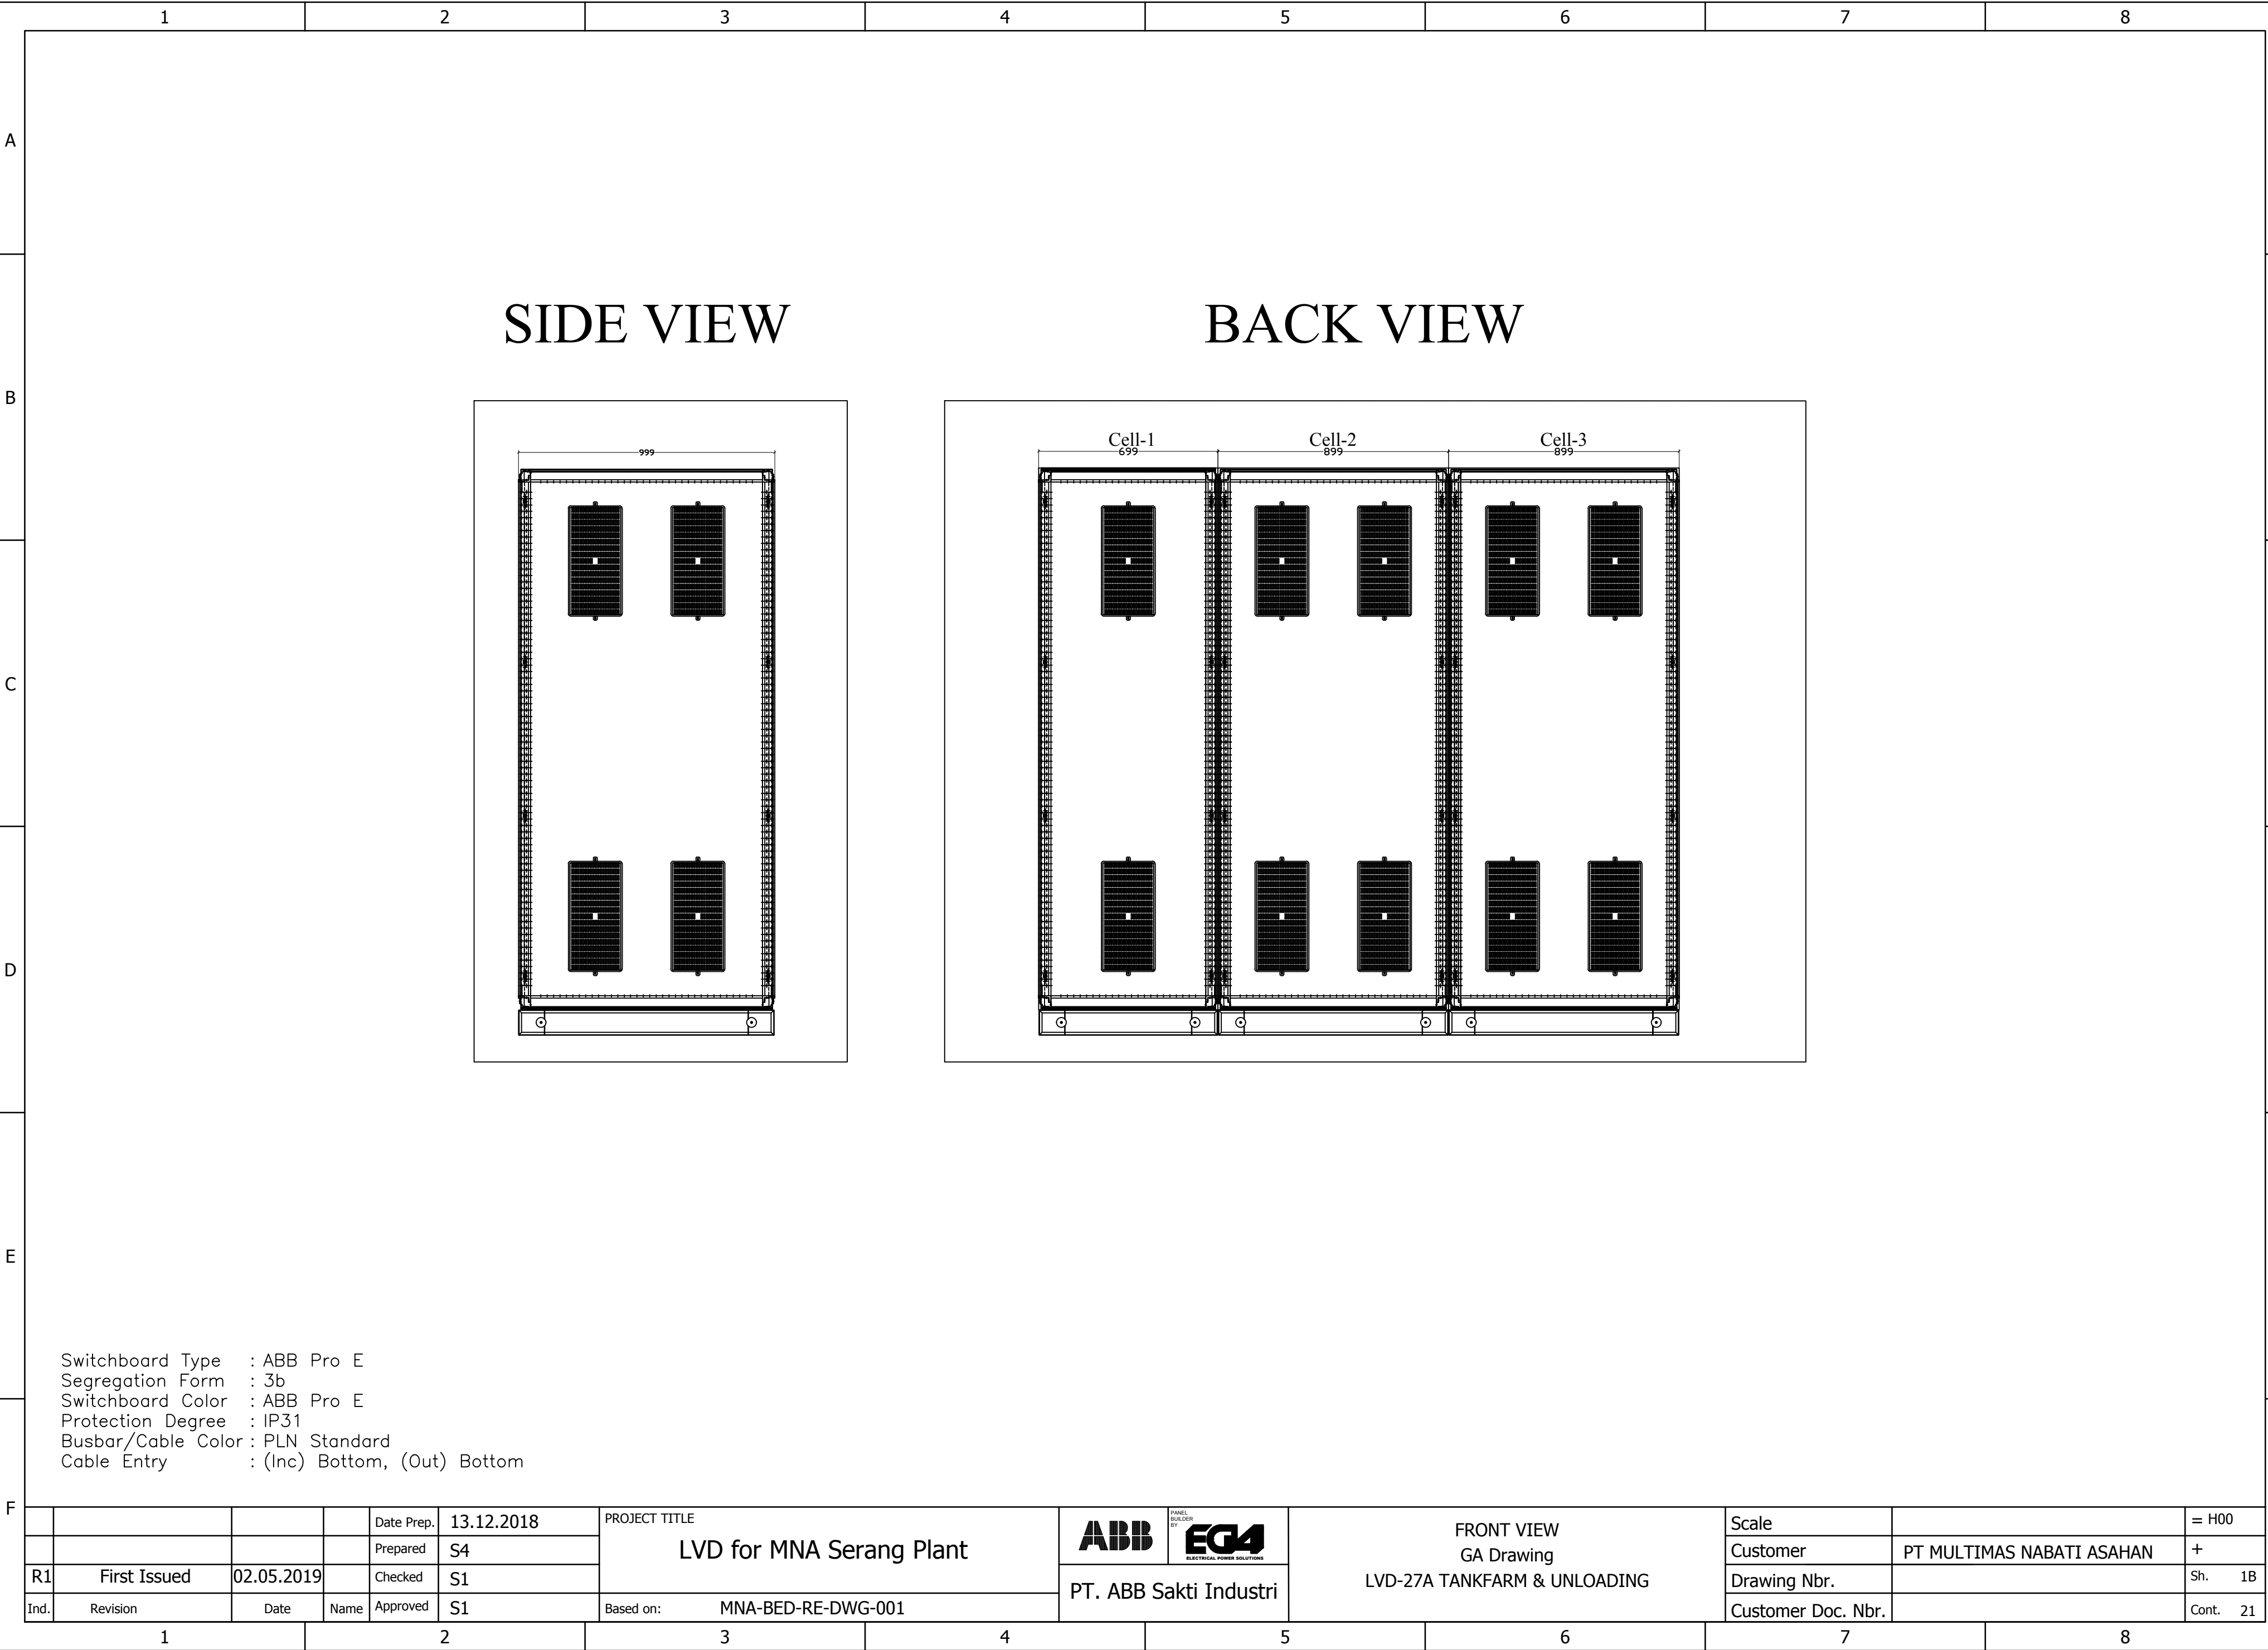


WE RESERVE ALL RIGHTS IN THIS DOCUMENT AND IN THE INFORMATION CONTAINED THEREIN. REPRODUCTION, USE OR DISCLOSURE TO THIRD PARTIES WITHOUT EXPRESS AUTHORITY IS STRICTLY FORBIDDEN.

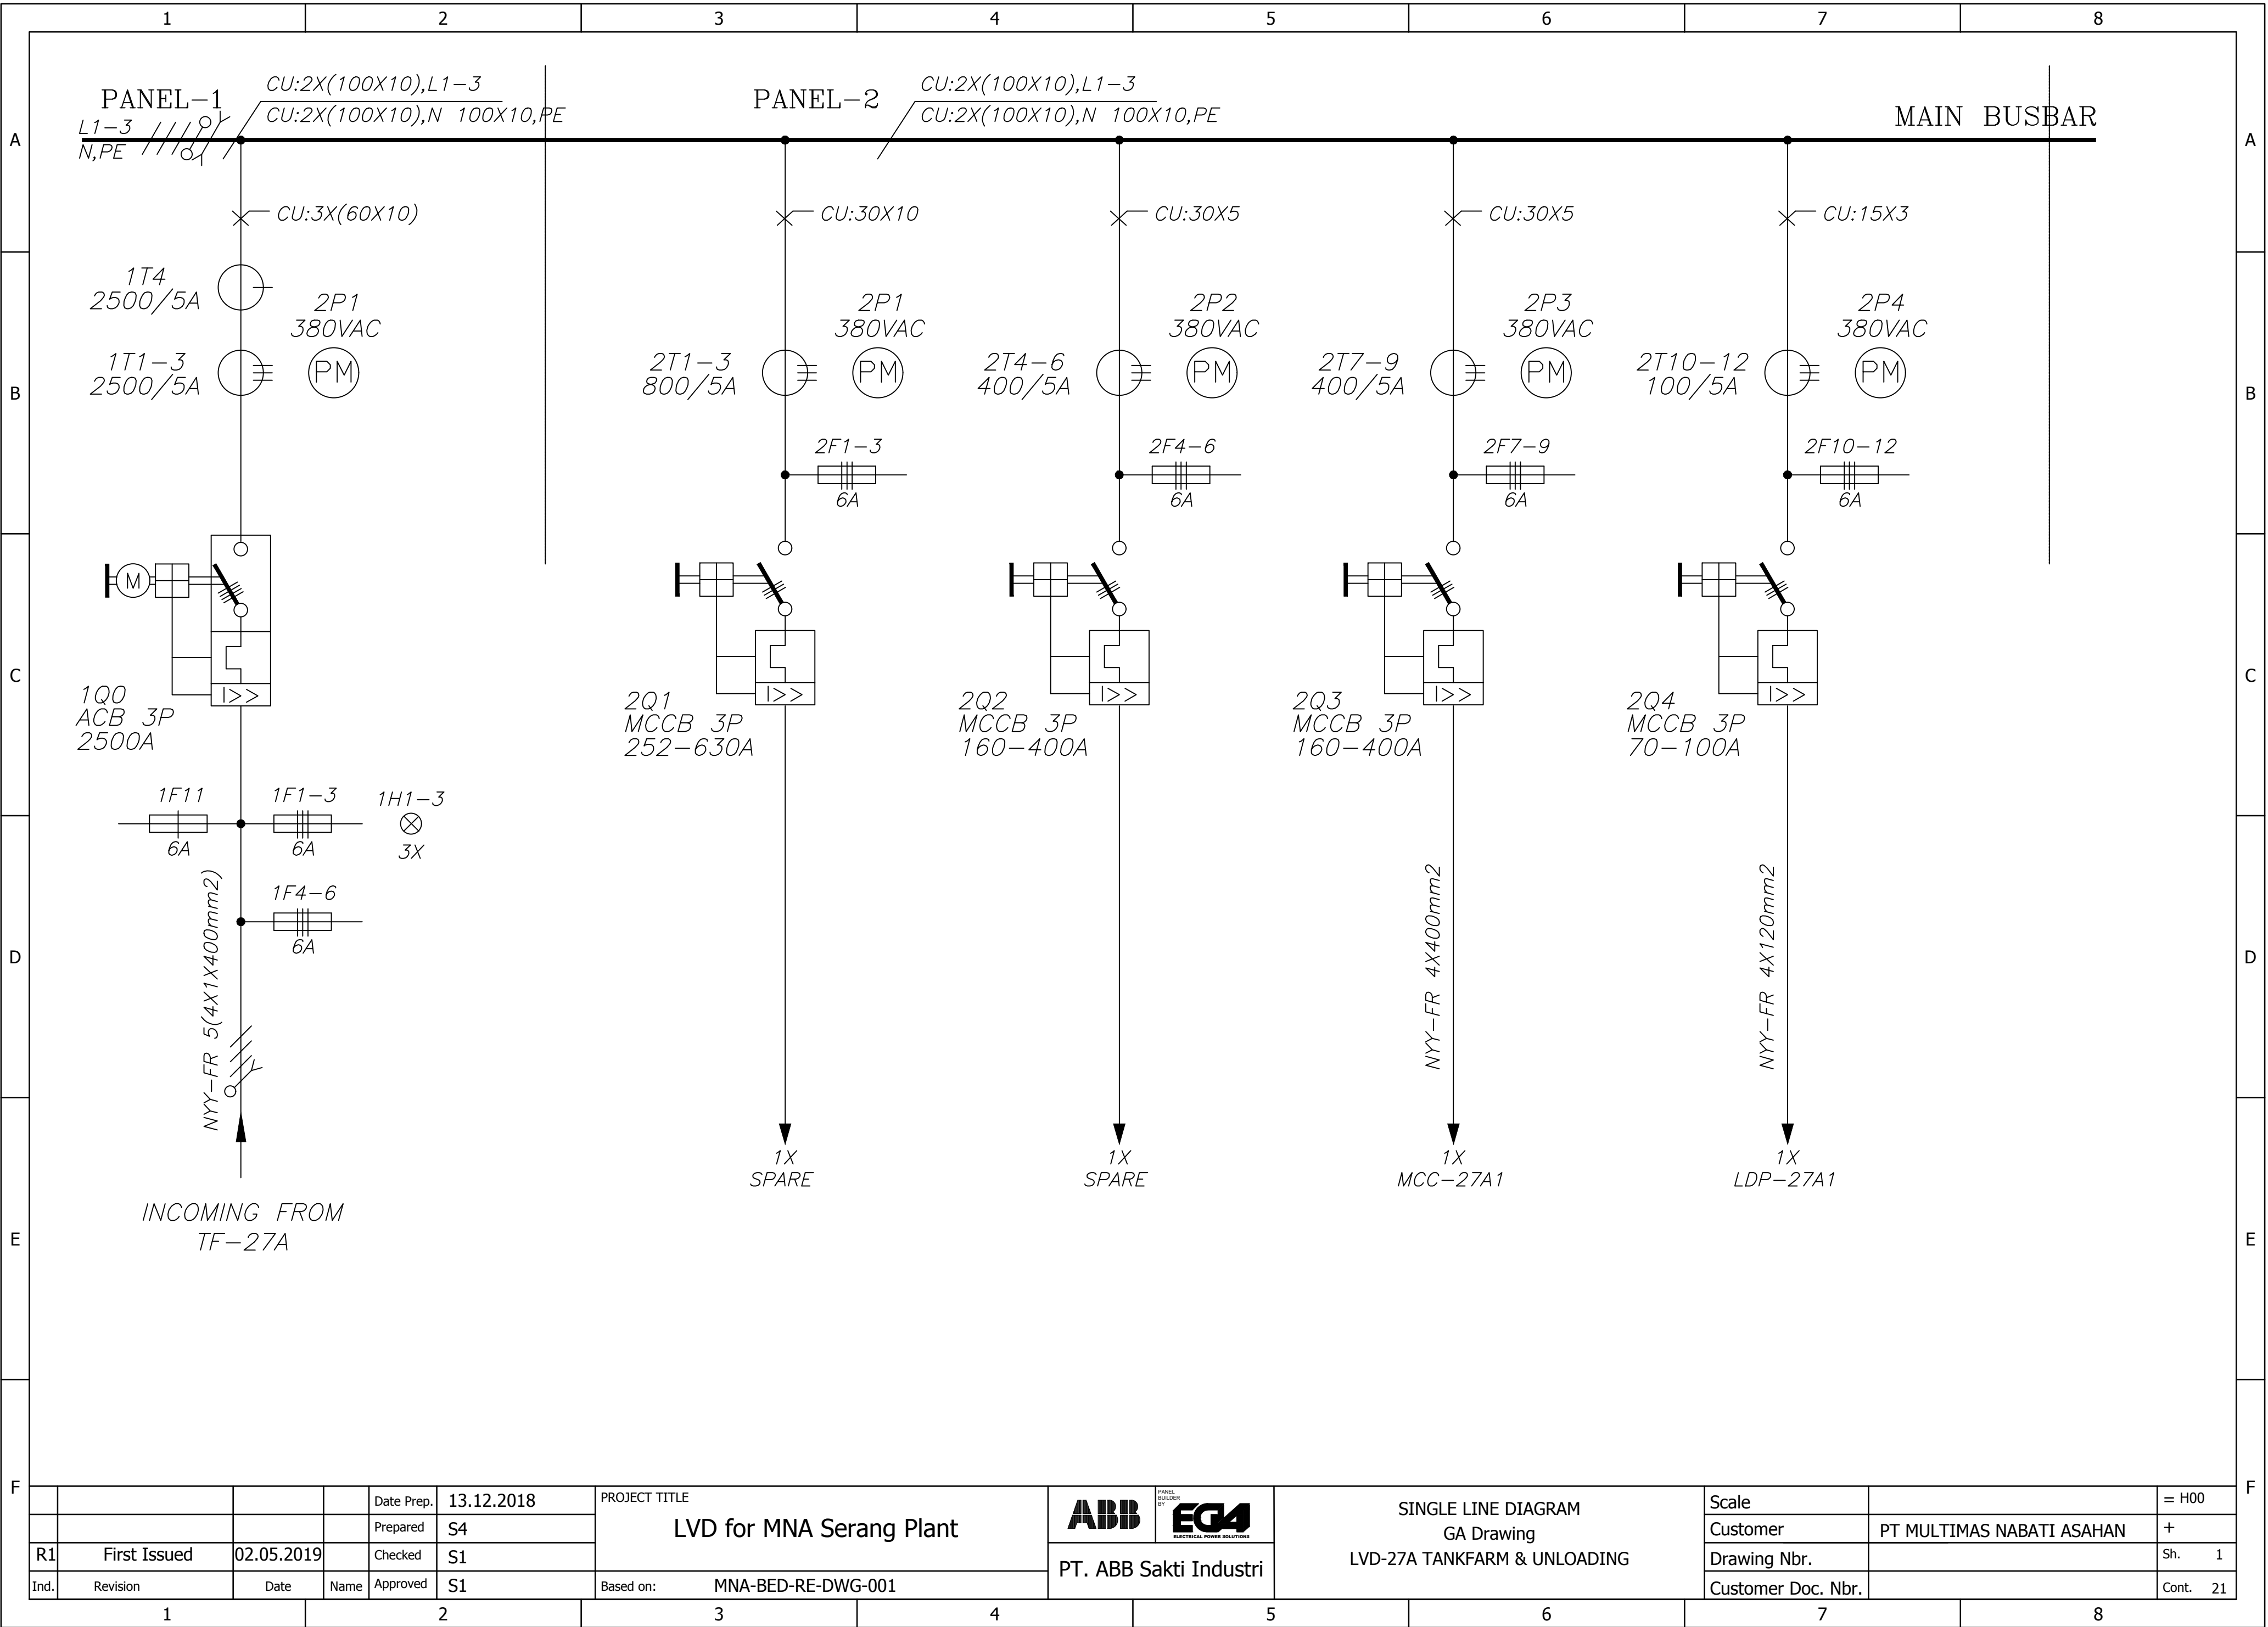


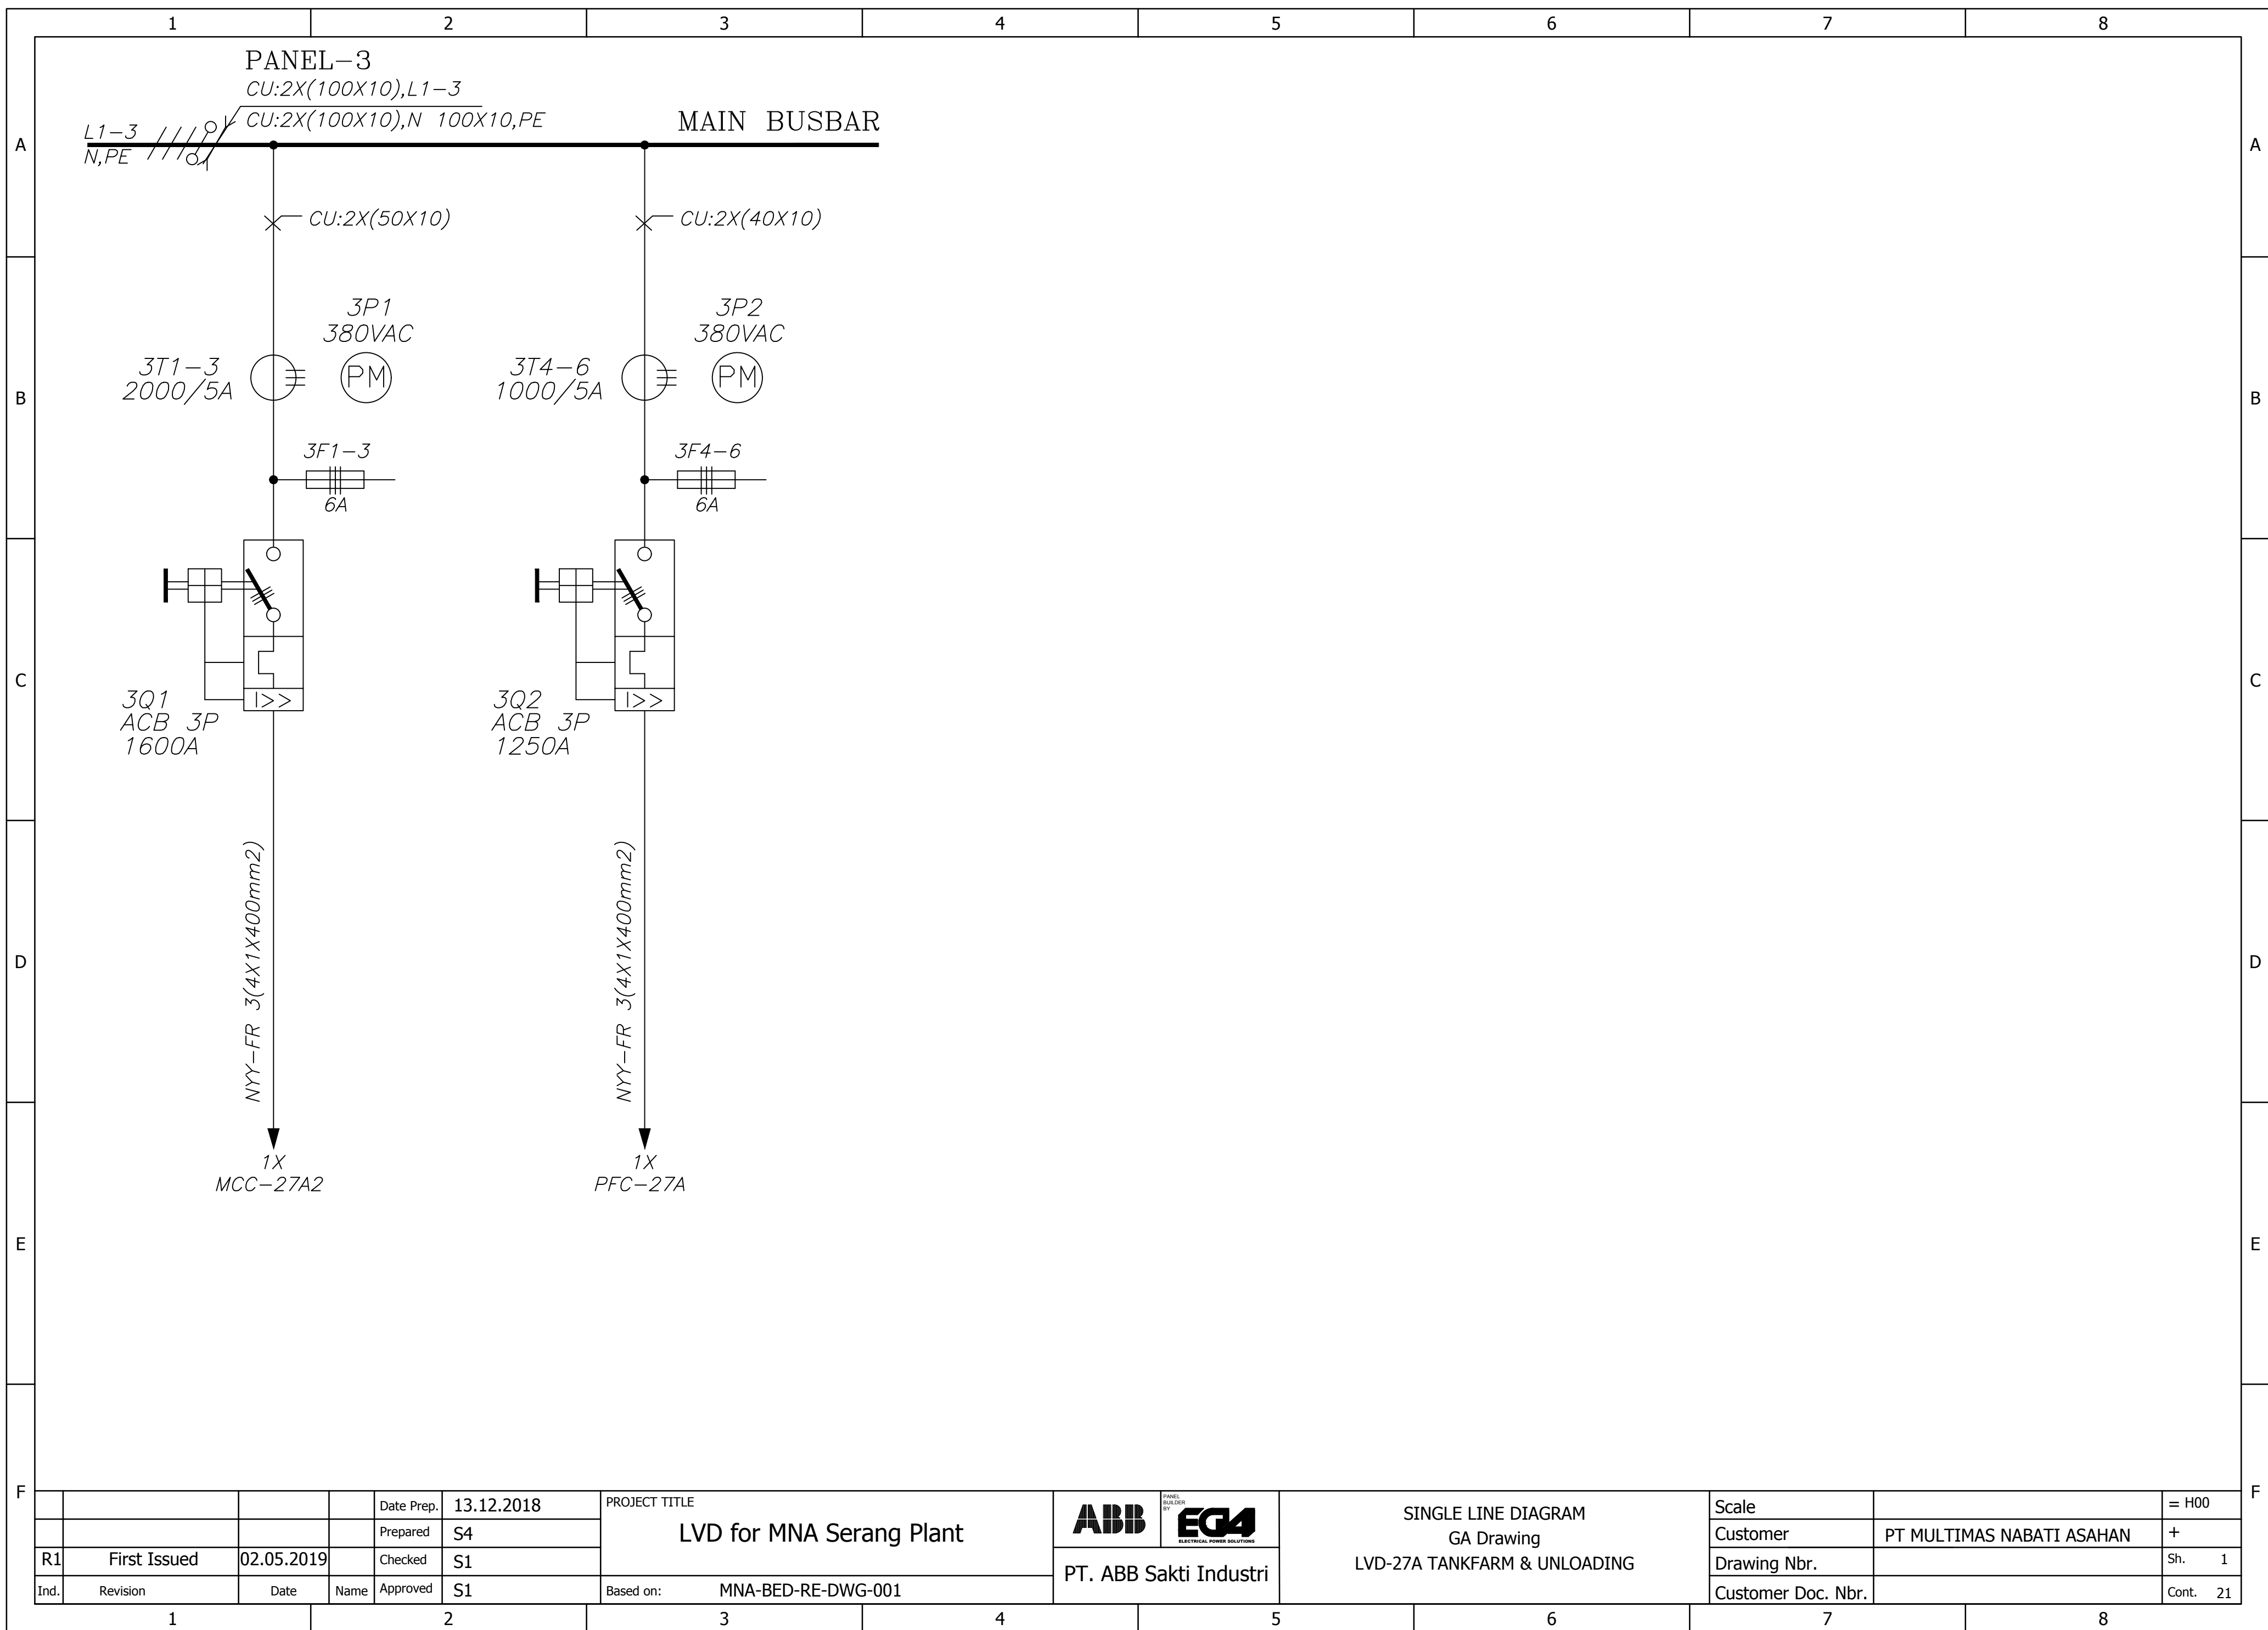


WE RESERVE ALL RIGHTS IN THIS DOCUMENT AND IN THE INFORMATION CONTAINED THEREIN. REPRODUCTION, USE OR DISCLOSURE TO THIRD PARTIES WITHOUT EXPRESS AUTHORITY IS STRICTLY FORBIDDEN.

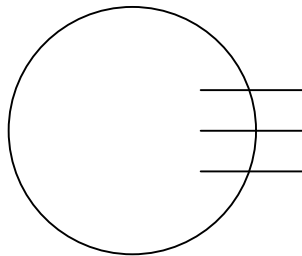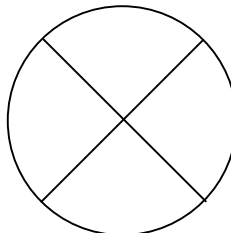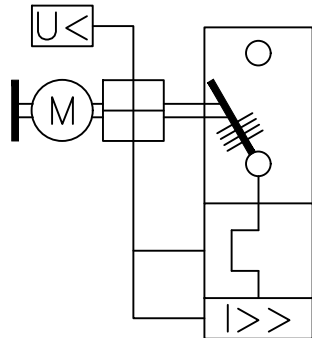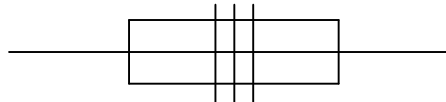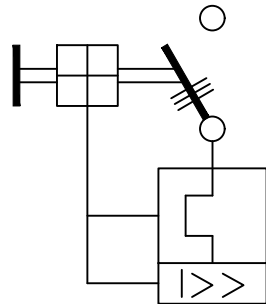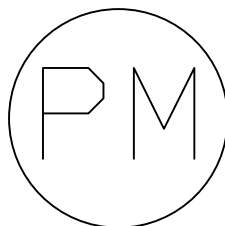1		2		3		4		5		6		7		8																	
A																A															
		 CT  PILOT LAMP  ACB  FUSE  MCCB  DIGITAL POWER METER														B															
B																B															
																C															
C																C															
																D															
D																D															
																E															
E																E															
																F															
F																F															
R1		First Issued		02.05.2019				Checked		S1						Based on:		MNA-BED-RE-DWG-001		PT. ABB Sakti Industri		LEGEND		GA Drawing		LVD-27A TANKFARM & UNLOADING		Scale		= H00	
Ind.		Revision		Date		Name		Approved		S1																Customer		PT MULTIMAS NABATI ASAHAN		+	
																										Drawing Nbr.				Sh. 1	
																										Customer Doc. Nbr.				Cont. 21	
1		2		3		4		5		6		7		8																	

WE RESERVE ALL RIGHTS IN THIS DOCUMENT AND IN THE INFORMATION CONTAINED THEREIN. REPRODUCTION, USE OR DISCLOSURE TO THIRD PARTIES WITHOUT EXPRESS AUTHORITY IS STRICTLY FORBIDDEN.

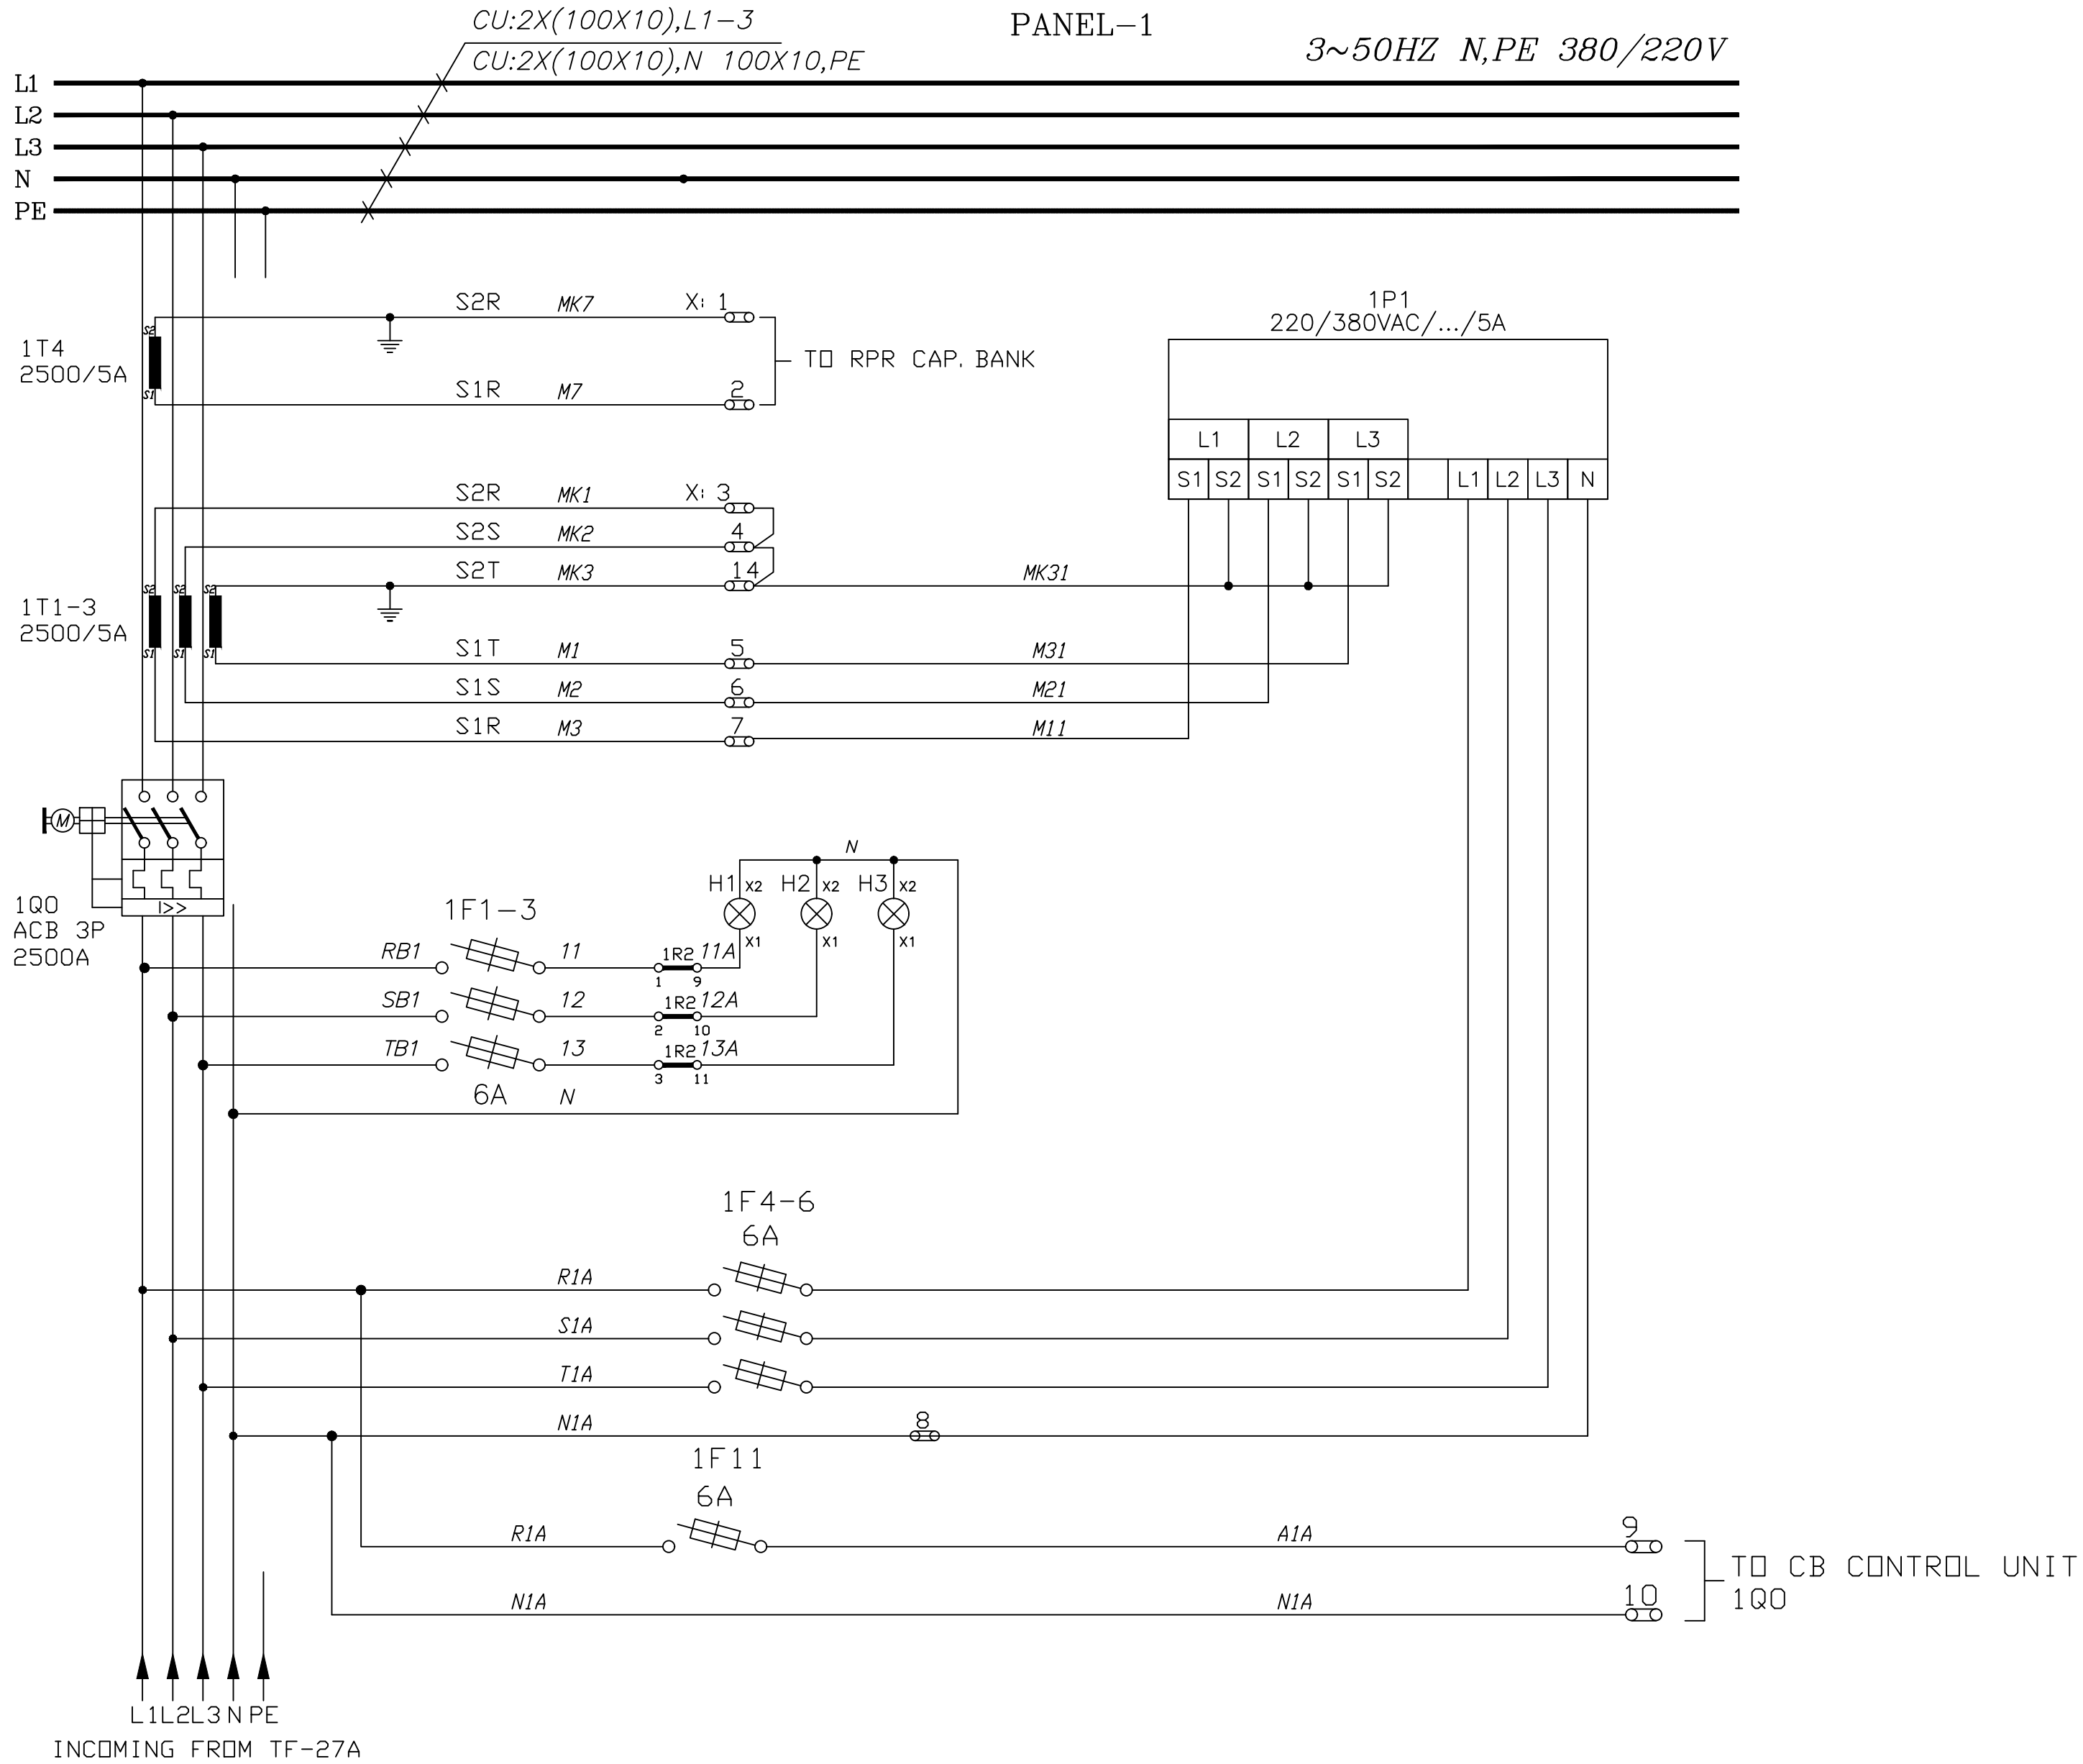

				Date Prep.	13.12.2018	PROJECT TITLE LVD for MNA Serang Plant		 PANEL DRAWN BY  ELECTRICAL POWER SOLUTIONS	WIRING CONTROL DIAGRAM GA Drawing LVD-27A TANKFARM & UNLOADING	Scale		= H00
R1	First Issued	02.05.2019		Prepared	S4					Customer	PT MULTIMAS NABATI ASAHAN	+
Ind.	Revision	Date	Name	Checked	S1					Drawing Nbr.		Sh. 1
			Approved	S1		Based on:	MNA-BED-RE-DWG-001			Customer Doc. Nbr.		Cont. 21

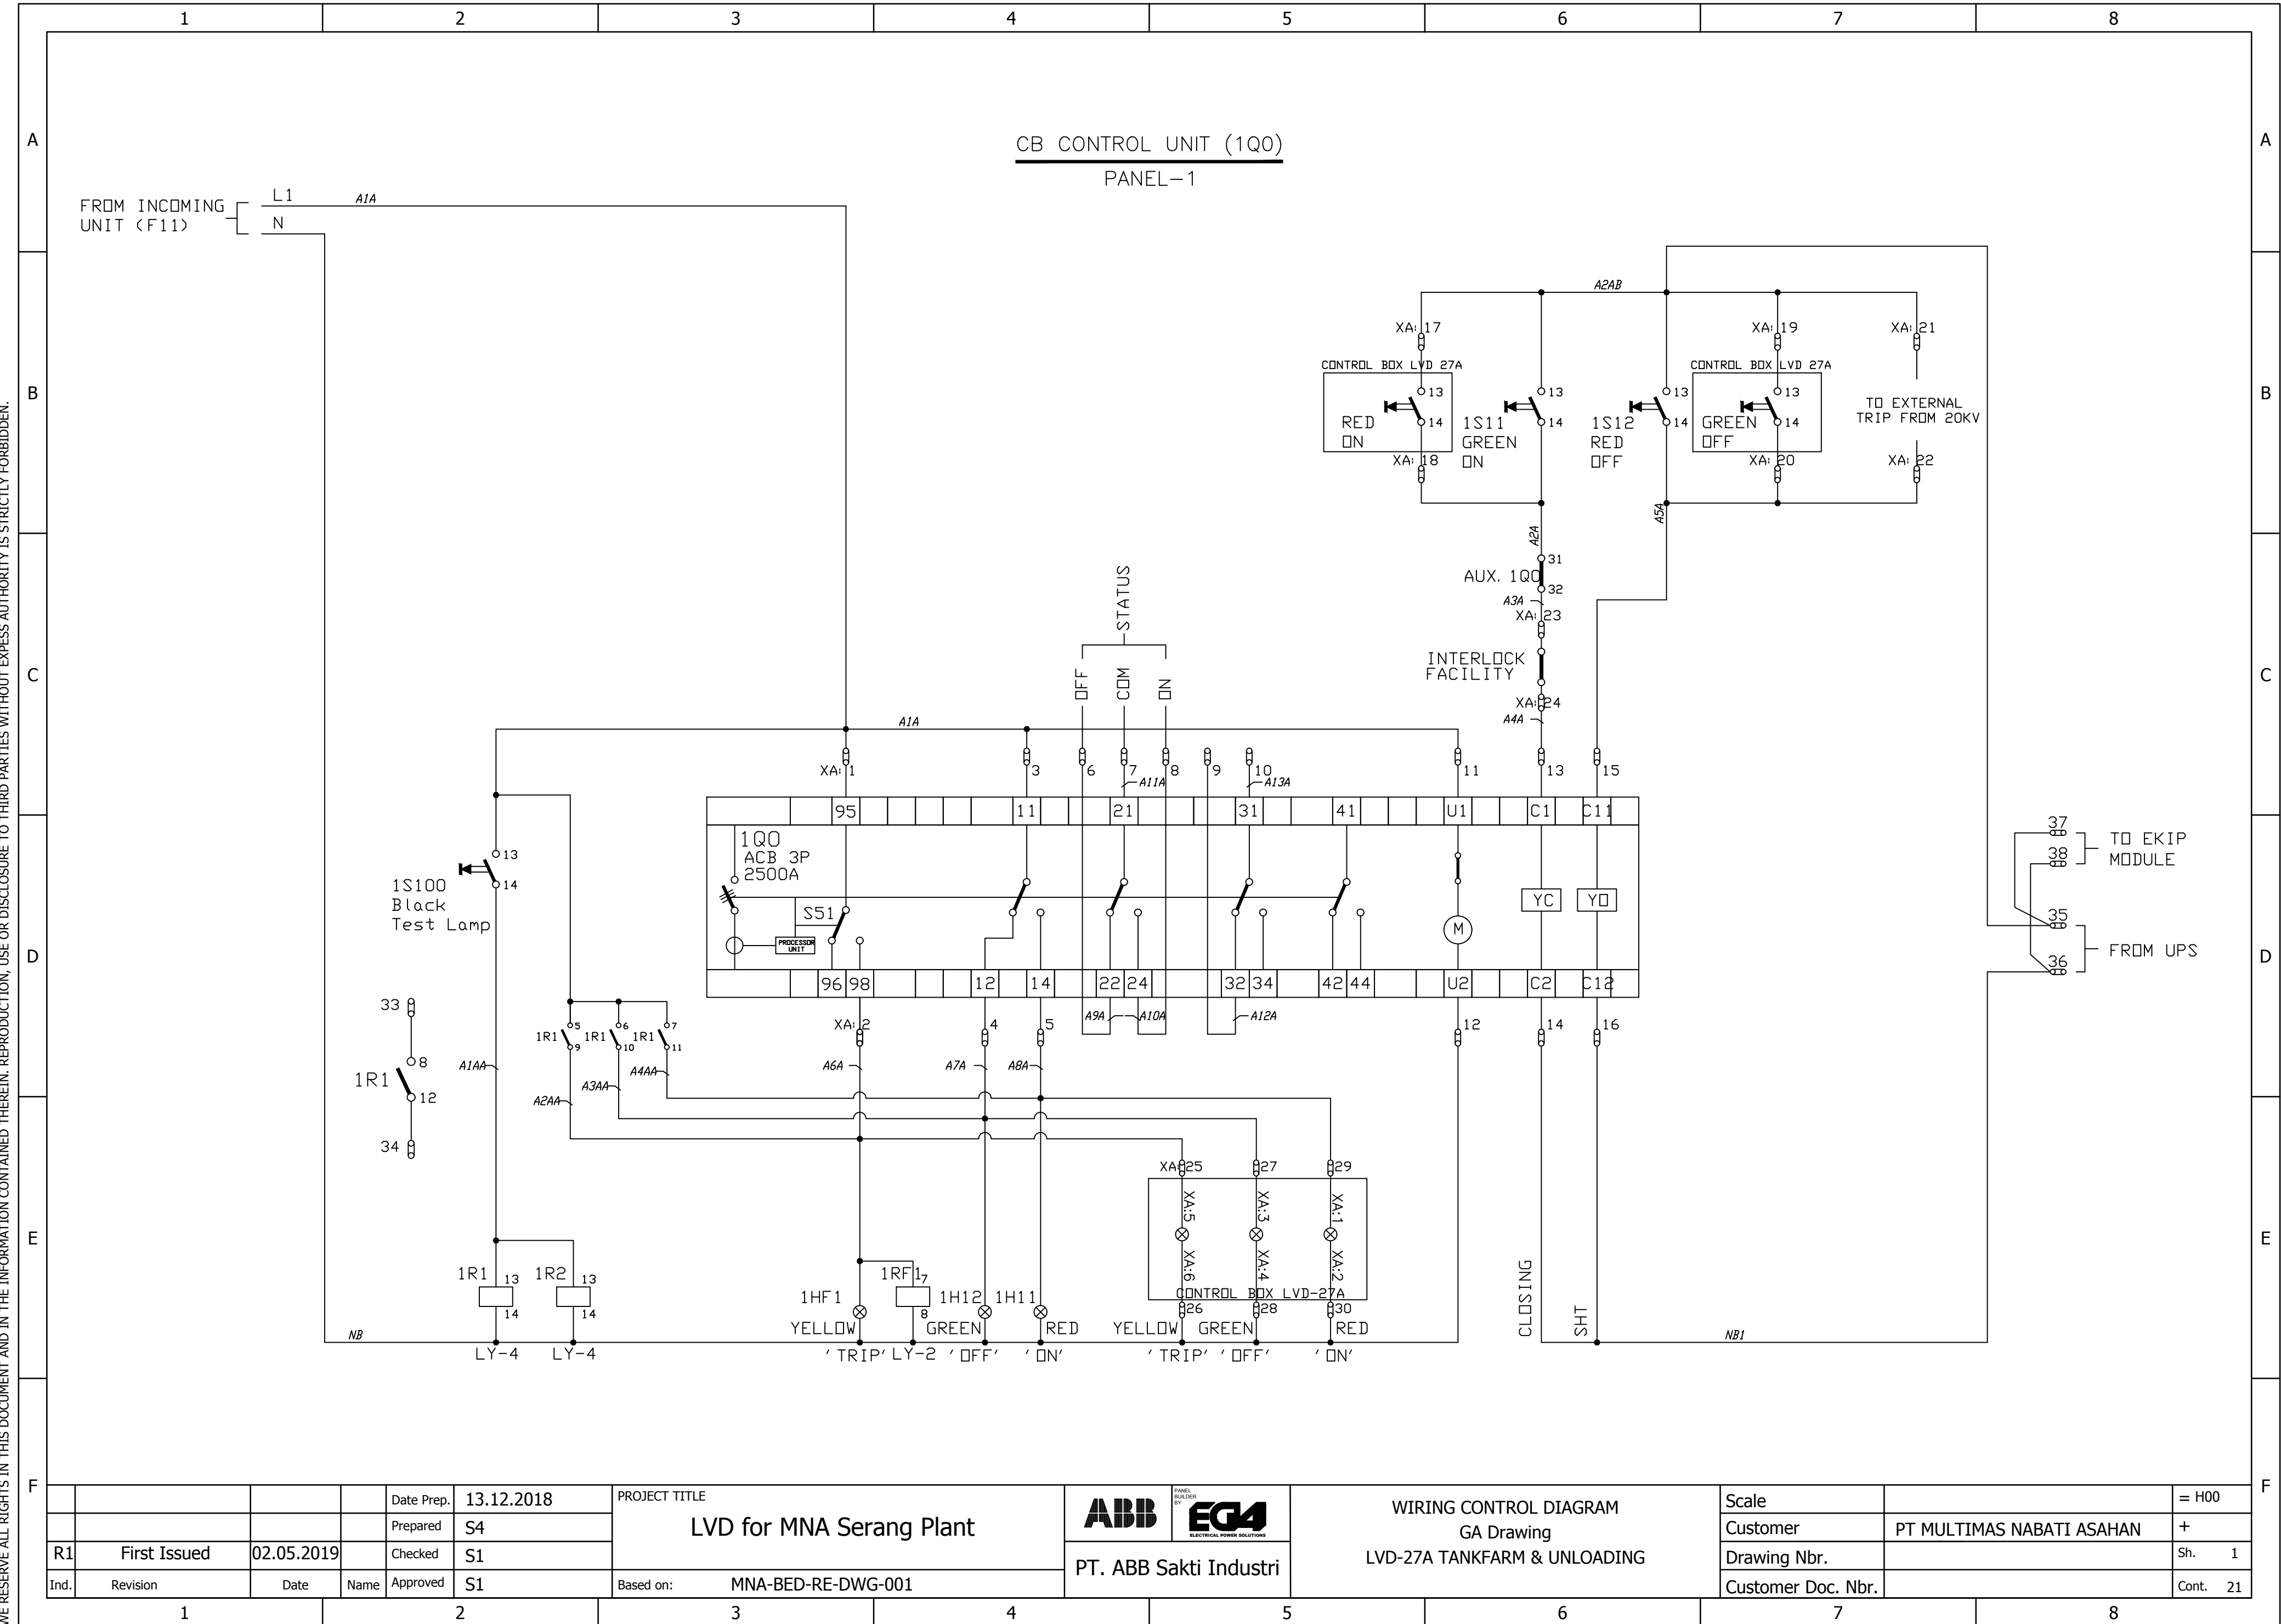

WE RESERVE ALL RIGHTS IN THIS DOCUMENT AND IN THE INFORMATION CONTAINED THEREIN. REPRODUCTION, USE OR DISCLOSURE TO THIRD PARTIES WITHOUT EXPRESS AUTHORITY IS STRICTLY FORBIDDEN.

1 2 3 4 5 6 7 8

A

B

C

D

E

F

FROM INCOMING UNIT (F11)

L1

N

A1A

1S100 Black Test Lamp

1R1

33

8

12

34

1R1

13

14

1R2

13

14

LY-4

LY-4

NB

1S111 GREEN ON

1S12 RED OFF

1S122 GREEN OFF

CONTROL BOX LVD 27A

XA: 17

13

14

XA: 18

XA: 19

13

14

XA: 20

XA: 21

TO EXTERNAL TRIP FROM 20KV

XA: 22

A2AB

A5A

AUX. 1QO

31

32

A3A

XA: 23

INTERLOCK FACILITY

XA: 24

A4A

11

13

15

1QO ACB 3P 2500A

S51

PROCESSOR UNIT

95

11

21

31

41

U1

C1

C11

96

98

12

14

22

24

32

34

42

44

U2

C2

C12

XA: 1

3

6

7

8

9

10

11A

A1A

A13A

A6A

A7A

A8A

A9A

A10A

A12A

1H11

1H12

1

WE RESERVE ALL RIGHTS IN THIS DOCUMENT AND IN THE INFORMATION CONTAINED THEREIN. REPRODUCTION, USE OR DISCLOSURE TO THIRD PARTIES WITHOUT EXPRESS AUTHORITY IS STRICTLY FORBIDDEN.

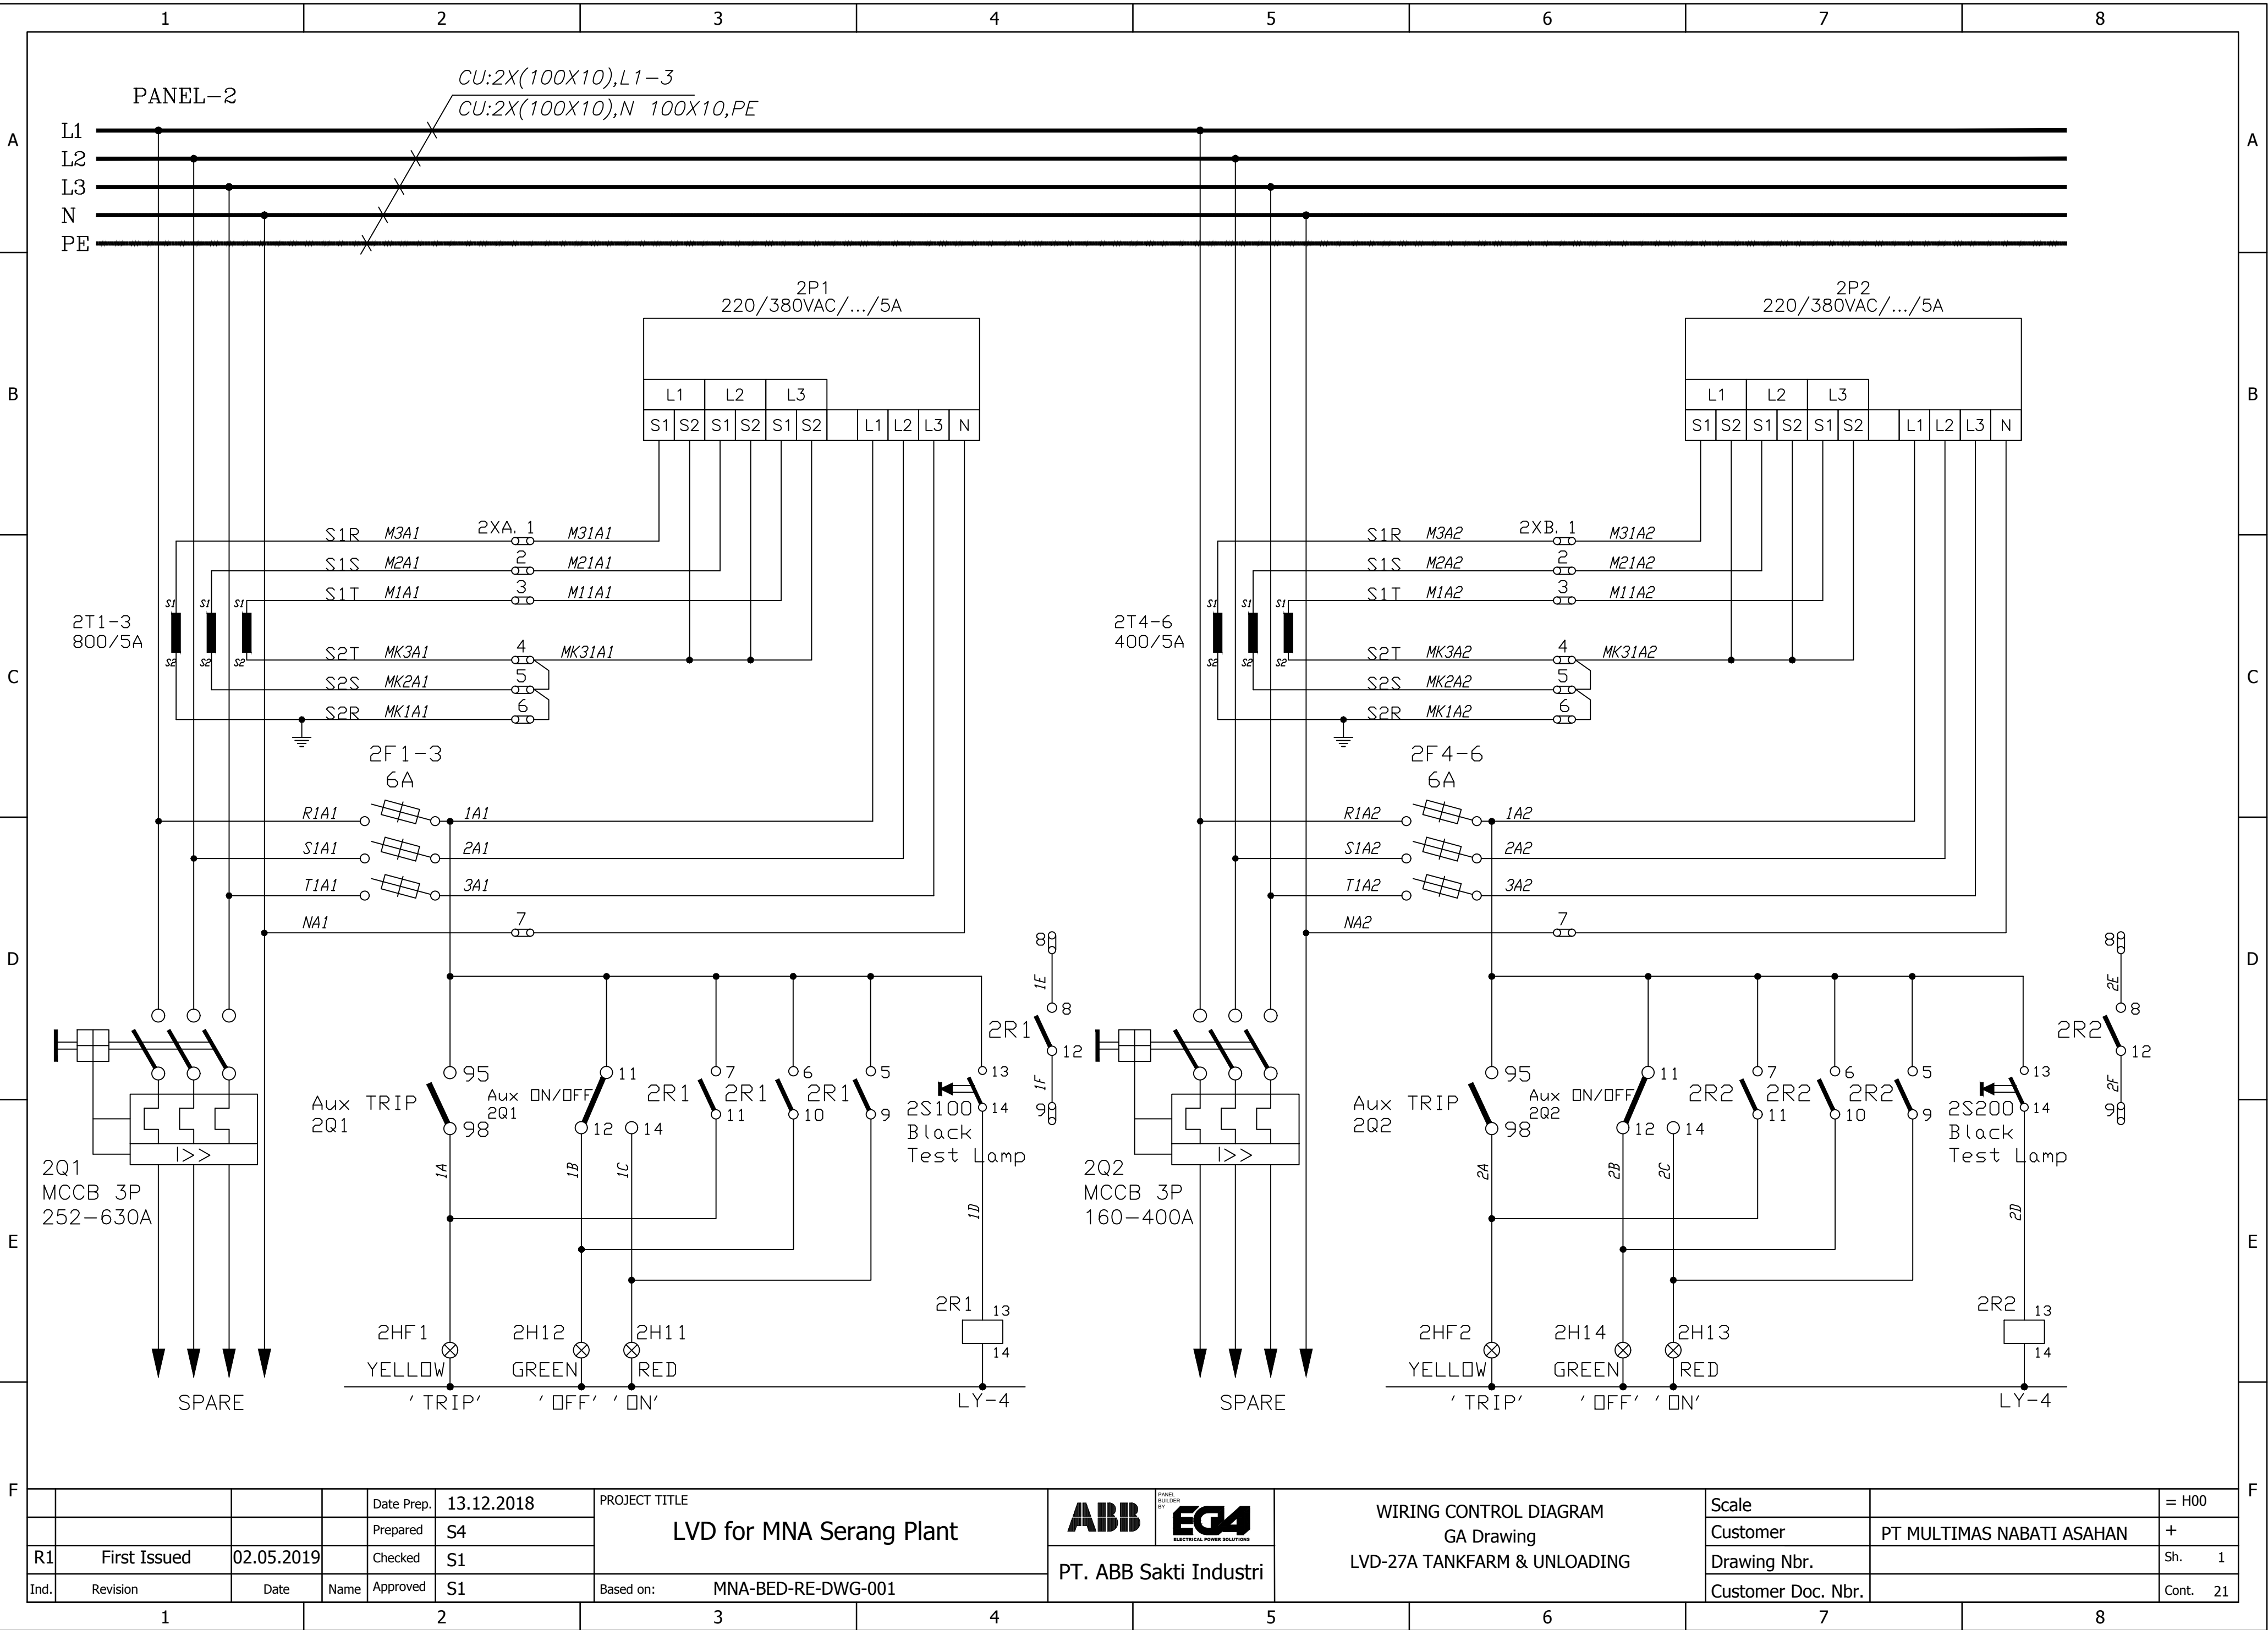

WE RESERVE ALL RIGHTS IN THIS DOCUMENT AND IN THE INFORMATION CONTAINED THEREIN. REPRODUCTION, USE OR DISCLOSURE TO THIRD PARTIES WITHOUT EXPRESS AUTHORITY IS STRICTLY FORBIDDEN.

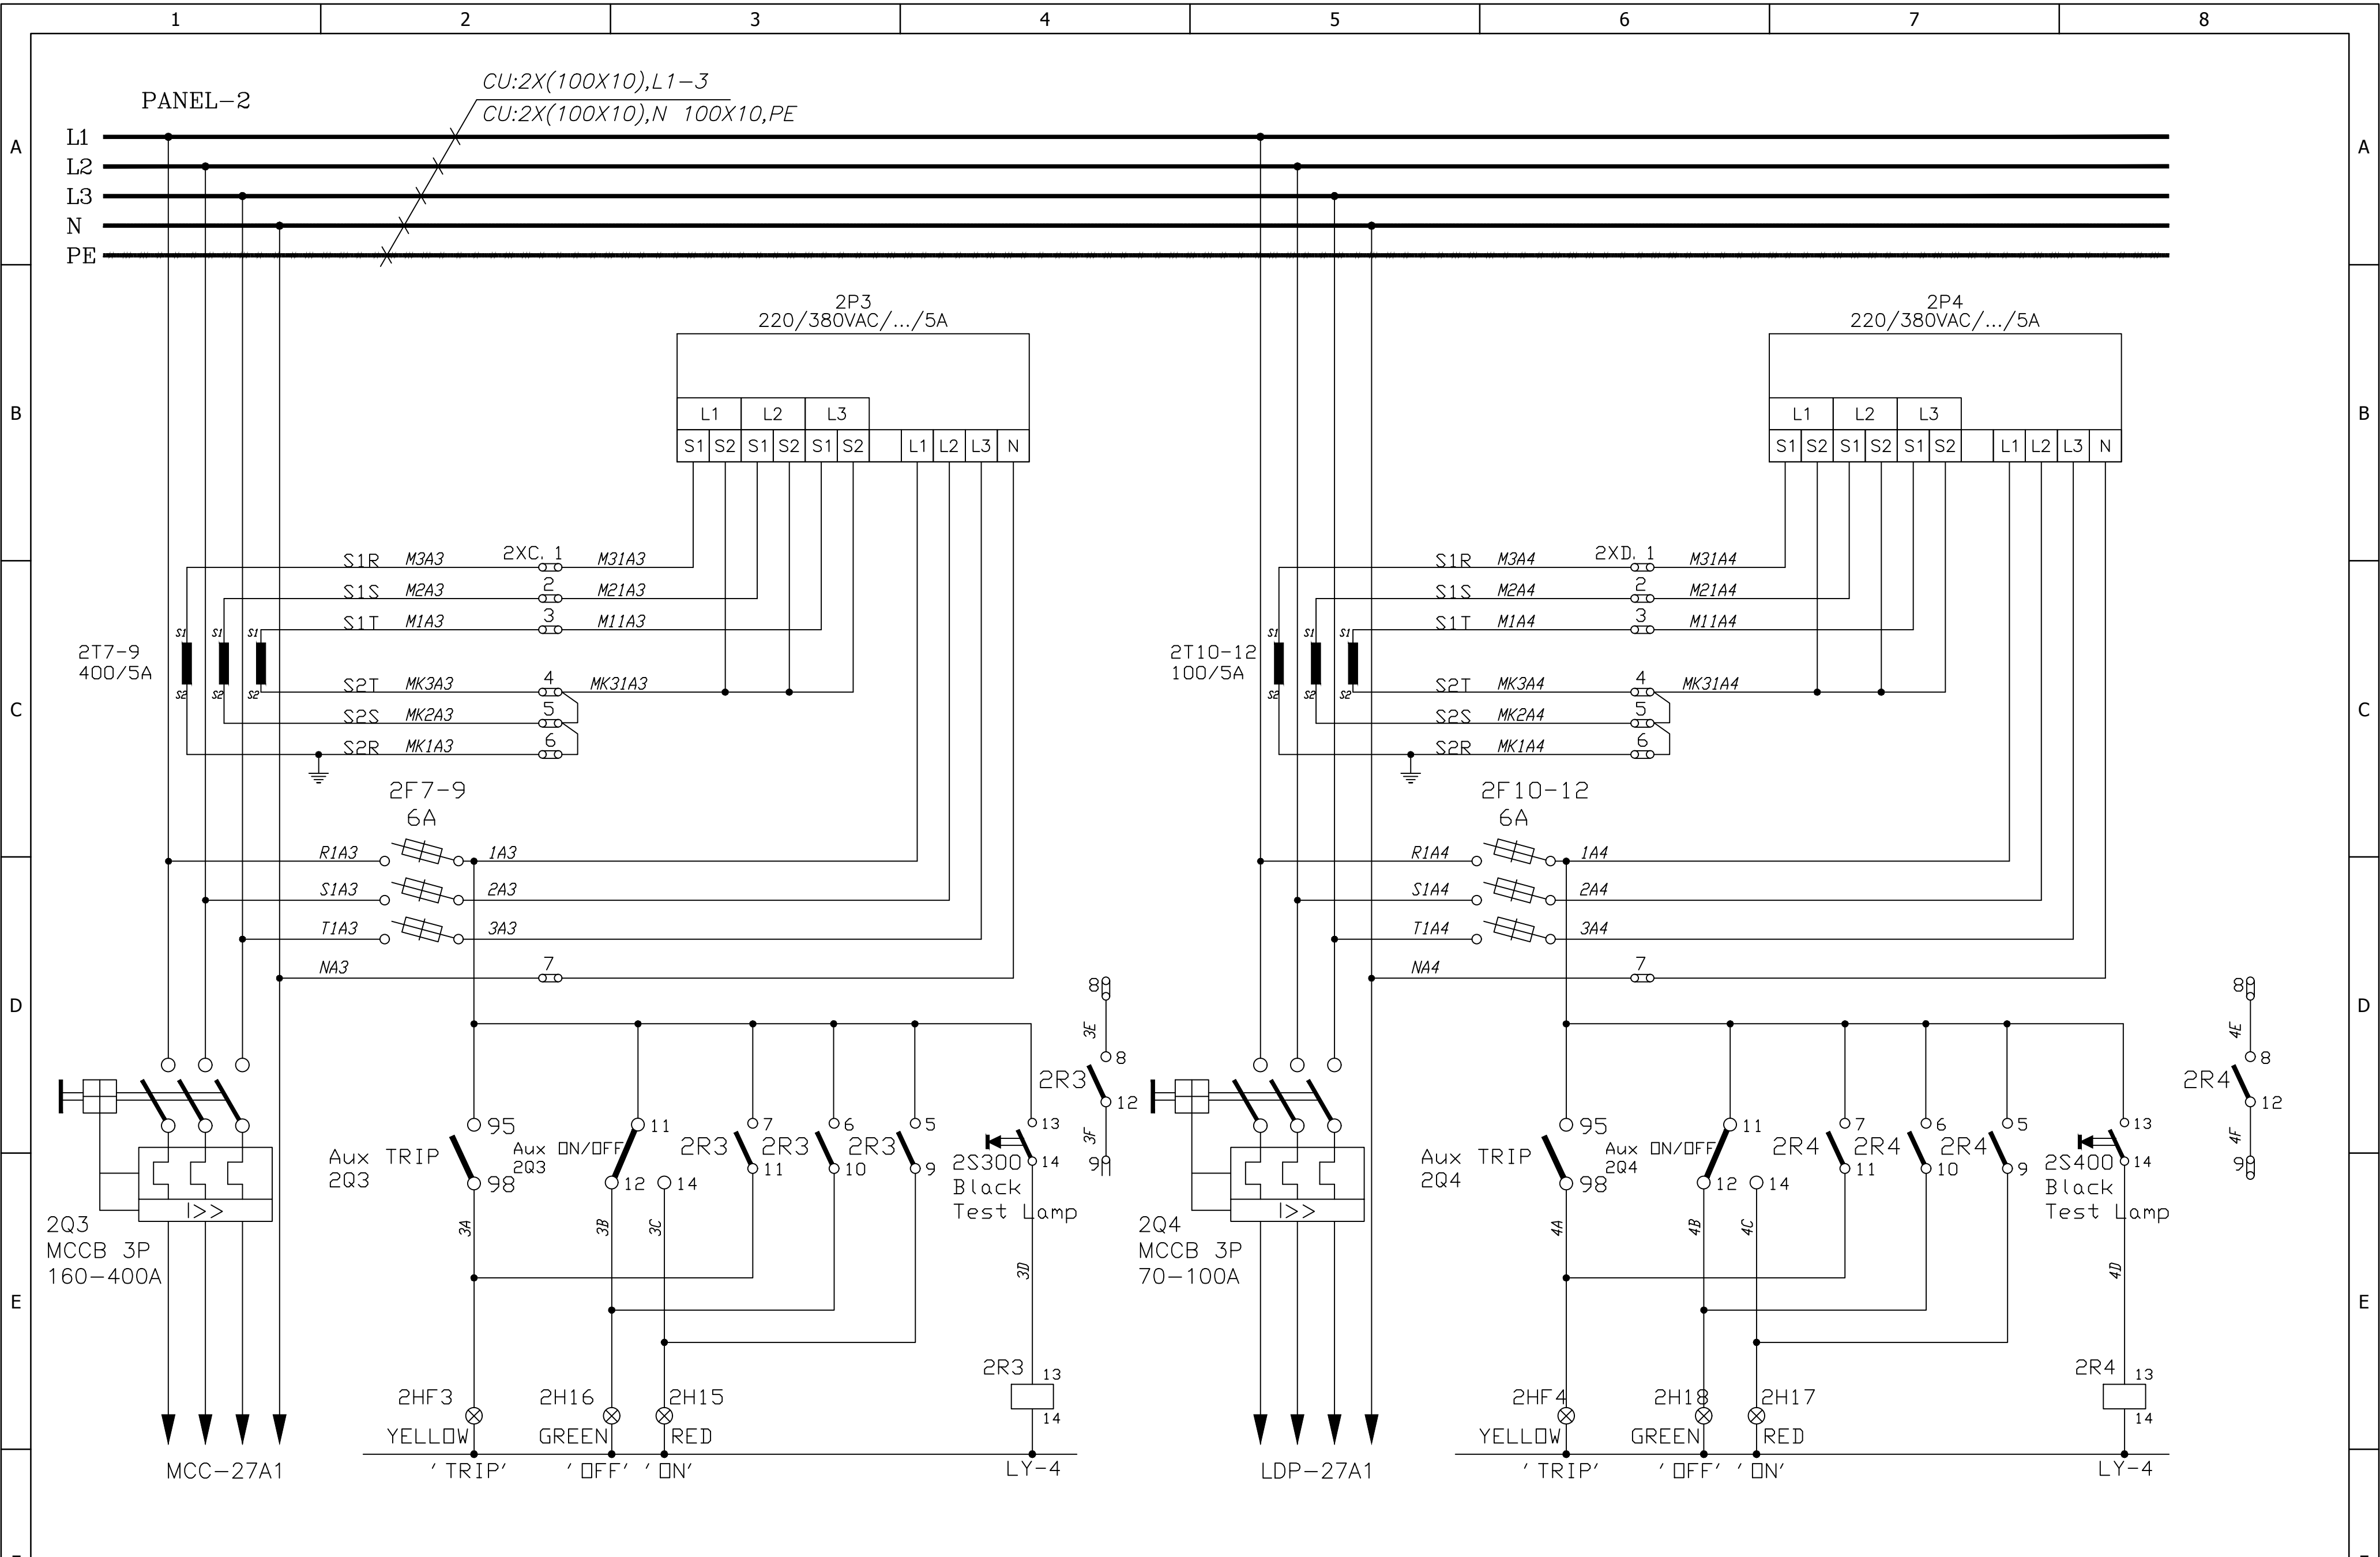

				Date Prep.	13.12.2018	PROJECT TITLE		  PANEL BUILDER BY	WIRING CONTROL DIAGRAM GA Drawing LVD-27A TANKFARM & UNLOADING	Scale		= H00
R1	First Issued	02.05.2019		Prepared	S4					Customer	PT MULTIMAS NABATI ASAHAN	+
Ind.	Revision	Date	Name	Checked	S1					Drawing Nbr.		Sh. 1
				Approved	S1	Based on:		PT. ABB Sakti Industri		Customer Doc. Nbr.		Cont. 21

1

2

3

4


5

6


7

8

WE RESERVE ALL RIGHTS IN THIS DOCUMENT AND IN THE INFORMATION CONTAINED THEREIN. REPRODUCTION, USE OR DISCLOSURE TO THIRD PARTIES WITHOUT EXPRESS AUTHORITY IS STRICTLY FORBIDDEN.

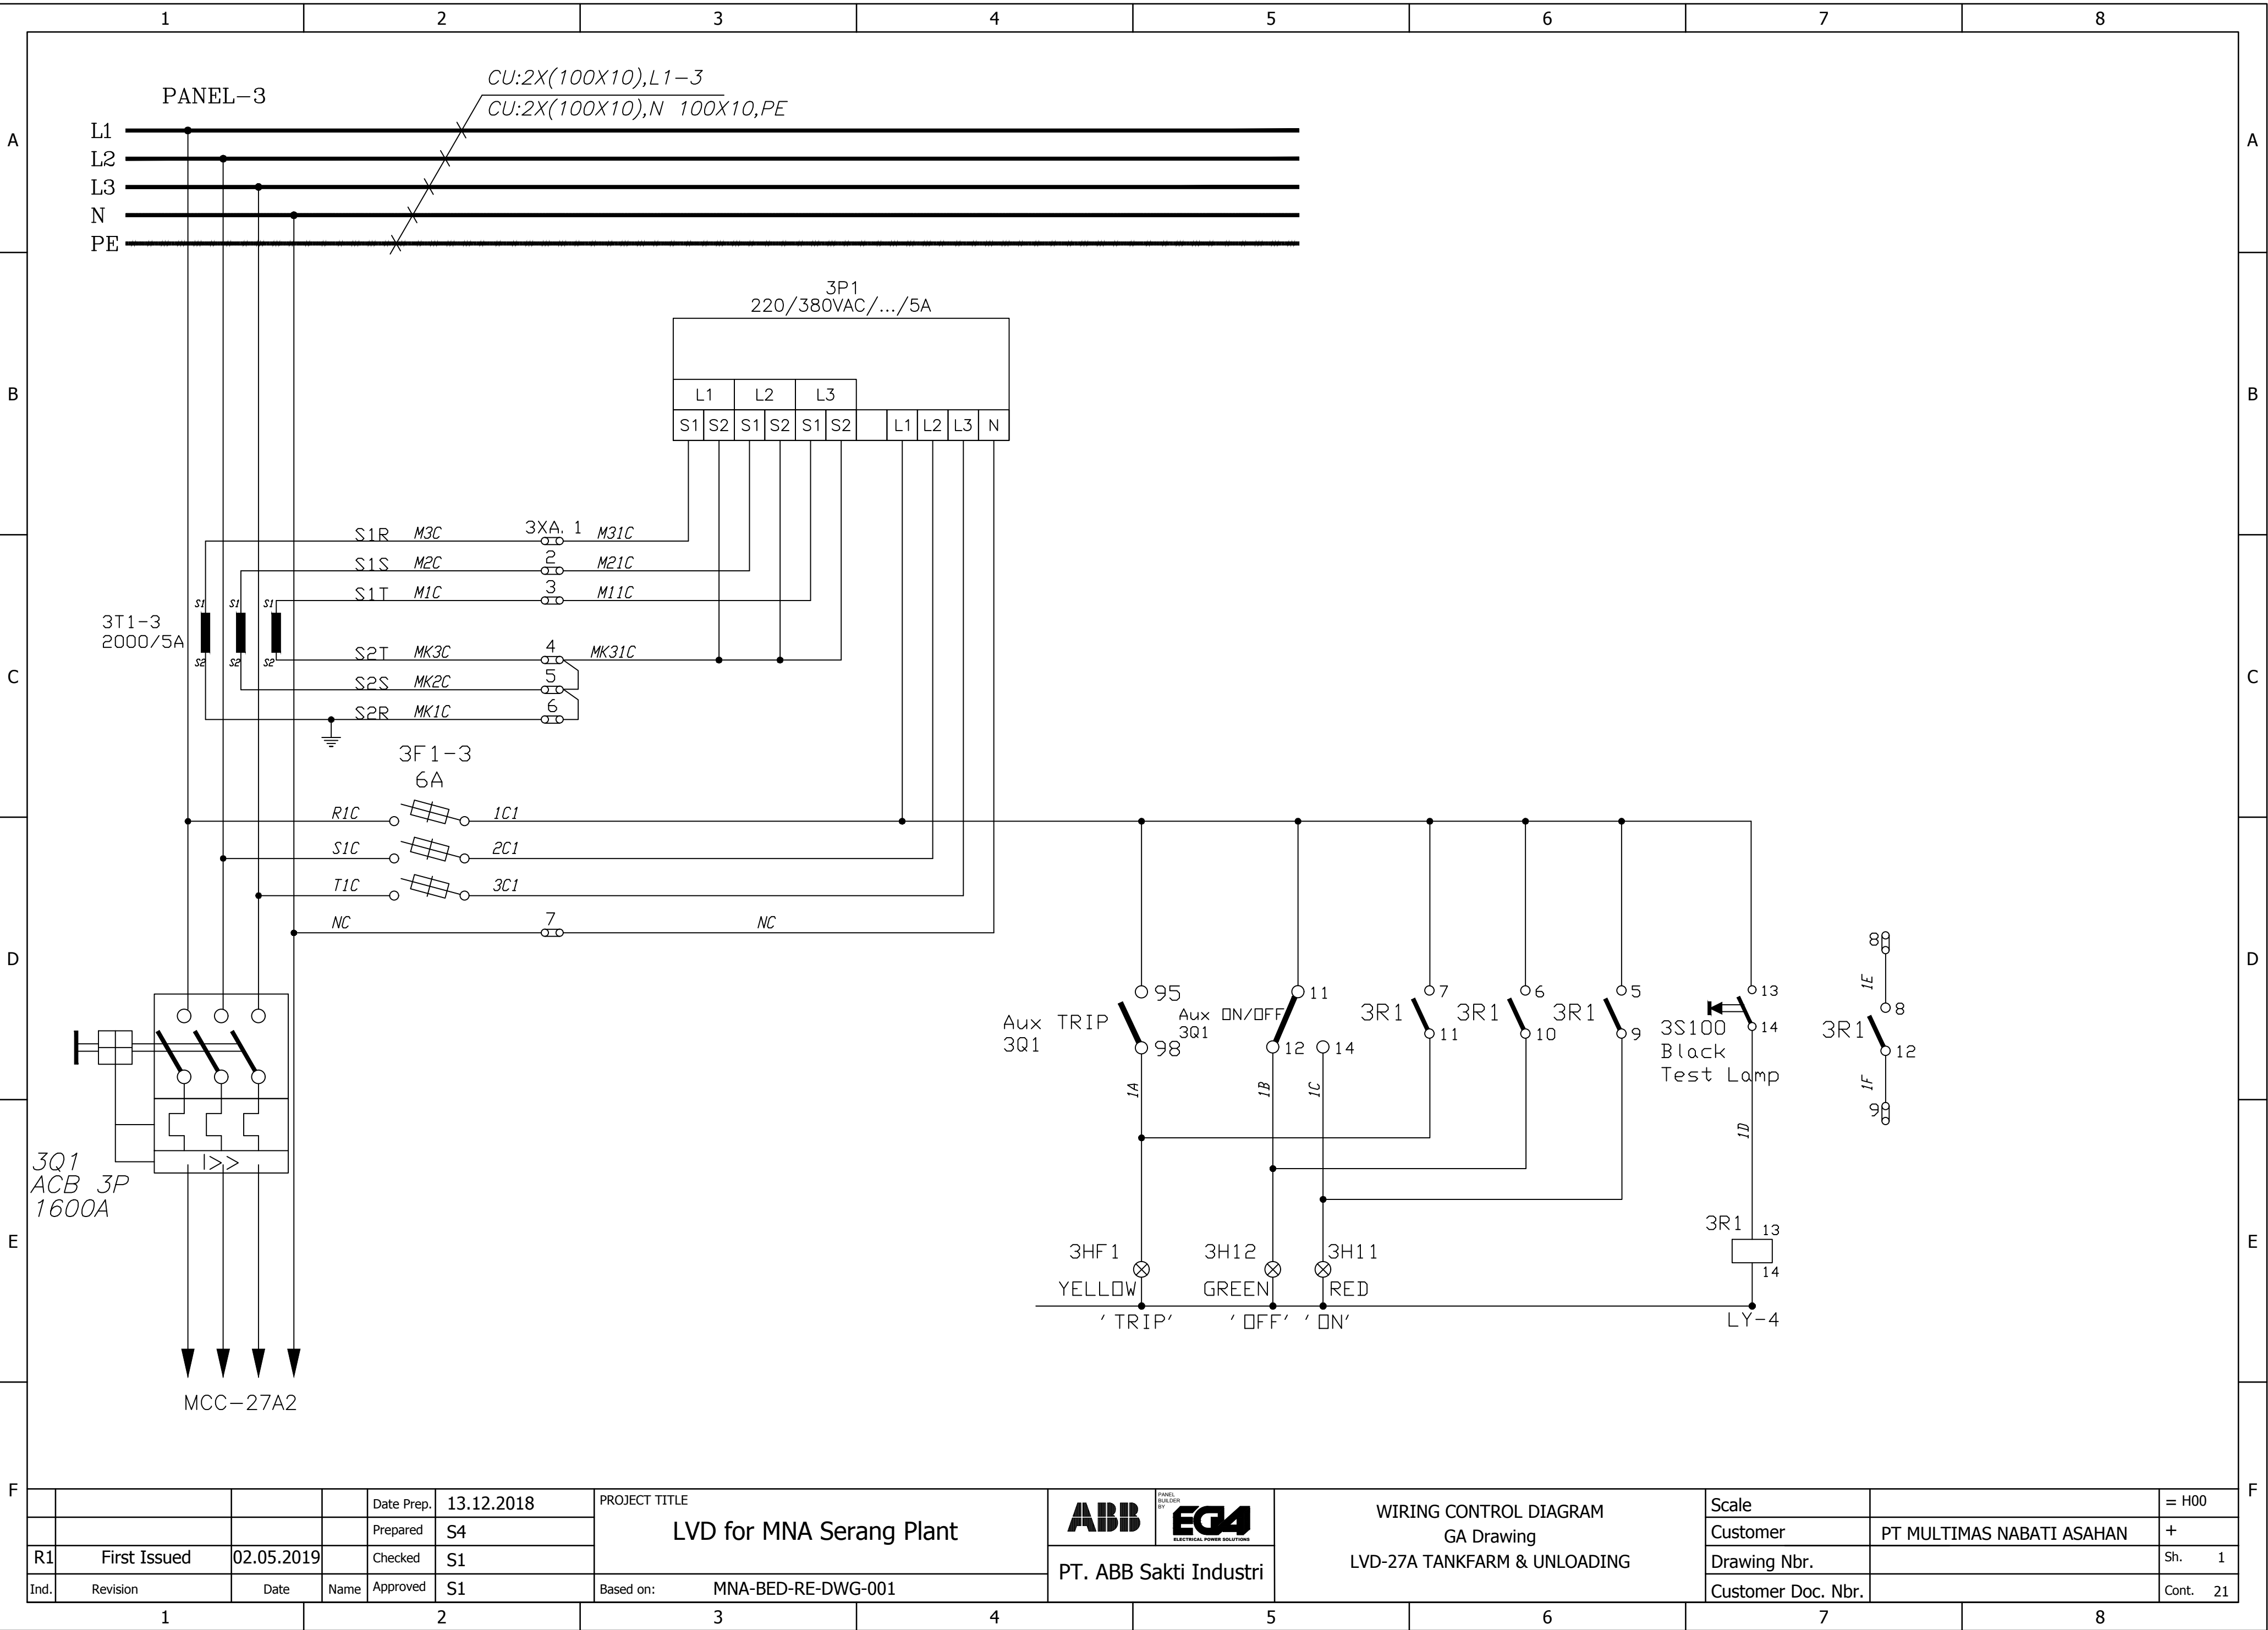

WE RESERVE ALL RIGHTS IN THIS DOCUMENT AND IN THE INFORMATION CONTAINED THEREIN. REPRODUCTION, USE OR DISCLOSURE TO THIRD PARTIES WITHOUT EXPRESS AUTHORITY IS STRICTLY FORBIDDEN.

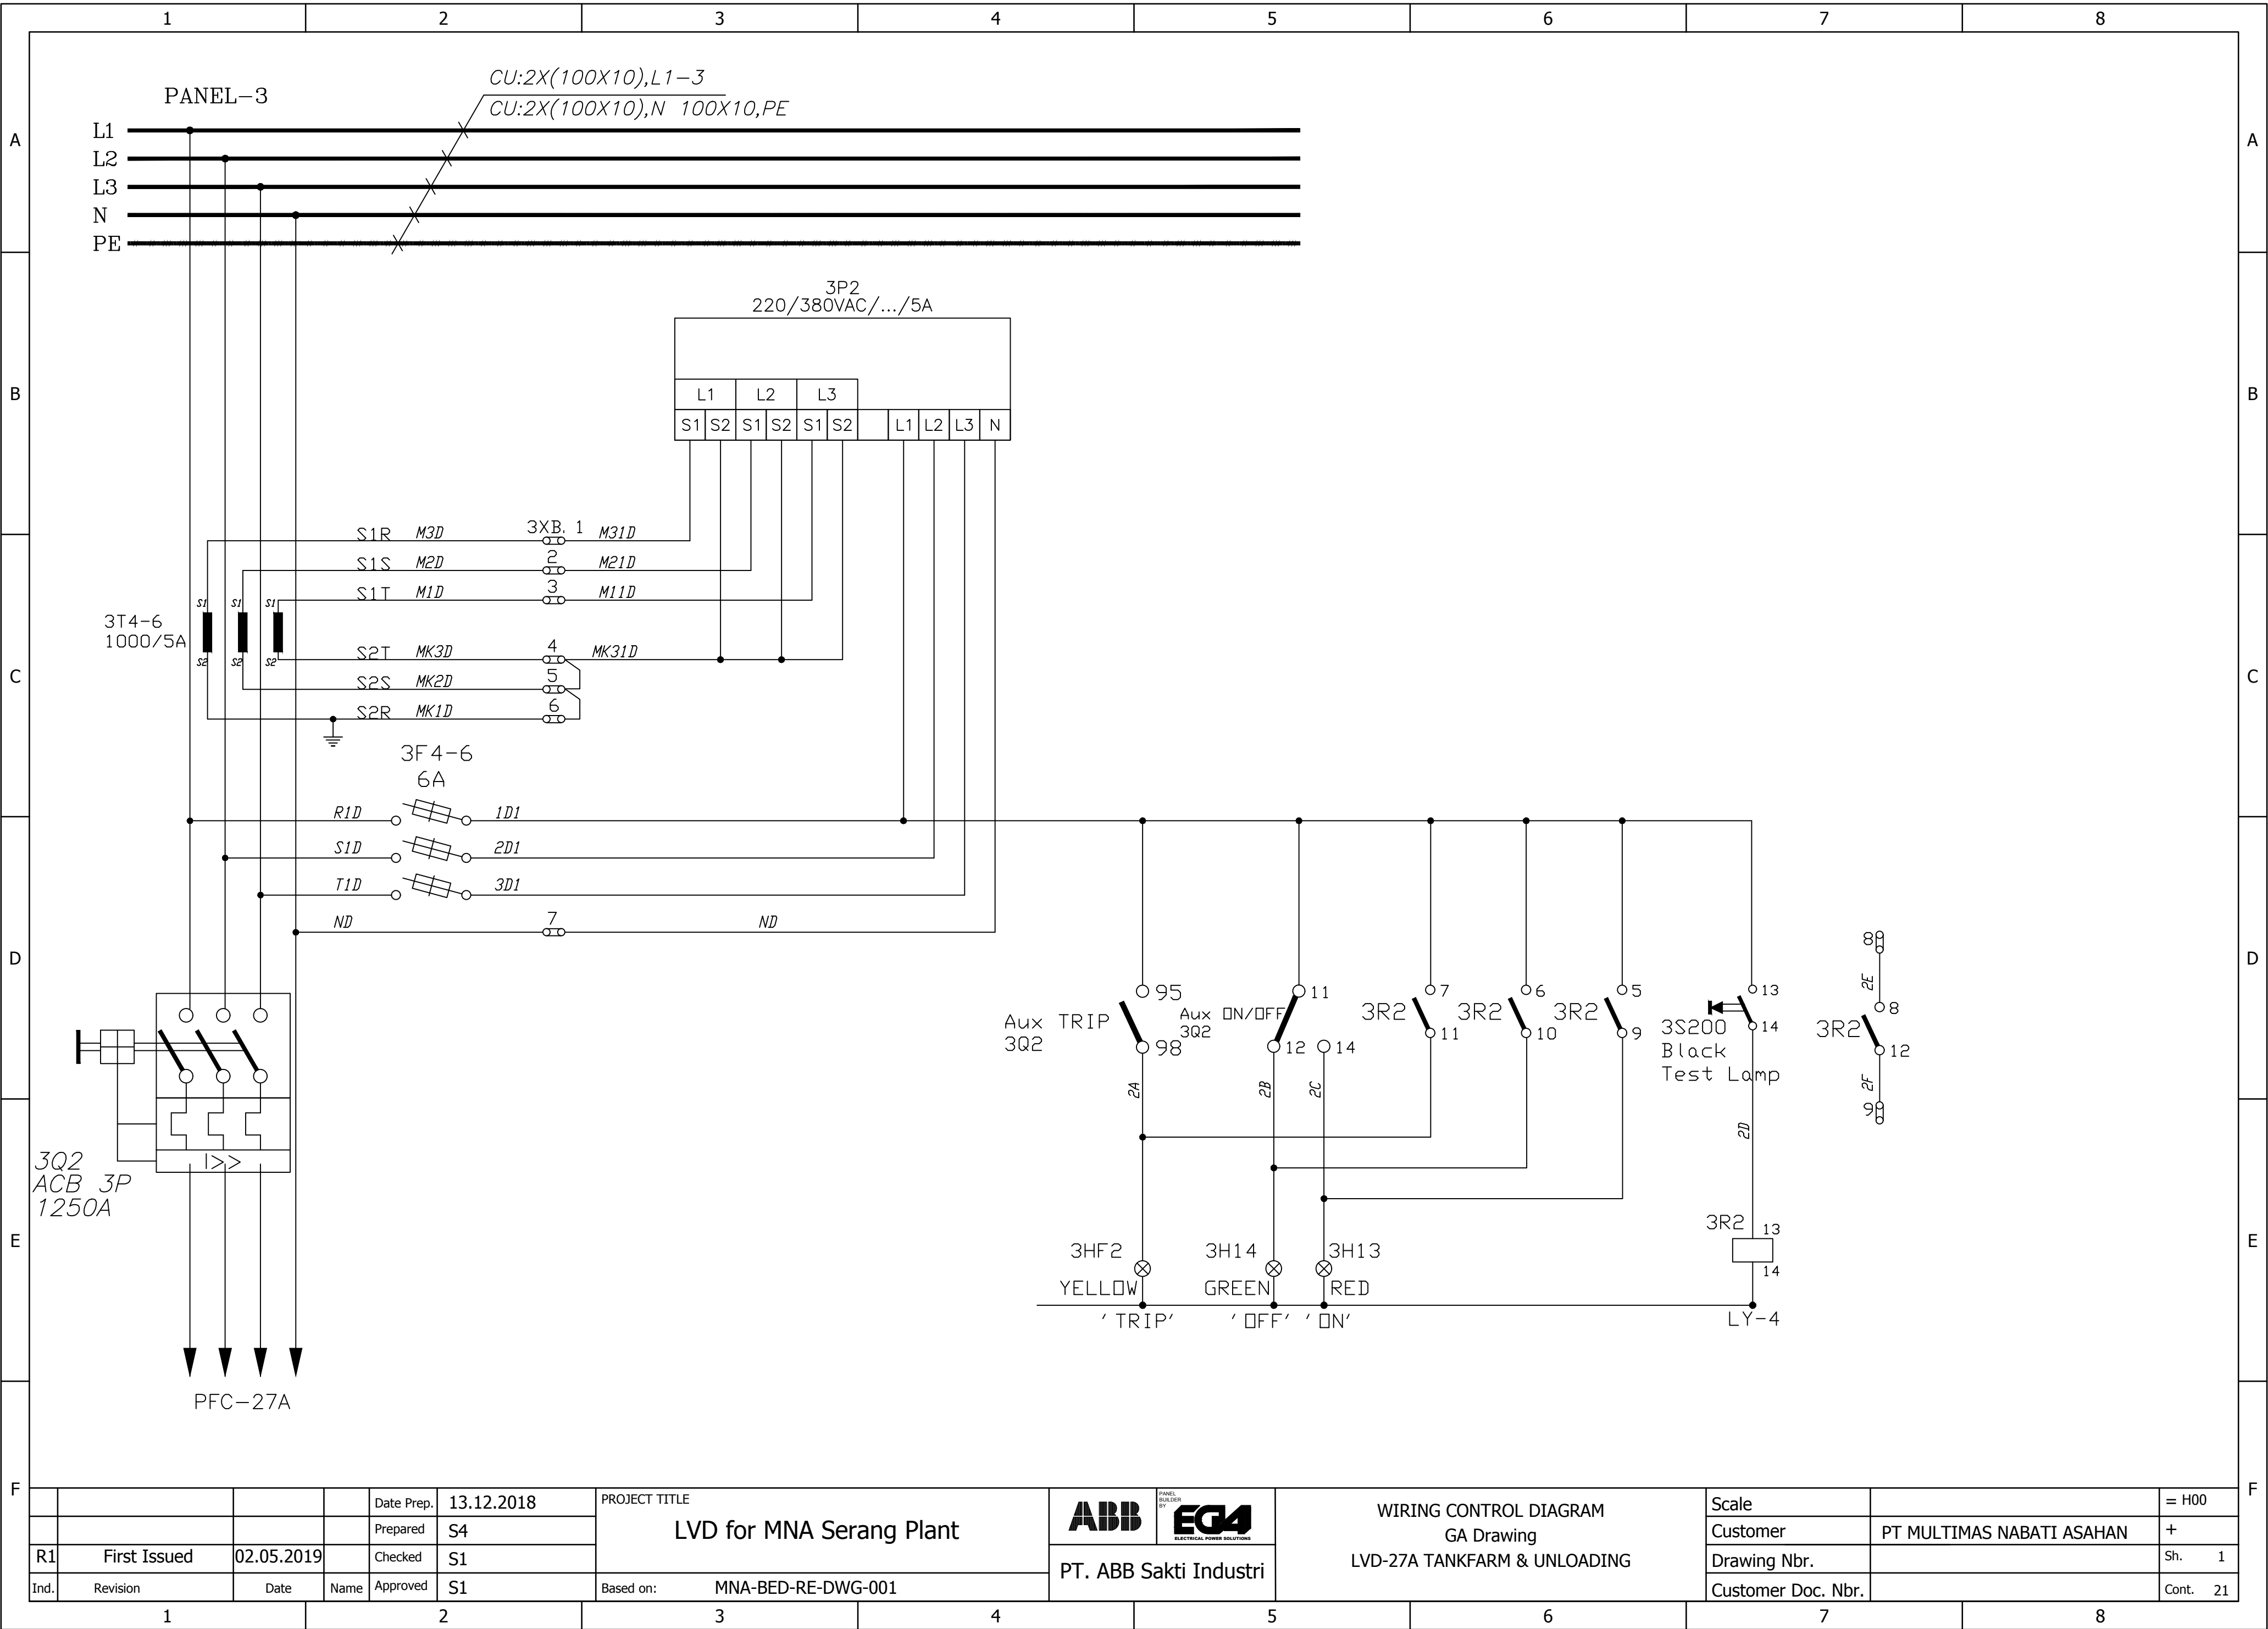

WE RESERVE ALL RIGHTS IN THIS DOCUMENT AND IN THE INFORMATION CONTAINED THEREIN. REPRODUCTION, USE OR DISCLOSURE TO THIRD PARTIES WITHOUT EXPRESS AUTHORITY IS STRICTLY FORBIDDEN.

1		2		3		4		5		6		7		8	
A	N O	D E S C R I P T I O N				T E C H N I C A L D A T A				Q T Y	D E S I G N A T I O N				
		INCOMING													
	1	Fuse Carrier 6A				AXLE/Setara				7	1F11,1F1-6				
	2	Pilot Lamp (LED) 220Vac/50Hz, Red				AXLE/Setara				2	1H1,12				
	3	Pilot Lamp (LED) 220Vac/50Hz, Yellow				AXLE/Setara				2	1H2,HF1				
	4	Pilot Lamp (LED) 220Vac/50Hz, Green				AXLE/Setara				2	1H3,H11				
	5	DIGITAL POWER METER (*)				ABB, M2M ETHERNET				1	1P1				
	6	CT 2500/5A CL.0.5 40VA				Howig, HG 120-2500				4	1T1-4				
	7	ACB 3P 2500A, 66KA, DO, Ekip Touch LSIG (*)				ABB, E2.2N25 D/O				1	1Q0				
	8	+ Shunt Trip Release (Y0) (*)				ABB, Y0				1	-				
	9	+ Motor (M) + Closing Release (YC) For E2.2-E6.2 (*)				ABB, M+YC				1	-				
	10	+ Padlocks For E2.2-E6.2 (*)				ABB,				1	-				
	11	+ Ekip Com Protocol IEC 61850 (*)				ABB,				1	-				
	12	Push Button On, 1NO, Green				Ega				1	S11				
	13	Push Button Off, 1NO, Red				Ega				1	S12				
	14	Control Relay 220Vac				Omron, LY-2				1	1RF1				
	15	Control Relay 220Vac				Omron, LY-4				2	1R1-2				
	B	16	Push Button On, 1NO, Black				Ega				1	1S100			
17															
18		OUTGOING													
19		Fuse Carrier 6A				AXLE				18	2F1-12 ; 3F1-6				
20		Pilot Lamp (LED) 220Vac/50Hz, Red				AXLE				6	2H11,13,15,17 ;3H12,14				
21		Pilot Lamp (LED) 220Vac/50Hz, Yellow				AXLE				6	2HF1-4 ;3HF1-2				
22		Pilot Lamp (LED) 220Vac/50Hz, Green				AXLE				6	2H12,14,16,18 ;3H11,13				
23		DIGITAL POWER METER (*)				ABB, M2M ETHERNET				6	2P1-4 ; 3P1-2				
24		CT 2000/5A CL.0.5 20VA				Howig, HG 82-2000				3	3T1-3				
25		CT 1500/5A CL.0.5 20VA				Howig, HG 82-1500				3	3T4-6				
26															
C															
D															
	E														
F															

1		2		3		4		5		6		7		8		
A															A	
B																B
C																C
D																D
E																E
F																F

				Date Prep.	13.12.2018	PROJECT TITLE		 	COMPONENT LIST		Scale		= H00
				Prepared	S4	LVD for MNA Serang Plant			GA Drawing		Customer	PT MULTIMAS NABATI ASAHAN	+
R1	First Issued	02.05.2019		Checked	S1			PT. ABB Sakti Industri	LVD-27A TANKFARM & UNLOADING		Drawing Nbr.		Sh. 1
Ind.	Revision	Date	Name	Approved	S1	Based on: MNA-BED-RE-DWG-001					Customer Doc. Nbr.		Cont. 21

1		2		3		4		5		6		7		8	
---	--	---	--	---	--	---	--	---	--	---	--	---	--	---	--