
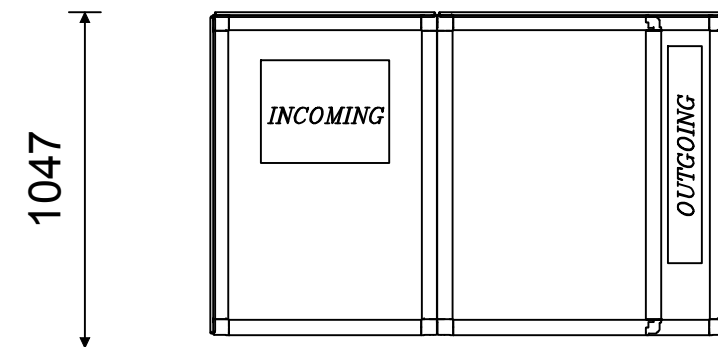
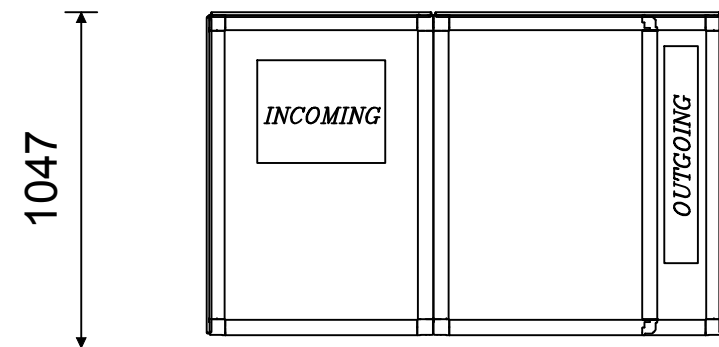
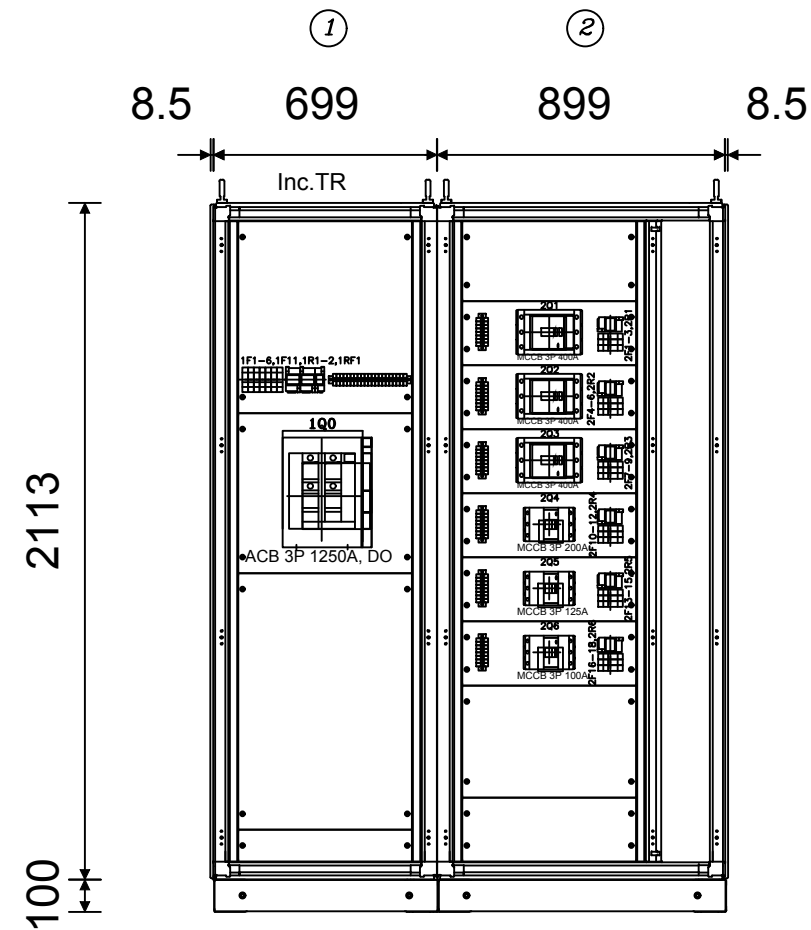



WE RESERVE ALL RIGHTS IN THIS DOCUMENT AND IN THE INFORMATION CONTAINED THEREIN. REPRODUCTION, USE OR DISCLOSURE TO THIRD PARTIES WITHOUT EXPRESS AUTHORITY IS STRICTLY FORBIDDEN.

FRONT VIEW
LVD-28A CENTRAL OFFICE AND WEIGHT BRIDGE

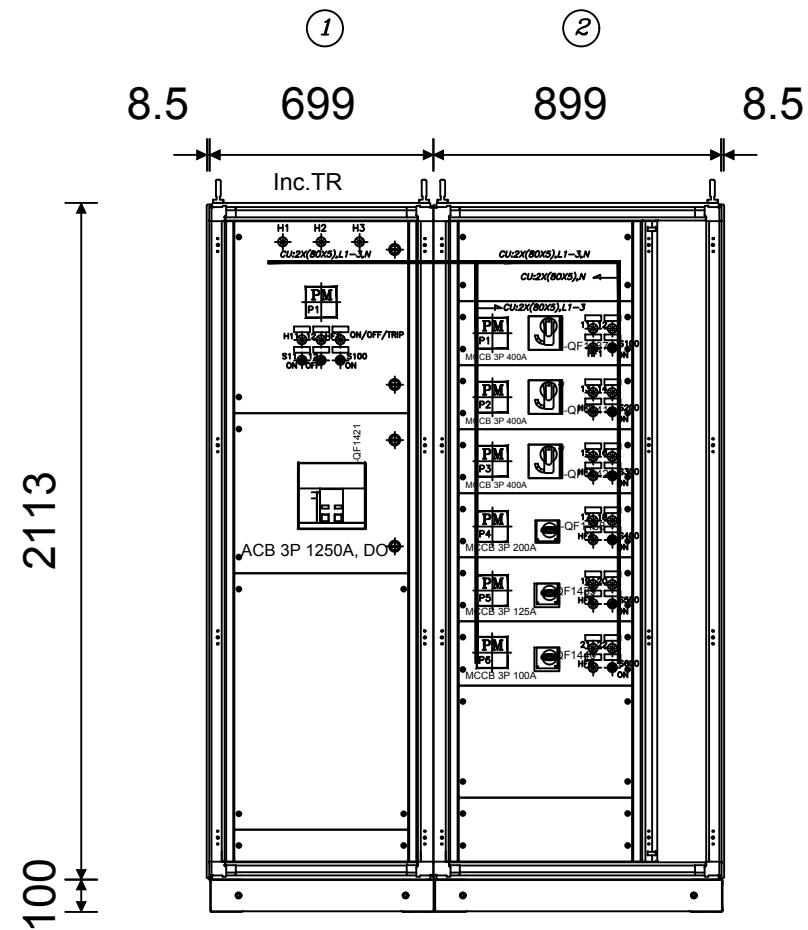

Switchboard Type : ABB Pro E
Segregation Form : 3b
Switchboard Color : ABB Pro E
Protection Degree : IP31
Busbar/Cable Color : PLN Standard
Cable Entry : (Inc) Bottom, (Out) Bottom


				Date Prep.	13.12.2018	PROJECT TITLE LVD for MNA Serang Plant	  PT. ABB Sakti Industri	FRONT VIEW GA Drawing LVD-28A CENTRAL OFFICE AND WEIGHT BRIDGE	Scale		= H00
				Prepared	S4				Customer	PT MULTIMAS NABATI ASAHAN	+
R1	First Issued	02.05.2019		Checked	S1				Drawing Nbr.		Sh. 1
Ind.	Revision	Date	Name	Approved	S1	Based on:	MNA-BED-RE-DWG-001		Customer Doc. Nbr.		Cont. 21

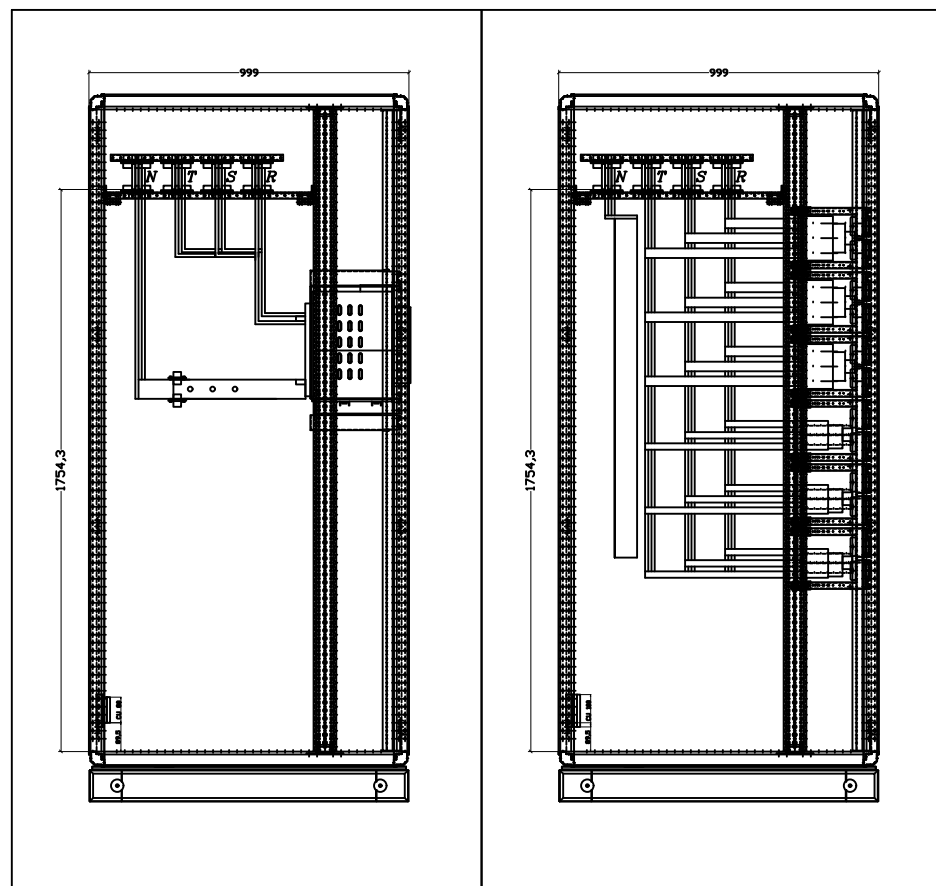

Switchboard Type : ABB Pro E
Segregation Form : 3b
Switchboard Color : ABB Pro E
Protection Degree : IP31
Busbar/Cable Color : PLN Standard
Cable Entry : (Inc) Bottom, (Out) Bottom

			Date Prep.	13.12.2018	PROJECT TITLE LVD for MNA Serang Plant	 	FRONT VIEW GA Drawing	Scale		= H00
			Prepared	S4				Customer	PT MULTIMAS NABATI ASAHAN	+
R1	First Issued	02.05.2019	Checked	S1				Drawing Nbr.		Sh. 1A
Ind.	Revision	Date	Name	Approved	S1	Based on: MNA-BED-RE-DWG-001	PT. ABB Sakti Industri	LVD-28A CENTRAL OFFICE AND WEIGHT BRIDGE	Customer Doc. Nbr.	Cont. 21

WE RESERVE ALL RIGHTS IN THIS DOCUMENT AND IN THE INFORMATION CONTAINED THEREIN. REPRODUCTION, USE OR DISCLOSURE TO THIRD PARTIES WITHOUT EXPRESS AUTHORITY IS STRICTLY FORBIDDEN.

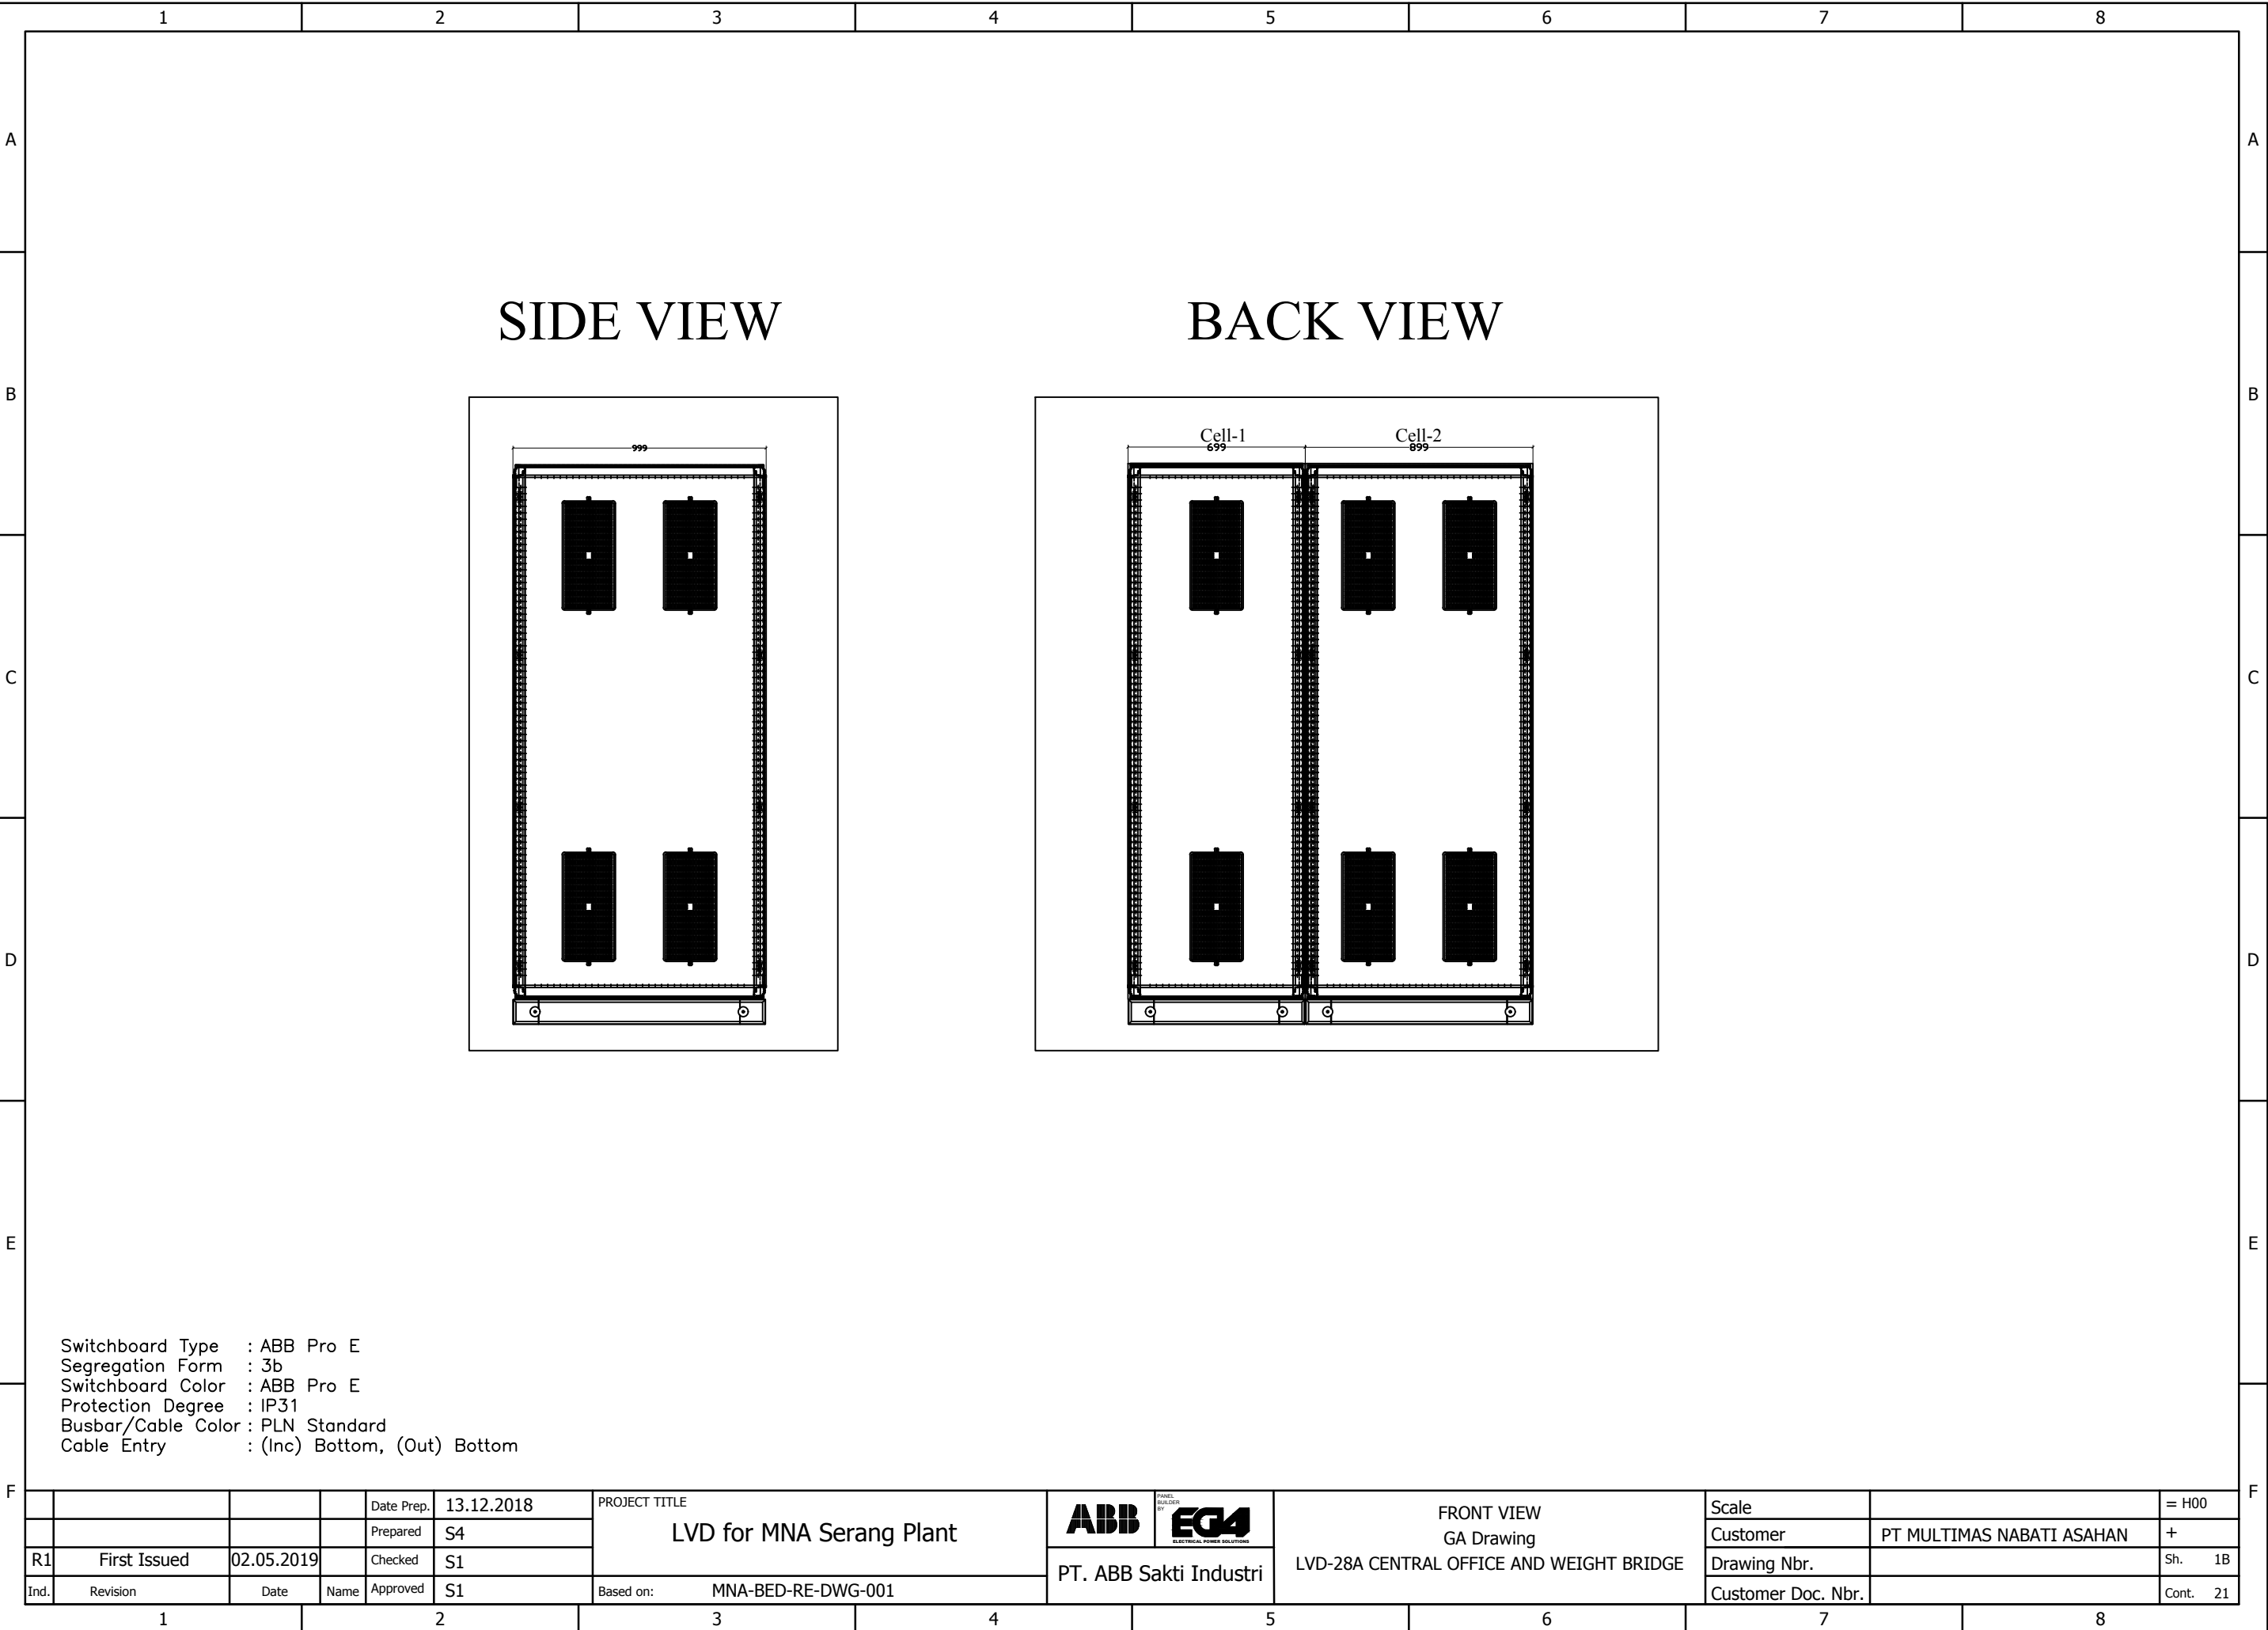

A

B


C

D

E


F

WE RESERVE ALL RIGHTS IN THIS DOCUMENT AND IN THE INFORMATION CONTAINED THEREIN. REPRODUCTION, USE OR DISCLOSURE TO THIRD PARTIES WITHOUT EXPRESS AUTHORITY IS STRICTLY FORBIDDEN.

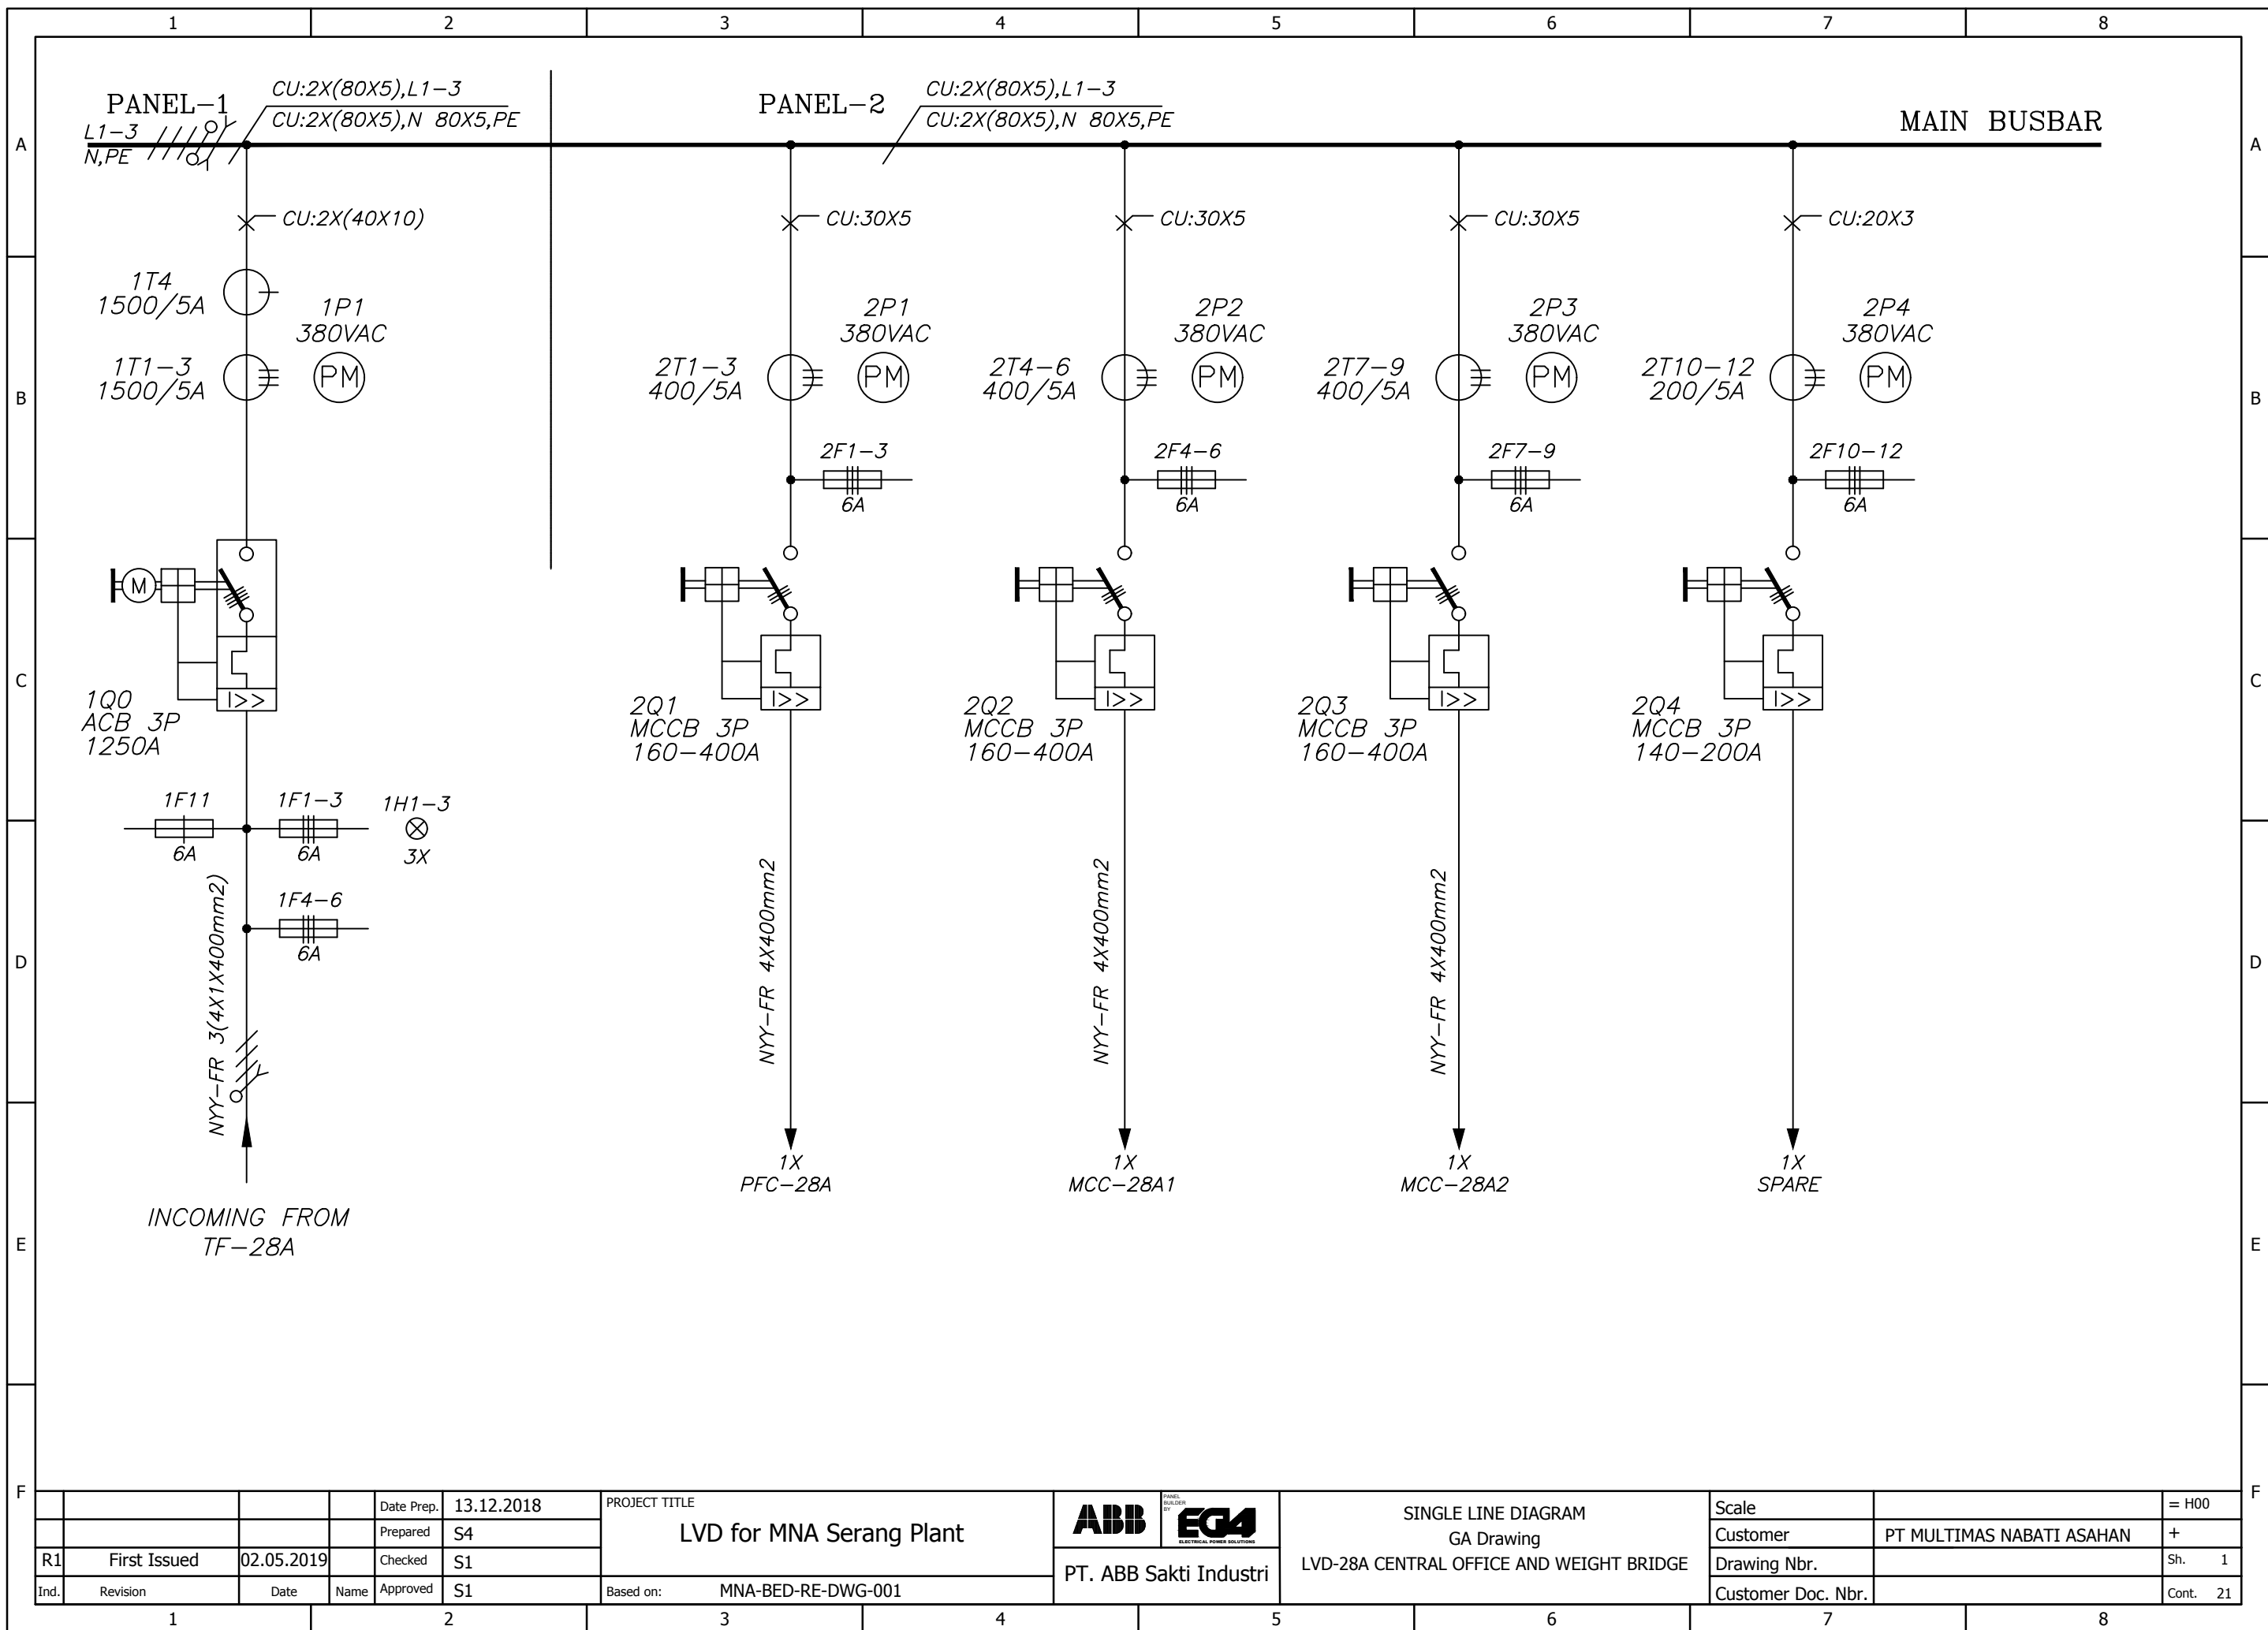

			Date Prep.	13.12.2018	PROJECT TITLE LVD for MNA Serang Plant	 	SINGLE LINE DIAGRAM GA Drawing LVD-28A CENTRAL OFFICE AND WEIGHT BRIDGE	Scale		= H00	
			Prepared	S4				Customer	PT MULTIMAS NABATI ASAHAN	+	
R1	First Issued	02.05.2019	Checked	S1		PT. ABB Sakti Industri		Drawing Nbr.		Sh.	1
Ind.	Revision	Date	Name	Approved	S1	Based on: MNA-BED-RE-DWG-001		Customer Doc. Nbr.		Cont.	21

WE RESERVE ALL RIGHTS IN THIS DOCUMENT AND IN THE INFORMATION CONTAINED THEREIN. REPRODUCTION, USE OR DISCLOSURE TO THIRD PARTIES WITHOUT EXPRESS AUTHORITY IS STRICTLY FORBIDDEN.

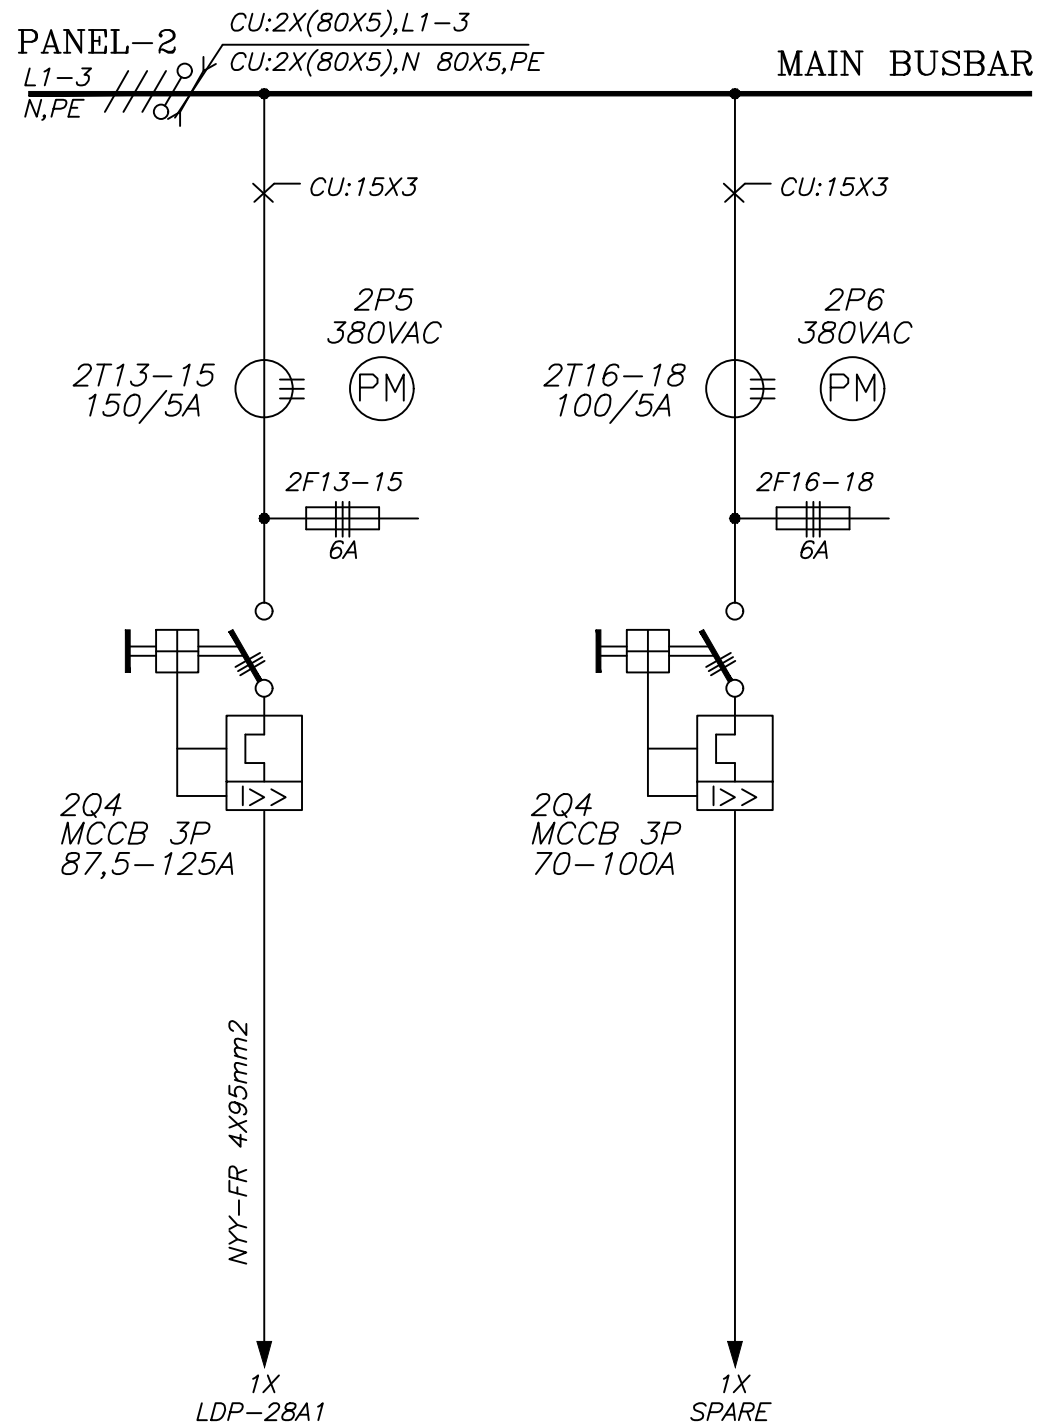

				Date Prep.	13.12.2018	PROJECT TITLE LVD for MNA Serang Plant	  PT. ABB Sakti Industri	SINGLE LINE DIAGRAM GA Drawing LVD-28A CENTRAL OFFICE AND WEIGHT BRIDGE	Scale		= H00
				Prepared	S4				Customer	PT MULTIMAS NABATI ASAHAN	+
R1	First Issued	02.05.2019		Checked	S1				Drawing Nbr.		Sh. 1
Ind.	Revision	Date	Name	Approved	S1	Based on:	MNA-BED-RE-DWG-001		Customer Doc. Nbr.		Cont. 21

1

2

3

4


5

6

7

8

WE RESERVE ALL RIGHTS IN THIS DOCUMENT AND IN THE INFORMATION CONTAINED THEREIN. REPRODUCTION, USE OR DISCLOSURE TO THIRD PARTIES WITHOUT EXPRESS AUTHORITY IS STRICTLY FORBIDDEN.

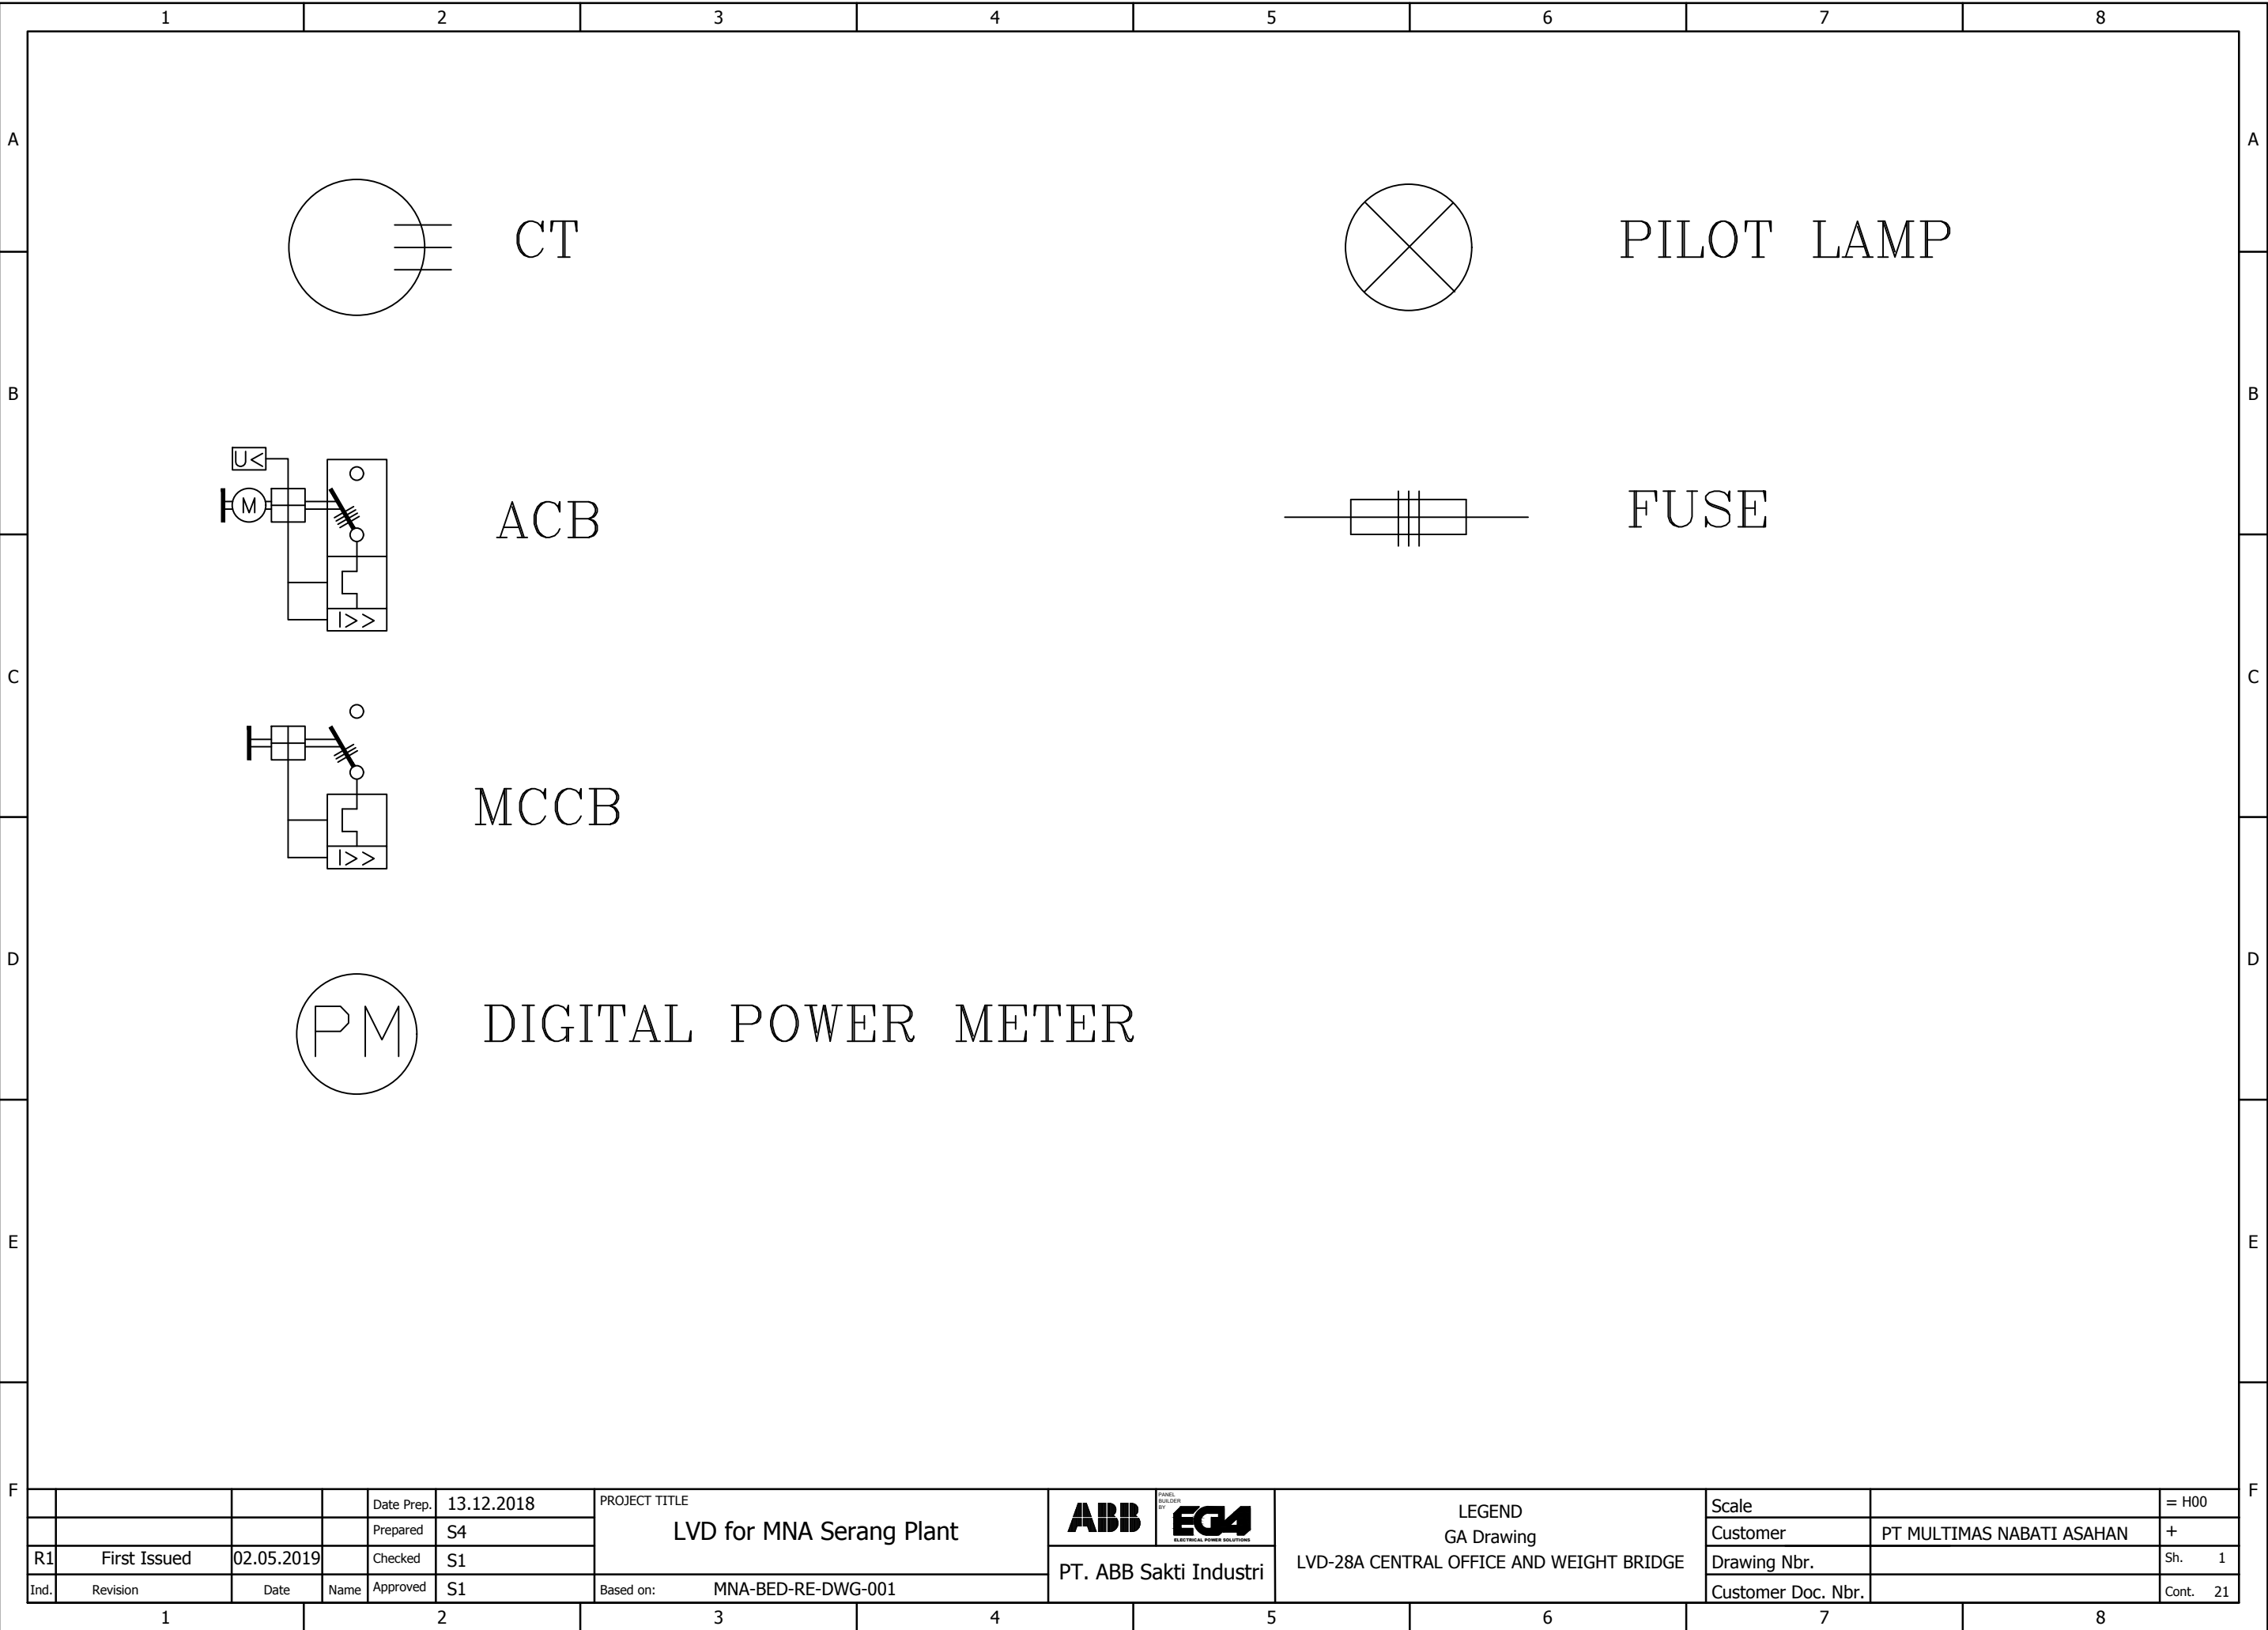

PROJECT TITLE
LVD for MNA Serang Plant


ABB **EG4**
ELECTRICAL POWER SOLUTIONS
PT. ABB Sakti Industri

LEGEND
GA Drawing
LVD-28A CENTRAL OFFICE AND WEIGHT BRIDGE


Scale		= H00
Customer	PT MULTIMAS NABATI ASAHAN	+
Drawing Nbr.		Sh. 1
Customer Doc. Nbr.		Cont. 21

Based on: MNA-BED-RE-DWG-001


WE RESERVE ALL RIGHTS IN THIS DOCUMENT AND IN THE INFORMATION CONTAINED THEREIN. REPRODUCTION, USE OR DISCLOSURE TO THIRD PARTIES WITHOUT EXPRESS AUTHORITY IS STRICTLY FORBIDDEN.

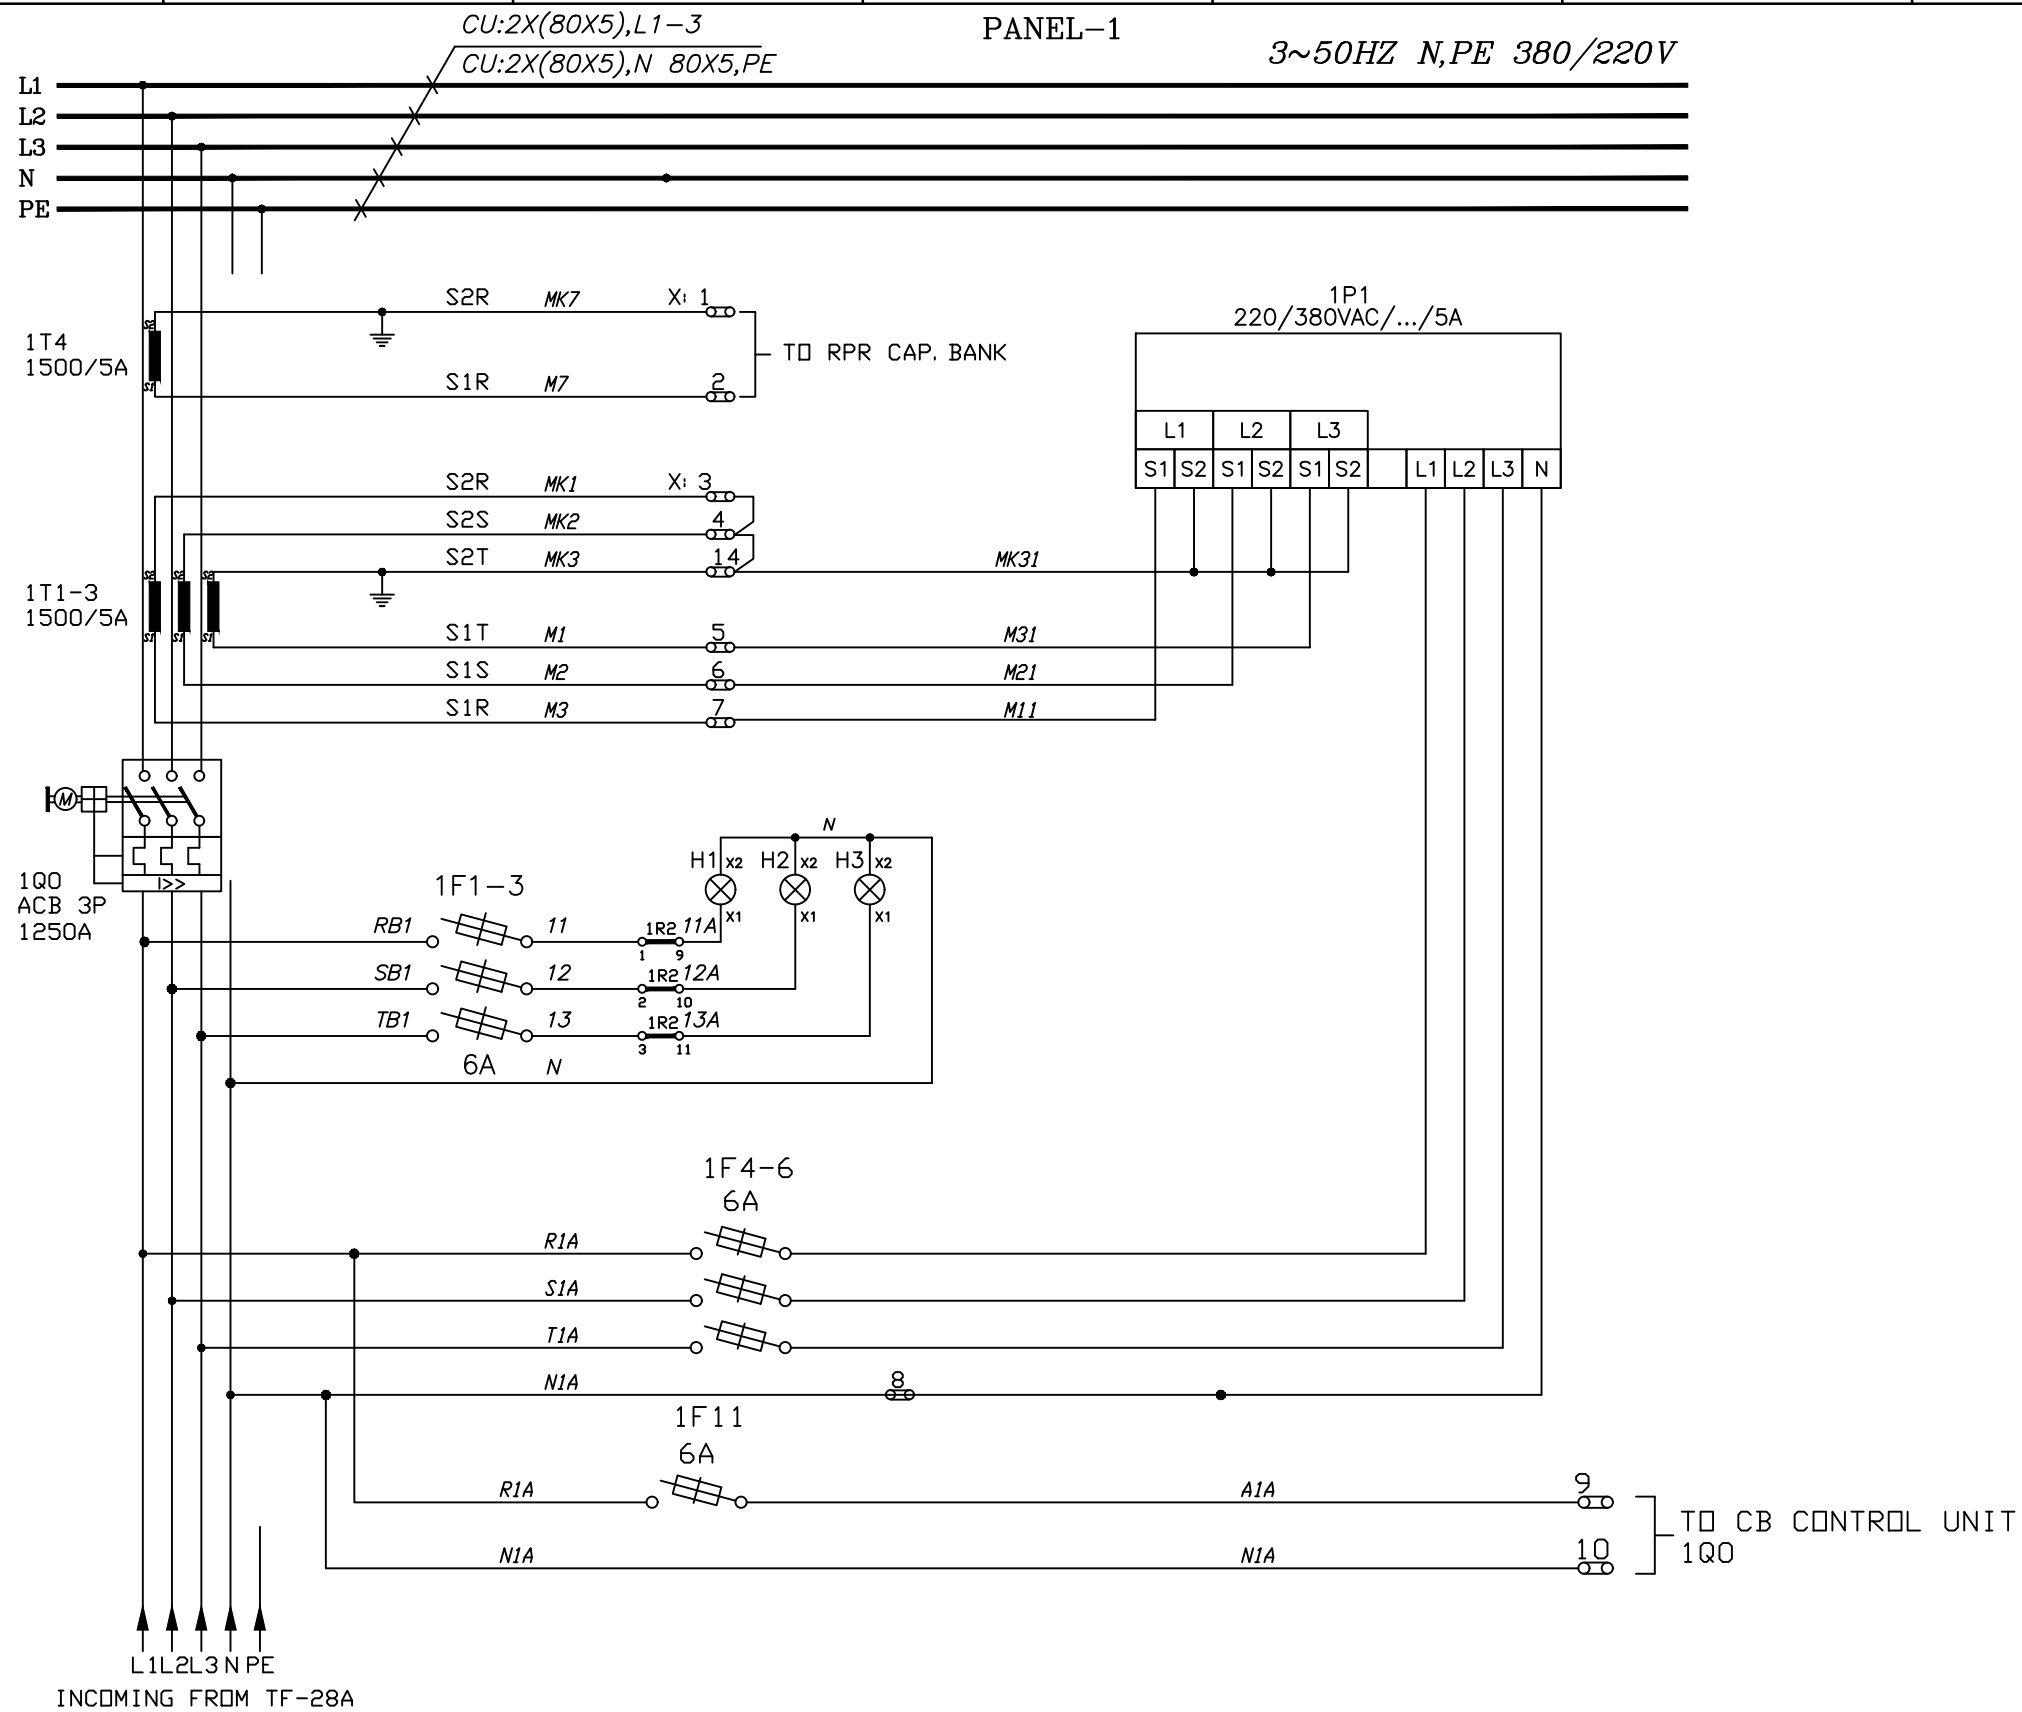


				Date Prep.	13.12.2018	PROJECT TITLE LVD for MNA Serang Plant	ABB PANEL BUILDER BY EG4 ELECTRICAL POWER SOLUTIONS PT. ABB Sakti Industri	WIRING CONTROL DIAGRAM GA Drawing LVD-28A CENTRAL OFFICE AND WEIGHT BRIDGE	Scale		= H00
				Prepared	S4				Customer	PT MULTIMAS NABATI ASAHAN	+
R1	First Issued	02.05.2019		Checked	S1				Drawing Nbr.		Sh. 1
Ind.	Revision	Date	Name	Approved	S1	Based on:	MNA-BED-RE-DWG-001		Customer Doc. Nbr.		Cont. 21

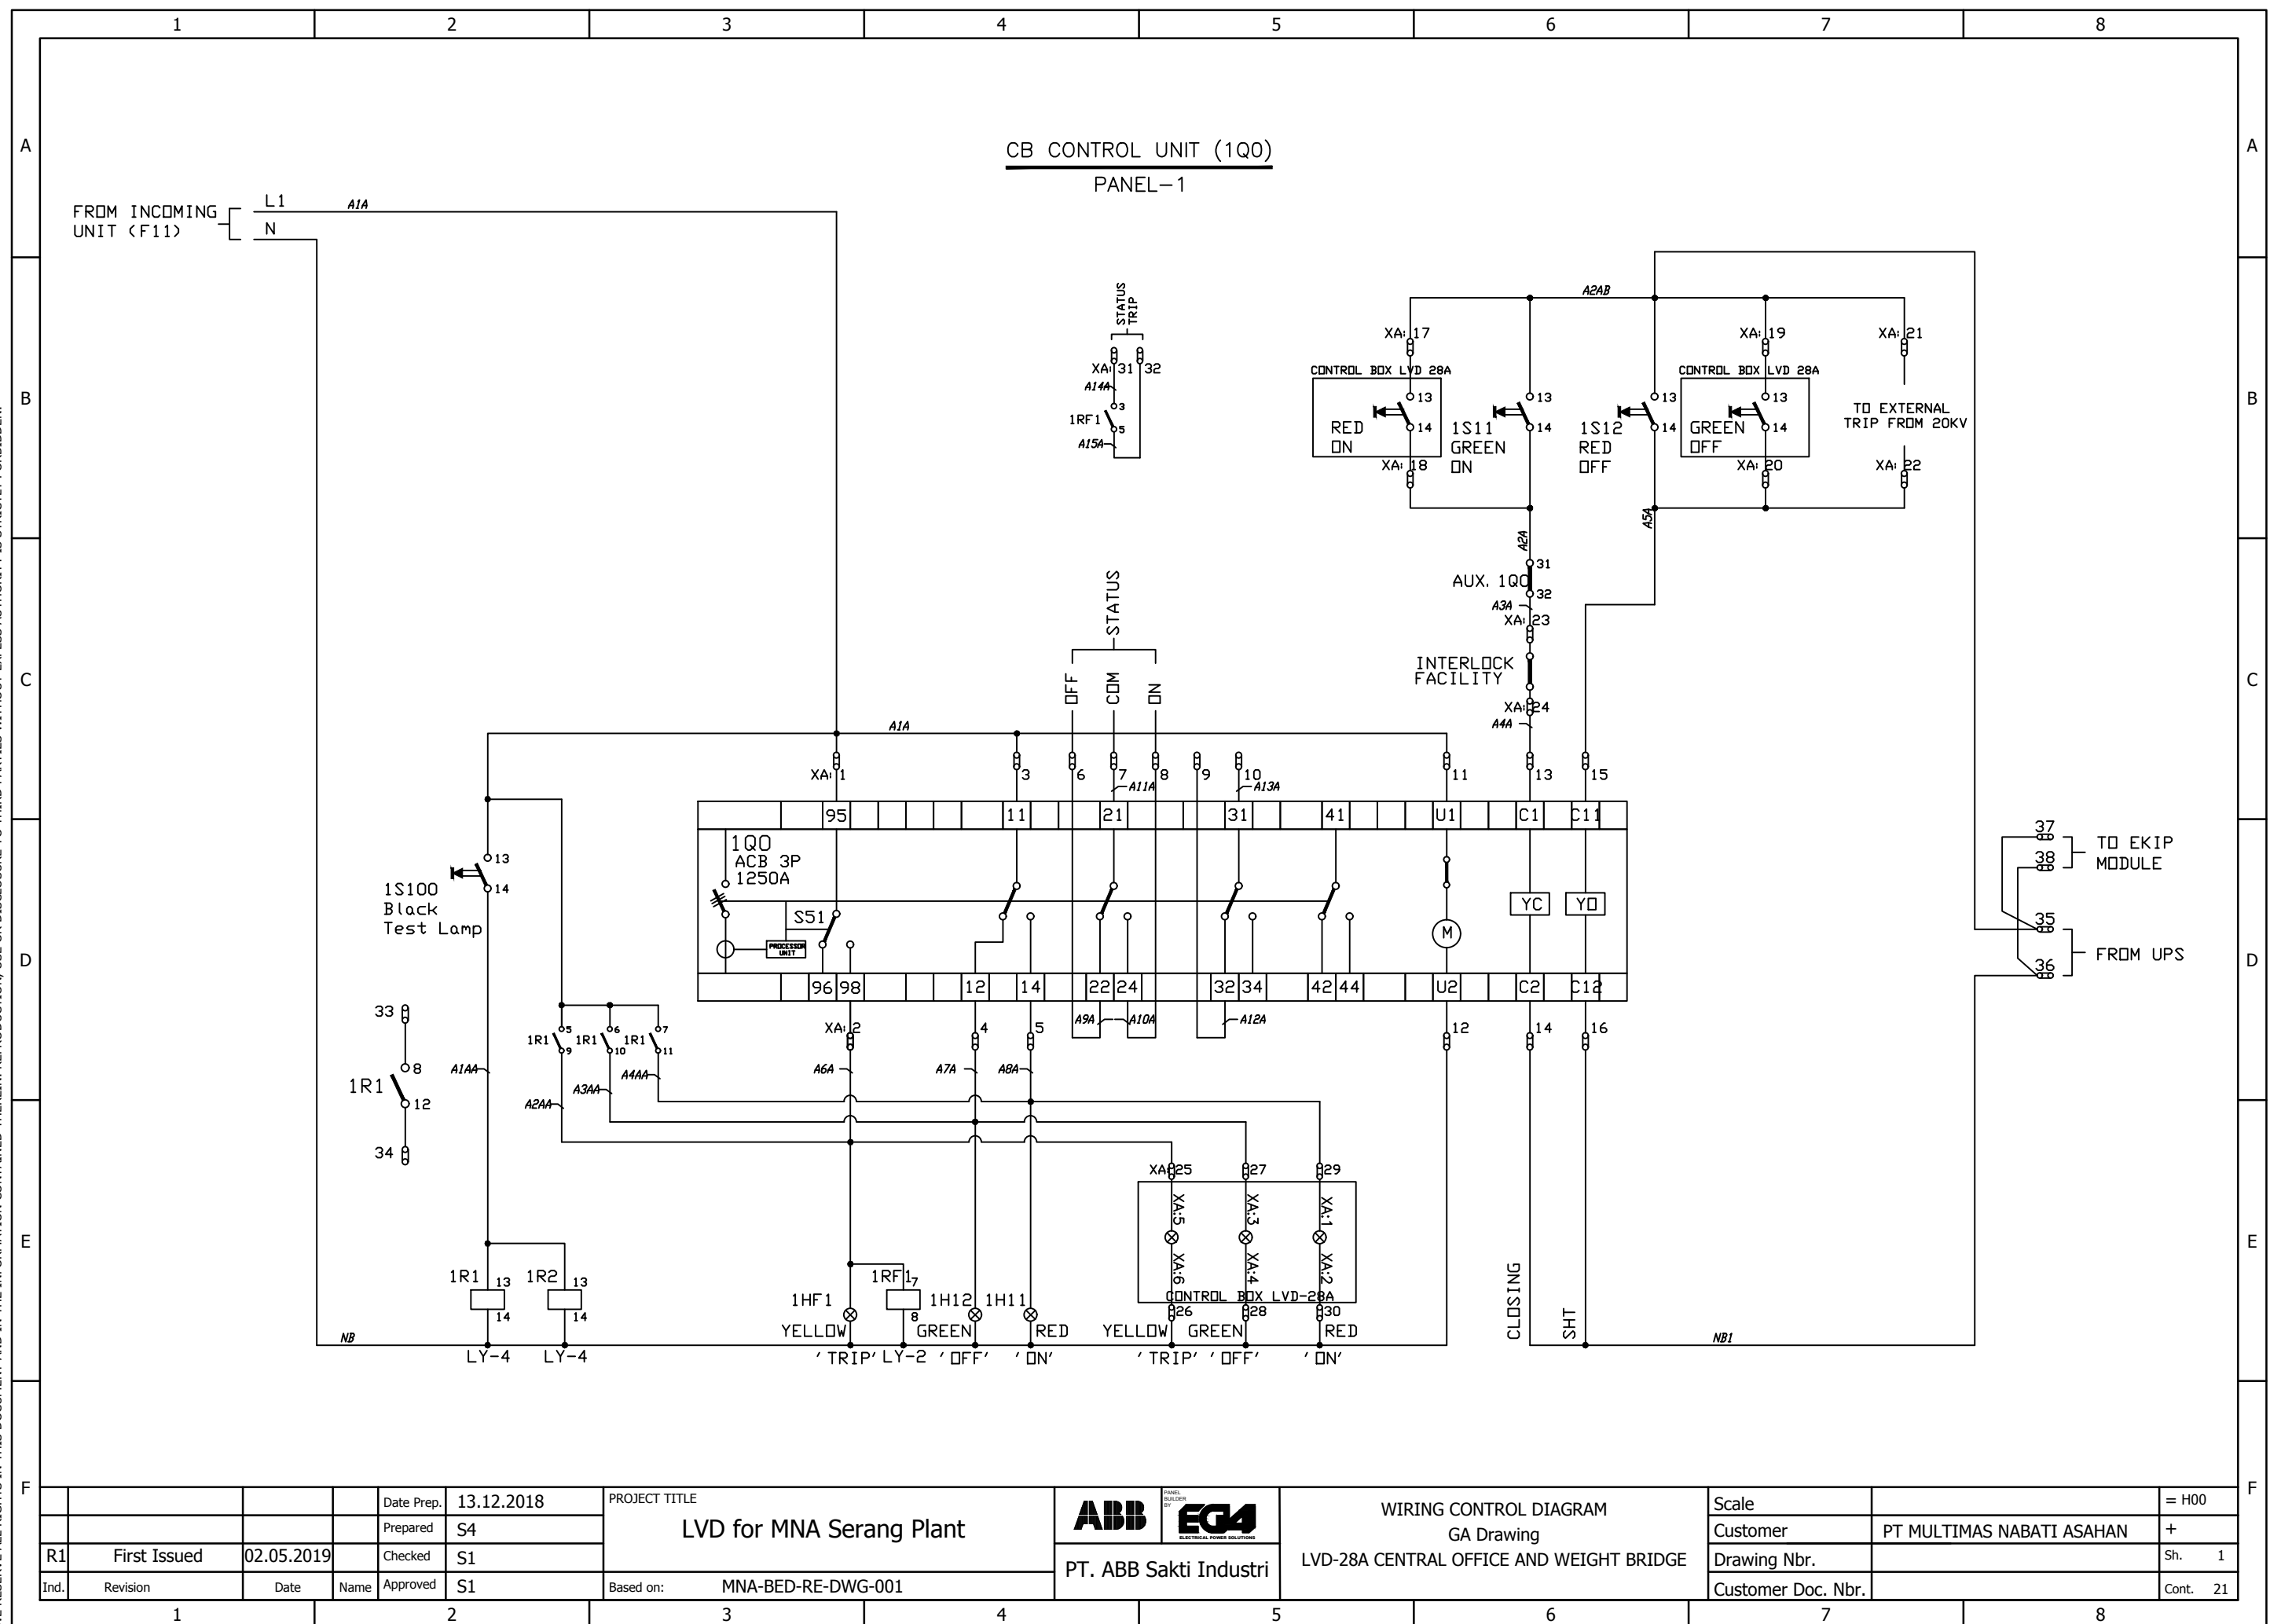

WE RESERVE ALL RIGHTS IN THIS DOCUMENT AND IN THE INFORMATION CONTAINED THEREIN. REPRODUCTION, USE OR DISCLOSURE TO THIRD PARTIES WITHOUT EXPRESS AUTHORITY IS STRICTLY FORBIDDEN.

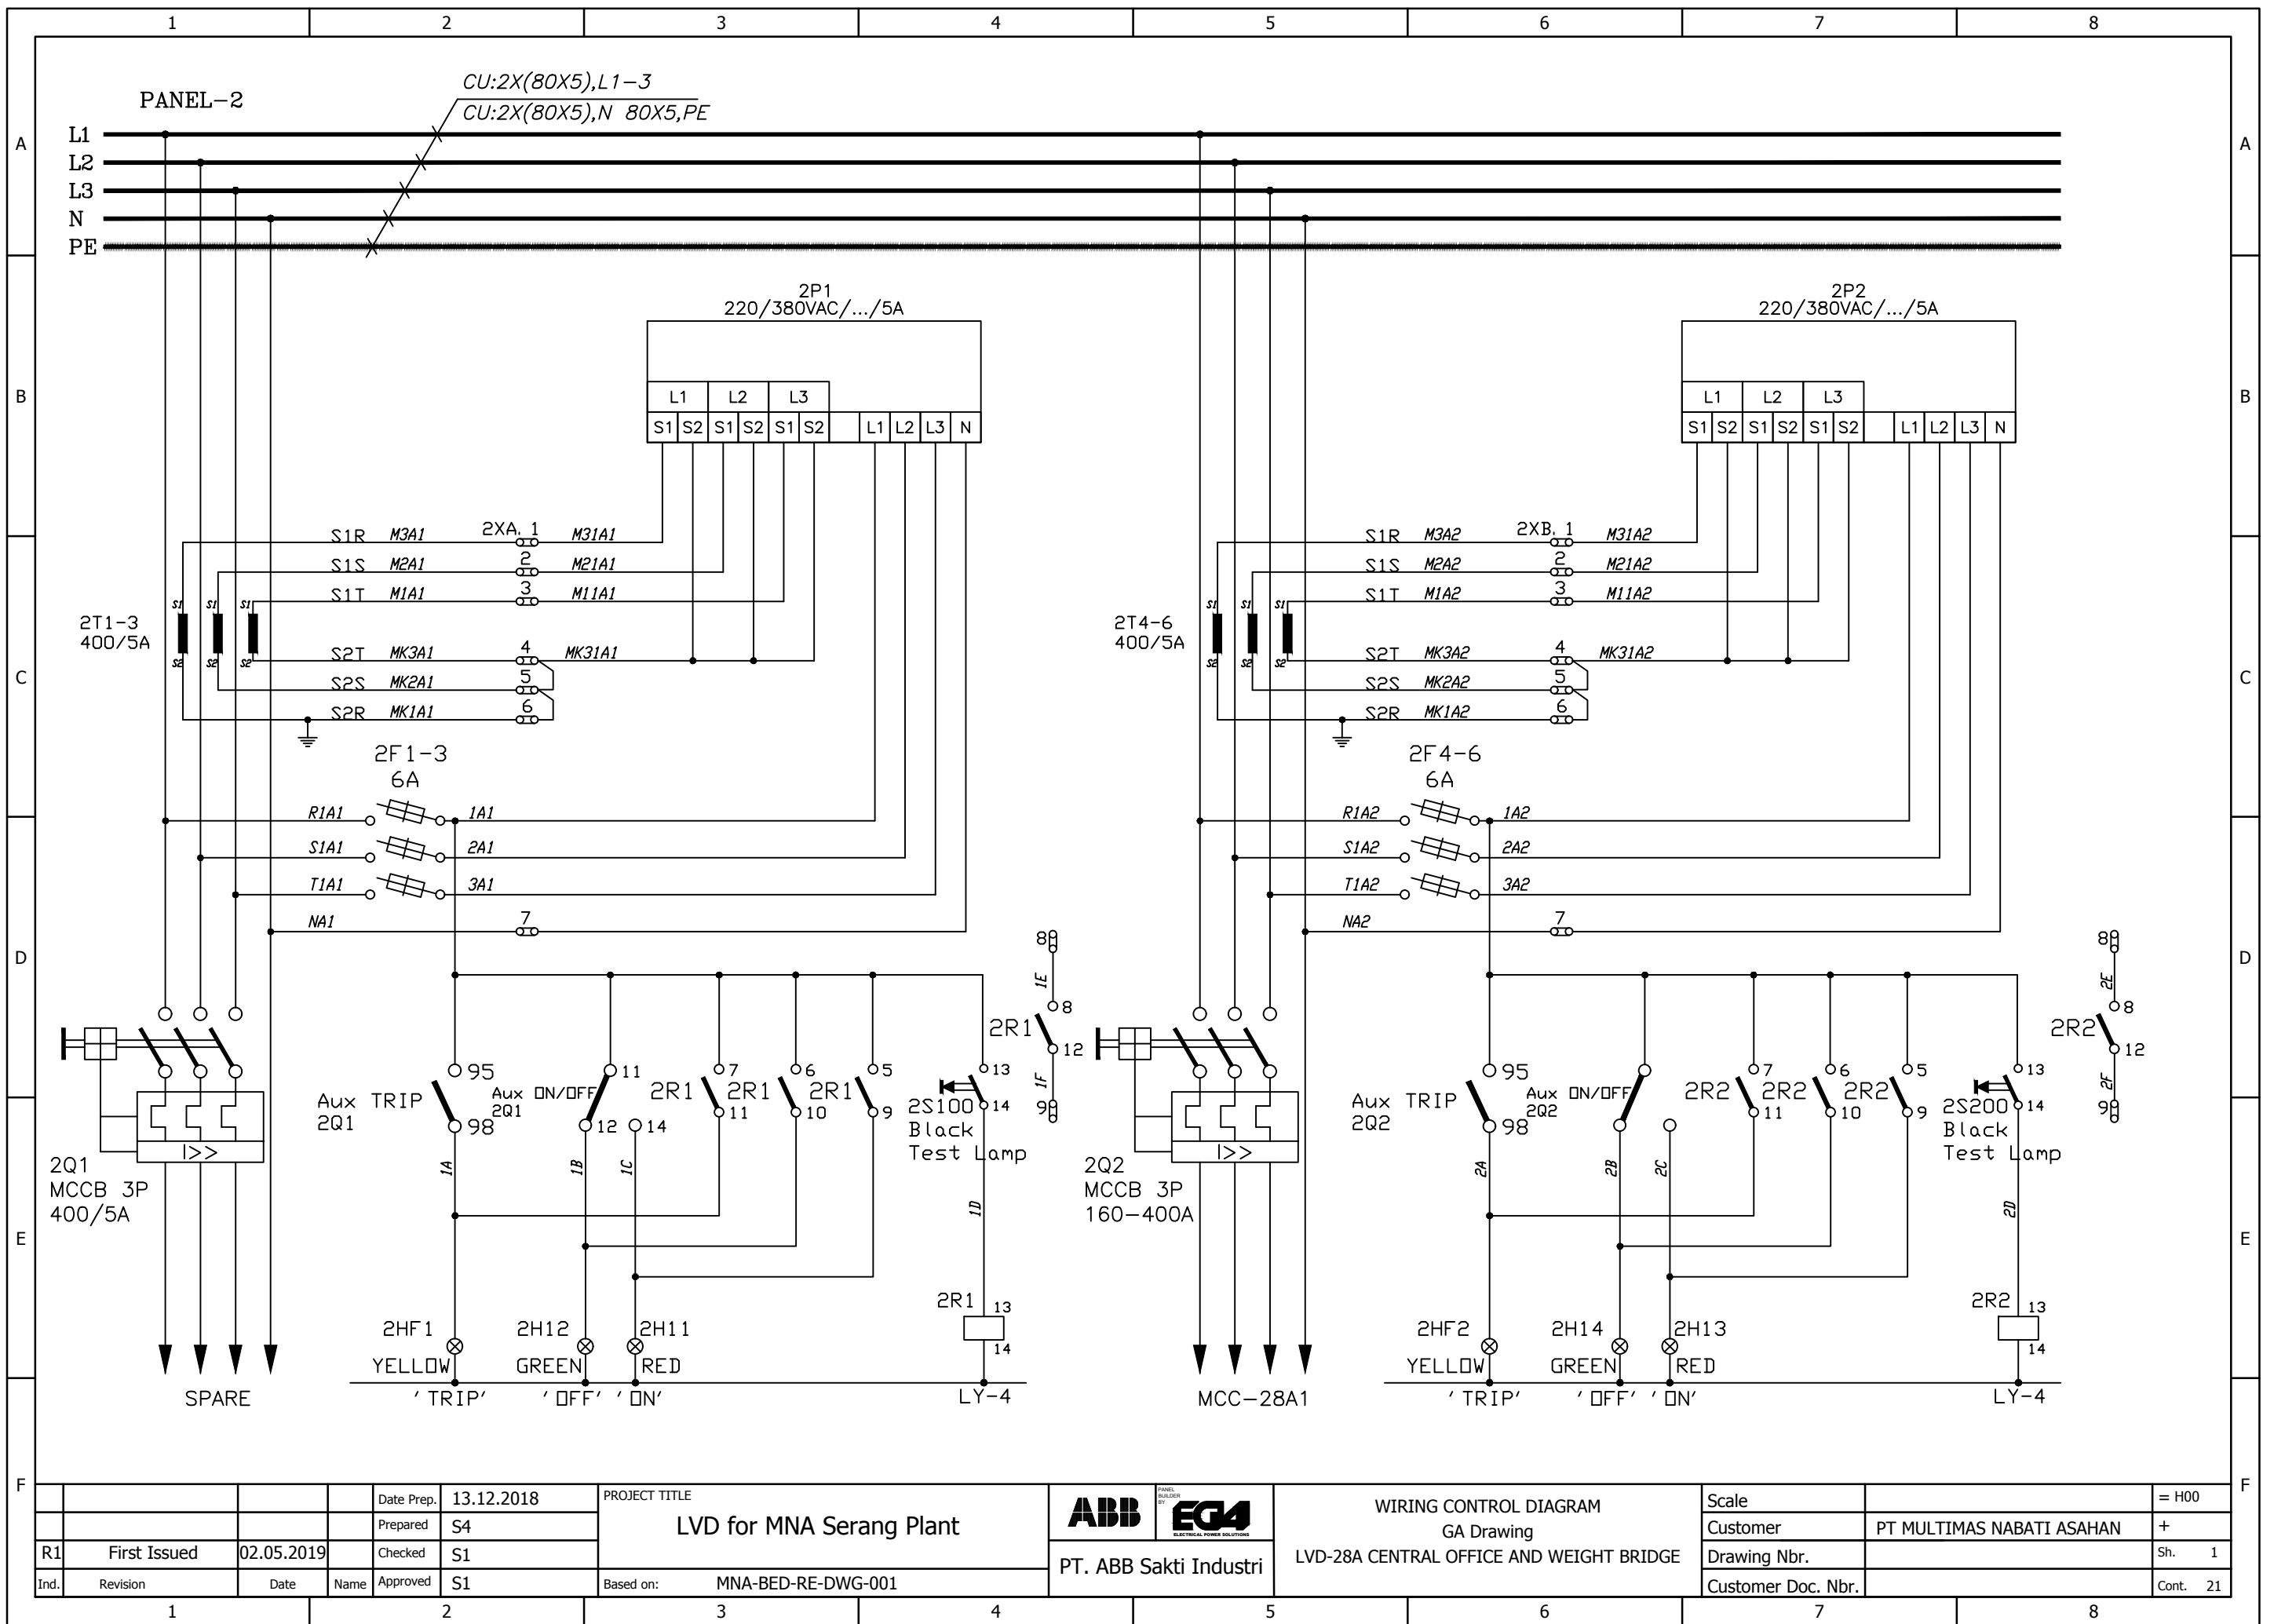


WE RESERVE ALL RIGHTS IN THIS DOCUMENT AND IN THE INFORMATION CONTAINED THEREIN. REPRODUCTION, USE OR DISCLOSURE TO THIRD PARTIES WITHOUT EXPRESS AUTHORITY IS STRICTLY FORBIDDEN.

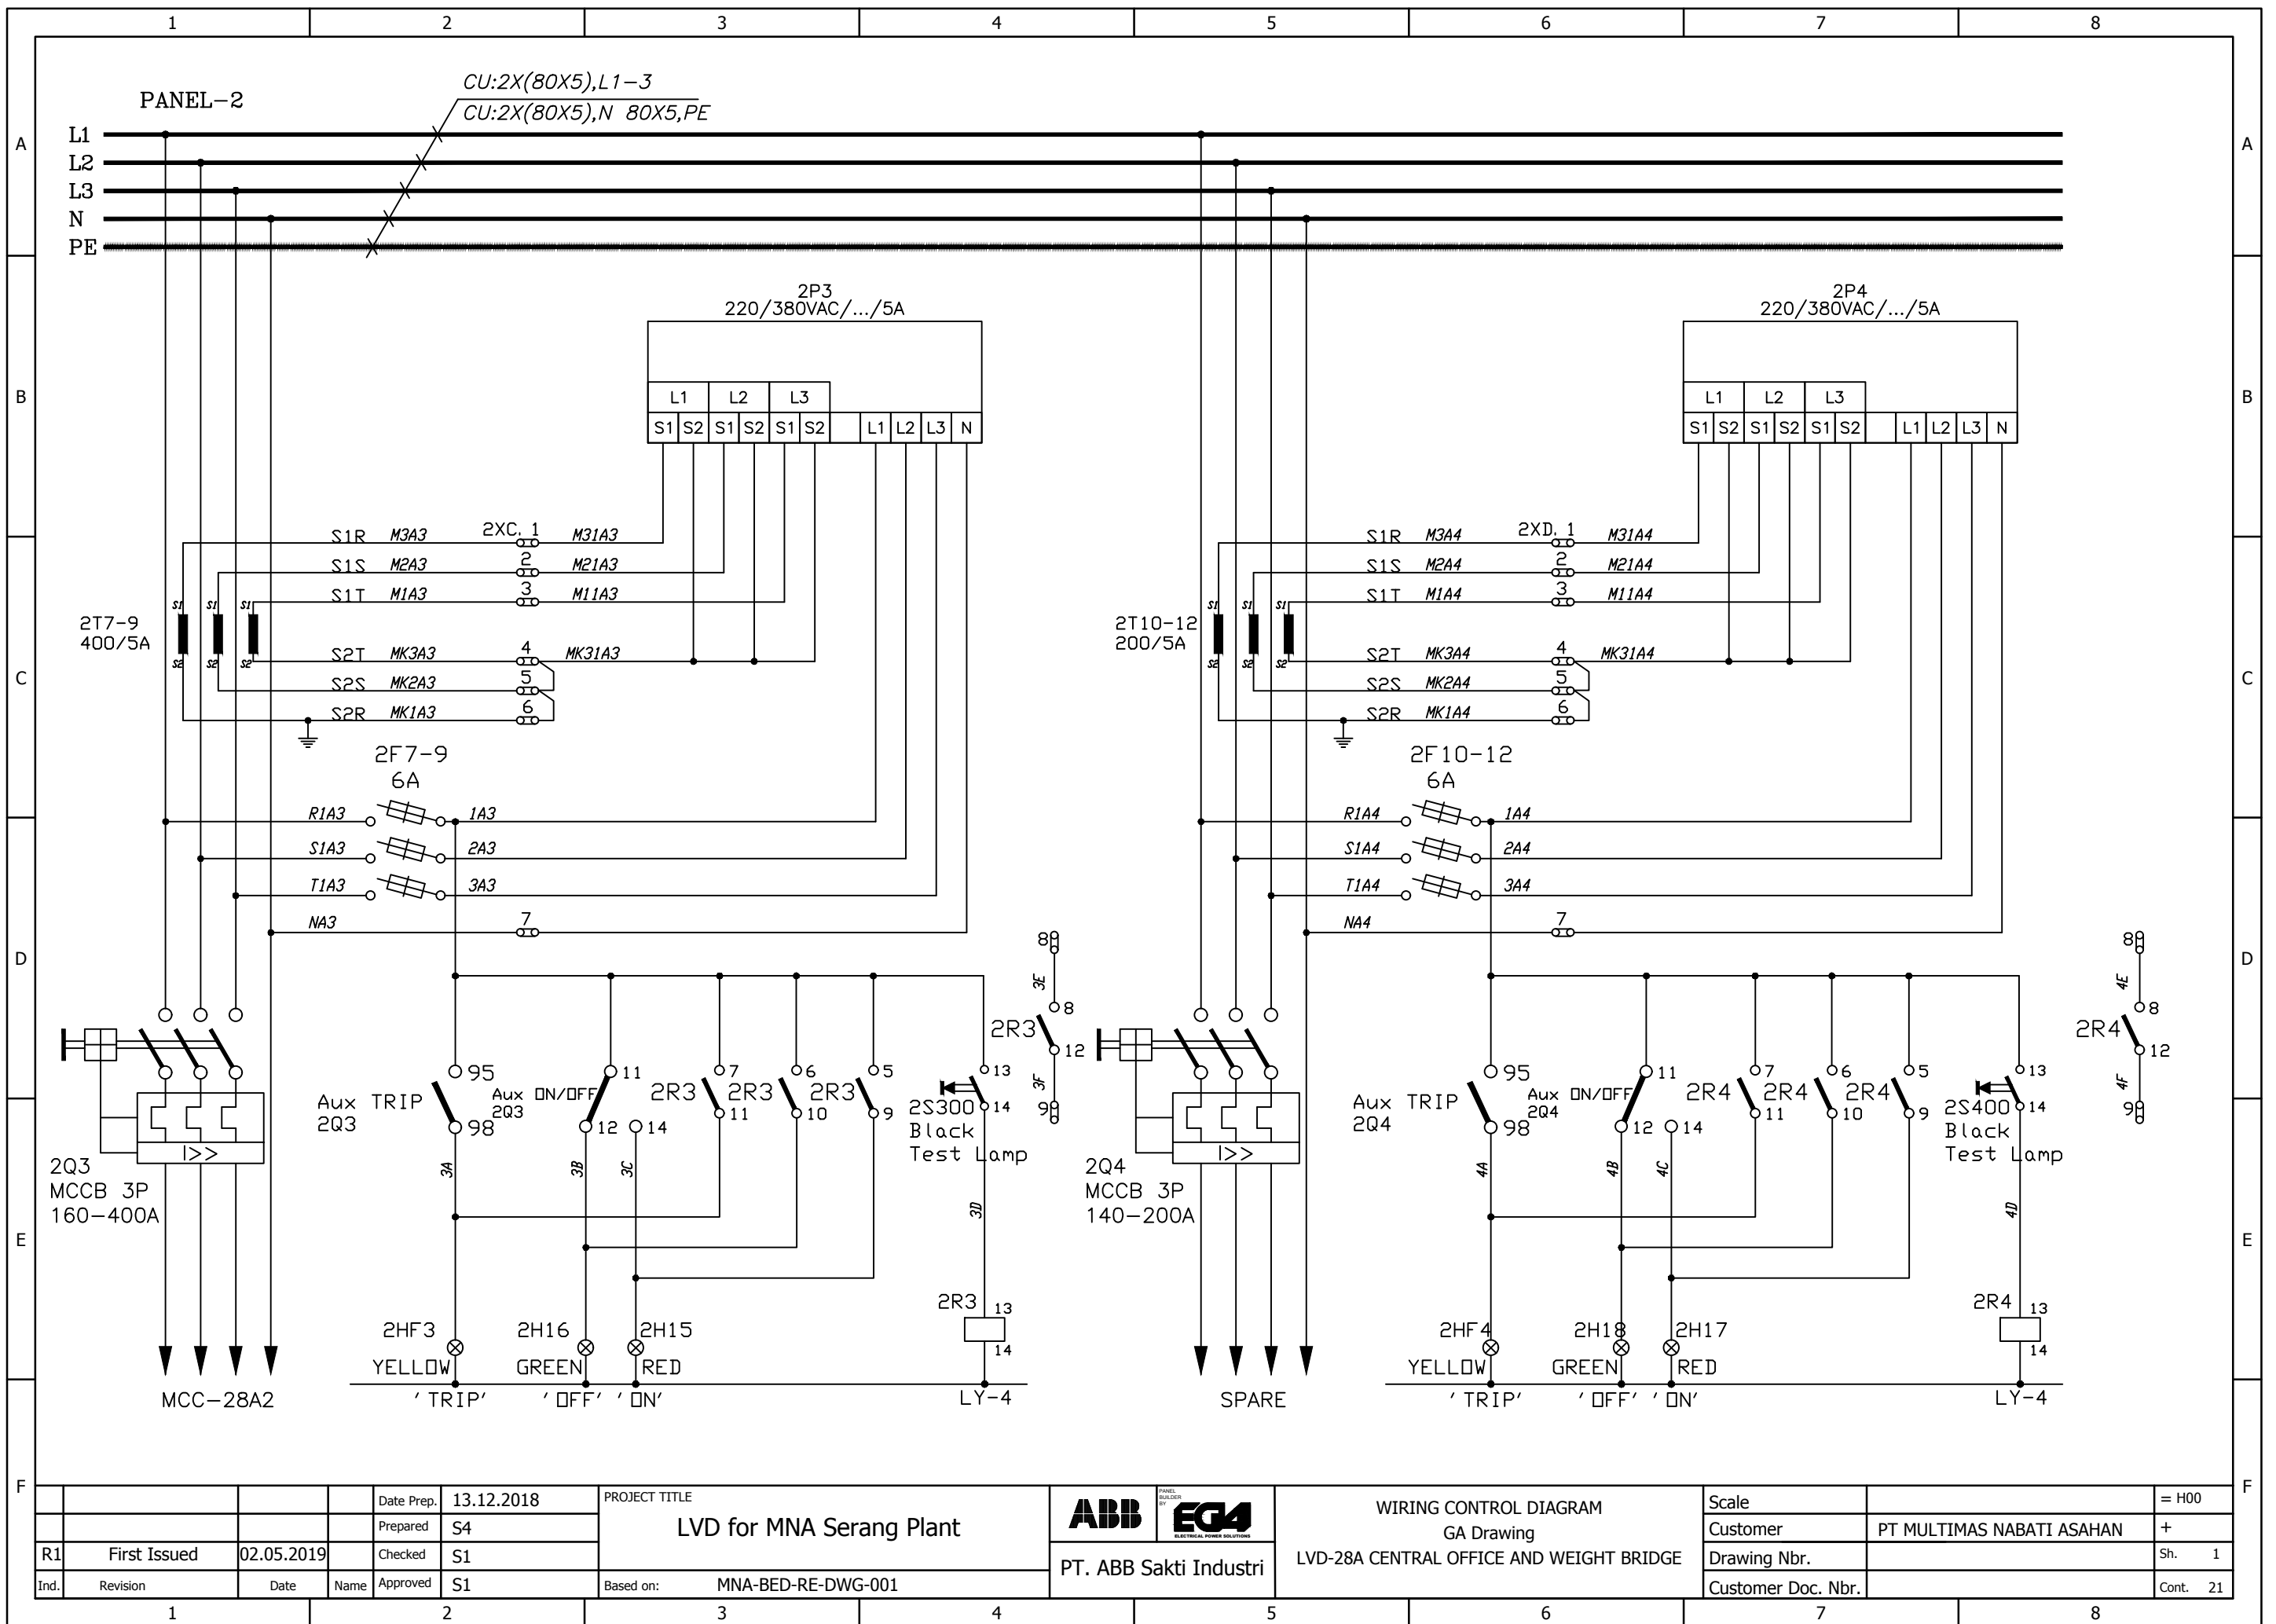

Date Prep.		13.12.2018		PROJECT TITLE		WIRING CONTROL DIAGRAM		Scale		= H00	
Prepared		S4		LVD for MNA Serang Plant		GA Drawing		Customer		PT MULTIMAS NABATI ASAHAN	
Checked		S1		Based on:		MNA-BED-RE-DWG-001		Drawing Nbr.		Sh. 1	
Ind.		Revision		Date		Name		Customer Doc. Nbr.		Cont. 21	

WE RESERVE ALL RIGHTS IN THIS DOCUMENT AND IN THE INFORMATION CONTAINED THEREIN. REPRODUCTION, USE OR DISCLOSURE TO THIRD PARTIES WITHOUT EXPRESS AUTHORITY IS STRICTLY FORBIDDEN.

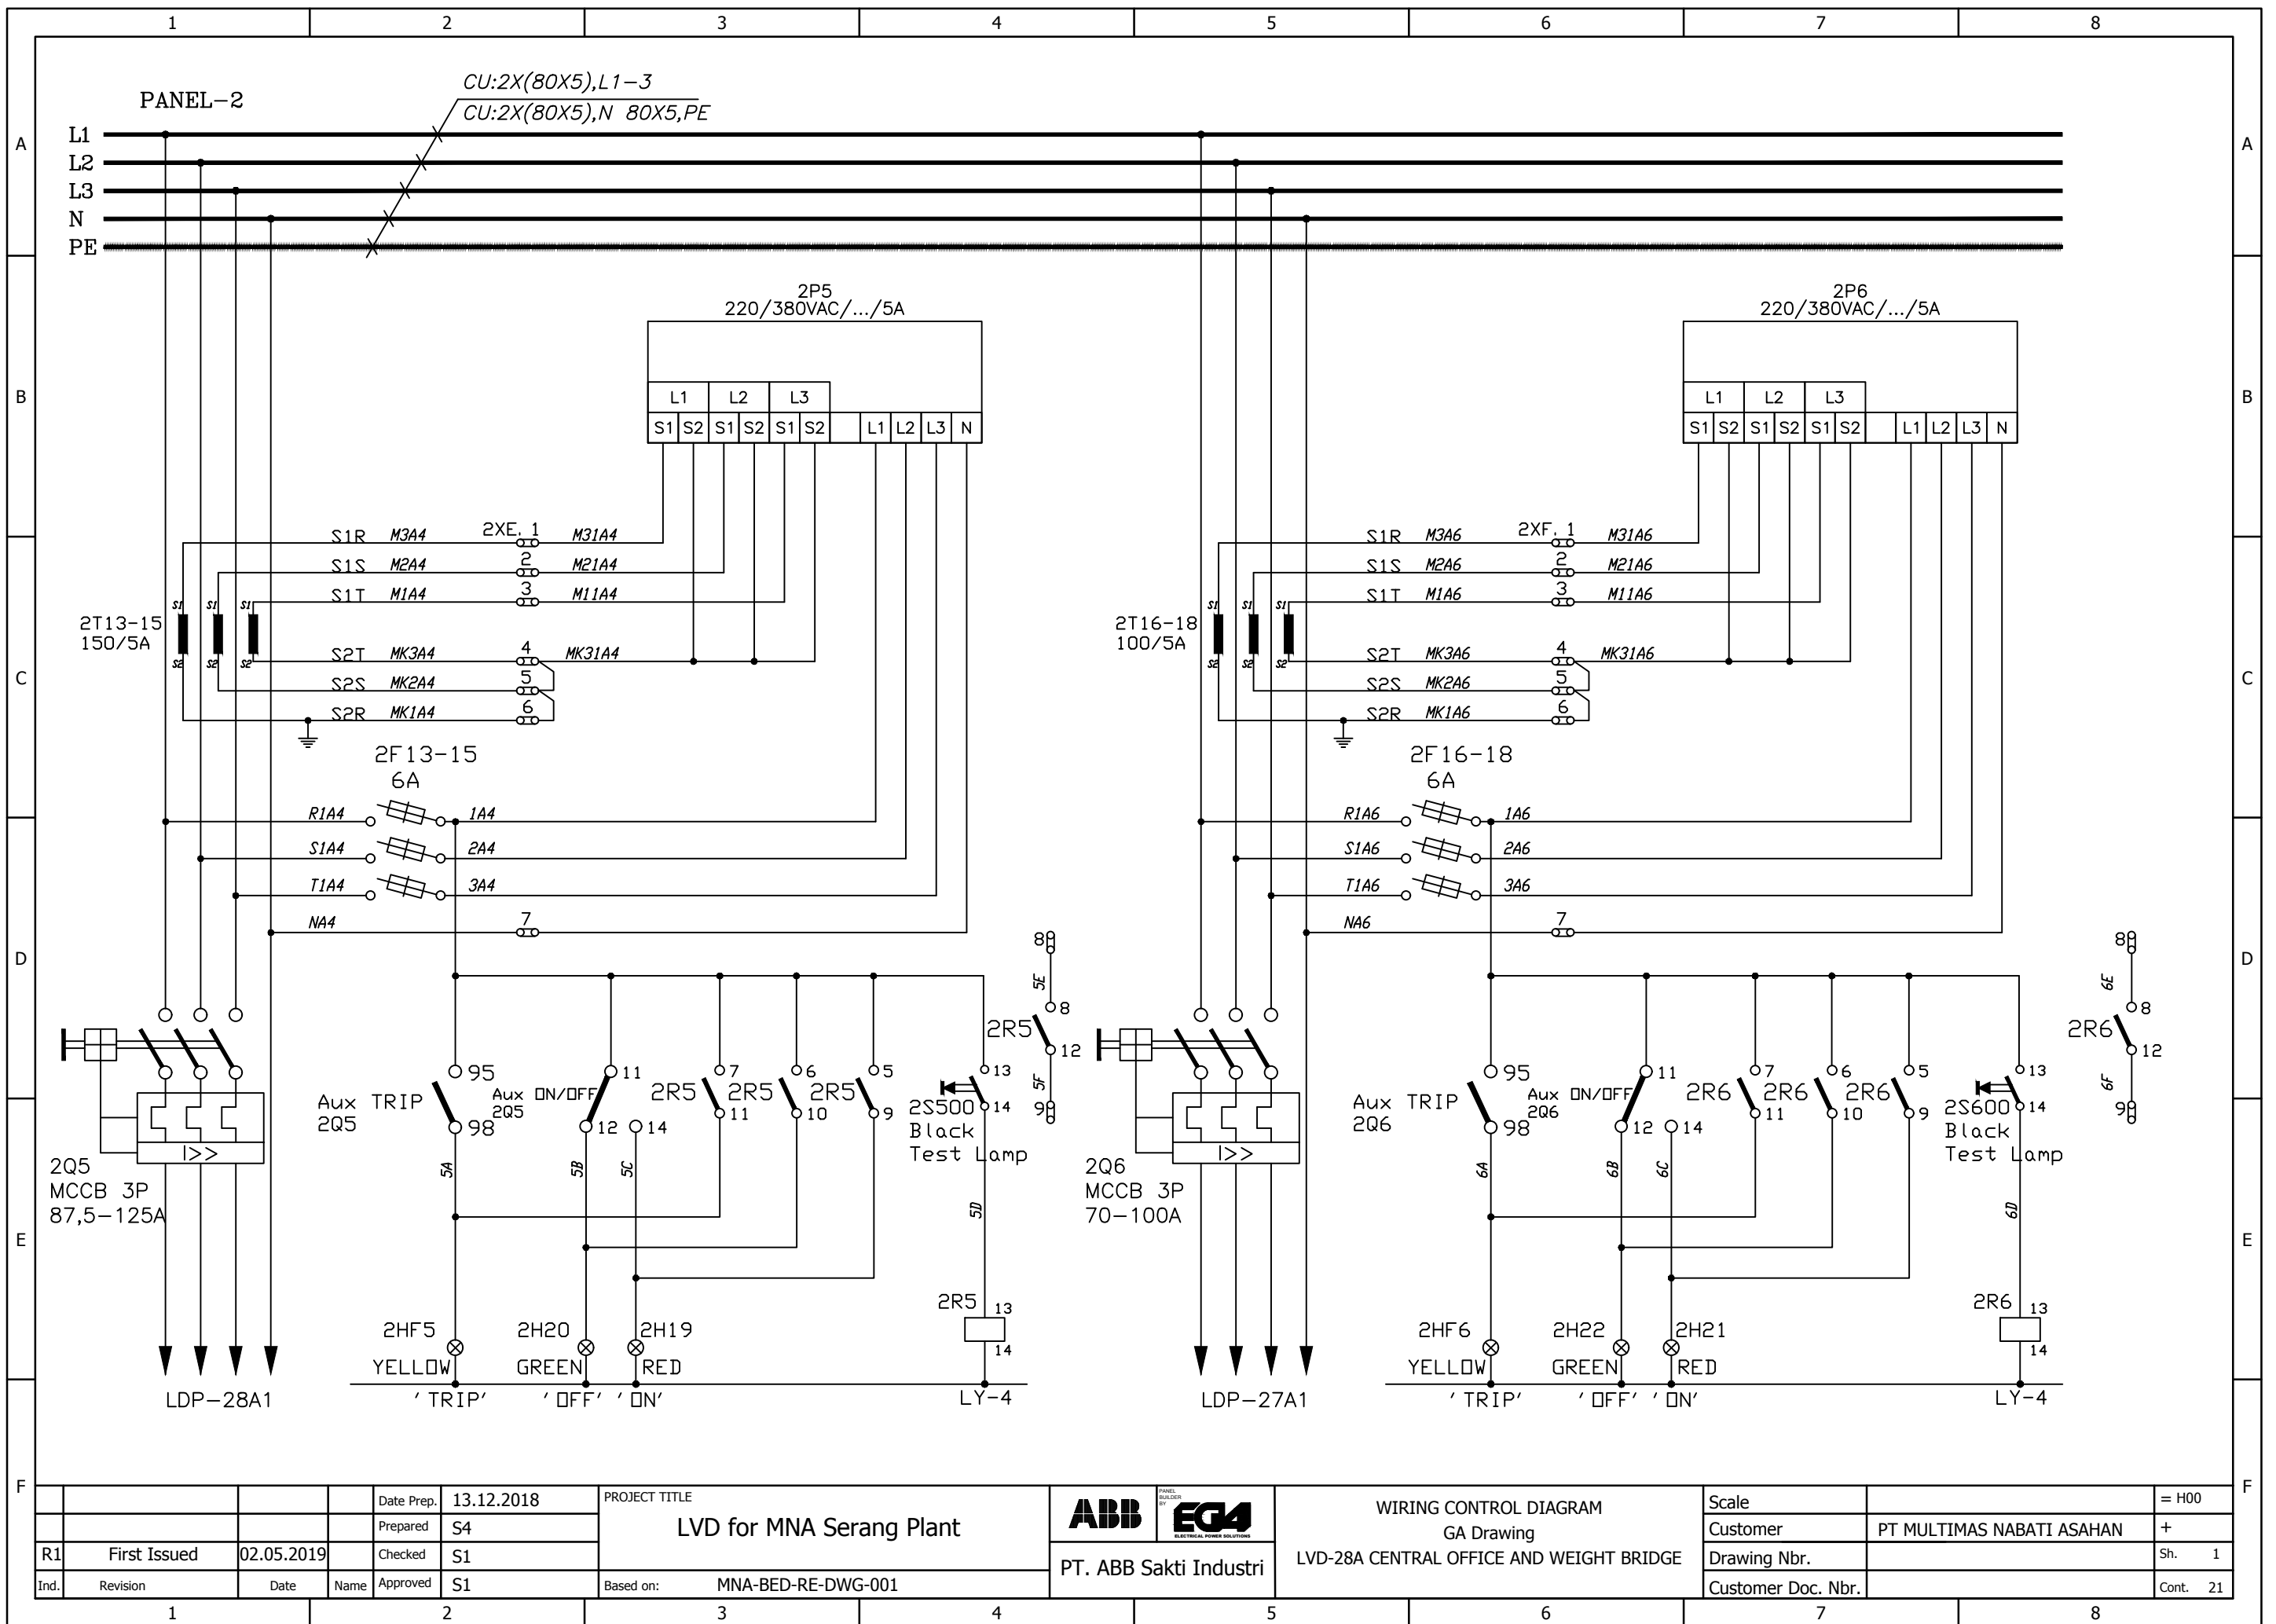

			Date Prep.	13.12.2018	PROJECT TITLE LVD for MNA Serang Plant	 	WIRING CONTROL DIAGRAM GA Drawing LVD-28A CENTRAL OFFICE AND WEIGHT BRIDGE	Scale		= H00
			Prepared	S4				Customer	PT MULTIMAS NABATI ASAHAN	+
R1	First Issued	02.05.2019	Checked	S1		PT. ABB Sakti Industri		Drawing Nbr.		Sh.
Ind.	Revision	Date	Name	Approved	S1	Based on: MNA-BED-RE-DWG-001		Customer Doc. Nbr.		Cont. 21

WE RESERVE ALL RIGHTS IN THIS DOCUMENT AND IN THE INFORMATION CONTAINED THEREIN. REPRODUCTION, USE OR DISCLOSURE TO THIRD PARTIES WITHOUT EXPRESS AUTHORITY IS STRICTLY FORBIDDEN.

1		2		3		4		5		6		7		8			
A	N O	DESCRIPTION				TECHNICAL DATA				QTY	DESIGNATION					A	
		INCOMING															
B	1	Fuse Carrier 6A				AXLE/Setara				7	1F11,1F1-6					B	
	2	Pilot Lamp (LED) 220Vac/50Hz, Red				Ega				2	1H1,12						
	3	Pilot Lamp (LED) 220Vac/50Hz, Yellow				Ega				2	1H2,HF1						
	4	Pilot Lamp (LED) 220Vac/50Hz, Green				Ega				2	1H3,H11						
	5	DIGITAL POWER METER (*)				ABB, M2M ETHERNET				1	1P1						
	6	CT 1500/5A CL.0.5 20VA				Howig, HG 82-1500				4	1T1-4						
	7	ACB 3P 1250A, 50KA, DO, Ekip Touch LSIG (*)				ABB, E1.2C12 D/O				1	1Q0						
	8	+ Shunt Trip Release (Y0) (*)				ABB, Y0				1	-						
	9	+ Motor (M) + Closing Release (YC) For E1.2 (*)				ABB, M+YC				1	-						
	10	+ Padlocks For E1.2 (*)				ABB,				1	-						
C	11	+ Ekip Com Protocol IEC 61850 (*)				ABB,				1	-					C	
	12	Push Button On, 1NO, Green				Ega				1	1S11						
	13	Push Button Off, 1NO, Red				Ega				1	1S12						
	14	Control Relay 220Vac				Omron, LY-2				1	1RF1						
	15	Control Relay 220Vac				Omron, LY-4				2	1R1-2						
	16	Push Button On/Test Lamp , 1NO, Black				Ega				1	1S100						
D	17	OUTGOING														D	
	18	Fuse Carrier 6A				AXLE				18	F1-18						
	19	DIGITAL POWER METER (*)				ABB, M2M ETHERNET				6	2P1-6						
	20	Pilot Lamp (LED) 220Vac/50Hz, Red				AXLE/Setara				6	2H11,13,15,17,19,21						
	21	Pilot Lamp (LED) 220Vac/50Hz, Yellow				AXLE/Setara				6	2HF1-6						
	22	Pilot Lamp (LED) 220Vac/50Hz, Green				AXLE/Setara				6	2H12,14,16,18,20,22						
	23	CT 400/5A CL.1 5VA				Howig, HG 40I-400				9	2T1-9						
	24	CT 200/5A CL.1 5VA				Howig, HG 30I-200				3	2T10-12						
	25	CT 150/5A CL.1 2.5VA				Howig, HG 30I-150				3	2T13-15						
	26	CT 100/5A CL.1 2.5VA				Howig, HG 30I-100				3	2T16-18						
E																E	
F																F	
				Date Prep.	13.12.2018	PROJECT TITLE LVD for MNA Serang Plant				  PT. ABB Sakti Industri		COMPONENT LIST GA Drawing LVD-28A CENTRAL OFFICE AND WEIGHT BRIDGE		Scale		= H00	
				Prepared	S4									Customer	PT MULTIMAS NABATI ASAHAN		+
R1	First Issued	02.05.2019		Checked	S1									Drawing Nbr.			Sh.
Ind.	Revision	Date	Name	Approved	S1	Based on: MNA-BED-RE-DWG-001						Customer Doc. Nbr.			Cont.	21	
1		2		3		4		5		6		7		8			

