



WE RESERVE ALL RIGHTS IN THIS DOCUMENT AND IN THE INFORMATION CONTAINED THEREIN. REPRODUCTION, USE OR DISCLOSURE TO THIRD PARTIES WITHOUT EXPRESS AUTHORITY IS STRICTLY FORBIDDEN.

WE RESERVE ALL RIGHTS IN THIS DOCUMENT AND IN THE INFORMATION CONTAINED THEREIN. REPRODUCTION, USE OR DISCLOSURE TO THIRD PARTIES WITHOUT EXPRESS AUTHORITY IS STRICTLY FORBIDDEN.

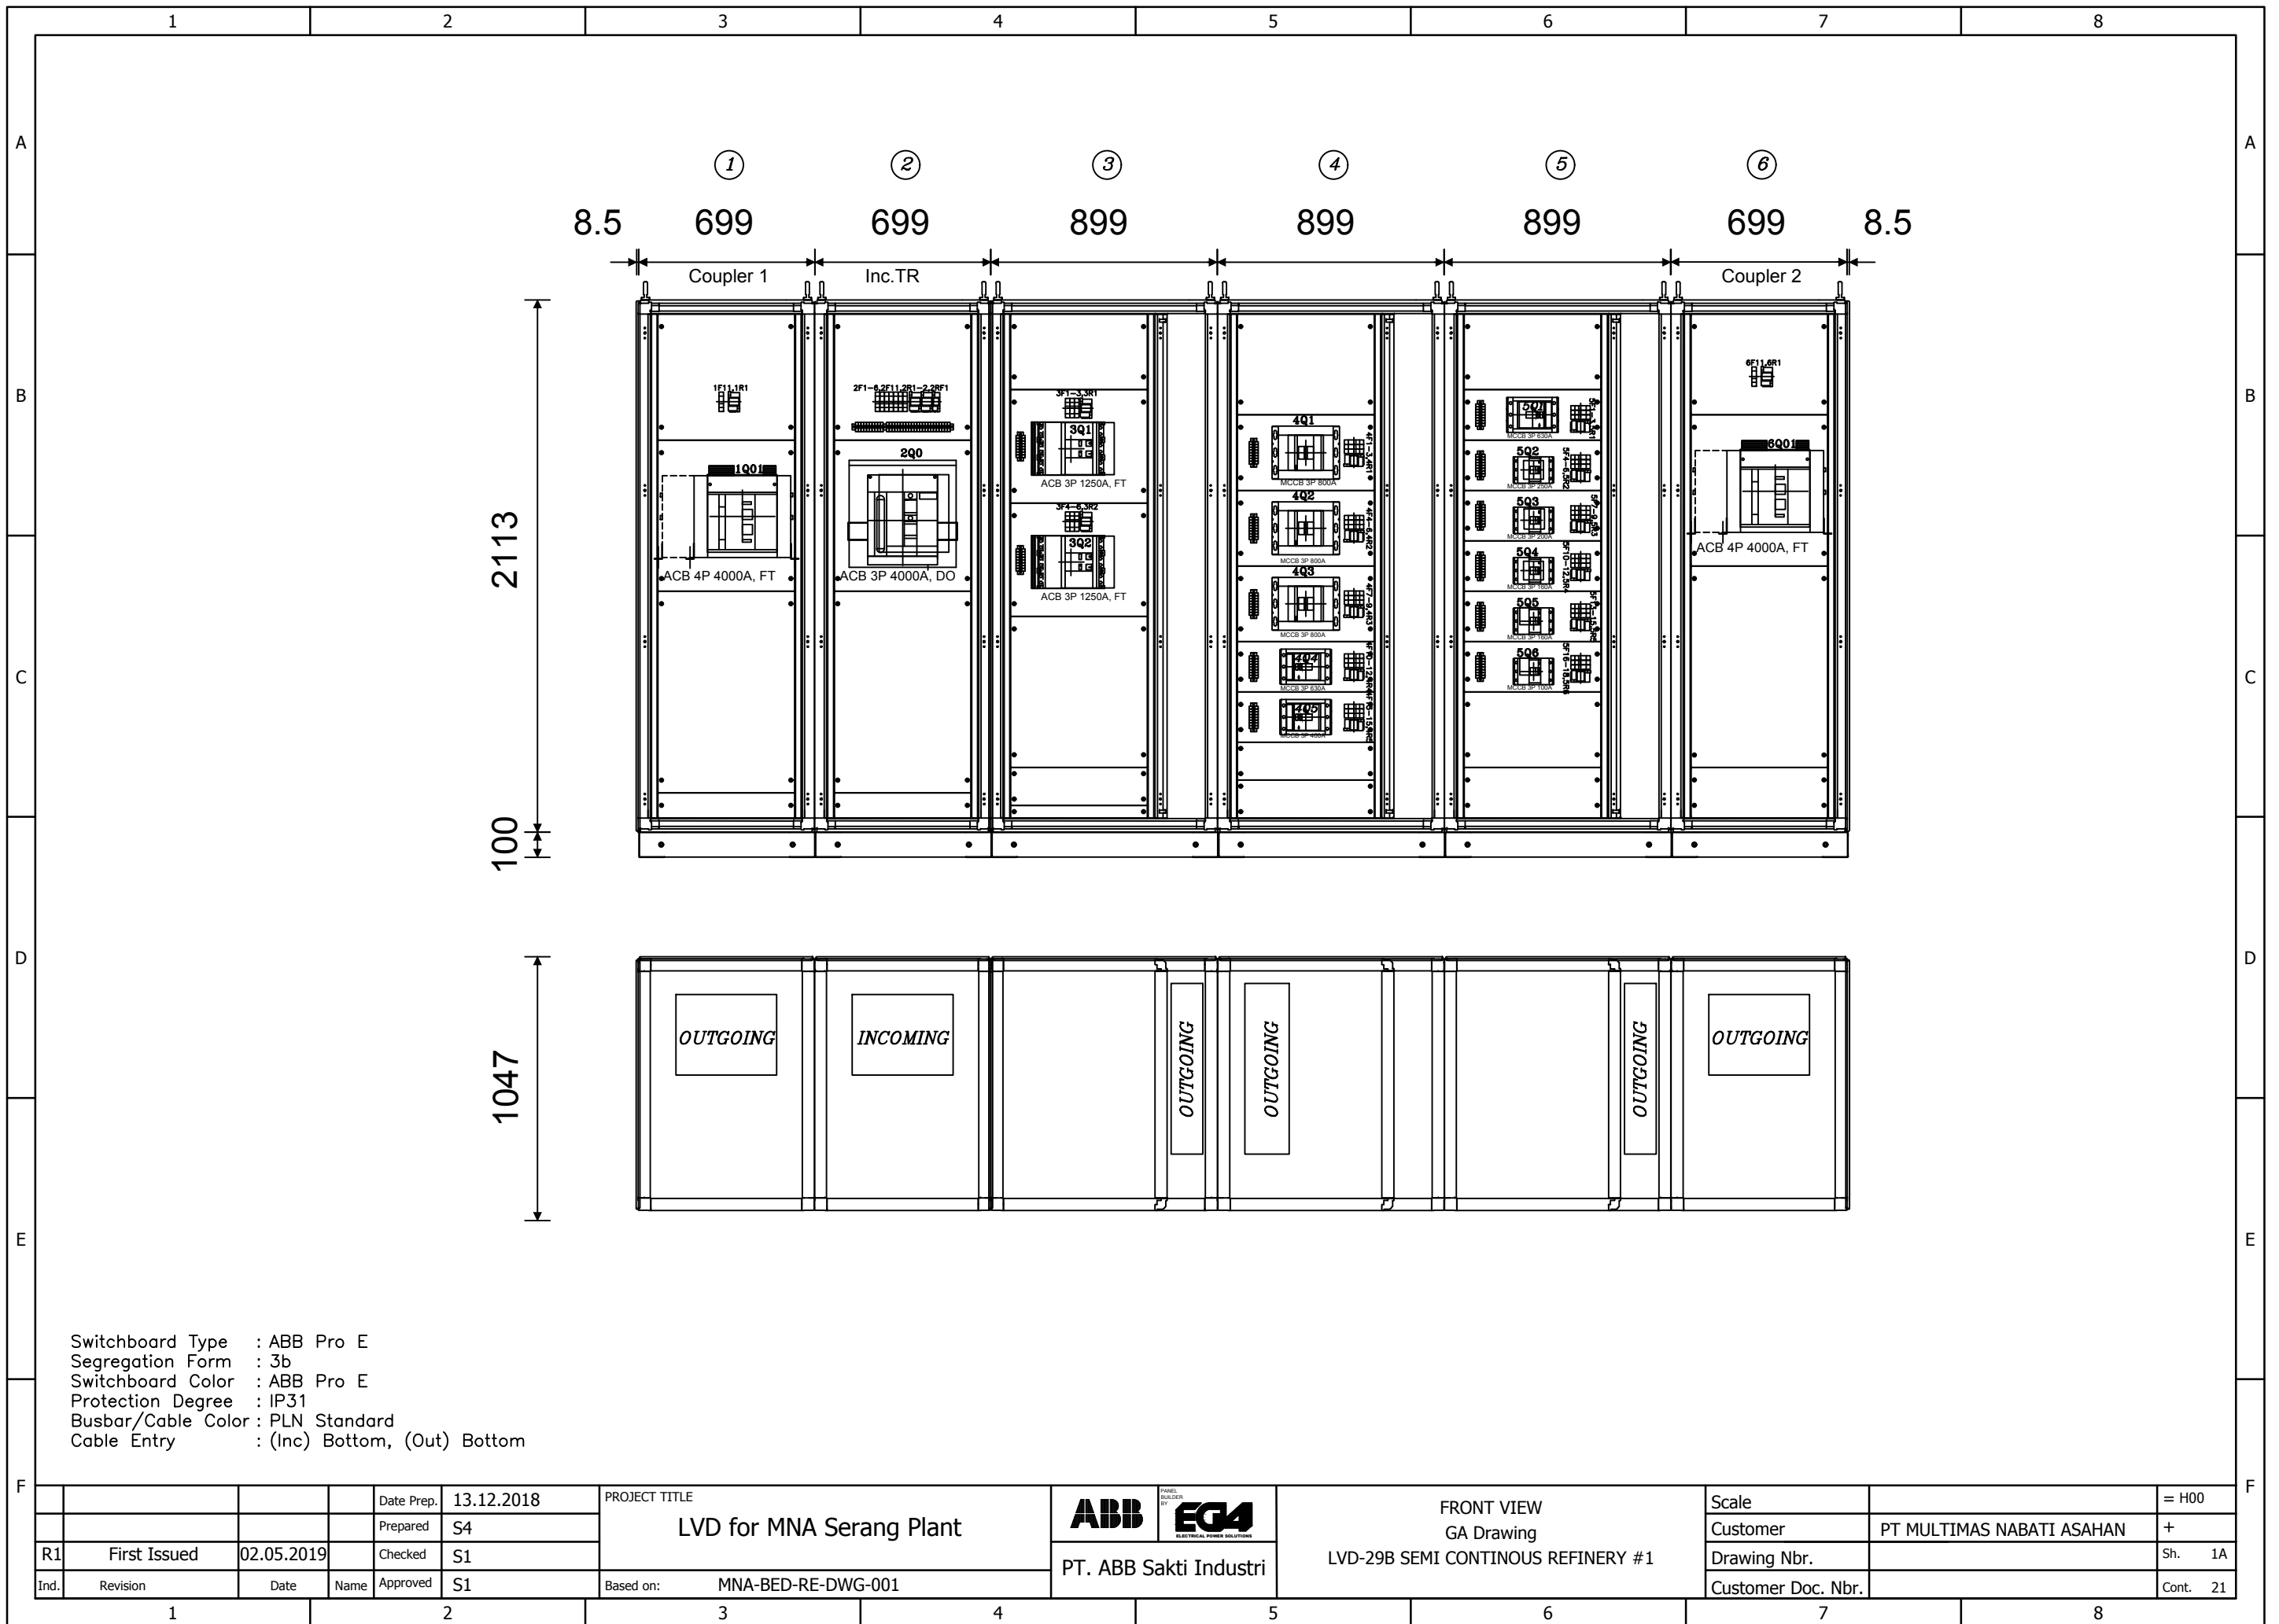


WE RESERVE ALL RIGHTS IN THIS DOCUMENT AND IN THE INFORMATION CONTAINED THEREIN. REPRODUCTION, USE OR DISCLOSURE TO THIRD PARTIES WITHOUT EXPRESS AUTHORITY IS STRICTLY FORBIDDEN.

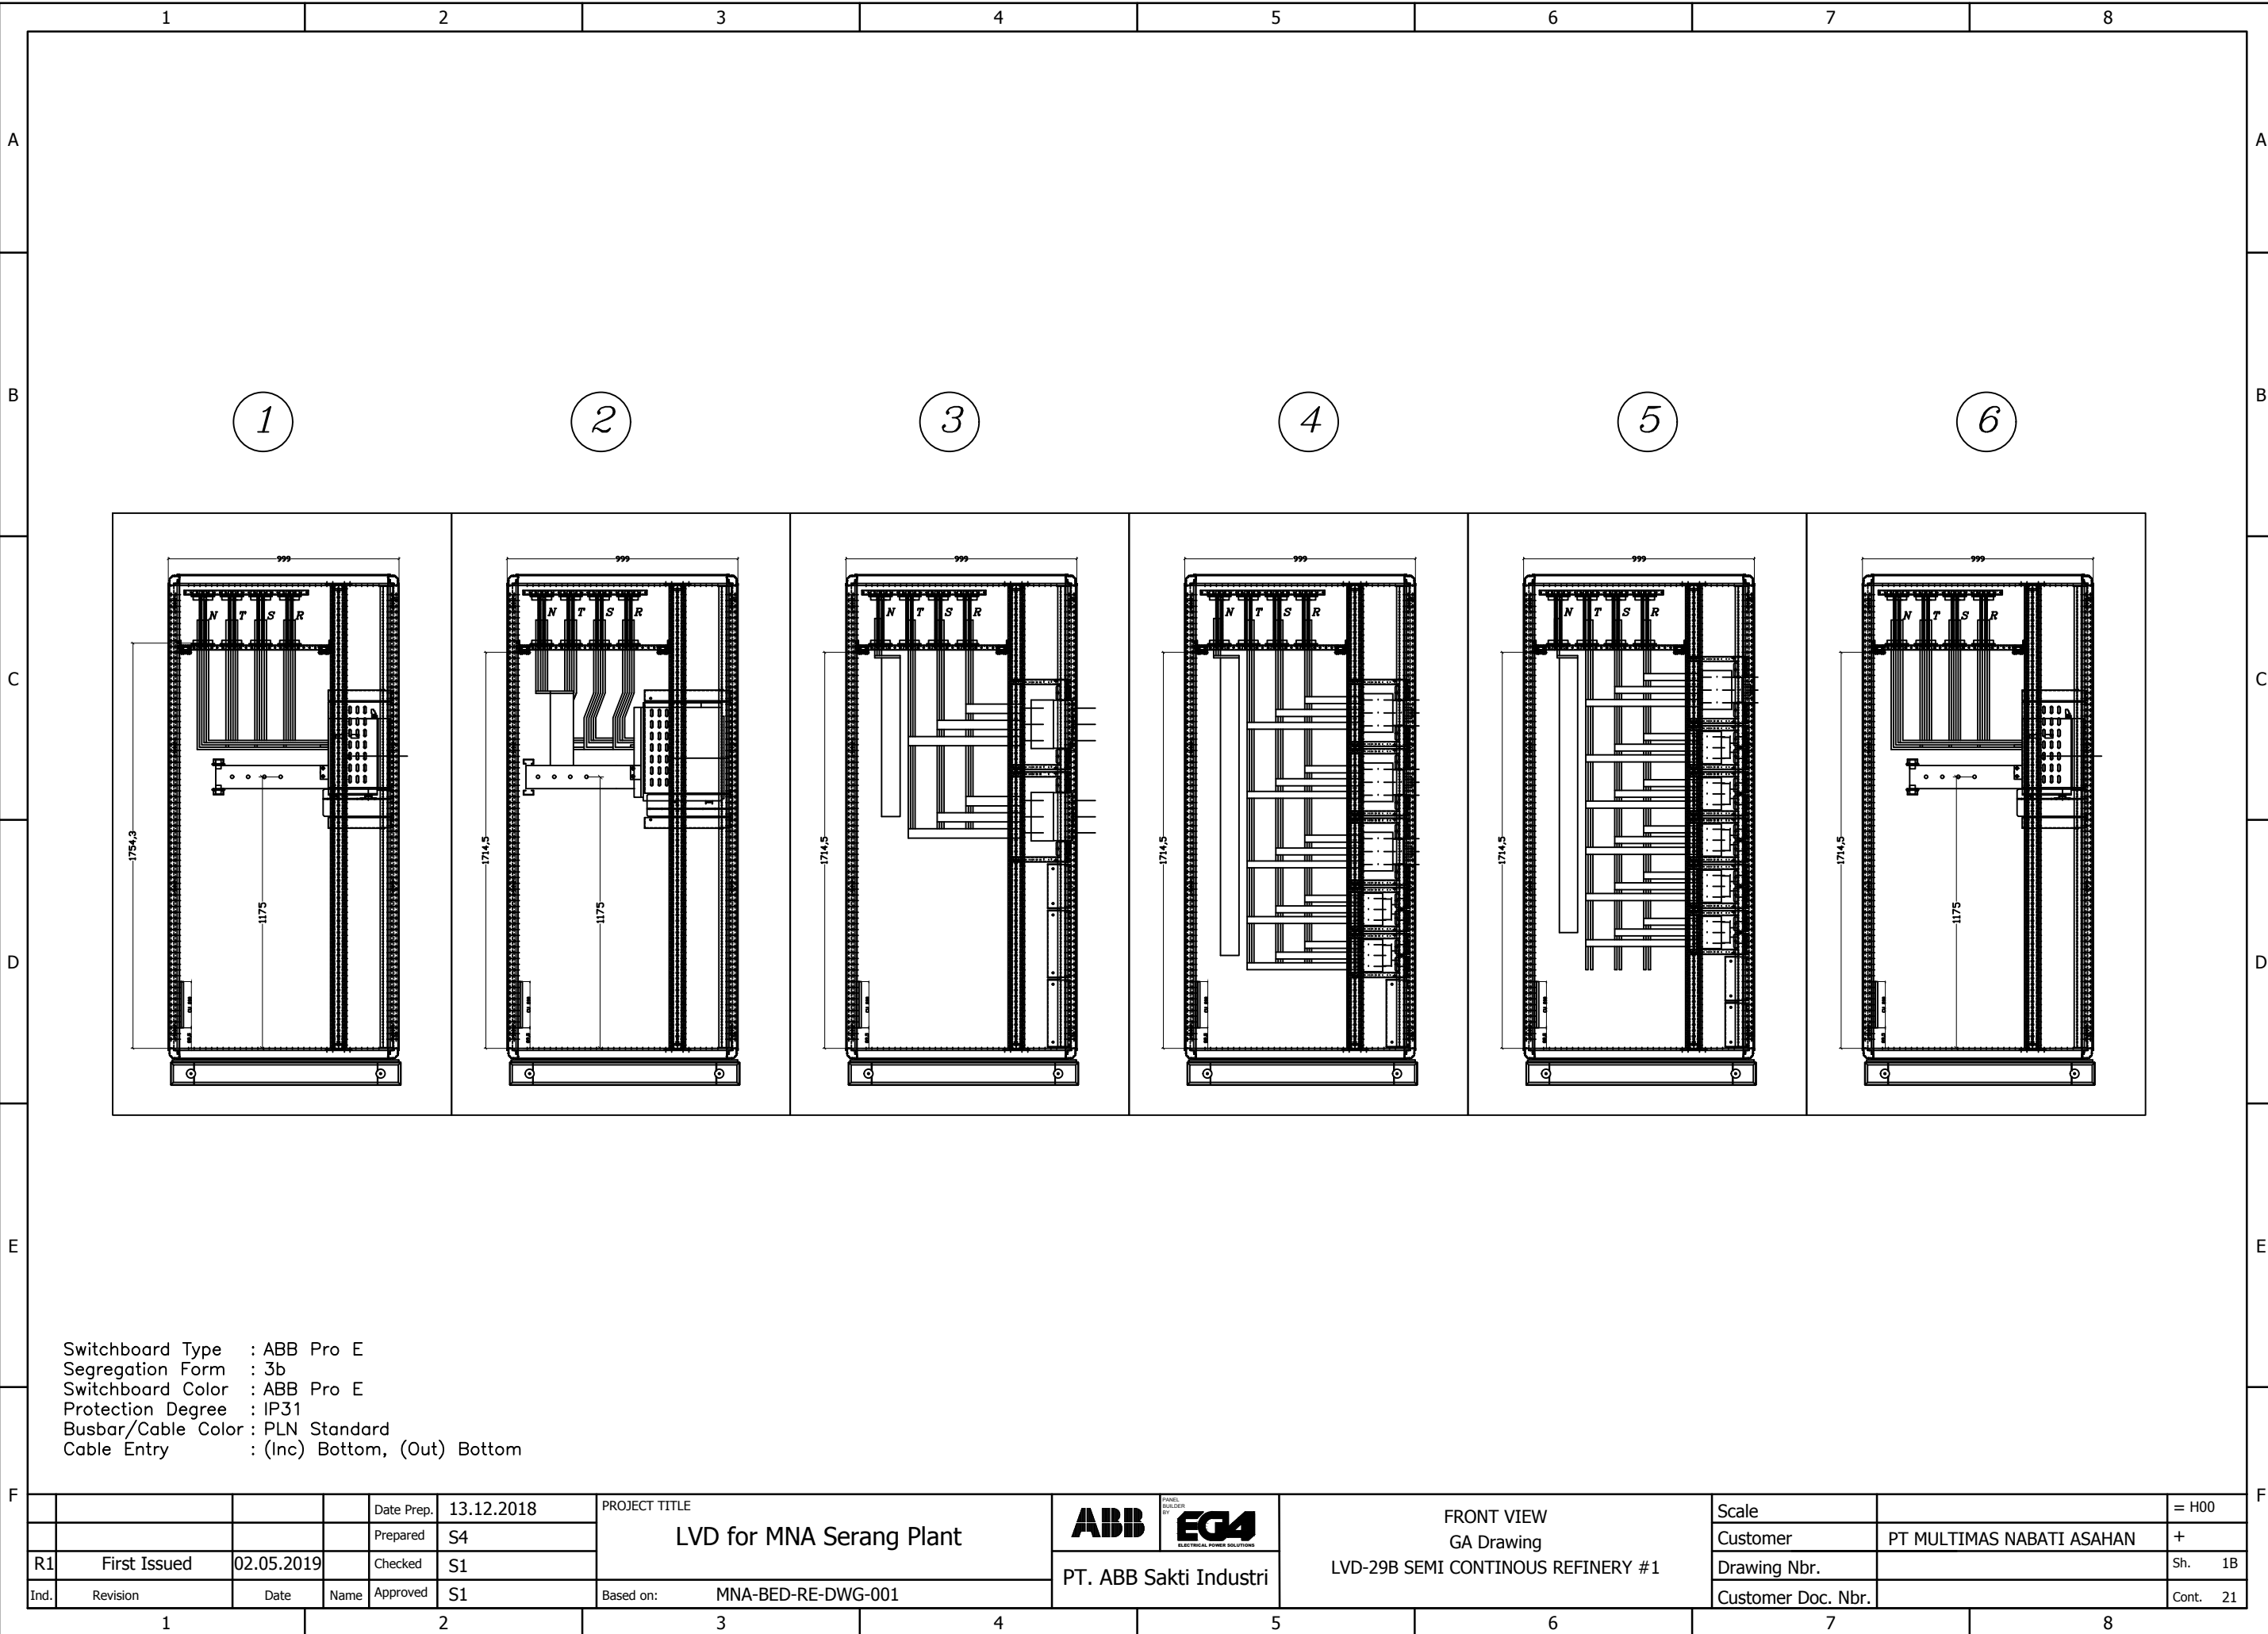


WE RESERVE ALL RIGHTS IN THIS DOCUMENT AND IN THE INFORMATION CONTAINED THEREIN. REPRODUCTION, USE OR DISCLOSURE TO THIRD PARTIES WITHOUT EXPRESS AUTHORITY IS STRICTLY FORBIDDEN.

SIDE VIEW

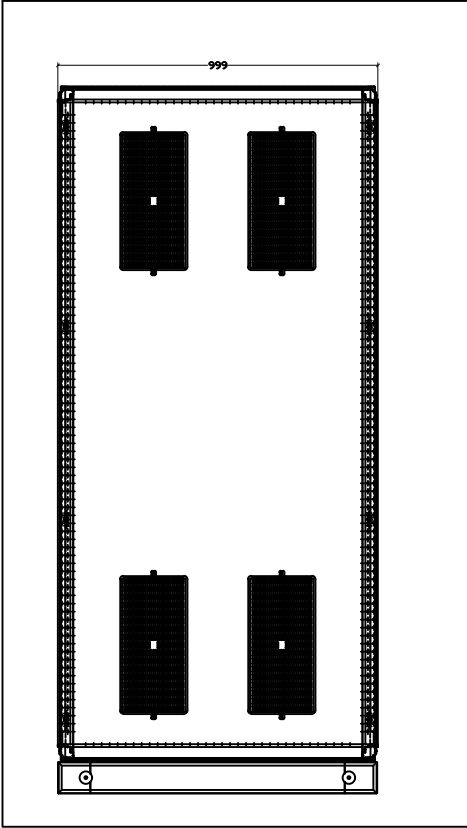


BACK VIEW

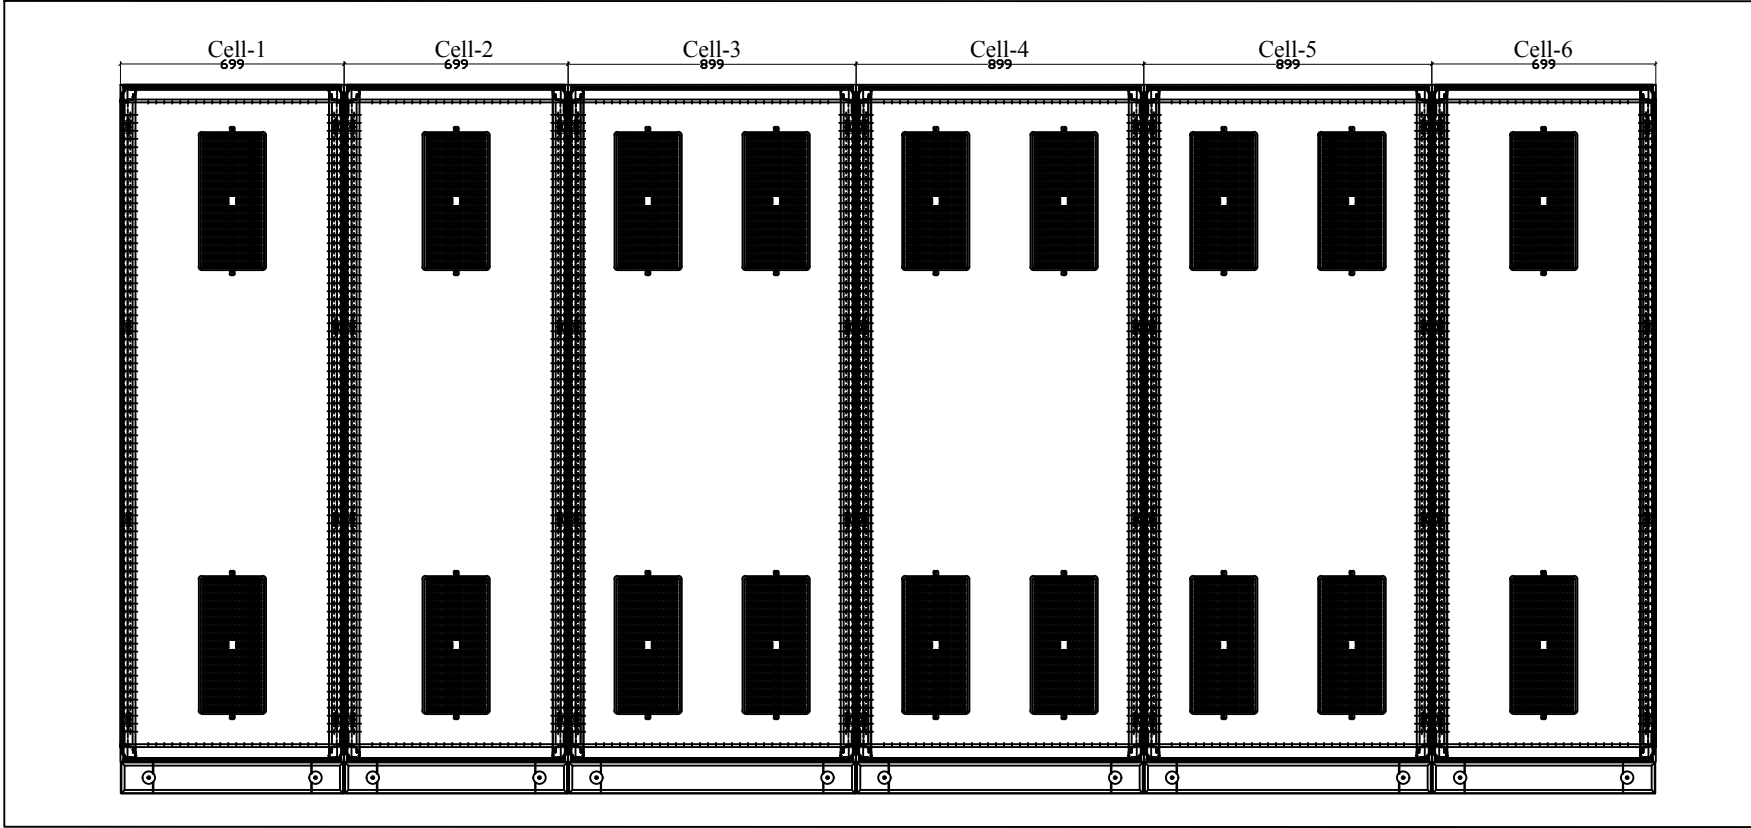

Switchboard Type : ABB Pro E
Segregation Form : 3b
Switchboard Color : ABB Pro E
Protection Degree : IP31
Busbar/Cable Color : PLN Standard
Cable Entry : (Inc) Bottom, (Out) Bottom


				Date Prep.	13.12.2018	PROJECT TITLE LVD for MNA Serang Plant	ABB PANEL BUILDING BY EG4 ELECTRICAL POWER SOLUTIONS PT. ABB Sakti Industri	FRONT VIEW GA Drawing LVD-29B SEMI CONTINOUS REFINERY #1	Scale		= H00
				Prepared	S4				Customer	PT MULTIMAS NABATI ASAHAN	+
R1	First Issued	02.05.2019		Checked	S1				Drawing Nbr.		Sh. 1C
Ind.	Revision	Date	Name	Approved	S1	Based on:	MNA-BED-RE-DWG-001		Customer Doc. Nbr.		Cont. 21

WE RESERVE ALL RIGHTS IN THIS DOCUMENT AND IN THE INFORMATION CONTAINED THEREIN. REPRODUCTION, USE OR DISCLOSURE TO THIRD PARTIES WITHOUT EXPRESS AUTHORITY IS STRICTLY FORBIDDEN.

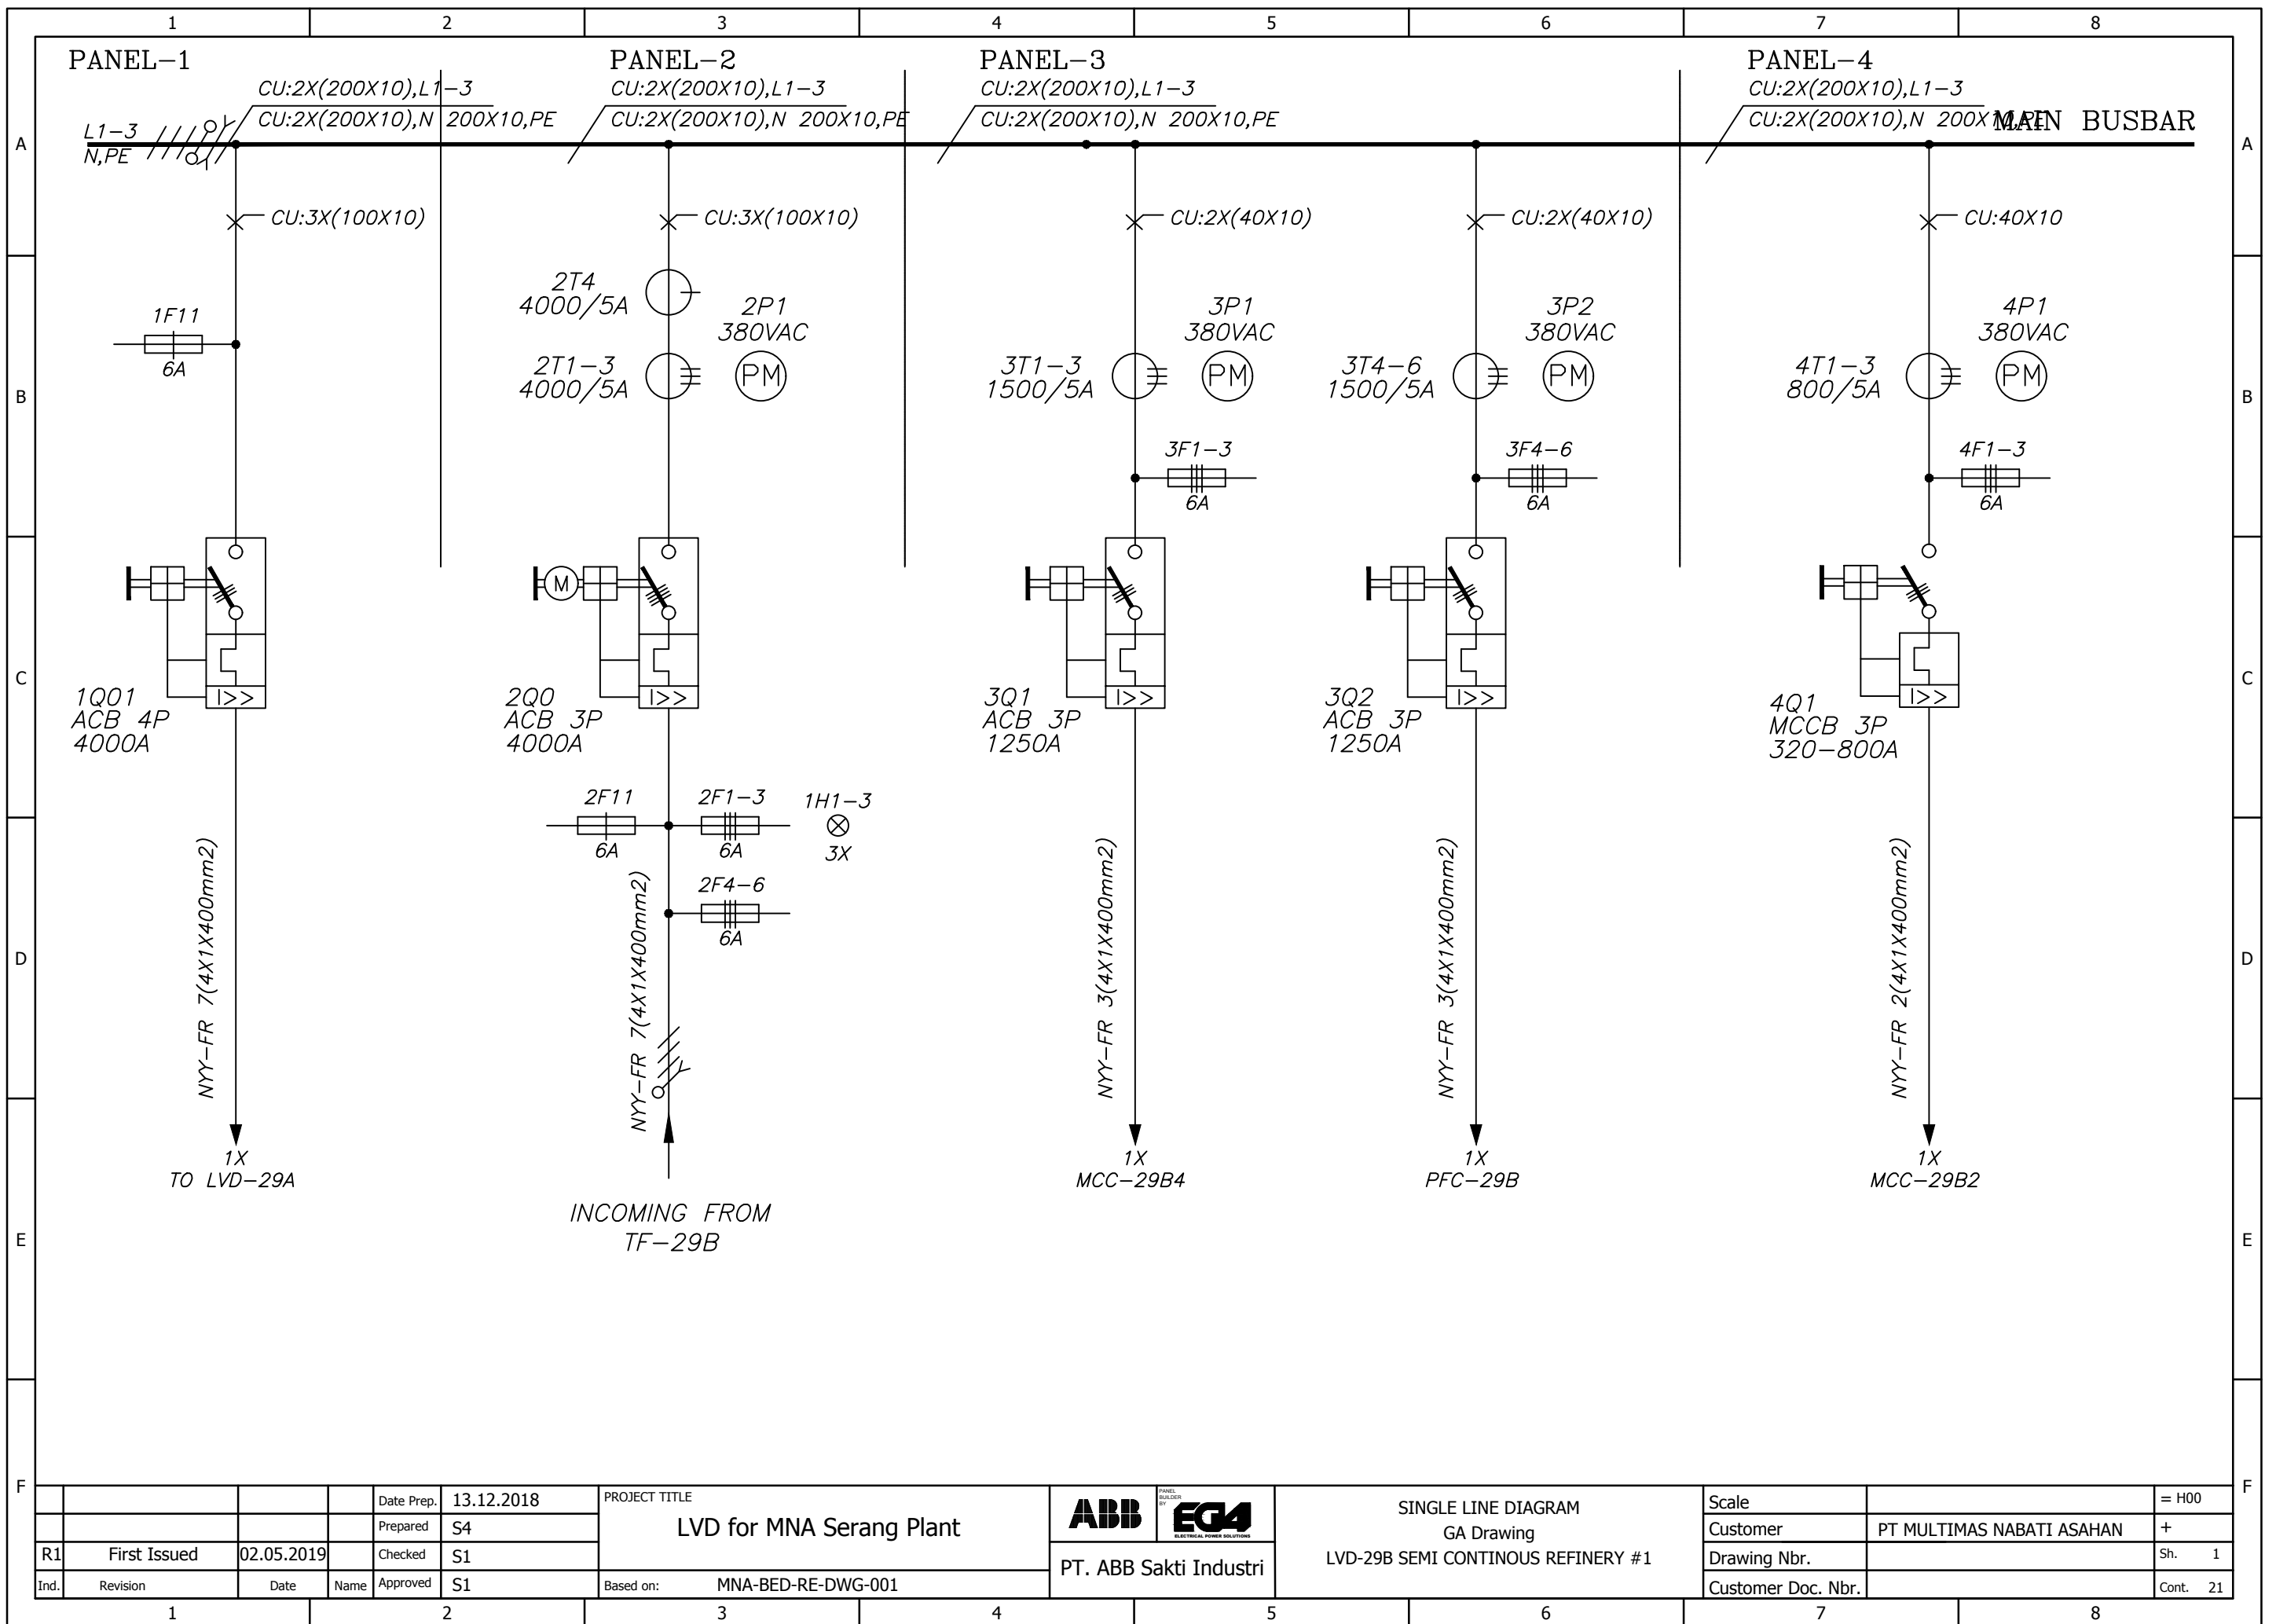


R1		First Issued	02.05.2019	Checked	S1	PROJECT TITLE LVD for MNA Serang Plant Based on: MNA-BED-RE-DWG-001	ABB PANEL BUILDING BY EG4 ELECTRICAL POWER SOLUTIONS PT. ABB Sakti Industri	SINGLE LINE DIAGRAM GA Drawing LVD-29B SEMI CONTINUOUS REFINERY #1	Scale	= H00
Ind.		Revision	Date	Name	Approved				Customer	PT MULTIMAS NABATI ASAHAN
									Drawing Nbr.	Sh. 1
									Customer Doc. Nbr.	Cont. 21

WE RESERVE ALL RIGHTS IN THIS DOCUMENT AND IN THE INFORMATION CONTAINED THEREIN. REPRODUCTION, USE OR DISCLOSURE TO THIRD PARTIES WITHOUT EXPRESS AUTHORITY IS STRICTLY FORBIDDEN.

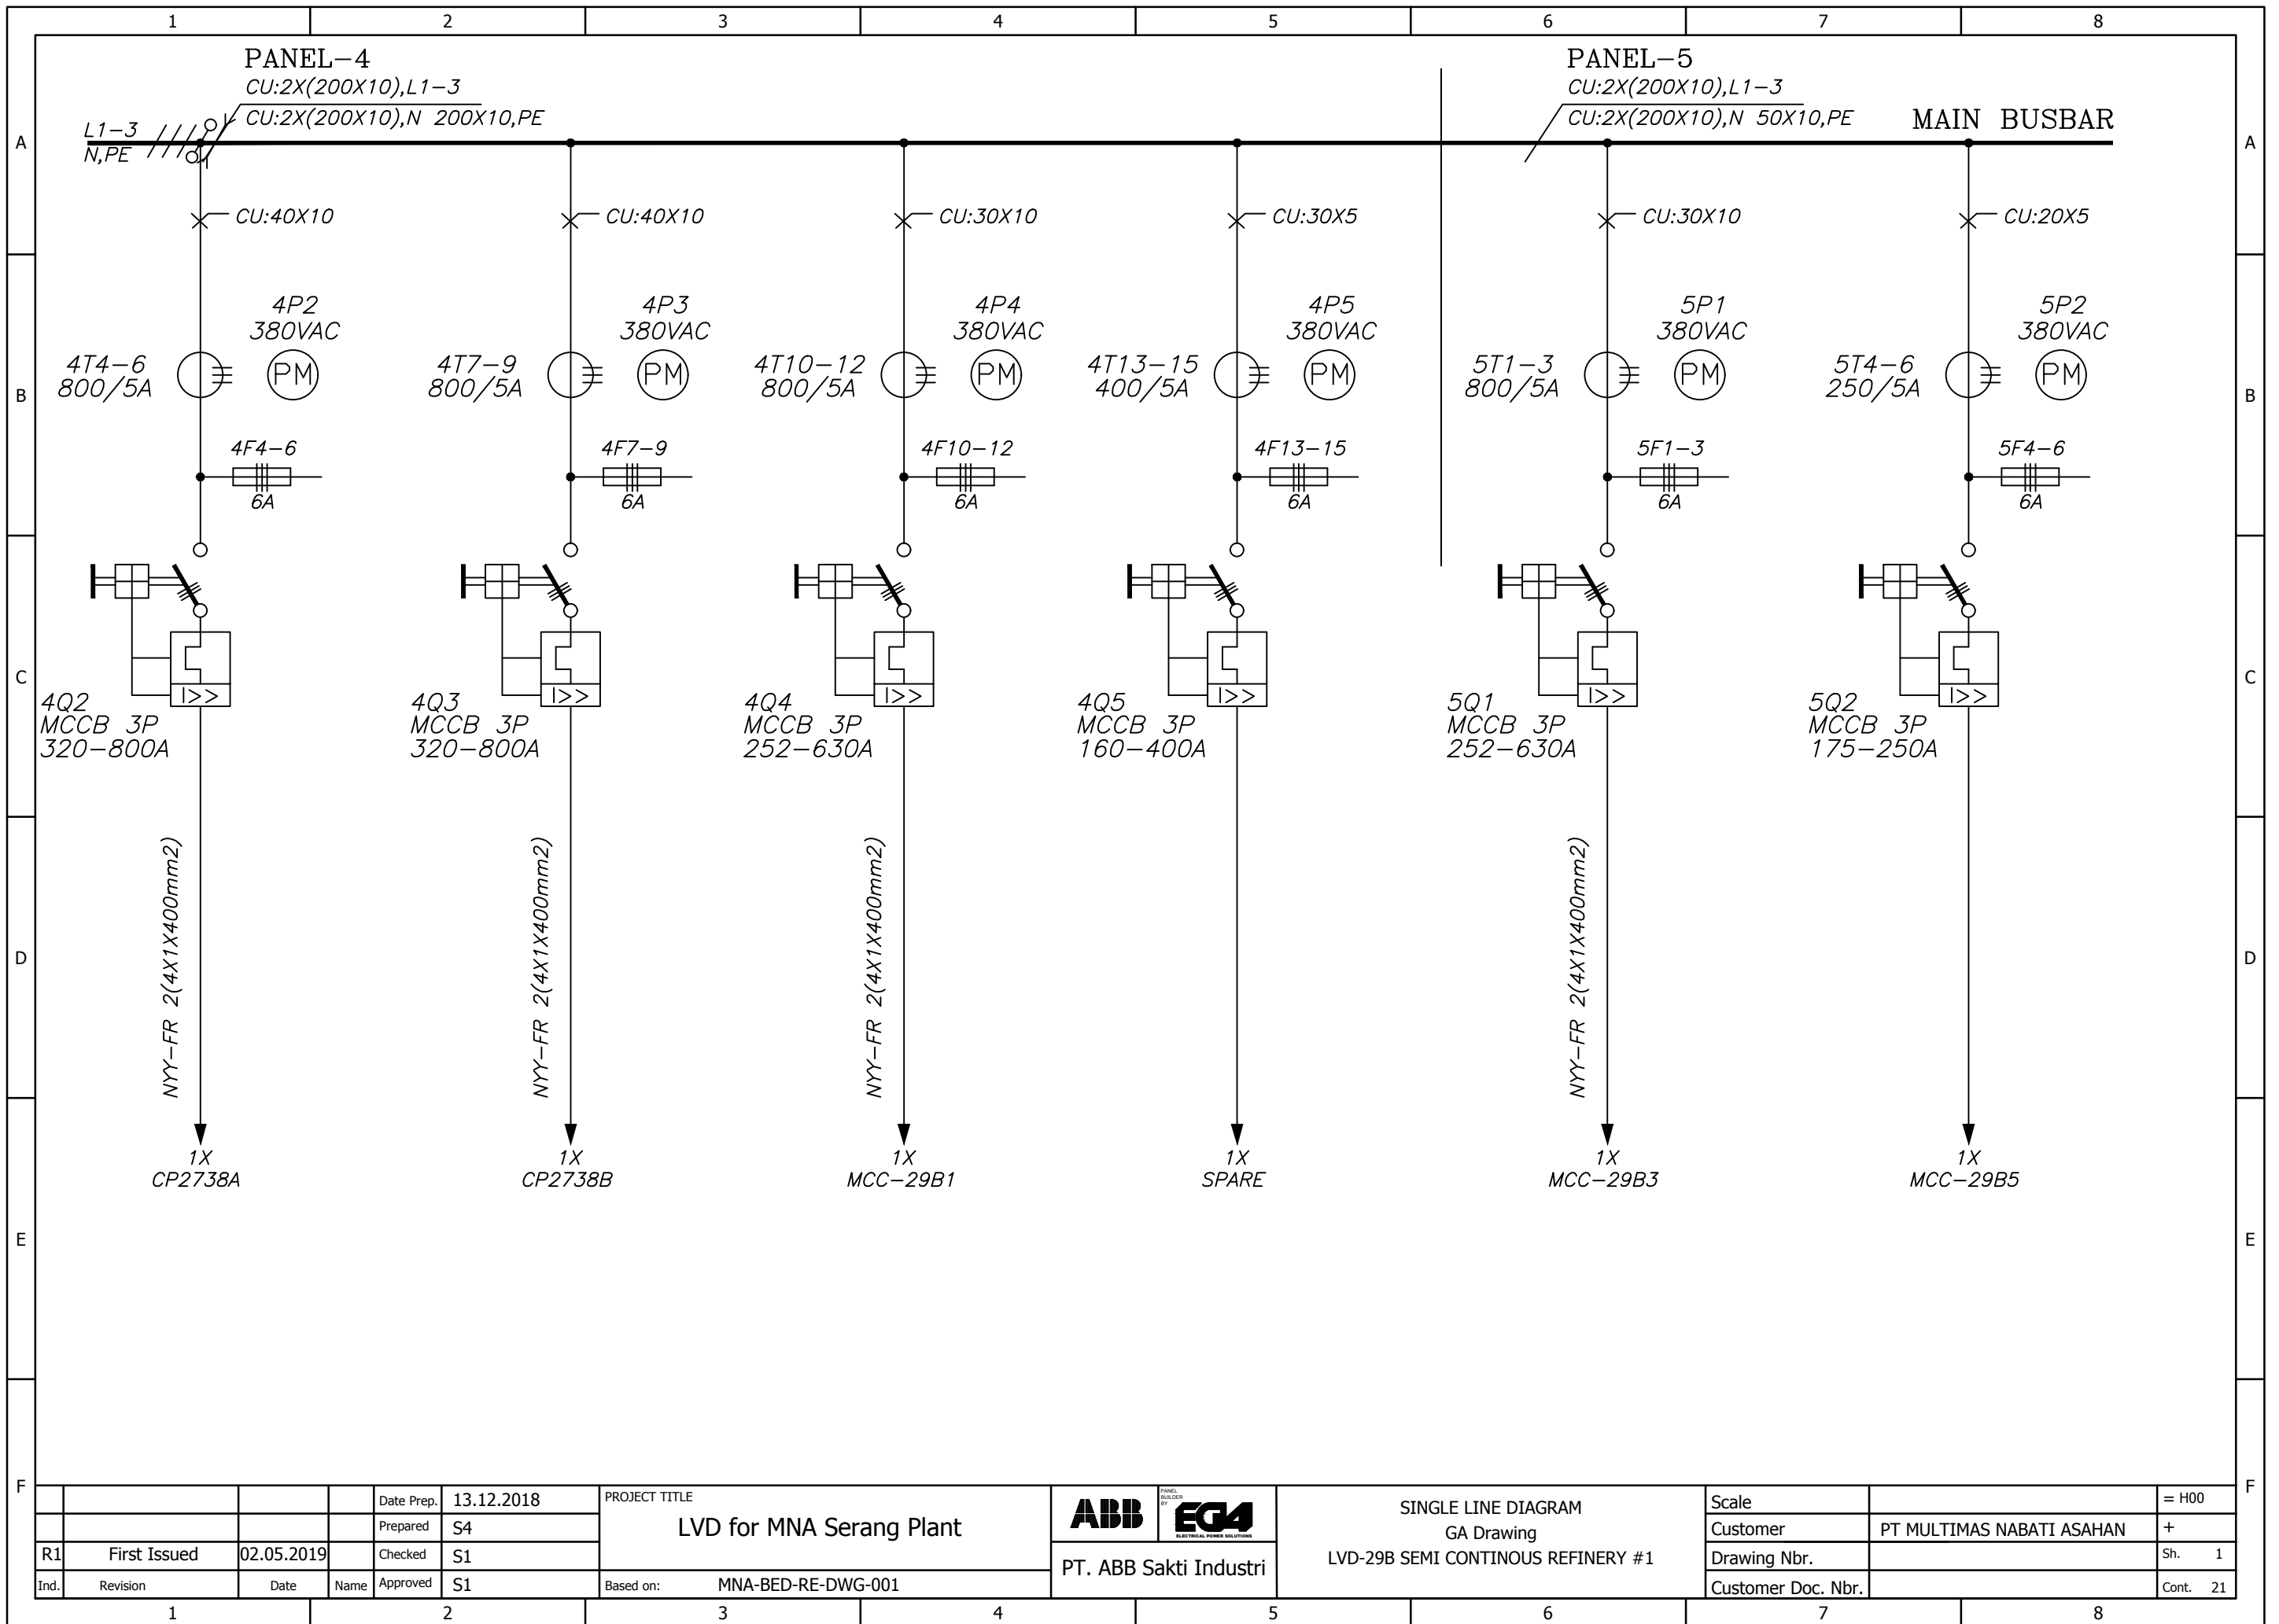






R1		First Issued	02.05.2019	Checked	S1	PROJECT TITLE LVD for MNA Serang Plant	  PT. ABB Sakti Industri	SINGLE LINE DIAGRAM GA Drawing LVD-29B SEMI CONTINOUS REFINERY #1	Scale	= H00
Ind.		Revision	Date	Name	Approved				Customer	PT MULTIMAS NABATI ASAHAN
									Drawing Nbr.	Sh. 1
						Based on:	MNA-BED-RE-DWG-001		Customer Doc. Nbr.	Cont. 21

WE RESERVE ALL RIGHTS IN THIS DOCUMENT AND IN THE INFORMATION CONTAINED THEREIN. REPRODUCTION, USE OR DISCLOSURE TO THIRD PARTIES WITHOUT EXPRESS AUTHORITY IS STRICTLY FORBIDDEN.





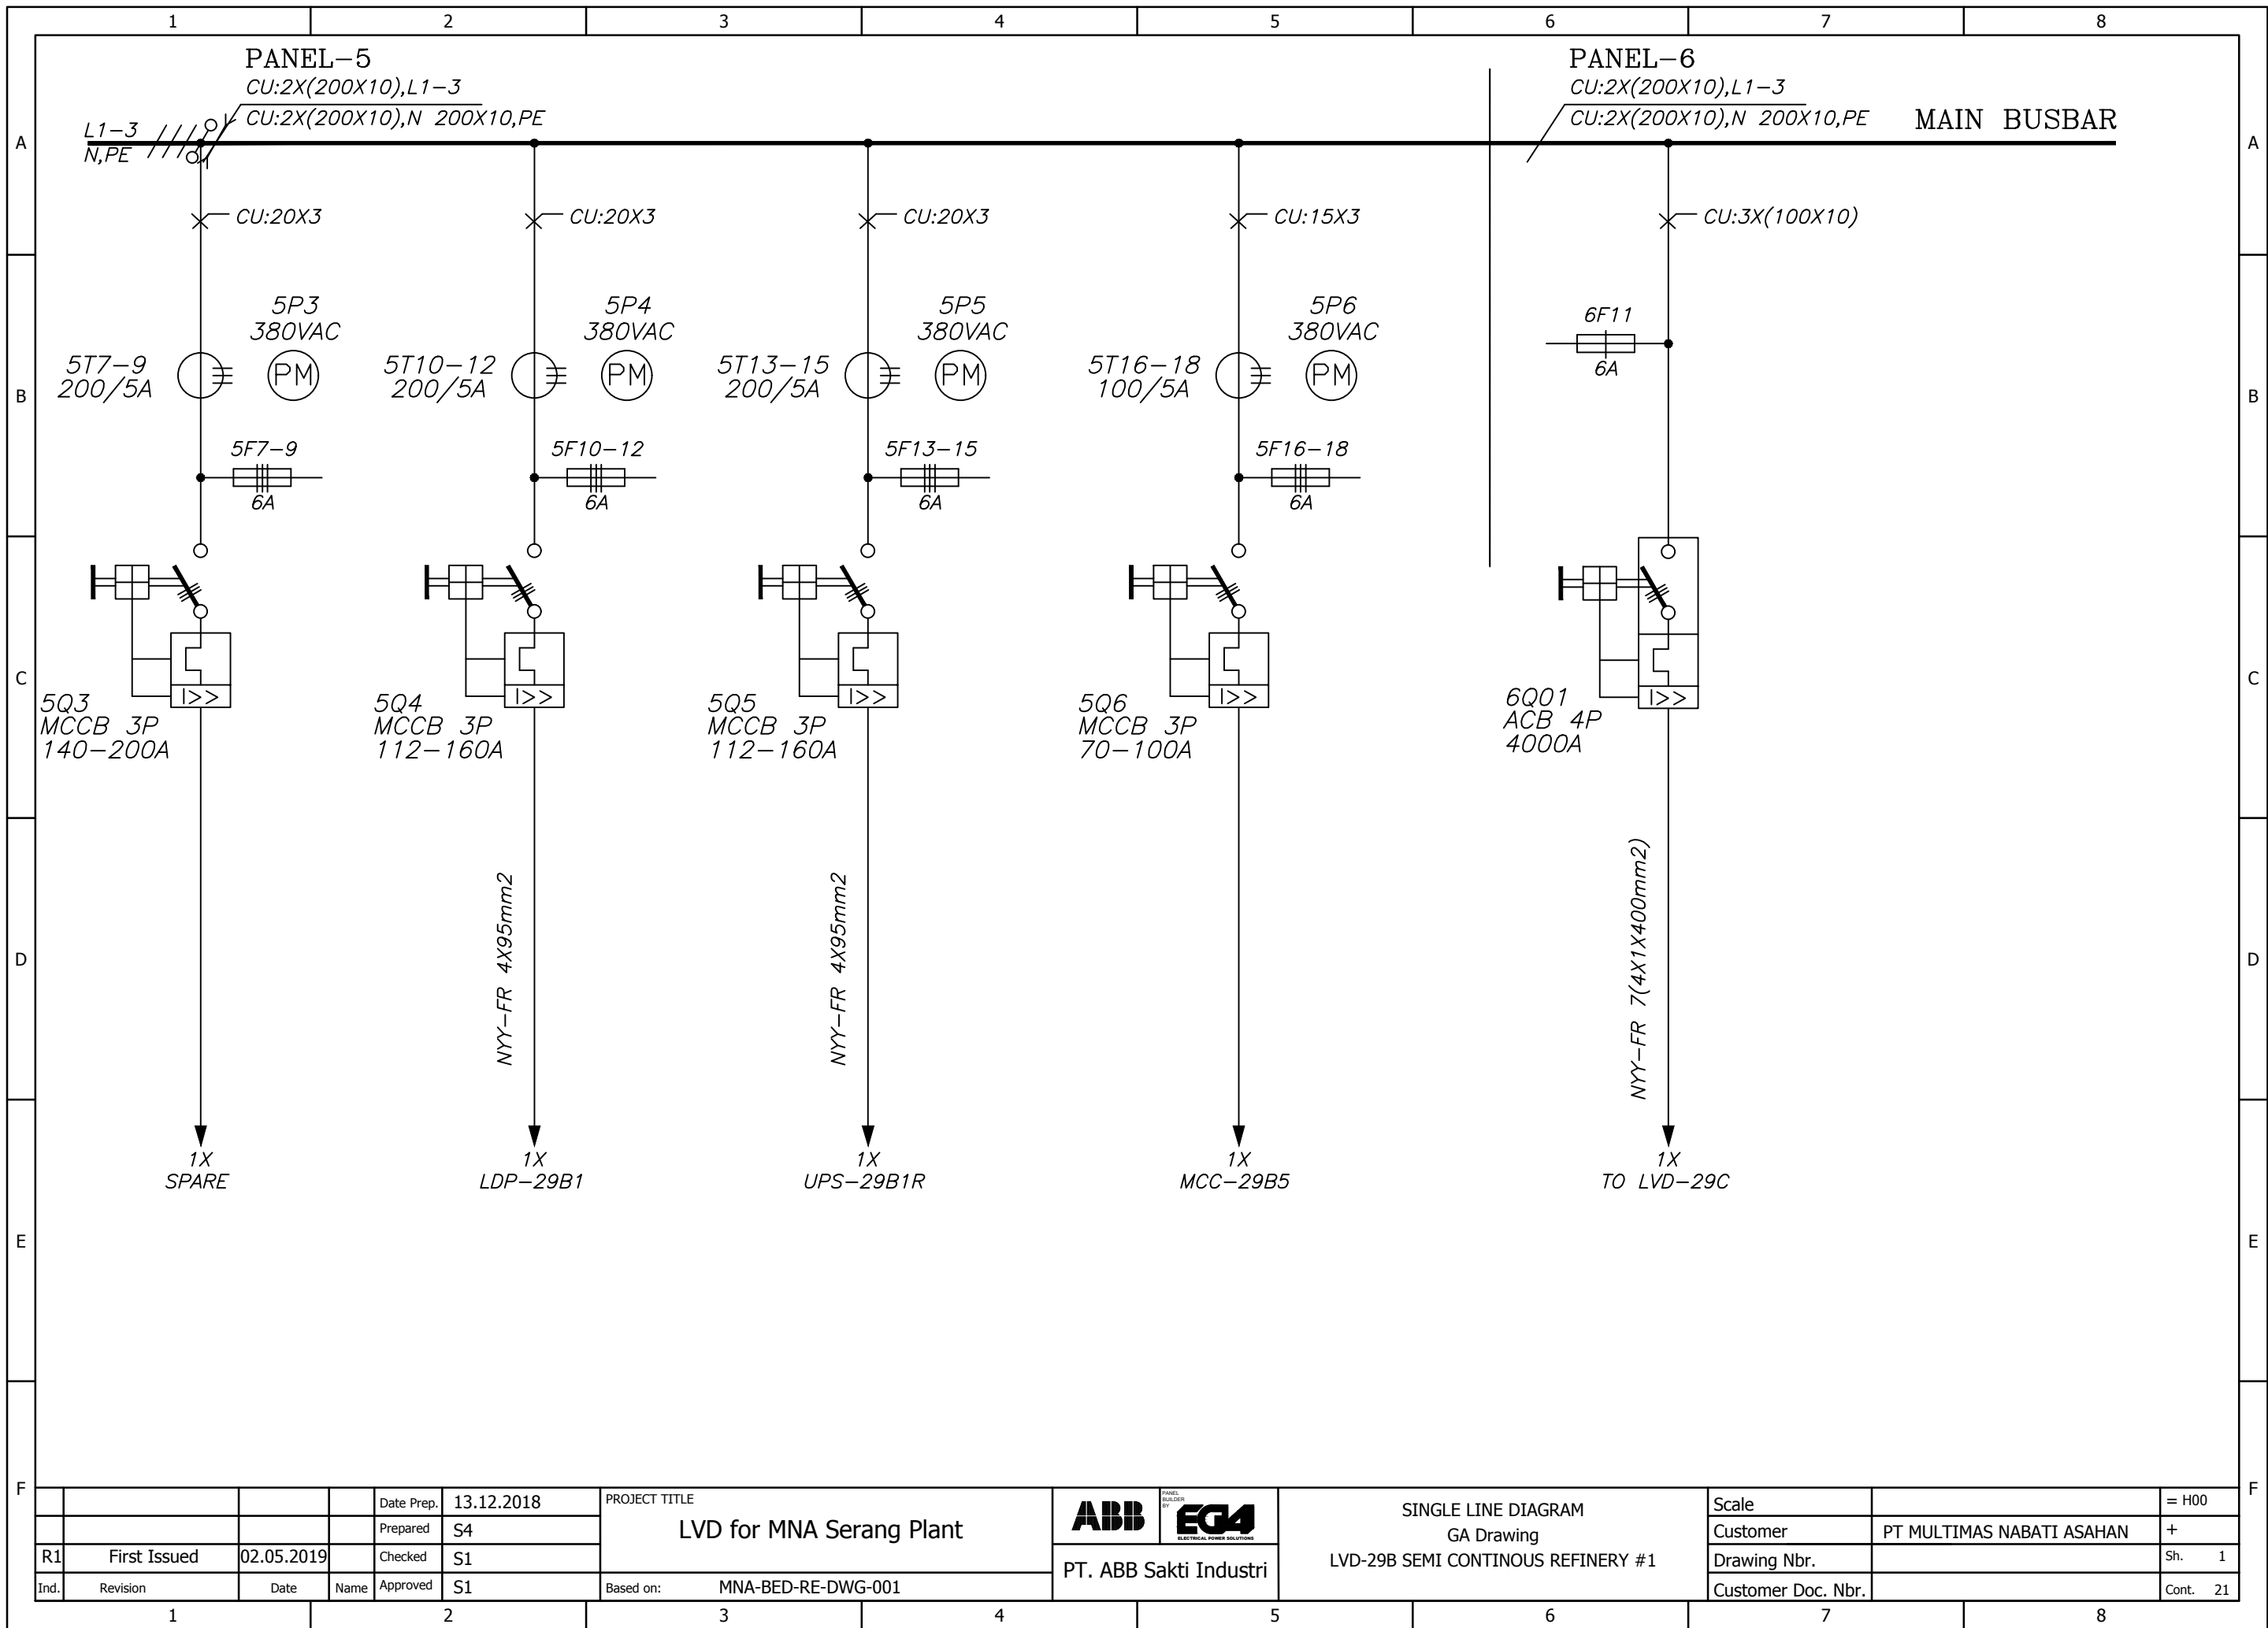


			Date Prep.	13.12.2018	PROJECT TITLE LVD for MNA Serang Plant	ABB PANEL BUILDING BY EG4 ELECTRICAL POWER SOLUTIONS	SINGLE LINE DIAGRAM GA Drawing LVD-29B SEMI CONTINUOUS REFINERY #1	Scale		= H00
			Prepared	S4				Customer	PT MULTIMAS NABATI ASAHAN	+
R1	First Issued	02.05.2019	Checked	S1				Drawing Nbr.		Sh. 1
Ind.	Revision	Date	Name	Approved				S1	Based on:	MNA-BED-RE-DWG-001

WE RESERVE ALL RIGHTS IN THIS DOCUMENT AND IN THE INFORMATION CONTAINED THEREIN. REPRODUCTION, USE OR DISCLOSURE TO THIRD PARTIES WITHOUT EXPRESS AUTHORITY IS STRICTLY FORBIDDEN.

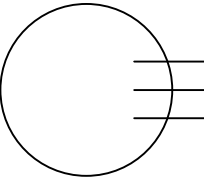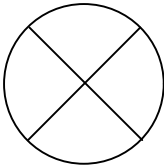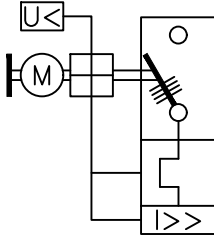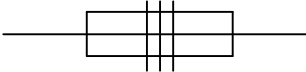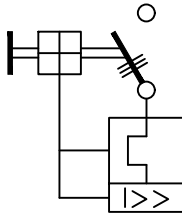
1		2		3		4		5		6		7		8	
A		B		C		D		E		F		A		B	
				CT						PILOT LAMP					
				ACB						FUSE					
				MCCB											
				DIGITAL POWER METER											
F												F			

1		2		3		4		5		6		7		8	
				Date Prep.	13.12.2018	PROJECT TITLE LVD for MNA Serang Plant		 	LEGEND GA Drawing LVD-29B SEMI CONTINUOUS REFINERY #1		Scale			= H00	
				Prepared	S4						Customer		PT MULTIMAS NABATI ASAHAN		+
R1	First Issued	02.05.2019		Checked	S1						Drawing Nbr.				Sh.
Ind.	Revision	Date	Name	Approved	S1	Based on: MNA-BED-RE-DWG-001		PT. ABB Sakti Industri		Customer Doc. Nbr.				Cont.	21

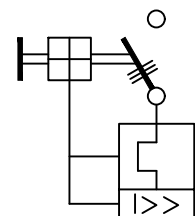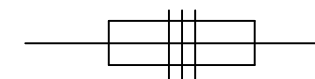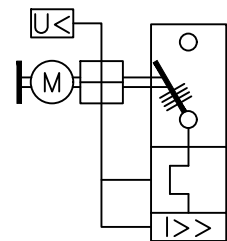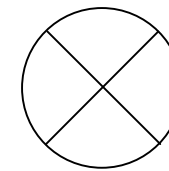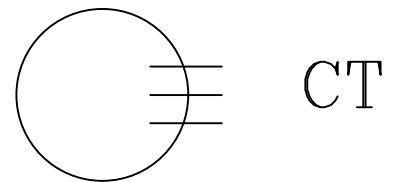


				Date Prep.	13.12.2018	PROJECT TITLE LVD for MNA Serang Plant	 	LEGEND GA Drawing LVD-29B SEMI CONTINOUS REFINERY #1	Scale		= H00
				Prepared	S4				Customer	PT MULTIMAS NABATI ASAHAN	+
R1	First Issued	02.05.2019		Checked	S1				Drawing Nbr.		Sh. 1
Ind.	Revision	Date	Name	Approved	S1	Based on: MNA-BED-RE-DWG-001	PT. ABB Sakti Industri		Customer Doc. Nbr.		Cont. 21

WE RESERVE ALL RIGHTS IN THIS DOCUMENT AND IN THE INFORMATION CONTAINED THEREIN. REPRODUCTION, USE OR DISCLOSURE TO THIRD PARTIES WITHOUT EXPRESS AUTHORITY IS STRICTLY FORBIDDEN.

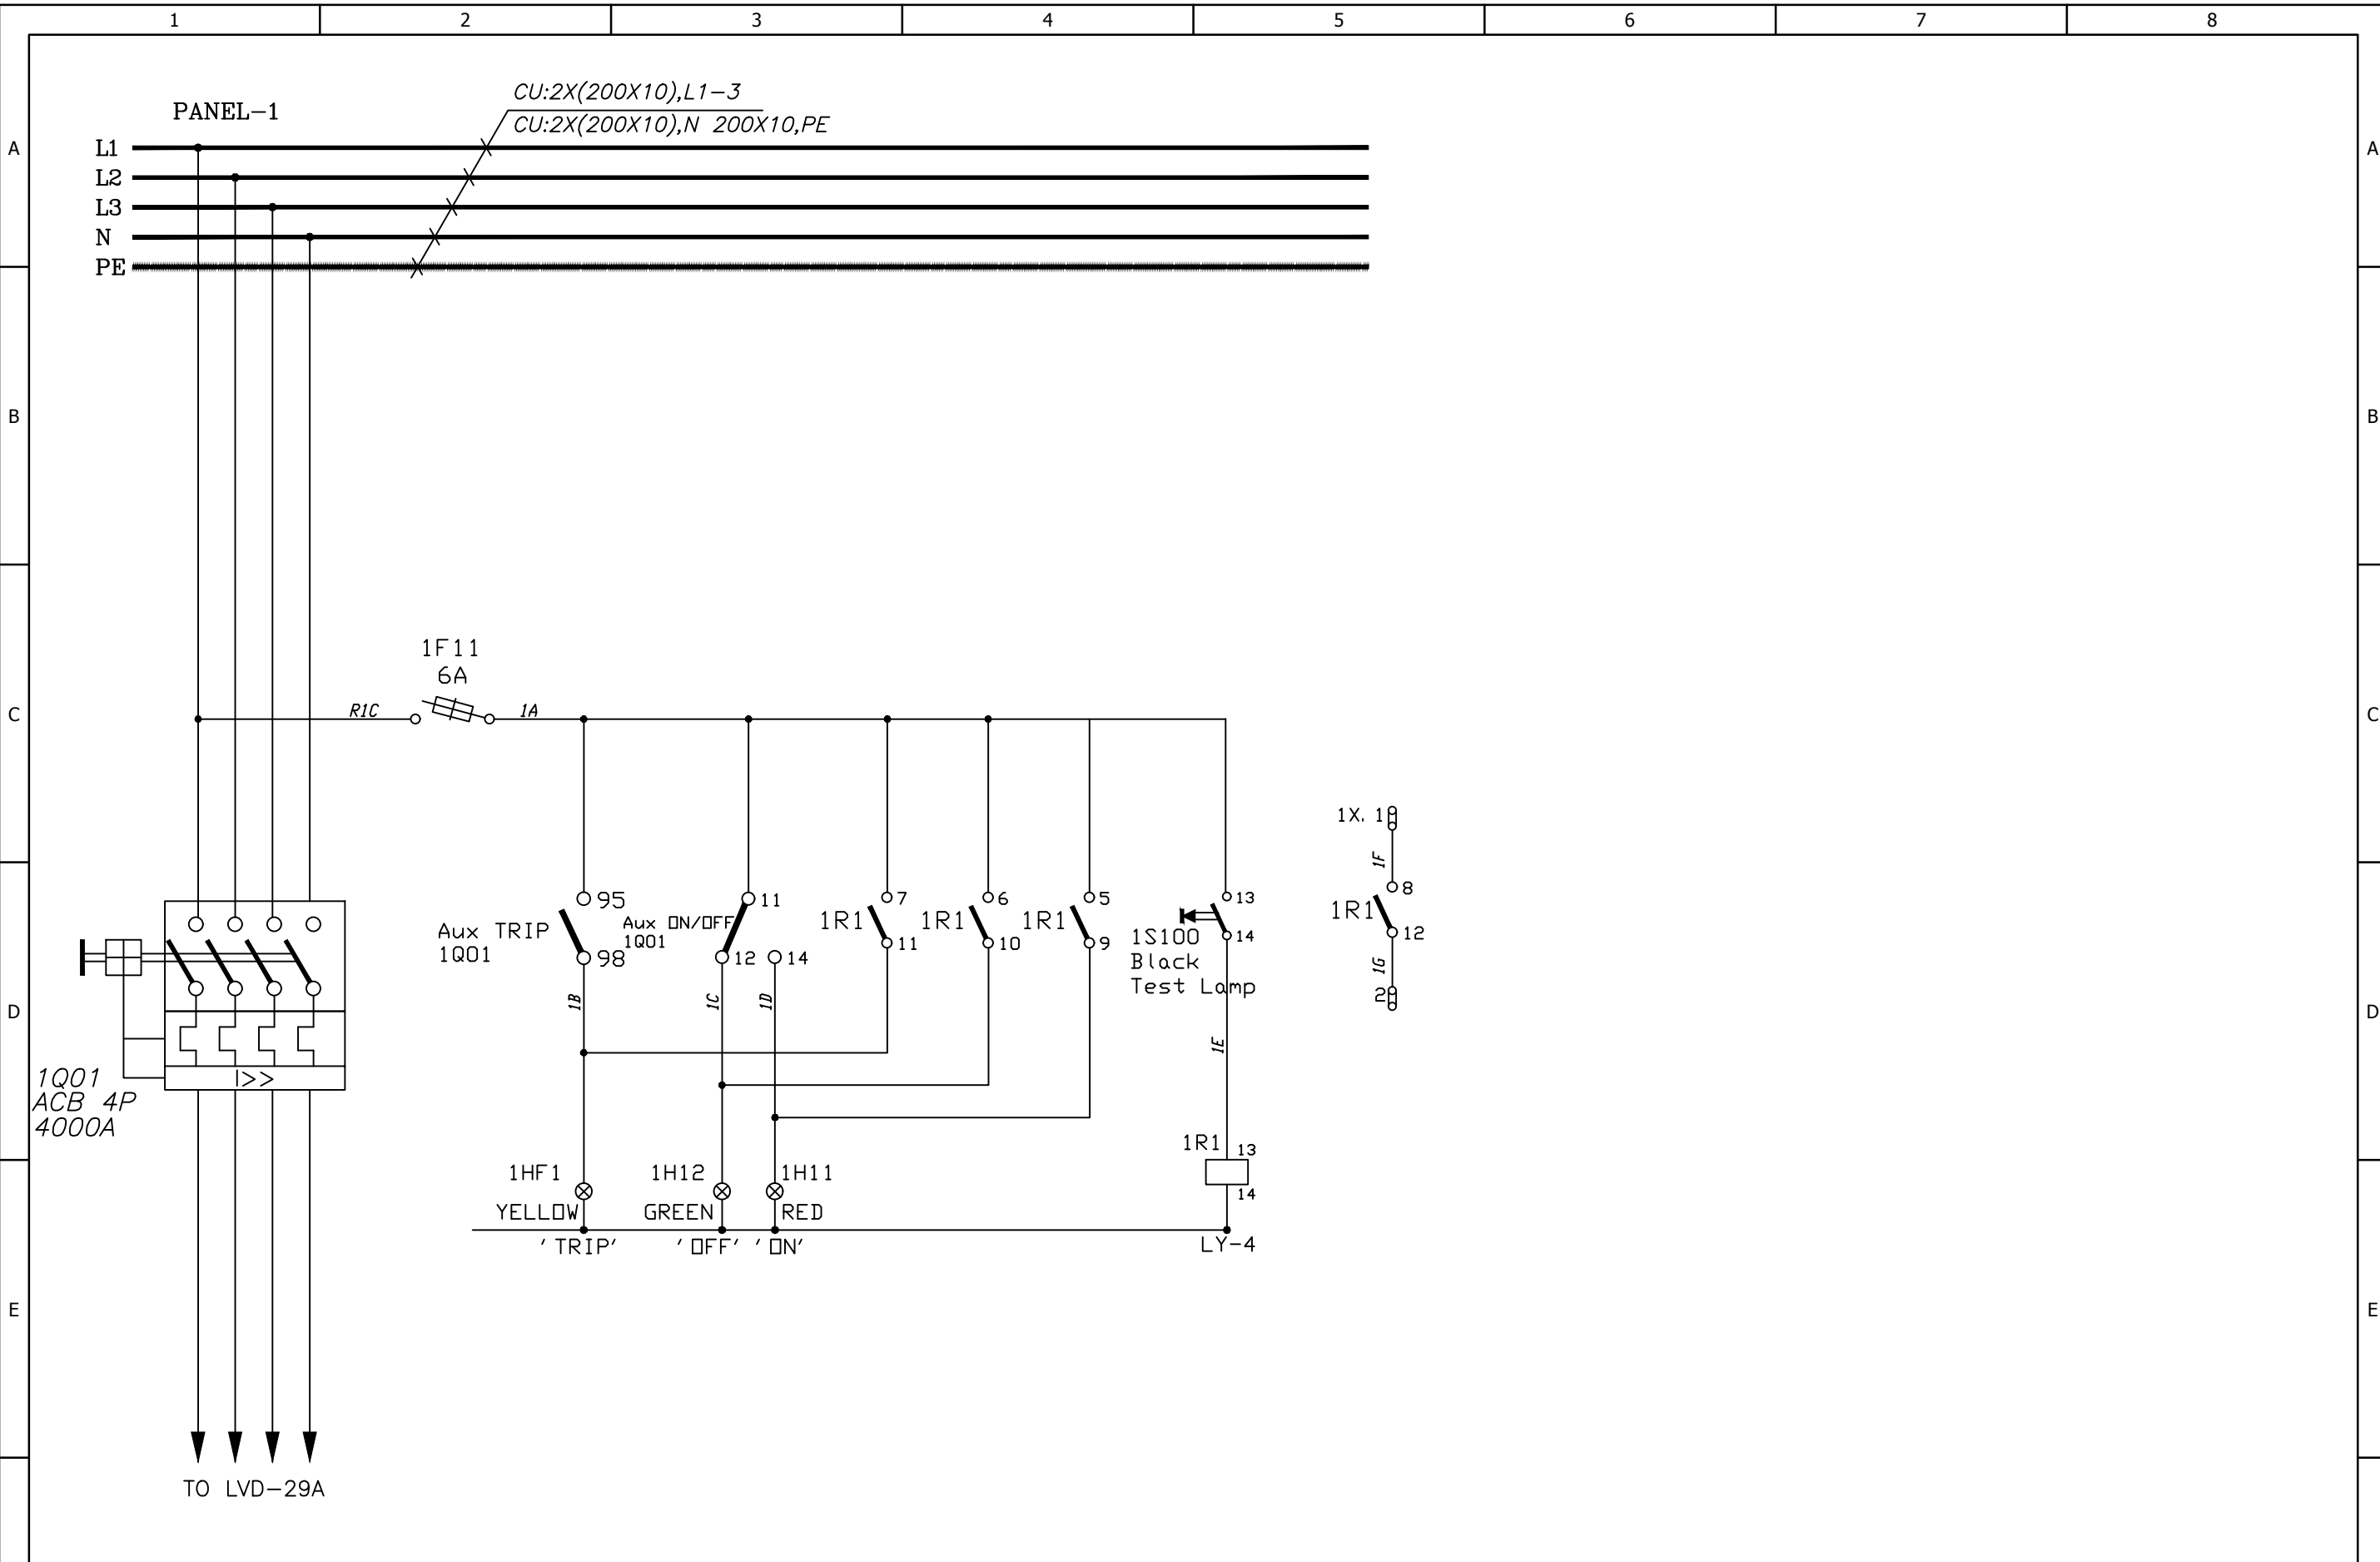

				Date Prep.	13.12.2018	PROJECT TITLE LVD for MNA Serang Plant	ABB PANEL BUILDER BY EG4 ELECTRICAL POWER SOLUTIONS	WIRING CONTROL DIAGRAM GA Drawing LVD-29B SEMI CONTINUOUS REFINERY #1	Scale			= H00				
				Prepared	S4				Customer	PT MULTIMAS NABATI ASAHAN		+				
R1	First Issued	02.05.2019		Checked	S1				PT. ABB Sakti Industri	Drawing Nbr.			Sh. 1			
Ind.	Revision	Date	Name	Approved	S1	Based on: MNA-BED-RE-DWG-001			Customer Doc. Nbr.			Cont. 21				
1			2			3		4		5		6	7		8	

WE RESERVE ALL RIGHTS IN THIS DOCUMENT AND IN THE INFORMATION CONTAINED THEREIN. REPRODUCTION, USE OR DISCLOSURE TO THIRD PARTIES WITHOUT EXPRESS AUTHORITY IS STRICTLY FORBIDDEN.

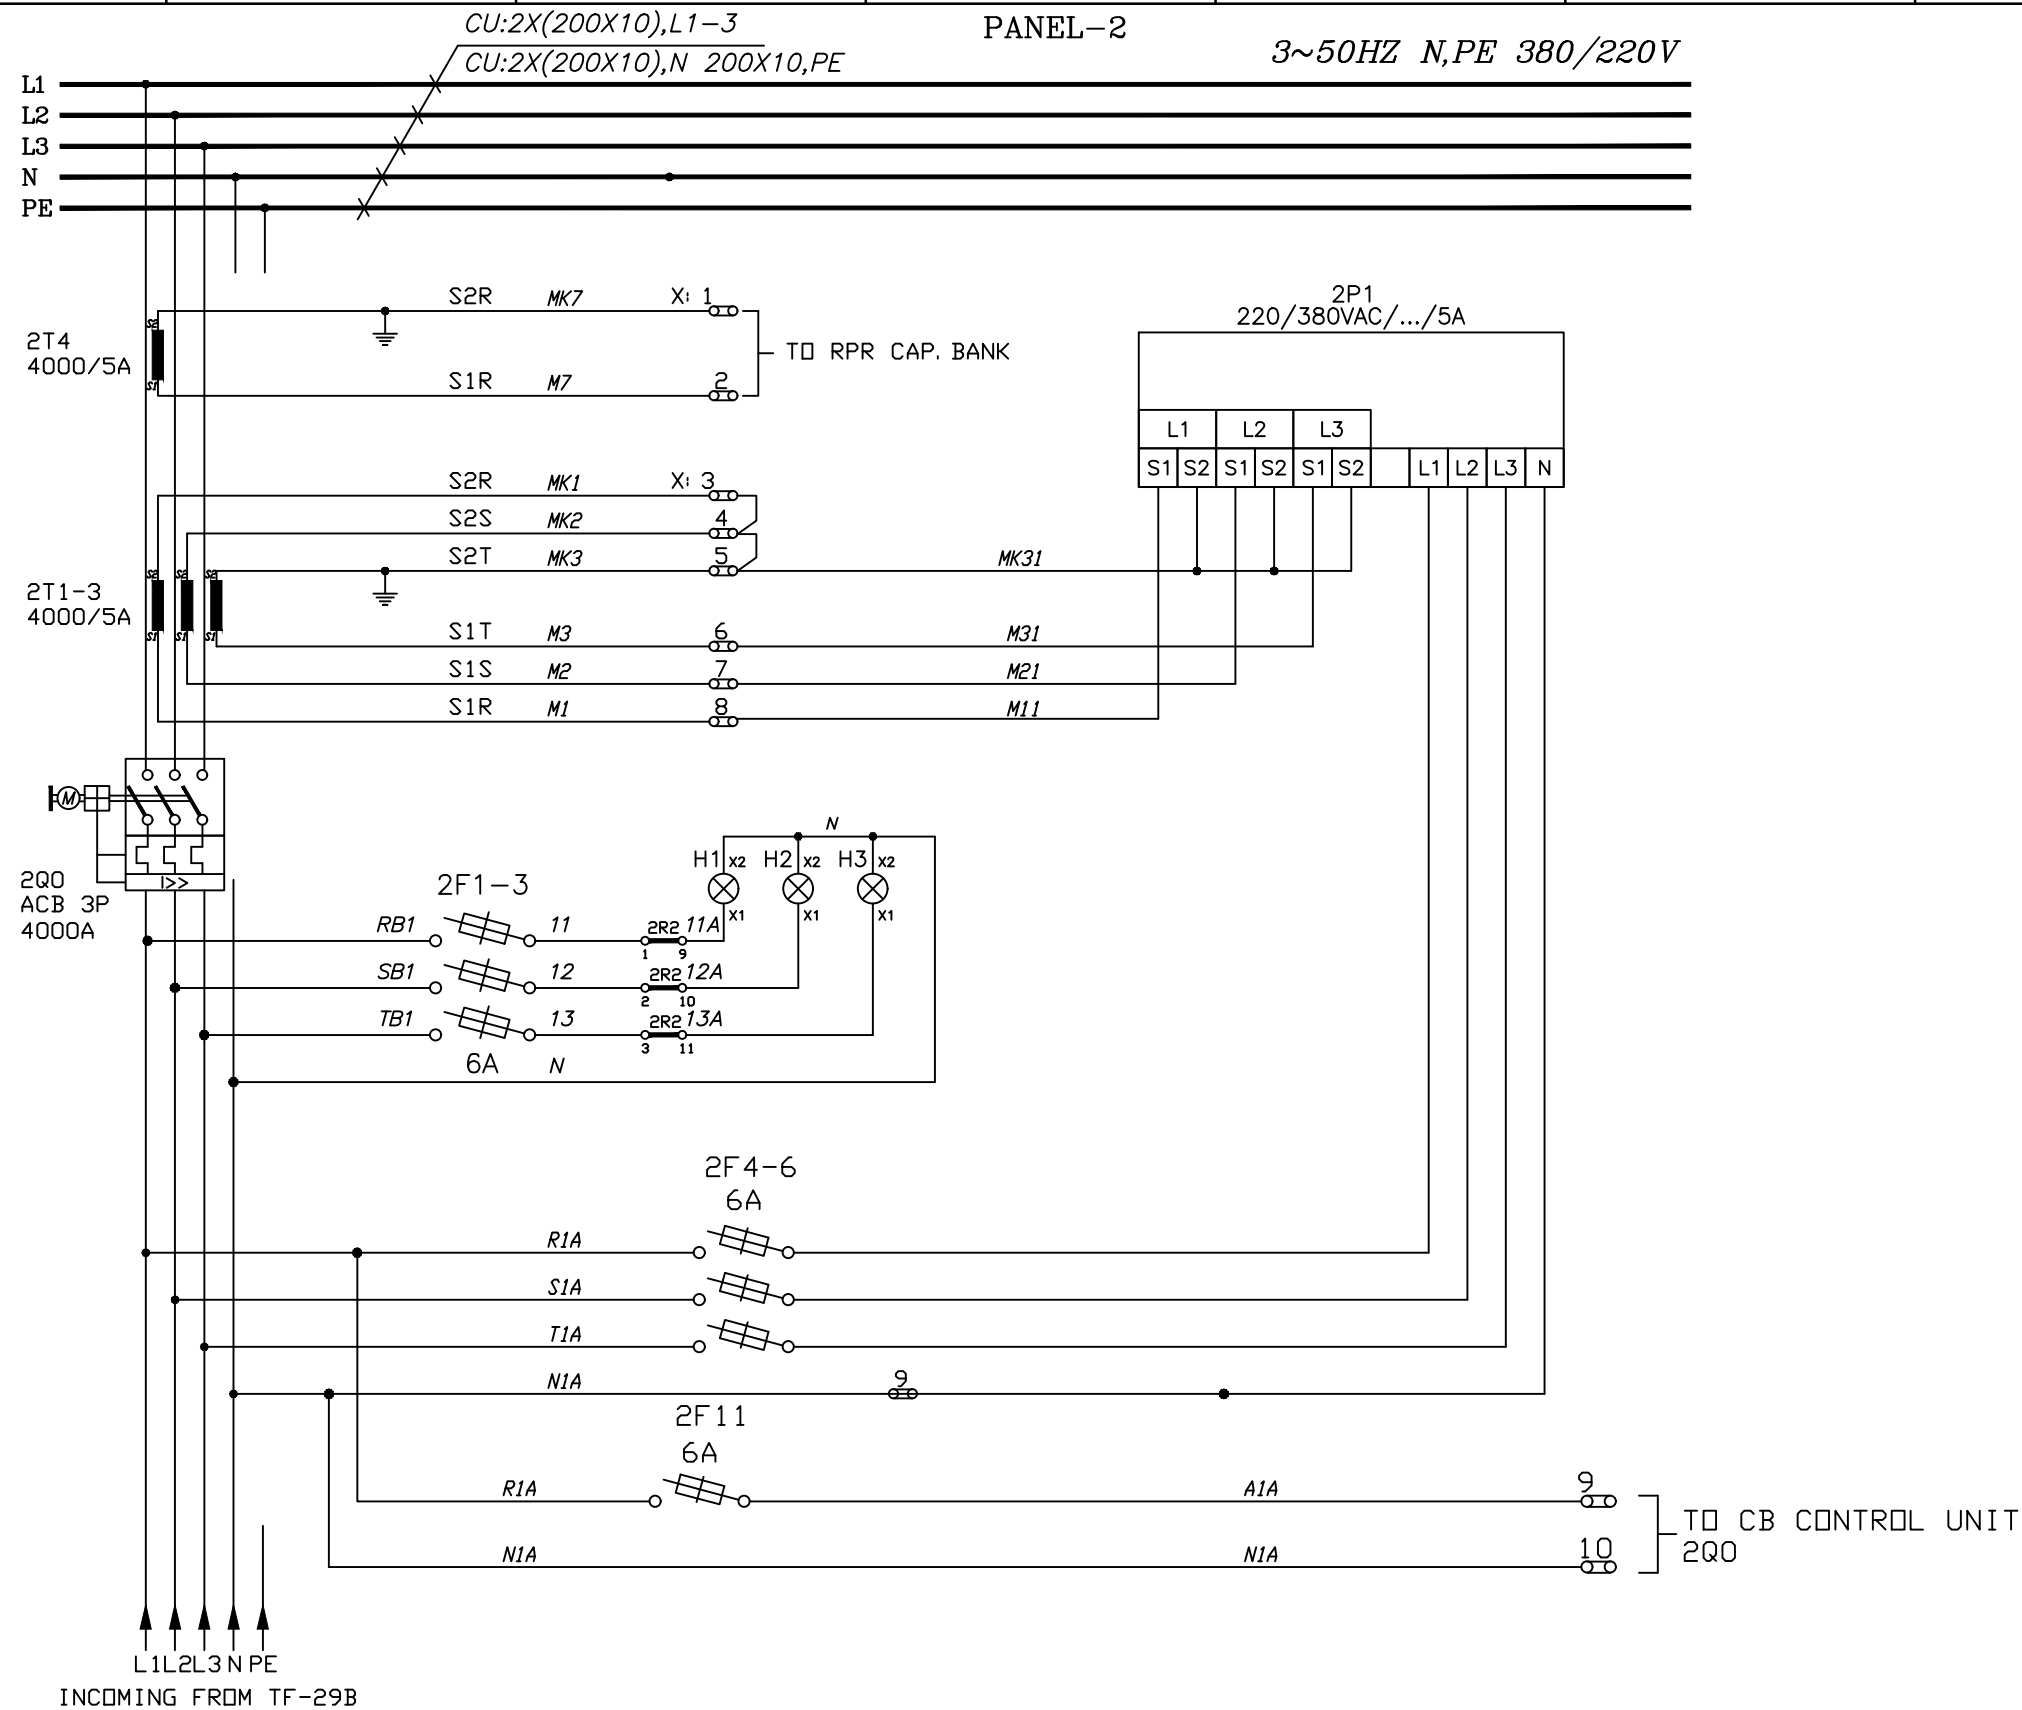

				Date Prep.	13.12.2018	PROJECT TITLE LVD for MNA Serang Plant	  PT. ABB Sakti Industri	WIRING CONTROL DIAGRAM GA Drawing LVD-29B SEMI CONTINUOUS REFINERY #1	Scale		= H00
				Prepared	S4				Customer	PT MULTIMAS NABATI ASAHAN	+
R1	First Issued	02.05.2019		Checked	S1				Drawing Nbr.		Sh. 1
Ind.	Revision	Date	Name	Approved	S1	Based on:	MNA-BED-RE-DWG-001		Customer Doc. Nbr.		Cont. 21

1

2

3

4


5

6


7

8

WE RESERVE ALL RIGHTS IN THIS DOCUMENT AND IN THE INFORMATION CONTAINED THEREIN. REPRODUCTION, USE OR DISCLOSURE TO THIRD PARTIES WITHOUT EXPRESS AUTHORITY IS STRICTLY FORBIDDEN.

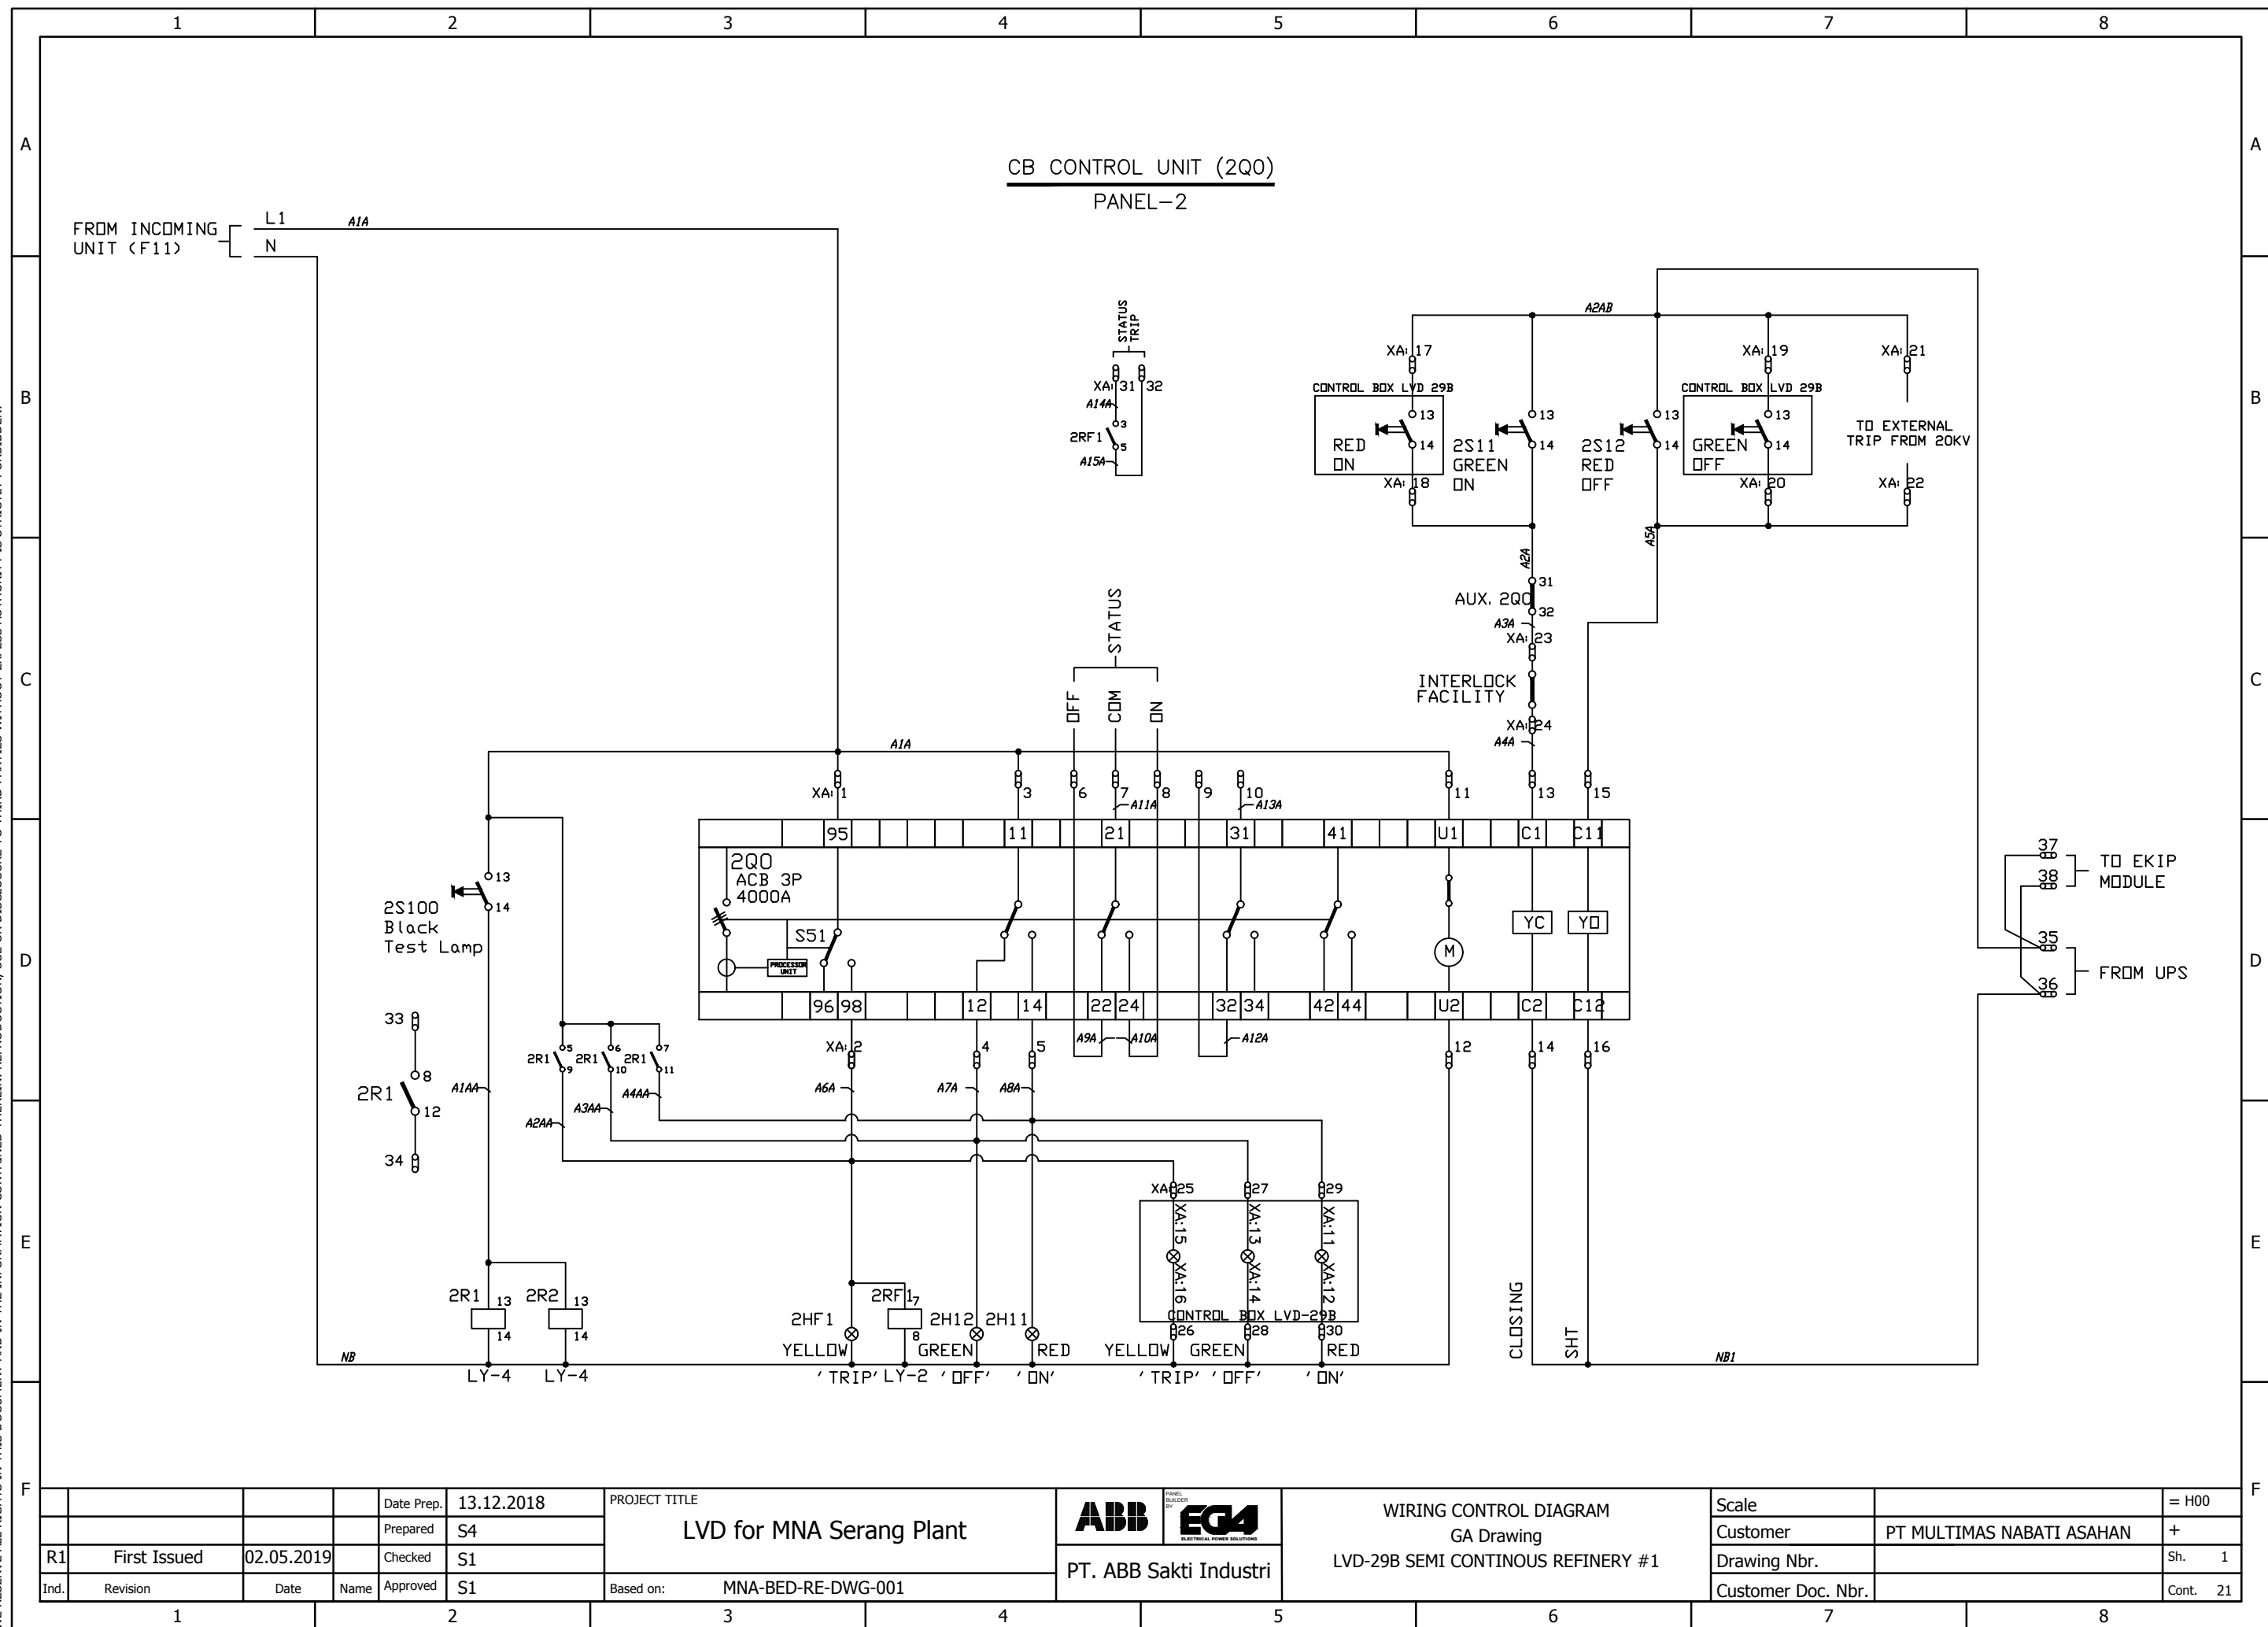


WE RESERVE ALL RIGHTS IN THIS DOCUMENT AND IN THE INFORMATION CONTAINED THEREIN. REPRODUCTION, USE OR DISCLOSURE TO THIRD PARTIES WITHOUT EXPRESS AUTHORITY IS STRICTLY FORBIDDEN.

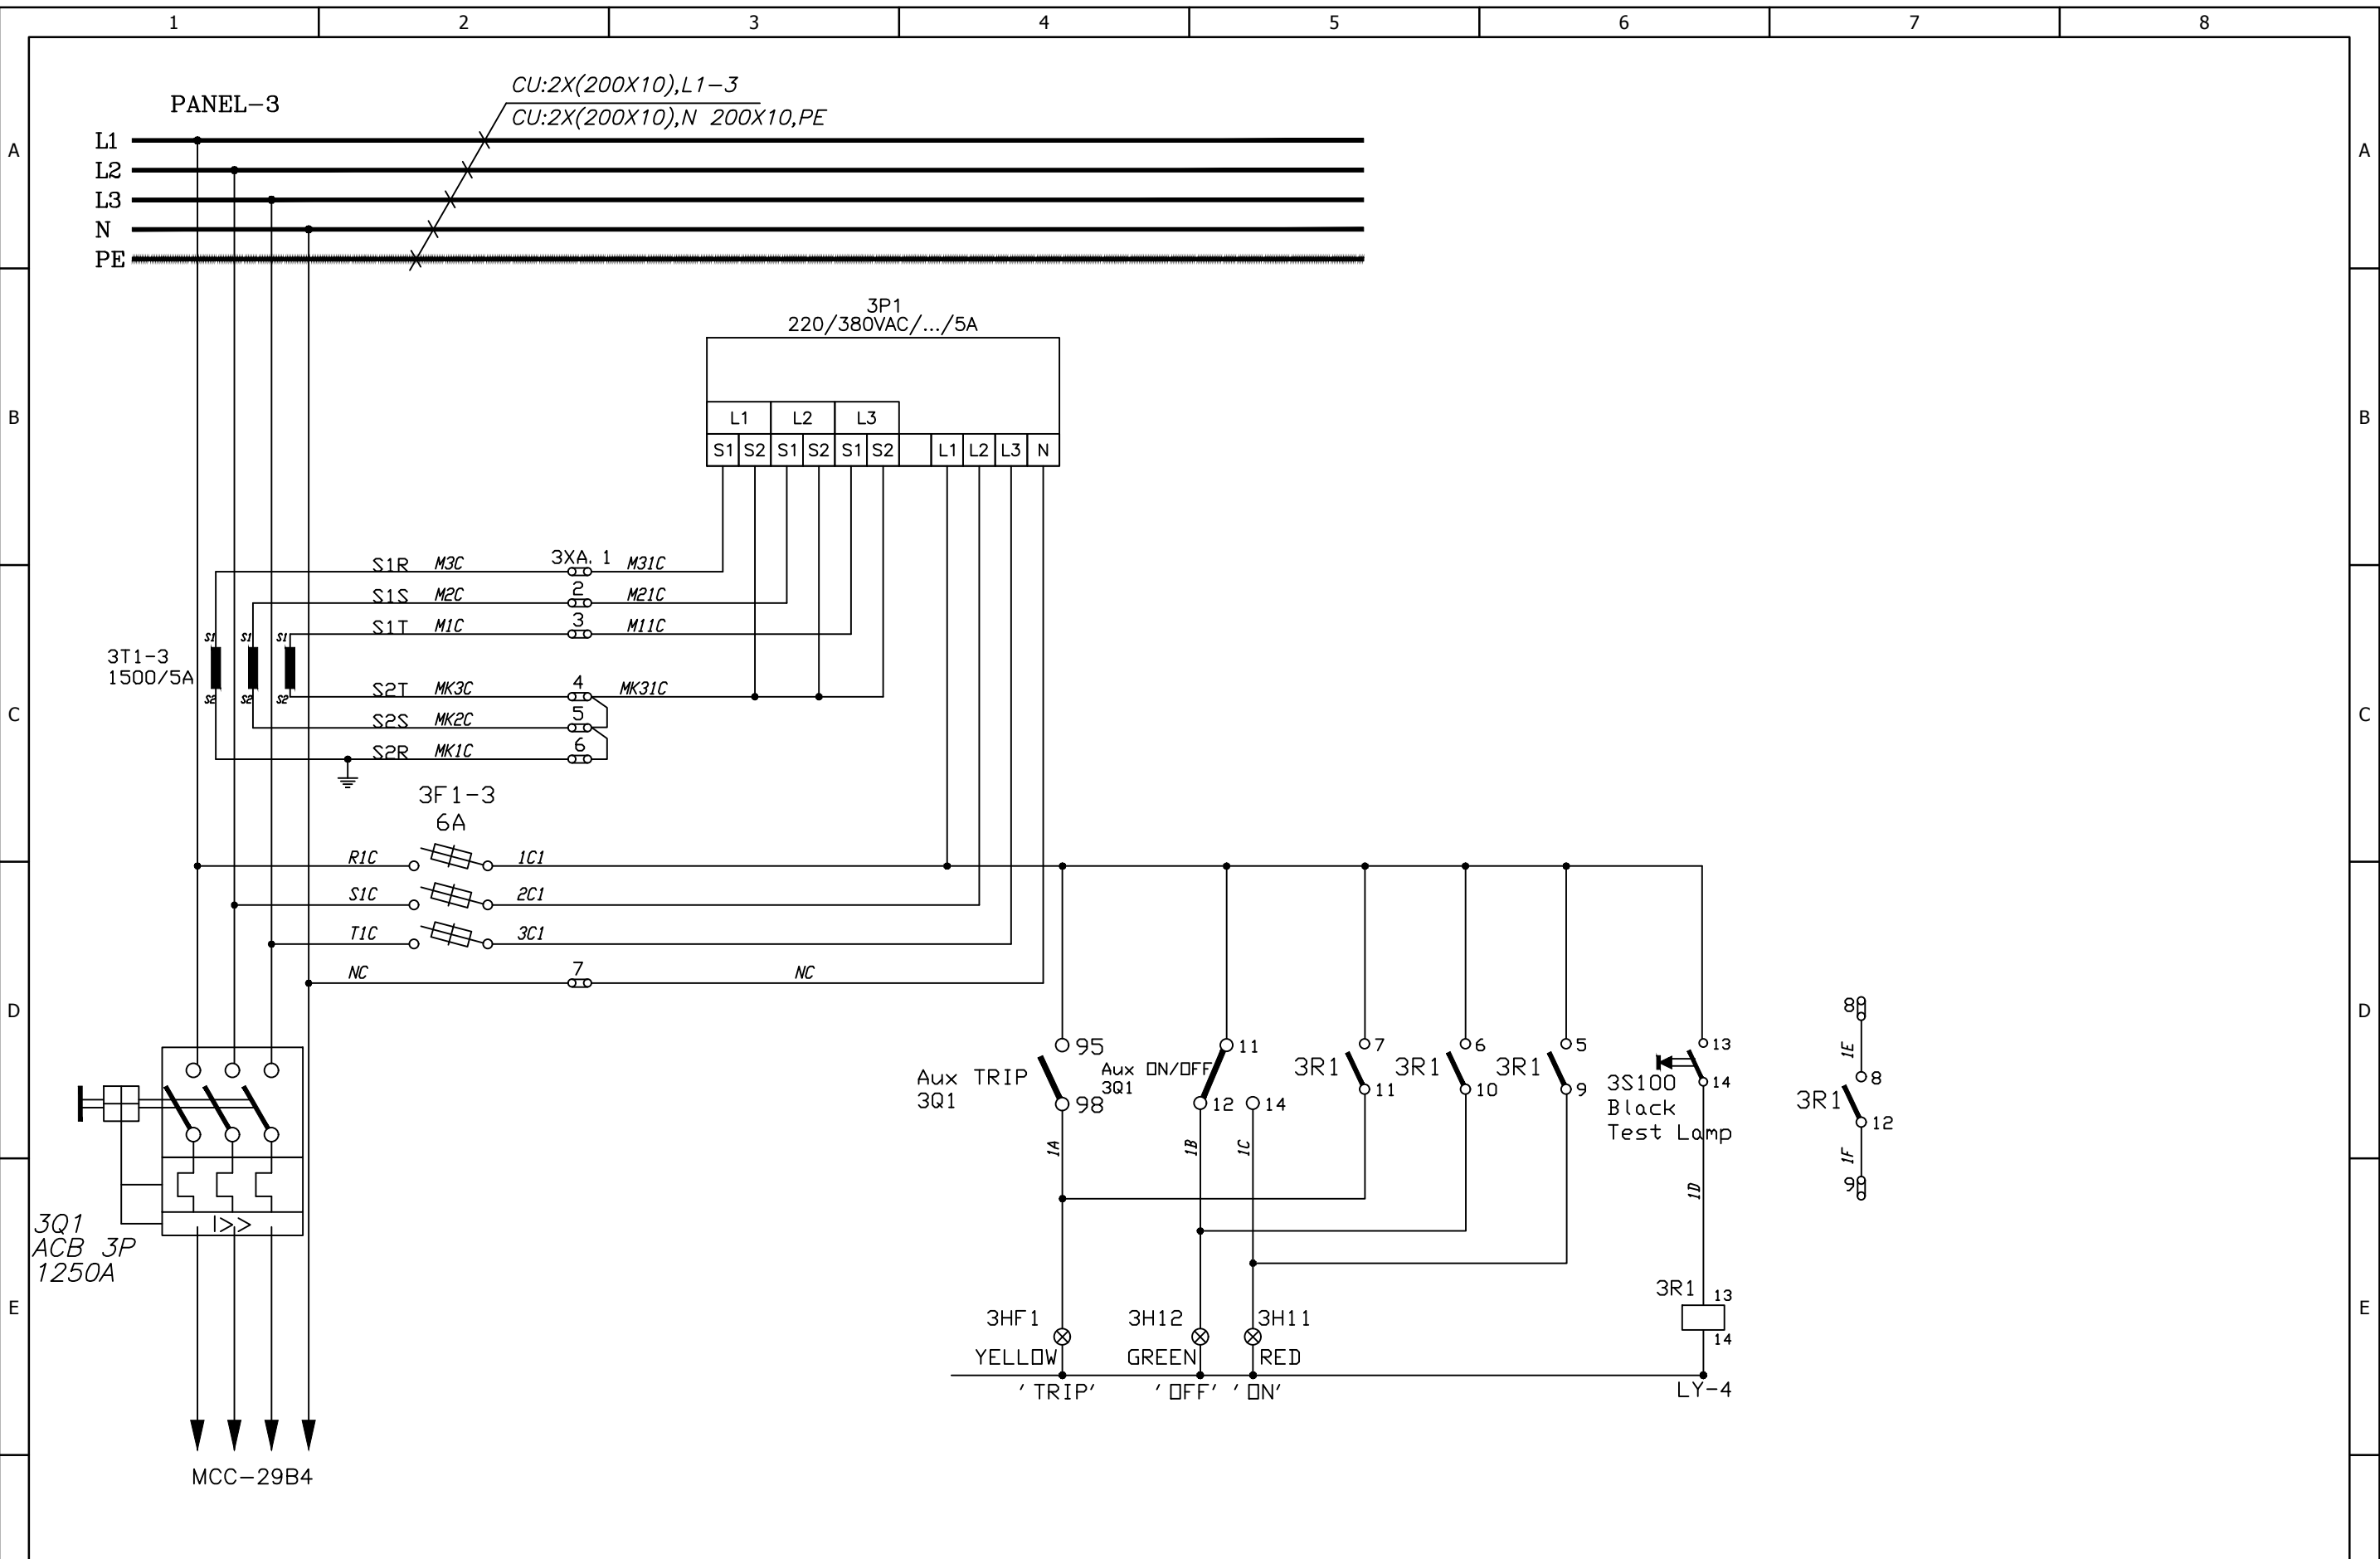


Ind.		Revision	Date	Name	Approved	Based on:	MNA-BED-RE-DWG-001		PT. ABB Sakti Industri		WIRING CONTROL DIAGRAM GA Drawing LVD-29B SEMI CONTINUOUS REFINERY #1		Scale	= H00	
R1		First Issued	02.05.2019	Checked	S1	PROJECT TITLE		LVD for MNA Serang Plant		ABB EG4 ELECTRICAL POWER SOLUTIONS		Customer		PT MULTIMAS NABATI ASAHAN	
		Date Prep.		13.12.2018		Prepared		S4		Drawing Nbr.		Sh. 1		Customer Doc. Nbr.	
														Cont. 21	

WE RESERVE ALL RIGHTS IN THIS DOCUMENT AND IN THE INFORMATION CONTAINED THEREIN. REPRODUCTION, USE OR DISCLOSURE TO THIRD PARTIES WITHOUT EXPRESS AUTHORITY IS STRICTLY FORBIDDEN.

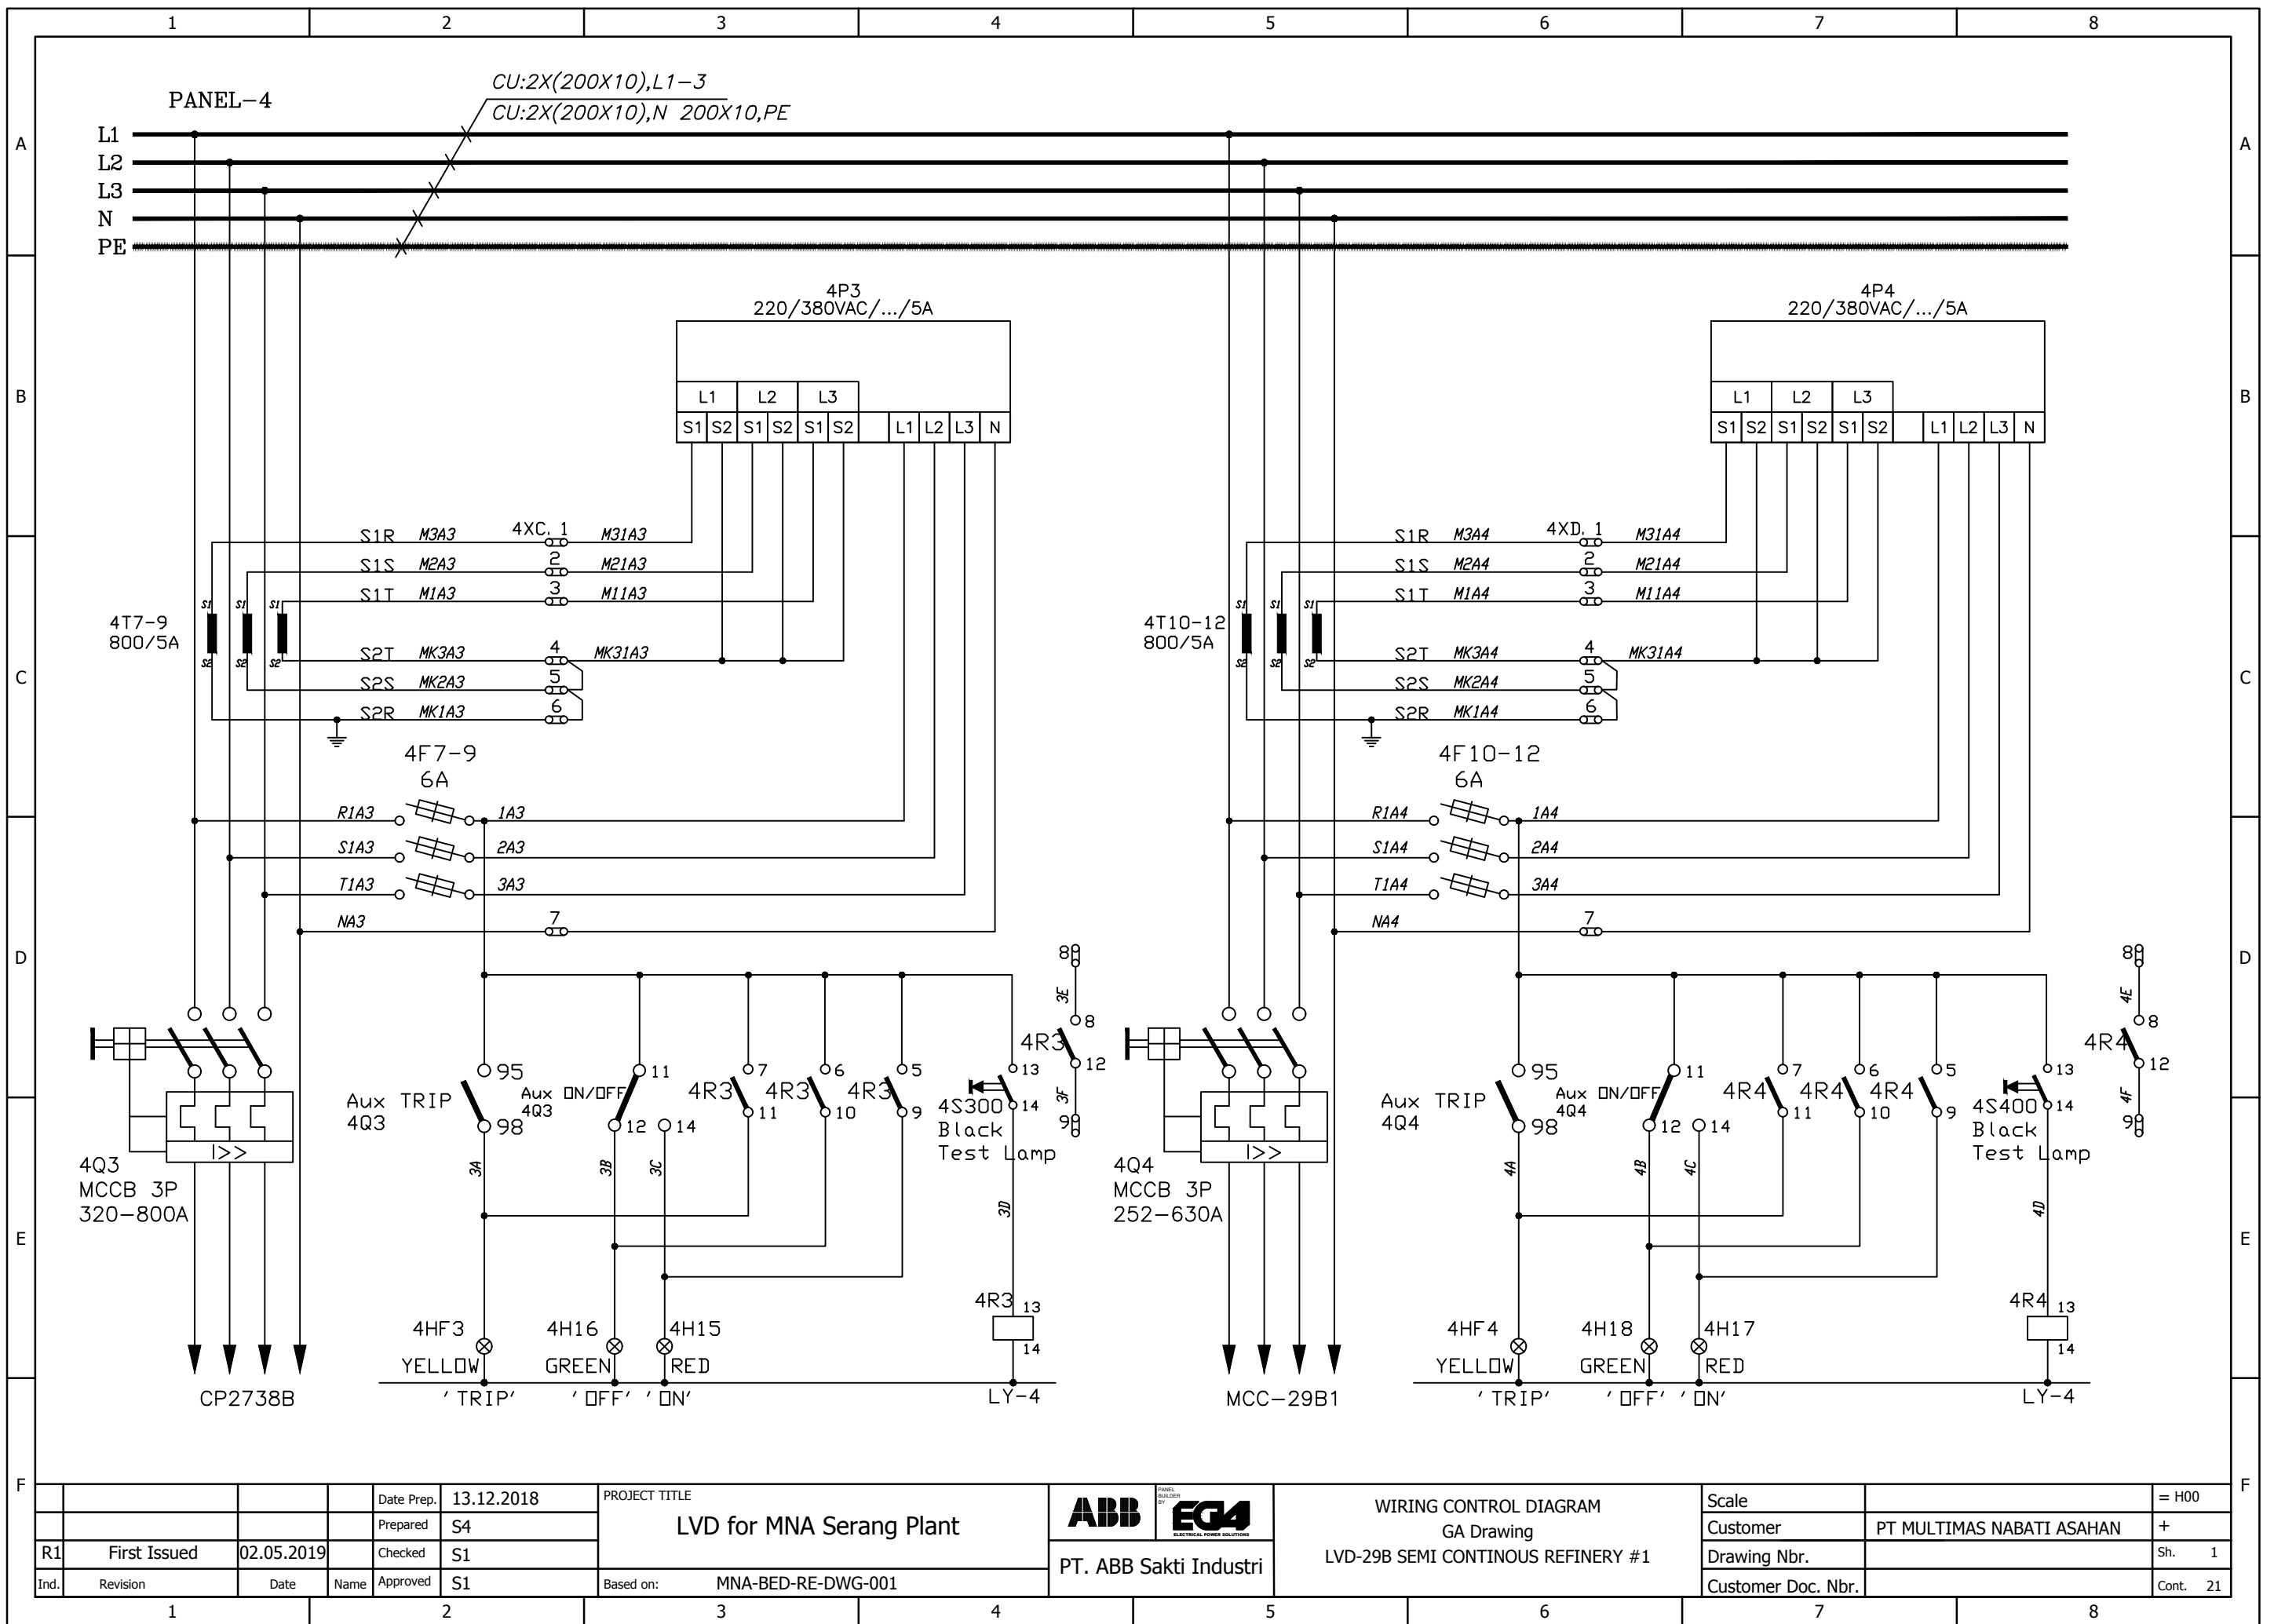


			Date Prep.	13.12.2018	PROJECT TITLE LVD for MNA Serang Plant	ABB PANEL FACTORY BY EG4 ELECTRICAL POWER SOLUTIONS	WIRING CONTROL DIAGRAM GA Drawing LVD-29B SEMI CONTINUOUS REFINERY #1	Scale		= H00
			Prepared	S4				Customer	PT MULTIMAS NABATI ASAHAN	+
R1	First Issued	02.05.2019	Checked	S1				Drawing Nbr.		Sh. 1
Ind.	Revision	Date	Name	Approved	S1	Based on: MNA-BED-RE-DWG-001	PT. ABB Sakti Industri	Customer Doc. Nbr.		Cont. 21

WE RESERVE ALL RIGHTS IN THIS DOCUMENT AND IN THE INFORMATION CONTAINED THEREIN. REPRODUCTION, USE OR DISCLOSURE TO THIRD PARTIES WITHOUT EXPRESS AUTHORITY IS STRICTLY FORBIDDEN.

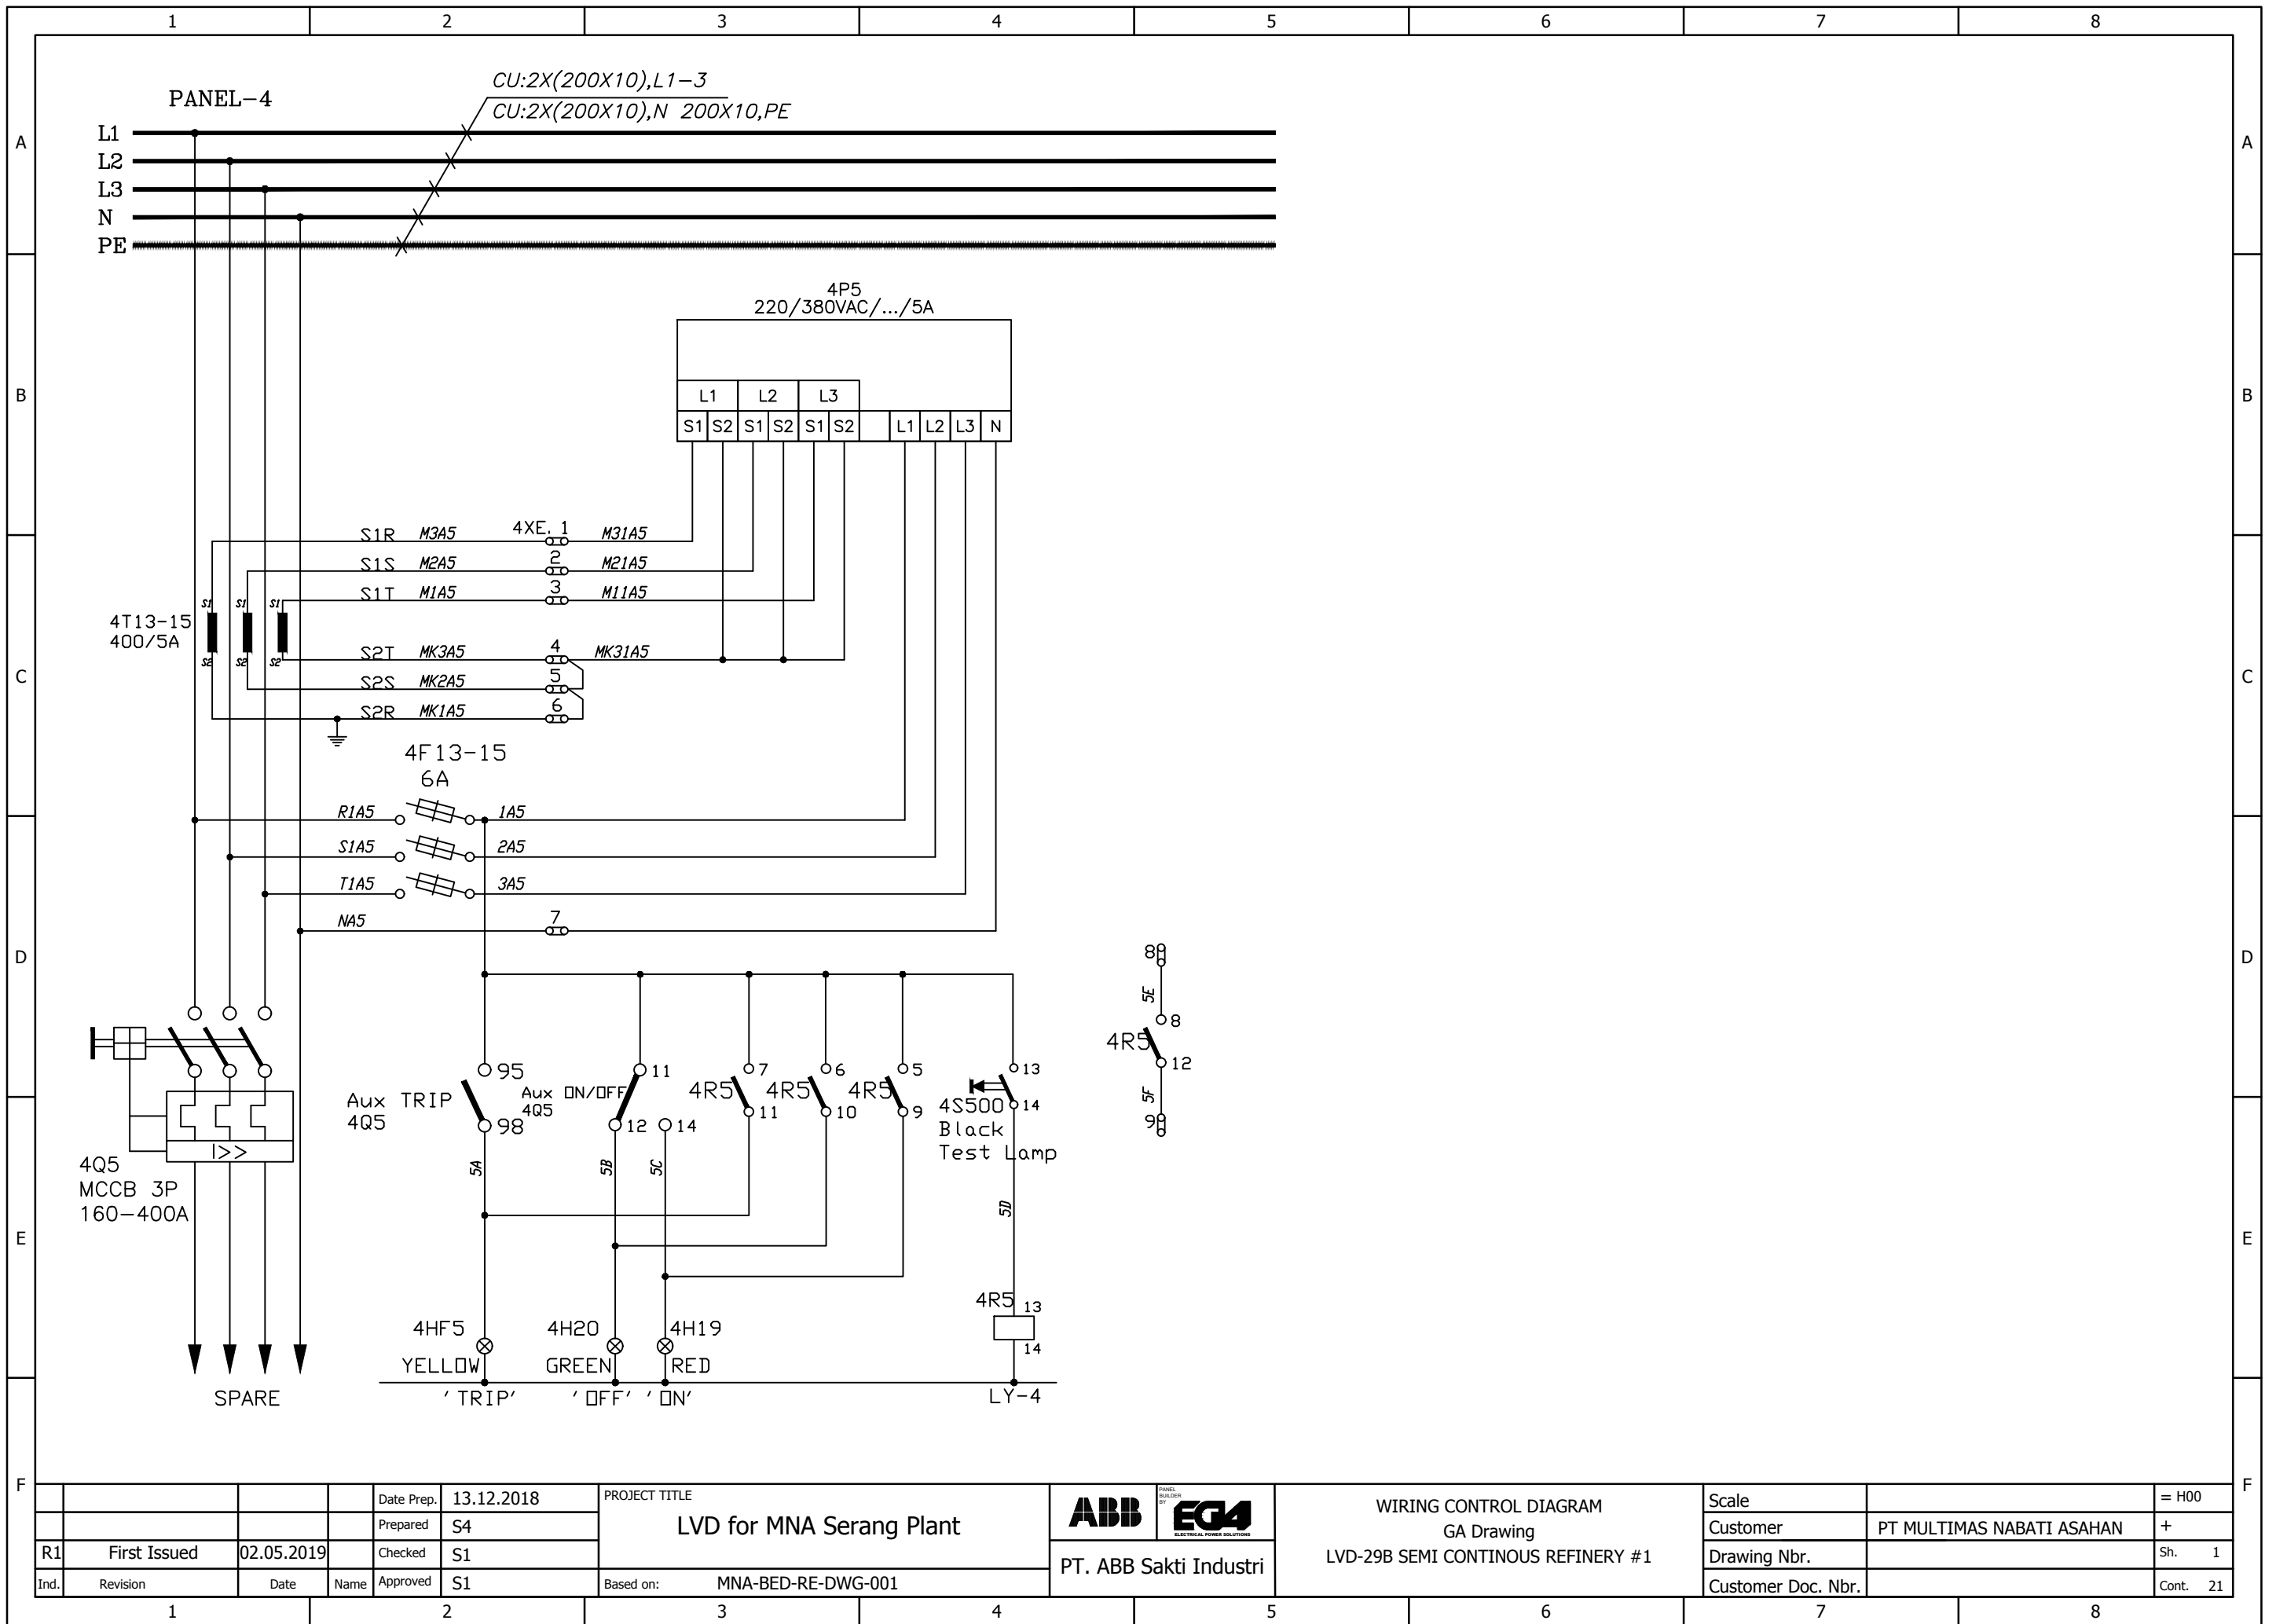

WE RESERVE ALL RIGHTS IN THIS DOCUMENT AND IN THE INFORMATION CONTAINED THEREIN. REPRODUCTION, USE OR DISCLOSURE TO THIRD PARTIES WITHOUT EXPRESS AUTHORITY IS STRICTLY FORBIDDEN.

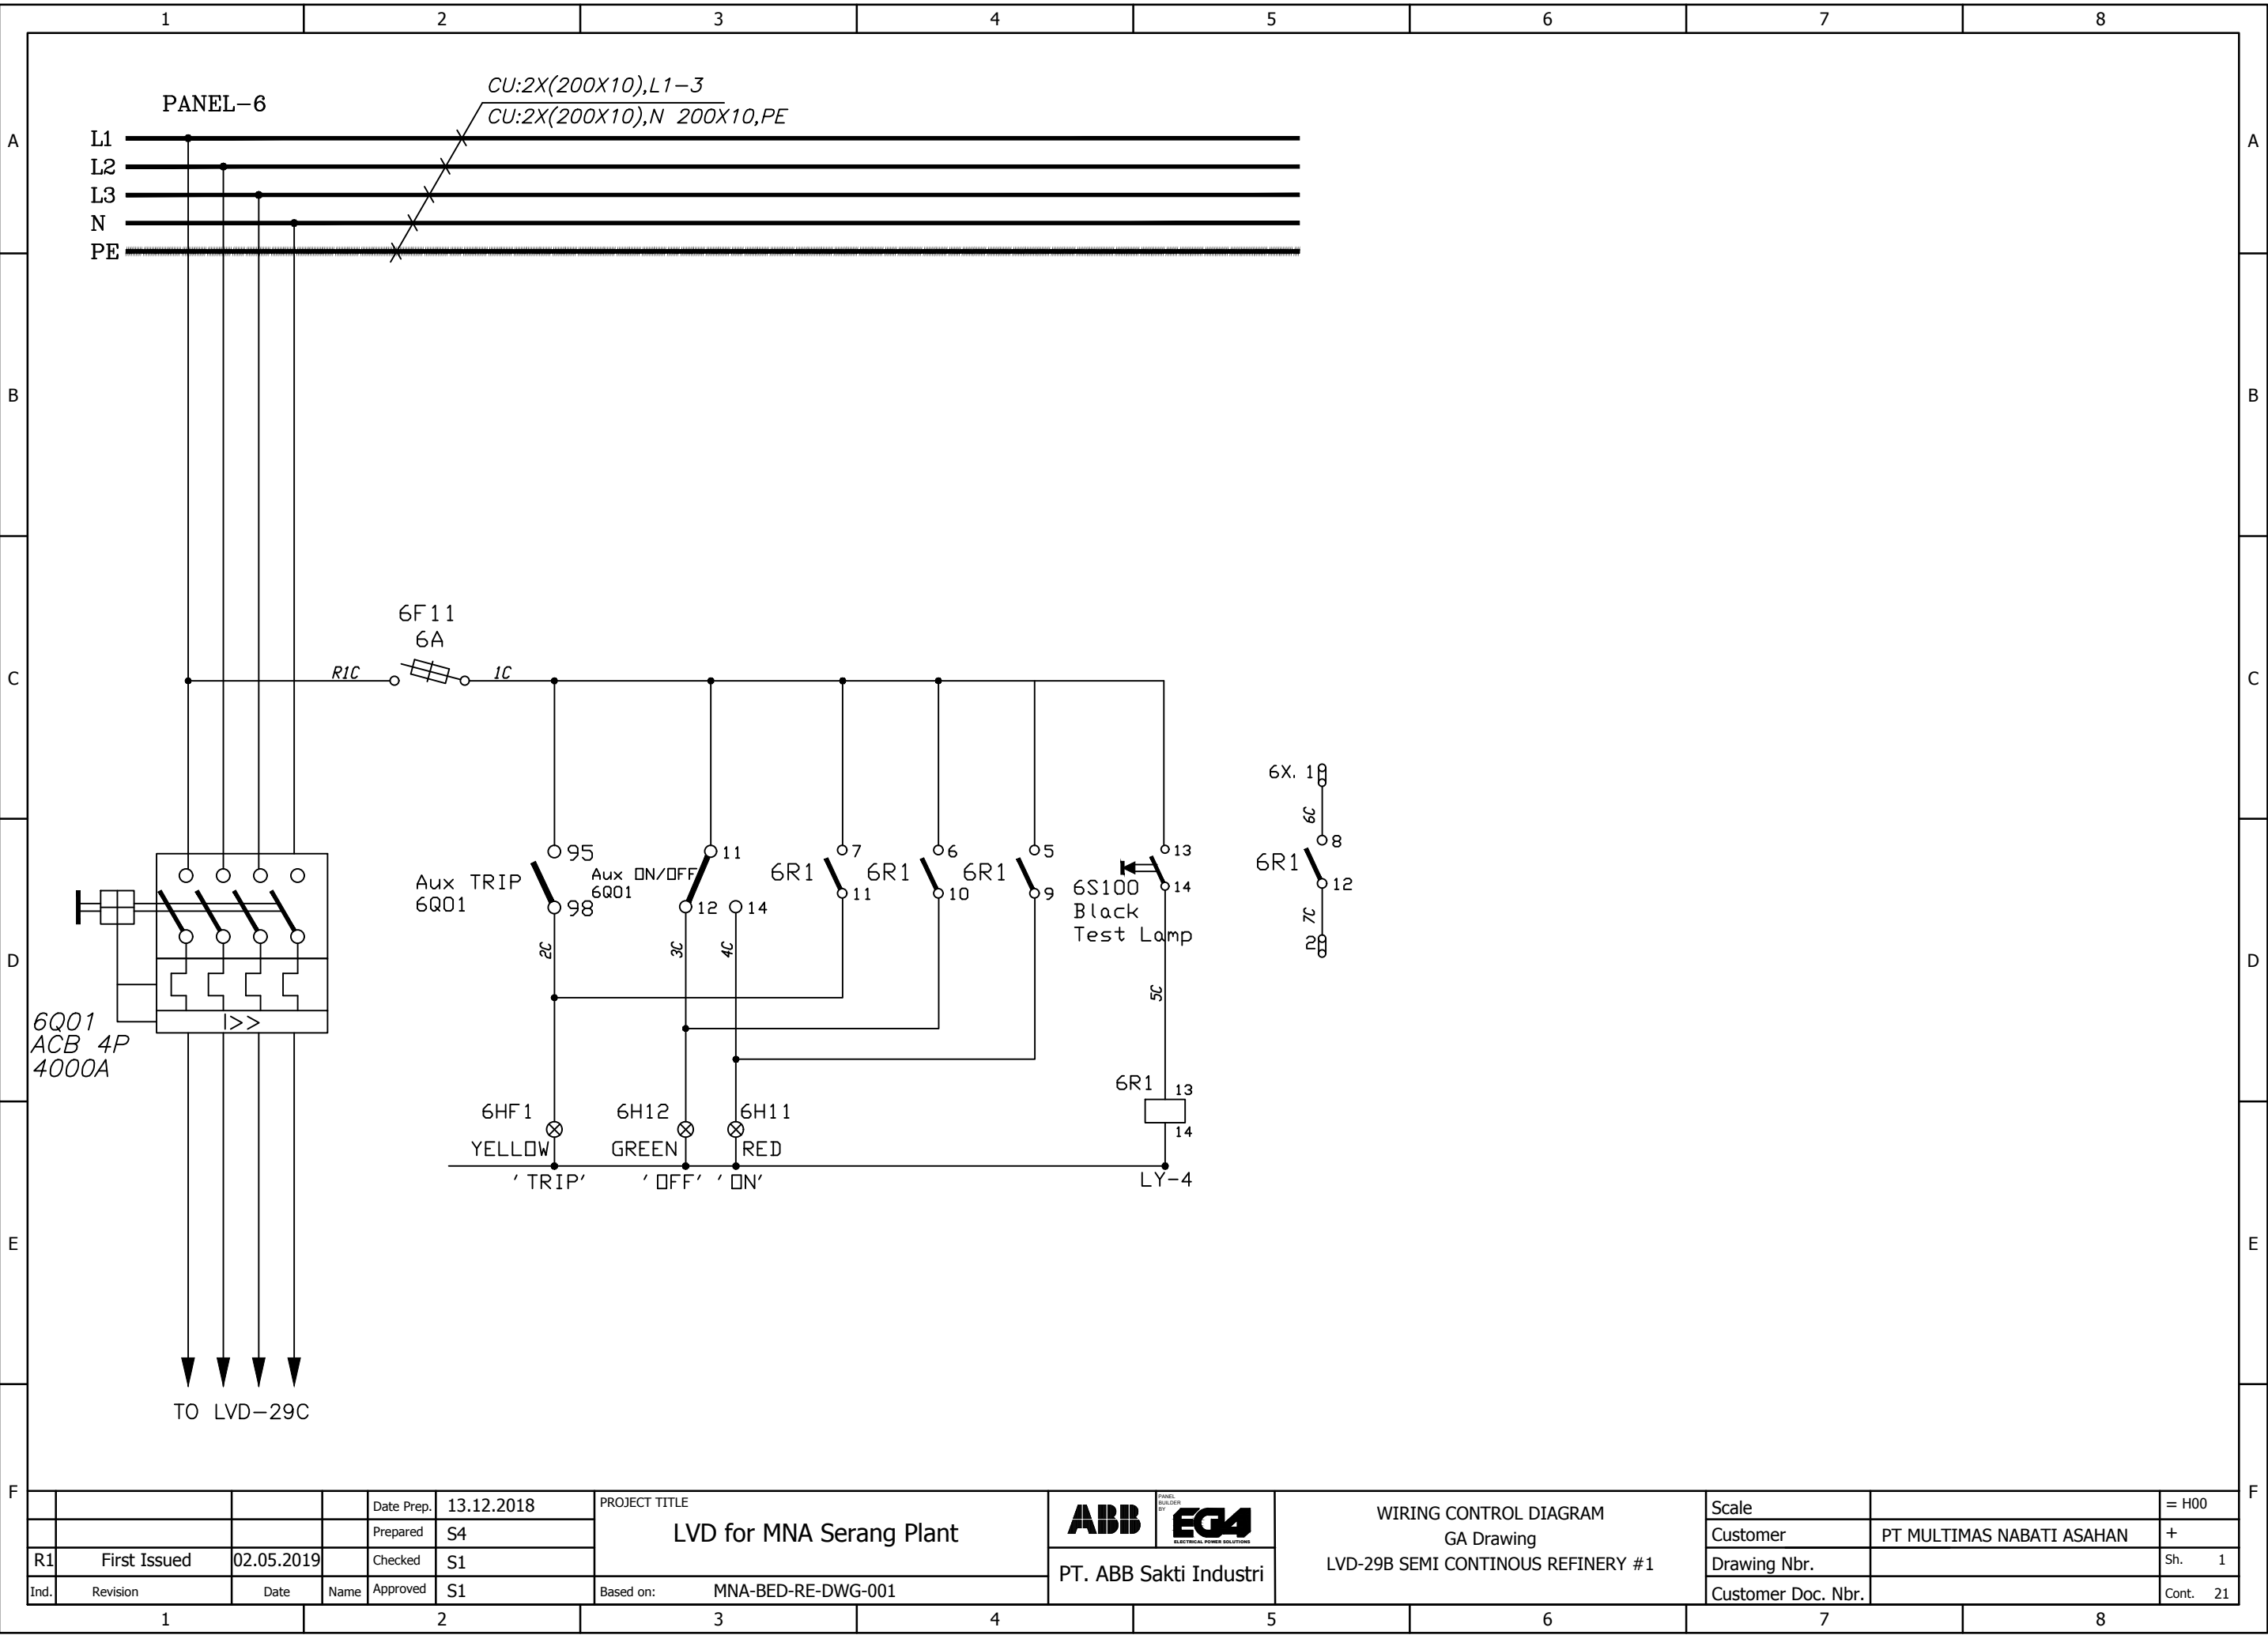

WE RESERVE ALL RIGHTS IN THIS DOCUMENT AND IN THE INFORMATION CONTAINED THEREIN. REPRODUCTION, USE OR DISCLOSURE TO THIRD PARTIES WITHOUT EXPRESS AUTHORITY IS STRICTLY FORBIDDEN.

1		2		3		4		5		6		7		8	
A																A	
B	<table><thead><tr><th>N O</th><th>DESCRIPTION</th><th>TECHNICAL DATA</th><th>QTY</th><th>DESIGNATION</th></tr></thead><tbody><tr><td></td><td colspan="2">INCOMING</td><td></td><td></td></tr><tr><td>1</td><td>Fuse Carrier 6A</td><td>AXLE/Setara</td><td>7</td><td>2F11,2F1-6</td></tr><tr><td>2</td><td>Pilot Lamp (LED) 220Vac/50Hz, Red</td><td>AXLE/Setara</td><td>2</td><td>2H1,11</td></tr><tr><td>3</td><td>Pilot Lamp (LED) 220Vac/50Hz, Yellow</td><td>AXLE/Setara</td><td>2</td><td>2H2,HF1</td></tr><tr><td>4</td><td>Pilot Lamp (LED) 220Vac/50Hz, Green</td><td>AXLE/Setara</td><td>2</td><td>2H3,12</td></tr></tbody></table>																	N O	DESCRIPTION	TECHNICAL DATA	QTY	DESIGNATION		INCOMING				1	Fuse Carrier 6A	AXLE/Setara	7	2F11,2F1-6	2	Pilot Lamp (LED) 220Vac/50Hz, Red	AXLE/Setara	2	2H1,11	3	Pilot Lamp (LED) 220Vac/50Hz, Yellow	AXLE/Setara	2	2H2,HF1	4	Pilot Lamp (LED) 220Vac/50Hz, Green	AXLE/Setara	2	2H3,12	B	
	N O	DESCRIPTION	TECHNICAL DATA	QTY	DESIGNATION	
		INCOMING	
	1	Fuse Carrier 6A	AXLE/Setara	7	2F11,2F1-6	
	2	Pilot Lamp (LED) 220Vac/50Hz, Red	AXLE/Setara	2	2H1,11	
	3	Pilot Lamp (LED) 220Vac/50Hz, Yellow	AXLE/Setara	2	2H2,HF1	
4	Pilot Lamp (LED) 220Vac/50Hz, Green	AXLE/Setara	2	2H3,12	
C	<table><tbody><tr><td>5</td><td>DIGITAL POWER METER (*)</td><td>ABB, M2M ETHERNET</td><td>1</td><td>2P1</td></tr><tr><td>6</td><td>CT 4000/5A CL.0.5 40VA</td><td>Howig, HG 120-4000</td><td>4</td><td>2T1-4</td></tr><tr><td>7</td><td>ACB 3P 4000A, 66KA, DO, Ekip Touch LSIG (*)</td><td>ABB, E4.2N40 D/O</td><td>1</td><td>2Q0</td></tr><tr><td>8</td><td>+ Shunt Trip Release (Y0) (*)</td><td>ABB, Y0</td><td>1</td><td>-</td></tr><tr><td>9</td><td>+ Motor (M) + Closing Release (YC) For E2.2-E6.2 (*)</td><td>ABB, M+YC</td><td>1</td><td>-</td></tr><tr><td>10</td><td>+ Padlocks For E2.2-E6.2 (*)</td><td>ABB,</td><td>1</td><td>-</td></tr></tbody></table>																	5	DIGITAL POWER METER (*)	ABB, M2M ETHERNET	1	2P1	6	CT 4000/5A CL.0.5 40VA	Howig, HG 120-4000	4	2T1-4	7	ACB 3P 4000A, 66KA, DO, Ekip Touch LSIG (*)	ABB, E4.2N40 D/O	1	2Q0	8	+ Shunt Trip Release (Y0) (*)	ABB, Y0	1	-	9	+ Motor (M) + Closing Release (YC) For E2.2-E6.2 (*)	ABB, M+YC	1	-	10	+ Padlocks For E2.2-E6.2 (*)	ABB,	1	-	C	
	5	DIGITAL POWER METER (*)	ABB, M2M ETHERNET	1	2P1	
	6	CT 4000/5A CL.0.5 40VA	Howig, HG 120-4000	4	2T1-4	
	7	ACB 3P 4000A, 66KA, DO, Ekip Touch LSIG (*)	ABB, E4.2N40 D/O	1	2Q0	
	8	+ Shunt Trip Release (Y0) (*)	ABB, Y0	1	-	
	9	+ Motor (M) + Closing Release (YC) For E2.2-E6.2 (*)	ABB, M+YC	1	-	
10	+ Padlocks For E2.2-E6.2 (*)	ABB,	1	-	
D	<table><tbody><tr><td>11</td><td>+ Ekip Com Protocol IEC 61850 (*)</td><td>ABB,</td><td>1</td><td>-</td></tr><tr><td>12</td><td>Control Relay 220Vac</td><td>Omron, LY-2</td><td>1</td><td>2RF1</td></tr><tr><td>13</td><td>Control Relay 220Vac</td><td>Omron, LY-4</td><td>2</td><td>2R1-2</td></tr><tr><td>14</td><td>Push Button On, 1NO, Green</td><td>Ega</td><td>1</td><td>2S11</td></tr><tr><td>15</td><td>Push Button Off, 1NO, Red</td><td>Ega</td><td>1</td><td>2S12</td></tr><tr><td>16</td><td>Push Button Test Lamp , 1NO, Black</td><td>Ega</td><td>1</td><td>2S100</td></tr></tbody></table>																	11	+ Ekip Com Protocol IEC 61850 (*)	ABB,	1	-	12	Control Relay 220Vac	Omron, LY-2	1	2RF1	13	Control Relay 220Vac	Omron, LY-4	2	2R1-2	14	Push Button On, 1NO, Green	Ega	1	2S11	15	Push Button Off, 1NO, Red	Ega	1	2S12	16	Push Button Test Lamp , 1NO, Black	Ega	1	2S100	D	
	11	+ Ekip Com Protocol IEC 61850 (*)	ABB,	1	-	
	12	Control Relay 220Vac	Omron, LY-2	1	2RF1	
	13	Control Relay 220Vac	Omron, LY-4	2	2R1-2	
	14	Push Button On, 1NO, Green	Ega	1	2S11	
	15	Push Button Off, 1NO, Red	Ega	1	2S12	
16	Push Button Test Lamp , 1NO, Black	Ega	1	2S100	
E	<table><tbody><tr><td>17</td><td></td><td></td><td></td><td></td></tr><tr><td>18</td><td>COUPLER</td><td></td><td></td><td></td></tr><tr><td>19</td><td>Fuse Carrier 6A</td><td>AXLE/Setara</td><td>2</td><td>1,6F11</td></tr><tr><td>20</td><td>Pilot Lamp (LED) 220Vac/50Hz, Red</td><td>AXLE/Setara</td><td>2</td><td>1,6H11</td></tr><tr><td>21</td><td>Pilot Lamp (LED) 220Vac/50Hz, Yellow</td><td>AXLE/Setara</td><td>2</td><td>1,6HF1</td></tr><tr><td>22</td><td>Pilot Lamp (LED) 220Vac/50Hz, Green</td><td>AXLE/Setara</td><td>2</td><td>1,6H12</td></tr></tbody></table>																	17					18	COUPLER				19	Fuse Carrier 6A	AXLE/Setara	2	1,6F11	20	Pilot Lamp (LED) 220Vac/50Hz, Red	AXLE/Setara	2	1,6H11	21	Pilot Lamp (LED) 220Vac/50Hz, Yellow	AXLE/Setara	2	1,6HF1	22	Pilot Lamp (LED) 220Vac/50Hz, Green	AXLE/Setara	2	1,6H12	E	
	17	
	18	COUPLER	
	19	Fuse Carrier 6A	AXLE/Setara	2	1,6F11	
	20	Pilot Lamp (LED) 220Vac/50Hz, Red	AXLE/Setara	2	1,6H11	
	21	Pilot Lamp (LED) 220Vac/50Hz, Yellow	AXLE/Setara	2	1,6HF1	
22	Pilot Lamp (LED) 220Vac/50Hz, Green	AXLE/Setara	2	1,6H12	
F	<table><tbody><tr><td>23</td><td>ACB 4P 4000A, 66KA, FT, Ekip Dip LI (*)</td><td>ABB, E4.2N40 F/T</td><td>2</td><td>1,6Q01</td></tr><tr><td>24</td><td>+ Padlocks For E2.2-E6.2 (*)</td><td>ABB,</td><td>2</td><td>-</td></tr><tr><td>25</td><td>Push Button Test Lamp , 1NO, Black</td><td>Ega</td><td>2</td><td>S100</td></tr><tr><td>26</td><td>Control Relay 220Vac</td><td>Omron, LY-4</td><td>2</td><td>1,6R1</td></tr></tbody></table>																	23	ACB 4P 4000A, 66KA, FT, Ekip Dip LI (*)	ABB, E4.2N40 F/T	2	1,6Q01	24	+ Padlocks For E2.2-E6.2 (*)	ABB,	2	-	25	Push Button Test Lamp , 1NO, Black	Ega	2	S100	26	Control Relay 220Vac	Omron, LY-4	2	1,6R1	F	
	23	ACB 4P 4000A, 66KA, FT, Ekip Dip LI (*)	ABB, E4.2N40 F/T	2	1,6Q01	
	24	+ Padlocks For E2.2-E6.2 (*)	ABB,	2	-	
	25	Push Button Test Lamp , 1NO, Black	Ega	2	S100	
26	Control Relay 220Vac	Omron, LY-4	2	1,6R1	
<table><thead><tr><th colspan="2"></th><th colspan="2"></th><th colspan="2">Date Prep.</th><th colspan="2">13.12.2018</th><th colspan="2">PROJECT TITLE</th><th colspan="2"> </th><th colspan="2">COMPONENT LIST</th><th colspan="2">Scale</th><th colspan="2">= H00</th></tr><tr><th colspan="2"></th><th colspan="2"></th><th colspan="2">Prepared</th><th colspan="2">S4</th><th colspan="2" rowspan="2">LVD for MNA Serang Plant</th><th colspan="2" rowspan="2">PT. ABB Sakti Industri</th><th colspan="2" rowspan="2">GA Drawing LVD-29B SEMI CONTINOUS REFINERY #1</th><th colspan="2">Customer</th><th colspan="2">PT MULTIMAS NABATI ASAHAN</th><th colspan="2">+</th></tr><tr><th colspan="2">R1</th><th colspan="2">First Issued</th><th colspan="2">02.05.2019</th><th colspan="2">Checked</th><th colspan="2">S1</th><th colspan="2">Drawing Nbr.</th><th colspan="2"></th><th colspan="2">Sh.</th><th colspan="2">1</th></tr><tr><th colspan="2">Ind.</th><th colspan="2">Revision</th><th colspan="2">Date</th><th colspan="2">Name</th><th colspan="2">Approved</th><th colspan="2">S1</th><th colspan="2">Based on:</th><th colspan="2">MNA-BED-RE-DWG-001</th><th colspan="2">Customer Doc. Nbr.</th><th colspan="2">Cont.</th><th colspan="2">21</th></tr></thead><tbody><tr><td colspan="2">1</td><td colspan="2"></td><td colspan="2">2</td><td colspan="2"></td><td colspan="2">3</td><td colspan="2"></td><td colspan="2">4</td><td colspan="2"></td><td colspan="2">5</td><td colspan="2"></td><td colspan="2">6</td><td colspan="2"></td><td colspan="2">7</td><td colspan="2"></td><td colspan="2">8</td><td colspan="2"></td></tr><tr><td colspan="28"></td></tr></tbody></table>																					Date Prep.		13.12.2018		PROJECT TITLE		 		COMPONENT LIST		Scale		= H00						Prepared		S4		LVD for MNA Serang Plant		PT. ABB Sakti Industri		GA Drawing LVD-29B SEMI CONTINOUS REFINERY #1		Customer		PT MULTIMAS NABATI ASAHAN		+		R1		First Issued		02.05.2019		Checked		S1		Drawing Nbr.				Sh.		1		Ind.		Revision		Date		Name		Approved		S1		Based on:		MNA-BED-RE-DWG-001		Customer Doc. Nbr.		Cont.		21		1				2				3				4				5				6				7				8																															
				Date Prep.		13.12.2018		PROJECT TITLE		 		COMPONENT LIST		Scale		= H00	
				Prepared		S4		LVD for MNA Serang Plant		PT. ABB Sakti Industri		GA Drawing LVD-29B SEMI CONTINOUS REFINERY #1		Customer		PT MULTIMAS NABATI ASAHAN		+	
R1		First Issued		02.05.2019		Checked								S1		Drawing Nbr.				Sh.		1	
Ind.		Revision		Date		Name		Approved		S1		Based on:		MNA-BED-RE-DWG-001		Customer Doc. Nbr.		Cont.		21	
1				2				3				4				5				6				7				8	

