


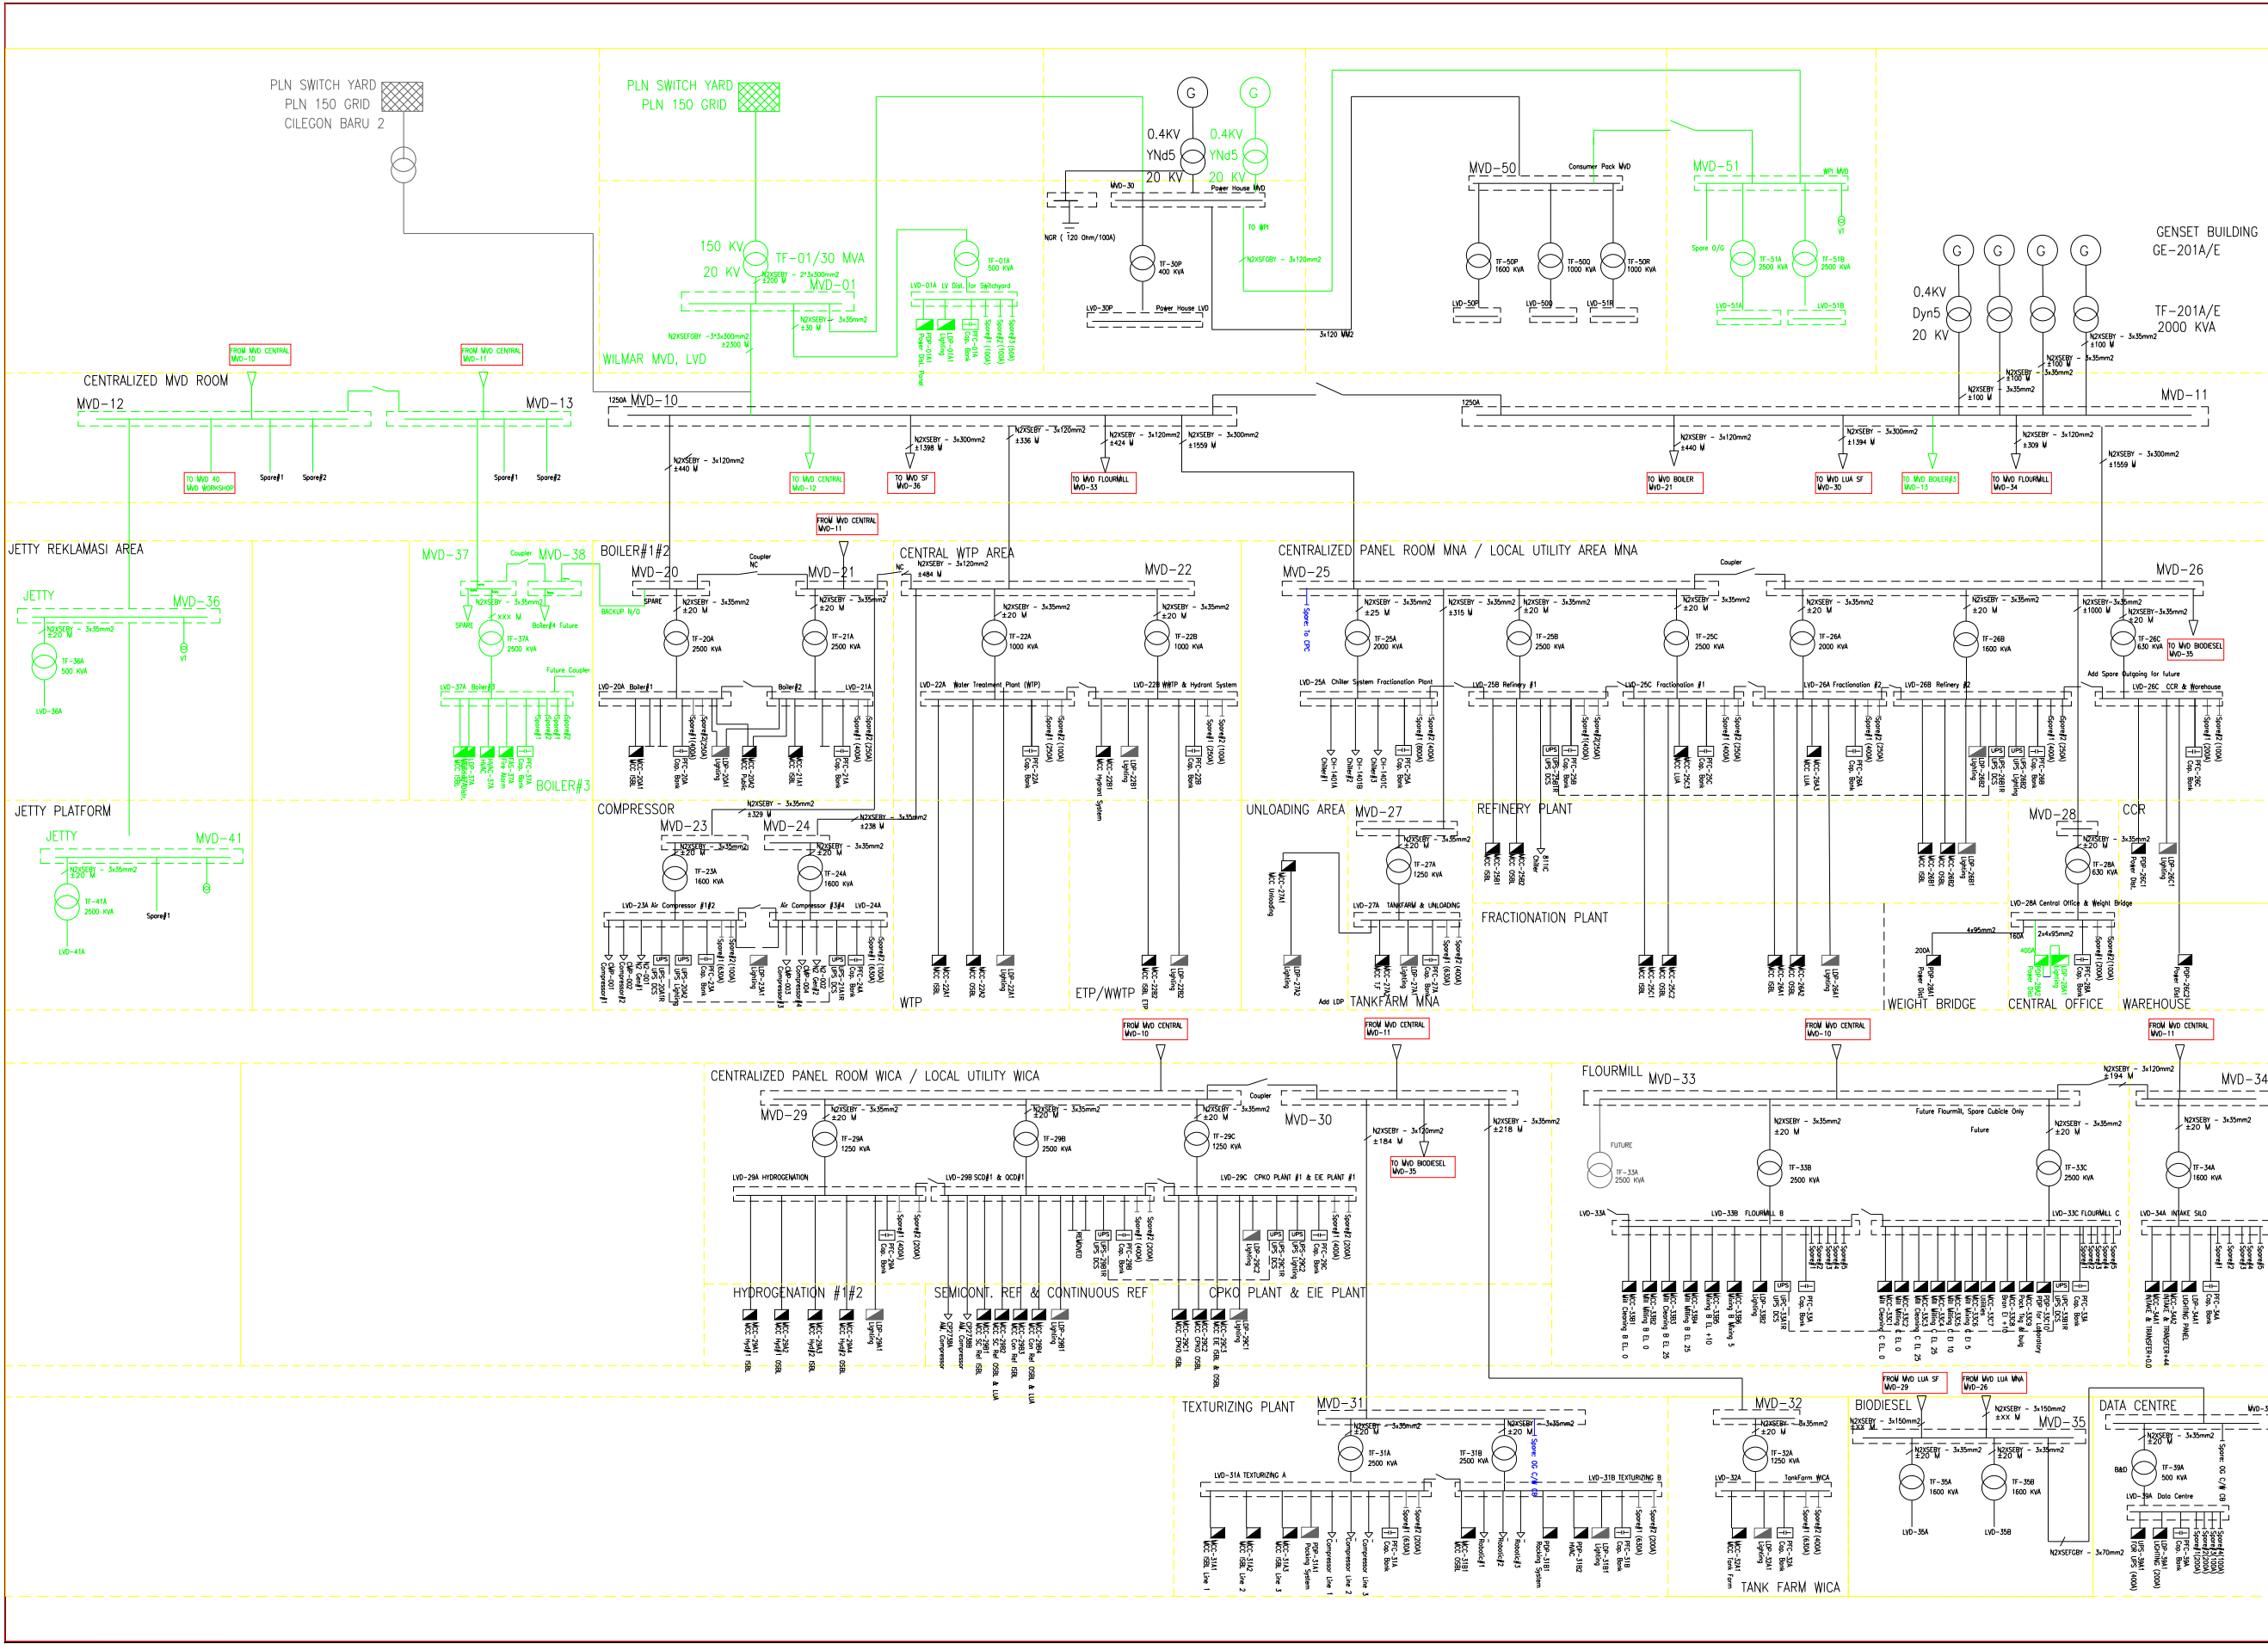

LEGENDA/LEGEND

STATUS

AWAL/INITIAL

| NO | KETERANGAN<br>DESCRIPTION | PARAF<br>SIGN | TANGGAL<br>DATE |
|----|---------------------------|---------------|-----------------|
| 1  | Relocated LDP-26A1        | AMM           | 12/10/18        |
| 2  | Remove MCC EIE OSBL       | AMM           | 12/10/18        |
| 3  | Remove MCC-29B5           | AMM           | 01/11/18        |
| 4  | Remove MCC-29B6           | AMM           | 01/11/18        |
| 5  | Update Plant              | AMM           | 18/09/20        |
| 6  |                           |               |                 |

PEKERJAAN  
PROJECT

Power Distribution

LOKASI  
LOCATION

KRAMATWATU - SERANG  
BANTEN

| SKALA<br>SCALE         | SEE TO DRAW  | PARAF<br>SIGN | TANGGAL<br>DATE |
|------------------------|--------------|---------------|-----------------|
| DIGAMBAR<br>DRAWN      | AMM          |               |                 |
| DIPERIKSA<br>CHECKED   | YAZID, WAWAN |               |                 |
| DISETUIJUI<br>APPROVED | COR          |               |                 |

GAMBAR  
TITLE

Power Distribution Connection Diagram  
HV to LV Distribution

| NO. GAMBAR<br>DRAWING NO. | REVISI<br>REV | PAGE<br>SHEET |
|---------------------------|---------------|---------------|
| MNA-BED-RE-DWG-001-01     | 01            | 1/1           |

MNA  
wilmar

PT. MULTIMAS NABATI ASAHAN  
MAILING ADDRESS : KAWASAN INDUSTRI MNA SERANG  
JL. RAYA BONGCAGARA KM.5 KAY.162  
KEC. KRAMATWATU, SERANG - BANTEN  
PHONE. (0254) - 8495263