


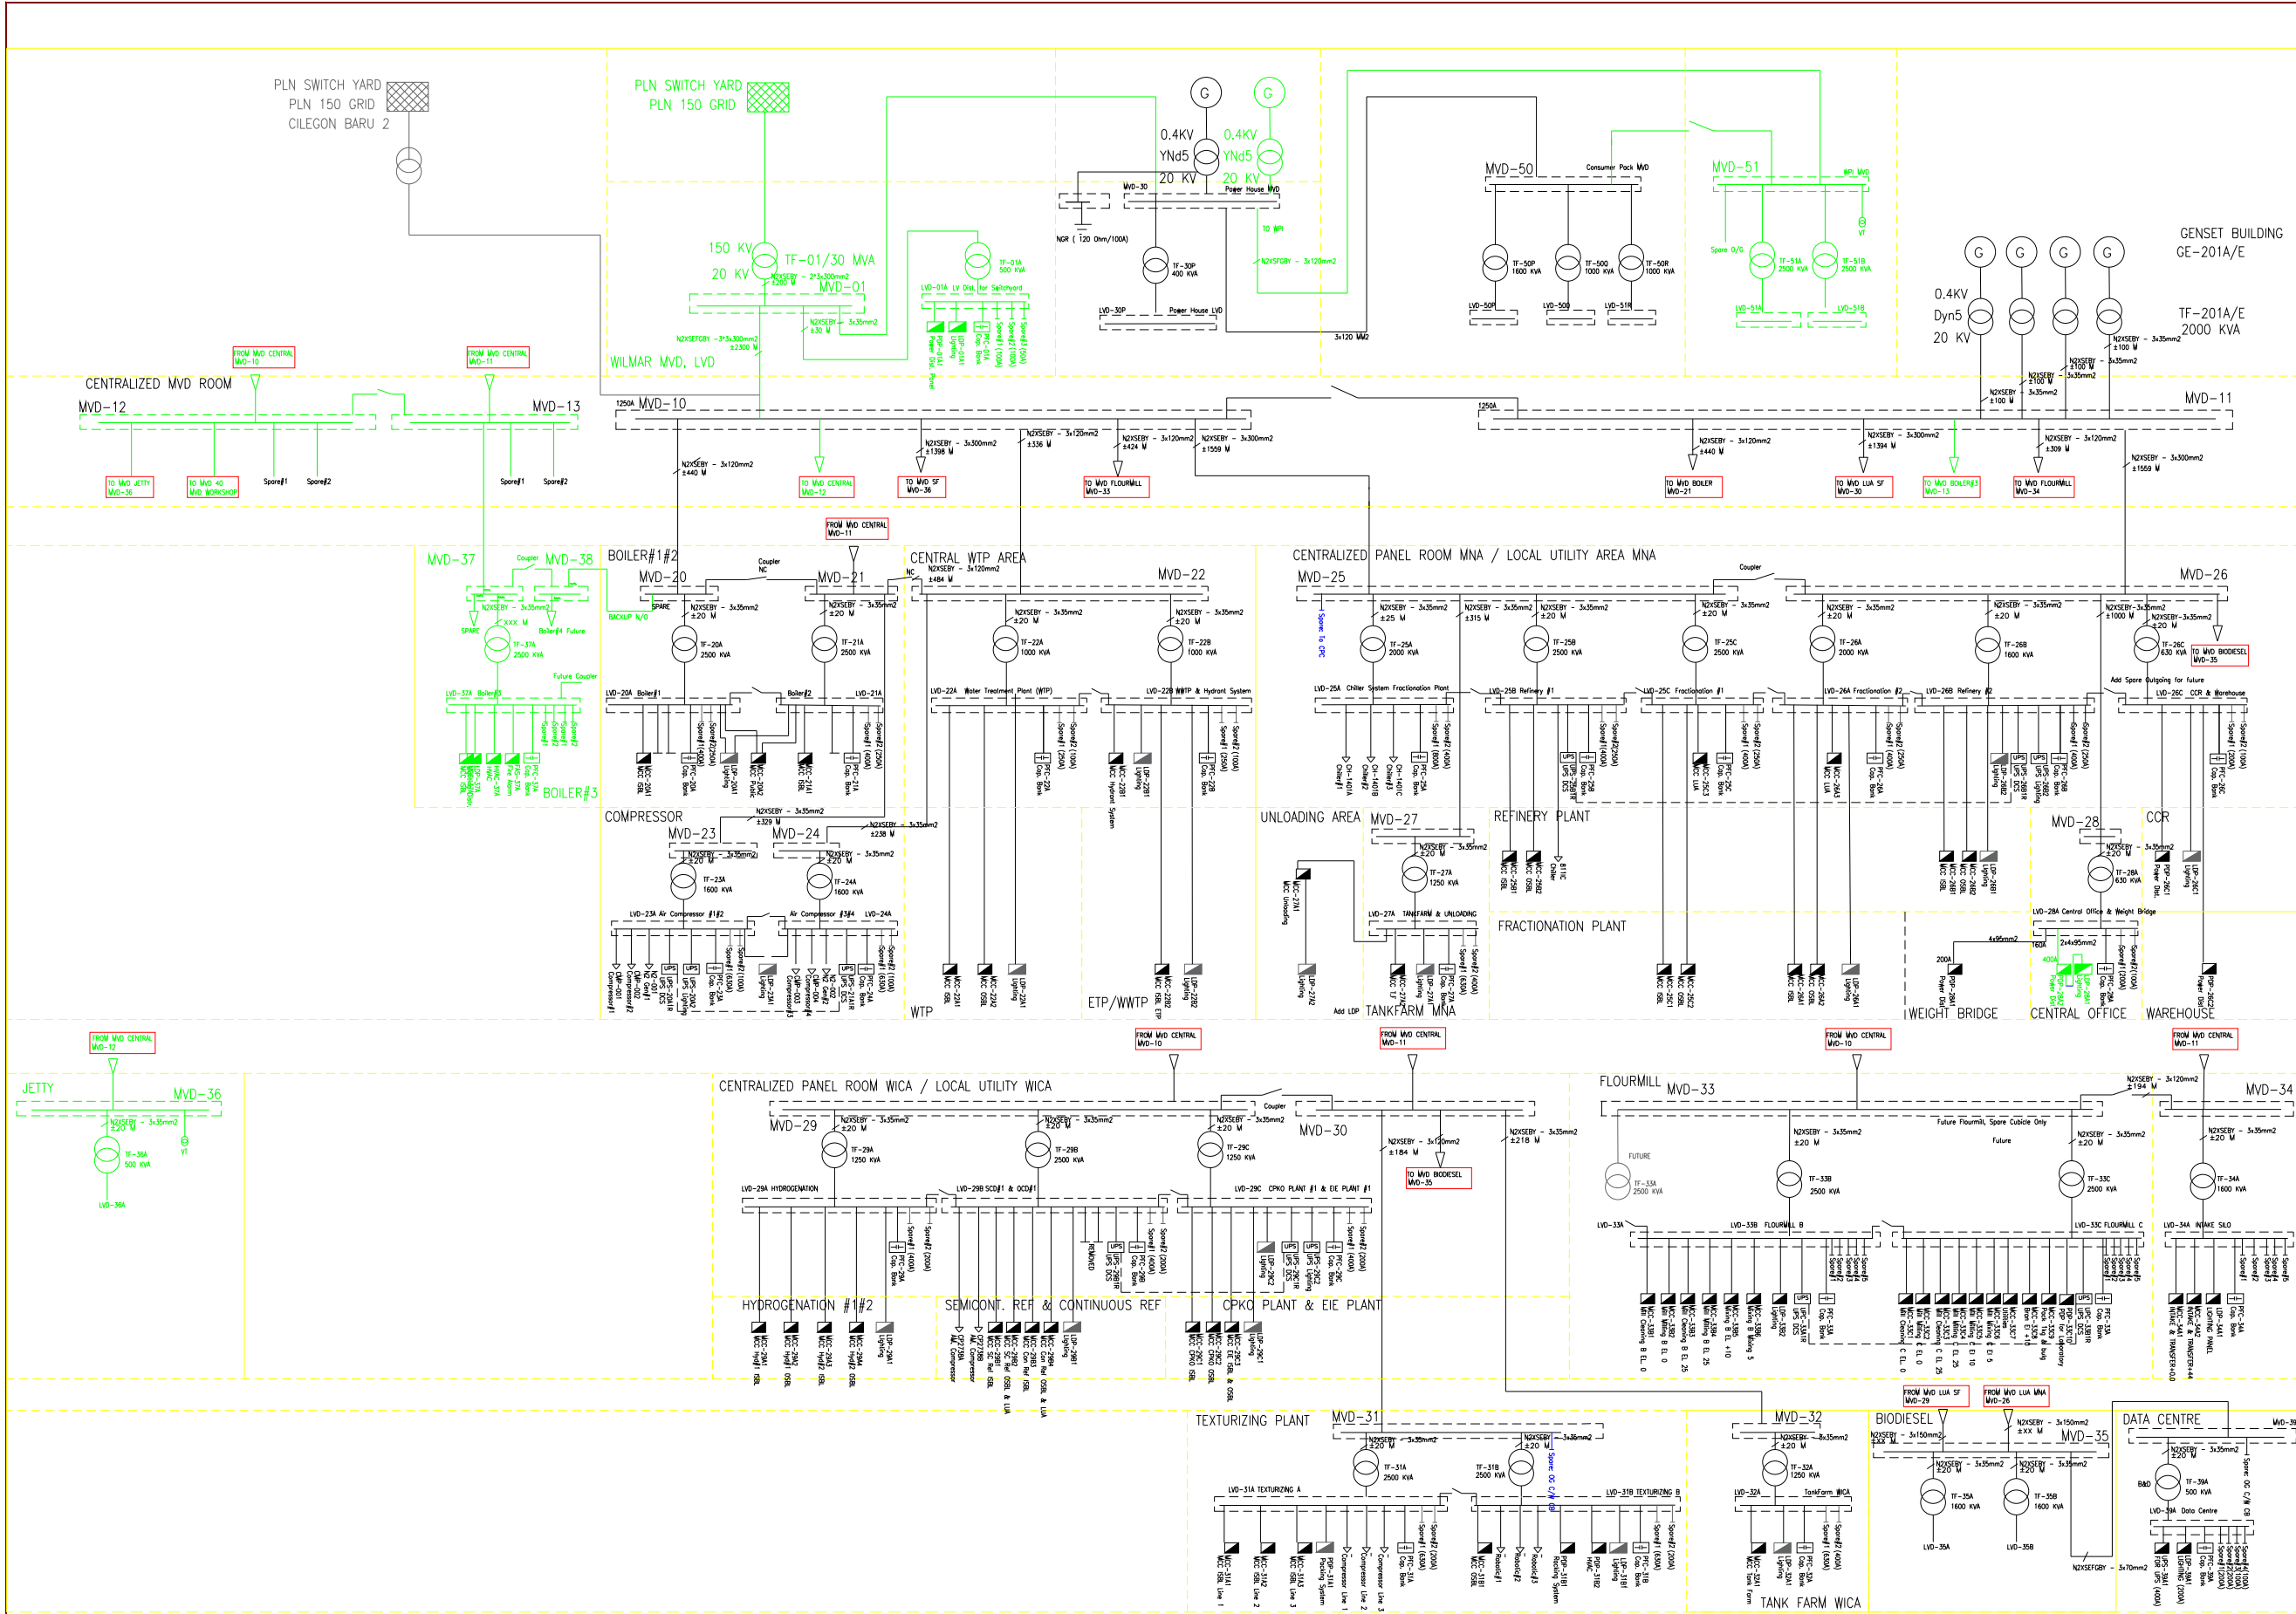

LEGENDA/LEGEND

STATUS

AWAL/INITIAL

NO	KETERANGAN DESCRIPTION	PARAF SIGN	TANGGAL DATE
1	Relocated LDP-26A1	AMM	12/10/18
2	Remove MCC-EIE OSBL	AMM	12/10/18
3	Remove MCC-29B5	AMM	01/11/18
4	Remove MCC-29B6	AMM	01/11/18
5	Update Plant	AMM	18/09/20
6			

PEKERJAAN
PROJECT

Power Distribution

LOKASI
LOCATION

KRAMATWATU – SERANG
BANTEN

SKALA SCALE	SEE TO DRAW	PARAF SIGN	TANGGAL DATE
DIGAMBAR DRAWN	AMM		
DIPERIKSA CHECKED	YAZID, WAWAN		
DISETUJUI APPROVED	COR		

GAMBAR
TITLE

Power Distribution Connection Diagram
HV to LV Distribution

NO. GAMBAR DRAWING NO.	MNA-BED-RE-DWG-001	REVISI REVISION	PAGE SHEET
			1/1

MNA
wimar

PT.MULTIMAS NABATI ASAHAN
MAILING ADDRESS : KABUPATEN INDRAJATI, KOTA SERANG
JL. RAYA BOJONEGARA KM.5 KAW. 162
KEC.KRAMATWATU SERANG – BANTEN
PHONE. (0254) – 8495283